


17000

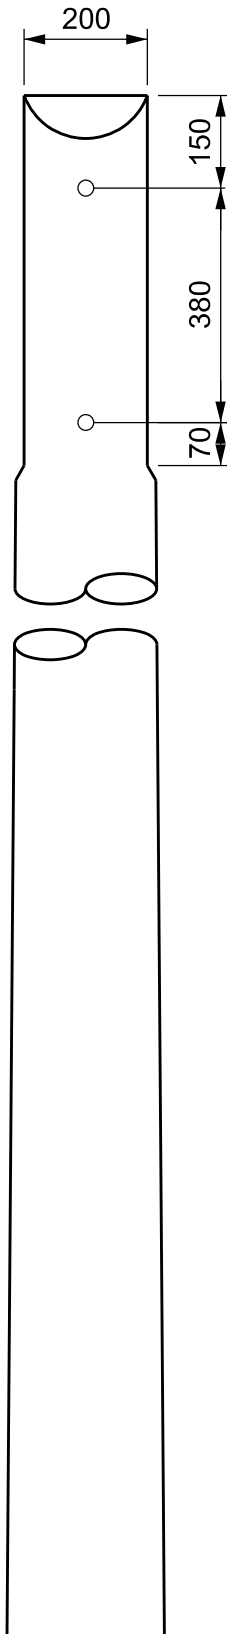

All drillings 22mm diameter

Description:
17m stout pole to ENATS 43-88

All dimensions in millimetres except where otherwise stated.

DRAWING STATUS	FOR APPROVAL	☒
	FOR TENDER	☐
	FOR CONSTRUCTION	☐
	AS BUILT	☐

 Yorkshire House
York Road
Little Driffield
East Yorkshire
YO25 5KA
Tel 01377 253617
Fax 01377 259555

THIS DRAWING AND ANY INFORMATION OR DESCRIPTIVE MATTER SET OUT HEREON ARE THE CONFIDENTIAL AND COPYRIGHT PROPERTY OF ELECTRICITY NORTH WEST LIMITED AND MUST NOT BE DISCLOSED, LOANED, COPIED OR USED FOR ANY PURPOSE WITHOUT WRITTEN PERMISSION.						
NOT TO BE SCALED. UNLESS OTHERWISE STATED DIMENSIONS ARE IN MILLIMETRES.						
REV	AMENDMENTS	DWN	CHKD	APP.	DATE	



DRAWN	L.B.	SCALE	N.T.S.
CHECKED (LSTC)	D.T.C.	DATE	17-2-15
APPROVED (ENW)		SHEET SIZE	A4

ELECTRICITY NORTH WEST
WHITEBIRK DEPOT
WHITEBIRK DRIVE
BLACKBURN
BB1 3HT

DRILLING DETAILS FOR TEMPORARY TERMINAL WOODPOLES AT DP10			
SITE NAME	PEEL - LYTHAM		
DWG NO	18-14537-30	REV	A