


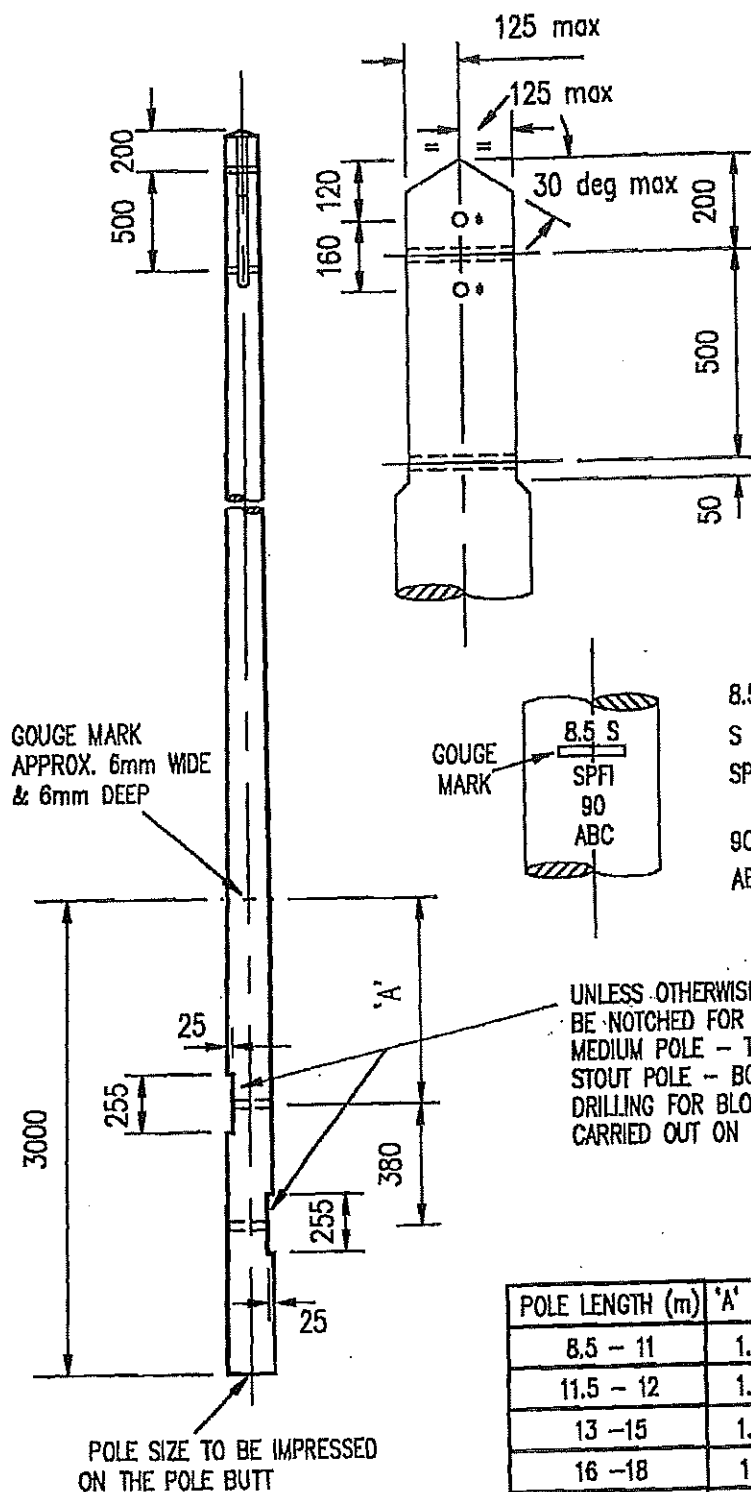

SCARFING TO BE CUT TO GIVE A 50mm FACE AND THE END CHAMFERED OFF BEYOND THE LENGTH SHOWN

DRILLINGS 22mm DIA.

POLE SCARFED ON BOTH SIDES OF MEDIUM AND STOUT POLES, ONE SIDE ONLY ON LIGHT POLES

* POSITION OF ANTI-SPLIT BOLTS IF REQUIRED

8.5 LENGTH OF POLE IN METRES
S GRADE OF POLE (L, M, S)
SPFI TIMBER SPECIES AND COUNTRY OF ORIGIN
90 YEAR OF CREOSOTING (1990)
ABC SUPPLIER'S MARK

UNLESS OTHERWISE SPECIFIED POLES TO BE NOTCHED FOR BLOCKS AS FOLLOWS:-
MEDIUM POLE - TOP BLOCK ONLY
STOUT POLE - BOTH BLOCKS
DRILLING FOR BLOCK BOLT TO BE CARRIED OUT ON SITE AS REQUIRED

POLE LENGTH (m)	'A' (m)
8.5 - 11	1.9
11.5 - 12	1.7
13 - 15	1.4
16 - 18	1.1
20	0.5

ALL DIMENSIONS IN MILLIMETRES UNLESS OTHERWISE SHOWN

Date	12.09.91	Title			
Drawn	W.J.B.	SINGLE POLE DRILLING, SCARFING & MARKING			
Checked					
Approved		Project 11 & 33KV WOOD POLE OVERHEAD LINE SPECIFICATION	Drawing Number	Sht. No.	Rev.
Scale			501/1109/0205		1



PERTH