

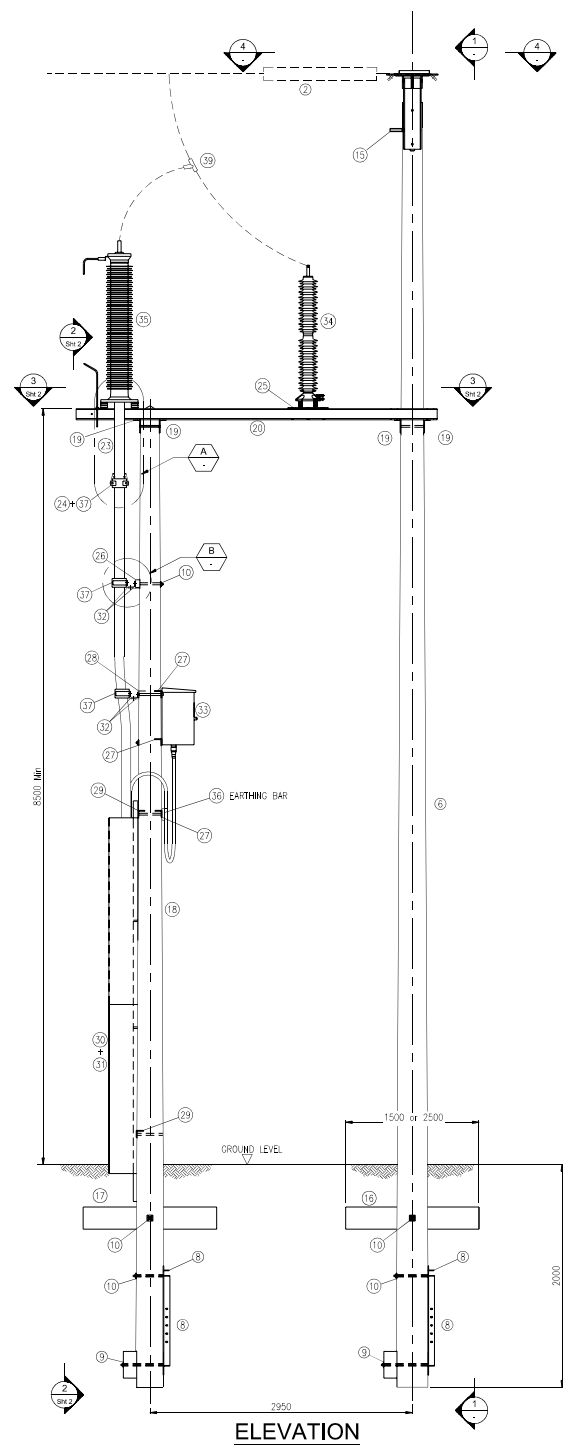




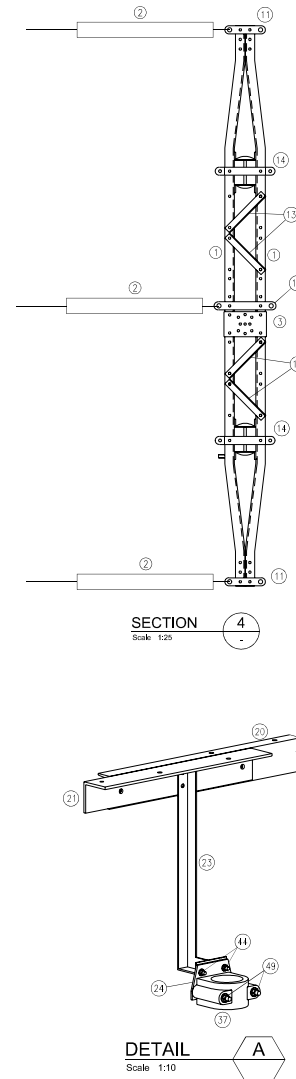


ELEVATION

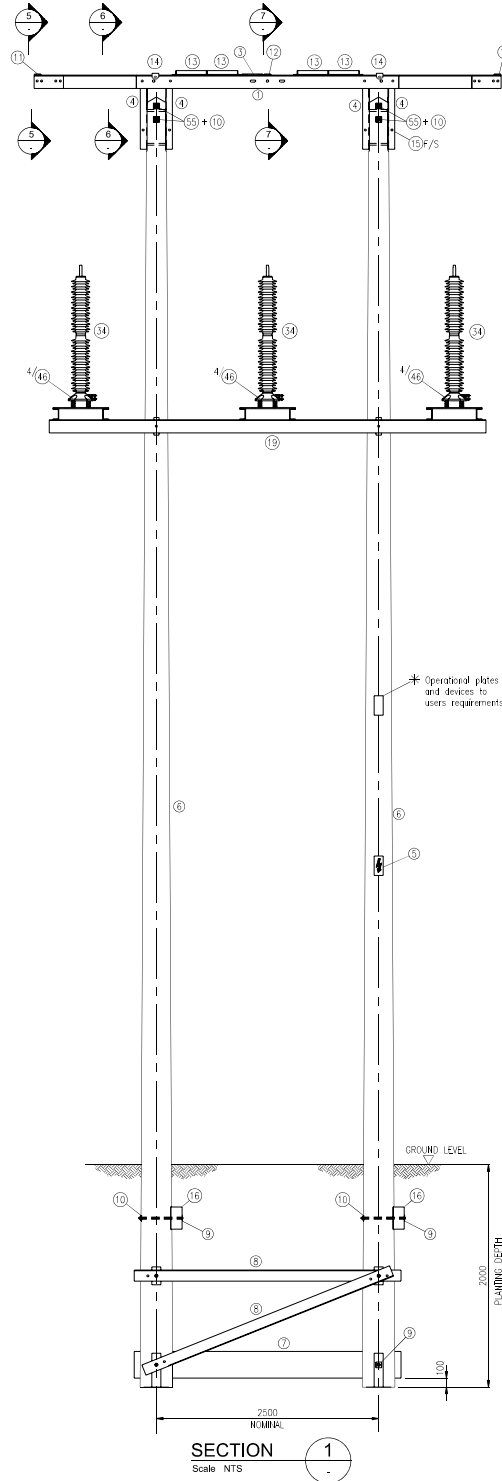

DETAIL A

DETAIL B

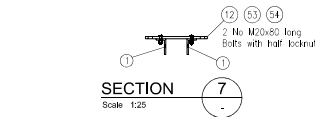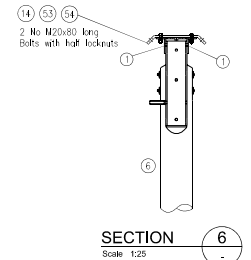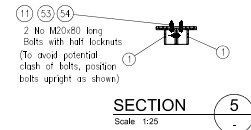

- NOTES
1. ALL DIMENSIONS IN MILLIMETRES.
  2. THIS DRAWING TO BE READ IN CONJUNCTION WITH BBUS DRAWING NUMBER A0/PTD/6547/135.
  3. STAY ARRANGEMENTS AND TOP BAULKS REQUIRED TO SUIT GROUND CONDITIONS. REFER TO DRAWINGS A2/PTD/6510/006, AND SCHEDULES BK/PTD/6547/063 & BK/PTD/6547/161 FOR DETAILS.

|   |                                                         |                                                          |                                            |                                                |                                                |                                          |                                                         |
|---|---------------------------------------------------------|----------------------------------------------------------|--------------------------------------------|------------------------------------------------|------------------------------------------------|------------------------------------------|---------------------------------------------------------|
| A0/PTD/6547/134   |                                                         |                                                          |                                            |                                                |                                                |                                          |                                                         |
| Designer's site specific risk assessment   |                                                         |                                                          |                                            |                                                |                                                |                                          |                                                         |
| By: LRB/gwy   | Date: 14/03/16                                          |                                                          |                                            |                                                |                                                |                                          |                                                         |
| <input type="checkbox"/> No works associated with this drawing   |                                                         |                                                          |                                            |                                                |                                                |                                          |                                                         |
| <input checked="" type="checkbox"/> Controlled by existing procedure/work instruction   |                                                         |                                                          |                                            |                                                |                                                |                                          |                                                         |
| <input type="checkbox"/> Spelled control required:-<br><input type="checkbox"/> Detailed on drawing<br><input type="checkbox"/> Detailed on separate document   |                                                         |                                                          |                                            |                                                |                                                |                                          |                                                         |
| <input checked="" type="checkbox"/> No temporary works required<br><input type="checkbox"/> Temporary works required and documented separately   |                                                         |                                                          |                                            |                                                |                                                |                                          |                                                         |
| <input type="checkbox"/> Drawing contains temporary works:<br><table><tr><td><input type="checkbox"/> Generic or proprietary solution</td><td><input type="checkbox"/> Complex temporary</td></tr><tr><td><input type="checkbox"/> Specific basic design</td><td><input type="checkbox"/> Specific design check</td></tr><tr><td><input type="checkbox"/> Specific design</td><td><input type="checkbox"/> High risk or specialist design</td></tr></table>                            |                                                         | <input type="checkbox"/> Generic or proprietary solution | <input type="checkbox"/> Complex temporary | <input type="checkbox"/> Specific basic design | <input type="checkbox"/> Specific design check | <input type="checkbox"/> Specific design | <input type="checkbox"/> High risk or specialist design |
| <input type="checkbox"/> Generic or proprietary solution   | <input type="checkbox"/> Complex temporary              |                                                          |                                            |                                                |                                                |                                          |                                                         |
| <input type="checkbox"/> Specific basic design   | <input type="checkbox"/> Specific design check          |                                                          |                                            |                                                |                                                |                                          |                                                         |
| <input type="checkbox"/> Specific design   | <input type="checkbox"/> High risk or specialist design |                                                          |                                            |                                                |                                                |                                          |                                                         |
| Red<br><input type="checkbox"/> OK to proceed providing specific design hazards and risks have been recognised, acknowledged and understood by the construction team. Site operatives may require additional instruction/training   |                                                         |                                                          |                                            |                                                |                                                |                                          |                                                         |
| Amber<br><input type="checkbox"/> OK to proceed as detailed in existing work instruction or procedure detailed on drawing or separate document   |                                                         |                                                          |                                            |                                                |                                                |                                          |                                                         |
| Green<br><input type="checkbox"/> OK to proceed: no significant design hazards and risks, standard control measures apply   |                                                         |                                                          |                                            |                                                |                                                |                                          |                                                         |
| <b>CDM REGULATIONS RESIDUAL RISKS</b><br>Design based hazards are actively eliminated where possible. Where hazards cannot be eliminated, the symbol along with an attached note will identify the hazard and indicate that an action is required to the extent of the works to manage the design hazard during construction.<br>Other than those noted, we are not aware of any further residual design risks apart from those that a competent contractor would inherently consider. |                                                         |                                                          |                                            |                                                |                                                |                                          |                                                         |

|   |        |                                            |                          |      |     |
|---|--------|--------------------------------------------|--------------------------|------|-----|
| B   | 200/16 | UPDATED TO REFERENCE GENERAL NOTES DRAWING | PLANTING DEPTH SHORTENED | B    | REC |
| A   | 200/16 | FIRST ISSUE                                |                          |      |     |
| ISSUE   | DATE   | REVISION                                   | CHKD                     | APPD |     |
| BHLARADH/BEINNEUN SCHEME OVERHEAD LINE WORKS   |        |                                            |                          |      |     |
| PROJECT:-<br>FORT AUGUSTUS - GLENMORISTON (FM)<br>FORT AUGUSTUS - CEANNACROC (FC)   |        |                                            |                          |      |     |
|   |        |                                            |                          |      |     |
| TITLE:-<br>POLE MOUNTED CABLE TERMINATION ASSEMBLY   |        |                                            |                          |      |     |
| 132kV WOOD POLE OHL   |        |                                            |                          |      |     |
| APPD   | DATE   | 15/03/16                                   |                          |      |     |
| DESIGN   | IR     | APPD                                       | WJ                       |      |     |
| <b>Balfour Beatty</b>   |        |                                            |                          |      |     |
| © Balfour Beatty plc 2016<br>THE COMPANY AND ITS SUBSIDIARIES ARE NOT RESPONSIBLE FOR THE REPRODUCTION OR DISTRIBUTION OF THIS DRAWING IN ANY FORM OR BY ANY MEANS, WITHOUT THE WRITTEN CONSENT OF Balfour Beatty plc. THE COMPANY AND ITS SUBSIDIARIES ARE NOT RESPONSIBLE FOR THE REPRODUCTION OR DISTRIBUTION OF THIS DRAWING IN ANY FORM OR BY ANY MEANS, WITHOUT THE WRITTEN CONSENT OF Balfour Beatty plc. |        |                                            |                          |      |     |
| DRAWING No. A0/PTD/6547/134   |        |                                            |                          |      |     |
| SSE CONTRACT No. MSTN   |        |                                            |                          |      |     |
| SSE DRAWING No. A0   |        |                                            |                          |      |     |
| B   |        |                                            |                          |      |     |