


USED ON LSTC/STD/GNA/500

POLE SCARFED PARALLEL ON BOTH
SIDES TO GIVE 50mm WIDE FLAT FACE

DESCRIPTION		FOR ISSUE			
REV	DATE	BY	CHKD	APPD	GS
7	03/03/08	JR	SP		

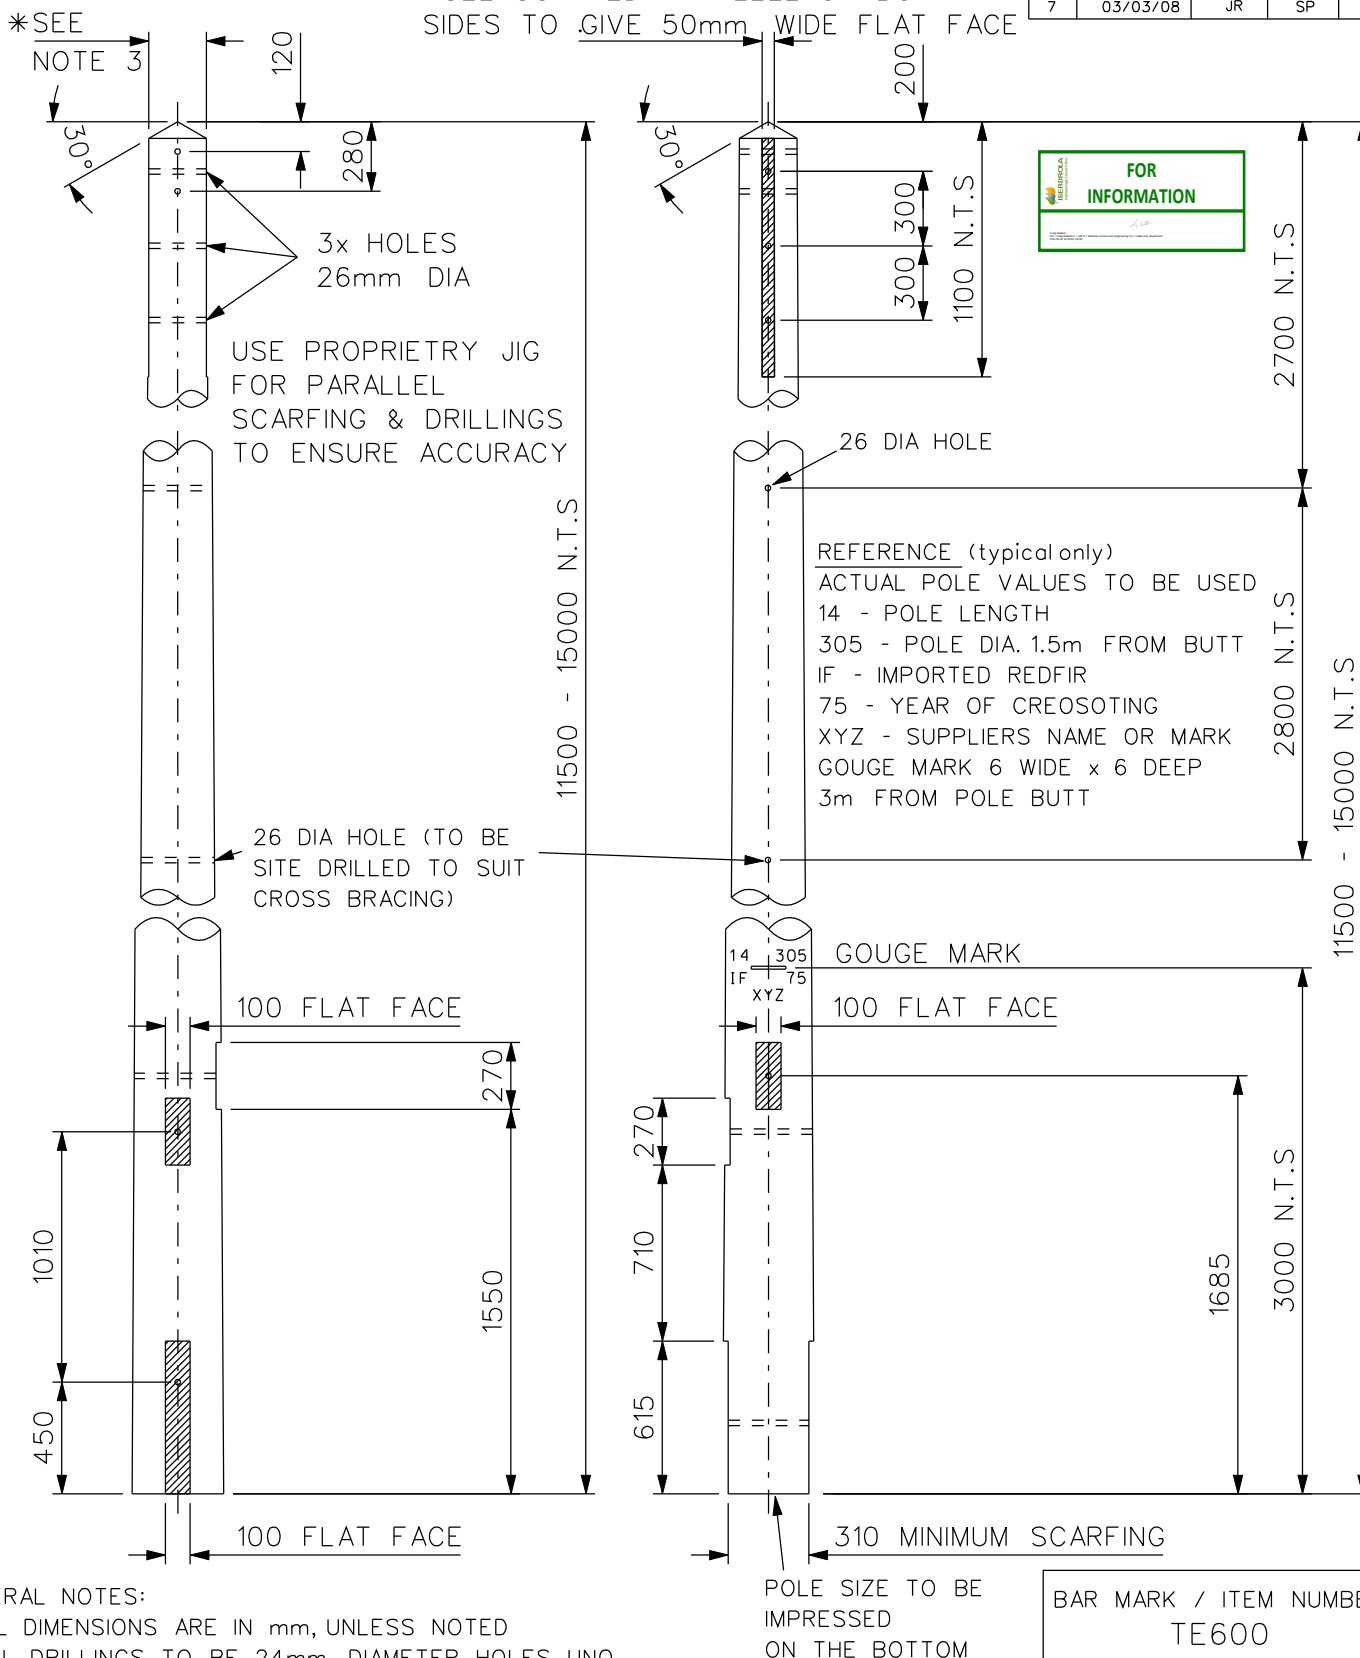

GENERAL NOTES:

1. ALL DIMENSIONS ARE IN mm, UNLESS NOTED
2. ALL DRILLINGS TO BE 24mm DIAMETER HOLES UNO.
3. POLE SIZES BASED ON BS1990, EXTRA STOUT POLES RANGE

LENGTH = 11.5m - 15m & PARALLEL WITHIN LIMITS

* MINIMUM TOP DIST BETWEEN FLATS = 200mm

* MAXIMUM TOP DIST BETWEEN FLATS = 265mm

MINIMUM DIAMETER 1.5m FROM BUTT = 305mm

SUPPLIER TO NOTE THESE DIMENSIONS ARE FOR GENERIC POLE DRILLING AND SCARFING ONLY TO SUIT A RANGE OF POLE SIZES, ACTUAL POLE MINIMUM DIMENSIONS TO BE SPECIFIED AT TIME OF ORDERING. ORDER VALUES WILL SUPERSEDE THESE STATED VALUES. MAXIMUM VALUE NOT TO BE EXCEEDED.

CLIENT	PowerSystems	TITLE	PART - WOOD POLE SCARFING DETAILS 'H' POLE INTERMEDIATE	SCALE 1:30 (UNLESS OTHERWISE STATED)	ORIGINAL SIZE A4	LS TRANSMISSION CONSULTANCY LIMITED Yorkshire House York Road Little Driffield East Yorkshire YO25 5XA 01377 253617
SPECIFICATION	OHL-03-132			DATE 17/01/05	CHECKED GS	
				DRAWN JN	APPROVED PP	
				DRAWING NUMBER LSTC/STD/PAR/600	REV 7	

