


H POLE
FOUNDATION TIMBER BAULK
300x150x3500
(net weight 135kg)

DESCRIPTION		FOR ISSUE			
REV	DATE	BY	MA	CHKD	APPD
2	19/07/07			SP	PP

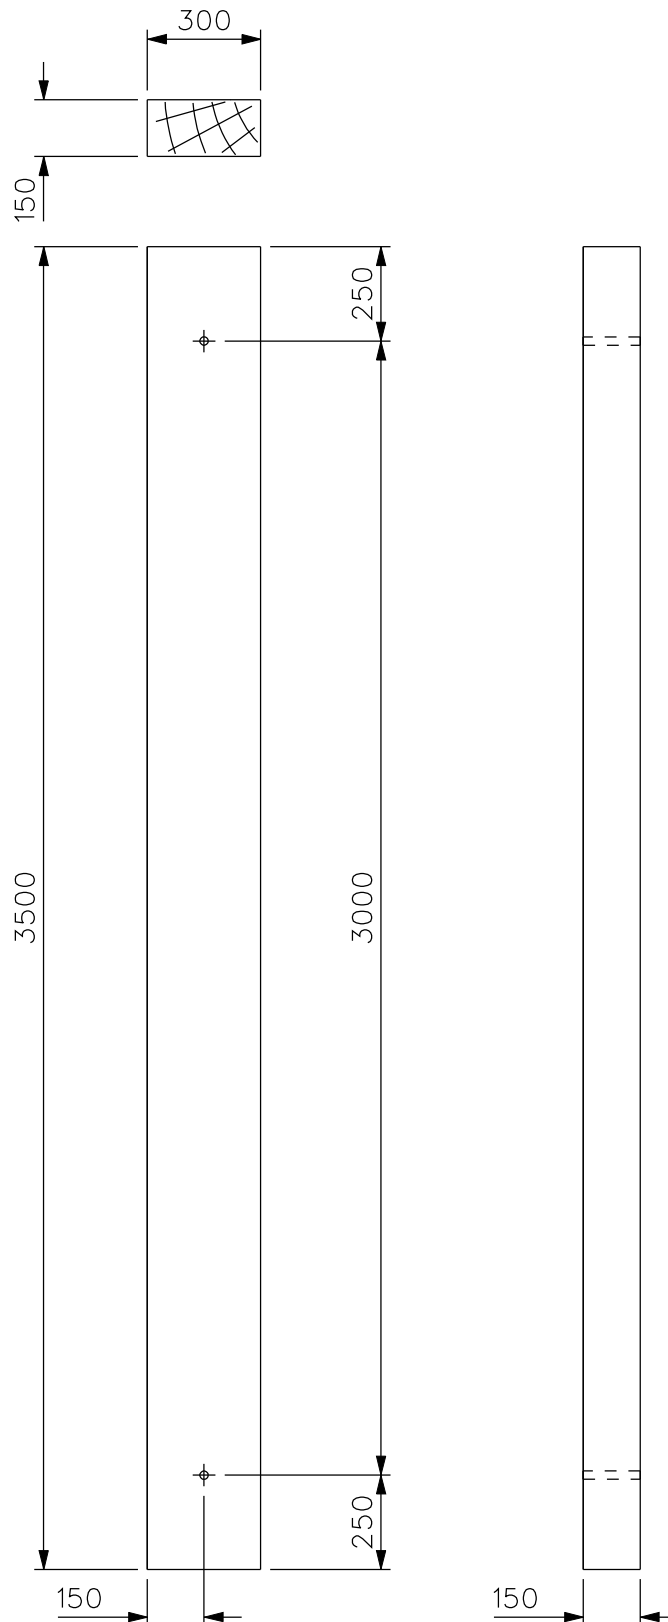

GENERAL NOTES:

1. ALL DIMENSIONS IN MILLIMETERS (mm)
2. ALL HOLES 22mm DIAMETER (unless noted)
3. MEMBER TO BE CLEARLY MARKED WITH PREFIX 'TE' AND ITEM NUMBER FOR SITE IDENTIFICATION



BAR MARK / ITEM NUMBER
TE601

CLIENT PowerSystems	TITLE PART - H POLE FOUNDATION TIMBER BAULK	SCALE 1 : 20 (UNLESS OTHERWISE STATED)		ORIGINAL SIZE A4		LS TRANSMISSION CONSULTANCY LIMITED Yorkshire House York Road Little Driffield East Yorkshire YO25 5XA 01377 253617 	
		DATE 23/11/04		CHECKED GS			
SPECIFICATION OHL-03-132		DRAWN JN		APPROVED PP			
		DRAWING NUMBER LSTC/STD/PAR/601		REV 2			

