


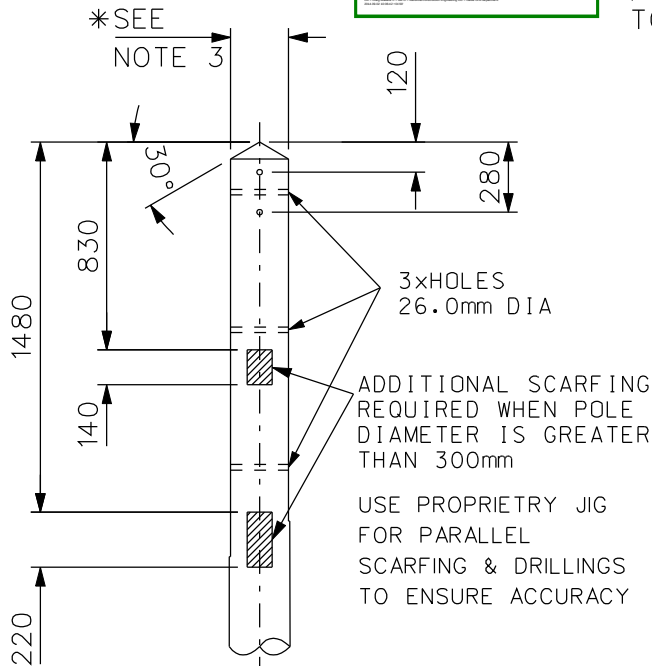


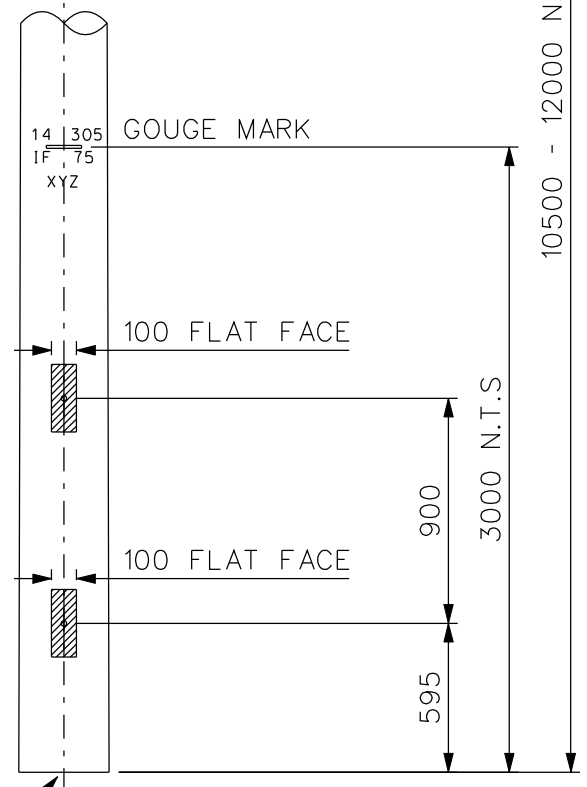

DESCRIPTION		FOR ISSUE				
REV	DATE	BY	RF	CHKD	SP	APPD
5	28/11/07					GS

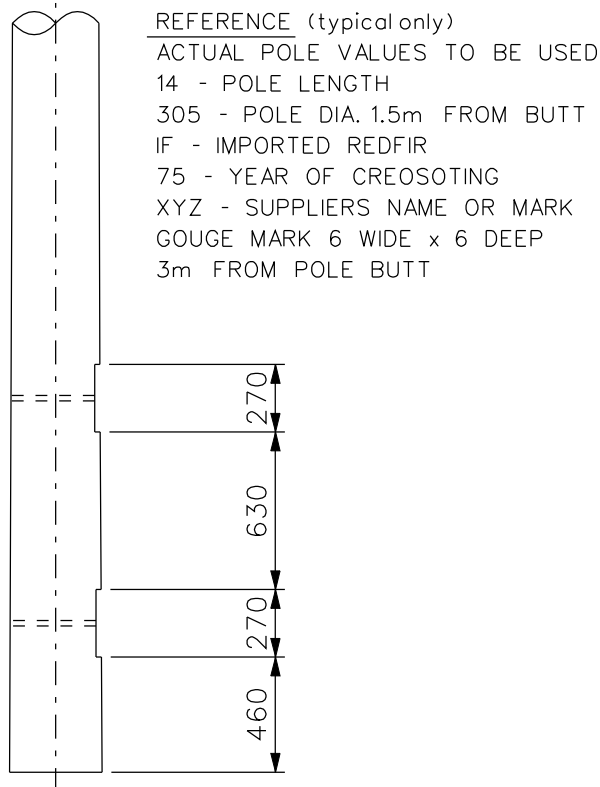

POLE SCARFED PARALLEL ON BOTH SIDES
TO GIVE 50mm WIDE FLAT FACE

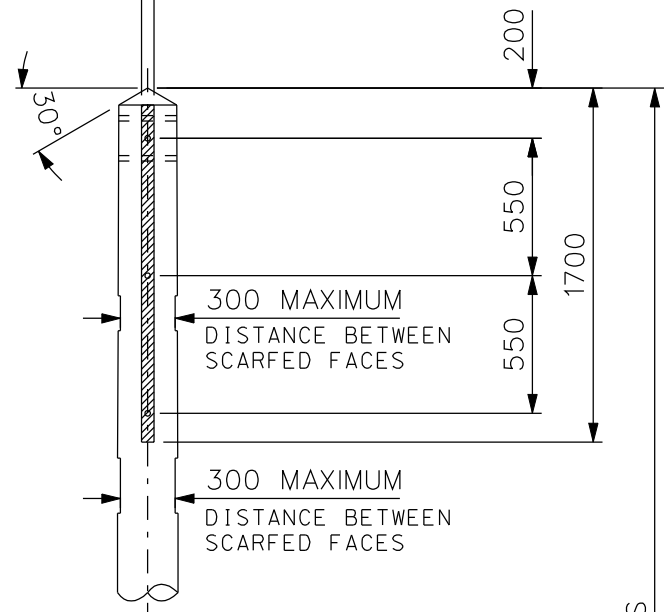

GENERAL NOTES:

- ALL DIMENSIONS ARE IN mm, UNLESS NOTED
- ALL DRILLINGS TO BE 24mm DIAMETER HOLES
- POLE SIZES BASED ON BS1990, EXTRA STOUT POLES RANGE

LENGTH = 10.5m - 12m & PARALLEL WITHIN LIMITS
MINIMUM TOP DIST BETWEEN FLATS = 280mm
*MAXIMUM TOP DIST BETWEEN FLATS = 345mm
*MINIMUM DIAMETER 1.5m FROM BUTT = 410mm

POLE SIZE TO BE
IMPRESSED
ON THE BOTTOM

BAR MARK / ITEM NUMBER
TE625

SUPPLIER TO NOTE THESE DIMENSIONS ARE FOR GENERIC
POLE DRILLING AND SCARFING ONLY TO SUIT A RANGE OF
POLE SIZES, ACTUAL POLE MINIMUM DIMENSIONS TO BE
SPECIFIED AT TIME OF ORDERING. ORDER VALUES WILL
SUPERSEDE THESE STATED VALUES. MAXIMUM VALUE NOT
TO BE EXCEEDED

CLIENT	TITLE	SCALE 1 : 30 (UNLESS OTHERWISE STATED)	ORIGINAL SIZE A4	LS TRANSMISSION CONSULTANCY LIMITED Yorkshire House York Road Little Driffield East Yorkshire YO25 5XA 01377 253617
PowerSystems		DATE 17/01/05	CHECKED GS	
SPECIFICATION		DRAWN JN	APPROVED PP	
		DRAWING NUMBER LSTC/STD/PAR/625		
OHL-03-132	PART - WOOD POLE SCARFING SINGLE POLE INTERMEDIATE			

