


USED ON LSTC/STD/GNA/502 & 514

POLE SCARFED PARALLEL ON BOTH SIDES
TO GIVE 50mm. WIDE FLAT FACE



DESCRIPTION		FOR ISSUE			
REV	DATE	BY	RF	CHKD	APPD
7	27/11/07			SP	GS

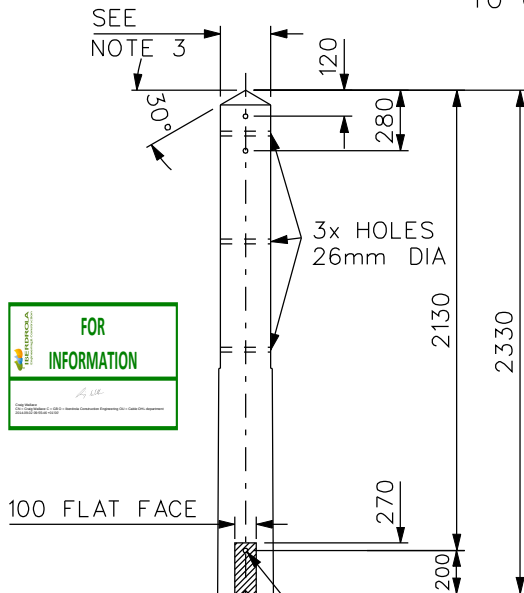

USE PROPRIETARY
JIG FOR PARALLEL
SCARFING &
DRILLINGS
TO ENSURE
ACCURACY

POLES SUPPLIED IN PAIRS
OPGW HOLES REQUIRED IN
1 POLE ONLY.

REFERENCE (typical only)
ACTUAL POLE VALUES TO BE USED
14 - POLE LENGTH
305 - POLE DIA. 1.5m FROM BUTT
IF - IMPORTED REDFIR
75 - YEAR OF CREOSOTING
XYZ - SUPPLIERS NAME OR MARK
GOUGE MARK 6 WIDE x 6 DEEP
3m FROM POLE BUTT

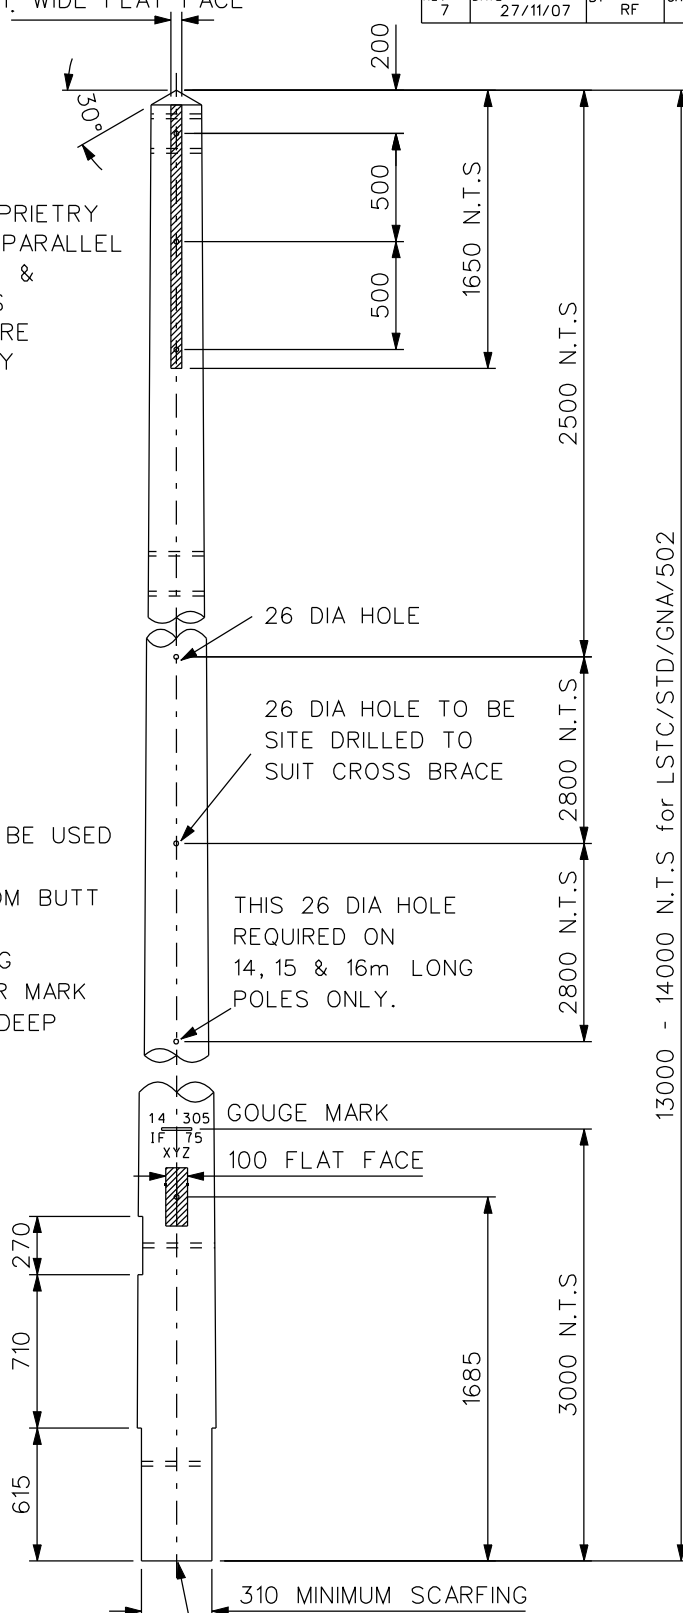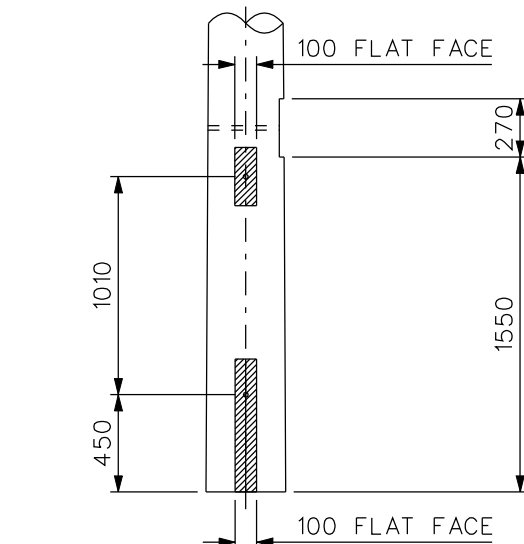

13000 - 14000 N.T.S for LSTC/STD/GNA/502
13000 - 16000 N.T.S for LSTC/STD/GNA/514

GENERAL NOTES:

1. ALL DIMENSIONS ARE IN mm, UNLESS NOTED
2. ALL DRILLINGS TO BE 24mm DIAMETER HOLES UNO.
3. POLE SIZES BASED ON BS1990, EXTRA STOUT POLES RANGE

LENGTH = 13m - 16m & PARALLEL WITHIN LIMITS.

*MINIMUM TOP DIST BETWEEN FLATS = 200mm

*MAXIMUM TOP DIST BETWEEN FLATS = 265mm

MINIMUM DIAMETER 1.5m FROM BUTT = 305mm

SUPPLIER TO NOTE THESE DIMENSIONS ARE FOR GENERIC
POLE DRILLING AND SCARFING ONLY TO SUIT A RANGE OF
POLE SIZES, ACTUAL POLE MINIMUM DIMENSIONS TO BE
SPECIFIED AT TIME OF ORDERING. ORDER VALUES WILL
SUPERSEDE THESE STATED VALUES. MAXIMUM VALUE NOT
TO BE EXCEEDED

BAR MARK / ITEM NUMBER
TE626

CLIENT	TITLE	SCALE 1 : 35 (UNLESS OTHERWISE STATED)	ORIGINAL SIZE A4	LS TRANSMISSION CONSULTANCY LIMITED Yorkshire House York Road Little Driffield East Yorkshire YO25 5XA 01377 253617
PowerSystems	PART - WOOD POLE SCARFING DETAILS	DATE 17/01/05	CHECKED GS	
SPECIFICATION		DRAWN JN	APPROVED PP	
OHL-03-132		DRAWING NUMBER LSTC/STD/PAR/626	REV 7	

