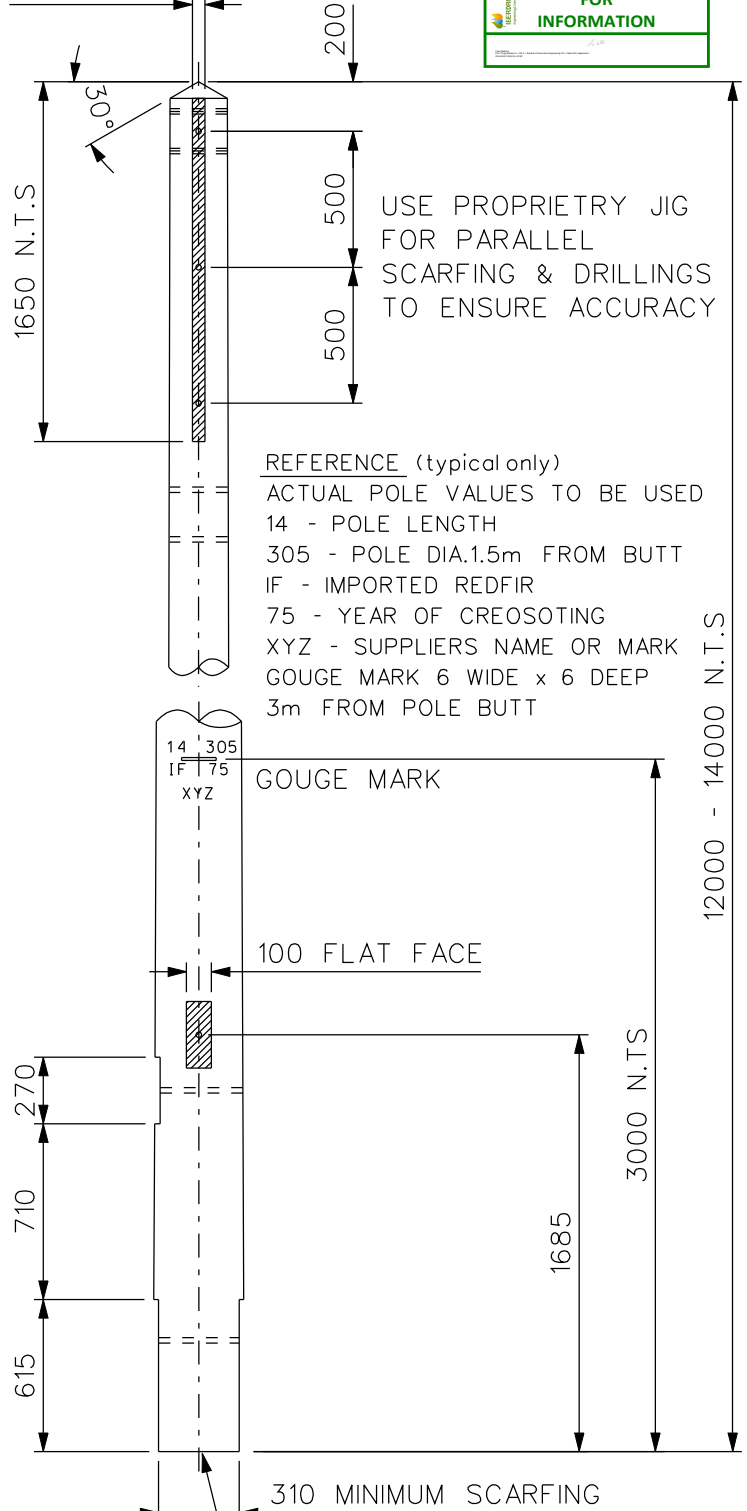
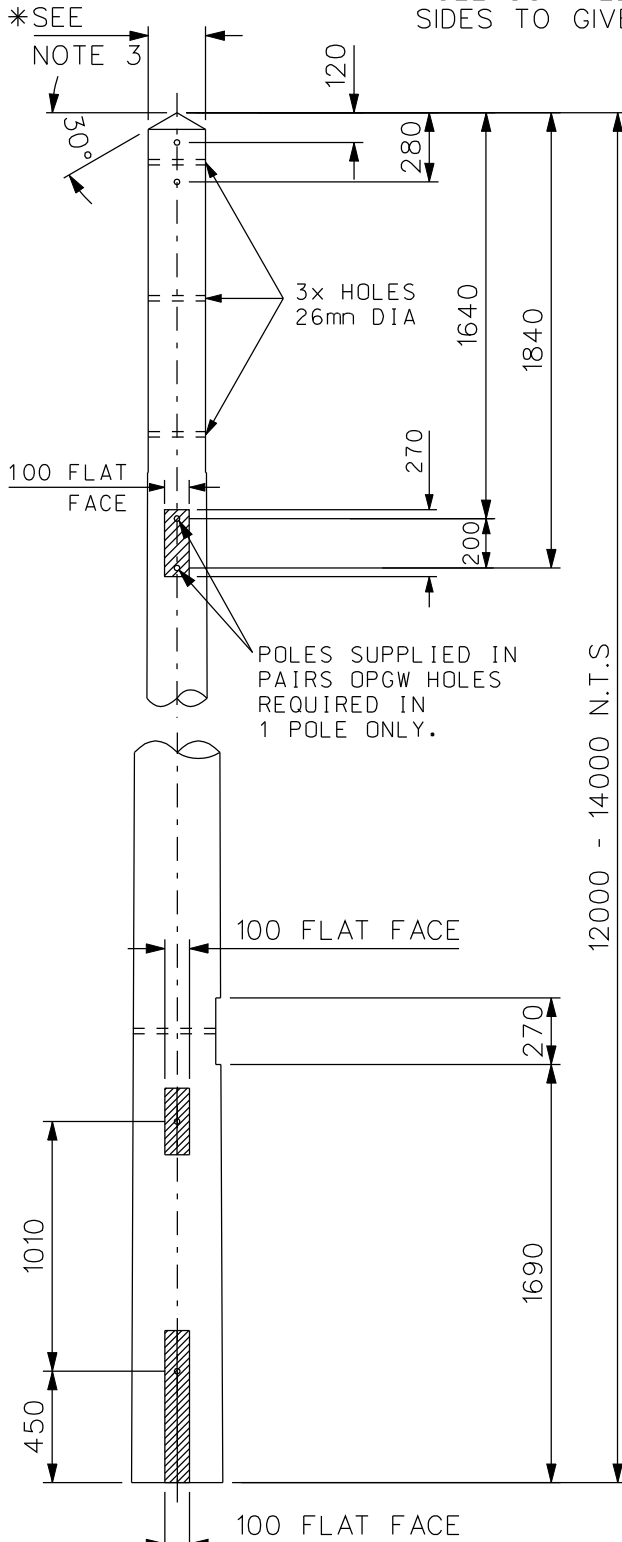


USED ON LSTC/STD/GNA/508

POLE SCARFED PARALLEL ON BOTH
SIDES TO GIVE 50mm WIDE FLAT FACE.

DESCRIPTION		FOR ISSUE			
REV	DATE	BY	RF	CHKD	APPD
6	27/11/07			SP	GS

FOR
INFORMATION

GENERAL NOTES:

1. ALL DIMENSIONS ARE IN mm, UNLESS NOTED
2. ALL DRILLINGS TO BE 24mm DIAMETER HOLES
3. POLE SIZES BASED ON BS1990, EXTRA STOUT POLES RANGE

LENGTH = 12m - 14m & PARALLEL WITHIN LIMITS.

* MINIMUM TOP DIST BETWEEN FLATS = 200mm

* MAXIMUM TOP DIST BETWEEN FLATS = 265mm

MINIMUM DIAMETER 1.5m FROM BUTT = 305mm

SUPPLIER TO NOTE THESE DIMENSIONS ARE FOR GENERIC POLE DRILLING AND SCARFING ONLY TO SUIT A RANGE OF POLE SIZES, ACTUAL POLE MINIMUM DIMENSIONS TO BE SPECIFIED AT TIME OF ORDERING. ORDER VALUES WILL SUPERSEDE THESE STATED VALUES. MAXIMUM VALUE NOT TO BE EXCEEDED.

CLIENT
PowerSystemsSPECIFICATION
OHL-03-132

TITLE
PART -
WOOD POLE
SCARFING DETAILS
20-35° ANGLE
STRUCTURES

SCALE 1 : 30
(UNLESS OTHERWISE STATED)

DATE 17/01/05

DRAWN JN

DRAWING NUMBER
LSTC/STD/PAR/667

ORIGINAL SIZE A4

CHECKED GS

APPROVED PP

REV 6

LS TRANSMISSION CONSULTANCY LIMITED
Yorkshire House
York Road
Little Driffield
East Yorkshire
YO25 5XA
01377 253617

