




FOR

INFORMATION

Craig Wallace
CN = Craig Wallace C = G8 O =
Bentley Construction Engineering
OU = Cable OHL department
2024.09.02 09:59:55 +0100

DESCRIPTION		FOR ISSUE			
REV	DATE	BY	CHKD	SP	APPD
6	22/11/07	RF		SP	GS

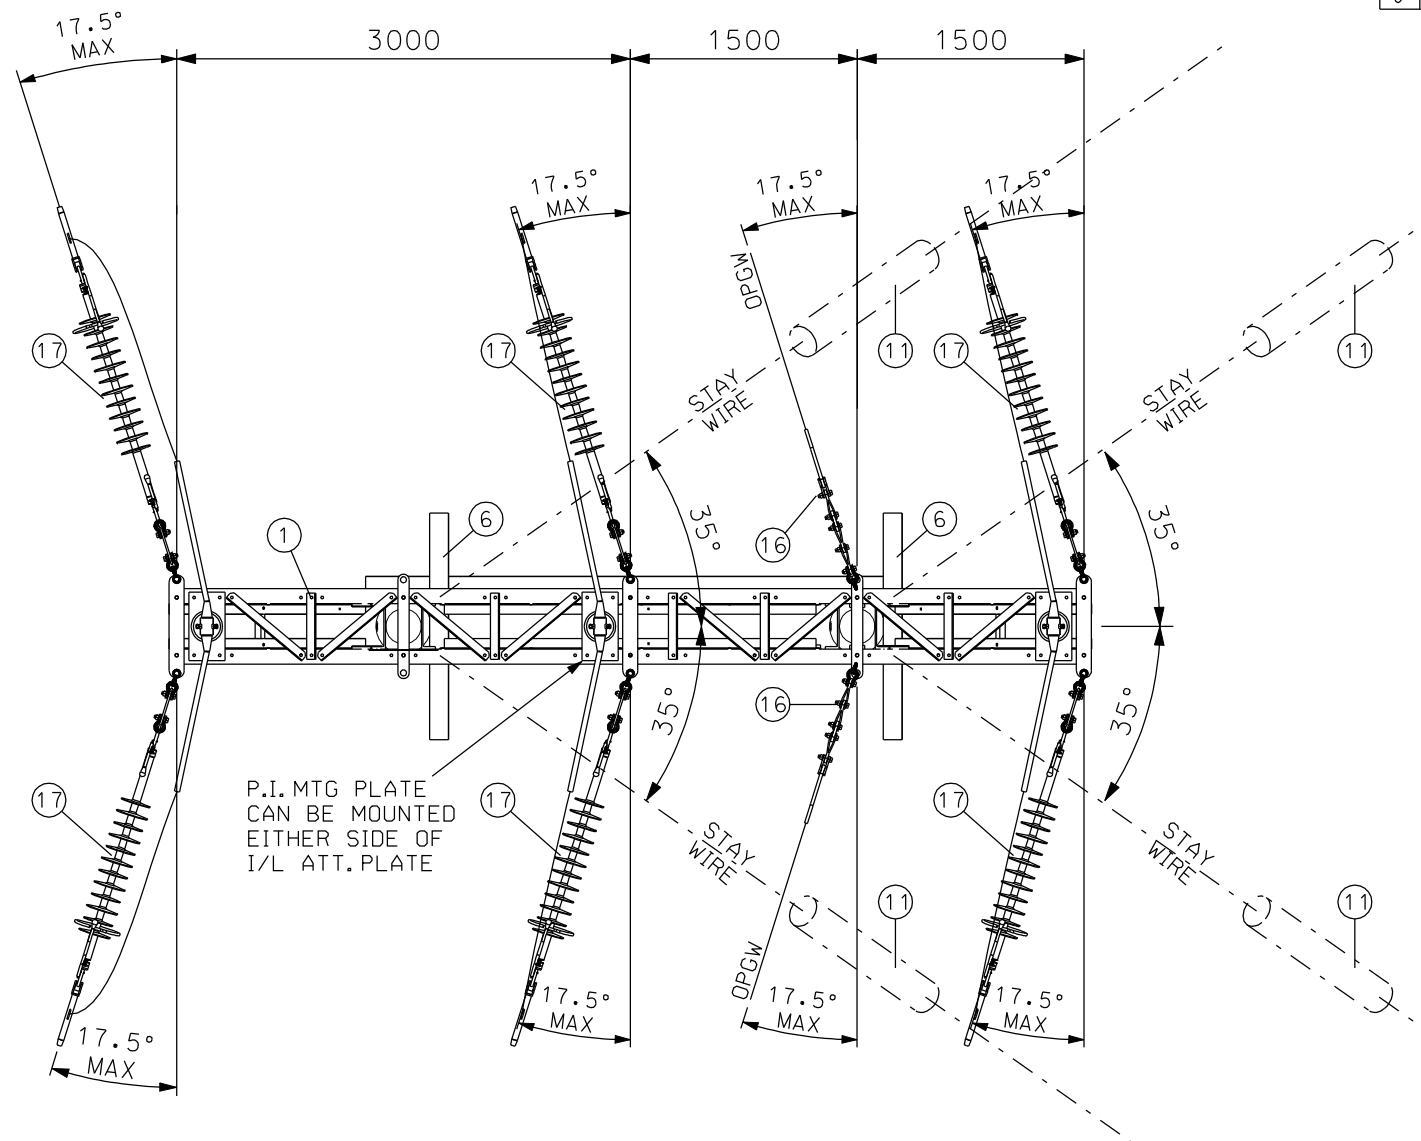

GENERAL NOTES:

- ALL STEELWORK TO BE CHECK ERECTED BEFORE MASS PRODUCTION.
- SAFETY SIGNS TO BE INSTALLED TO CONFORM TO POWER SYSTEMS PROCEDURES

- FOR FRONT ELEVATION SEE LSTC/STD/GNA/508
- FOR MATERIAL LIST SEE LSTC/STD/GNA/510

- FOR STAY WIRE SETTING OUT DETAILS SEE LSTC/STD/GNA/782.
- FOR MAINTENANCE ATTACHMENT LOCATIONS SEE LSTC/STD/GNA/551.

GENERAL NOTES:	CLIENT	TITLE	SCALE	1:50	ORIGINAL SIZE	A4	LS TRANSMISSION CONSULTANCY LIMITED Yorkshire House York Road Little Driffield East Yorkshire YO25 5XA 01377 253617
	PowerSystems		(UNLESS OTHERWISE STATED)				
			DATE	28/10/04	CHECKED	GS	
			DRAWN	R.T.J	APPROVED	PP	
			DRAWING NUMBER		REV		
			LSTC/STD/GNA/509		6		
SPECIFICATION	OHL -03-132	GA - PLAN VIEW 20-35° ANGLE STRUCTURE					