
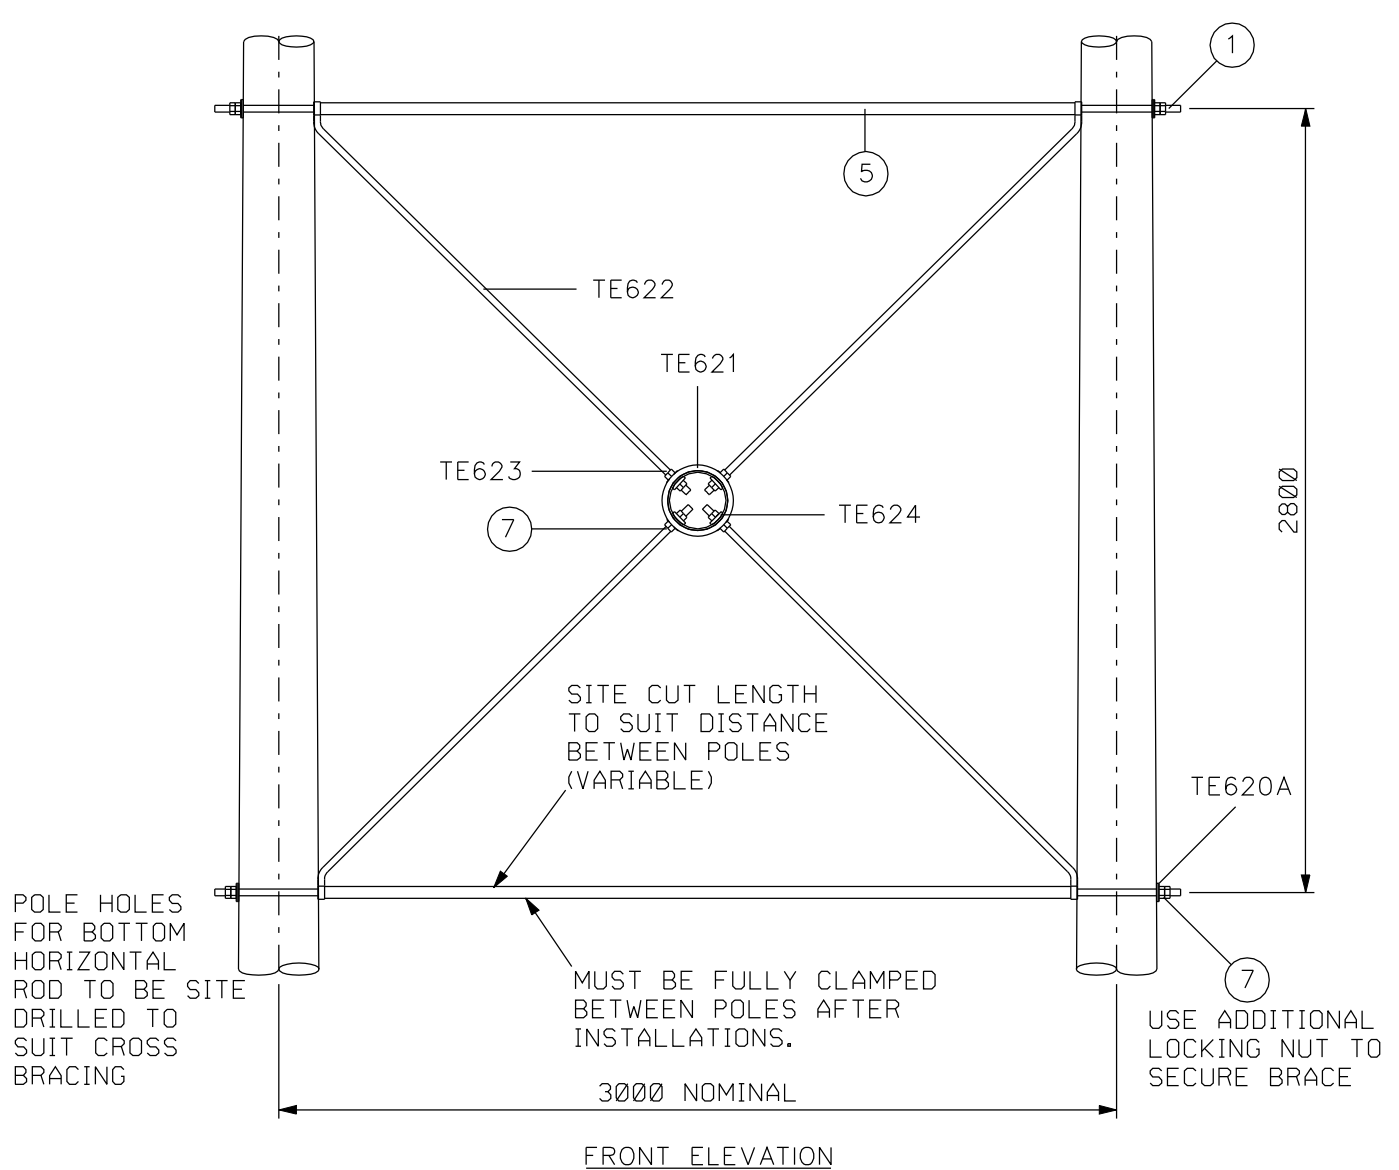


DESCRIPTION		FOR ISSUE			
REV	DATE	BY	CHKD	APPD	
3	03/08/07	JR	GS	PP	

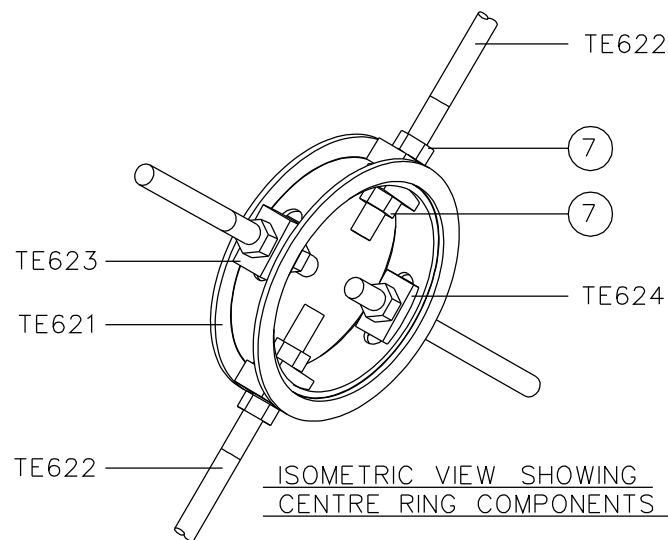

GENERAL NOTES:
 1. ALL STEELWORK TO BE PROTOTYPE CHECK
 ERECTED BEFORE MASS PRODUCTION.
 2. FOR MATERIAL LIST SEE LSTC/STD/GNA/557

CLIENT PowerSystems	TITLE PART - WOOD POLE BRACE ASSEMBLY SINGLE	SCALE 1:25 (UNLESS OTHERWISE STATED)	ORIGINAL SIZE A4	LS TRANSMISSION CONSULTANCY LIMITED Yorkshire House York Road Little Driffield East Yorkshire YO25 5XA 01377 253617
		DATE 01/12/04	CHECKED GS	
DRAWN R.T.J		APPROVED PP		
DRAWING NUMBER LSTC/STD/GNA/556		REV 3		
SPECIFICATION OHL-03-132				