


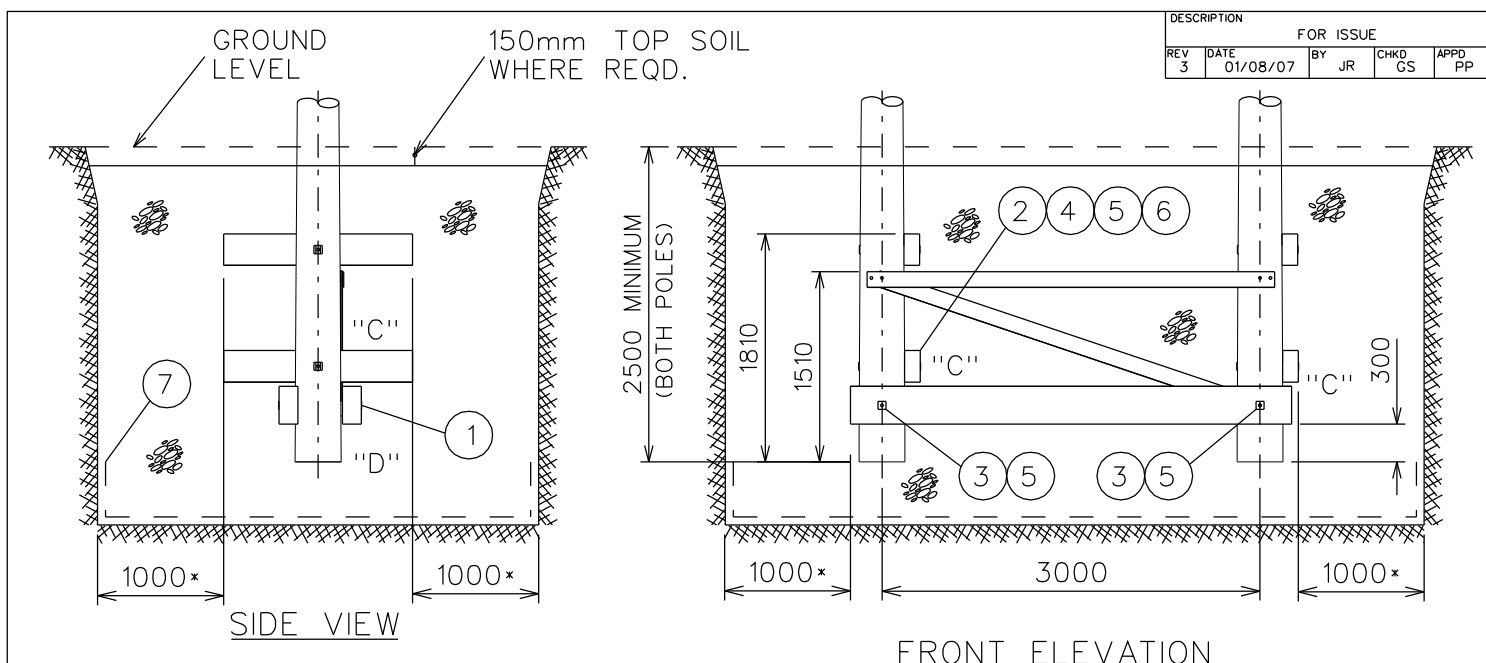

* MINIMUM DISTANCE BETWEEN FACE OF EXCAVATION & STRUCTURE TO ALLOW ACCESS TO PLACE GRANULAR FILL & COMPACT

	ITEM - DESCRIPTION	REFERENCE No.	QTY REQ'D	WEIGHT EACH (Kg)	REMARKS
1	"H" Pole Timber Baulk	LSTC/STD/PAR/601	1	135	Timber Baulk "D" in addition to LSTC/STD/GNA/508
2	Foundation Block	LSTC/STD/PAR/602	2	42	Foundation Block "C" in addition to LSTC/STD/GNA/508
3	M20 Bolts x Length To Suit Pole Diameter	LSTC/STD/GNA/555	2	0.5	M20 Bolts to attach additional Timber Baulk "D" to Foundation
4	M20 Bolts x Length To Suit Pole Diameter	LSTC/STD/GNA/555	2	1.5	M20 Bolts to attach additional Foundation Block "C"
5	Square Flat Washer	LSTC/STD/PAR/619	4	0.1	Flat Washers in addition to LSTC/STD/GNA/508
6	Square Curved Washer	LSTC/STD/PAR/620	2	0.2	Curved Washers in addition to LSTC/STD/GNA/508
7	Geotextile Membrane	--	1	--	Place in Bottom of Excavation Prior to Granular Backfill
8					

Total Additional Calculated Weight = 225Kg

GENERAL NOTES:

- ALL STEELWORK TO BE PROTOTYPE CHECK ERECTED PRIOR TO MASS PRODUCTION.
- ALL DIMENSIONS ARE IN MILLIMETRES.
- MATERIAL LIST INDICATES ADDITIONAL ITEMS REQUIRED WHEN "VERY POOR" SOIL CONDITIONS ARE ENCOUNTERED.
THESE FOUNDATIONS CAN ONLY BE INSTALLED IN LEVEL GROUND.
TO BE READ IN CONJUNCTION WITH:
LSTC/STD/GNA/508: 20-35° ANGLE STRUCTURE
LSTC/STD/GNA/510: MATERIAL LIST
LSTC/STD/GNA/555: BOLT LENGTH DETERMINATION
- IMPORTANT:** REFER TO LSTC/STD/GNA/779 SHEETS 1 TO 4 FOR FOUNDATION DESIGN CRITERIA.

SHT 1 : SOIL CLASSIFICATIONS & POLE EMBEDMENT DETAILS.
SHT 2 : FOUNDATION DETAILS / STRUCTURE TYPES.
SHT 3 : FACTORS OF SAFETY.
SHT 4 : OUTLINE DESIGN FOR "VERY POOR" SOIL FOUNDATIONS.



CLIENT PowerSystems	TITLE ADDITIONAL MATERIAL 20-35° ANGLE STRUCTURE VERY POOR SOIL CONDITIONS	SCALE 1:60 (UNLESS OTHERWISE STATED)	ORIGINAL SIZE A4	LS TRANSMISSION CONSULTANCY LIMITED Yorkshire House York Road Little Driffield East Yorkshire YO25 5XA 01377 253617
		DATE 11/05/05	CHECKED GS	
DRAWN R.F.		APPROVED PP		
DRAWING NUMBER LSTC/STD/GNA/797		REV 3		
SPECIFICATION OHL-03-132				