


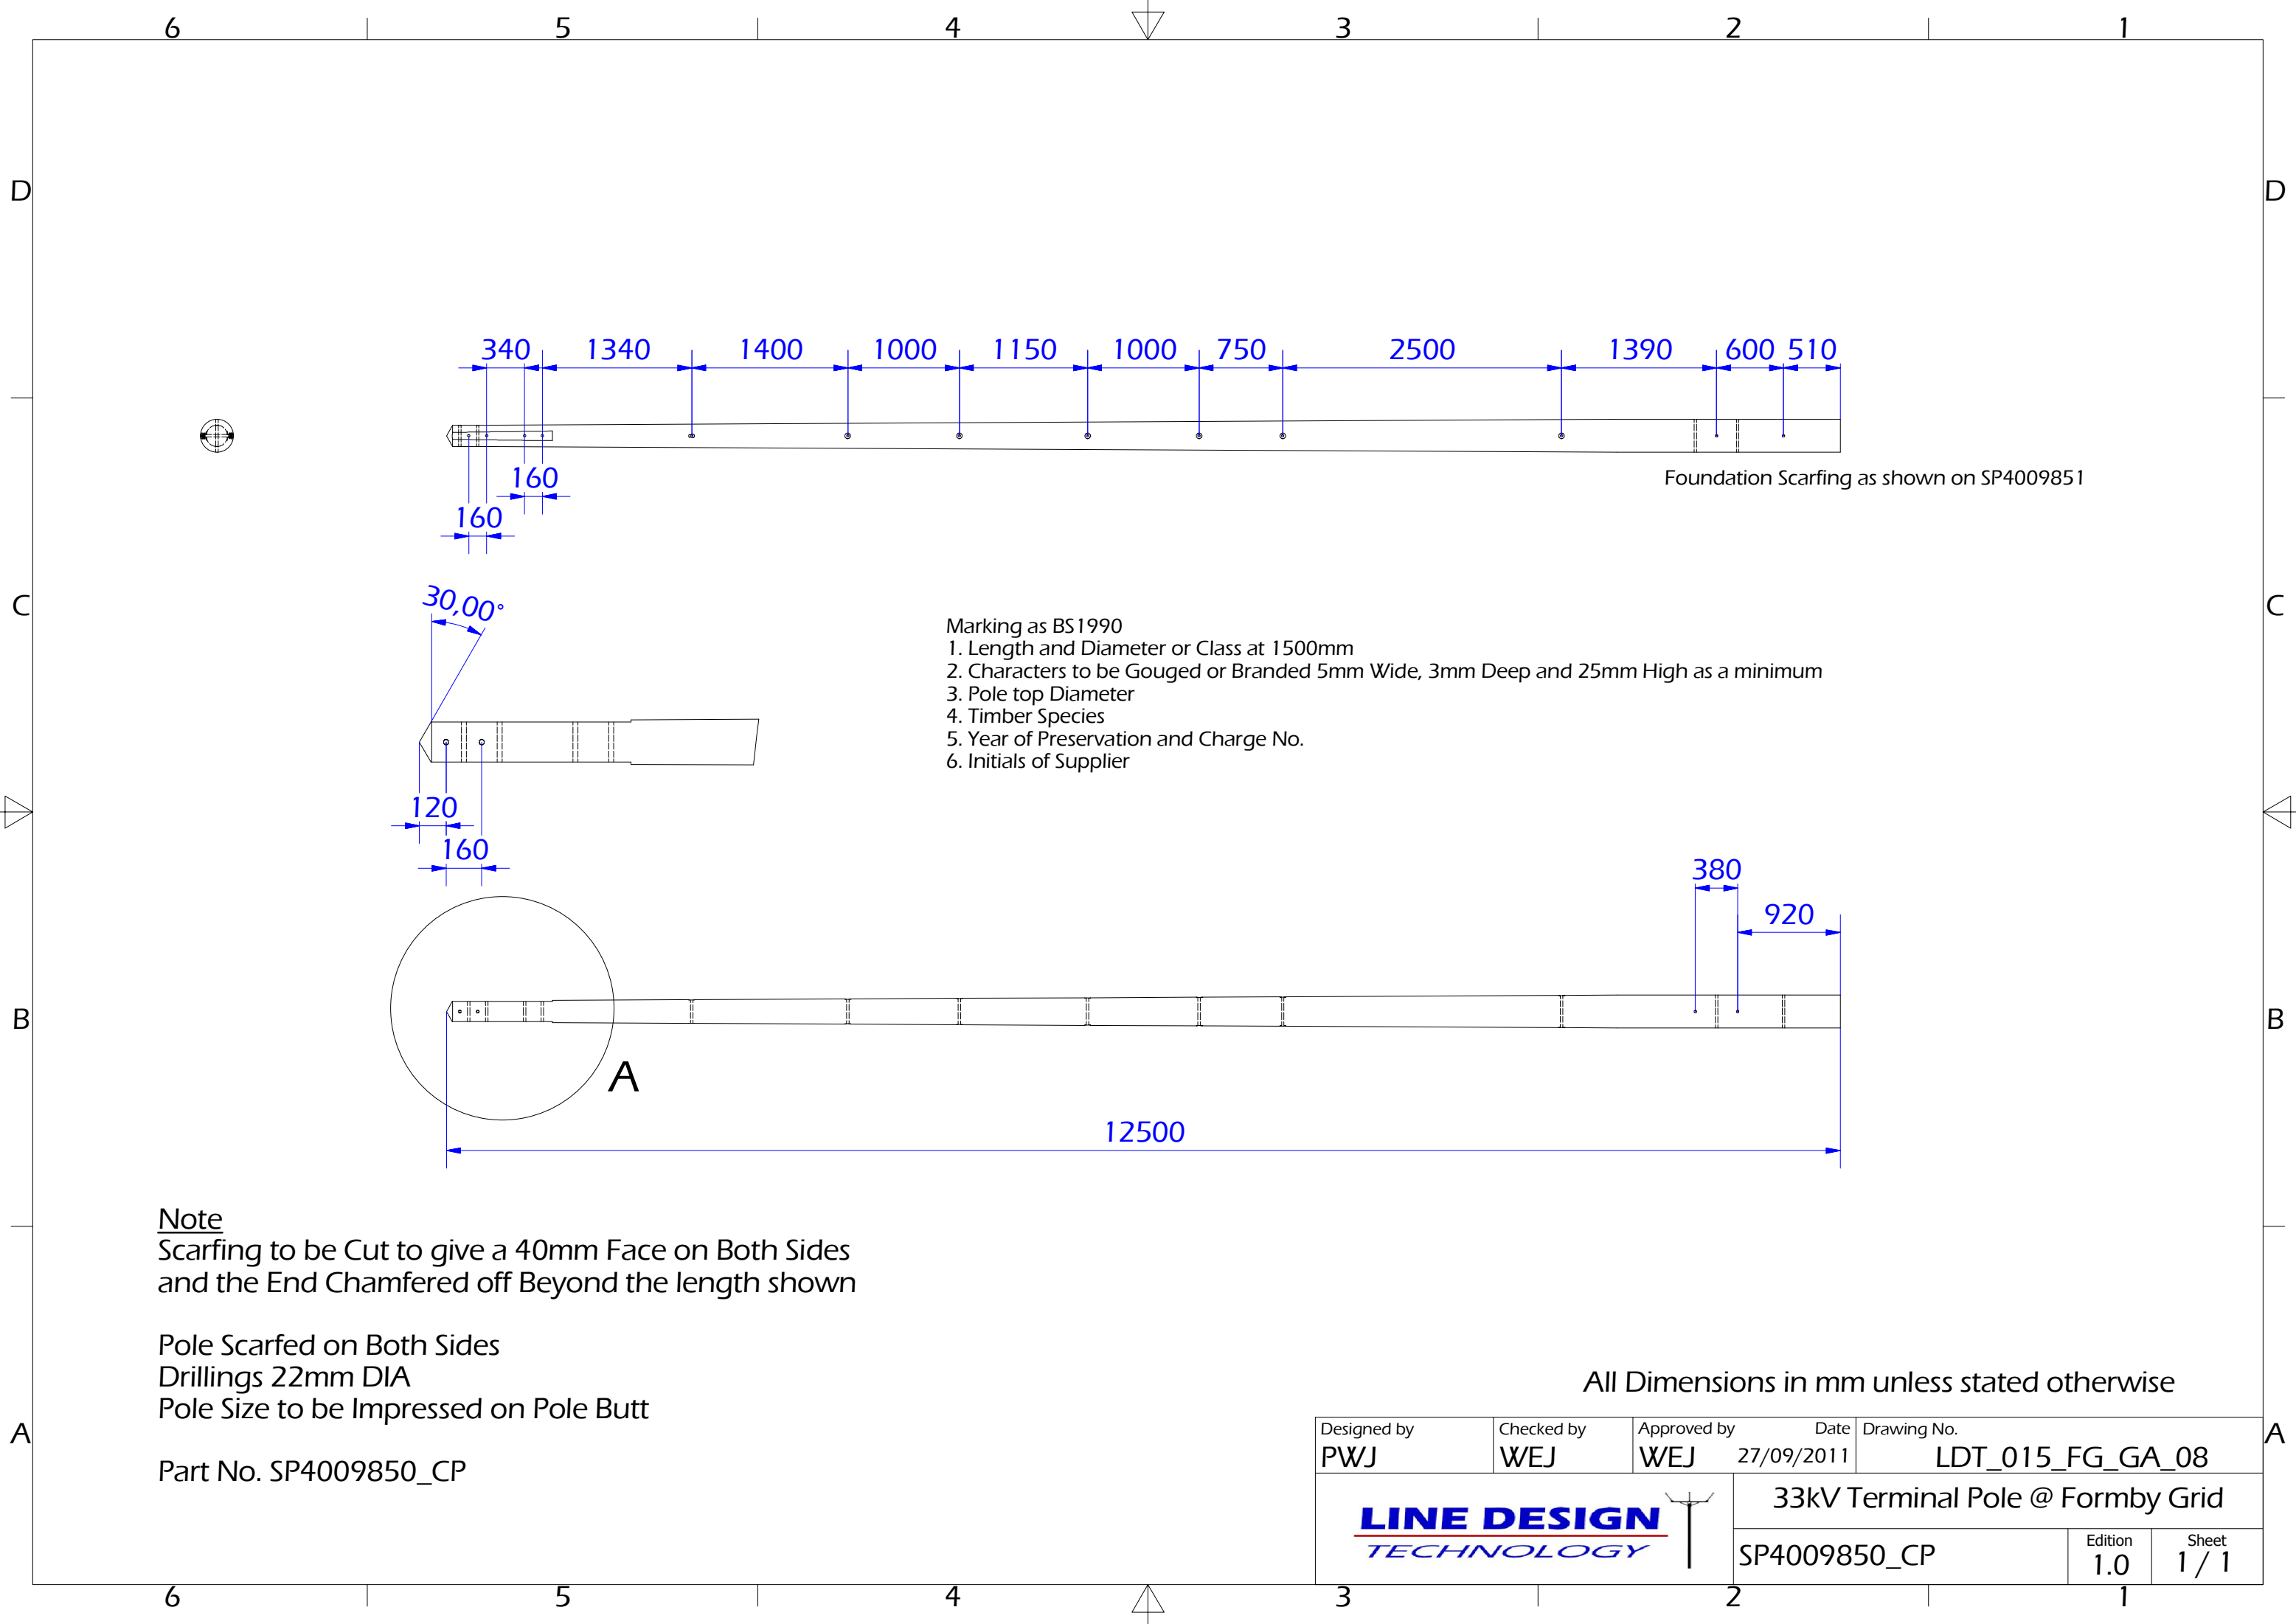

Designed by PWJ	Checked by WEJ	Approved by WEJ	Date 27/09/2011	Drawing No. LDT_015_FG_GA_08
LINE DESIGN TECHNOLOGY				33kV Terminal Pole @ Formby Grid
SP4009850_CP				Edition 1.0
				Sheet 1 / 1