



STOCK NO.: 334240
334241

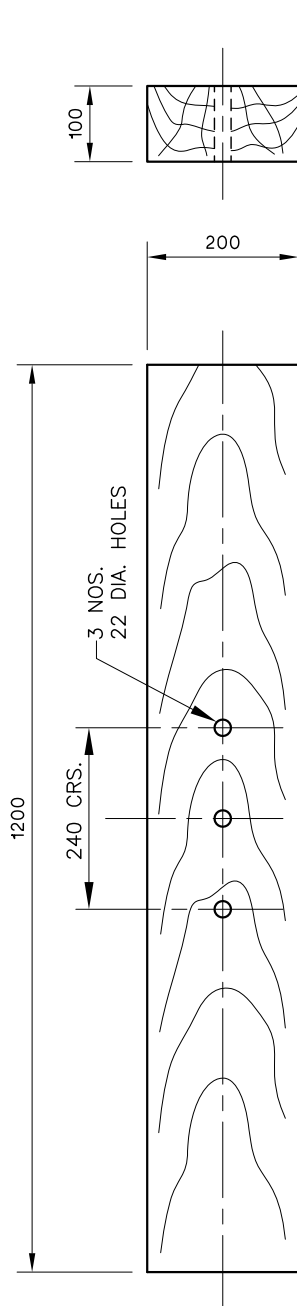

LV & 11kV POLE FOUNDATION & STAY FOUNDATION BAULK
(CLP STOCK NO. 334-240)

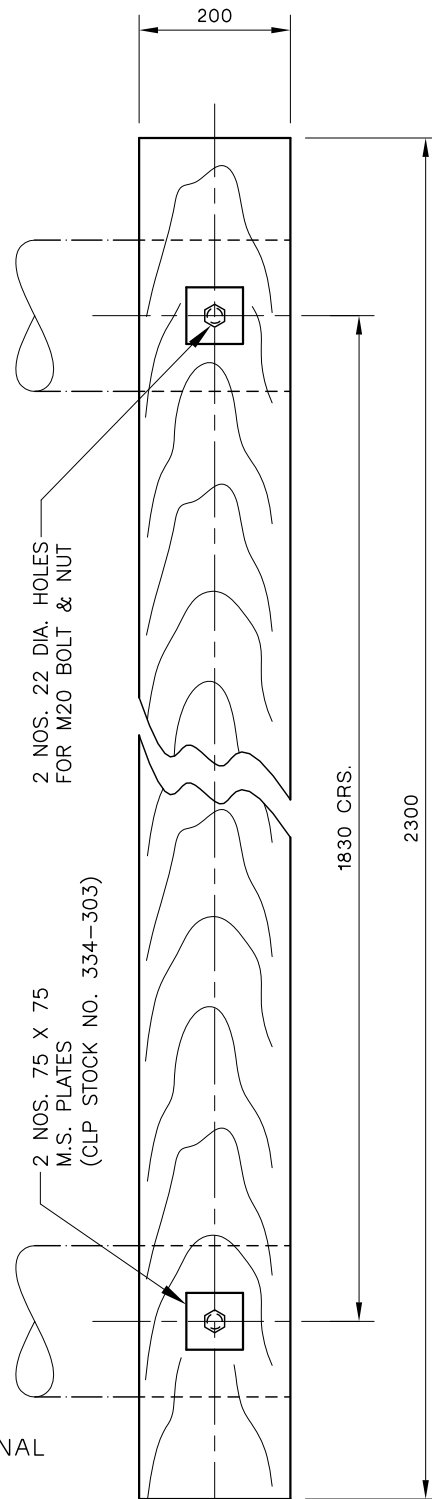

11kV TRANSFORMER 'H' POLE FOUNDATION BAULK
(CLP STOCK NO. 334-241)

NOTES:

1. FRENCH MARITIME PINE OR EQUIVALENT.
2. PRESERVATIVE TREATED W.R.T. INTERNATIONAL STANDARD.
3. THIS DRAWING SUPERSEDES DRG. NO. ESC/G/96-73
4. ALL DIMENSIONS ARE IN mm.

B NOTES ADDED



REVS.	28-1-03	03.07.18												
INITIAL	A	B	C	D	E	F	G	H	J	K	L			
	H.C.C	CHRIS C												

TITLE :

WOOD BAULK FOR POLE FOUNDATION
AND FOR STAY ANCHORS

DRAWN: S.C.TO DATE: 17-3-99
CHECKED: Y.N.S APPROVED: K. S. YEUNG
SCALE: N.T.S. SHEET(S) IN SET: 1

PROJECT NO.

CONTRACT NO.

ASSET MANAGEMENT

DRG. NO. T G E N 5 1 2 0 D E 3 3 0 0 2 6 0 1 B S