


CLP STOCK NO.: 334-246

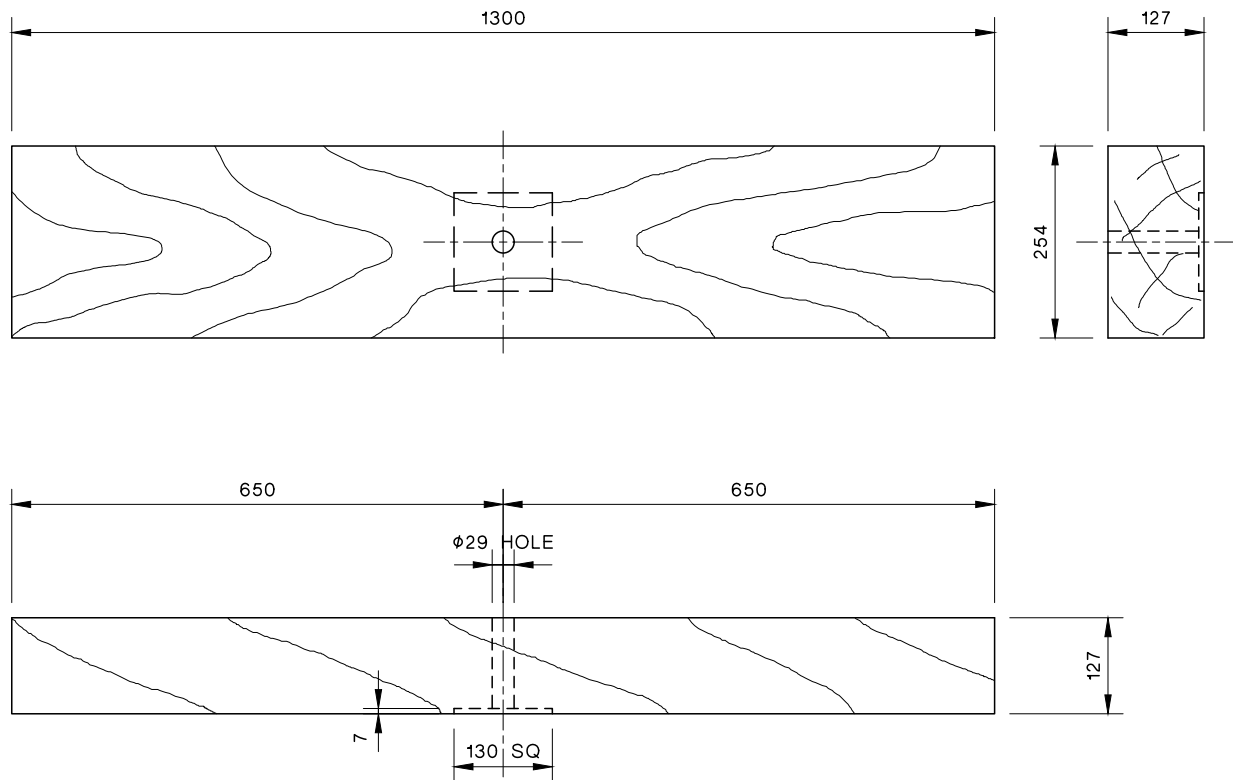

ALL CUTTINGS & DRILLINGS MUST BE COMPLETED BEFORE TANALISING

MATERIAL : FRENCH MARITIME PINE CCA TREATED TO B.S.4072
AVERAGE NET DRY SALT RETENTION
NOT LESS THAN 16kg./m³



REVS.	28.01.03												
INITIAL	A	B	C	D	E	F	G	H	J	K	L		
	H.C.C												

TITLE :

WOOD BAULK FOR STAY ROD ANCHOR

DRAWN: K.K.HO	DATE: 01-09-2000
CHECKED: F.C./Y.N.S.	APPROVED: K. S. YEUNG
SCALE: 1 : 10	SHEET(S) IN SET: 1

PROJECT NO.

CONTRACT NO.

ASSET MANAGEMENT

DRG. NO.	T	S	D	D	5	1	5	1	0	D	E	3	3	0	0	0	1	0	1	A	A
----------	---	---	---	---	---	---	---	---	---	---	---	---	---	---	---	---	---	---	---	---	---