


DRAWING ISSUE SHEET

[illegible]

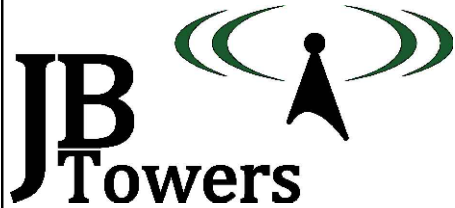

02	NOTES UPDATED			AM	08/05/18
01	FIRST ISSUE			AM	01/05/18
REV	REV			BY	DATE
SCALE AS SHOWN WHEN PRINTED AT A3		DRAWN	AM	CHECKED	MP
		DATE	01/05/18	DATE	01/05/18
APPROVED					
JBT					
DATE 01/05/18					
ALL DIMENSIONS IN mm UNLESS OTHERWISE STATED. THIS DRAWING TO BE READ IN CONJUNCTION WITH OTHER RELEVANT DRAWINGS.					


TITLE
EAST DEAN
GENERAL ARRANGEMENT
SHEET 1 OF 3

SITE ADDRESS
EAST DEAN
EAST SUSSEX
BN20 0JZ

ARQIVA REF.
140649

DRG No.
200

REV
02

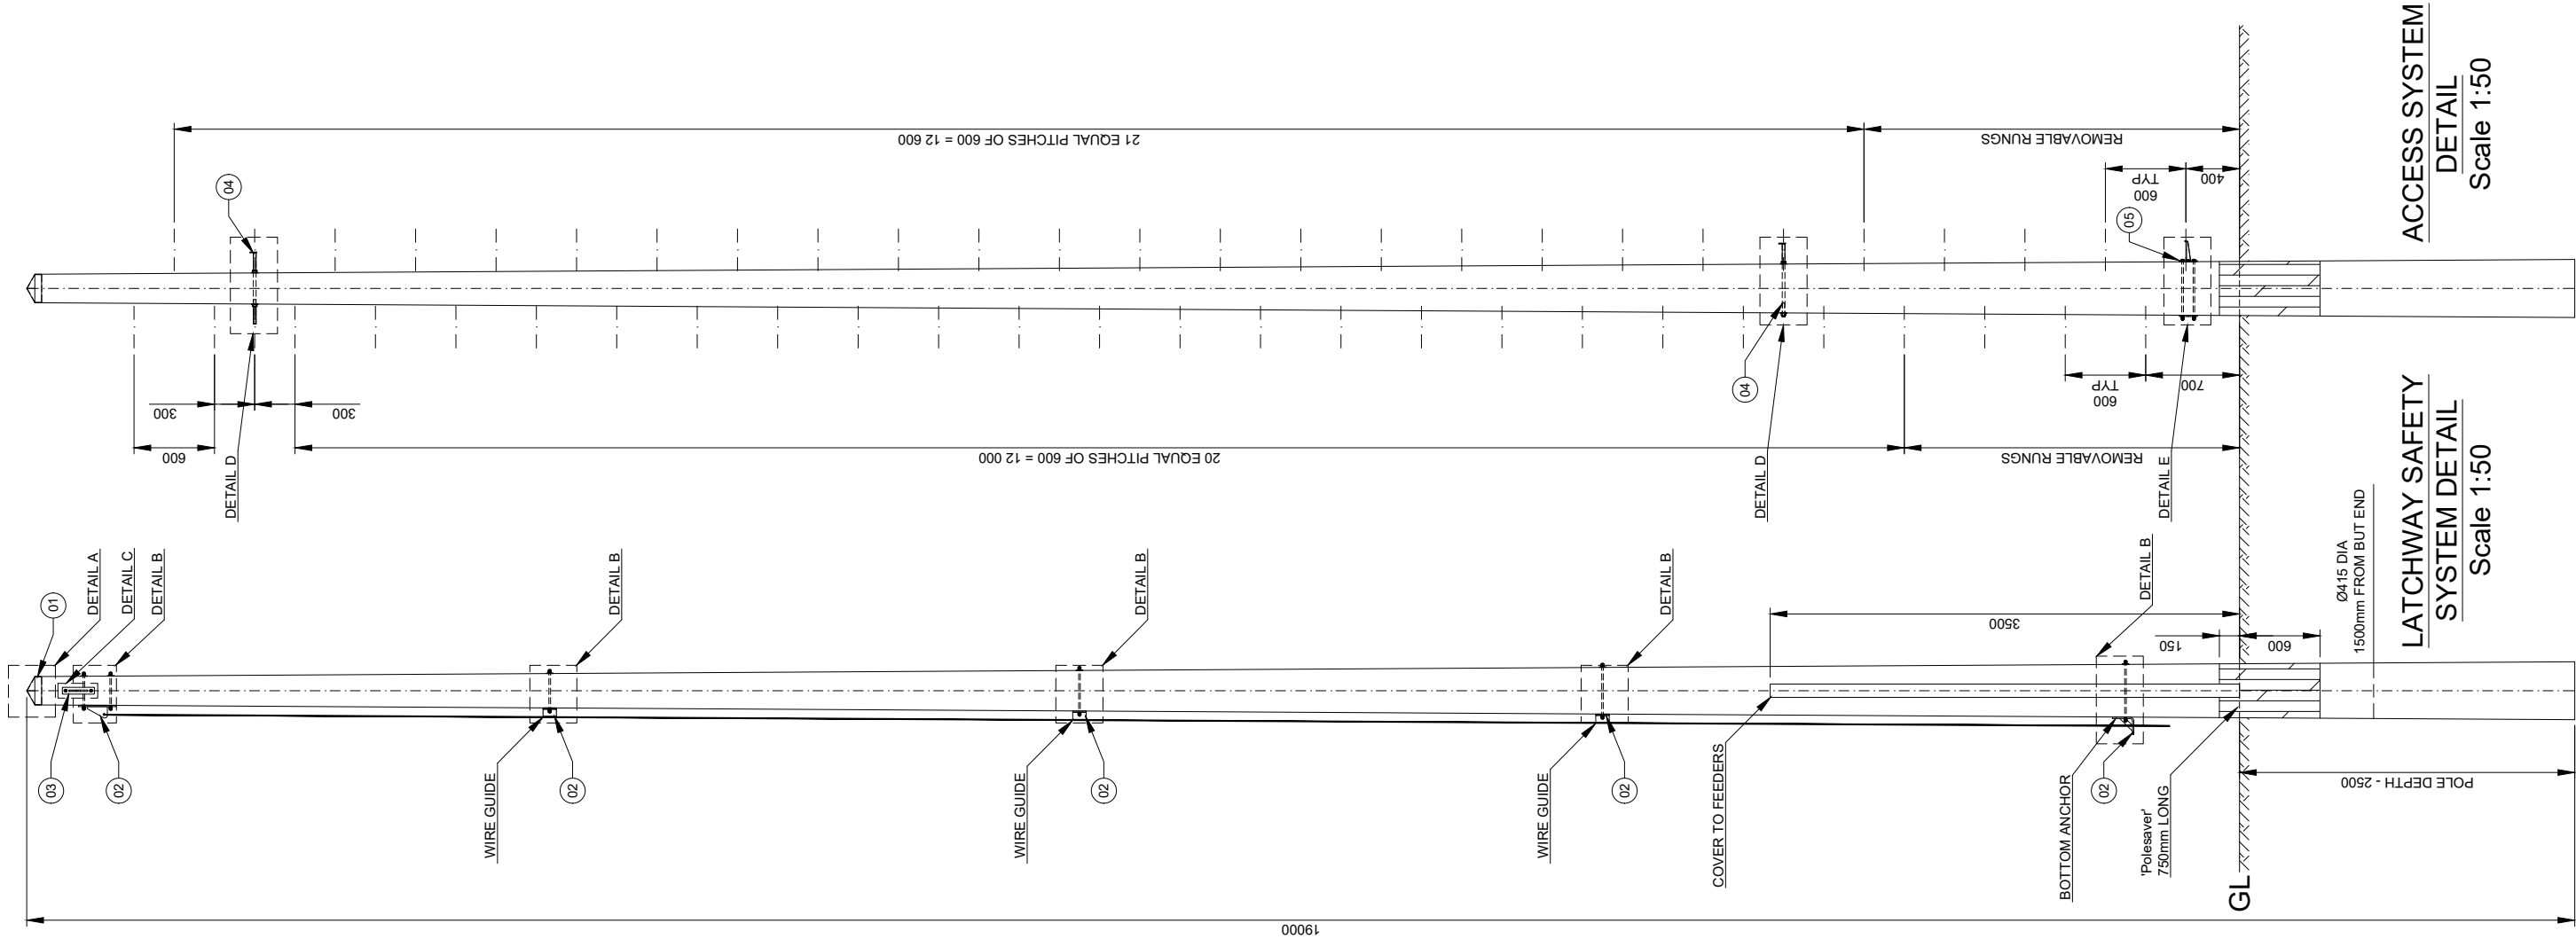

NOTES

- SEE DRAWING 305 FOR PARTS LIST
- ALL BOLTS TO BE CUT ON SITE TO EXTEND MAX 10mm BEYOND THE NUT WHEN TIGHTENED UNO.
- ALL SITE DRILLED HOLE/CUT ENDS TO BE TREATED WITH METAFUX 70-40 ZINC PASTE FOLLOWED BY 1 COAT OF 7-42 ZINC ALU OR 70-16 ALUMINIUM SPRAY

TIMBER POLE

- POLE TO BE SUPPLIED IN ACCORDANCE WITH BS EN14229 & SHALL HAVE MIN. CHARACTERISTIC BENDING STRENGTH OF 30N/mm² & MIN. YOUNGS MODULUS (PARALLEL TO GRAIN) OF 10KN/mm².
- MARKINGS ON FINISHED POLE SHALL BE AT 4m FROM BUT AND COMPLY WITH BS EN 14229 UNO
- AS FAR AS PRACTICABLE ALL CUTTING, SCARFING & DRILLING TO BE DONE BEFORE CREOSOTING. IF NOT ALL CUT, DRILLED & SCARFED SURFACES TO BE COATED WITH A MIXTURE OF CREOSOTE & TAR.
- POLE TO BE PRESSURE IMPREGNATED WITH CREOSOTE IN ACCORDANCE WITH BS EN 14229
- MINIMUM DIAMETERS
TOP - Ø210mm
BOTTOM - Ø425mm
- 19m LONG POLE TO BE SOURCED BY TRIMMING 20m LONG POLE BY 1m AT THE TOP

PLANTING




- CAT SCANNER IS TO BE USED IN ORDER TO CONFIRM THE POSITIONS OF BURIED SERVICES.
- 'Perma-Soil Stabiliser' OR A SIMILAR APPROVED SHOULD BE USED IN ACCORDANCE WITH THE MANUFACTURER'S RECOMMENDATION.
- ANY MATERIAL USED FOR BACK-FILLING IS TO BE OF EQUAL OR BETTER QUALITY THAN THE EXCAVATED MATERIAL.
- ALL BACK-FILLING MATERIAL IS TO BE PLACED AND COMPACTED IN 150mm THICK LAYERS.
- TIMBER POLE TO BE PLANTED WITH N MARKING AT 4m FROM BUT FACING NORTH

ACCESS SYSTEM
DETAIL
Scale 1:50

LATCHWAY SAFETY
SYSTEM DETAIL
Scale 1:50

ALL SCALES AS SHOWN WHEN PRINTED AT A3

ALL SCALES AS SHOWN WHEN PRINTED AT A3

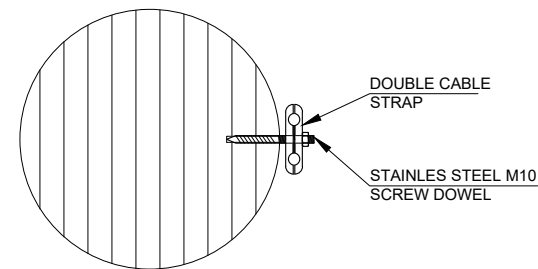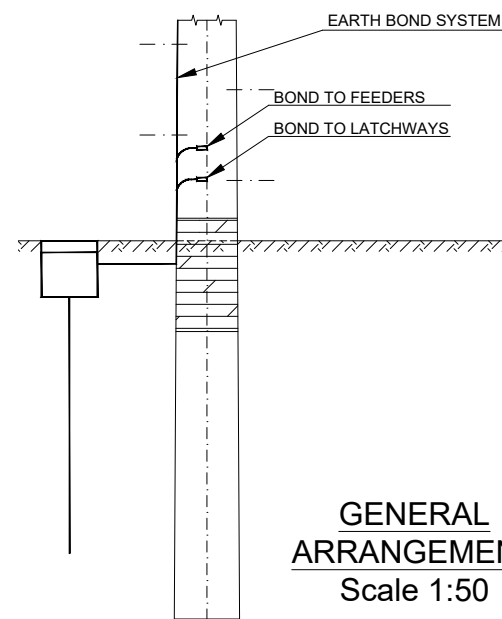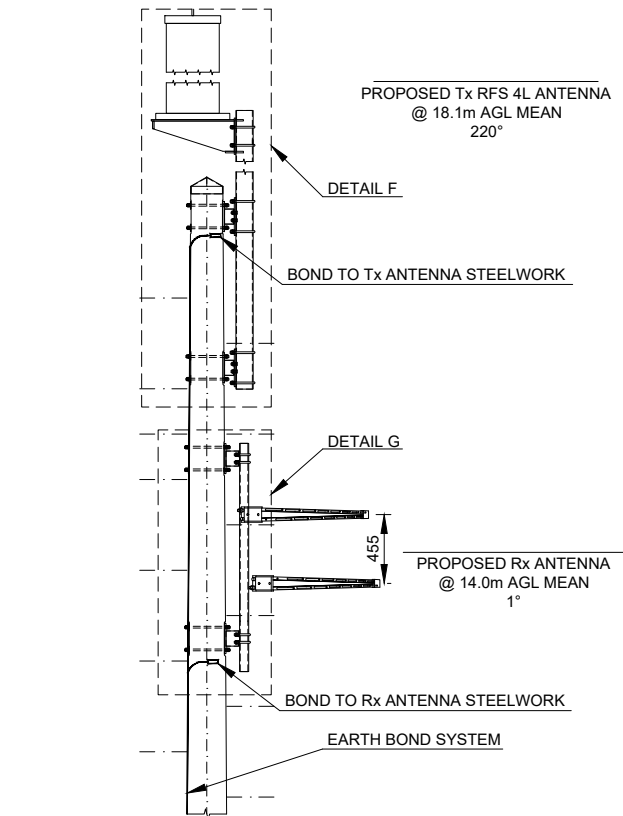

**FEEDER
MANAGEMENT**
Scale 1:10

NOTES


1. AS FAR AS IS PRACTICABLE ALL CUTTING SCARFING AND DRILLING TO BE DONE BEFORE CREOSOTING. WHERE THIS IS NOT POSSIBLE ALL CUT, DRILLED, AND SCARFED SURFACES TO BE COATED WITH A MIXTURE OF CREOSOTE AND TAR

FEEDERS

1. SUPPLY OF FEEDERS BY OTHERS LCF78-50 TO Tx ANTENNA & LCF12-50 TO Rx ANTENNA
2. FEEDERS FIXED AT 1000mm CENTRES

EARTHING

1. CONNECT EARTH BOND TO NEW EARTHING SYSTEM
2. MAXIMUM VALUE FOR GROUND RESISTANCE TO BE 10 OHMS
3. CABLE OR TAPE TO BE FIXED TO POLE AT 1000mm CENTRES
4. EARTHING SHOULD COMPLY WITH ARQIVA'S DOCUMENT BOS147

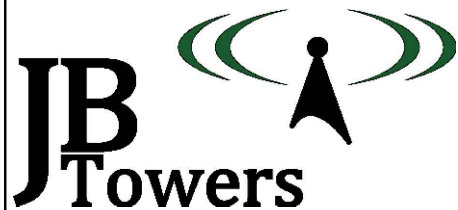


01	FIRST ISSUE	AM	01/05/18
REV	REV	BY	DATE
SCALE AS SHOWN WHEN PRINTED AT A3	DRAWN DATE 01/05/18	CHECKED DATE 01/05/18	APPROVED DATE 01/05/18
ALL DIMENSIONS IN mm UNLESS OTHERWISE STATED. THIS DRAWING TO BE READ IN CONJUNCTION WITH OTHER RELEVANT DRAWINGS.			

TITLE		SITE ADDRESS	
EAST DEAN		EAST DEAN EAST SUSSEX BN20 0JZ	
GENERAL ARRANGEMENT SHEET 2 OF 3		ARQIVA REF. 140649	DRG No. 200 REV 01

ALL SCALES AS SHOWN WHEN PRINTED AT A3




ALL SCALES AS SHOWN WHEN PRINTED AT A3

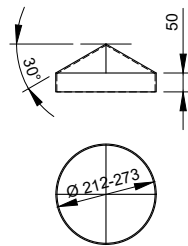


MATL.: 3mm THK LEAD
FINISH: NATURAL
FORM: 4 WAY PYRAMID / CONE


DETAIL A - LEAD CAP
Scale 1:20

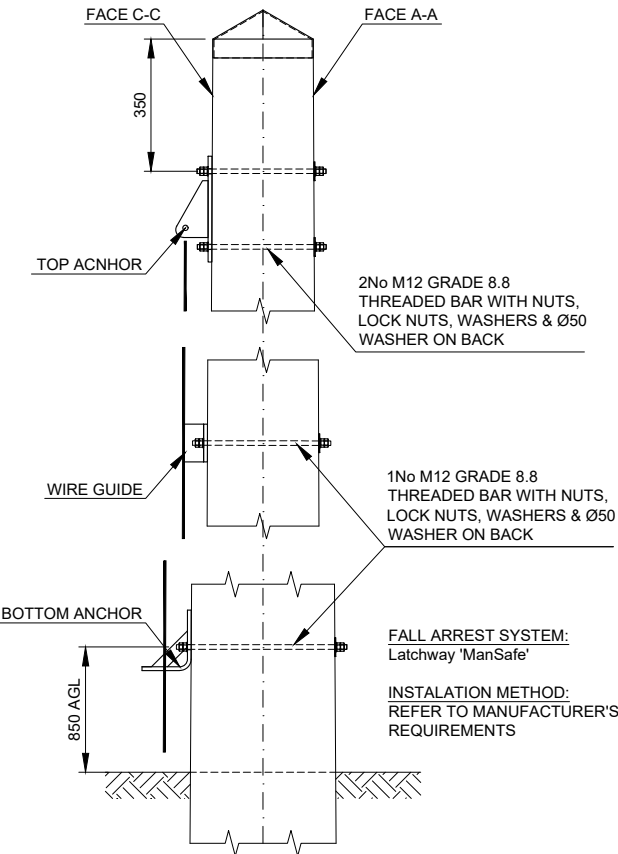


DETAIL B - FALL ARREST SYSTEM
Scale 1:20

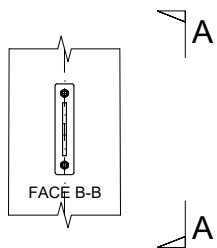

DETAIL C - FALL ARREST
ATTACHMENT POINT
Scale 1:20

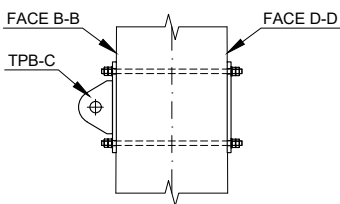


VIEW A-A
Scale 1:20

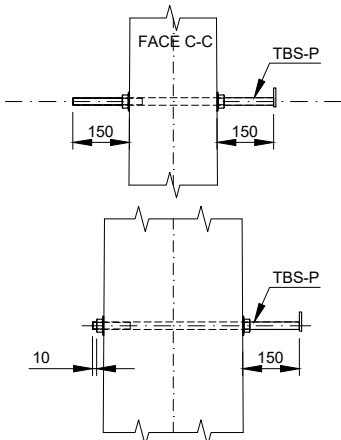


DETAIL D - PERMANENT
CLIMBING STEPS
Scale 1:20

ALL STEP BOLTS TO BE CUT ON
SITE TO EXTEND MAX 10mm
BEYOND THE NUT WHEN
TIGHTENED, EXCLUDING THE
DETAIL ABOVE

NOTE:
ALL SITE DRILLED HOLE/CUT
ENDS TO BE TREATED WITH
METAFLUX 70-40 ZINC PASTE
FOLLOWED BY 1 COAT OF
7-42 ZINC ALU OR 70-16
ALUMINIUM SPRAY

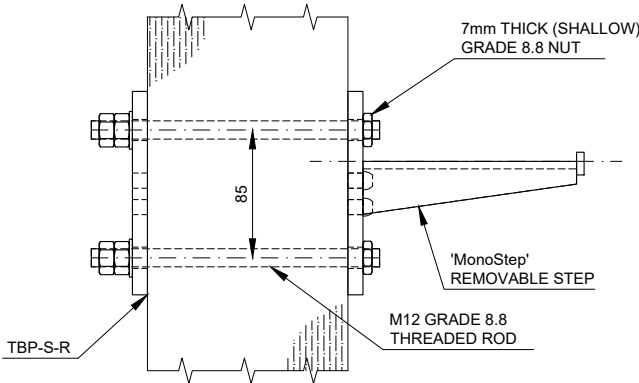

DETAIL E - REMOVABLE
CLIMBING STEPS
Scale 1:5

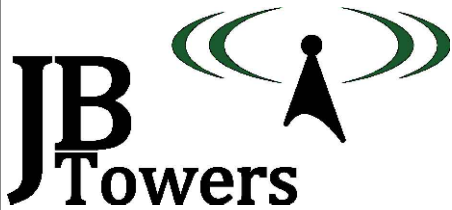

02	DETAIL A UPDATED	AM	08/05/18
01	FIRST ISSUE	AM	01/05/18
REV	REV	BY	DATE
SCALE AS SHOWN WHEN PRINTED AT A3	DRAWN DATE 01/05/18	CHECKED DATE 01/05/18	APPROVED DATE 01/05/18
ALL DIMENSIONS IN mm UNLESS OTHERWISE STATED. THIS DRAWING TO BE READ IN CONJUNCTION WITH OTHER RELEVANT DRAWINGS.			

TITLE
EAST DEAN
GENERAL ARRANGEMENT
SHEET 3 OF 3


SITE ADDRESS
EAST DEAN
EAST SUSSEX
BN20 0JZ

ARQIVA REF.
140649
DRG No.
200
REV
02

ALL SCALES AS SHOWN WHEN PRINTED AT A3



ALL SCALES AS SHOWN WHEN PRINTED AT A3

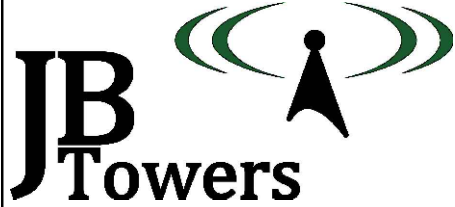

02	DETAILS A & B UPDATED			AM	08/05/18
01	FIRST ISSUE			AM	01/05/18
REV	REV			BY	DATE
SCALE AS SHOWN WHEN PRINTED AT A3		DRAWN	AM	CHECKED	MP
		DATE	01/05/18	DATE	01/05/18
		APPROVED		JBT	
		DATE		01/05/18	
ALL DIMENSIONS IN mm UNLESS OTHERWISE STATED. THIS DRAWING TO BE READ IN CONJUNCTION WITH OTHER RELEVANT DRAWINGS.					


TITLE
EAST DEAN
TIMBER POLE HOLE SET OUT
SHEET 1 OF 2

SITE ADDRESS
EAST DEAN
EAST SUSSEX
BN20 0JZ

ARQIVA REF.
140649

DRG No.
201


REV
02

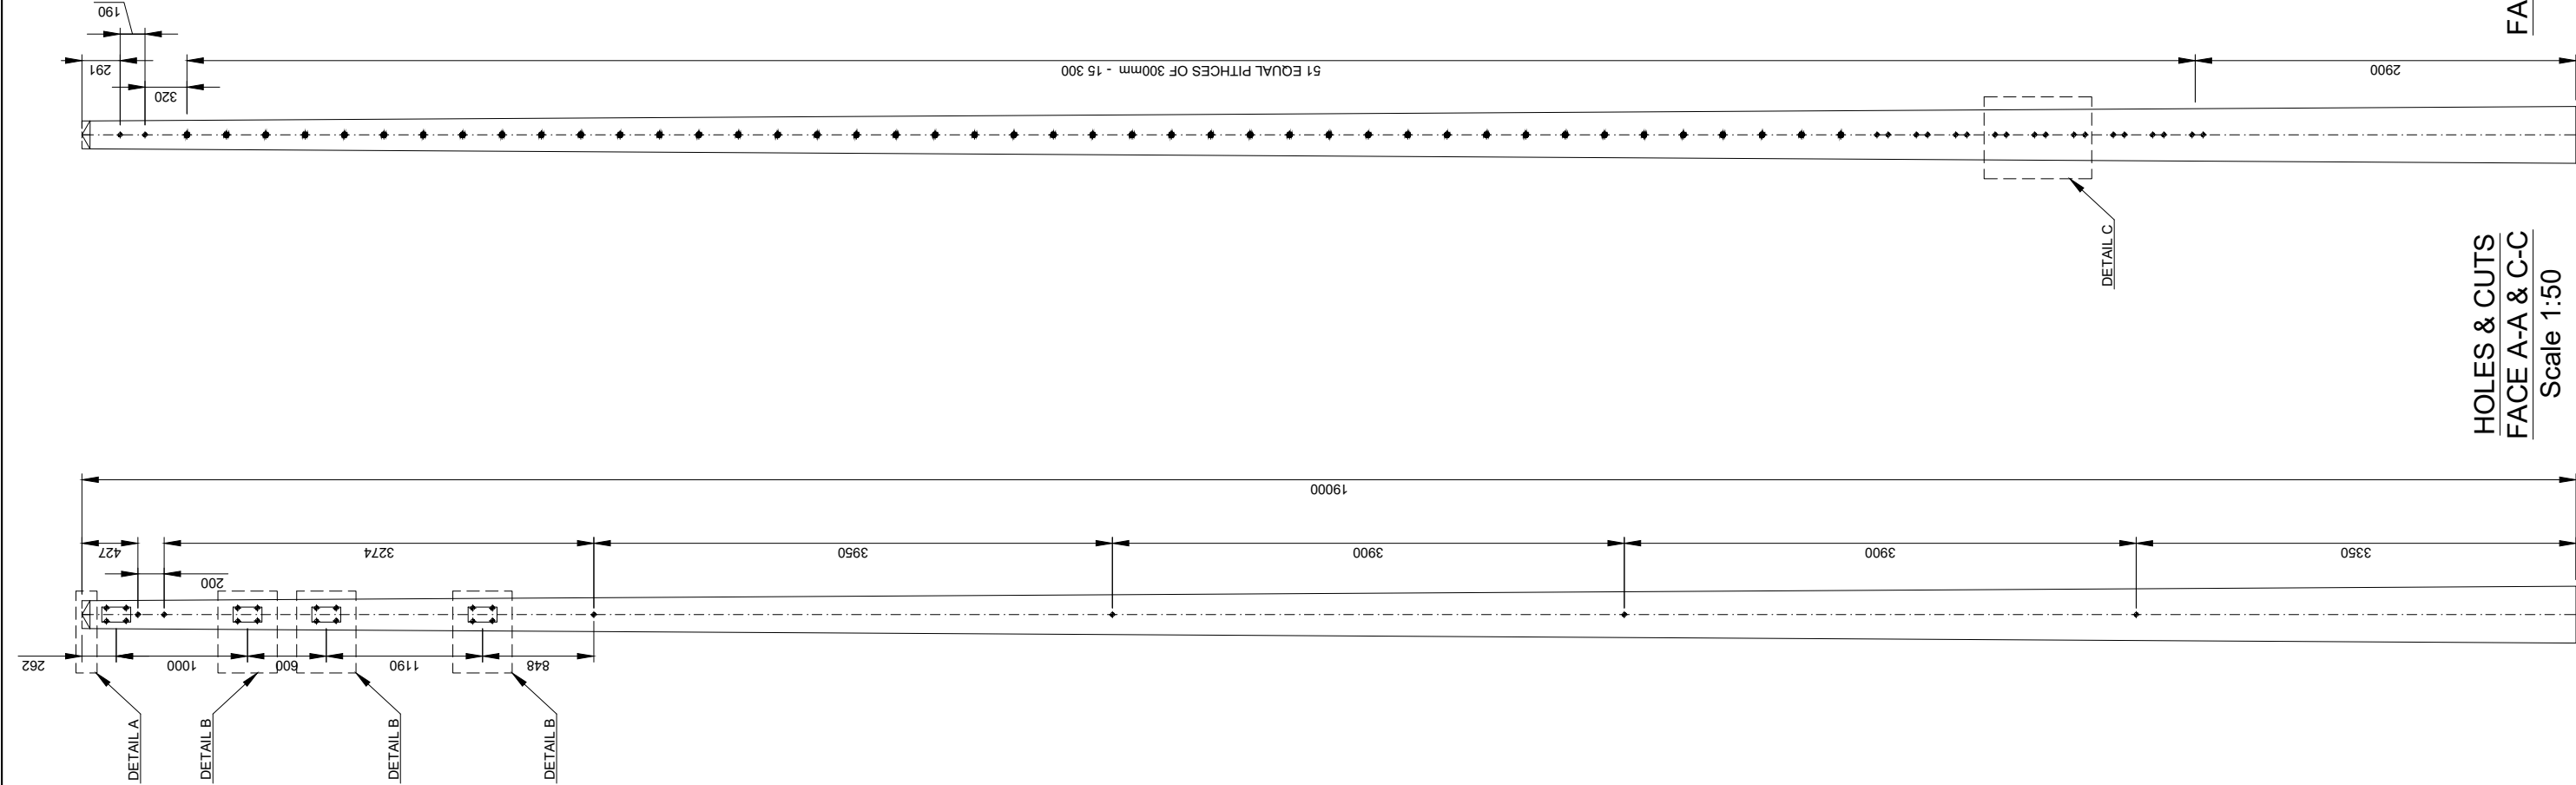


HOLES & CUTS
FACE A-A & C-C
Scale 1:50

HOLES
FACE B-B & D-D
Scale 1:50


DETAIL C - TYPICAL
Scale 1:10

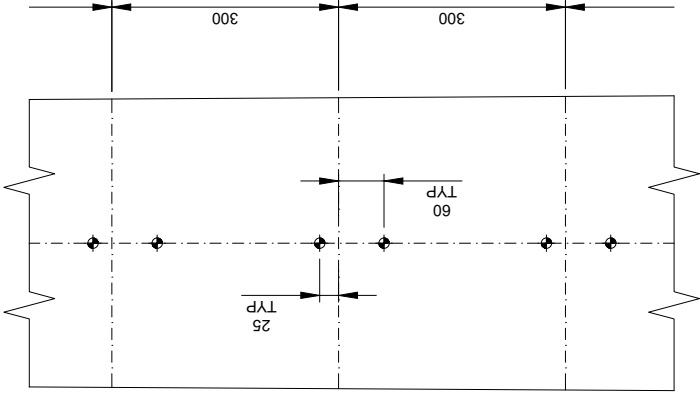


DETAIL B - TYPICAL
Scale 1:10

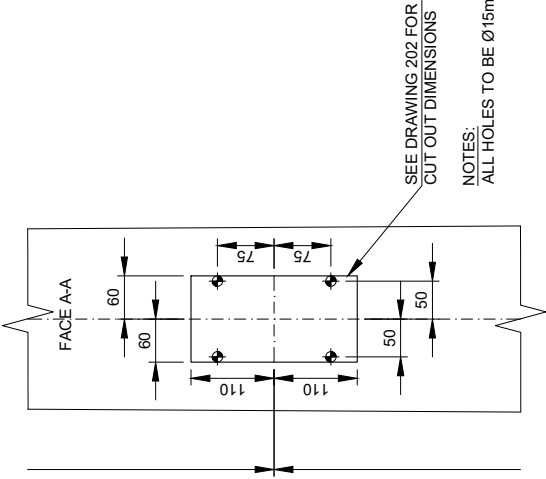

DETAIL A
Scale 1:10

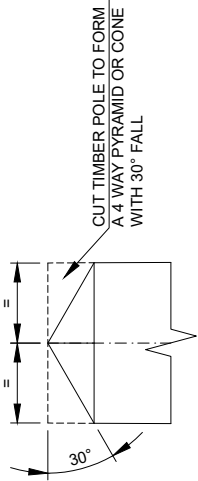

TIMBER POLE
FACE NOMENCLATURE
Scale 1:20

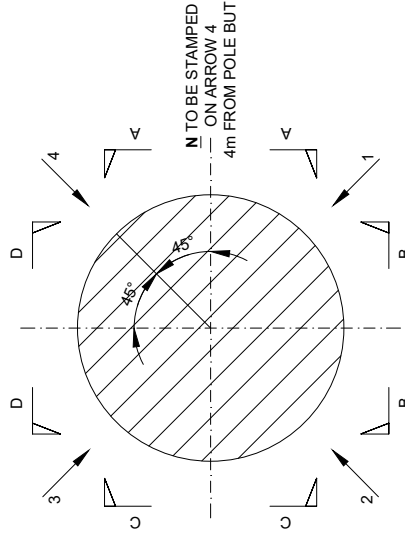


HOLE DIAMETERS	
	- 22mm THROUGH HOLE
	- 15mm THROUGH HOLE
	- 8mm HOLE 70mm LONG

ALL SCALES AS SHOWN WHEN PRINTED AT A3





ALL SCALES AS SHOWN WHEN PRINTED AT A3

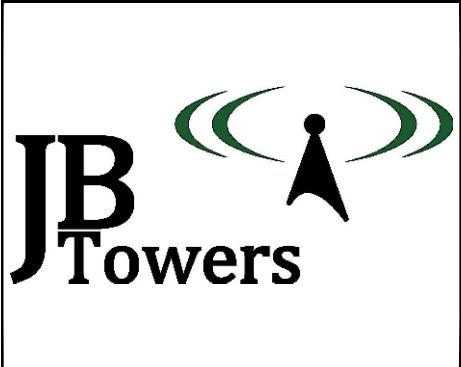

01	FIRST ISSUE							AM	01/05/18
REV	REV							BY	DATE
SCALE AS SHOWN		DRAWN		AM		CHECKED		MP	
WHEN PRINTED AT A3		DATE		01/05/18		DATE		01/05/18	
APPROVED		JBT							
DATE		01/05/18							
ALL DIMENSIONS IN mm UNLESS OTHERWISE STATED. THIS DRAWING TO BE READ IN CONJUNCTION WITH OTHER RELEVANT DRAWINGS.									

TITLE
EAST DEAN
TIMBER POLE HOLE SET OUT
SHEET 2 OF 2

SITE ADDRESS		
EAST DEAN EAST SUSSEX BN20 0JZ		
ARQIVA REF. 140649	DRG No. 201	REV 01

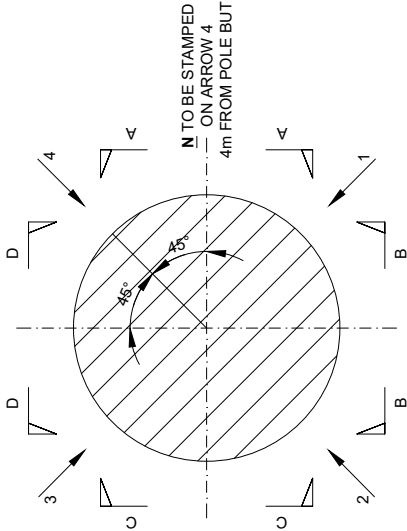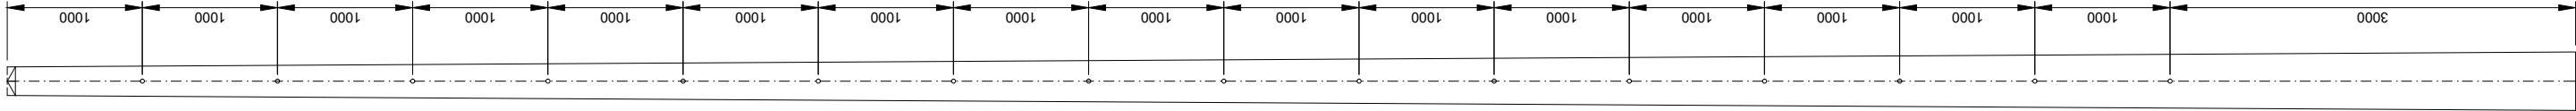

TIMBER POLE
FACE NOMENCLATURE
Scale 1:20

ALL HOLES ON ARROW 1
TO BE Ø8mm & 70mm LONG

HOLES
ARROW 1
Scale 1:50


HOLE DIAMETERS

- 22mm THROUGH HOLE
- 15mm THROUGH HOLE
- 8mm HOLE 70mm LONG



ALL SCALES AS SHOWN WHEN PRINTED AT A3

ALL SCALES AS SHOWN WHEN PRINTED AT A3

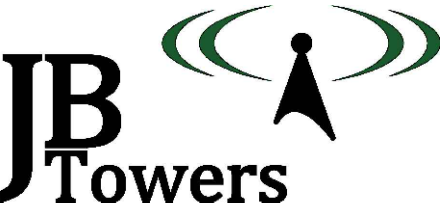


02	HEIGHT AMENDED			AM	08/05/18
01	FIRST ISSUE			AM	01/05/18
REV	REV			BY	DATE
SCALE AS SHOWN		DRAWN	AM	CHECKED	MP
WHEN PRINTED AT A3		DATE	01/05/18	DATE	01/05/18
		APPROVED		JBT	
		DATE		01/05/18	
ALL DIMENSIONS IN mm UNLESS OTHERWISE STATED. THIS DRAWING TO BE READ IN CONJUNCTION WITH OTHER RELEVANT DRAWINGS.					


TITLE
EAST DEAN
TIMBER POLE CUT OUT
DETAIL

SITE ADDRESS EAST DEAN EAST SUSSEX BN20 0JZ		
ARQIVA REF. 140649	DRG No. 202	REV 02


TIMBER POLE CUT OUT
DETAIL

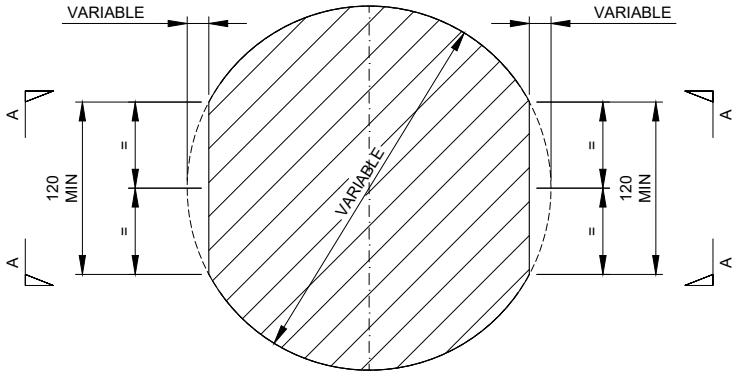

PLAN VIEW
Scale 1:5

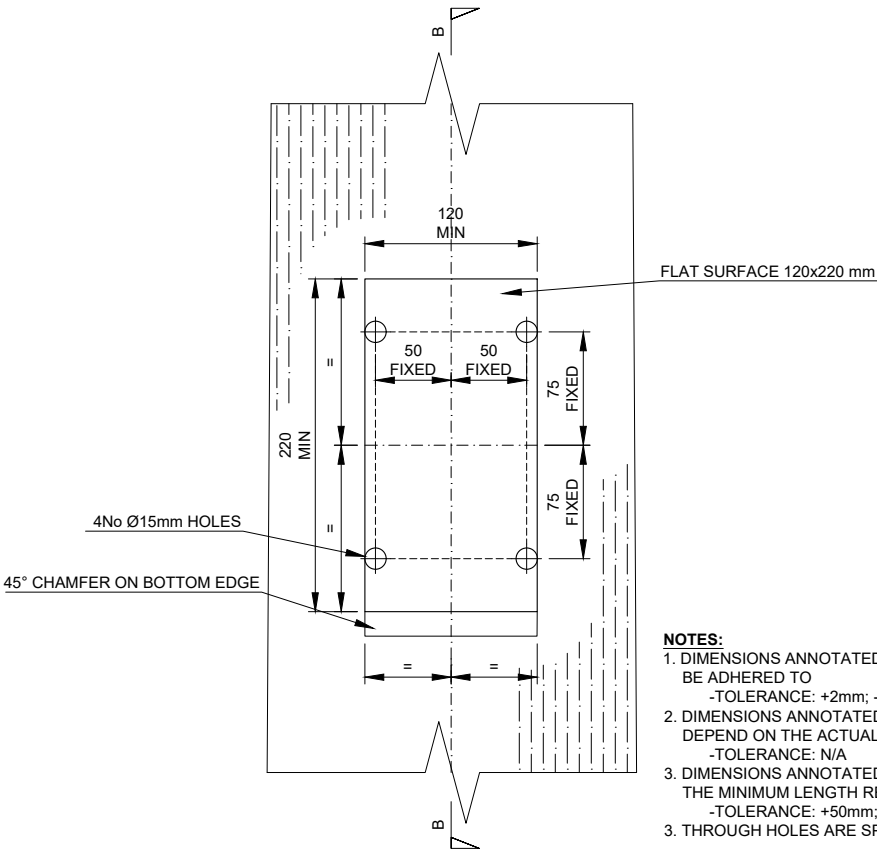

VIEW A-A
Scale 1:5

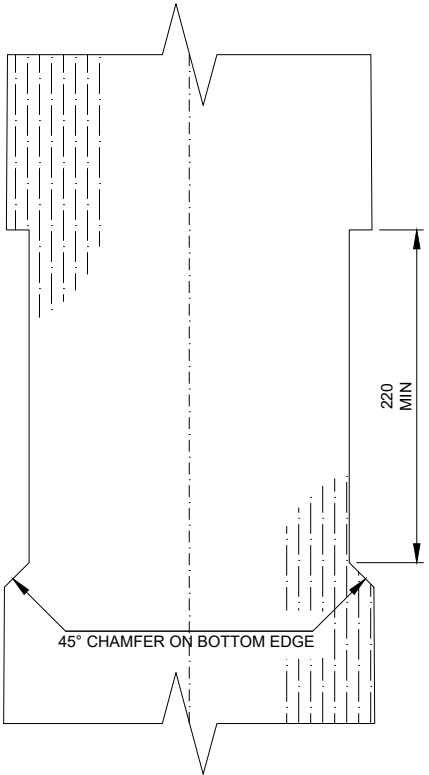


VIEW B-B
Scale 1:5

- NOTES:
- DIMENSIONS ANNOTATED AS 'FIXED' ARE TO BE ADHERED TO
-TOLERANCE: +2mm; -2mm
 - DIMENSIONS ANNOTATED AS 'VARIABLE' DEPEND ON THE ACTUAL DIAMETER
-TOLERANCE: N/A
 - DIMENSIONS ANNOTATED AS 'MIN' PROVIDE THE MINIMUM LENGTH REQUIRED
-TOLERANCE: +50mm; -0mm
 - THROUGH HOLES ARE SPECIFIED ON DRAWING 201


ALL SCALES AS SHOWN WHEN PRINTED AT A3



ALL SCALES AS SHOWN WHEN PRINTED AT A3

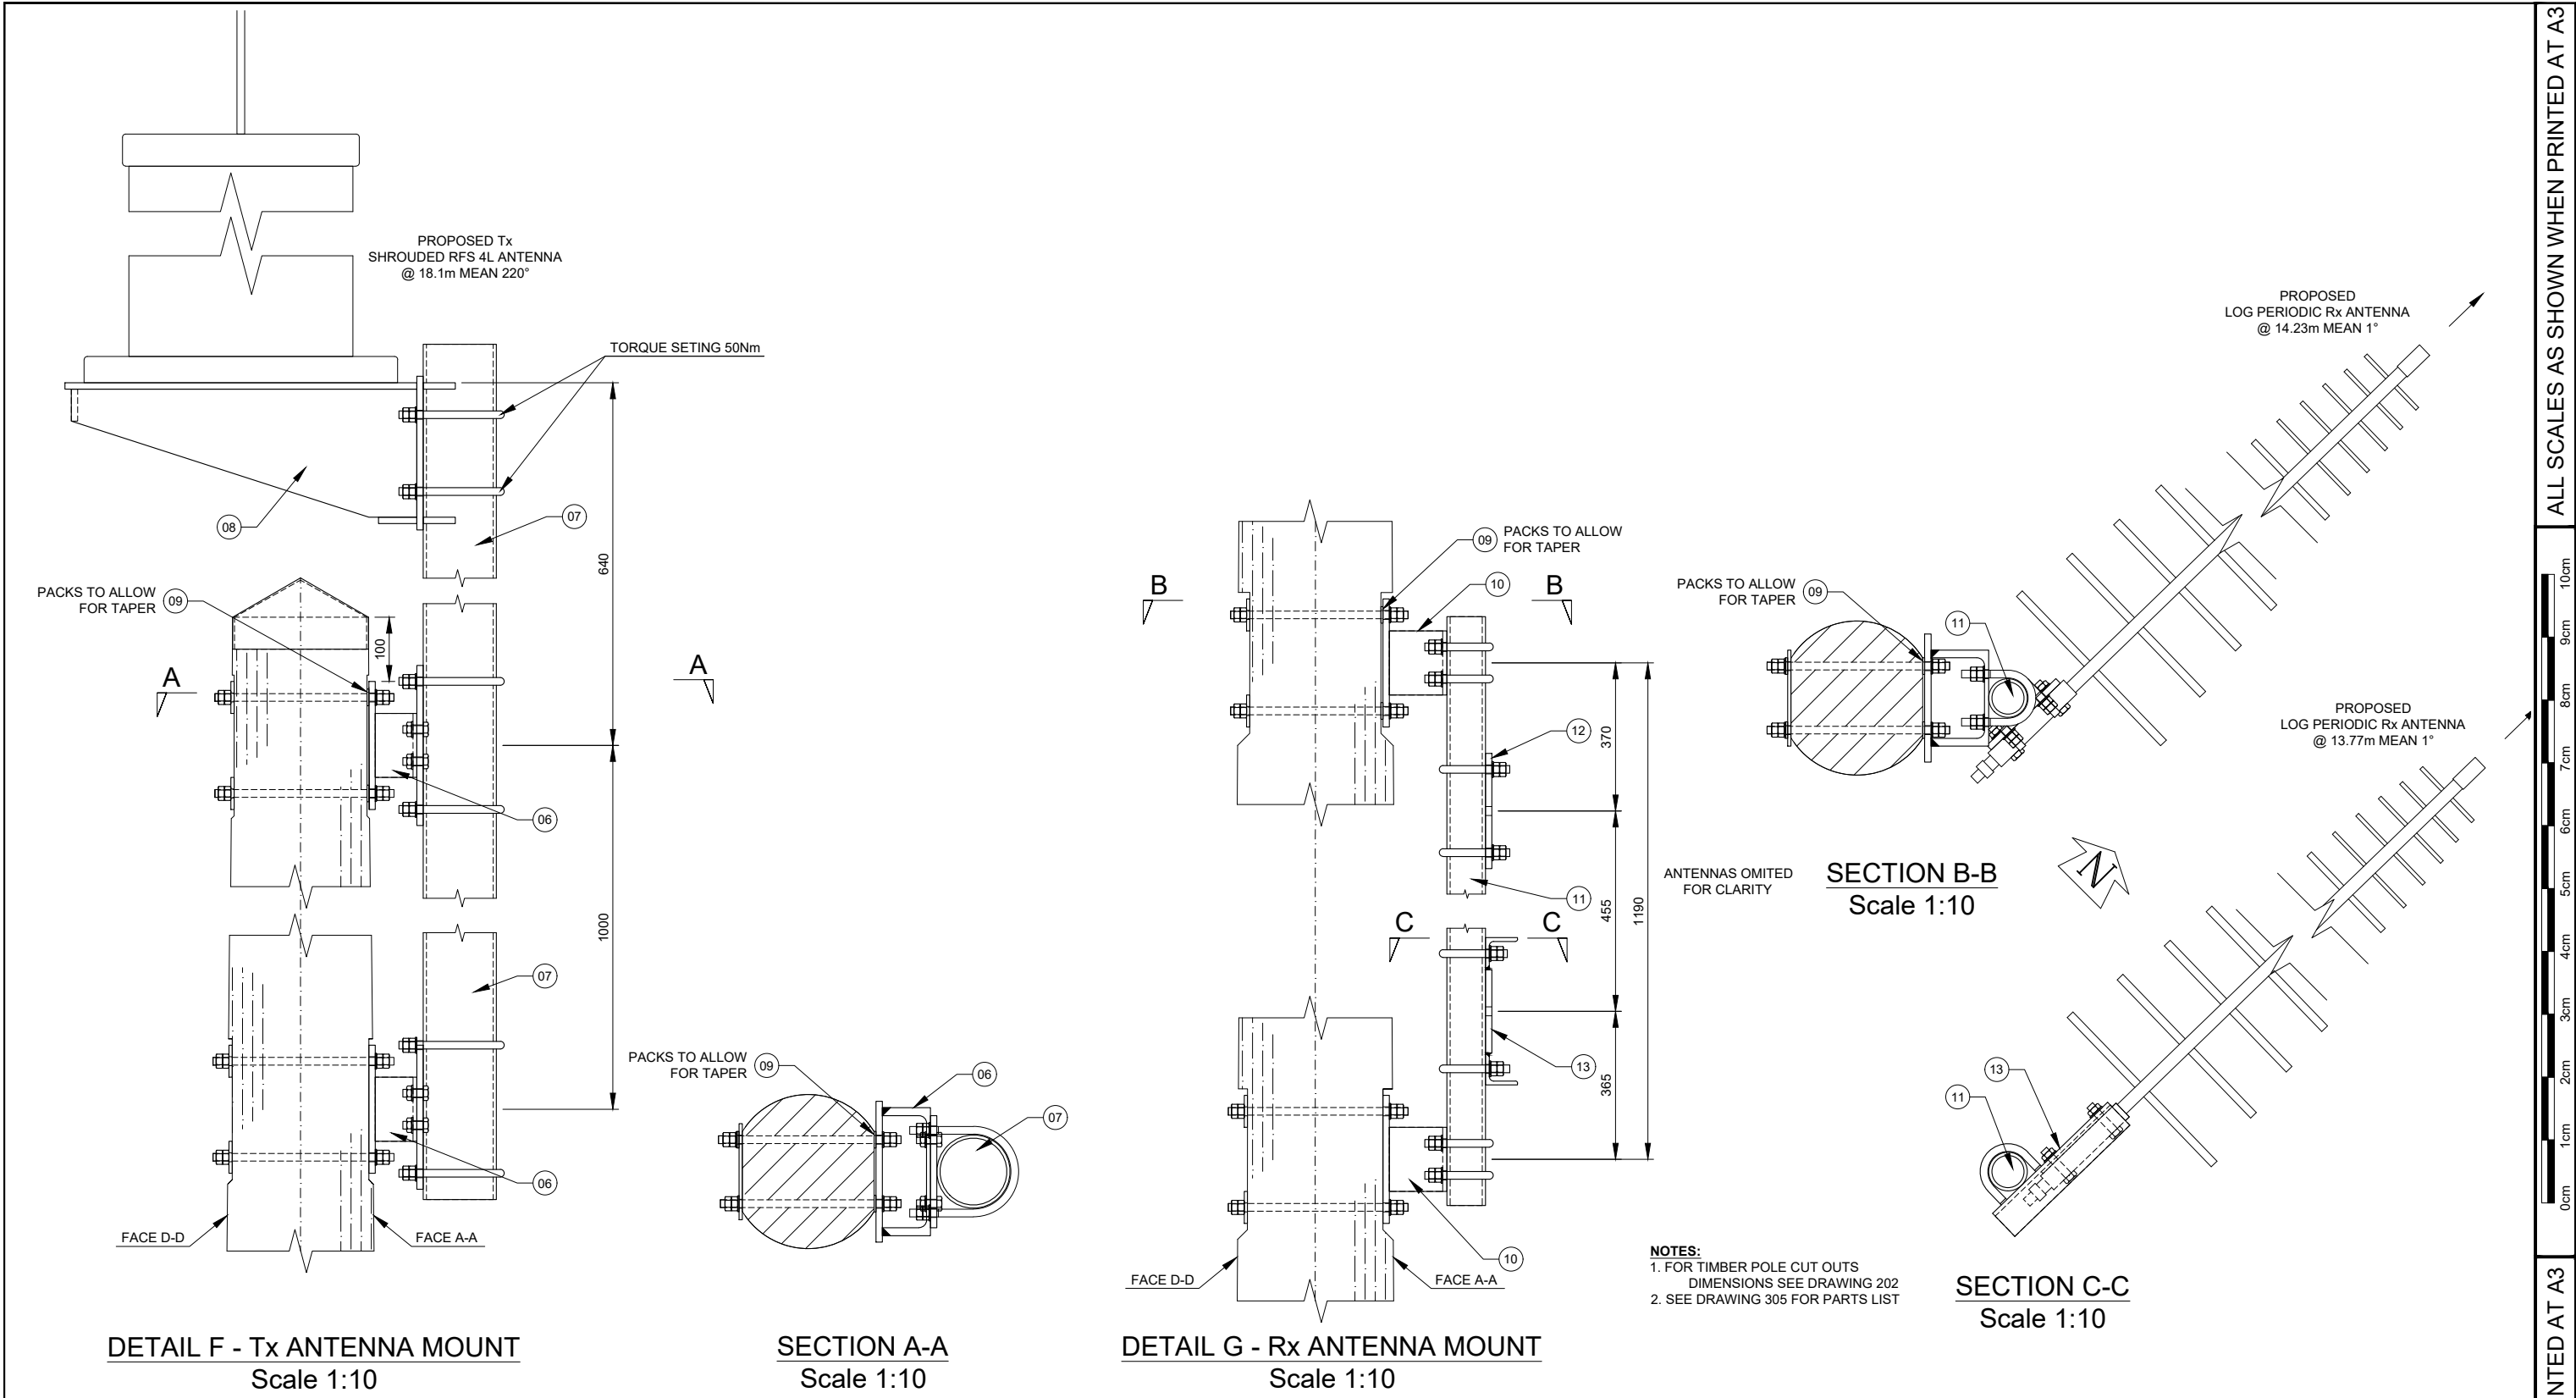


ALL SCALES AS SHOWN WHEN PRINTED AT A3

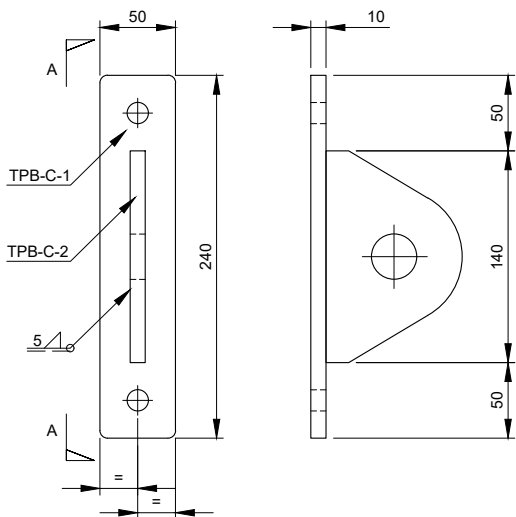

PART TPB-C
Scale 1:5

VIEW A-A
Scale 1:5

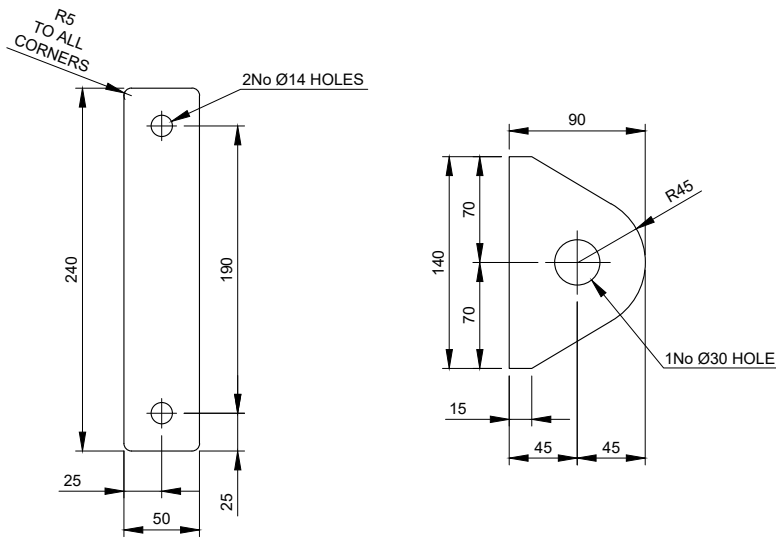


TPB-C-1 - 10mm THICK
Scale 1:5

TPB-C-2 - 10mm THICK
Scale 1:5

Parts list for TPB-C

Item	Part	Quantity	Part description	Length	Material
01	TPB-C-1	1	240x50x10mm	N/A	S275J0
02	TPB-C-2	1	140x90x10mm	N/A	S275J0
03	STUDS	2	M12 STUDDING	300mm	GRADE 8.8
04	SQ-WSH	2	50mm M12 SQUARE WASHER	N/A	GRADE 8.8

- All steel hot dip galvanized
- Each STUD to be supplied with 4 Full Nuts, 2 Flat Washers and 2 Spring Washers
- For fabrtaction notes see drawing 305

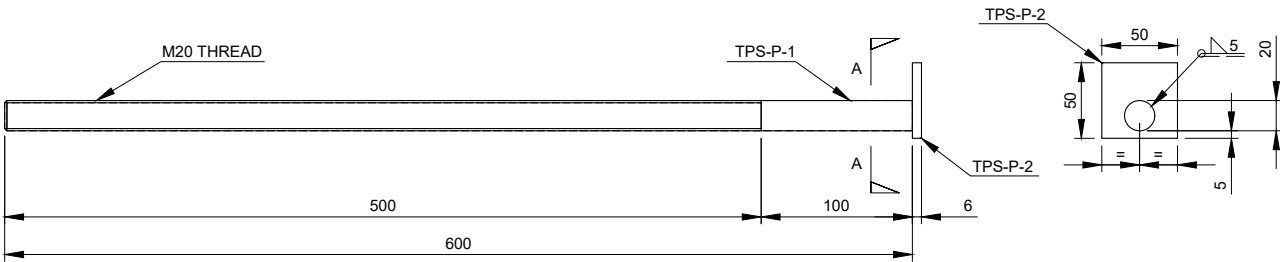


PART TPS-P
Scale 1:5

Parts list for TPS-P

Item	Part	Quantity	Part description	Length	Material
01	TPS-P-1	1	20mm THREADED ROD	600mm	S275J0
02	TPS-P-2	1	50x50x6mm	N/A	S275J0
03	SQ-WSH	2	50mm M12 SQUARE WASHER	N/A	GRADE 8.8
04	NUT	2	M20 NUT	N/A	GRADE 8.8

- All steel hot dip galvanized
- For fabrtaction notes see drawing 305

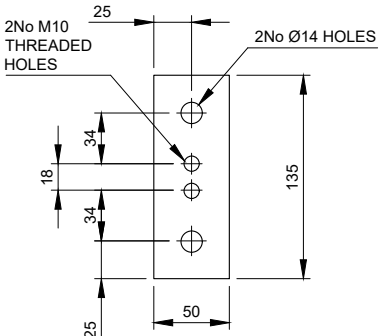


PART TPS-R
Scale 1:5

Parts list for TPS-R

Item	Part	Quantity	Part description	Length	Material
01	TPS-R	2	135x50x10mm	N/A	S275J0
02	STUDS	2	M12 STUDDING	460mm	GRADE 8.8
03	NUT-S	2	M12 SHALLOW NUT	N/A	GRADE 8.8
04	NUT	4	M12 NUT	N/A	GRADE 8.8
03	WSH	2	M12 WASHER	N/A	GRADE 8.8

- All steel hot dip galvanized
- For fabrtaction notes see drawing 305

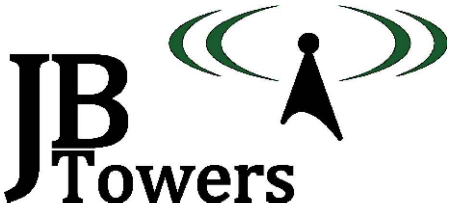

01	FIRST ISSUE	AM	01/05/18
REV	REV	BY	DATE
SCALE AS SHOWN WHEN PRINTED AT A3	DRAWN DATE 01/05/18	CHECKED DATE 01/05/18	APPROVED DATE 01/05/18
ALL DIMENSIONS IN mm UNLESS OTHERWISE STATED. THIS DRAWING TO BE READ IN CONJUNCTION WITH OTHER RELEVANT DRAWINGS.			

TITLE
ATTACHMENT POINT & STEP
RUNGS DETAILS
PARTS: TPB-C; TPS-P; TPS-R

SITE ADDRESS
EAST DEAN
EAST SUSSEX
BN20 0JZ

ARQIVA REF.
140649







DRG No.
300

REV
01

ALL SCALES AS SHOWN WHEN PRINTED AT A3




ALL SCALES AS SHOWN WHEN PRINTED AT A3

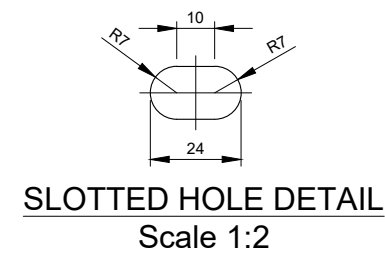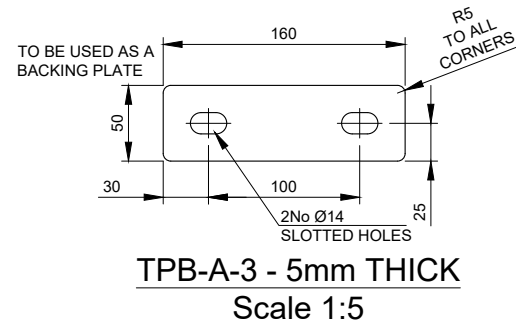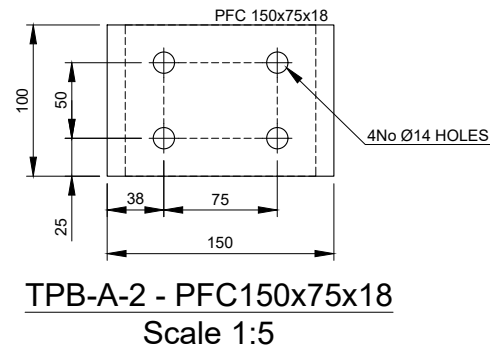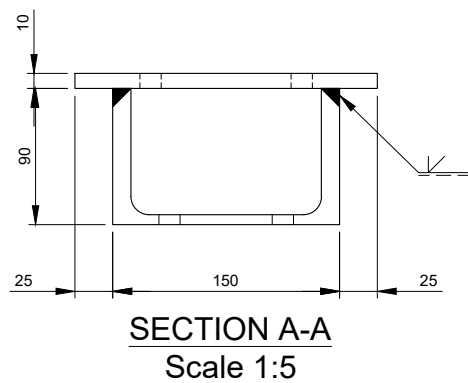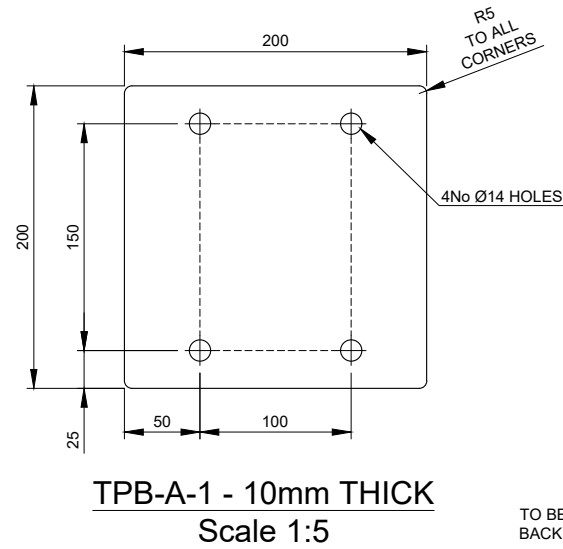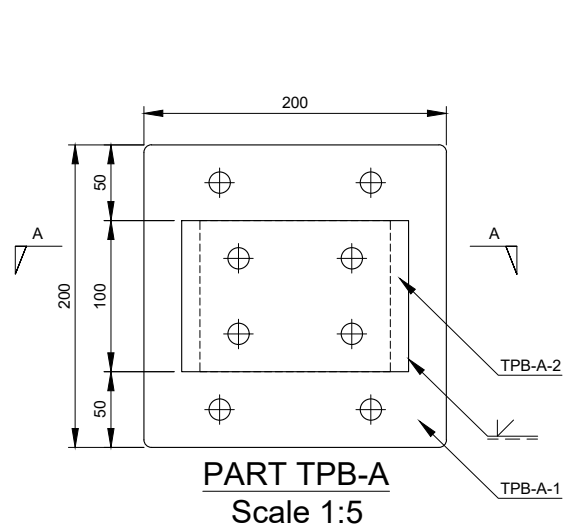

Parts list for TPB-A

Item	Part	Quantity	Part description	Length	Material
01	TPB-A-1	1	200x200x10mm	N/A	S275J0
02	TPB-A-2	1	PFC 150x75x18	100mm	S275J0
03	TPB-A-3	2	160x50x5mm	N/A	S275J0
04	STUDS	4	M12 STUDDING	350mm	GRADE 8.8
05	U-BOLT	2	M12 U-BOLT FOR CHS 60.3mm	N/A	GRADE 8.8

- All steel hot dip galvanized
- Each STUD & U-BOLT to be supplied with 4 Full Nuts, 2 Flat Washers and 2 Spring Washers
- For fabrtication notes see drawing 305

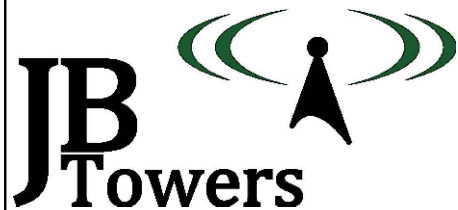


01	FIRST ISSUE			AM	01/05/18
REV	REV			BY	DATE
SCALE AS SHOWN WHEN PRINTED AT A3		DRAWN	AM	CHECKED	MP
		DATE	01/05/18	DATE	01/05/18
		APPROVED			
		JBT			
ALL DIMENSIONS IN mm UNLESS OTHERWISE STATED. THIS DRAWING TO BE READ IN CONJUNCTION WITH OTHER RELEVANT DRAWINGS.					

TITLE		SITE ADDRESS	
Rx STEELWORK BRACKET		EAST DEAN EAST SUSSEX BN20 0JZ	
PART: TPB-A			
ARQIVA REF. 140649		DRG No. 301	REV 01


ALL SCALES AS SHOWN WHEN PRINTED AT A3




ALL SCALES AS SHOWN WHEN PRINTED AT A3

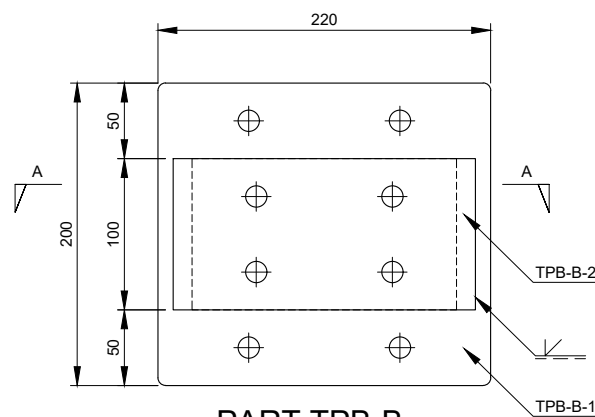


PART TPB-B
Scale 1:5

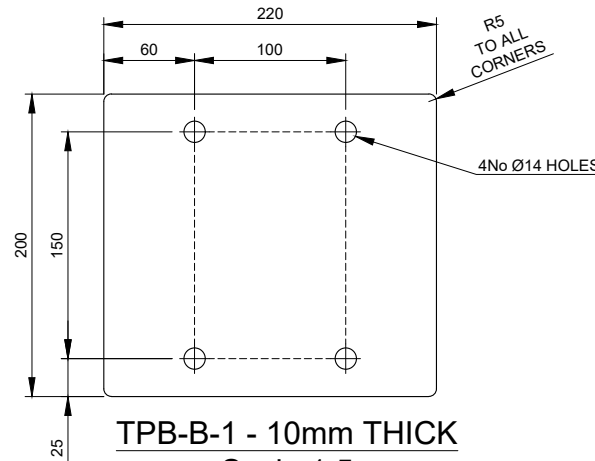


TPB-B-1 - 10mm THICK
Scale 1:5

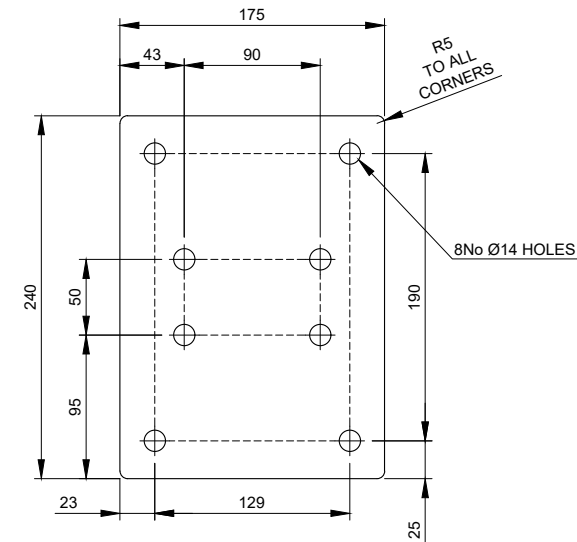


TPB-B-3 - 10mm THICK
Scale 1:5

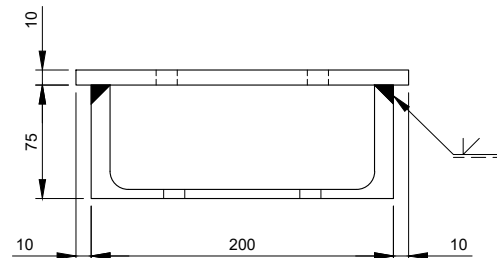


SECTION A-A
Scale 1:5

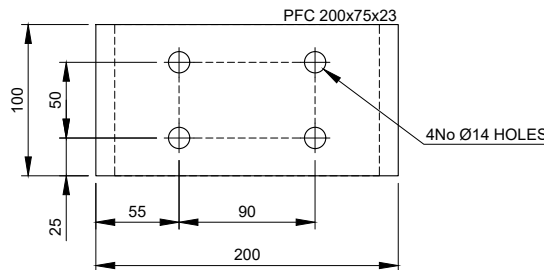

TPB-B-2 - PFC 200x75x23
Scale 1:5

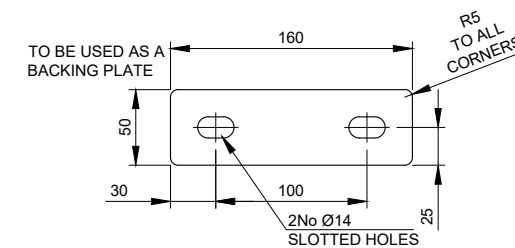

TPB-B-4 - 5mm THICK
Scale 1:5

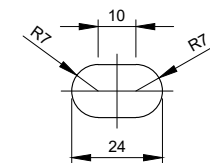


SLOTTED HOLE DETAIL
Scale 1:2

Parts list for TPB-B

Item	Part	Quantity	Part description	Length	Material
01	TPB-B-1	1	220x200x10mm	N/A	S275J0
02	TPB-B-2	1	PFC 200x75x23	100mm	S275J0
03	TPB-B-3	1	240x175x10mm	N/A	S275J0
04	TPB-B-4	2	160x50x5mm	N/A	S275J0
05	STUDS	4	M12 STUDDING	330mm	GRADE 8.8
06	BOLT	4	M12 40mm LONG (2D+6)	40mm	GRADE 8.8
07	U-BOLT	2	M12 U-BOLT FOR CHS 114.3mm	N/A	GRADE 8.8

- All steel hot dip galvanized
- Each STUD & U-BOLT to be supplied with 4 Full Nuts, 2 Flat Washers and 2 Spring Washers
- Each BOLT to be supplied with 1 Full Nut, 1 Form E Flat Washer and 1 Spring Washer
- For fabrication notes see drawing 305

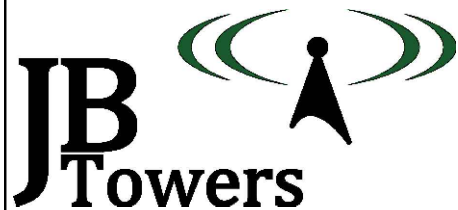











01	FIRST ISSUE	AM	01/05/18
REV	REV	BY	DATE
SCALE AS SHOWN WHEN PRINTED AT A3	DRAWN DATE 01/05/18	CHECKED DATE 01/05/18	APPROVED DATE 01/05/18
ALL DIMENSIONS IN mm UNLESS OTHERWISE STATED. THIS DRAWING TO BE READ IN CONJUNCTION WITH OTHER RELEVANT DRAWINGS.			

TITLE	Tx STEELWORK BRACKET		
PART: TPB-B			
SITE ADDRESS	EAST DEAN EAST SUSSEX BN20 0JZ		
ARQIVA REF. 140649	DRG No. 302	REV 01	

ALL SCALES AS SHOWN WHEN PRINTED AT A3




ALL SCALES AS SHOWN WHEN PRINTED AT A3

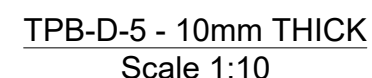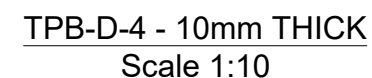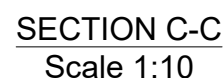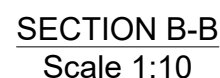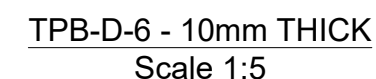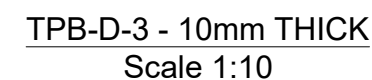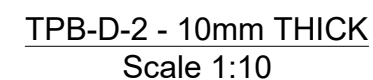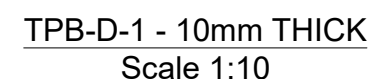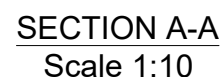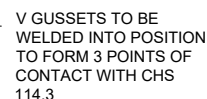

Parts list for TPB-D

Item	Part	Quantity	Part description	Length	Material
01	TPB-D-1	1	550x550x10mm	N/A	S275J0
02	TPB-D-2	1	550x240x10mm	N/A	S275J0
03	TPB-D-3	2	550x200x10mm	N/A	S275J0
04	TPB-D-4	1	510x50x10mm	N/A	S275J0
05	TPB-D-5	1	510x60x10mm	N/A	S275J0
06	TPB-D-6	4	50x50x10mm	N/A	S275J0
07	U-BOLT	2	M12 U-BOLT FOR CHS 114.3mm	N/A	GRADE 8.8

- All steel hot dip galvanized
- Each U-BOLT to be supplied with 4 Full Nuts, 2 Flat Washers and 2 Spring Washers
- For fabrication notes see drawing 305

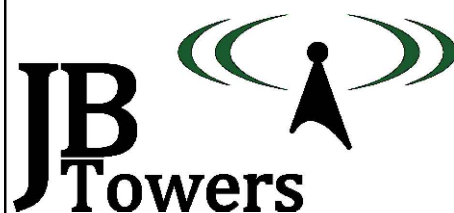

chalcroft
construction built on teamwork

argiva

01	FIRST ISSUE		AM	01/05/18	
REV	REV		BY	DAT	
SCALE AS SHOWN WHEN PRINTED AT A3	DRAWN AM DATE 01/05/18	CHECKED MP DATE 01/05/18	APPROVED JB DATE 01/05/18		
ALL DIMENSIONS IN mm UNLESS OTHERWISE STATED. THIS DRAWING TO BE READ IN CONJUNCTION WITH OTHER RELEVANT DRAWINGS					

TITLE

Tx MOUNTING PLATE

PART: TPB-D

SITE ADDRESS


EAST DEAN
EAST SUSSEX
BN20 0JZ

ARQIVA REF.
140649


DRG No.	303
---------	-----

REV
01

ALL SCALES AS SHOWN WHEN PRINTED AT A3

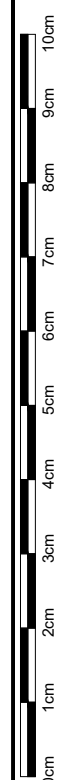

ALL SCALES AS SHOWN WHEN PRINTED AT A3

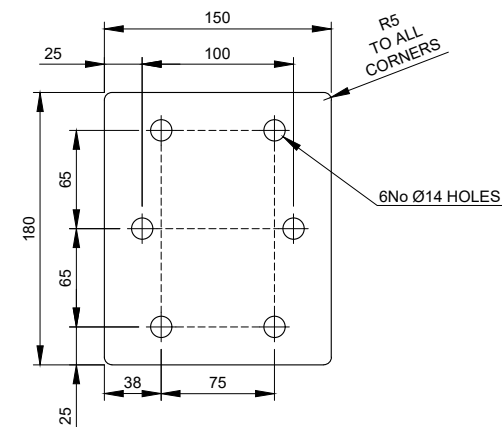


PART TPC-1 - 10mm THICK
Scale 1:5

Parts list for TPC-1

Item	Part	Quantity	Part description	Length	Material
01	TPC-1	1	180x150x10mm	N/A	S275J0
02	U-BOLT	2	M12 U-BOLT FOR CHS 60.3mm	N/A	GRADE 8.8

- All steel hot dip galvanized
- Each U-BOLT to be supplied with 4 Full Nuts, 2 Flat Washers and 2 Spring Washers
- For fabrtaion notes see drawing 305

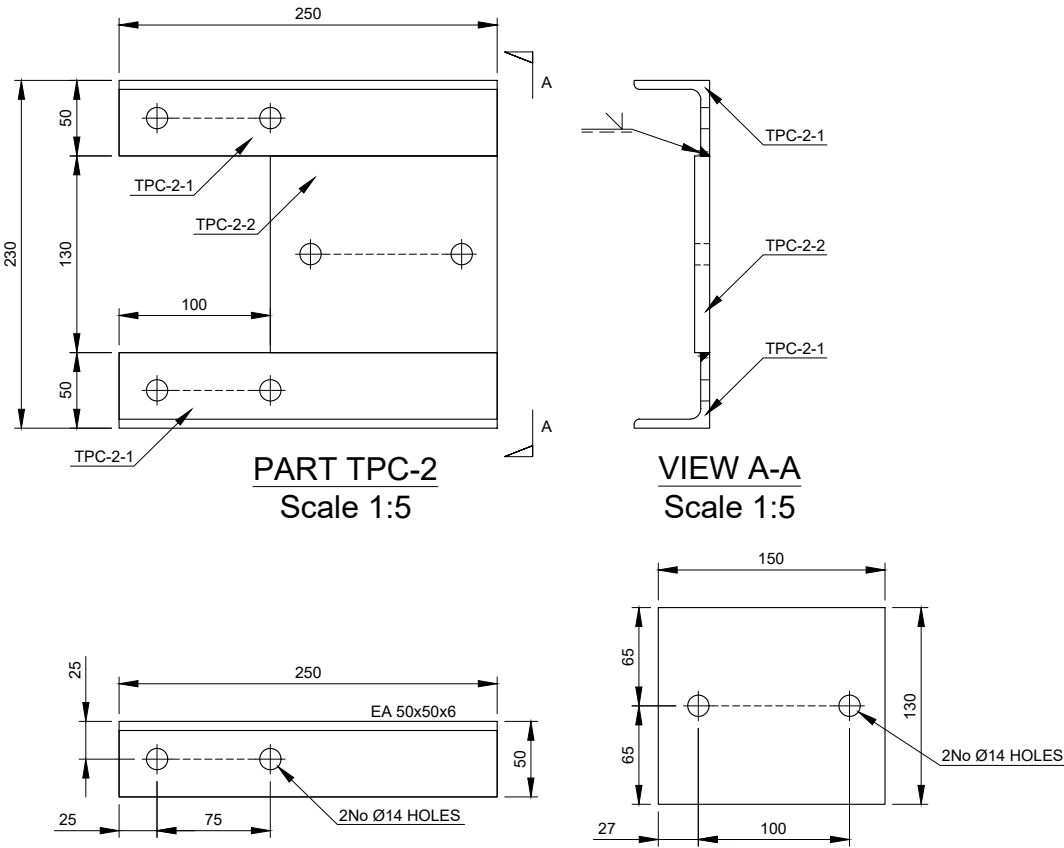


PART TPC-2
Scale 1:5

VIEW A-A
Scale 1:5

Parts list for TPC-2

Item	Part	Quantity	Part description	Length	Material
01	TPC-2-1	2	EA 50x50x6	250mm	S275J0
02	TPC-2-2	1	150x130x10mm	N/A	S275J0
03	U-BOLT	2	M12 U-BOLT FOR CHS 60.3mm	N/A	GRADE 8.8

- All steel hot dip galvanized
- Each U-BOLT to be supplied with 4 Full Nuts, 2 Flat Washers and 2 Spring Washers
- For fabrtaion notes see drawing 305

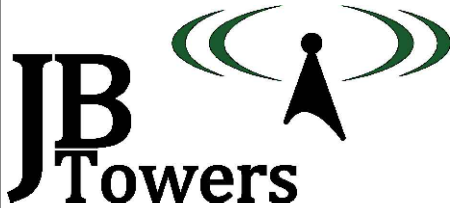

01	FIRST ISSUE	AM	01/05/18
REV	REV	BY	DATE
SCALE AS SHOWN WHEN PRINTED AT A3	DRAWN DATE 01/05/18	CHECKED DATE 01/05/18	APPROVED DATE 01/05/18
ALL DIMENSIONS IN mm UNLESS OTHERWISE STATED. THIS DRAWING TO BE READ IN CONJUNCTION WITH OTHER RELEVANT DRAWINGS.			

TITLE	SITE ADDRESS
Rx OFFSET BRACKET	EAST DEAN EAST SUSSEX BN20 0JZ
PARTS: TPC-1; TPC-2	ARQIVA REF. 140649
	DRG No. 304
	REV 01

ALL SCALES AS SHOWN WHEN PRINTED AT A3




ALL SCALES AS SHOWN WHEN PRINTED AT A3

- All steel hot dip galvanized
- All U-BOLTS to be FLA supply, each Supplied with 4 Full Nuts, 2 Flat Washers and 2 Spring Washers

Item	Part	Drawing	Quantity	Part description	Length	Material
01	01	200	1	LEAD CAP	N/A	LEAD
02	02	200	1	3 MAN LATCHWAY SYSTEM & 3No. WIRE GUIDES FOR FACE MOUNTED MONOPOLE	16500	N/A
03	TPB-C	300	1	FALL ARREST ATTACHMENT POINT	N/A	S275J0
04	TPS-P	300	43	STEP BOLT	N/A	S275J0
05	TPS-R	300	9	'MonoStep' ASSEMBLY	N/A	S275J0
06	TPB-B	302	2	Tx STEELWORK BRACKET	N/A	S275J0
07	07	203	1	CHS 114.3x5mm	2000mm	S355J2H
08	TPB-D	303	1	MOUNTING BRACKET ASSEMBLY	N/A	S275J0
09	09	-	24	M12 WASHER	N/A	GRADE 8.8
10	TPB-A	301	2	Rx STEELWORK BRACKET	N/A	S275J0
11	11	203	1	CHS 60.3x5mm	1500mm	S355J2H
12	TPC-1	304	1	Rx OFFSET BRACKET	N/A	S275J0
13	TPC-2	304	1	Rx OFFSET BRACKET	N/A	S275J0
14	14	-	1	FEEDER COVER - 2/CG/100	3500mm	UV RESISTANT PLASTIC
15	15	-	20	FEEDER CLAMP - 2/FCD/028	N/A	POLYPROPYLENE
16	16	-	20	M10 SCREW DOWELS WTH M10 NUT	100mm	STAINLESS STEEL
17	17	200	1	PoleSaver	750mm	N/A
18	18	200	8	M12 STUD + 4No NUTS + 2No FLAT WASHERS + 1No Ø50mm WASHER (FOR FALL ARREST SYSTEM)	470mm	GRADE 8.8

NOTES:

1. WELDING TO BE IN ACCORDANCE WITH BS EN 1011-1:2009
2. LINEAR DIMS TO BE WITHIN ±1mm;
3. ANGULAR TOLERANCES TO BE WITHIN 0.5°
4. WELDING SYMBOLS ARE IN ACCORDANCE WITH BS EN 22553:1995
5. ALL PROFILE EDGES TO BE DRESSED AND SHARP CORNERS REMOVED
6. ALL WELD SIZES ARE FINAL SIZES
7. ALL WELDED JOINTS ARE TO BE PICKLE TIGHT
8. ALL STEELWORK TO BE BS EN 10025 GRADE S275 J0 UNO & 9. HOT DIPPED GALVANISED TO BS EN ISO 1461. (ALL HOLLOW SECTIONS TO BE GRADE S355 J0H)
10. ALL STEEL IS TO BE SUPPLIED IN ACCORDANCE WITH EN 1090 TO EXECUTION CLASS 2
11. ALL NON PRE-LOADED BOLTS TO BE COMPLIANT STRUCTURAL BOLTS TO BS EN ISO 15048 PARTS 1&2.
12. STEELWORK COMPONENTS SHALL BE HOT DIP GALVANISED TO ACHIEVE A "VERY HIGH" DURABILITY FOR AN ENVIRONMENT CATEGORY CODE C4 FROM TABLE 1 IN BS EN ISO 14713
13. BOLTS AND NUTS SHALL BE SUPPLIED IN ACCORDANCE WITH BS 7371, SPUN GALVANISED IN ACCORDANCE WITH ISO 10684, THE NUTS RE-TAPPED AFTER GALVANISING, AND THE THREADS TREATED WITH GREASE.
14. ALL BOLTS TO BE CUT ON SITE TO EXTEND MAX 10mm BEYOND THE NUT WHEN TIGHTENED UNO.
15. ALL SITE DRILLED HOLE/CUT ENDS TO BE TREATED WITH METAFLUX 70-40 ZINC PASTE FOLLOWED BY 1 COAT OF 7-42 ZINC ALU OR 70-16 ALUMINIUM SPRAY

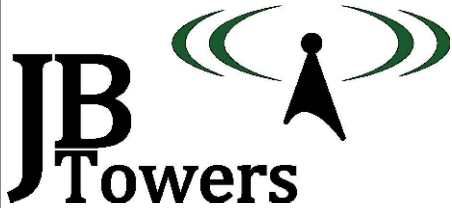

02	NOTES UPDATED			AM	08/05/18
01	FIRST ISSUE			AM	01/05/18
REV	REV			BY	DATE
SCALE AS SHOWN		DRAWN	AM	CHECKED	MP
WHEN PRINTED AT A3		DATE	01/05/18	DATE	01/05/18
		DATE	01/05/18	DATE	01/05/18
ALL DIMENSIONS IN mm UNLESS OTHERWISE STATED. THIS DRAWING TO BE READ IN CONJUNCTION WITH OTHER RELEVANT DRAWINGS.					

TITLE
PARTS LIST

SITE ADDRESS		
EAST DEAN EAST SUSSEX BN20 0JZ		
ARQIVA REF. 140649	DRG No. 305	REV 02

ALL SCALES AS SHOWN WHEN PRINTED AT A3



ALL SCALES AS SHOWN WHEN PRINTED AT A3