


DRAWING ISSUE SHEET

[illegible]

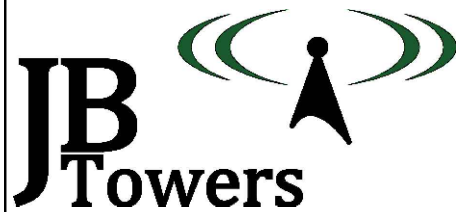

03	MINOR AMENDMENTS		AM	25/07/18	
02	LEAD CAP REMOVED		AM	30/05/18	
01	FIRST ISSUE		AM	22/05/18	
REV	REV		BY	DATE	
SCALE AS SHOWN WHEN PRINTED AT A3	DRAWN AM	CHECKED MP	APPROVED JBT		
	DATE 22/05/18	DATE 22/05/18	DATE 22/05/18		
ALL DIMENSIONS IN mm UNLESS OTHERWISE STATED. THIS DRAWING TO BE READ IN CONJUNCTION WITH OTHER RELEVANT DRAWINGS.					

TITLE


SALTDEAN

GENERAL ARRANGEMENT
SHEET 1 OF 3

SITE ADDRESS

COOMBE FARM
SALTDEAN
BRIGHTON
EAST SUSSEX
BN2 8HE

ARQIVA REF. 141568	DRG No. 200	REV 03
-----------------------	----------------	-----------

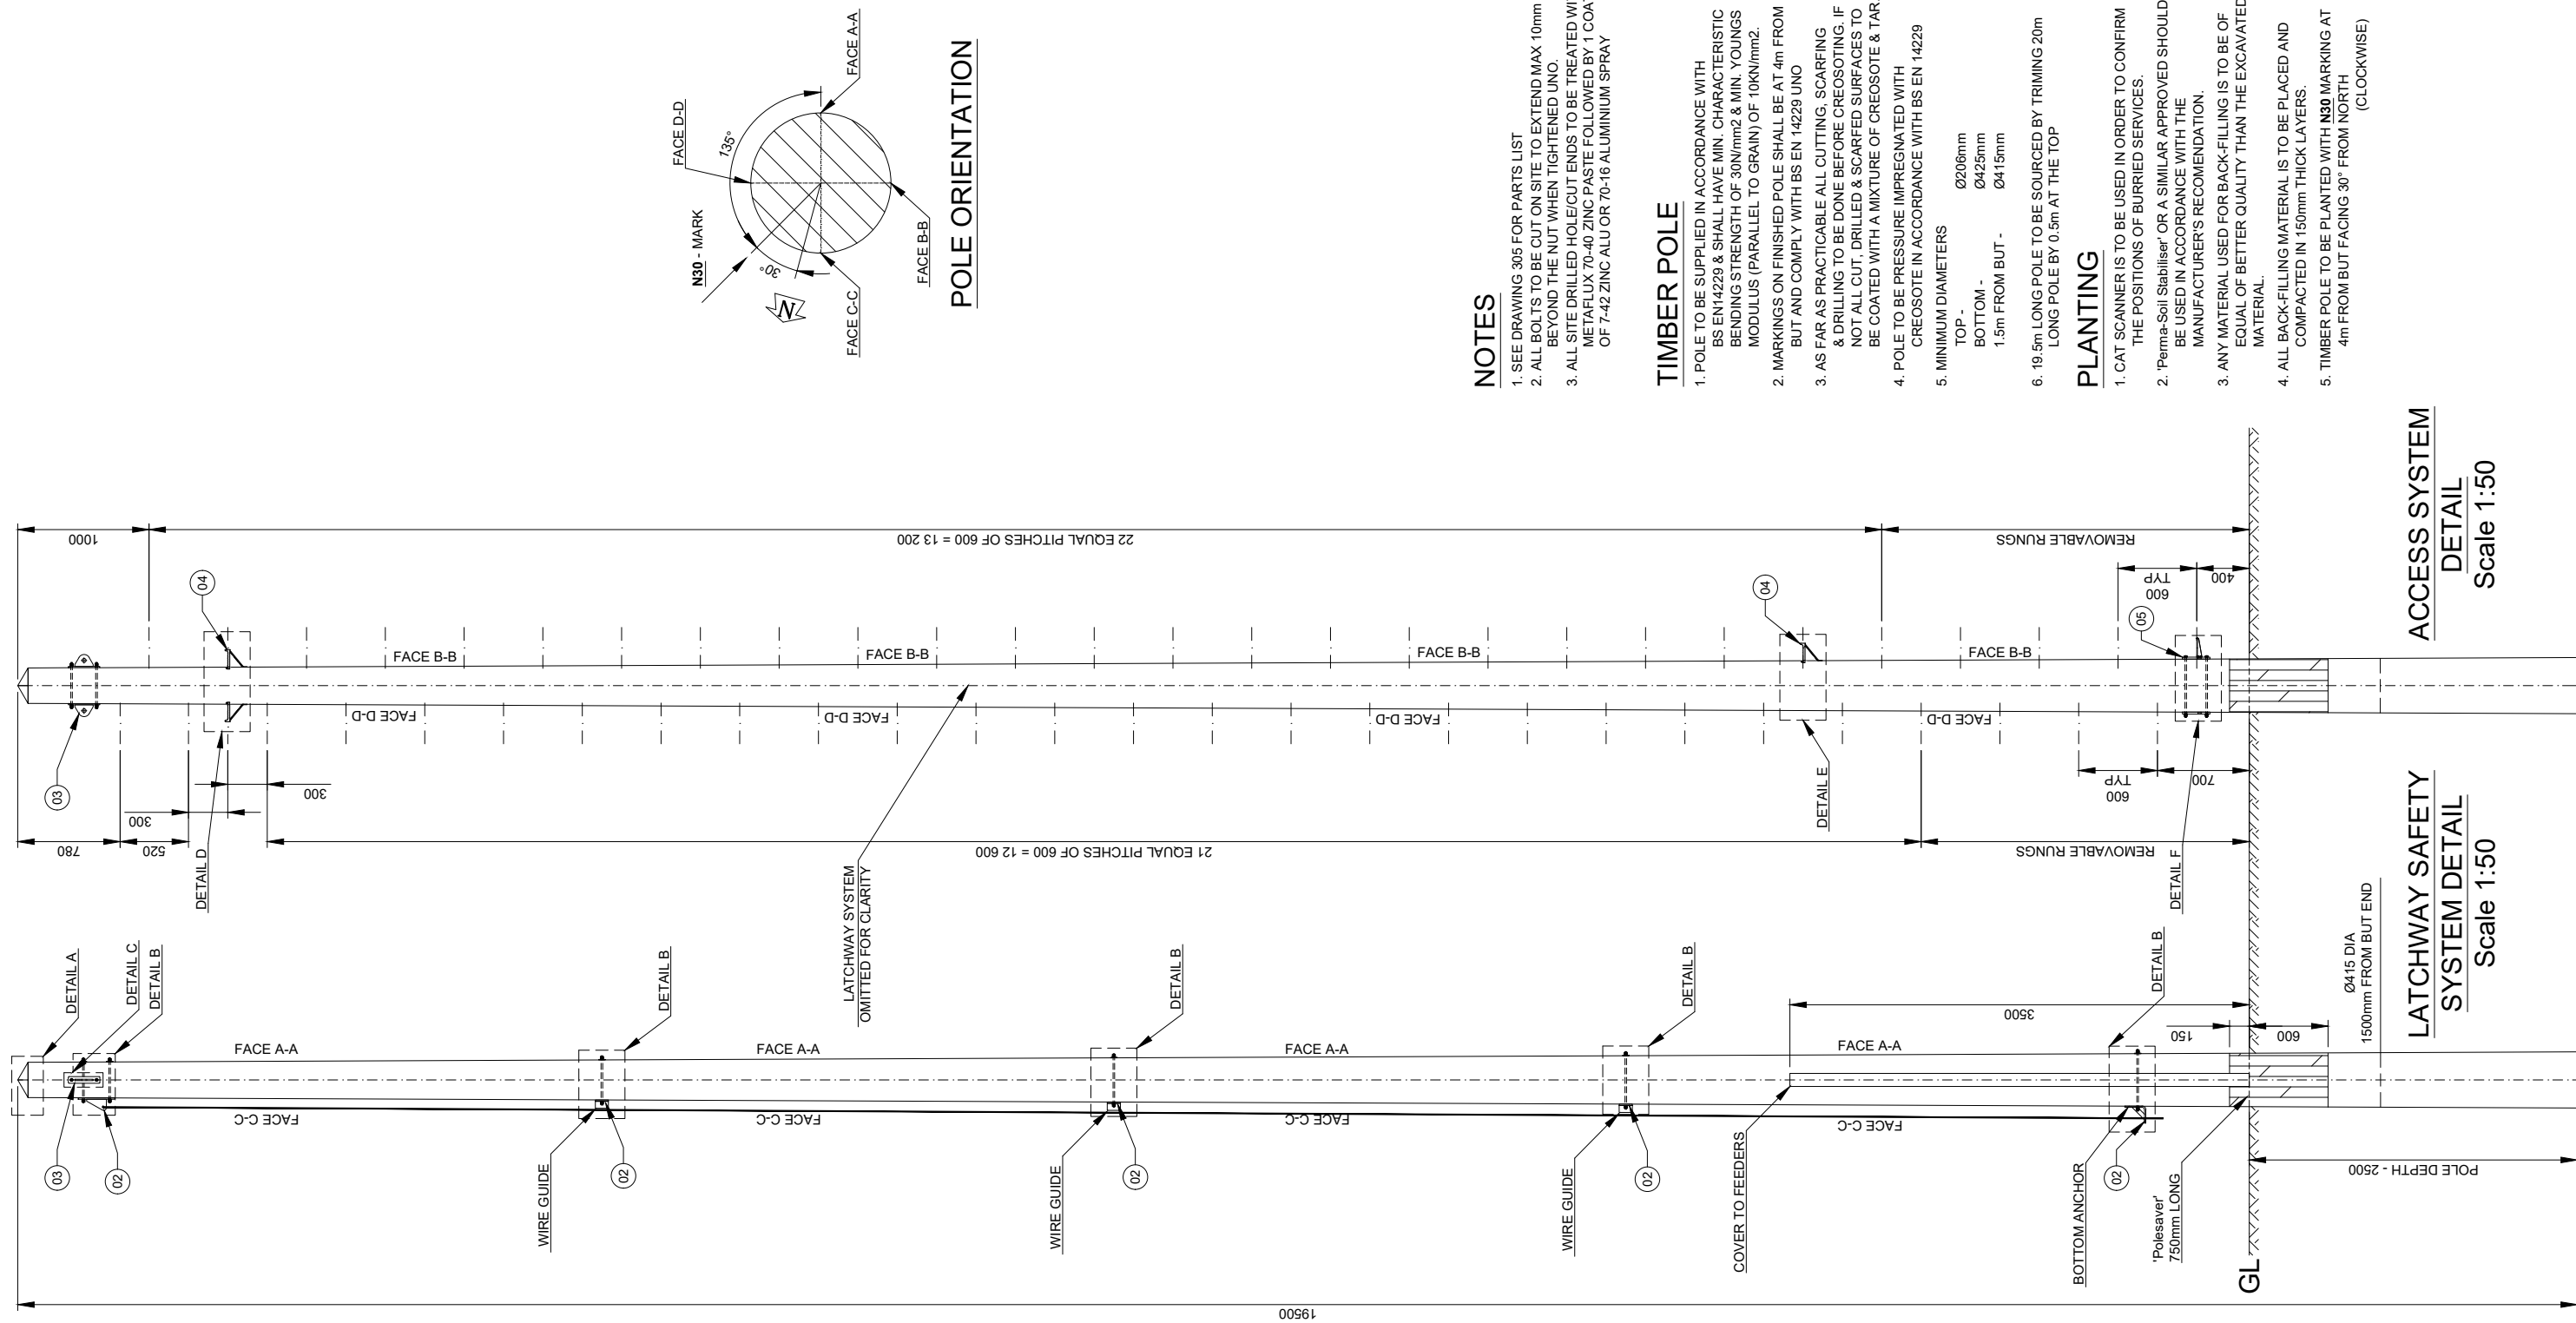

POLE ORIENTATION

NOTES

1. SEE DRAWING 305 FOR PARTS LIST
2. ALL BOLTS TO BE CUT ON SITE TO EXTEND MAX 10mm BEYOND THE NUT WHEN TIGHTENED UNO.
3. ALL SITE DRILLED HOLE/CUT ENDS TO BE TREATED WITH METAFLUX 70-40 ZINC PASTE FOLLOWED BY 1 COAT OF 7-42 ZINC ALU OR 70-16 ALUMINIUM SPRAY


TIMBER POLE

1. POLE TO BE SUPPLIED IN ACCORDANCE WITH BS EN14229 & SHALL HAVE MIN. CHARACTERISTIC BENDING STRENGTH OF 30N/mm² & MIN. YOUNGS MODULUS (PARALLEL TO GRAIN) OF 10KN/mm².
2. MARKINGS ON FINISHED POLE SHALL BE AT 4m FROM BUT AND COMPLY WITH BS EN 14229 UNO
3. AS FAR AS PRACTICABLE ALL CUTTING, SCARFING & DRILLING TO BE DONE BEFORE CREOSOTING. IF NOT ALL CUT, DRILLED & SCARFED SURFACES TO BE COATED WITH A MIXTURE OF CREOSOTE & TAR.
4. POLE TO BE PRESSURE IMPREGNATED WITH CREOSOTE IN ACCORDANCE WITH BS EN 14229
5. MINIMUM DIAMETERS
TOP - Ø206mm
BOTTOM - Ø425mm
1.5m FROM BUT - Ø415mm
6. 19.5m LONG POLE TO BE SOURCED BY TRIMMING 20m LONG POLE BY 0.5m AT THE TOP




PLANTING

1. CAT SCANNER IS TO BE USED IN ORDER TO CONFIRM THE POSITIONS OF BURIED SERVICES.
2. 'Perma-Soil Stabiliser' OR A SIMILAR APPROVED SHOULD BE USED IN ACCORDANCE WITH THE MANUFACTURER'S RECOMMENDATION.
3. ANY MATERIAL USED FOR BACK-FILLING IS TO BE OF EQUAL OR BETTER QUALITY THAN THE EXCAVATED MATERIAL.
4. ALL BACK-FILLING MATERIAL IS TO BE PLACED AND COMPACTED IN 150mm THICK LAYERS.
5. TIMBER POLE TO BE PLANTED WITH **N30** MARKING AT 4m FROM BUT FACING 30° FROM NORTH (CLOCKWISE)

ALL SCALES AS SHOWN WHEN PRINTED AT A3

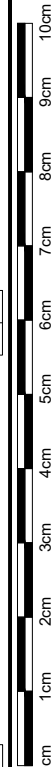

ALL SCALES AS SHOWN WHEN PRINTED AT A3

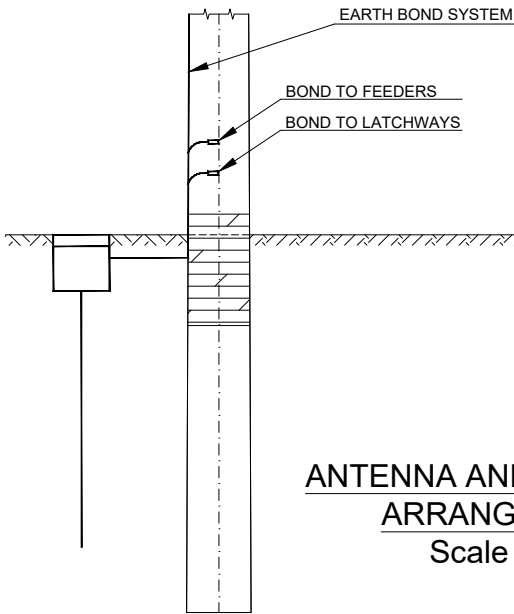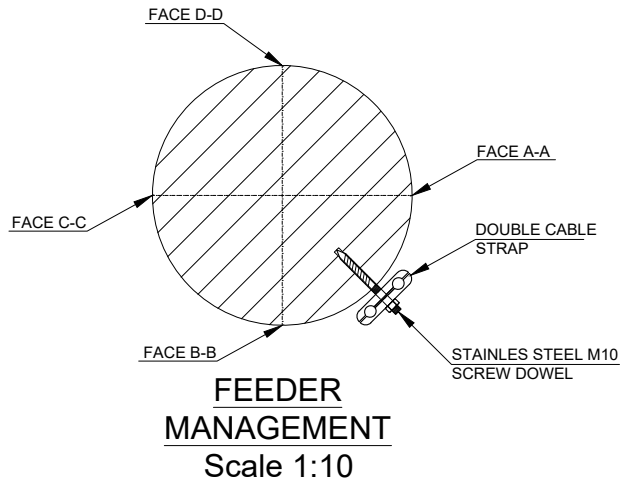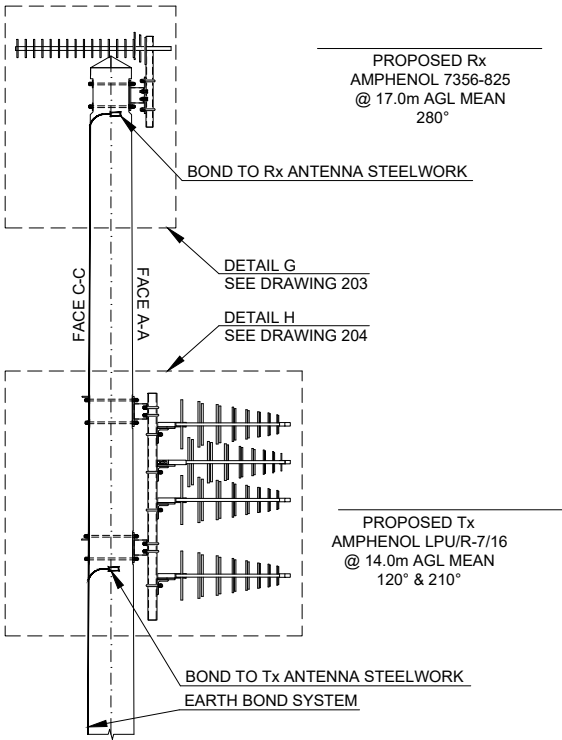

NOTES


1. AS FAR AS IS PRACTICABLE ALL CUTTING SCARFING AND DRILLING TO BE DONE BEFORE CREOSOTING. WHERE THIS IS NOT POSSIBLE ALL CUT, DRILLED, AND SCARFED SURFACES TO BE COATED WITH A MIXTURE OF CREOSOTE AND TAR

FEEDERS

1. SUPPLY OF FEEDERS BY OTHERS
LCF78-50 TO Tx ANTENNA &
LCF12-50 TO Rx ANTENNA
2. FEEDERS FIXED AT 1000mm CENTRES

EARTHING

1. CONNECT EARTH BOND TO NEW EARTHING SYSTEM
2. MAXIMUM VALUE FOR GROUND RESISTANCE TO BE 10 OHMS
3. CABLE OR TAPE TO BE FIXED TO POLE AT 1000mm CENTRES
4. EARTHING SHOULD COMPLY WITH ARQIVA'S DOCUMENT BOS147
5. THE POSITION OF THE EARTH BOND SYSTEM ALONG THE HEIGHT OF THE POLE IS TO BE DETERMINED ON SITE

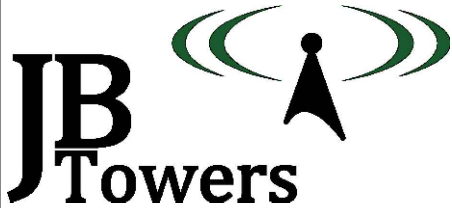


03	MINOR AMENDMENTS			AM	25/07/18
02	LABELS AMENDED			AM	30/05/18
01	FIRST ISSUE			AM	22/05/18
REV	REV			BY	DATE
SCALE AS SHOWN		DRAWN	AM	CHECKED	MP
WHEN PRINTED AT A3		DATE	22/05/18	DATE	22/05/18
		DATE	22/05/18	DATE	22/05/18
ALL DIMENSIONS IN mm UNLESS OTHERWISE STATED. THIS DRAWING TO BE READ IN CONJUNCTION WITH OTHER RELEVANT DRAWINGS.					

TITLE
SALTDEAN
GENERAL ARRANGEMENT
SHEET 2 OF 3


SITE ADDRESS
COOMBE FARM
SALTDEAN
BRIGHTON
EAST SUSSEX
BN2 8HE

ARQIVA REF.
141568
DRG No.
200
REV
03

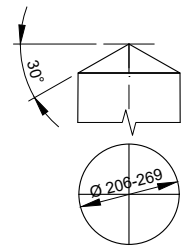


- NOTES:
1. A SINGLE COAT OF TIMBER COMPATIBLE BITUMINOUS PAINT (E.G. BIRD BRAND BLACK BITUMINOUS PAINT OR SIMILAR APPROVED PRODUCT) TO BE APPLIED TO THE UPPER SURFACES AT THE TOP OF THE POLE.
 2. PAINT TO BE APPLIED ON SITE JUST BEFORE ERECTION
- FORM: 4 WAY PYRAMID / CONE


DETAIL A - TIMBER POLE TOP
Scale 1:20

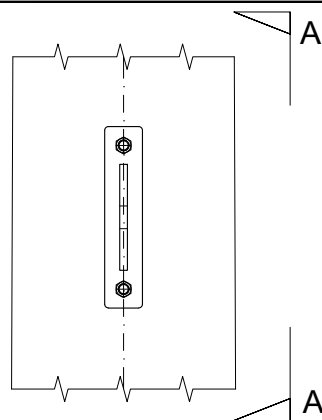


DETAIL C - FALL ARREST
ATTACHMENT POINT
Scale 1:10

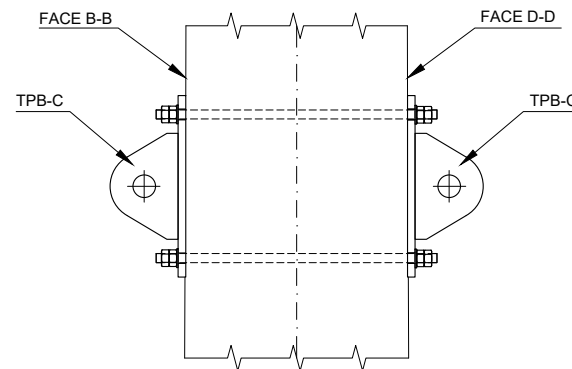

VIEW A-A
Scale 1:10

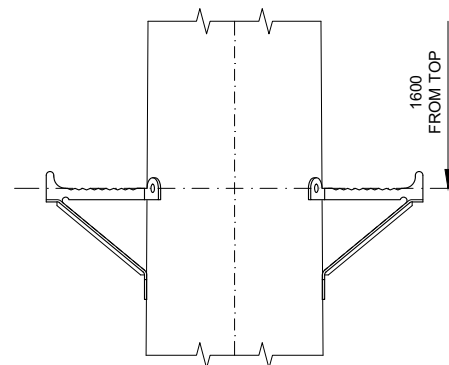


DETAIL D - ANTENNA
ACCESS CLIMBING STEP
Scale 1:10

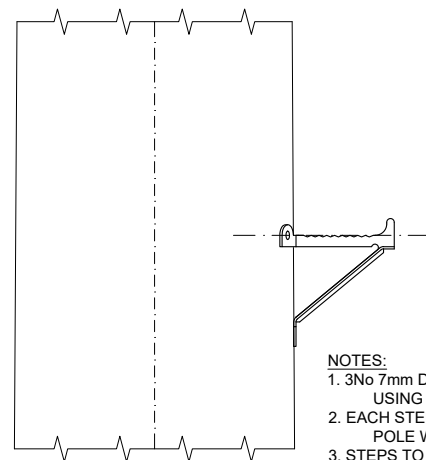


DETAIL E - PERMANENT
CLIMBING STEPS
Scale 1:10


- NOTES:
1. 3No 7mm DIA 70mm LONG PILOT HOLES TO BE DRILLED USING THE STEP AS A TEMPLATE
 2. EACH STEP SHOULD BE FIXED TO THE TIMBER POLE WITH 3No 10mm COACH SCREWS 75mm LONG
 3. STEPS TO BE INSTALLED ON FACES B-B & D-D ONLY

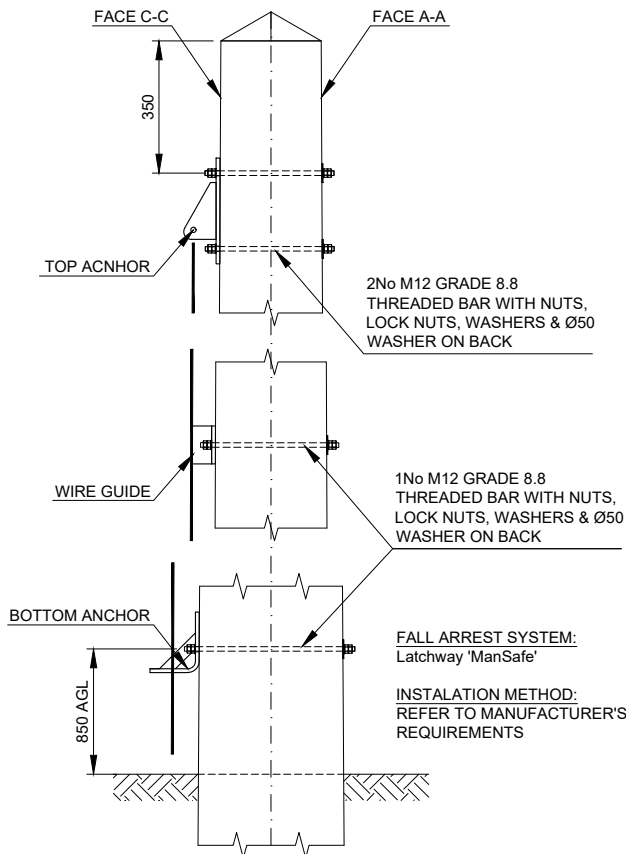

DETAIL B - FALL ARREST SYSTEM
Scale 1:20

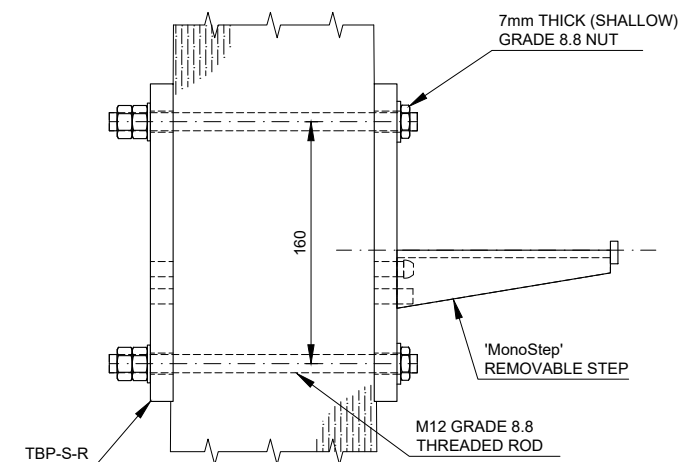

DETAIL F - REMOVABLE
CLIMBING STEPS
Scale 1:5

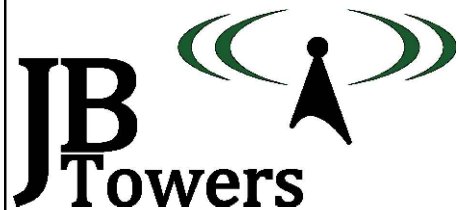

03	DETAILS C; D; E & F UPDATED	AM	25/07/18
02	CLIMBING STEP DETAILS UPDATED	AM	30/05/18
01	FIRST ISSUE	AM	22/05/18
REV	REV	BY	DATE
SCALE AS SHOWN WHEN PRINTED AT A3	DRAWN DATE 22/05/18	CHECKED DATE 22/05/18	APPROVED DATE 22/05/18
ALL DIMENSIONS IN mm UNLESS OTHERWISE STATED. THIS DRAWING TO BE READ IN CONJUNCTION WITH OTHER RELEVANT DRAWINGS.			

TITLE
SALTDEAN
GENERAL ARRANGEMENT
SHEET 3 OF 3


SITE ADDRESS
COOMBE FARM
SALTDEAN
BRIGHTON
EAST SUSSEX
BN2 8HE

ARQIVA REF.
141568
DRG No.
200
REV
03

ALL SCALES AS SHOWN WHEN PRINTED AT A3



ALL SCALES AS SHOWN WHEN PRINTED AT A3

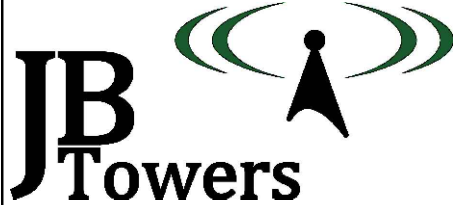

03	MINOR AMENDMENTS			AM	25/07/18
02	DETAIL LABELS UPDATED			AM	30/05/18
01	FIRST ISSUE			AM	22/05/18
REV	REV			BY	DATE
SCALE AS SHOWN		DRAWN	AM	CHECKED	MP
WHEN PRINTED AT A3		DATE	22/05/18	DATE	22/05/18
		APPROVED	JBT	DATE	22/05/18
ALL DIMENSIONS IN mm UNLESS OTHERWISE STATED. THIS DRAWING TO BE READ IN CONJUNCTION WITH OTHER RELEVANT DRAWINGS.					

TITLE

SALTDEAN

TIMBER POLE HOLE SET OUT

SHEET 1 OF 2

SITE ADDRESS

COOMBE FARM

SALTDEAN

BRIGHTON

EAST SUSSEX

BN2 8HE

ARQIVA REF.



141568

DRG No.

201


REV

03

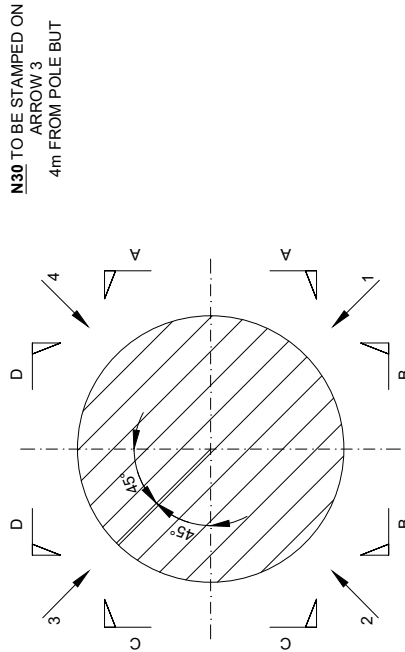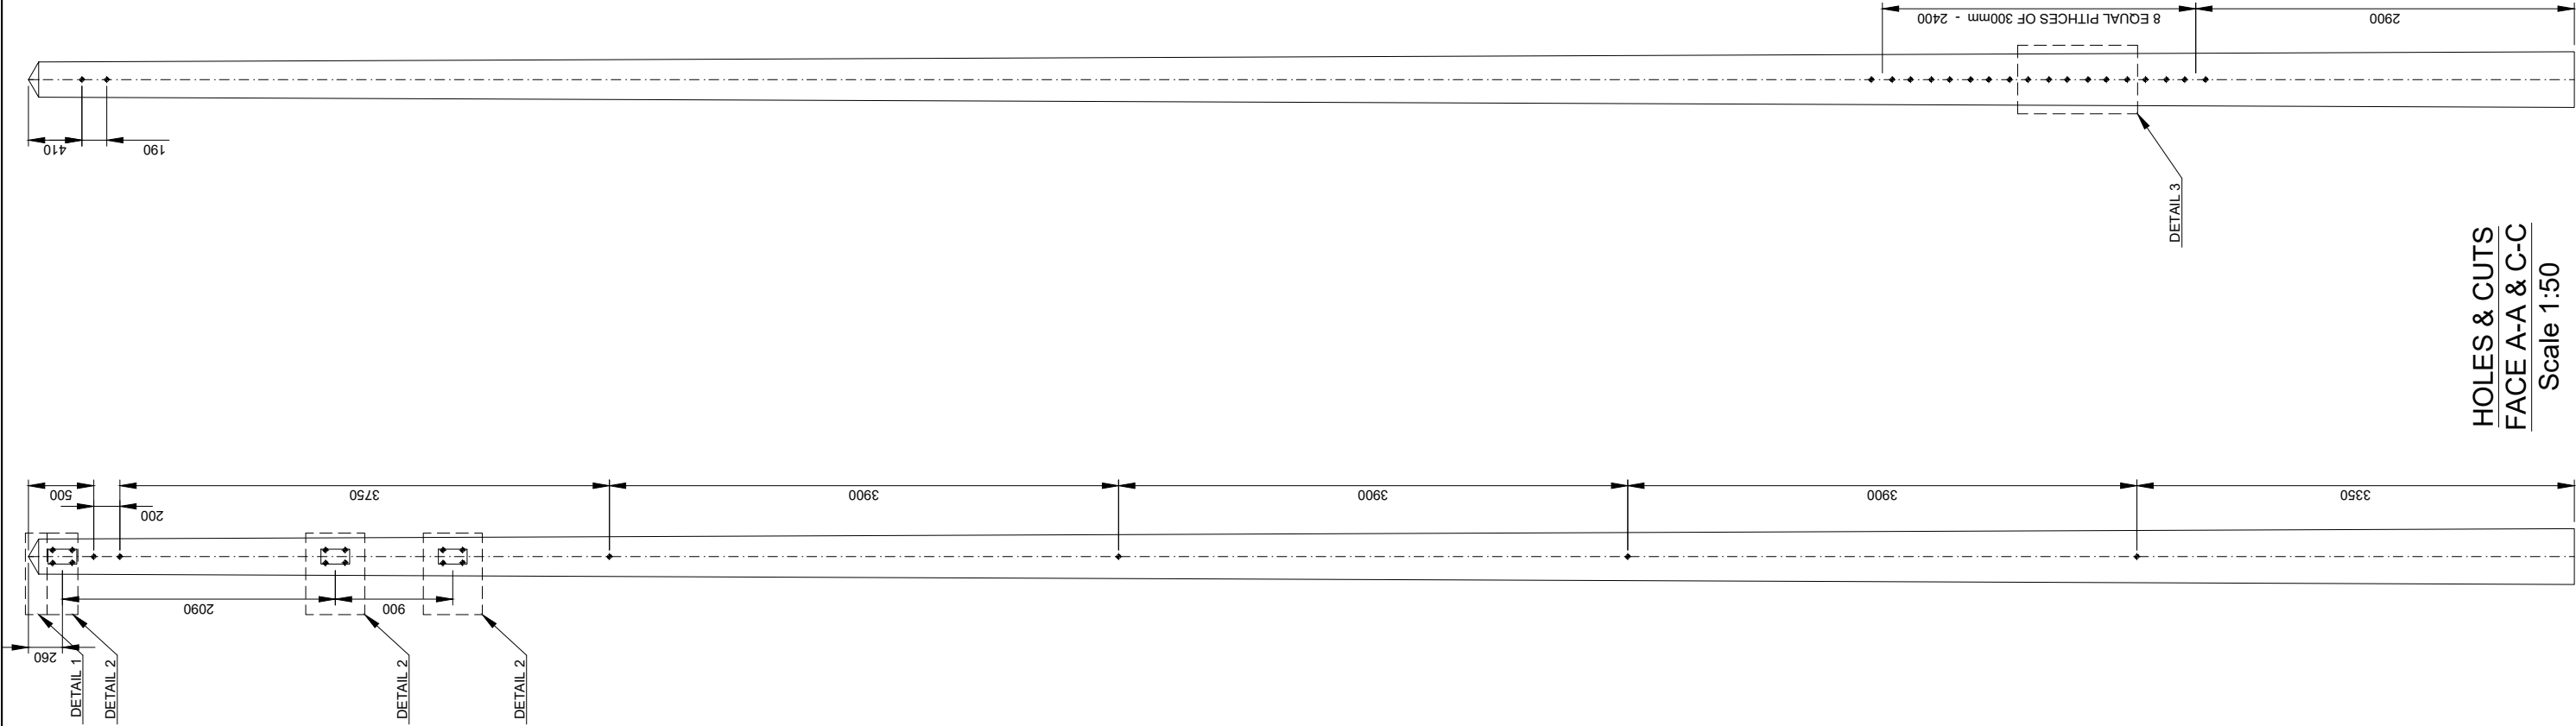


TIMBER POLE
FACE NOMENCLATURE

Scale 1:20

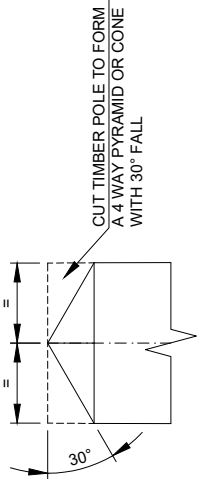

DETAIL 1


Scale 1:10

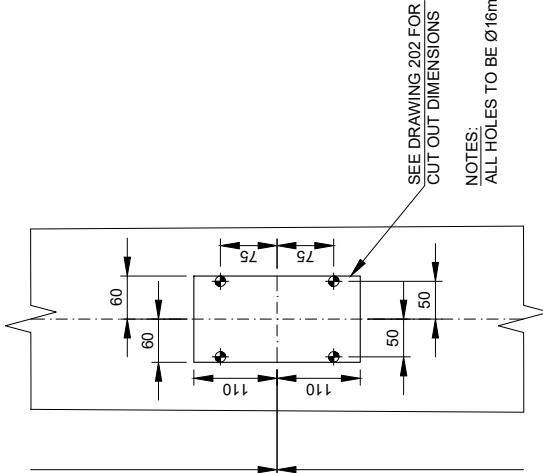

NOTES:
ALL HOLES TO BE Ø16mm THROUGH HOLES

DETAIL 2 - TYPICAL

Scale 1:10

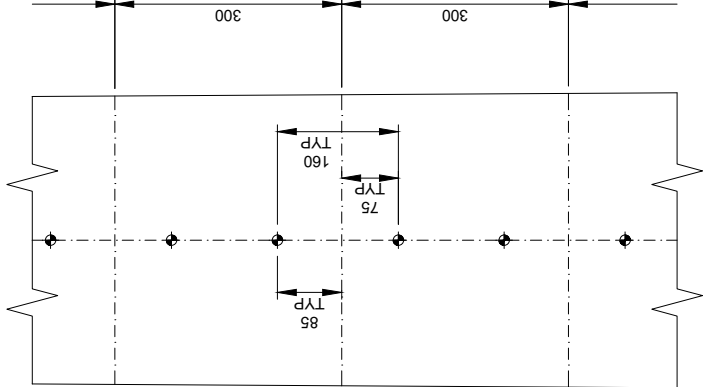

DETAIL 3 - TYPICAL

Scale 1:10



HOLES
FACE B-B & D-D


Scale 1:50

HOLES & CUTS
FACE A-A & C-C

Scale 1:50

ALL SCALES AS SHOWN WHEN PRINTED AT A3


ALL SCALES AS SHOWN WHEN PRINTED AT A3

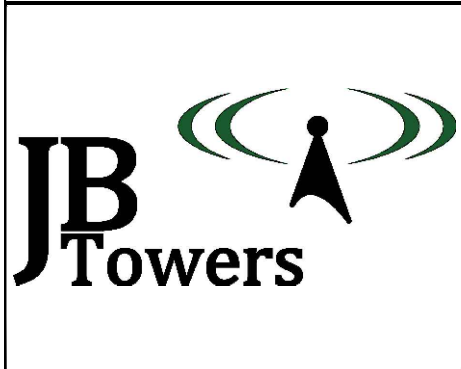


01	FIRST ISSUE			AM	22/05/18
REV	REV			BY	DATE
SCALE AS SHOWN		DRAWN	AM	CHECKED	MP
WHEN PRINTED AT A3		DATE	22/05/18	DATE	22/05/18
		DATE	22/05/18	DATE	22/05/18
ALL DIMENSIONS IN mm UNLESS OTHERWISE STATED. THIS DRAWING TO BE READ IN CONJUNCTION WITH OTHER RELEVANT DRAWINGS.					

TITLE
SALTDEAN
TIMBER POLE HOLE SET OUT
SHEET 2 OF 2

SITE ADDRESS		
COOMBE FARM SALTDEAN BRIGHTON EAST SUSSEX BN2 8HE		
ARQIVA REF. 141568	DRG No. 201	REV 01

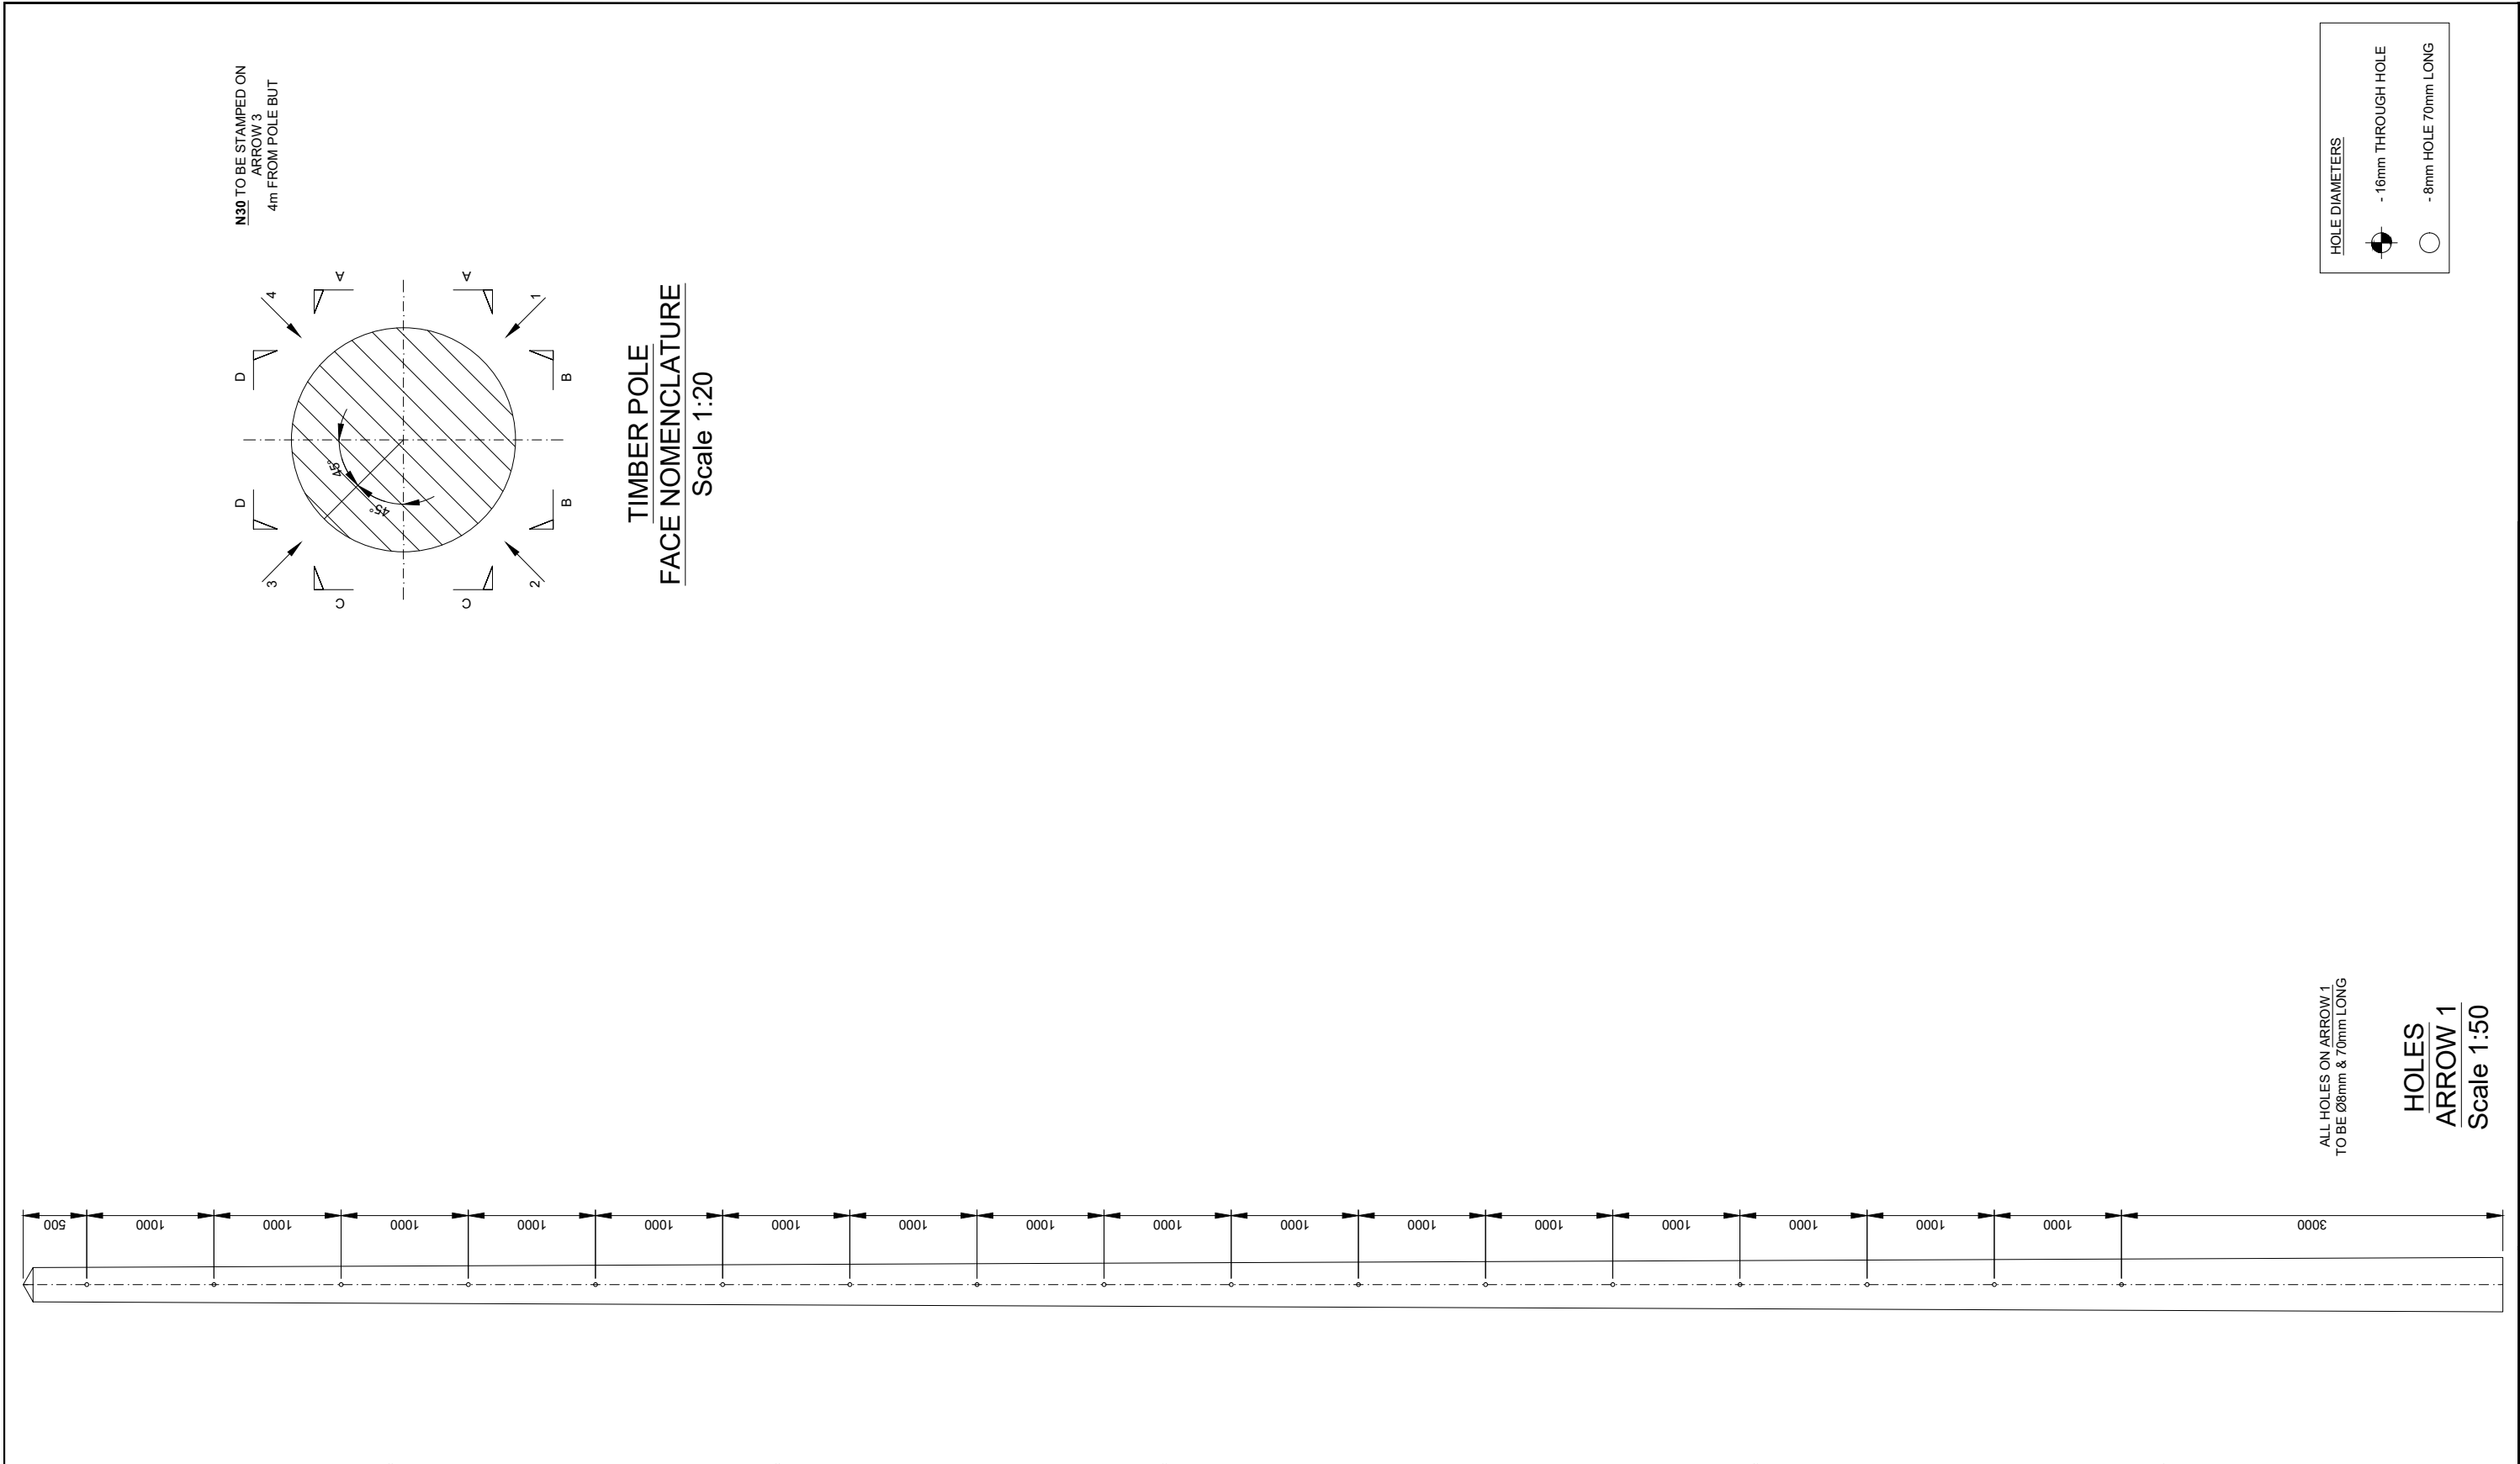

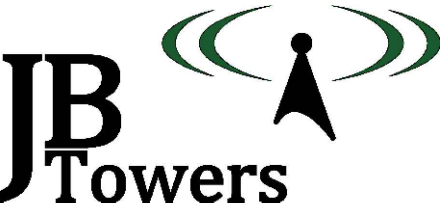


01	FIRST ISSUE			AM	22/05/18
REV	REV			BY	DATE
SCALE AS SHOWN		DRAWN	AM	CHECKED	MP
WHEN PRINTED AT A3		DATE	22/05/18	DATE	22/05/18
		APPROVED	JBT	DATE	22/05/18
ALL DIMENSIONS IN mm UNLESS OTHERWISE STATED. THIS DRAWING TO BE READ IN CONJUNCTION WITH OTHER RELEVANT DRAWINGS.					

TITLE

SALTDEAN

TIMBER POLE CUT OUT
DETAIL


SITE ADDRESS		
COOMBE FARM SALTDEAN BRIGHTON EAST SUSSEX BN2 8HE		
ARQIVA REF. 141568	DRG No. 202	REV 01

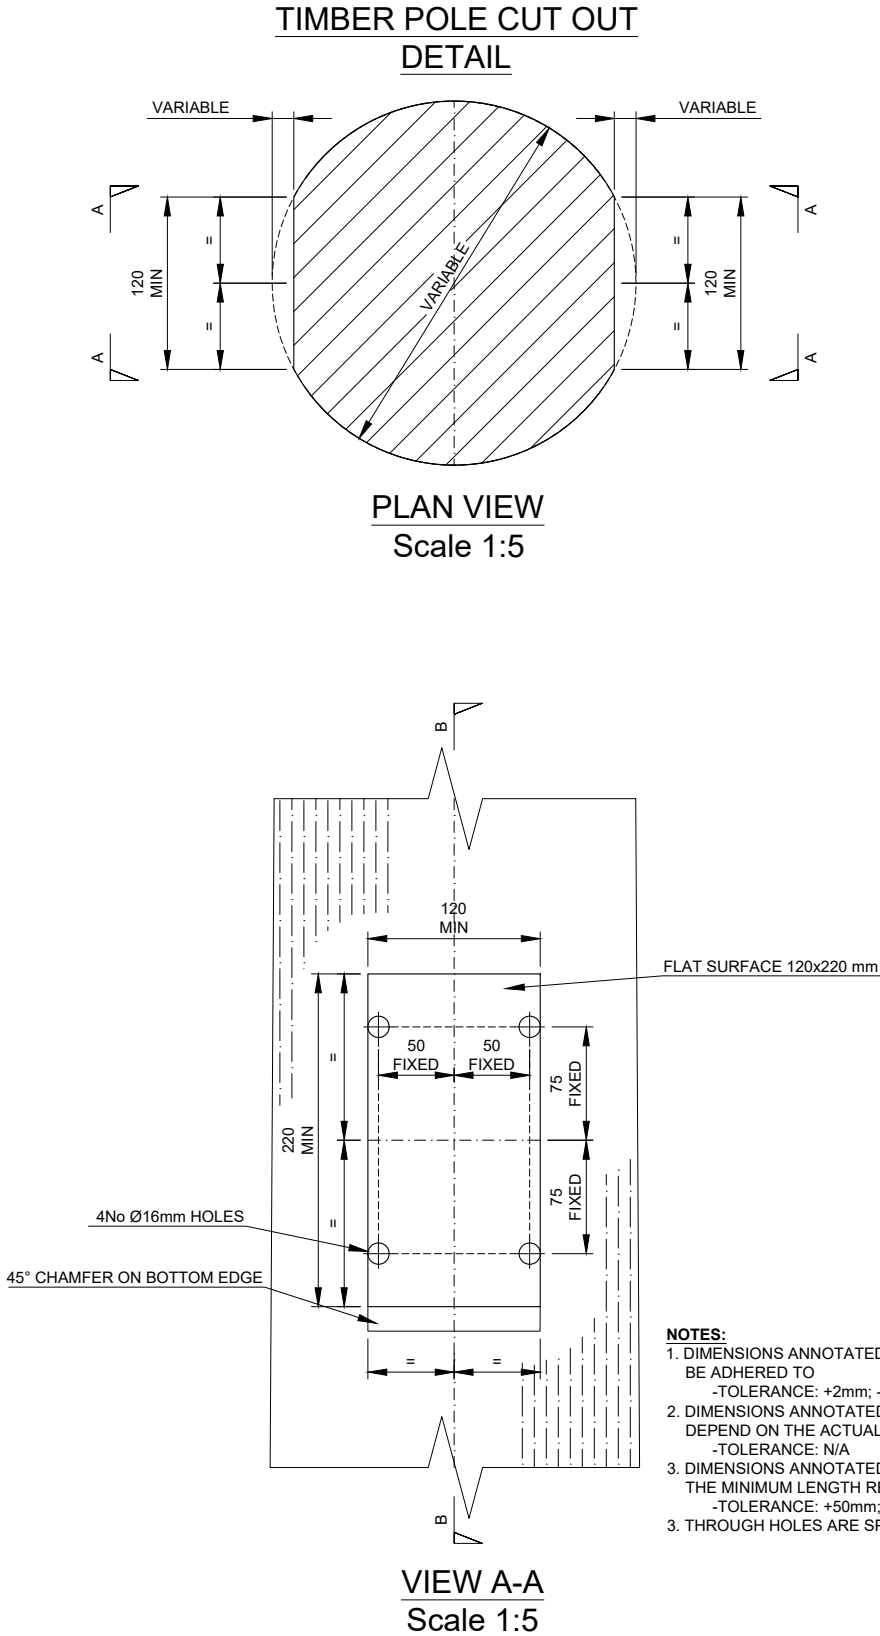

ALL SCALES AS SHOWN WHEN PRINTED AT A3



ALL SCALES AS SHOWN WHEN PRINTED AT A3

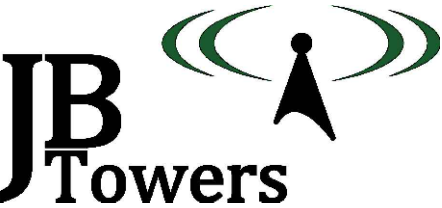

01		FIRST ISSUE			AM	22/05/18
REV		REV			BY	DATE
SCALE AS SHOWN		DRAWN	AM	CHECKED	MP	APPROVED JBT
WHEN PRINTED AT A3		DATE	22/05/18	DATE	22/05/18	DATE 22/05/18
ALL DIMENSIONS IN mm UNLESS OTHERWISE STATED. THIS DRAWING TO BE READ IN CONJUNCTION WITH OTHER RELEVANT DRAWINGS.						


TITLE
ANTENNA MOUNT
DETAIL G

SITE ADDRESS
COOMBE FARM
SALTDEAN
BRIGHTON
EAST SUSSEX
BN2 8HE


ARQIVA REF.
141568

DRG No.
203

REV
01

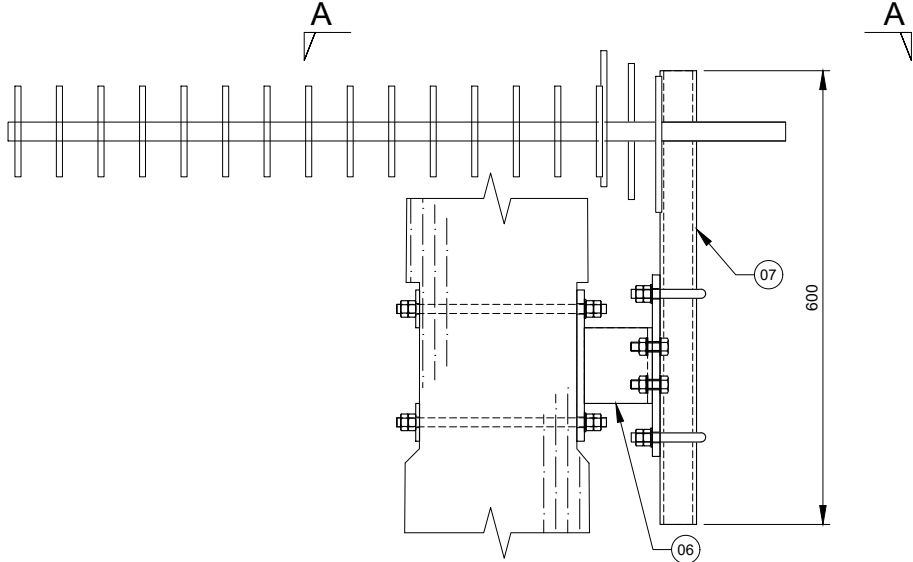

DETAIL G - Rx ANTENNA MOUNT
Scale 1:10

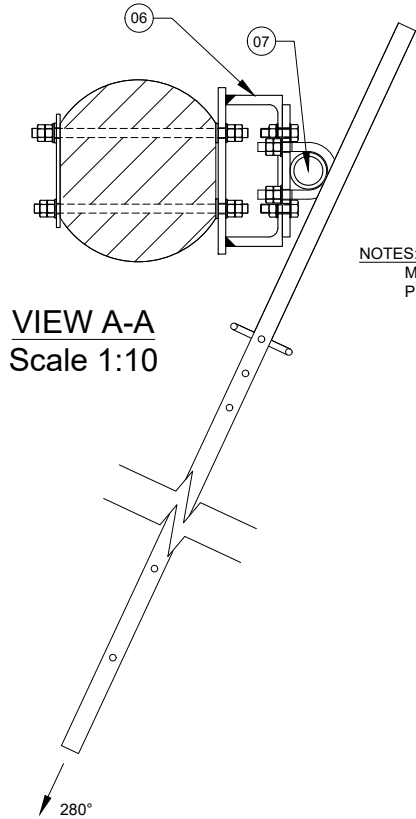


VIEW A-A
Scale 1:10

NOTES:
MOUNTING BRACKET FOR CHS Ø48.3 TO BE
PROVIDED BY THE ANTENNA MANUFACTURER




ALL SCALES AS SHOWN WHEN PRINTED AT A3


ALL SCALES AS SHOWN WHEN PRINTED AT A3

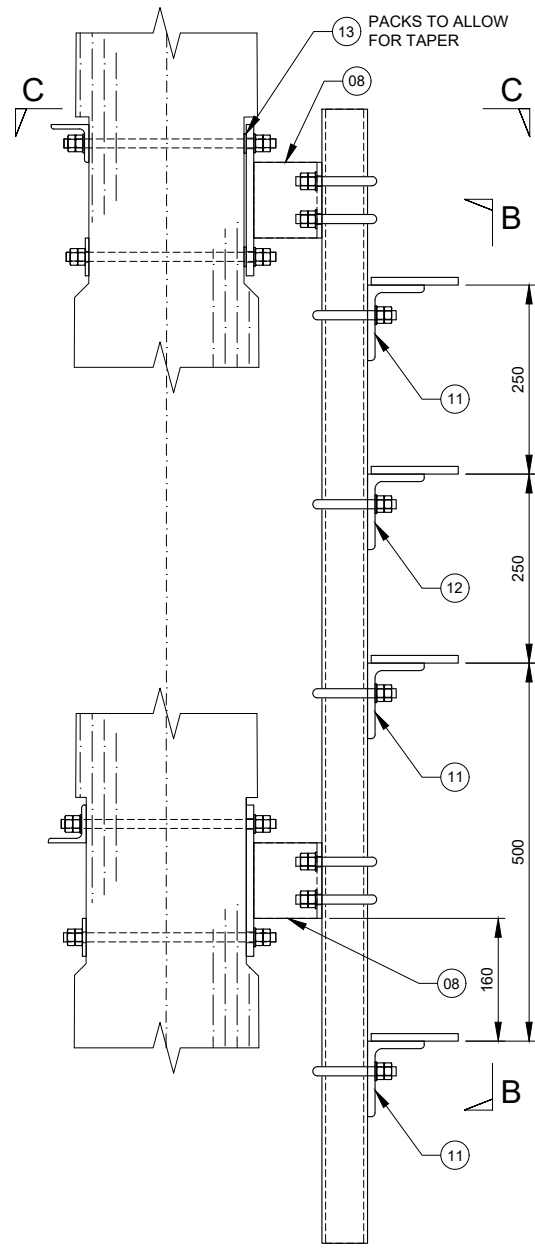

DETAIL H - Tx ANTENNA MOUNT
Scale 1:10

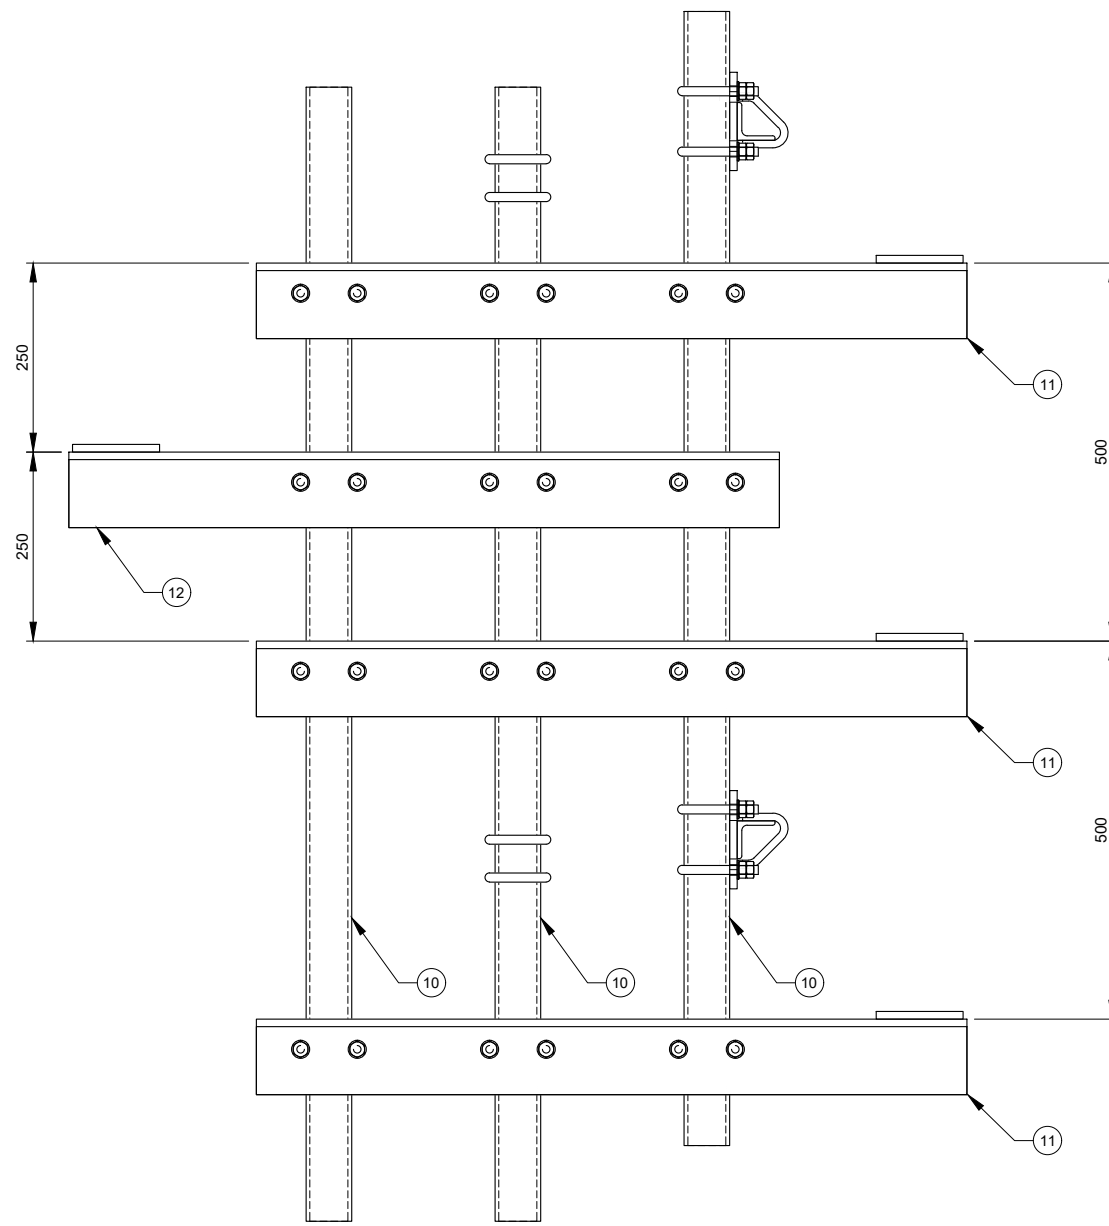

VIEW B-B
Scale 1:10

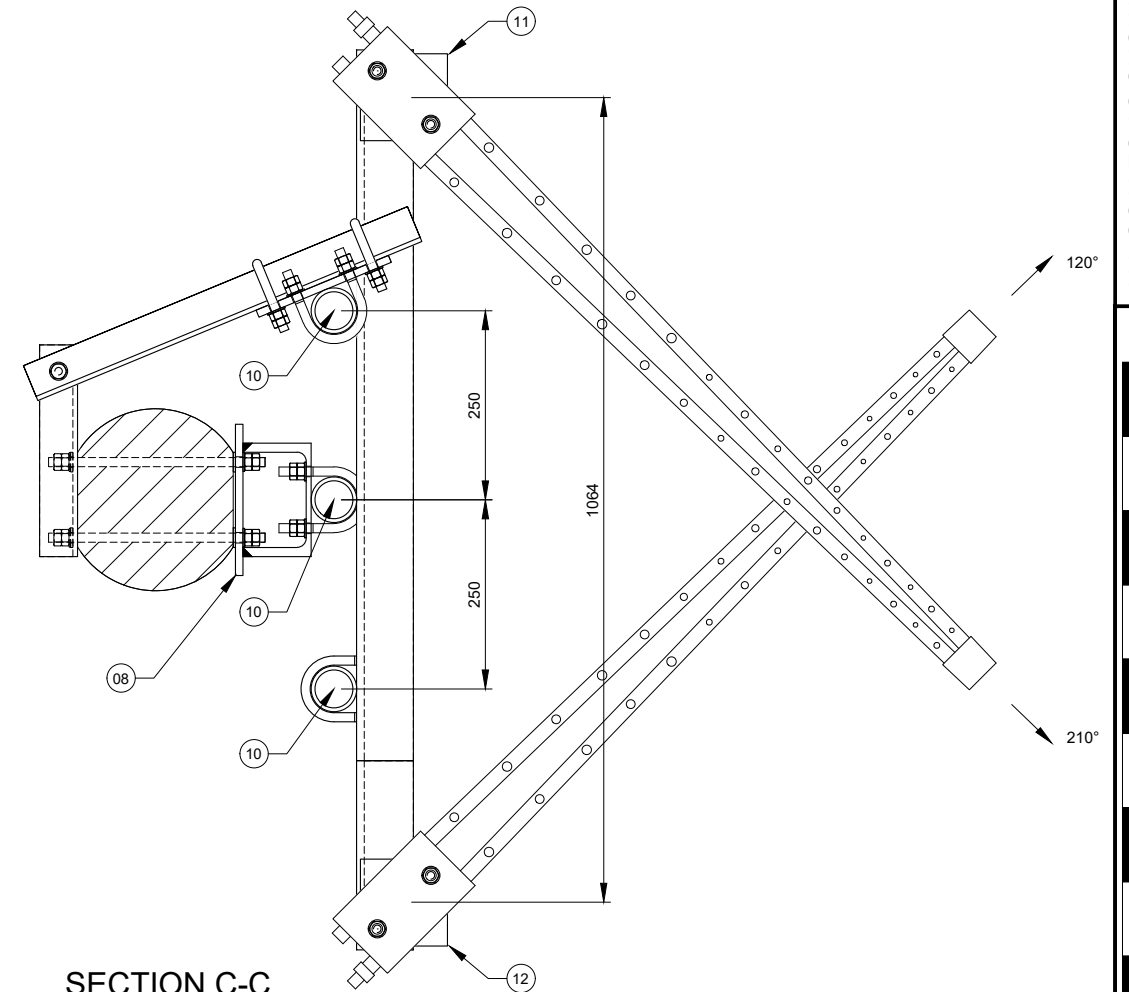


SECTION C-C
Scale 1:10



ALL SCALES AS SHOWN WHEN PRINTED AT A3

ALL SCALES AS SHOWN WHEN PRINTED AT A3

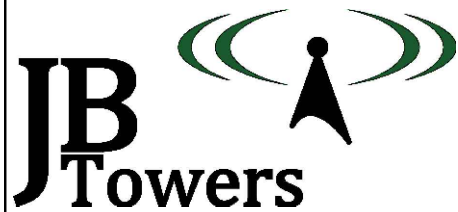

01	FIRST ISSUE				AM	22/05/18
REV	REV				BY	DATE
SCALE AS SHOWN		DRAWN	AM	CHECKED	MP	APPROVED JBT
WHEN PRINTED AT A3		DATE	22/05/18	DATE	22/05/18	DATE 22/05/18
ALL DIMENSIONS IN mm UNLESS OTHERWISE STATED.						THIS DRAWING TO BE READ IN CONJUNCTION WITH OTHER RELEVANT DRAWINGS.


TITLE
ANTENNA MOUNT
DETAIL H

SITE ADDRESS
COOMBE FARM
SALTDEAN
BRIGHTON
EAST SUSSEX
BN2 8HE

ARQIVA REF.
141568


DRG No.
204

REV
01

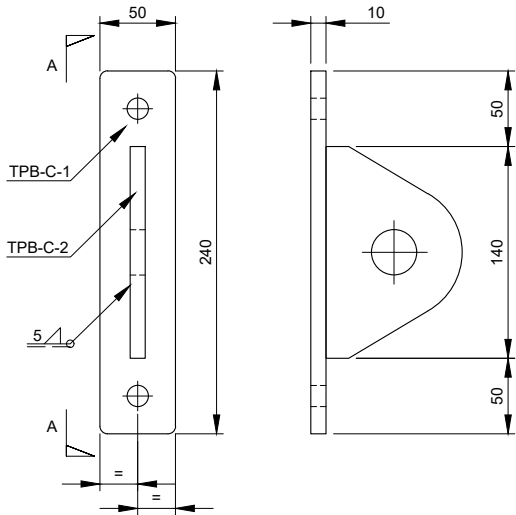

PART TPB-C
Scale 1:5

VIEW A-A
Scale 1:5

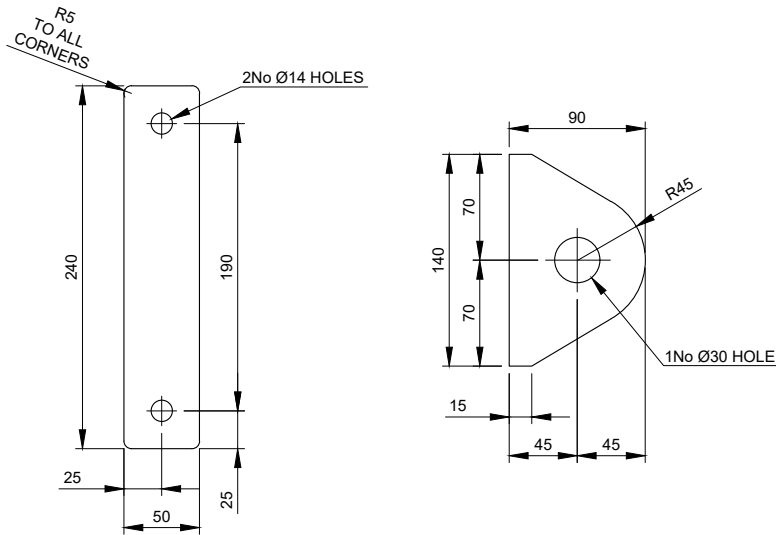

TPB-C-1 - 10mm THICK
Scale 1:5

TPB-C-2 - 10mm THICK
Scale 1:5

Parts list for TPB-C


Item	Part	Quantity	Part description	Length	Material	Weight
01	TPB-C-1	1	240x50x10mm	N/A	S275J0	0.94 kg
02	TPB-C-2	1	140x90x10mm	N/A	S275J0	0.99 kg
03	STUDS	1	M12 STUDDING	350mm	GRADE 8.8	0.31 kg
Total Weight:						2.24 kg

- All steel hot dip galvanized
- Each STUD to be supplied with 4 Full Nuts, 2 Flat Washers and 2 Spring Washers
- For fabrctation notes see drawing 305


Parts list for TPS-R

Item	Part	Quantity	Part description	Length	Material	Weight
01	TPS-R	2	210x60x15mm	N/A	S275J0	1.48 kg
02	STUDS	2	M12 STUDDING	500mm	GRADE 8.8	0.44 kg
03	NUT-S	2	M12 SHALLOW NUT	N/A	GRADE 8.8	-
04	NUT	4	M12 NUT	N/A	GRADE 8.8	-
03	WSH	4	M12 WASHER	N/A	GRADE 8.8	-
Total Weight:						3.40 kg

- All steel hot dip galvanized
- For fabrctation notes see drawing 305

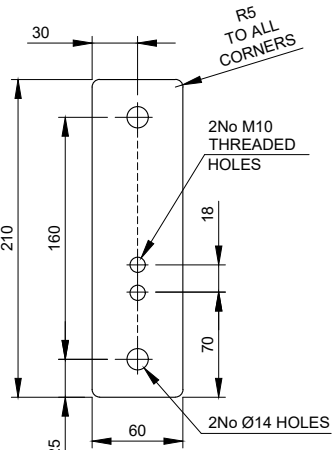

PART TPS-R
Scale 1:5

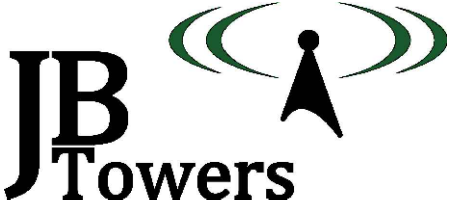

03	TPS-R UPDATED			AM	25/07/18
02	PERMANENT STEP RUNG REMOVED			AM	30/05/18
01	FIRST ISSUE			AM	22/05/18
REV	REV			BY	DATE
SCALE AS SHOWN WHEN PRINTED AT A3		DRAWN AM DATE 22/05/18	CHECKED MP DATE 22/05/18	APPROVED JBT DATE 22/05/18	
ALL DIMENSIONS IN mm UNLESS OTHERWISE STATED. THIS DRAWING TO BE READ IN CONJUNCTION WITH OTHER RELEVANT DRAWINGS.					

TITLE
ATTACHMENT POINT &
TEMPORARY STEP DETAILS
PARTS: TPB-C; TPS-R

SITE ADDRESS
COOMBE FARM
SALTDEAN
BRIGHTON
EAST SUSSEX
BN2 8HE

ARQIVA REF.
141568










DRG No.
300

REV
03

ALL SCALES AS SHOWN WHEN PRINTED AT A3



ALL SCALES AS SHOWN WHEN PRINTED AT A3

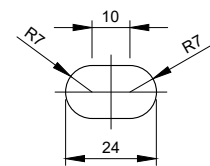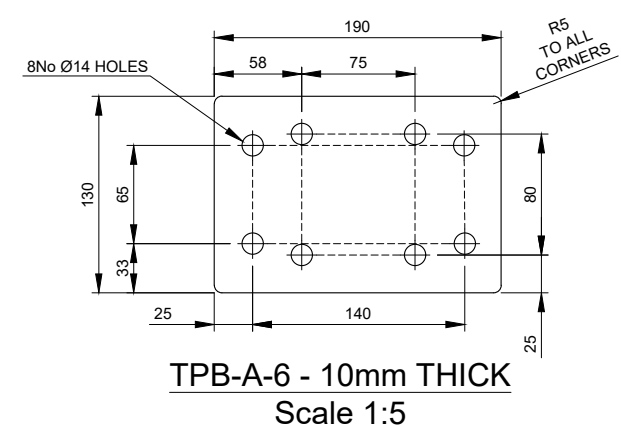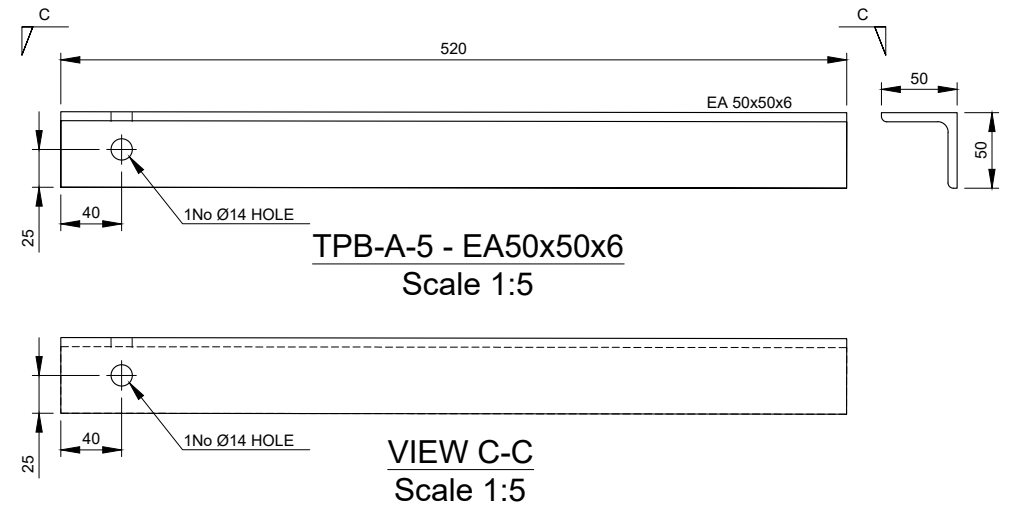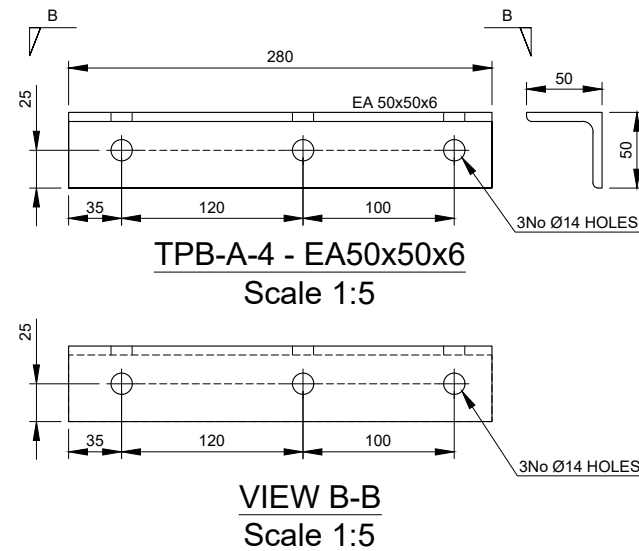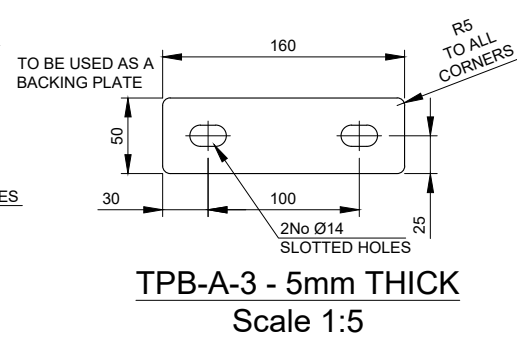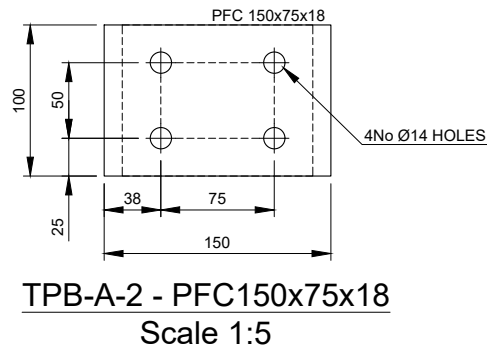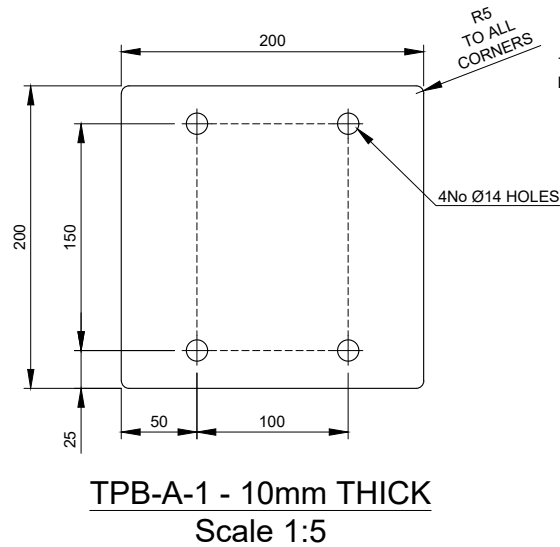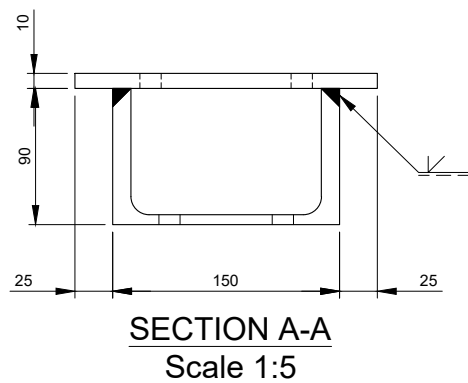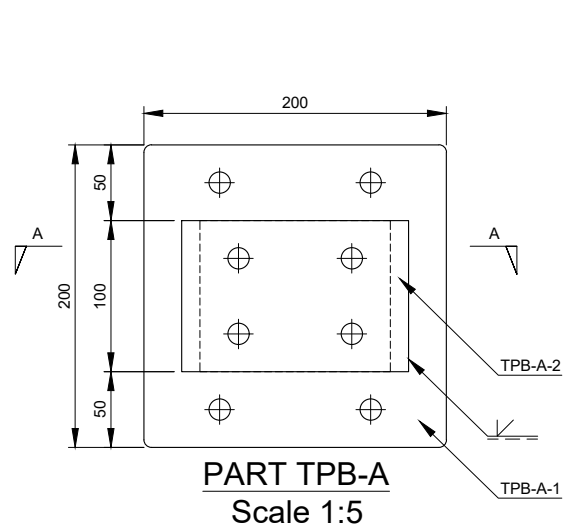


Parts list for TPB-A

Item	Part	Quantity	Part description	Length	Material	Weight
01	TPB-A-1	1	200x200x10mm	N/A	S275J0	3.14 kg
02	TPB-A-2	1	PFC 150x75x18	100mm	S275J0	1.79 kg
03	TPB-A-3	1	160x50x5mm	N/A	S275J0	0.31 kg
04	TPB-A-4	1	EA 50x50x6	280mm	S275J0	1.25 kg
05	TPB-A-5	1	EA 50x50x6	550mm	S275J0	2.46 kg
06	TPB-A-6	1	130x190x10mm	N/A	S275J0	1.94 kg
06	BOLT	1	M12 SET BOLT - 30mm LONG	N/A	GRADE 8.8	-
04	STUDS	4	M12 STUDDING	380mm	GRADE 8.8	0.34 kg
04	N-BOLT	2	M12 N-BOLT FOR EA 50x50x6	N/A	GRADE 8.8	-
05	U-BOLT	4	M12 U-BOLT FOR CHS 60.3mm	N/A	GRADE 8.8	-

Total Weight: 12.25 kg

- All steel hot dip galvanized
- Each BOLT to be supplied with 1 Full Nut, 1 Form E FLat Washer and 1 Spring Washer
- Each STUD & U-BOLT to be supplied with 4 Full Nuts, 2 Flat Washers and 2 Spring Washers
- For fabriction notes see drawing 305

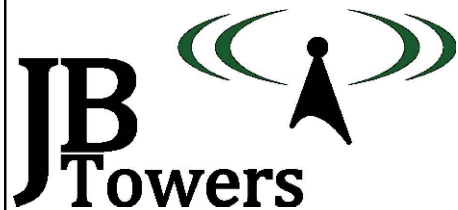


02	DRAWING NUMBER CHANGED	AM	30/05/18
01	FIRST ISSUE	AM	22/05/18
REV	REV	BY	DATE
SCALE AS SHOWN WHEN PRINTED AT A3	DRAWN AM	CHECKED MP	APPROVED JBT
DATE 22/05/18	DATE 22/05/18	DATE 22/05/18	DATE 22/05/18
ALL DIMENSIONS IN mm UNLESS OTHERWISE STATED. THIS DRAWING TO BE READ IN CONJUNCTION WITH OTHER RELEVANT DRAWINGS.			

TITLE		SITE ADDRESS	
Tx STEELWORK BRACKET & PANNING ARM		COOMBE FARM	
		SALTDEAN	
		BRIGHTON	
PART: TPB-A		EAST SUSSEX	
		BN2 8HE	
ARQIVA REF.		DRG No.	REV
141568		302	02

ALL SCALES AS SHOWN WHEN PRINTED AT A3



ALL SCALES AS SHOWN WHEN PRINTED AT A3

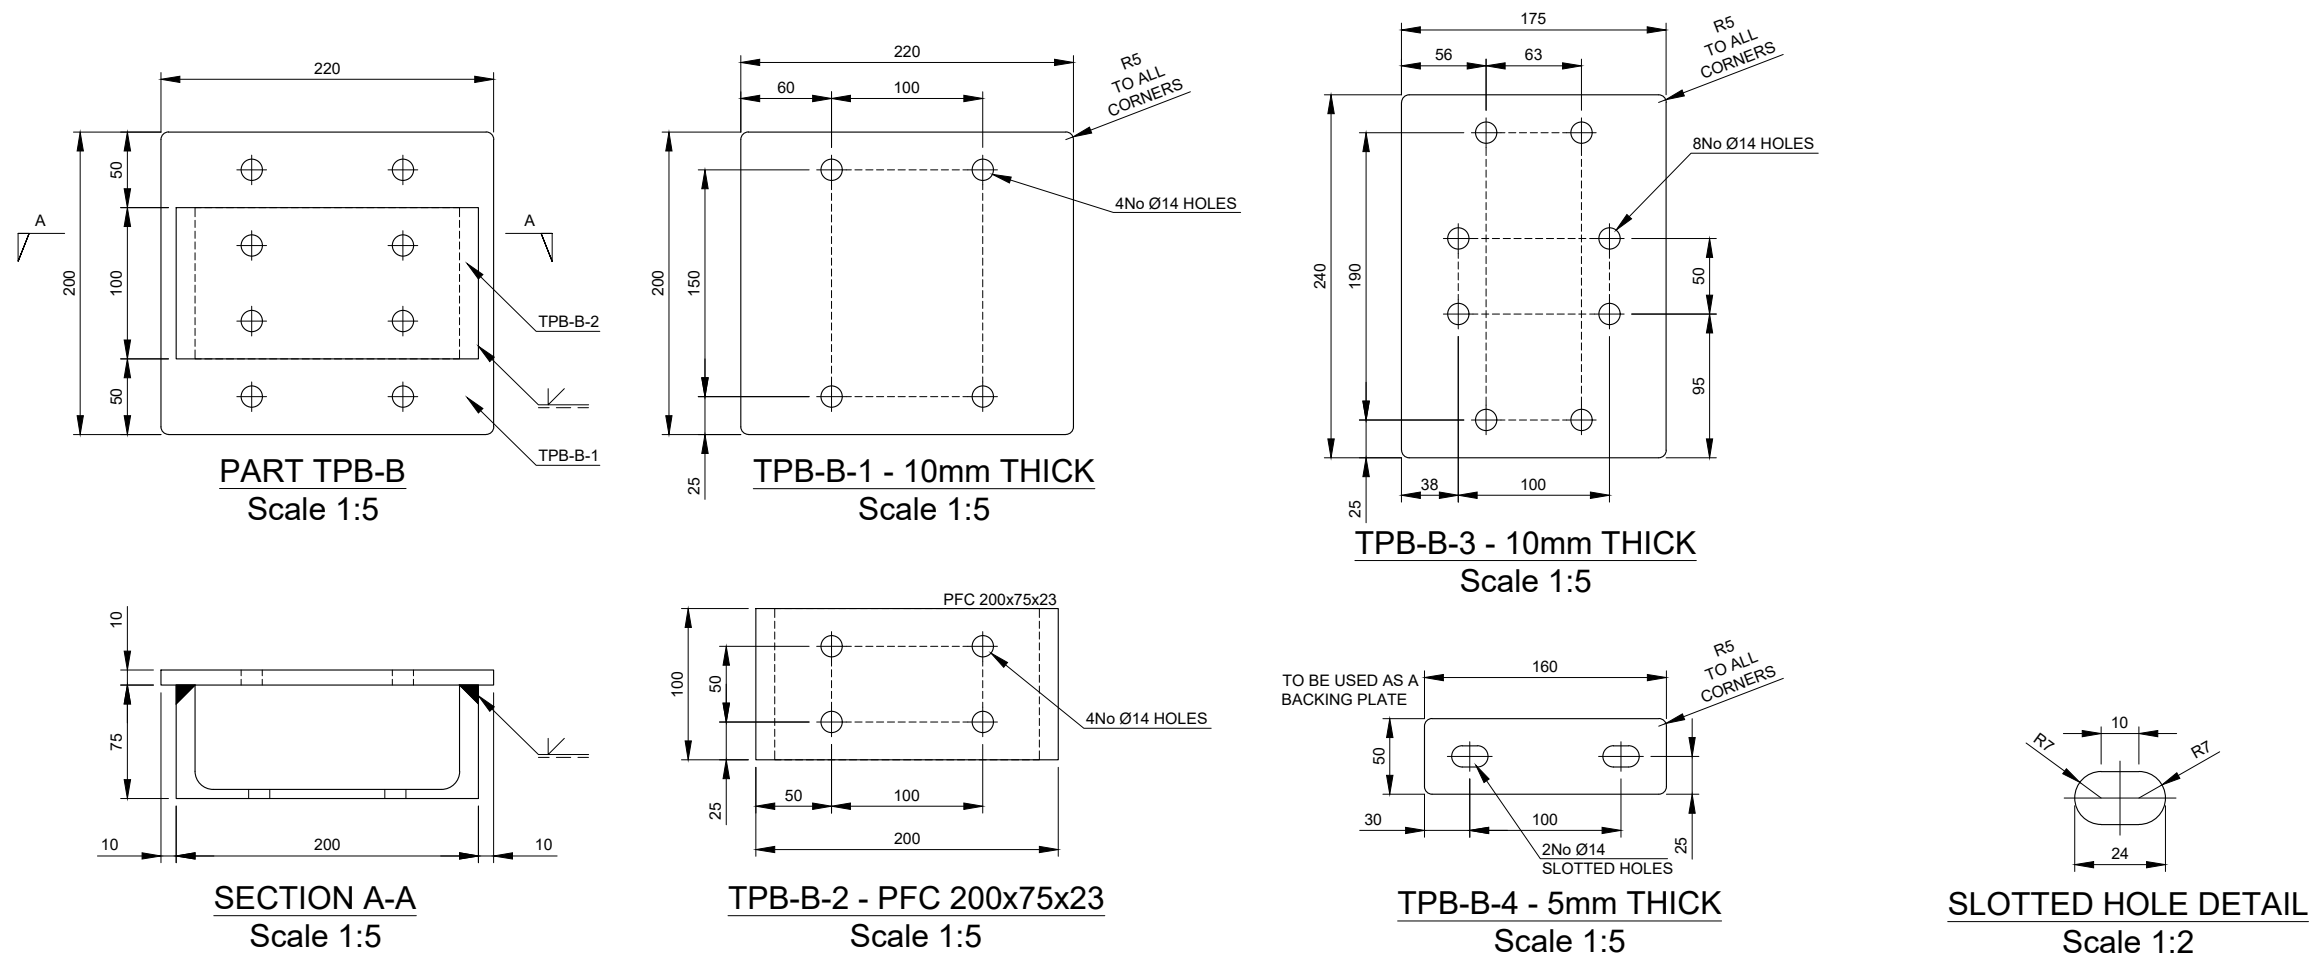

Parts list for TPB-B

Item	Part	Quantity	Part description	Length	Material	Weight
01	TPB-B-1	1	220x200x10mm	N/A	S275J0	3.45 kg
02	TPB-B-2	1	PFC 200x75x23	100mm	S275J0	2.30 kg
03	TPB-B-3	1	240x175x10mm	N/A	S275J0	3.30 kg
04	TPB-B-4	2	160x50x5mm	N/A	S275J0	0.31 kg
05	STUDS	4	M12 STUDDING	350mm	GRADE 8.8	0.31 kg
06	BOLT	4	M12 40mm LONG (2D+6)	40mm	GRADE 8.8	-
07	U-BOLT	2	M12 U-BOLT FOR CHS 48.3mm	N/A	GRADE 8.8	-
Total Weight:						10.91 kg

- All steel hot dip galvanized
- Each STUD & U-BOLT to be supplied with 4 Full Nuts, 2 Flat Washers and 2 Spring Washers
- Each BOLT to be supplied with 1 Full Nut, 1 Form E FLat Washer and 1 Spring Washer
- For fabrtruction notes see drawing 305

02		DRAWING NUMBER CHANGED		AM	30/05/18
01		FIRST ISSUE		AM	22/05/18
REV		REV		BY	DATE
SCALE AS SHOWN		DRAWN	AM	CHECKED	MP
WHEN PRINTED AT A3		DATE	22/05/18	DATE	22/05/18
		APPROVED	JBT	DATE 22/05/18	
ALL DIMENSIONS IN mm UNLESS OTHERWISE STATED. THIS DRAWING TO BE READ IN CONJUNCTION WITH OTHER RELEVANT DRAWINGS.					

TITLE

Rx STEELWORK BRACKET

PART: TPB-B

SITE ADDRESS

COOMBE FARM
SALTDEAN
BRIGHTON
EAST SUSSEX
BN2 8HE

ARQIVA REF.
141568




DRG No.
303

REV
02

ALL SCALES AS SHOWN WHEN PRINTED AT A3

0cm 1cm 2cm 3cm 4cm 5cm 6cm 7cm 8cm 9cm 10cm

ALL SCALES AS SHOWN WHEN PRINTED AT A3

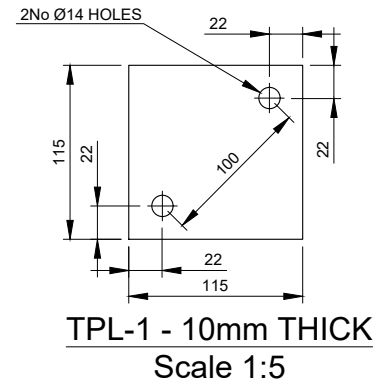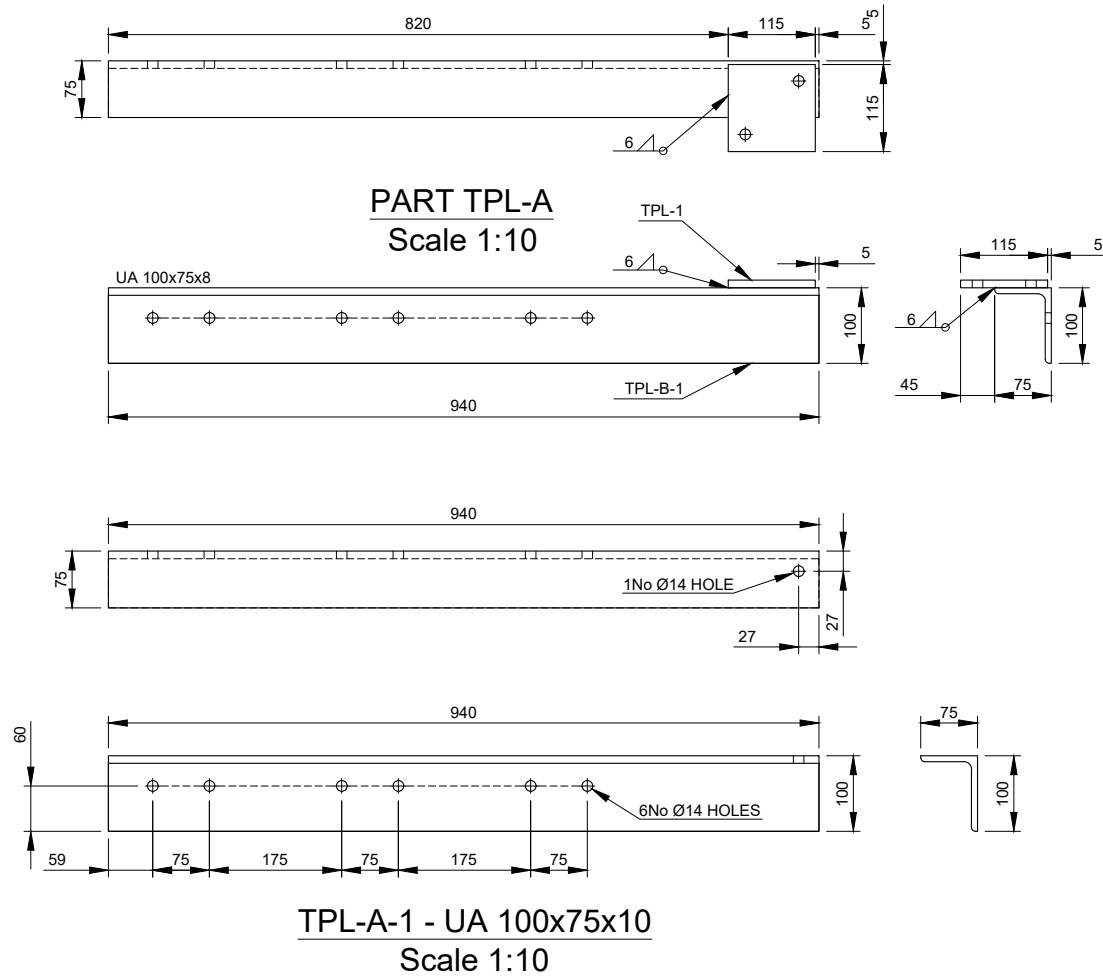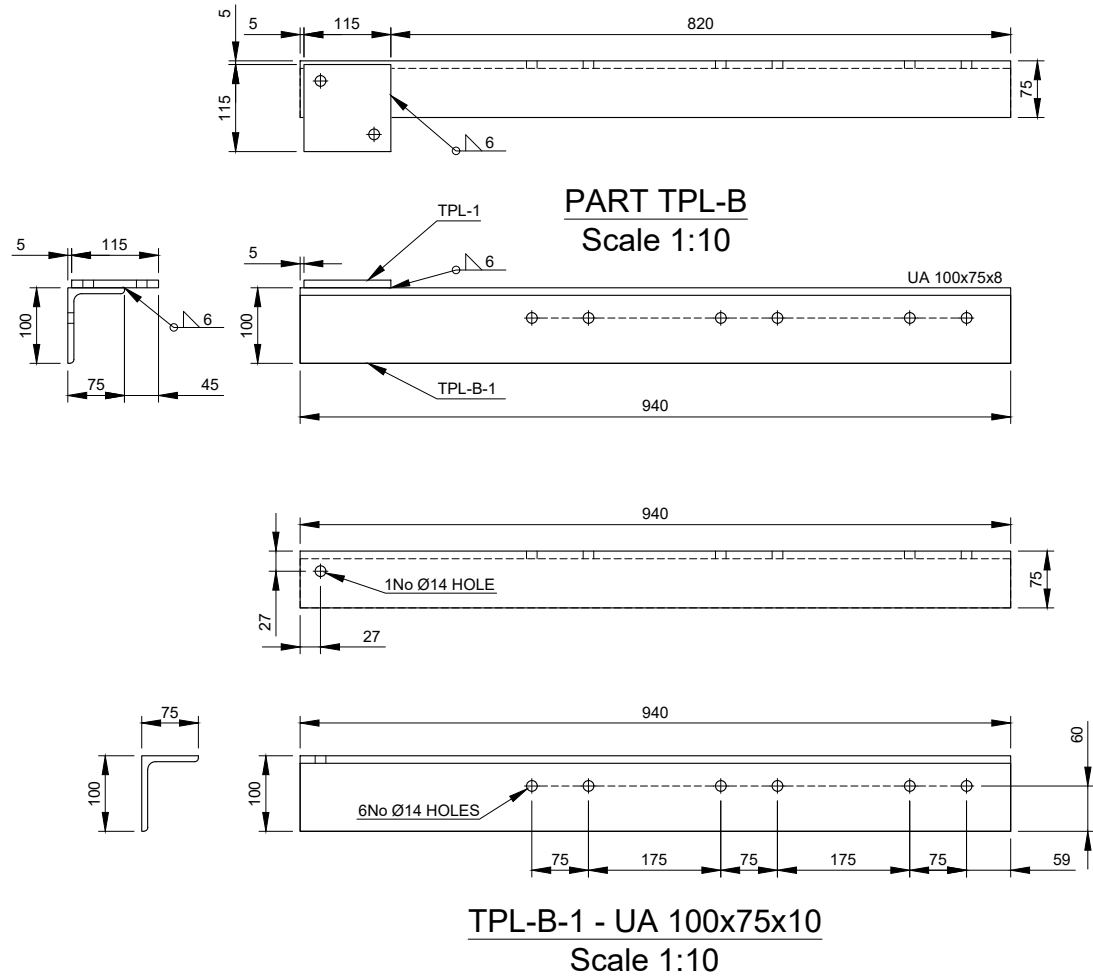

Parts list for TPL-B


Item	Part	Quantity	Part description	Length	Material	Weight
01	TPL-B-1	1	UA 100x75x8	940mm	S275J0	9.96 kg
02	TPL-1	1	115x115x10mm	N/A	S275J0	1.04 kg
03	U-BOLT	3	M12 U-BOLT FOR CHS 60.3mm	N/A	GRADE 8.8	-
Total Weight:						11.00 kg

- All steel hot dip galvanized
- Each U-BOLT to be supplied with 4 Full Nuts, 2 Flat Washers and 2 Spring Washers
- For fabrctation notes see drawing 305

Parts list for TPL-A

Item	Part	Quantity	Part description	Length	Material	Weight
01	TPL-A-1	1	UA 100x75x8	940mm	S275J0	9.96 kg
02	TPL-1	1	115x115x10mm	N/A	S275J0	1.04 kg
03	U-BOLT	3	M12 U-BOLT FOR CHS 60.3mm	N/A	GRADE 8.8	-
Total Weight:						11.00 kg

- All steel hot dip galvanized
- Each U-BOLT to be supplied with 4 Full Nuts, 2 Flat Washers and 2 Spring Washers
- For fabrctation notes see drawing 305

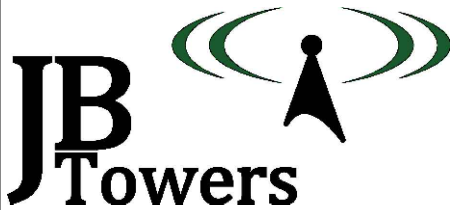

02	DRAWING NUMBER CHANGED	AM	30/05/18
01	FIRST ISSUE	AM	22/05/18
REV	REV	BY	DATE
SCALE AS SHOWN WHEN PRINTED AT A3	DRAWN DATE 22/05/18	CHECKED DATE 22/05/18	APPROVED DATE 22/05/18
ALL DIMENSIONS IN mm UNLESS OTHERWISE STATED. THIS DRAWING TO BE READ IN CONJUNCTION WITH OTHER RELEVANT DRAWINGS.			

TITLE
Tx MOUNTS
PARTS: TPL-A; TPL-B

SITE ADDRESS
COOMBE FARM
SALTDEAN
BRIGHTON
EAST SUSSEX
BN2 8HE

ARQIVA REF.
141568

DRG No.
304

REV
02

ALL SCALES AS SHOWN WHEN PRINTED AT A3




ALL SCALES AS SHOWN WHEN PRINTED AT A3

Item	Part	Drawing	Quantity	Part description	Length	Material	Weight
01	01	-	-	NOT REQUIRED	-	-	-
02	02	200	1	3 MAN LATCHWAY SYSTEM & 3No. WIRE GUIDES FOR FACE MOUNTED MONOPOLE	17000	N/A	-
03	TPB-C	300	2	FALL ARREST ATTACHMENT POINT	N/A	S275J0	4.48 kg
04	TPS-P	301	46	PERMANENT BT STEP c/w 3No 10x75mm ZINC-PLATED COACH SCREWS	N/A	S275J0	13.80 kg
05	TPS-R	300	9	'MonoStep' ASSEMBLY	N/A	S275J0	30.60 kg
06	TPB-B	303	1	Rx STEELWORK BRACKET	N/A	S275J0	10.91 kg
07	07	203	1	CHS 48.3x5mm	600mm	S355J2H	3.20 kg
08	TPB-A	302	2	Tx STEELWORK BRACKET	N/A	S275J0	24.50 kg
09	09	-	-	NOT REQUIRED	-	-	-
10	10	204	3	CHS 60.3x5mm	1500mm	S355J2H	30.69 kg
11	TPL-A	304	3	Tx MOUNT	940mm	S275J0	33.00 kg
12	TPL-B	304	1	Tx MOUNT	940mm	S275J0	11.00 kg
13	13	-	12	M12 WASHER	N/A	GRADE 8.8	-
14	14	-	1	FEEDER COVER - 2/CG/100	3500mm	UV RESISTANT PLASTIC	-
15	15	-	20	FEEDER CLAMP - 2/FCD/028	N/A	POLYPROPYLENE	-
16	16	-	20	M10 SCREW DOWELS WTH M10 NUT	100mm	STAINLESS STEEL	-
17	17	200	1	PoleSaver	750mm	N/A	-
18	18	200	8	M12 STUD + 4No NUTS + 2No FLAT WASHERS + 1No Ø50mm WASHER (FOR FALL ARREST SYSTEM)	470mm	GRADE 8.8	2.82 kg
Total Weight:							165.00 kg

- All steel hot dip galvanized
- All U-BOLTS to be FLA supply, each Supplied with 4 Full Nuts, 2 Flat Washers and 2 Spring Washers

NOTES:

1. WELDING TO BE IN ACCORDANCE WITH BS EN 1011-1:2009
2. LINEAR DIMS TO BE WITHIN ±1mm;
3. ANGULAR TOLERANCES TO BE WITHIN 0.5°
4. WELDING SYMBOLS ARE IN ACCORDANCE WITH BS EN 22553:1995
5. ALL PROFILE EDGES TO BE DRESSED AND SHARP CORNERS REMOVED
6. ALL WELD SIZES ARE FINAL SIZES
7. ALL WELDED JOINTS ARE TO BE PICKLE TIGHT
8. ALL STEELWORK TO BE BS EN 10025 GRADE S275 J0 UNO & HOT DIPPED GALVANISED TO BS EN ISO 1461. (ALL HOLLOW SECTIONS TO BE GRADE S355 J0H)
9. ALL STEEL IS TO BE SUPPLIED IN ACCORDANCE WITH EN 1090 TO EXECUTION CLASS 2
10. ALL NON PRE-LOADED BOLTS TO BE COMPLIANT STRUCTURAL BOLTS TO BS EN ISO 15048 PARTS 1&2.
11. STEELWORK COMPONENTS SHALL BE HOT DIP GALVANISED TO ACHIEVE A "VERY HIGH" DURABILITY FOR AN ENVIRONMENT CATEGORY CODE C4 FROM TABLE 1 IN BS EN ISO 14713
12. BOLTS AND NUTS SHALL BE SUPPLIED IN ACCORDANCE WITH BS 7371, SPUN GALVANISED IN ACCORDANCE WITH ISO 10684, THE NUTS RE-TAPPED AFTER GALVANISING, AND THE THREADS TREATED WITH GREASE.
13. ALL BOLTS TO BE CUT ON SITE TO EXTEND MAX 10mm BEYOND THE NUT WHEN TIGHTENED UNO.
14. ALL SITE DRILLED HOLE/CUT ENDS TO BE TREATED WITH METAFLUX 70-40 ZINC PASTE FOLLOWED BY 1 COAT OF 7-42 ZINC ALU OR 70-16 ALUMINIUM SPRAY

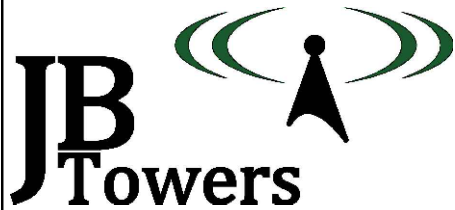

03	PARTS LIST UPDATED			AM	25/07/18
02	DRAWING NUMBER CHANGED			AM	30/05/18
01	FIRST ISSUE			AM	22/05/18
REV	REV			BY	DATE
SCALE AS SHOWN		DRAWN	AM	CHECKED	MP
WHEN PRINTED AT A3		DATE	22/05/18	DATE	22/05/18
		DATE	22/05/18	DATE	22/05/18
ALL DIMENSIONS IN mm UNLESS OTHERWISE STATED. THIS DRAWING TO BE READ IN CONJUNCTION WITH OTHER RELEVANT DRAWINGS.					

TITLE		SITE ADDRESS		
PARTS LIST		COOMBE FARM SALTDEAN BRIGHTON EAST SUSSEX BN2 8HE		
		ARQIVA REF. 141568	DRG No. 305	REV 04

ALL SCALES AS SHOWN WHEN PRINTED AT A3



ALL SCALES AS SHOWN WHEN PRINTED AT A3