
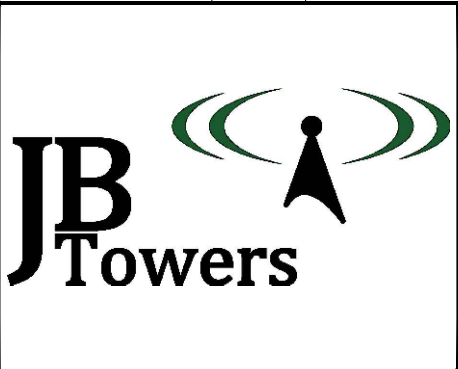


# DRAWING ISSUE SHEET

[illegible]

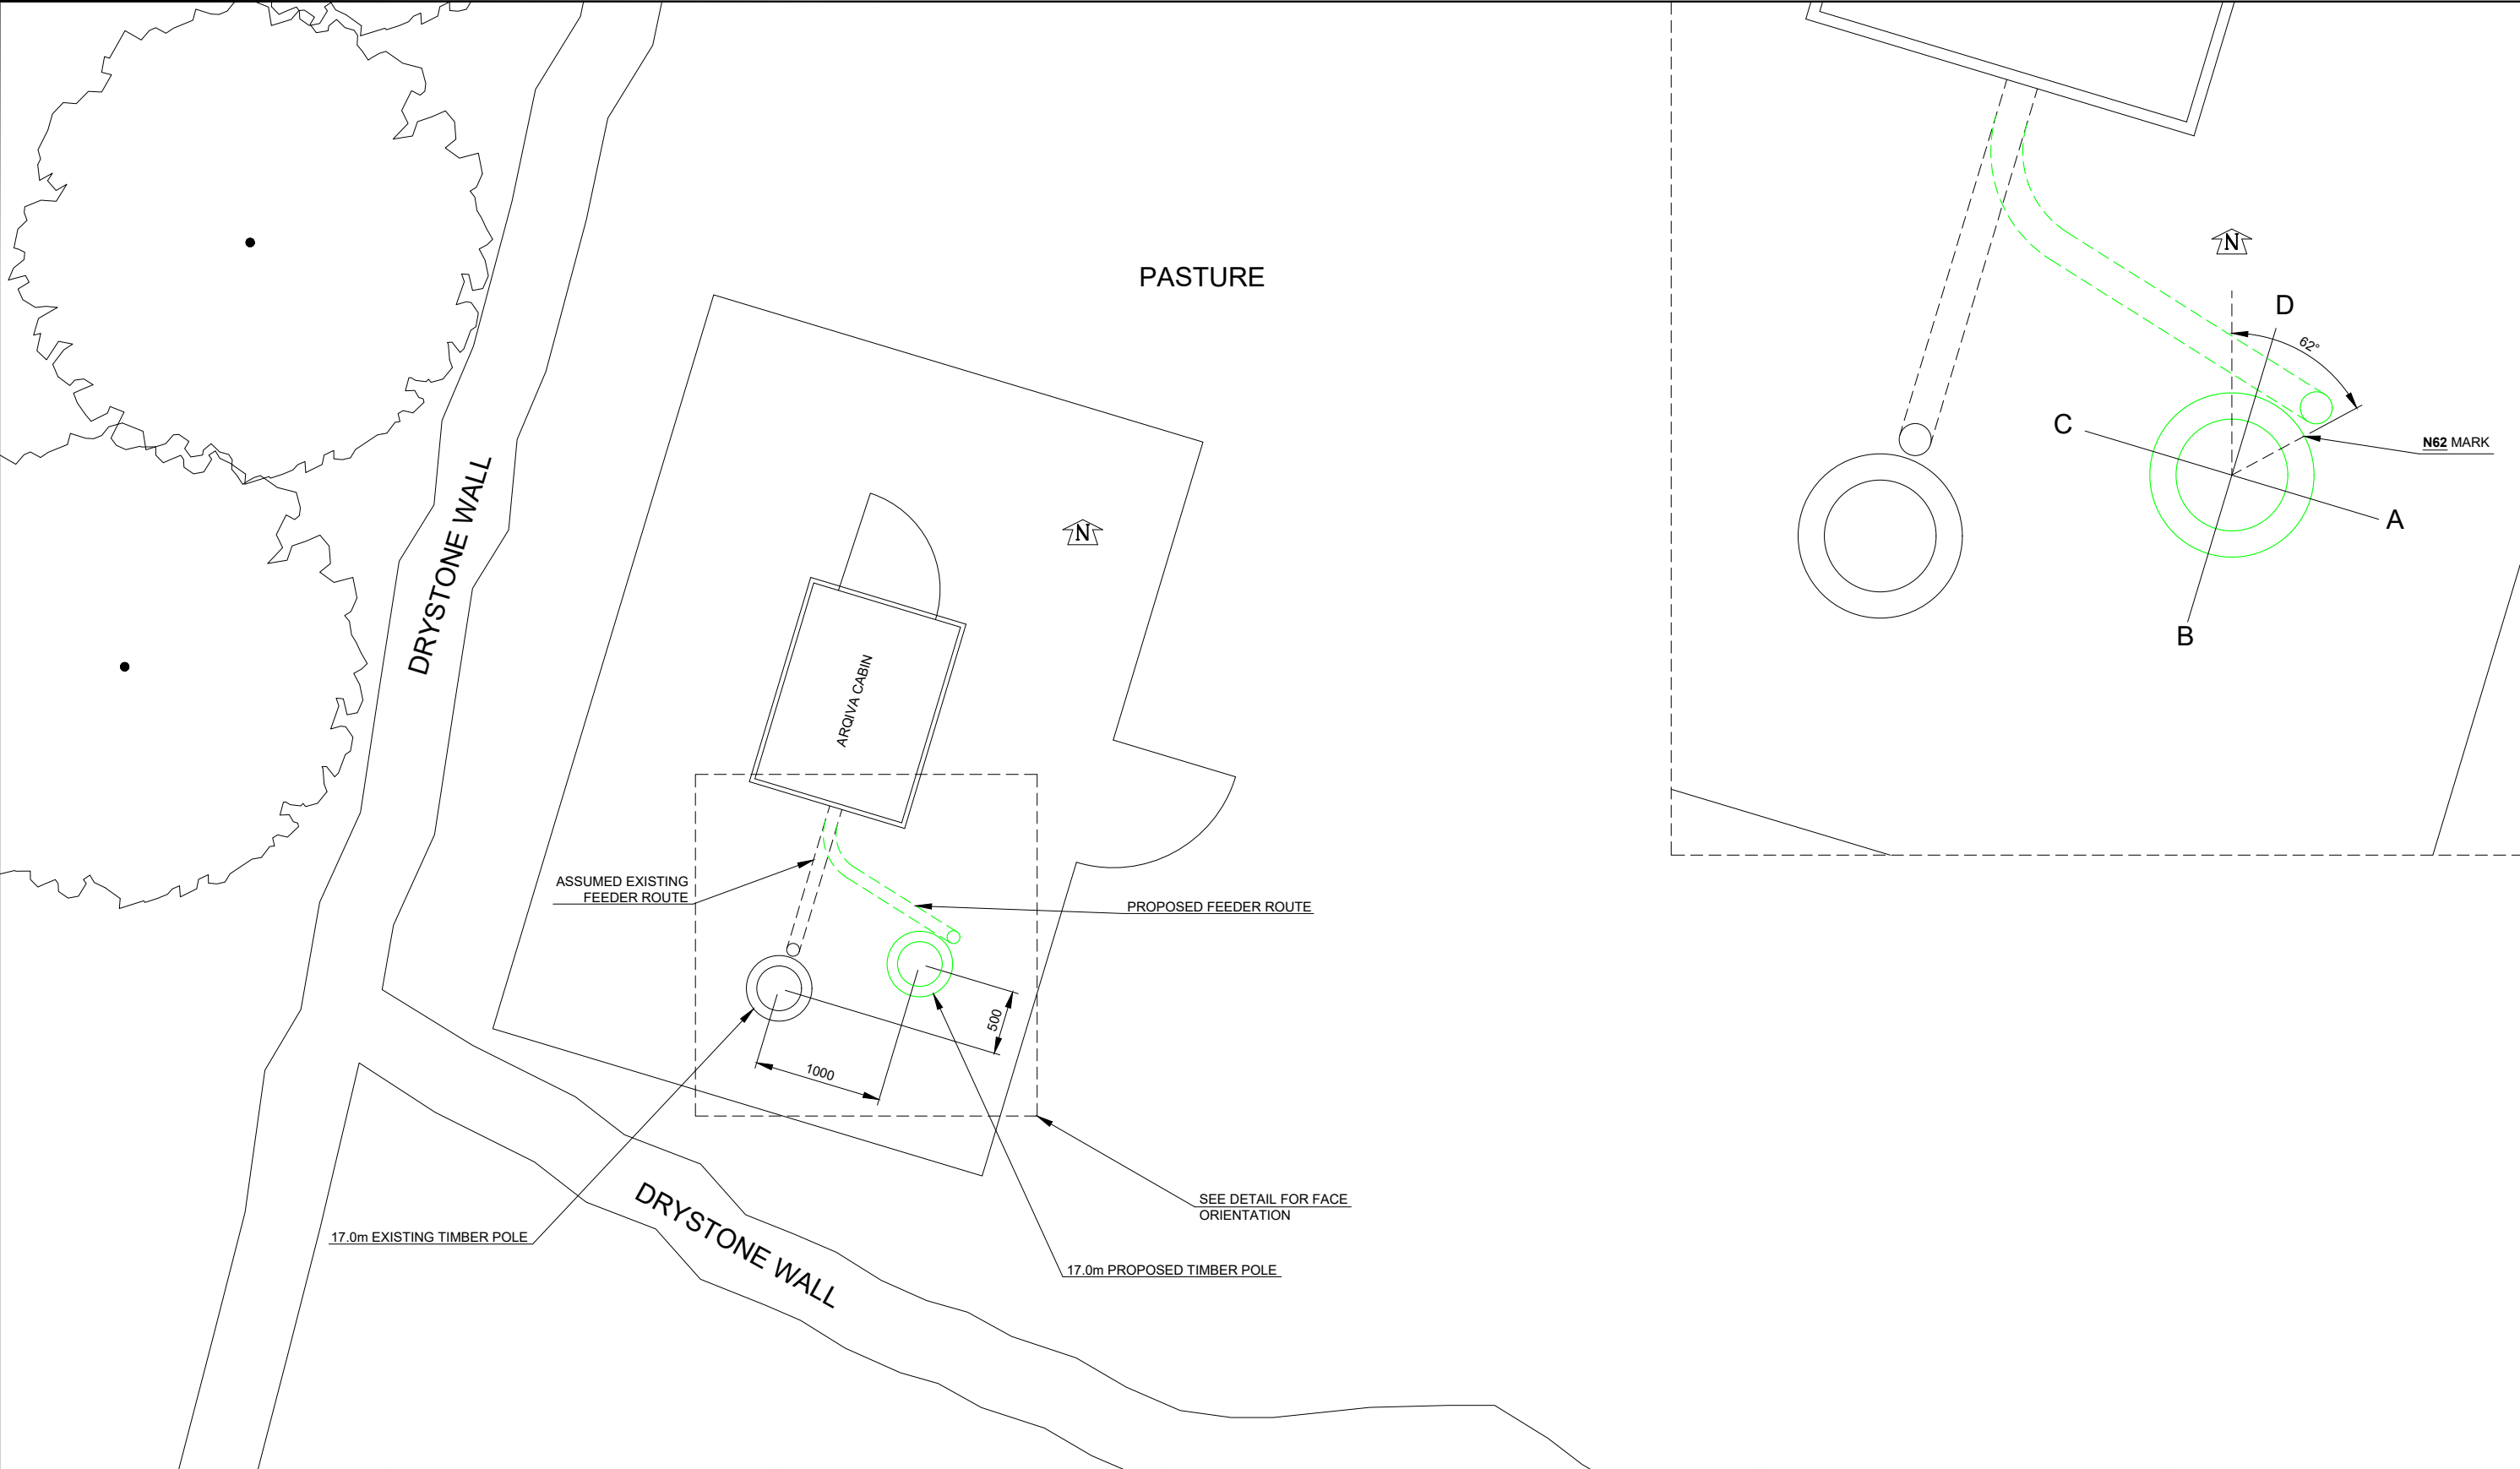


|                                               |             |       |          |         |          |                                                                      |
|-----------------------------------------------|-------------|-------|----------|---------|----------|----------------------------------------------------------------------|
| 01                                            | FIRST ISSUE |       |          |         | AM       | 12/10/18                                                             |
| REV                                           | REV         |       |          |         | BY       | DATE                                                                 |
| SCALE AS SHOWN                                |             | DRAWN | AM       | CHECKED | MP       | APPROVED JBT                                                         |
| WHEN PRINTED AT A3                            |             | DATE  | 12/10/18 | DATE    | 12/10/18 | DATE 12/10/18                                                        |
| ALL DIMENSIONS IN mm UNLESS OTHERWISE STATED. |             |       |          |         |          | THIS DRAWING TO BE READ IN CONJUNCTION WITH OTHER RELEVANT DRAWINGS. |

|           |
|-----------|
| TITLE     |
| BURBAGE   |
| SITE PLAN |

|                                                                  |                |           |
|------------------------------------------------------------------|----------------|-----------|
| SITE ADDRESS                                                     |                |           |
| THE PLAYING FIELD<br>GREEN LANE<br>BURBAGE<br>BUXTON<br>SK17 9DG |                |           |
| ARQIVA REF.<br>140357                                            | DRG No.<br>100 | REV<br>01 |

ALL SCALES AS SHOWN WHEN PRINTED AT A3

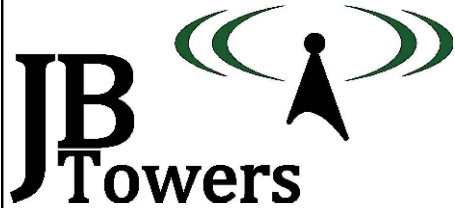

|   |             |       |          |         |          |
|---|-------------|-------|----------|---------|----------|
|   |             |       |          |         |          |
|   |             |       |          |         |          |
|   |             |       |          |         |          |
|   |             |       |          |         |          |
| 01   | FIRST ISSUE |       |          | AM      | 12/10/18 |
| REV   | REV         |       |          | BY      | DATE     |
| SCALE AS SHOWN   |             | DRAWN | AM       | CHECKED | MP       |
| WHEN PRINTED AT A3   |             | DATE  | 12/10/18 | DATE    | 12/10/18 |
|   |             | DATE  | 12/10/18 | DATE    | 12/10/18 |
| ALL DIMENSIONS IN mm UNLESS OTHERWISE STATED.<br>THIS DRAWING TO BE READ IN CONJUNCTION WITH<br>OTHER RELEVANT DRAWINGS. |             |       |          |         |          |

TITLE

BURBAGE

GENERAL ARRANGEMENT

SHEET 1 OF 3

SITE ADDRESS

THE PLAYING FIELD

GREEN LANE

BURBAGE

BUXTON

SK17 9DG

ARQIVA REF.



140357

DRG No.

200

REV

01

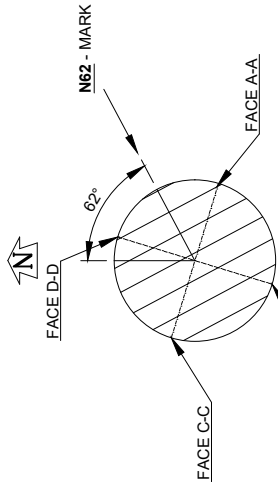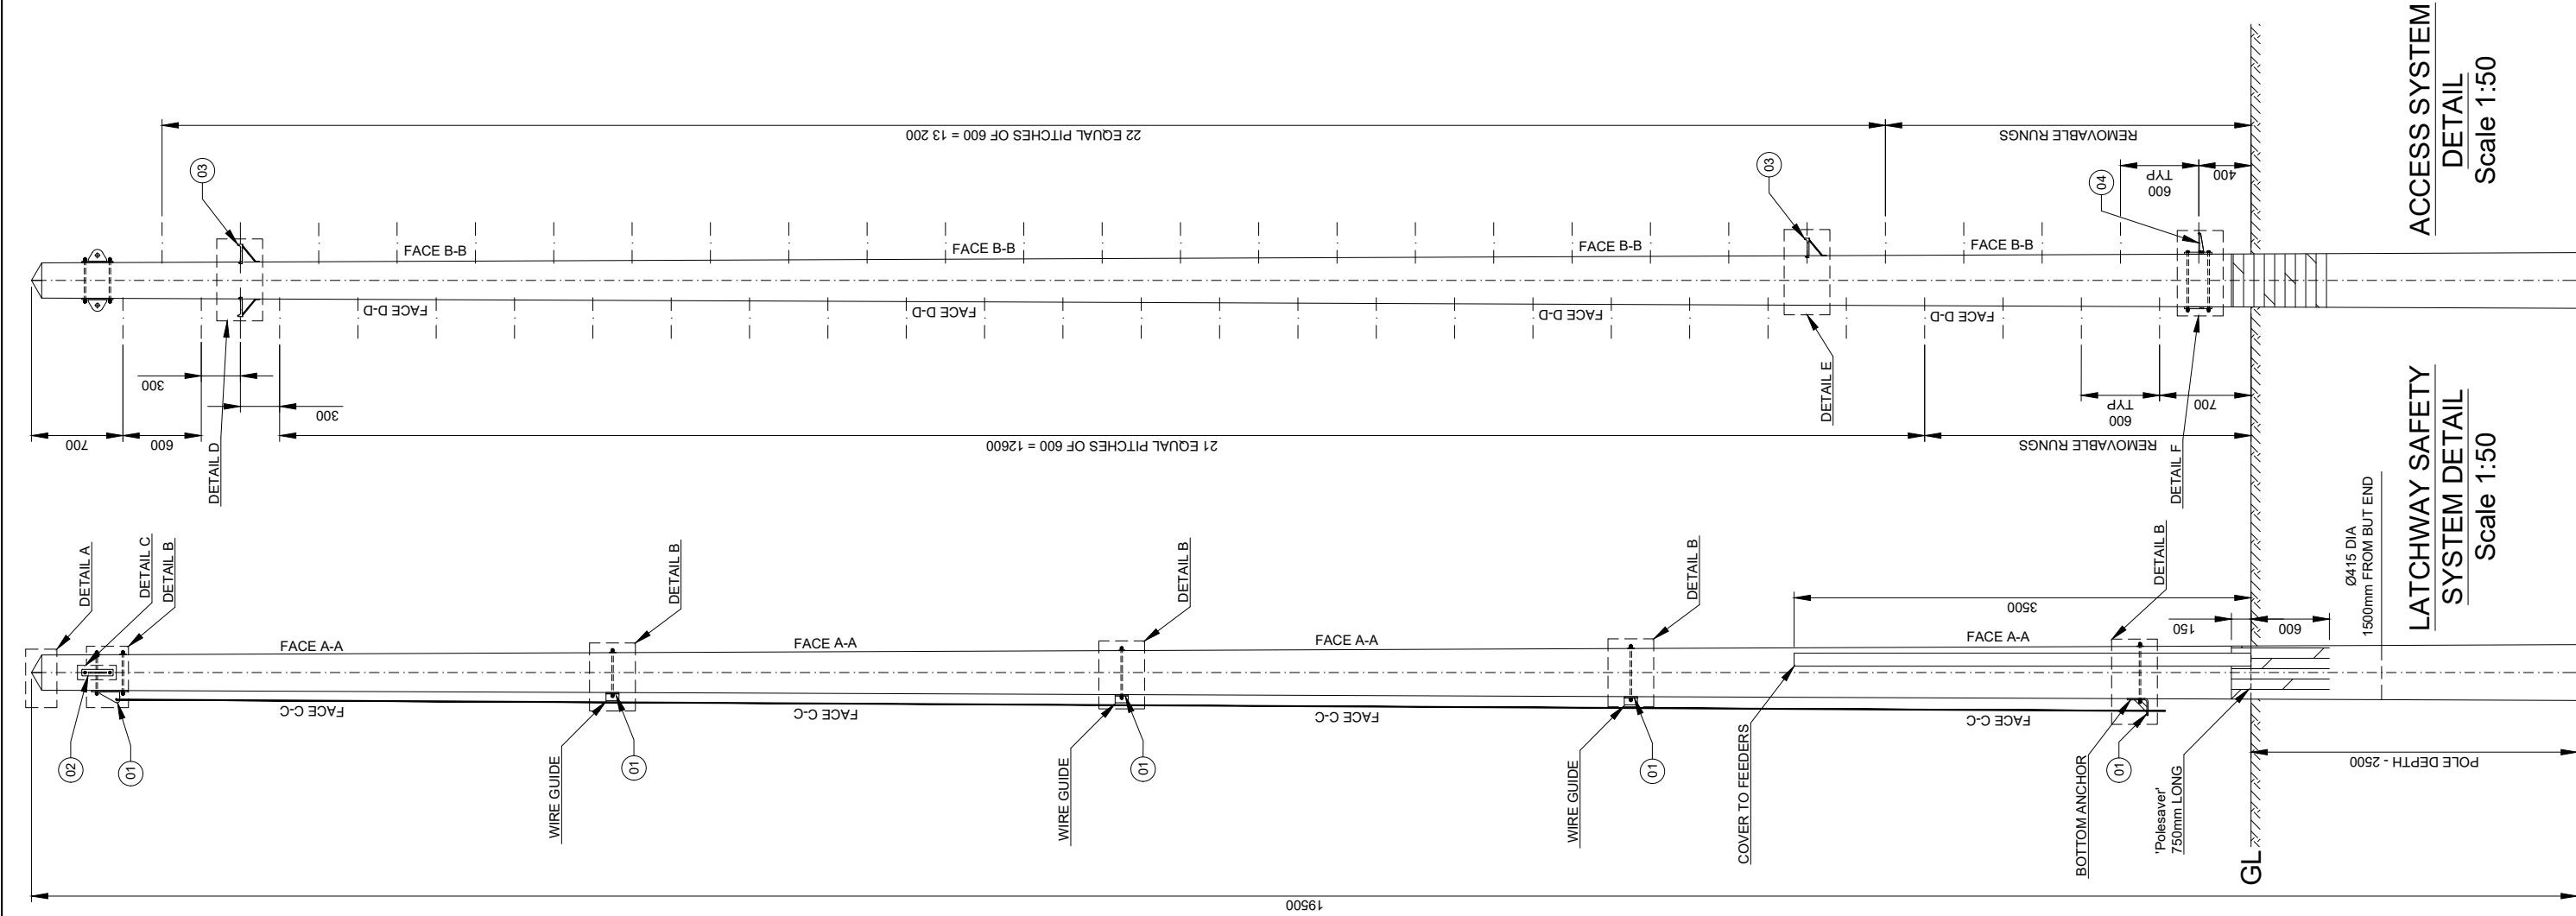

POLE ORIENTATION

Scale 1:20

NOTES

1. SEE DRAWING 303 FOR PARTS LIST
2. ALL BOLTS TO BE CUT ON SITE TO EXTEND MAX 10mm BEYOND THE NUT WHEN TIGHTENED UNO.
3. ALL SITE DRILLED HOLE/CUT ENDS TO BE TREATED WITH METAFUX 70-40 ZINC PASTE FOLLOWED BY 1 COAT OF 7-42 ZINC ALU OR 70-16 ALUMINIUM SPRAY

TIMBER POLE

1. POLE TO BE SUPPLIED IN ACCORDANCE WITH BS EN14229 & SHALL HAVE MIN. CHARACTERISTIC BENDING STRENGTH OF 30N/mm2 & MIN. YOUNGS MODULUS (PARALLEL TO GRAIN) OF 10KN/mm2.
2. MARKINGS ON FINISHED POLE SHALL BE AT 4m FROM BUT AND COMPLY WITH BS EN 14229 UNO
3. AS FAR AS PRACTICABLE ALL CUTTING, SCARFING & DRILLING TO BE DONE BEFORE CREOSOTING. IF NOT ALL CUT, DRILLED & SCARFED SURFACES TO BE COATED WITH A MIXTURE OF CREOSOTE & TAR.
4. POLE TO BE PRESSURE IMPREGNATED WITH CREOSOTE IN ACCORDANCE WITH BS EN 14229
5. MINIMUM DIAMETERS  
TOP - Ø205mm  
BOTTOM - Ø430mm
6. 19.5m LONG POLE TO BE SOURCED BY TRIMMING 20m LONG POLE BY 0.5m AT THE TOP

PLANTING

1. CAT SCANNER IS TO BE USED IN ORDER TO CONFIRM THE POSITIONS OF BURIED SERVICES.
2. 'Perma-Soil Stabiliser' OR A SIMILAR APPROVED SHOULD BE USED IN ACCORDANCE WITH THE MANUFACTURER'S RECOMMENDATION.
3. ANY MATERIAL USED FOR BACK-FILLING IS TO BE OF EQUAL OF BETTER QUALITY THAN THE EXCAVATED MATERIAL.
4. ALL BACK-FILLING MATERIAL IS TO BE PLACED AND COMPACTED IN 150mm THICK LAYERS.
5. TIMBER POLE TO BE PLANTED WITH N62 MARKING AT 3.5m FROM BUT FACING 62° FROM NORTH (CLOCKWISE)

ACCESS SYSTEM  
DETAIL

Scale 1:50




LATCHWAY SAFETY  
SYSTEM DETAIL

Scale 1:50

ALL SCALES AS SHOWN WHEN PRINTED AT A3



ALL SCALES AS SHOWN WHEN PRINTED AT A3

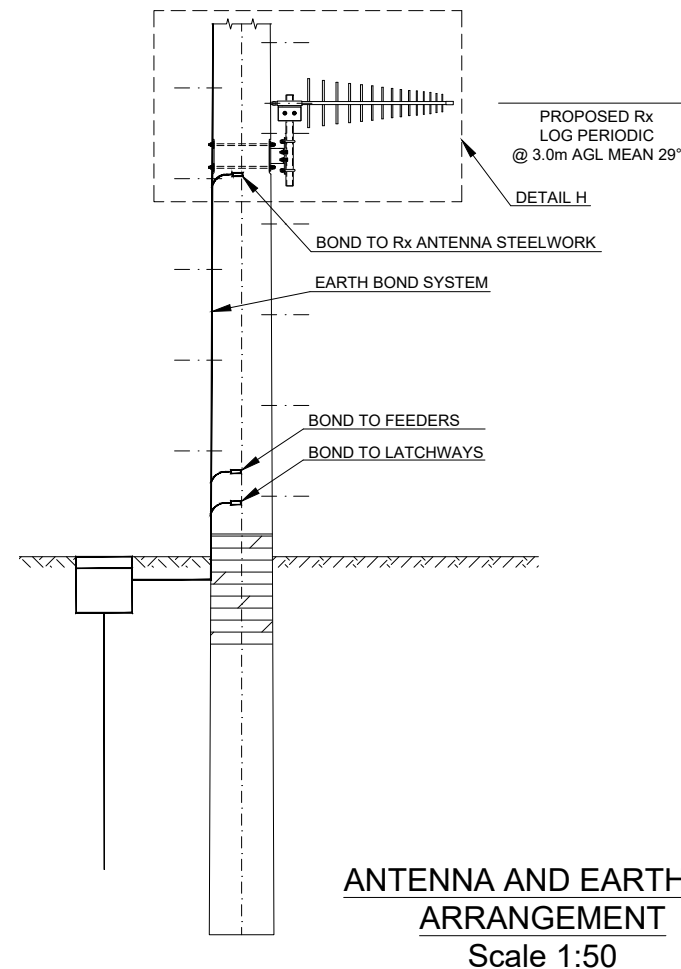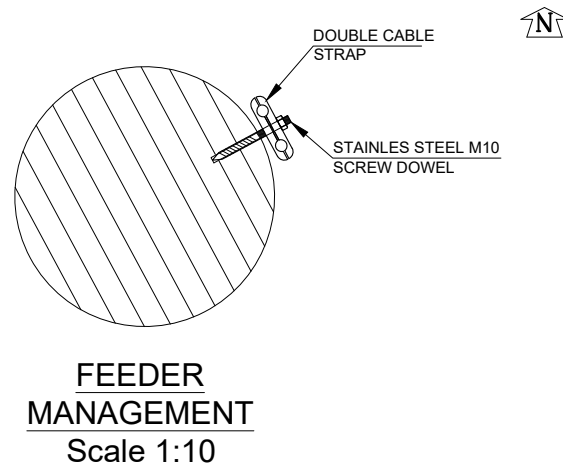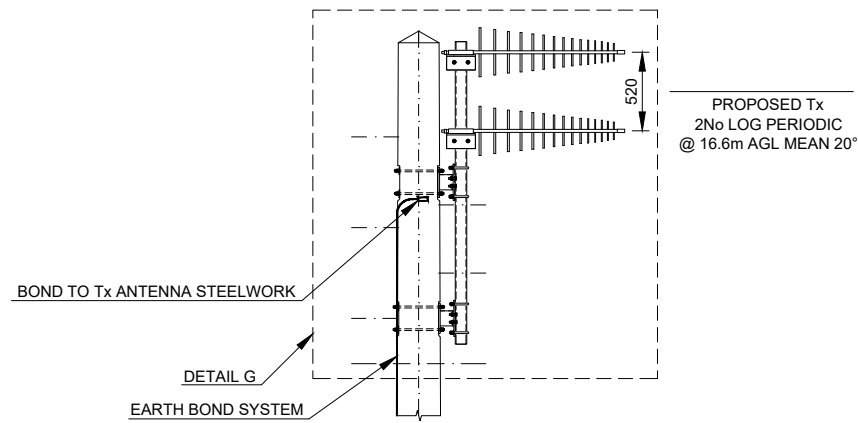

### NOTES

1. AS FAR AS IS PRACTICABLE ALL CUTTING SCARFING AND DRILLING TO BE DONE BEFORE CREOSOTING. WHERE THIS IS NOT POSSIBLE ALL CUT, DRILLED, AND SCARFED SURFACES TO BE COATED WITH A MIXTURE OF CREOSOTE AND TAR

### FEEDERS

1. SUPPLY OF FEEDERS BY OTHERS  
LCF78-50 TO Tx ANTENNA &  
LCF12-50 TO Rx ANTENNA
2. FEEDERS FIXED AT 1000mm CENTRES


### EARTHING

1. CONNECT EARTH BOND TO NEW EARTHING SYSTEM
2. MAXIMUM VALUE FOR GROUND RESISTANCE TO BE 10 OHMS
3. CABLE OR TAPE TO BE FIXED TO POLE AT 1000mm CENTRES
4. EARTHING SHOULD COMPLY WITH ARQIVA'S DOCUMENT BOS147

ALL SCALES AS SHOWN WHEN PRINTED AT A3




ALL SCALES AS SHOWN WHEN PRINTED AT A3

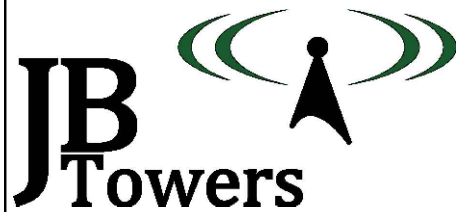


|   |             |                  |                |                 |                |
|---|-------------|------------------|----------------|-----------------|----------------|
| 01   | FIRST ISSUE |                  |                | AM              | 12/10/18       |
| REV   | REV         |                  |                | BY              | DATE           |
| SCALE AS SHOWN<br>WHEN PRINTED AT A3                                                                                     |             | DRAWN<br>DATE    | AM<br>12/10/18 | CHECKED<br>DATE | MP<br>12/10/18 |
| ALL DIMENSIONS IN mm UNLESS OTHERWISE STATED.<br>THIS DRAWING TO BE READ IN CONJUNCTION WITH<br>OTHER RELEVANT DRAWINGS. |             | APPROVED<br>DATE |                |                 |                |

|                       |  |                   |           |
|-----------------------|--|-------------------|-----------|
| TITLE                 |  | SITE ADDRESS      |           |
| BURBAGE               |  | THE PLAYING FIELD |           |
| GENERAL ARRANGEMENT   |  | GREEN LANE        |           |
| SHEET 2 OF 3          |  | BURBAGE           |           |
|                       |  | BUXTON            |           |
|                       |  | SK17 9DG          |           |
| ARQIVA REF.<br>140357 |  | DRG No.<br>200    | REV<br>01 |

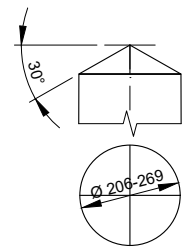


NOTES:  
 1. A SINGLE COAT OF TIMBER COMPATIBLE BITUMINOUS PAINT (E.G. BIRD BRAND BLACK BITUMINOUS PAINT OR SIMILAR APPROVED PRODUCT) TO BE APPLIED TO THE UPPER SURFACES AT THE TOP OF THE POLE.  
 2. PAINT TO BE APPLIED ON SITE JUST BEFORE ERECTION  
 FORM: 4 WAY PYRAMID / CONE


**DETAIL A - TIMBER POLE TOP**  
 Scale 1:20

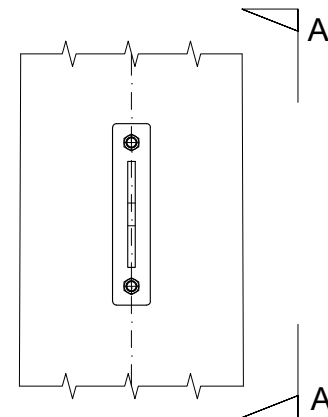


**DETAIL C - FALL ARREST ATTACHMENT POINT**  
 Scale 1:10

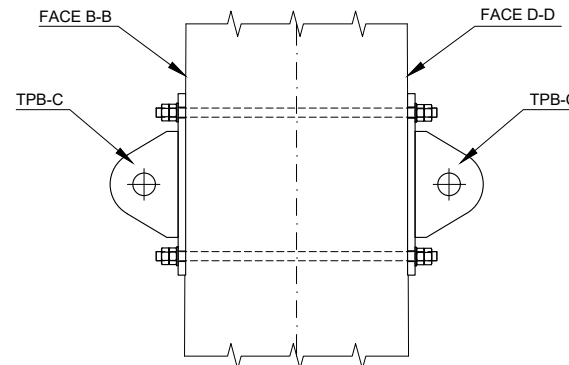


**VIEW A-A**  
 Scale 1:10

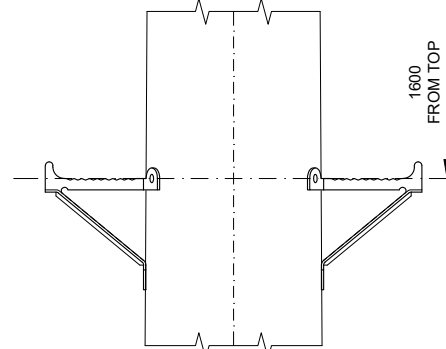

**DETAIL D - ANTENNA ACCESS CLIMBING STEP**  
 Scale 1:10

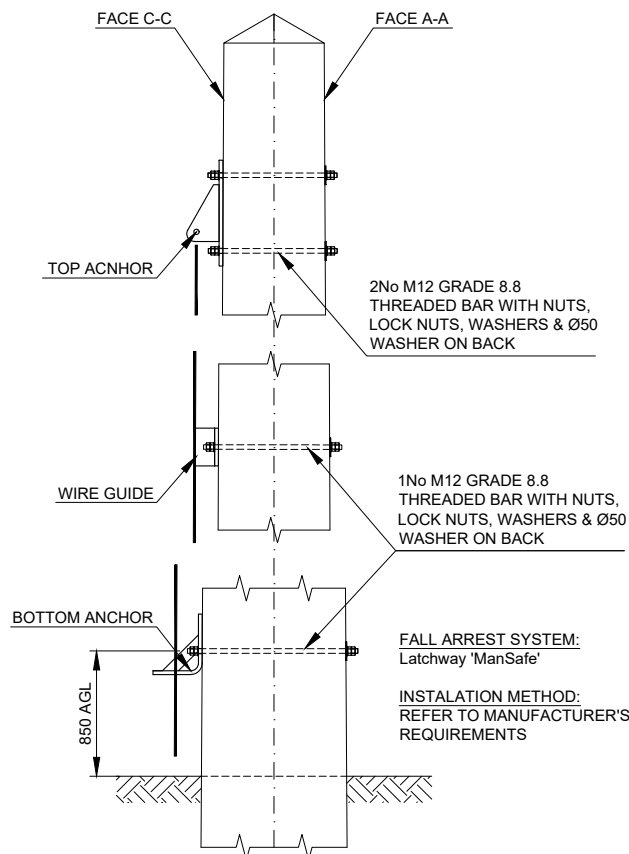


**DETAIL B - FALL ARREST SYSTEM**  
 Scale 1:20

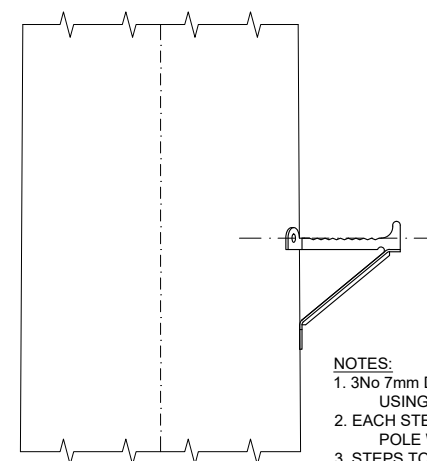

**DETAIL E - PERMANENT CLIMBING STEPS**  
 Scale 1:10

NOTES:  
 1. 3No 7mm DIA 70mm LONG PILOT HOLES TO BE DRILLED USING THE STEP AS A TEMPLATE  
 2. EACH STEP SHOULD BE FIXED TO THE TIMBER POLE WITH 3No 10mm COACH SCREWS 75mm LONG  
 3. STEPS TO BE INSTALLED ON FACES B-B & D-D ONLY

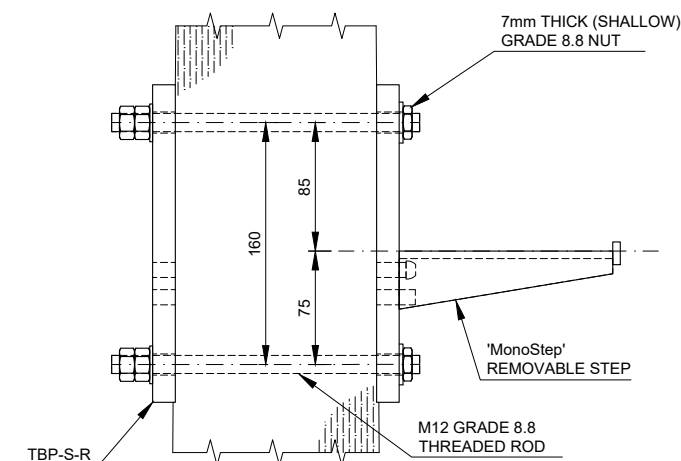


**DETAIL F - REMOVABLE CLIMBING STEPS**  
 Scale 1:5

ALL SCALES AS SHOWN WHEN PRINTED AT A3




ALL SCALES AS SHOWN WHEN PRINTED AT A3

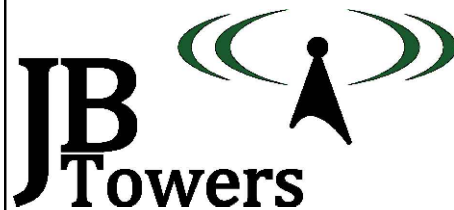

|   |               |               |              |
|---|---------------|---------------|--------------|
| 01   | FIRST ISSUE   | AM            | 12/10/18     |
| REV   | REV           | BY            | DATE         |
| SCALE AS SHOWN WHEN PRINTED AT A3                                                                                  | DRAWN AM      | CHECKED MP    | APPROVED JBT |
| DATE 12/10/18   | DATE 12/10/18 | DATE 12/10/18 |              |
| ALL DIMENSIONS IN mm UNLESS OTHERWISE STATED. THIS DRAWING TO BE READ IN CONJUNCTION WITH OTHER RELEVANT DRAWINGS. |               |               |              |

|                     |         |
|---------------------|---------|
| TITLE               | BURBAGE |
| GENERAL ARRANGEMENT |         |
| SHEET 3 OF 3        |         |

|              |                                                                  |
|--------------|------------------------------------------------------------------|
| SITE ADDRESS | THE PLAYING FIELD<br>GREEN LANE<br>BURBAGE<br>BUXTON<br>SK17 9DG |
| ARQIVA REF.  | 140357                                                           |
| DRG No.      | 200                                                              |
| REV          | 01                                                               |

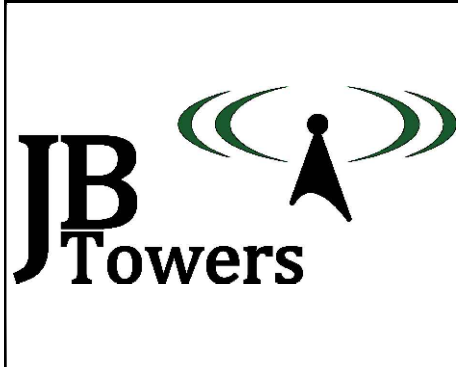




|   |               |               |               |    |          |
|---|---------------|---------------|---------------|----|----------|
|   |               |               |               |    |          |
|   |               |               |               |    |          |
| 01   | FIRST ISSUE   |               |               | AM | 12/10/18 |
| REV   | REV           |               |               | BY | DATE     |
| SCALE AS SHOWN<br>WHEN PRINTED AT A3                                                                                     | DRAWN AM      | CHECKED MP    | APPROVED JBT  |    |          |
|   | DATE 12/10/18 | DATE 12/10/18 | DATE 12/10/18 |    |          |
| ALL DIMENSIONS IN mm UNLESS OTHERWISE STATED.<br>THIS DRAWING TO BE READ IN CONJUNCTION WITH<br>OTHER RELEVANT DRAWINGS. |               |               |               |    |          |

TITLE


BURBAGE

TIMBER POLE HOLE SET OUT  
SHEET 1 OF 2


|                                                                  |                |           |
|------------------------------------------------------------------|----------------|-----------|
| SITE ADDRESS                                                     |                |           |
| THE PLAYING FIELD<br>GREEN LANE<br>BURBAGE<br>BUXTON<br>SK17 9DG |                |           |
| ARQIVA REF.<br>140357                                            | DRG No.<br>201 | REV<br>01 |

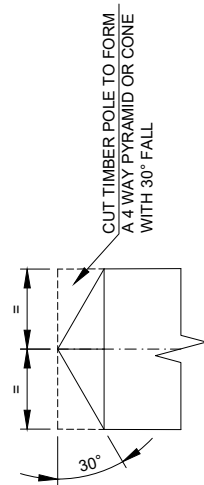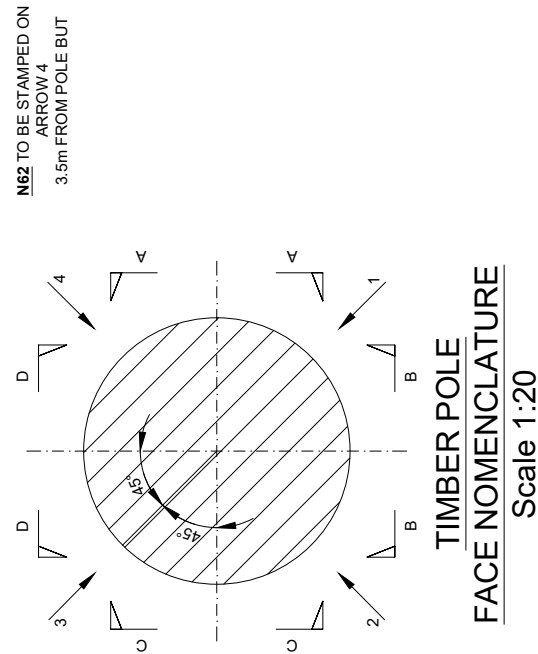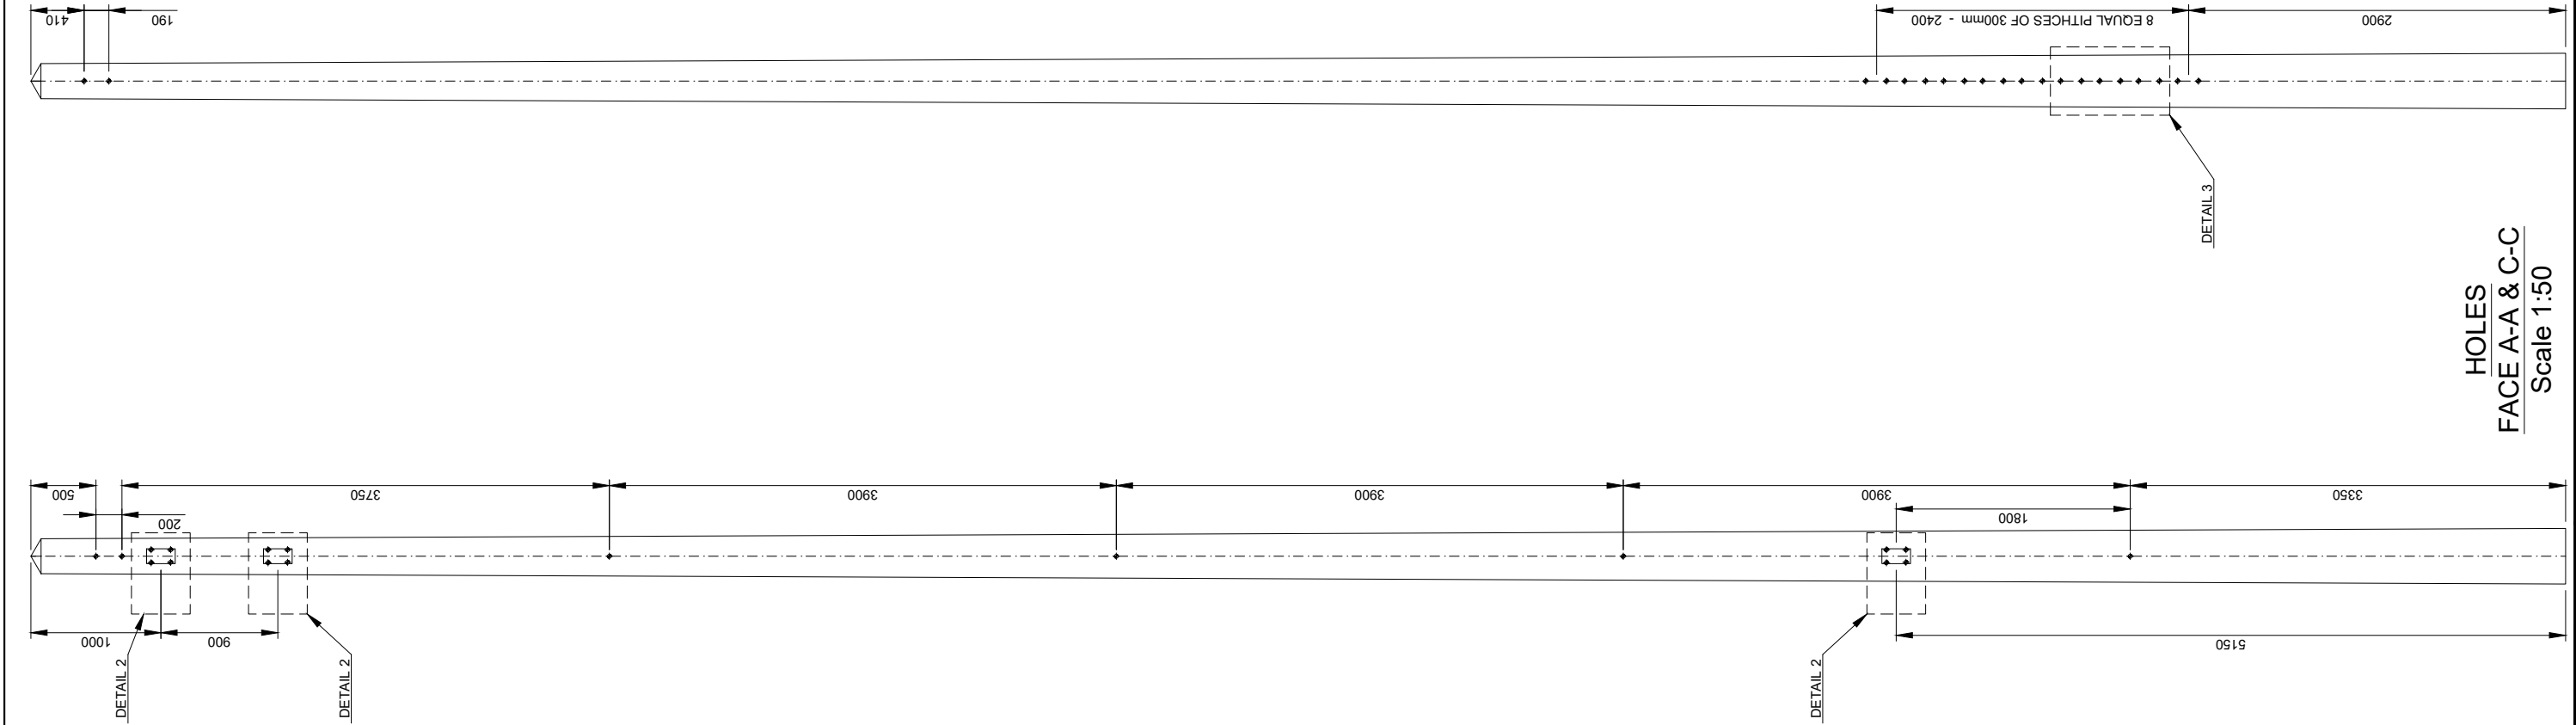


DETAIL 1  
Scale 1:10

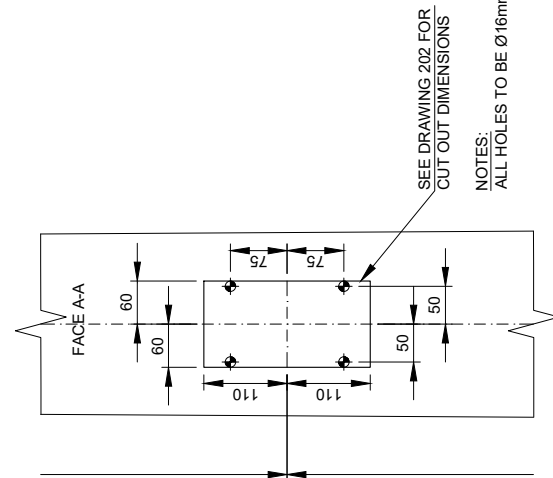

DETAIL 2 - TYPICAL  
Scale 1:10

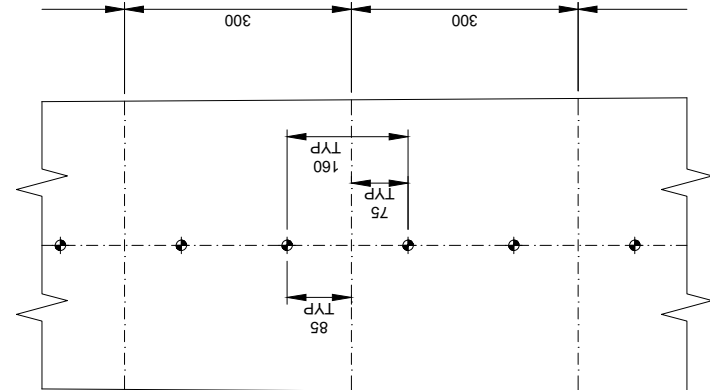


**DETAIL 3 - TYPICAL**  
Scale 1:10

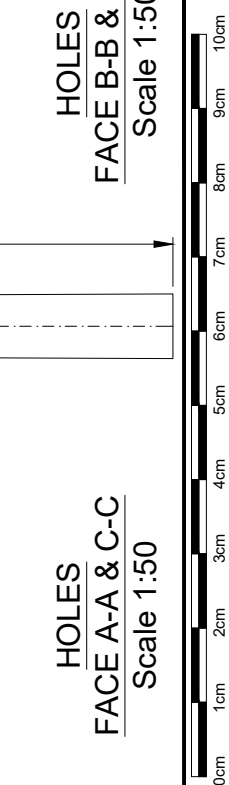

ALL SCALES AS SHOWN WHEN PRINTED AT A3


ALL SCALES AS SHOWN WHEN PRINTED AT A3

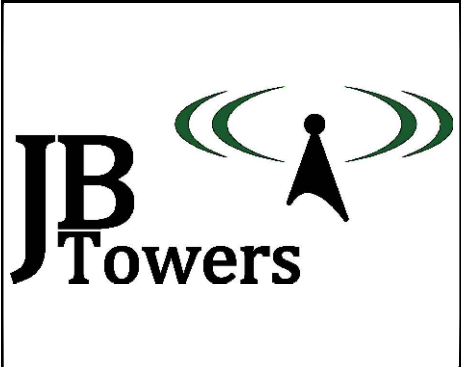


|   |             |       |          |         |          |
|---|-------------|-------|----------|---------|----------|
|   |             |       |          |         |          |
|   |             |       |          |         |          |
|   |             |       |          |         |          |
|   |             |       |          |         |          |
| 01   | FIRST ISSUE |       |          | AM      | 12/10/18 |
| REV   | REV         |       |          | BY      | DATE     |
| SCALE AS SHOWN   |             | DRAWN | AM       | CHECKED | MP       |
| WHEN PRINTED AT A3   |             | DATE  | 12/10/18 | DATE    | 12/10/18 |
|   |             | DATE  | 12/10/18 | DATE    | 12/10/18 |
| ALL DIMENSIONS IN mm UNLESS OTHERWISE STATED.<br>THIS DRAWING TO BE READ IN CONJUNCTION WITH<br>OTHER RELEVANT DRAWINGS. |             |       |          |         |          |

|                          |
|--------------------------|
| TITLE                    |
| BURBAGE                  |
| TIMBER POLE HOLE SET OUT |
| SHEET 2 OF 2             |

|                                                                  |                |           |
|------------------------------------------------------------------|----------------|-----------|
| SITE ADDRESS                                                     |                |           |
| THE PLAYING FIELD<br>GREEN LANE<br>BURBAGE<br>BUXTON<br>SK17 9DG |                |           |
| ARQIVA REF.<br>140357                                            | DRG No.<br>201 | REV<br>01 |

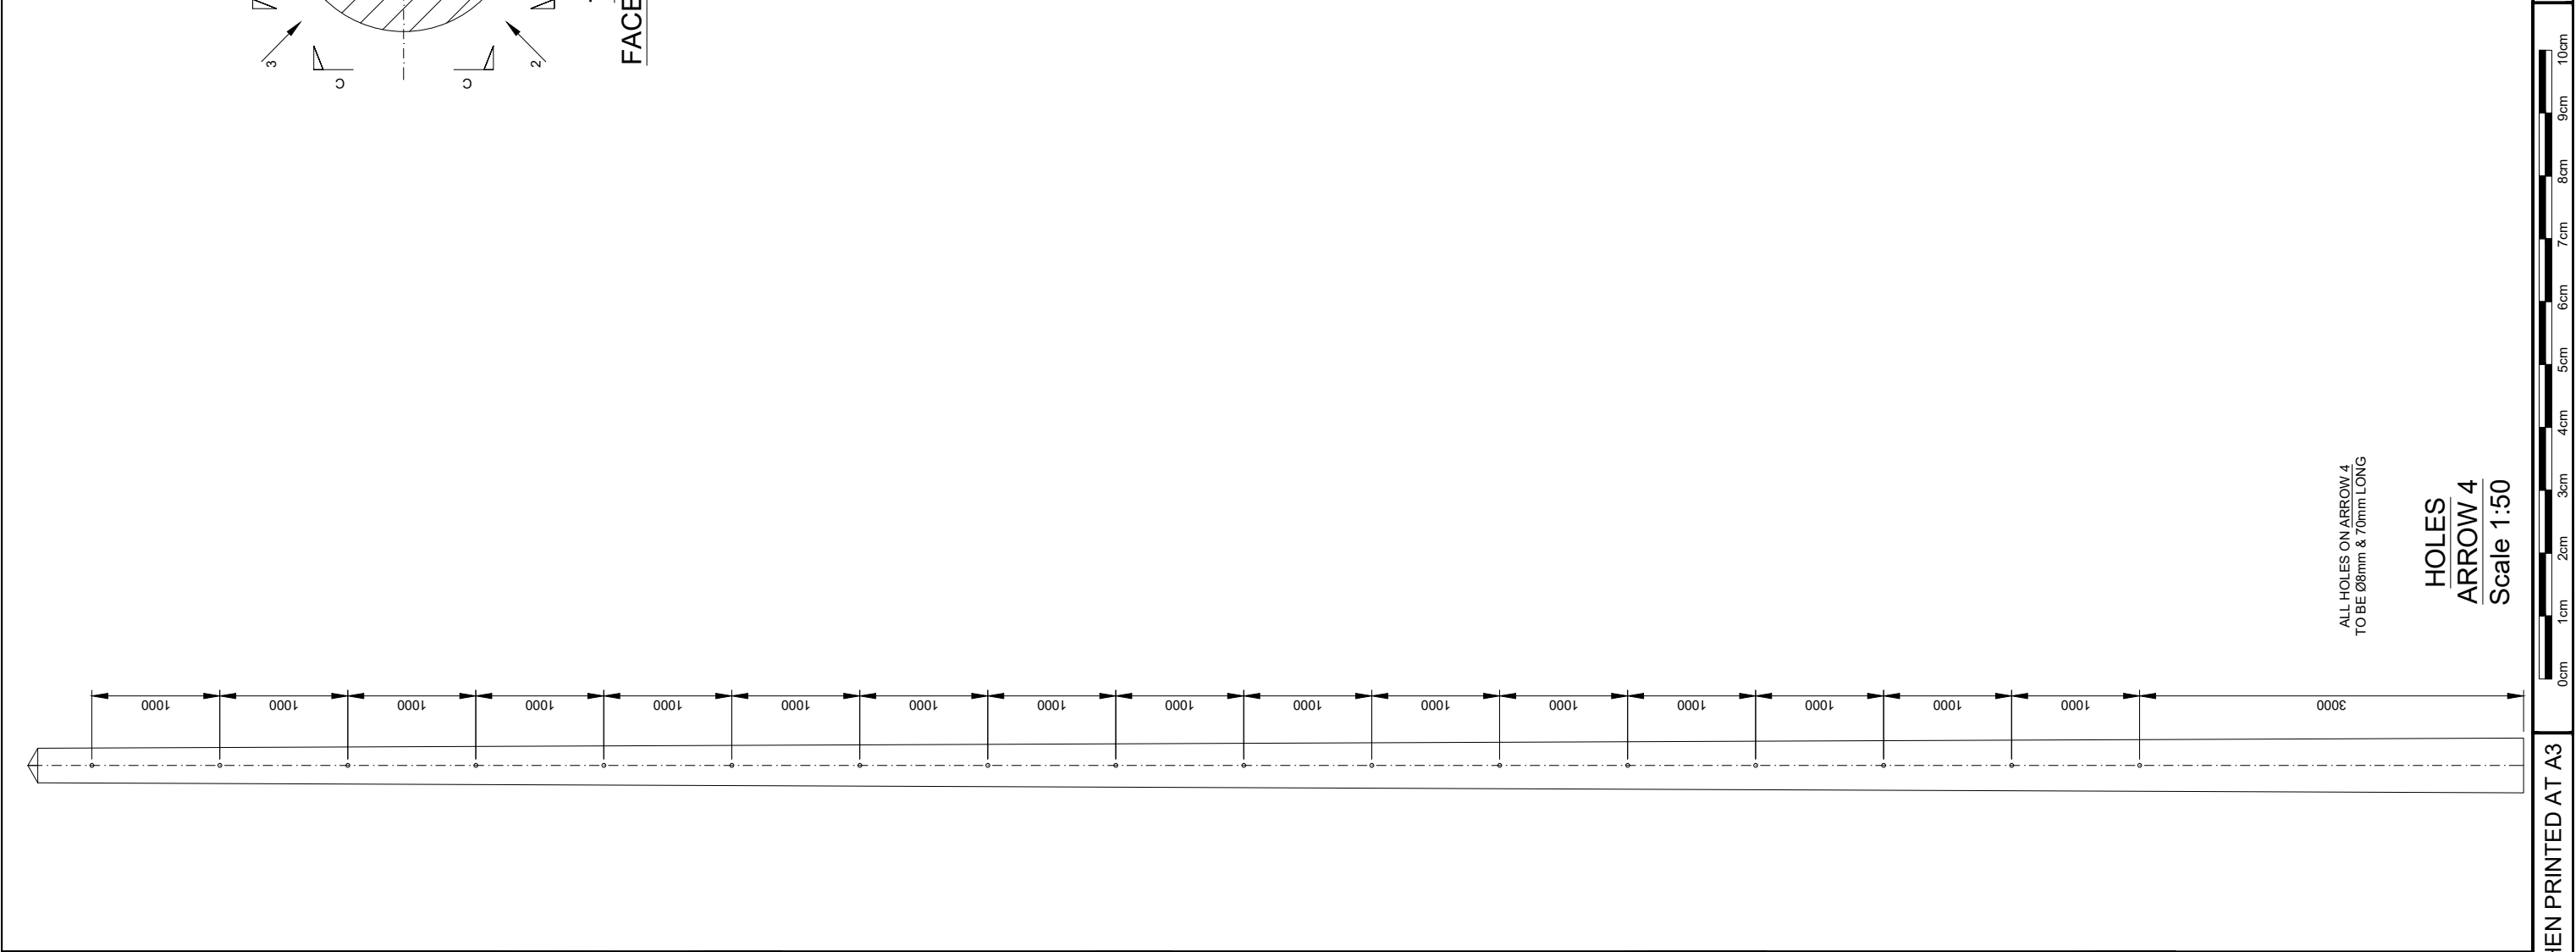



N62 TO BE STAMPED ON  
ARROW 4  
3.5m FROM POLE BUT

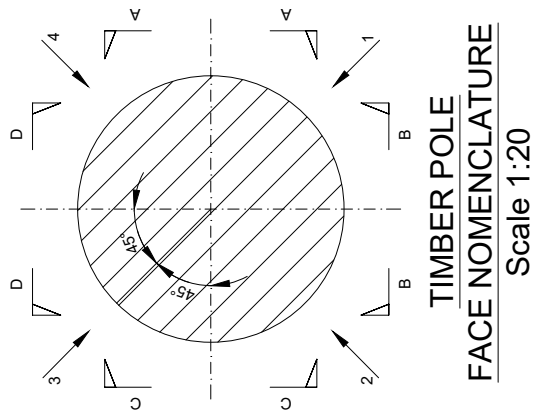

ALL HOLES ON ARROW 4  
TO BE Ø8mm & 70mm LONG

HOLES  
ARROW 4  
Scale 1:50

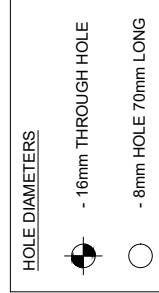

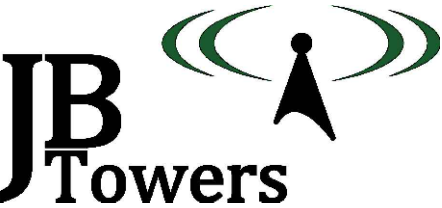

chalcroft  
construction built on teamwork

arqiva

|   |             |       |          |         |          |          |  |          |          |
|---|-------------|-------|----------|---------|----------|----------|--|----------|----------|
|   |             |       |          |         |          |          |  |          |          |
|   |             |       |          |         |          |          |  |          |          |
|   |             |       |          |         |          |          |  |          |          |
|   |             |       |          |         |          |          |  |          |          |
| 01   | FIRST ISSUE |       |          |         |          |          |  | AM       | 12/10/18 |
| REV   | REV         |       |          |         |          |          |  | BY       | DATE     |
| SCALE AS SHOWN   |             | DRAWN | AM       | CHECKED | MP       | APPROVED |  | JBT      |          |
| WHEN PRINTED AT A3   |             | DATE  | 12/10/18 | DATE    | 12/10/18 | DATE     |  | 12/10/18 |          |
| ALL DIMENSIONS IN mm UNLESS OTHERWISE STATED.<br>THIS DRAWING TO BE READ IN CONJUNCTION WITH<br>OTHER RELEVANT DRAWINGS. |             |       |          |         |          |          |  |          |          |


TITLE  
  
BURBAGE  
  
TIMBER POLE CUT OUT  
DETAIL

SITE ADDRESS  
  
THE PLAYING FIELD  
GREEN LANE  
BURBAGE  
BUXTON  
SK17 9DG

ARQIVA REF.  
140357





DRG No.  
202

REV  
01

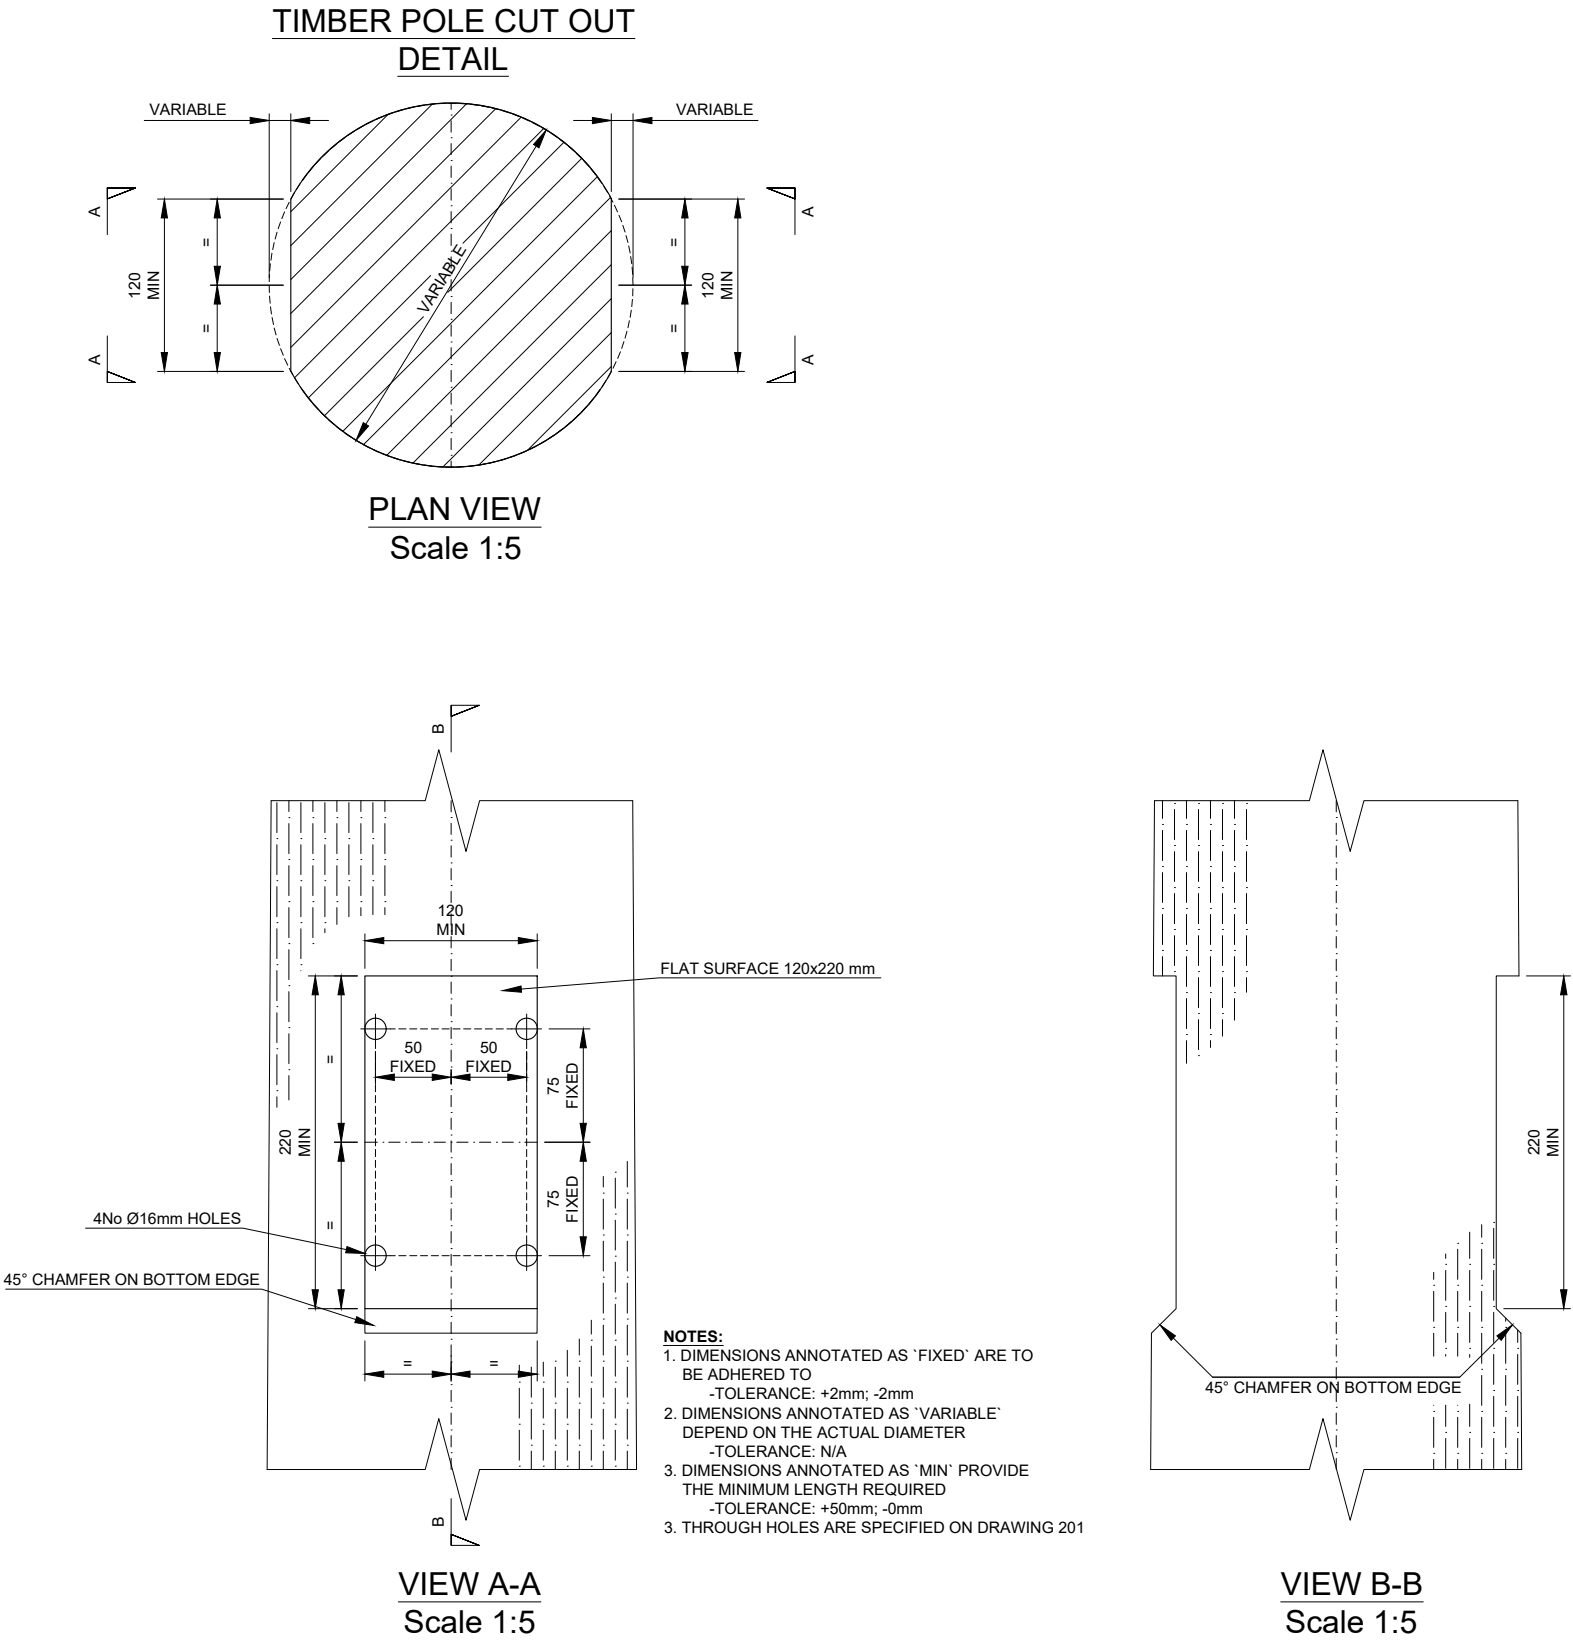

ALL SCALES AS SHOWN WHEN PRINTED AT A3

ALL SCALES AS SHOWN WHEN PRINTED AT A3

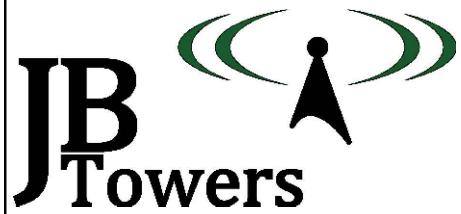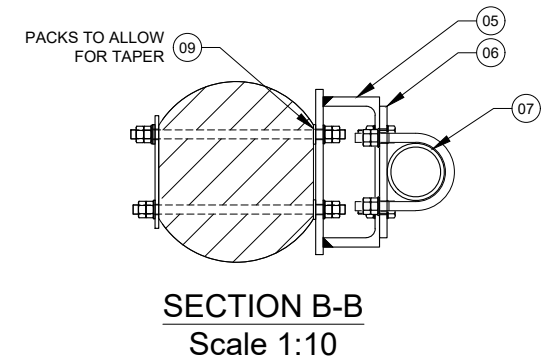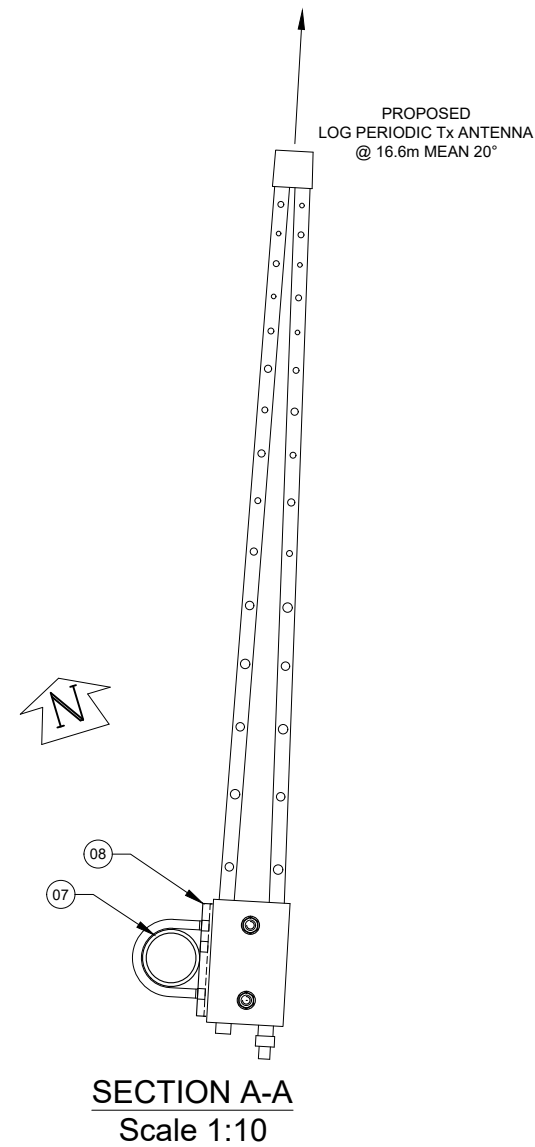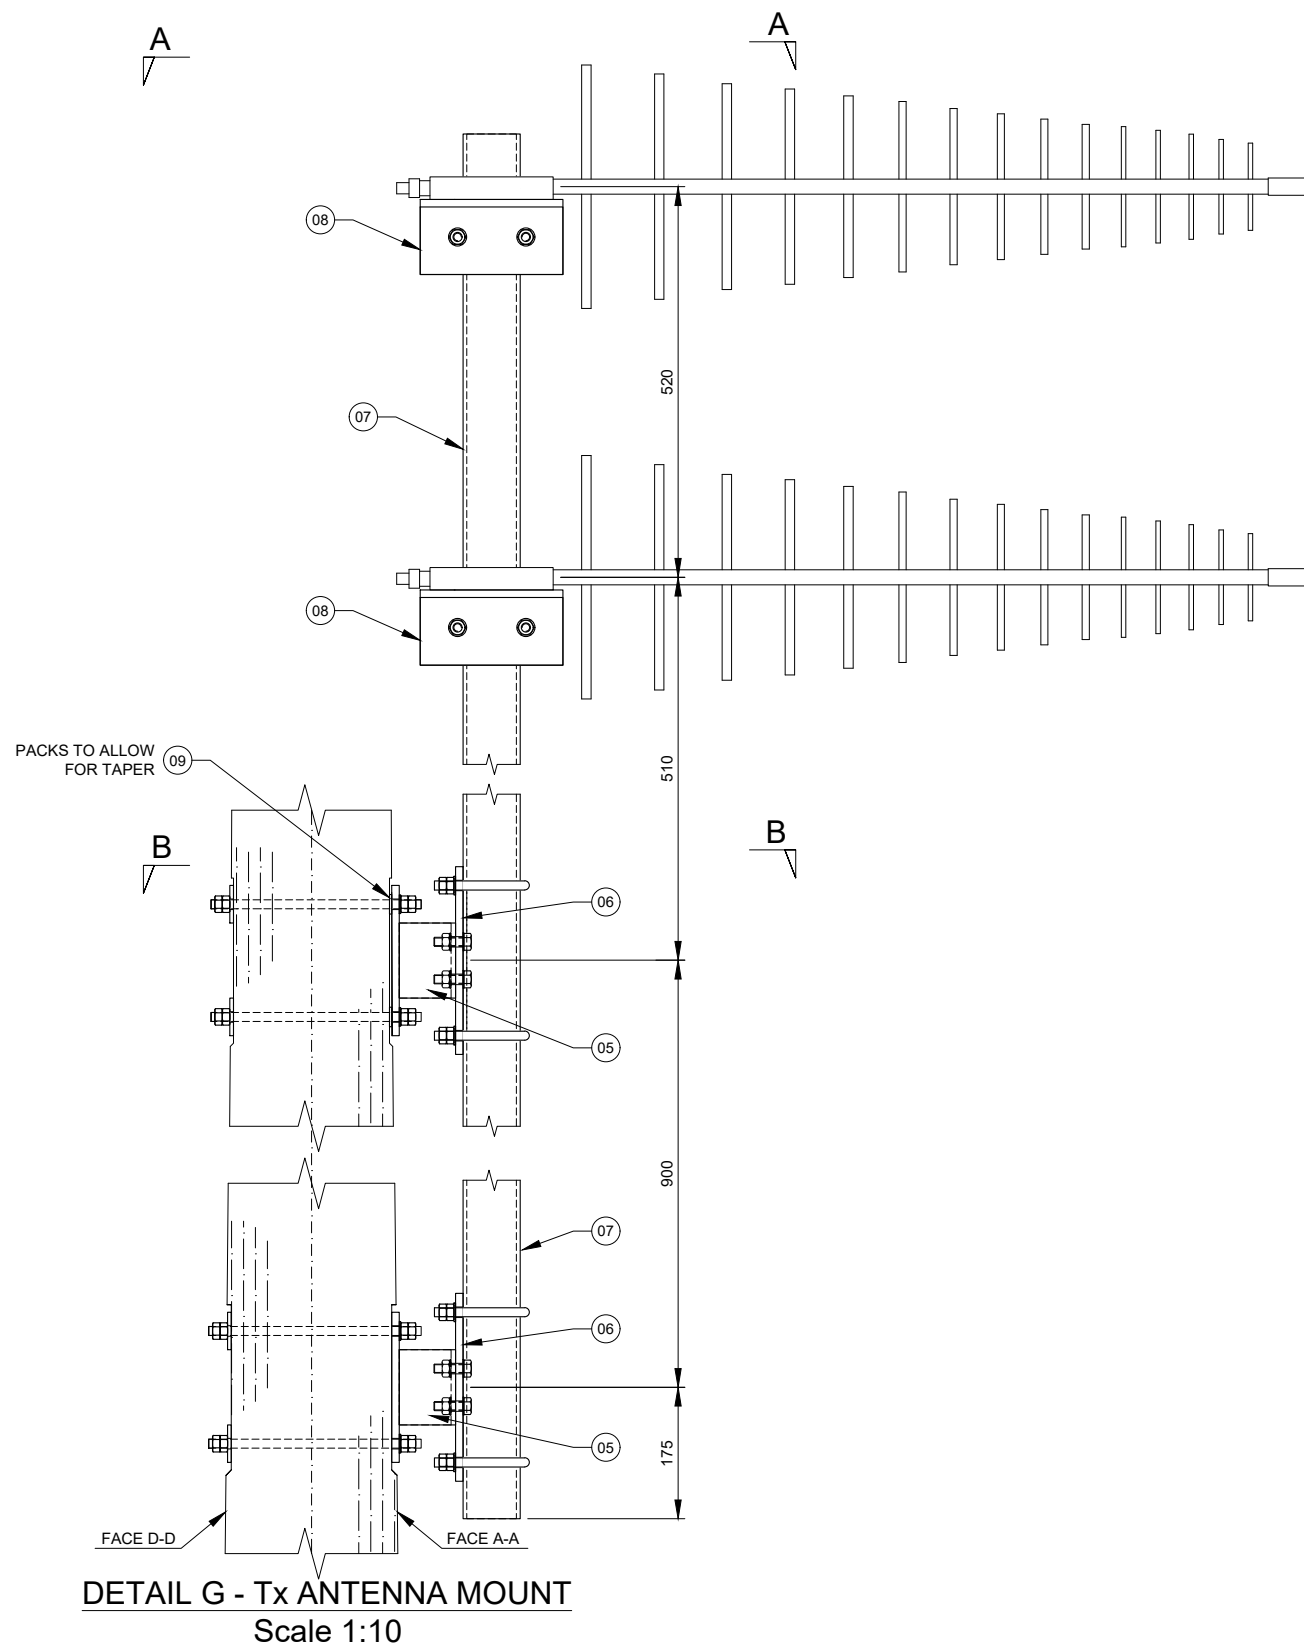

|   |             |       |          |         |          |               |
|---|-------------|-------|----------|---------|----------|---------------|
| 01   | FIRST ISSUE |       |          |         | AM       | 12/10/18      |
| REV   | REV         |       |          |         | BY       | DATE          |
| SCALE AS SHOWN WHEN PRINTED AT A3                                                                                  |             | DRAWN | AM       | CHECKED | MP       | APPROVED JBT  |
|   |             | DATE  | 12/10/18 | DATE    | 12/10/18 | DATE 12/10/18 |
| ALL DIMENSIONS IN mm UNLESS OTHERWISE STATED. THIS DRAWING TO BE READ IN CONJUNCTION WITH OTHER RELEVANT DRAWINGS. |             |       |          |         |          |               |

TITLE  
ANTENNA MOUNT  
DETAIL G

SITE ADDRESS  
THE PLAYING FIELD  
GREEN LANE  
BURBAGE  
BUXTON  
SK17 9DG


ARQIVA REF.  
140357

DRG No.  
203


REV  
01

ALL SCALES AS SHOWN WHEN PRINTED AT A3



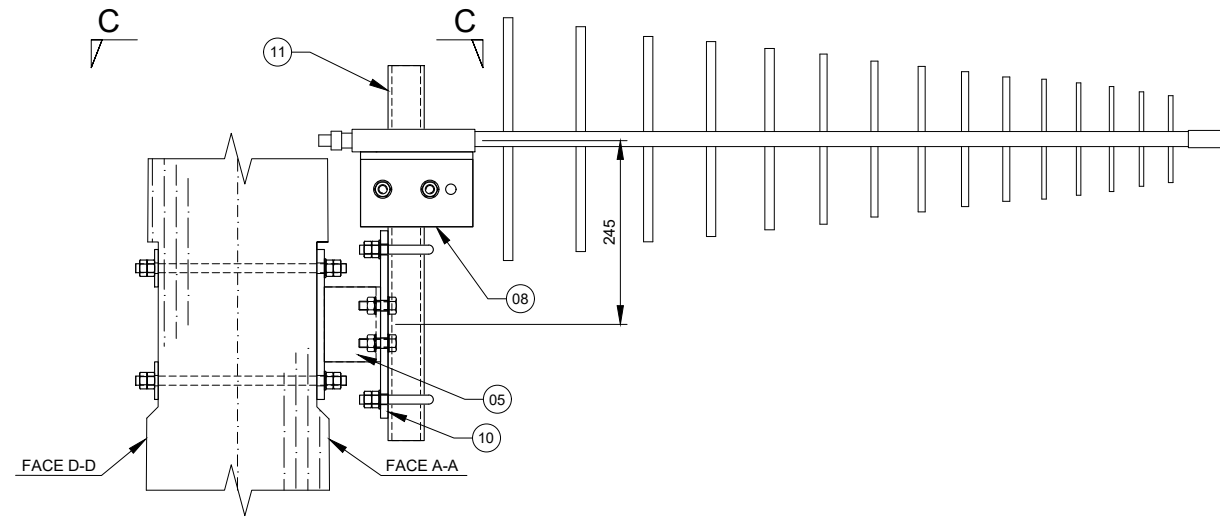


DETAIL H - Rx ANTENNA MOUNT  
Scale 1:10

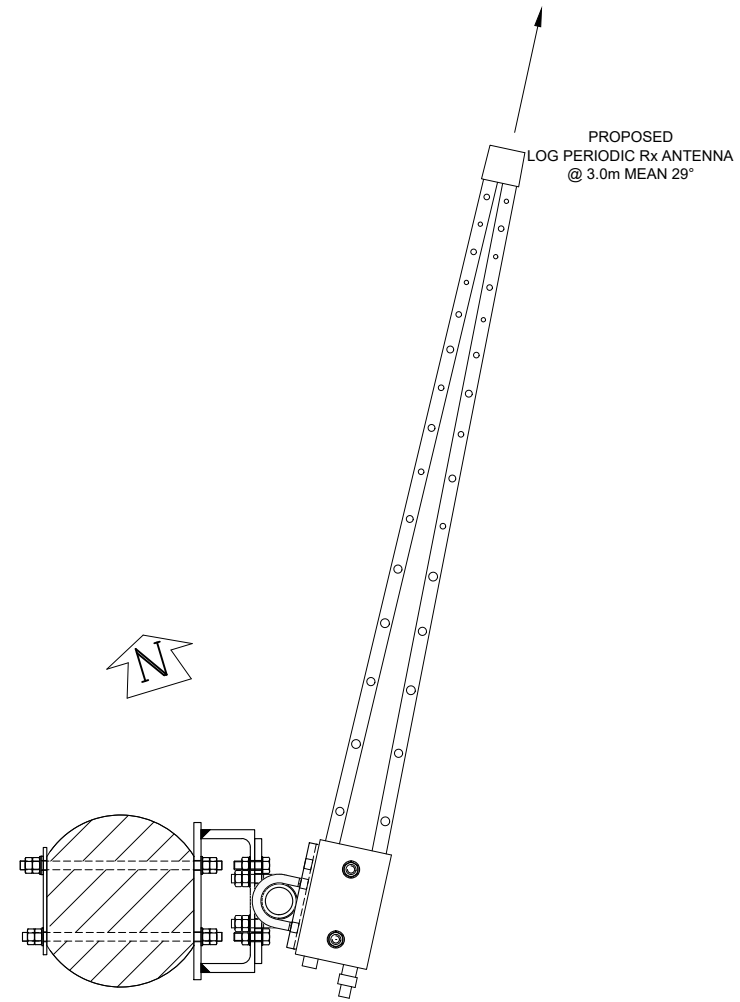

VIEW C-C  
Scale 1:10




ALL SCALES AS SHOWN WHEN PRINTED AT A3

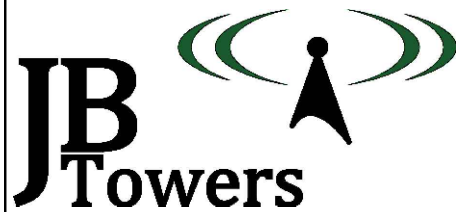

|   |             |       |          |         |          |               |
|---|-------------|-------|----------|---------|----------|---------------|
| 01   | FIRST ISSUE |       |          |         | AM       | 12/10/18      |
| REV   | REV         |       |          |         | BY       | DATE          |
| SCALE AS SHOWN<br>WHEN PRINTED AT A3                                                                                     |             | DRAWN | AM       | CHECKED | MP       | APPROVED JBT  |
|   |             | DATE  | 12/10/18 | DATE    | 12/10/18 | DATE 12/10/18 |
| ALL DIMENSIONS IN mm UNLESS OTHERWISE STATED.<br>THIS DRAWING TO BE READ IN CONJUNCTION WITH<br>OTHER RELEVANT DRAWINGS. |             |       |          |         |          |               |


|                       |  |                   |           |
|-----------------------|--|-------------------|-----------|
| TITLE                 |  | SITE ADDRESS      |           |
| ANTENNA MOUNT         |  | THE PLAYING FIELD |           |
| DETAIL H              |  | GREEN LANE        |           |
|                       |  | BURBAGE           |           |
|                       |  | BUXTON            |           |
|                       |  | SK17 9DG          |           |
| ARQIVA REF.<br>140357 |  | DRG No.<br>204    | REV<br>01 |

ALL SCALES AS SHOWN WHEN PRINTED AT A3

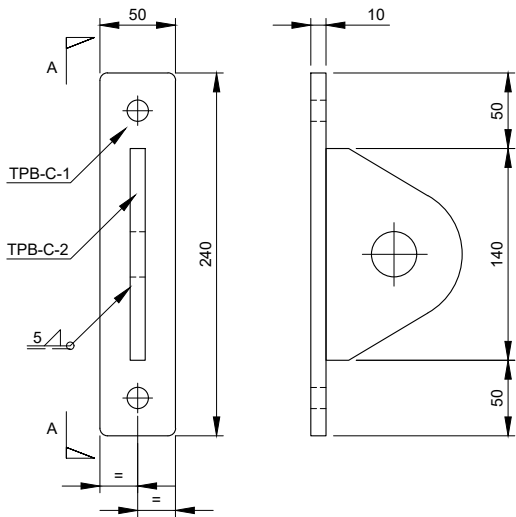

PART TPB-C  
Scale 1:5

VIEW A-A  
Scale 1:5

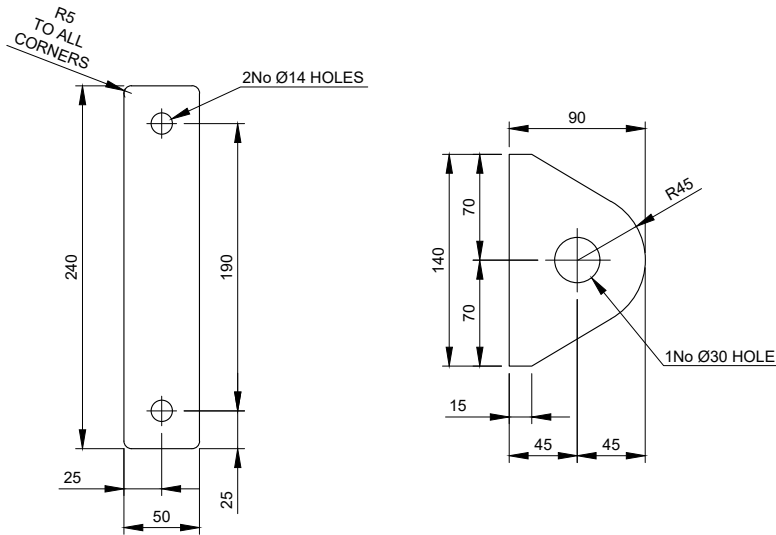


TPB-C-1 - 10mm THICK  
Scale 1:5

TPB-C-2 - 10mm THICK  
Scale 1:5

Parts list for TPB-C

| Item          | Part    | Quantity | Part description | Length | Material  | Weight  |
|---------------|---------|----------|------------------|--------|-----------|---------|
| 01            | TPB-C-1 | 1        | 240x50x10mm      | N/A    | S275J0    | 0.94 kg |
| 02            | TPB-C-2 | 1        | 140x90x10mm      | N/A    | S275J0    | 0.99 kg |
| 03            | STUDS   | 1        | M12 STUDDING     | 350mm  | GRADE 8.8 | 0.31 kg |
| Total Weight: |         |          |                  |        |           | 2.24 kg |

- All steel hot dip galvanized
- Each STUD to be supplied with 4 Full Nuts, 2 Flat Washers and 2 Spring Washers
- For fabrctation notes see drawing 303

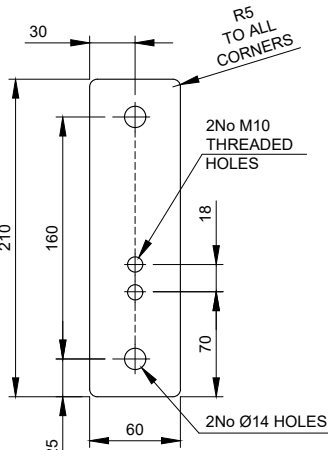


PART TPS-R  
Scale 1:5

Parts list for TPS-R

| Item          | Part  | Quantity | Part description | Length | Material  | Weight  |
|---------------|-------|----------|------------------|--------|-----------|---------|
| 01            | TPS-R | 2        | 210x60x15mm      | N/A    | S275J0    | 1.48 kg |
| 02            | STUDS | 2        | M12 STUDDING     | 500mm  | GRADE 8.8 | 0.44 kg |
| 03            | NUT-S | 2        | M12 SHALLOW NUT  | N/A    | GRADE 8.8 | -       |
| 04            | NUT   | 4        | M12 NUT          | N/A    | GRADE 8.8 | -       |
| 03            | WSH   | 4        | M12 WASHER       | N/A    | GRADE 8.8 | -       |
| Total Weight: |       |          |                  |        |           | 3.40 kg |

- All steel hot dip galvanized
- For fabrctation notes see drawing 303

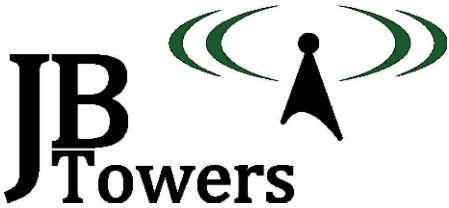

|   |                        |                          |                           |
|---|------------------------|--------------------------|---------------------------|
| 01   | FIRST ISSUE            | AM                       | 12/10/18                  |
| REV   | REV                    | BY                       | DATE                      |
| SCALE AS SHOWN<br>WHEN PRINTED AT A3                                                                                     | DRAWN<br>DATE 12/10/18 | CHECKED<br>DATE 12/10/18 | APPROVED<br>DATE 12/10/18 |
| ALL DIMENSIONS IN mm UNLESS OTHERWISE STATED.<br>THIS DRAWING TO BE READ IN CONJUNCTION WITH<br>OTHER RELEVANT DRAWINGS. |                        |                          |                           |

TITLE  
ATTACHMENT POINT &  
TEMPORARY STEP DETAILS  
PARTS: TPB-C; TPS-R

SITE ADDRESS  
THE PLAYING FIELD  
GREEN LANE  
BURBAGE  
BUXTON  
SK17 9DG

ARQIVA REF.  
140357  
DRG No.  
300  
REV  
01

ALL SCALES AS SHOWN WHEN PRINTED AT A3



ALL SCALES AS SHOWN WHEN PRINTED AT A3

|   |             |       |          |         |          |               |
|---|-------------|-------|----------|---------|----------|---------------|
| 01   | FIRST ISSUE |       |          |         | AM       | 12/10/18      |
| REV   | REV         |       |          |         | BY       | DATE          |
| SCALE AS SHOWN   |             | DRAWN | AM       | CHECKED | MP       | APPROVED JBT  |
| WHEN PRINTED AT A3   |             | DATE  | 12/10/18 | DATE    | 12/10/18 | DATE 12/10/18 |
| ALL DIMENSIONS IN mm UNLESS OTHERWISE STATED.<br>THIS DRAWING TO BE READ IN CONJUNCTION WITH<br>OTHER RELEVANT DRAWINGS. |             |       |          |         |          |               |

TITLE

STEELWORK BRACKET

PART: TPB-B







SITE ADDRESS

THE PLAYING FIELD  
GREEN LANE  
BURBAGE  
BUXTON  
SK17 9DG

ARQIVA REF.  
140357

DRG No.  
301

REV  
01

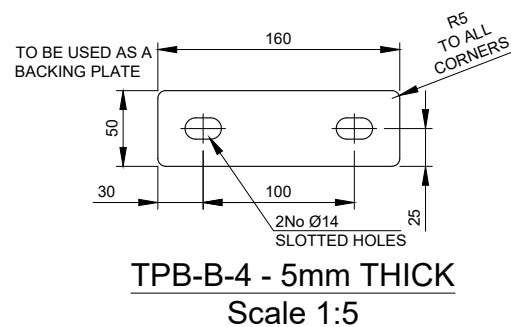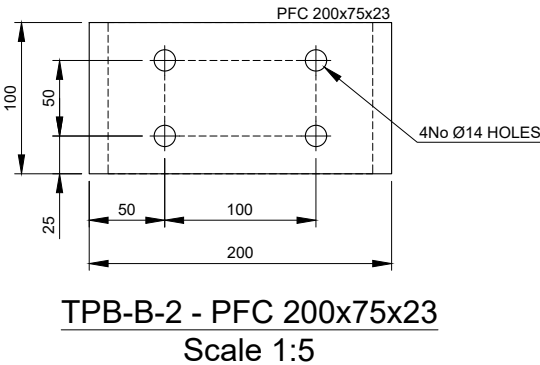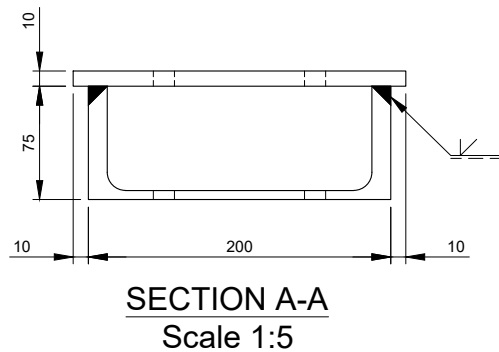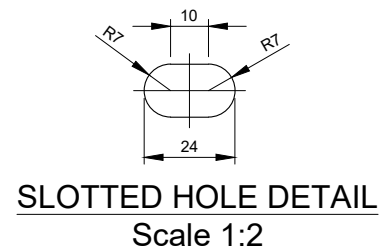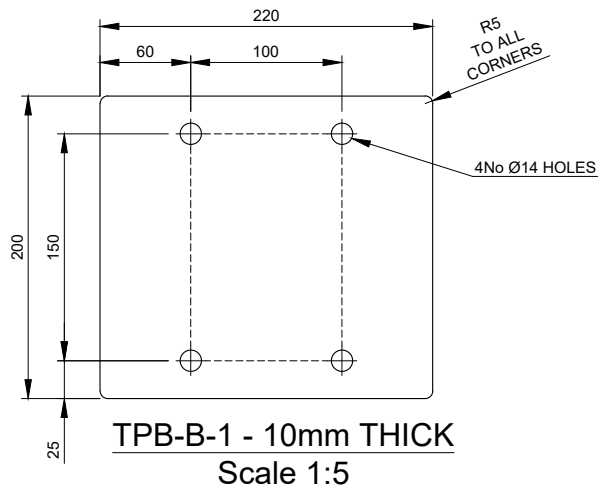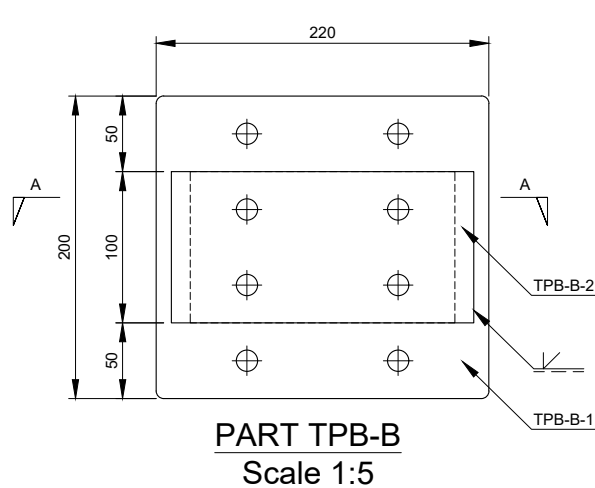


Parts list for TPB-B

| Item | Part    | Quantity | Part description | Length | Material  | Weight  |
|------|---------|----------|------------------|--------|-----------|---------|
| 01   | TPB-B-1 | 1        | 220x200x10mm     | N/A    | S275J0    | 3.45 kg |
| 02   | TPB-B-2 | 1        | PFC 200x75x23    | 100mm  | S275J0    | 2.30 kg |
| 03   | TPB-B-4 | 2        | 160x50x5mm       | N/A    | S275J0    | 0.31 kg |
| 04   | STUDS   | 4        | M12 STUDDING     | 400mm  | GRADE 8.8 | 0.35 kg |

Total Weight: 7.77 kg


- All steel hot dip galvanized
- Each STUD & U-BOLT to be supplied with 4 Full Nuts, 2 Flat Washers and 2 Spring Washers
- Each BOLT to be supplied with 1 Full Nut, 1 Form E FLat Washer and 1 Spring Washer
- For fabrctation notes see drawing 303

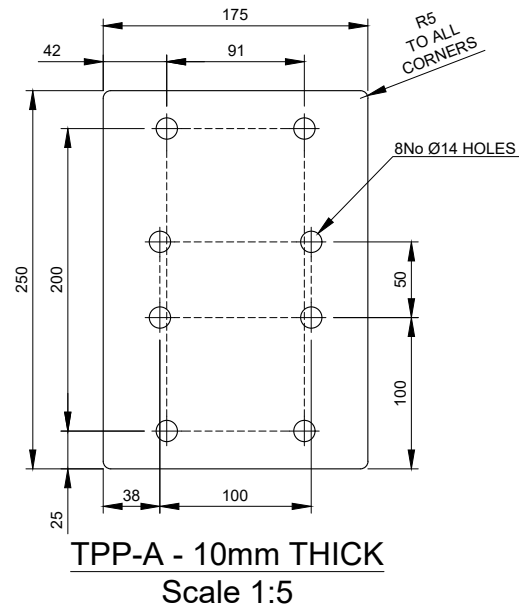

Parts list for TPP-A

| Item          | Part   | Quantity | Part description          | Length | Material  | Weight  |
|---------------|--------|----------|---------------------------|--------|-----------|---------|
| 01            | TPP-A  | 1        | 250x175x10mm              | N/A    | S275J0    | 3.45 kg |
| 02            | BOLT   | 4        | M12 45mm LONG (2D+6)      | 45mm   | GRADE 8.8 | -       |
| 03            | U-BOLT | 3        | M12 U-BOLT FOR CHS 76.1mm | N/A    | GRADE 8.8 | -       |
| Total Weight: |        |          |                           |        |           | 3.45 kg |


- All steel hot dip galvanized
- Each STUD & U-BOLT to be supplied with 4 Full Nuts, 2 Flat Washers and 2 Spring Washers
- Each BOLT to be supplied with 1 Full Nut, 1 Form E FLat Washer and 1 Spring Washer
- 1No U-BOLT to be used for TPL-A
- For fabrctation notes see drawing 303

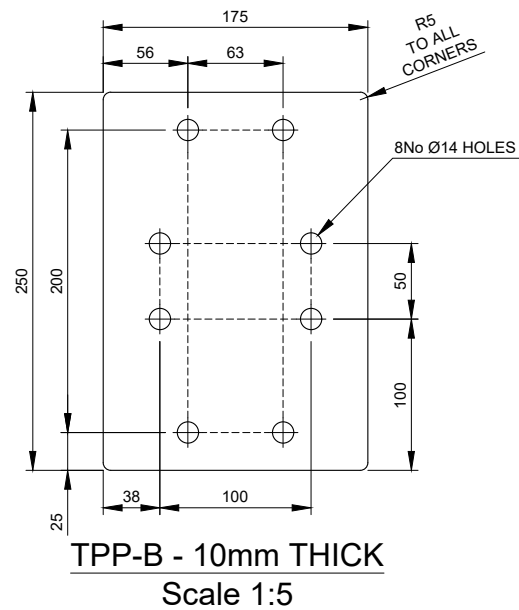

Parts list for TPP-B

| Item          | Part   | Quantity | Part description          | Length | Material  | Weight  |
|---------------|--------|----------|---------------------------|--------|-----------|---------|
| 01            | TPP-B  | 1        | 250x175x10mm              | N/A    | S275J0    | 3.45 kg |
| 02            | BOLT   | 4        | M12 45mm LONG (2D+6)      | 45mm   | GRADE 8.8 | -       |
| 03            | U-BOLT | 3        | M12 U-BOLT FOR CHS 48.3mm | N/A    | GRADE 8.8 | -       |
| Total Weight: |        |          |                           |        |           | 3.45 kg |


- All steel hot dip galvanized
- Each STUD & U-BOLT to be supplied with 4 Full Nuts, 2 Flat Washers and 2 Spring Washers
- Each BOLT to be supplied with 1 Full Nut, 1 Form E FLat Washer and 1 Spring Washer
- 1No U-BOLT to be used for TPL-A
- For fabrctation notes see drawing 303

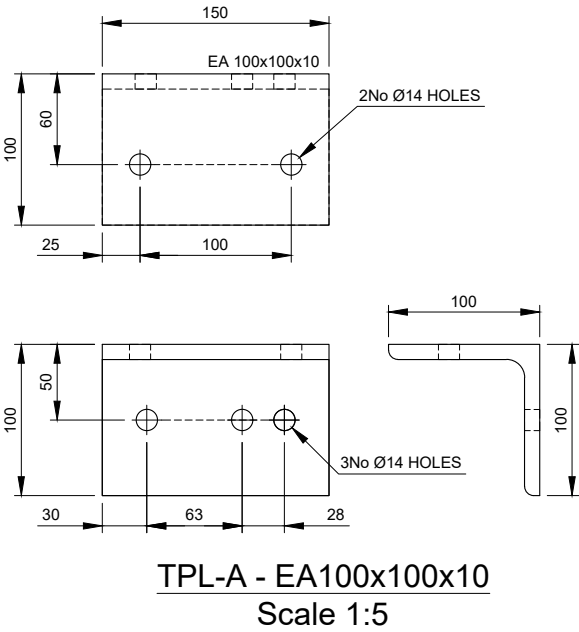

Parts list for TPL-A

| Item          | Part  | Quantity | Part description       | Length | Material  | Weight  |
|---------------|-------|----------|------------------------|--------|-----------|---------|
| 01            | TPL-A | 1        | EA100x100x10           | 150mm  | S275J0    | 2.25 kg |
| 02            | BOLT  | 2        | M12 55mm LONG SET BOLT | 55mm   | GRADE 8.8 | -       |
| Total Weight: |       |          |                        |        |           | 2.25 kg |

- All steel hot dip galvanized
- Each STUD & U-BOLT to be supplied with 4 Full Nuts, 2 Flat Washers and 2 Spring Washers
- Each BOLT to be supplied with 1 Full Nut, 1 Form E FLat Washer and 1 Spring Washer
- For fabrctation notes see drawing 303

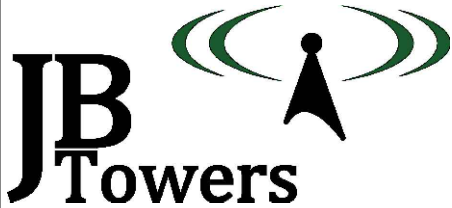

|   |             |         |          |
|---|-------------|---------|----------|
| 01   | FIRST ISSUE | AM      | 12/10/18 |
| REV   | REV         | BY      | DATE     |
| SCALE AS SHOWN   | DRAWN       | CHECKED | APPROVED |
| WHEN PRINTED AT A3   | AM          | MP      | JBT      |
| DATE   | 12/10/18    | DATE    | 12/10/18 |
| DATE   | 12/10/18    | DATE    | 12/10/18 |
| ALL DIMENSIONS IN mm UNLESS OTHERWISE STATED.<br>THIS DRAWING TO BE READ IN CONJUNCTION WITH<br>OTHER RELEVANT DRAWINGS. |             |         |          |

TITLE  
INTERFACE PLATES &  
LOG MOUNT  
PARTS: TPP-A; TPP-B; TPL-A

SITE ADDRESS  
THE PLAYING FIELD  
GREEN LANE  
BURBAGE  
BUXTON  
SK17 9DG

ARQIVA REF.  
140357  
DRG No.  
302  
REV  
01

ALL SCALES AS SHOWN WHEN PRINTED AT A3




ALL SCALES AS SHOWN WHEN PRINTED AT A3

| Item | Part  | Drawing | Quantity | Part description                                                                   | Length | Material             | Weight    |
|------|-------|---------|----------|------------------------------------------------------------------------------------|--------|----------------------|-----------|
| 01   | 01    | 200     | 1        | 3 MAN LATCHWAY SYSTEM & 3No. WIRE GUIDES FOR FACE MOUNTED MONOPOLE                 | 17000  | N/A                  | -         |
| 02   | TPB-C | 300     | 2        | FALL ARREST ATTACHMENT POINT                                                       | N/A    | S275J0               | 4.48 kg   |
| 03   | 03    | 200     | 46       | PERMANENT BT STEP c/w 3No 10x75mm ZINC-PLATED COACH SCREWS                         | N/A    | S275J0               | 13.80 kg  |
| 04   | TPS-R | 300     | 9        | 'MonoStep' ASSEMBLY                                                                | N/A    | S275J0               | 30.60 kg  |
| 05   | TPB-B | 301     | 3        | MOUNTING BRACKET                                                                   | N/A    | S275J0               | 23.31 kg  |
| 06   | TPP-A | 302     | 2        | PLATE A INTERFACE                                                                  | N/A    | S275J0               | 6.90 kg   |
| 07   | 07    | 203     | 1        | CHS 76.1x5mm                                                                       | 2000mm | S355J2H              | 17.54 kg  |
| 08   | TPL-A | 302     | 3        | LOG MOUNTING BRACKET                                                               | 150mm  | S275J0               | 6.75 kg   |
| 09   | 09    | 203     | 12       | M12 WASHER                                                                         | N/A    | GRADE 8.8            | -         |
| 10   | TPP-B | 302     | 1        | PLATE B INTERFACE                                                                  | N/A    | S275J0               | 3.45 kg   |
| 11   | 11    | 204     | 1        | CHS 48.3x5mm                                                                       | 600mm  | S355J2H              | 3.20 kg   |
| 12   | 12    | 200     | 1        | FEEDER COVER - 2/CG/100                                                            | 3500mm | UV RESISTANT PLASTIC | -         |
| 13   | 13    | 200     | 17       | FEEDER CLAMP - 2/FCD/028                                                           | N/A    | POLYPROPYLENE        | -         |
| 14   | 14    | 200     | 17       | M10 SCREW DOWELS WTH M10 NUT                                                       | 100mm  | STAINLESS STEEL      | -         |
| 15   | 15    | 200     | 1        | PoleSaver                                                                          | 750mm  | N/A                  | -         |
| 16   | 16    | 200     | 8        | M12 STUD + 4No NUTS + 2No FLAT WASHERS + 1No Ø50mm WASHER (FOR FALL ARREST SYSTEM) | 500mm  | GRADE 8.8            | 3.56 kg   |
|      |       |         |          |                                                                                    |        | Total Weight:        | 113.59 kg |

- All steel hot dip galvanized  
- All U-BOLTS to be FLA supply, each Supplied with 4 Full Nuts, 2 Flat Washers and 2 Spring Washers

NOTES:

1. WELDING TO BE IN ACCORDANCE WITH BS EN 1011-1:2009
2. LINEAR DIMS TO BE WITHIN ±1mm;
3. ANGULAR TOLERANCES TO BE WITHIN 0.5°
4. WELDING SYMBOLS ARE IN ACCORDANCE WITH BS EN 22553:1995
5. ALL PROFILE EDGES TO BE DRESSED AND SHARP CORNERS REMOVED
6. ALL WELD SIZES ARE FINAL SIZES
7. ALL WELDED JOINTS ARE TO BE PICKLE TIGHT
8. ALL STEELWORK TO BE BS EN 10025 GRADE S275 J0 UNO & 9. HOT DIPPED GALVANISED TO BS EN ISO 1461. (ALL HOLLOW SECTIONS TO BE GRADE S355 J0H)
10. ALL STEEL IS TO BE SUPPLIED IN ACCORDANCE WITH EN 1090 TO EXECUTION CLASS 2
11. ALL NON PRE-LOADED BOLTS TO BE COMPLIANT STRUCTURAL BOLTS TO BS EN ISO 15048 PARTS 1&2.
12. STEELWORK COMPONENTS SHALL BE HOT DIP GALVANISED TO ACHIEVE A "VERY HIGH" DURABILITY FOR AN ENVIRONMENT CATEGORY CODE C4 FROM TABLE 1 IN BS EN ISO 14713
13. BOLTS AND NUTS SHALL BE SUPPLIED IN ACCORDANCE WITH BS 7371, SPUN GALVANISED IN ACCORDANCE WITH ISO 10684, THE NUTS RE-TAPPED AFTER GALVANISING, AND THE THREADS TREATED WITH GREASE.
14. ALL BOLTS TO BE CUT ON SITE TO EXTEND MAX 10mm BEYOND THE NUT WHEN TIGHTENED UNO.
15. ALL SITE DRILLED HOLE/CUT ENDS TO BE TREATED WITH METAFLUX 70-40 ZINC PASTE FOLLOWED BY 1 COAT OF 7-42 ZINC ALU OR 70-16 ALUMINIUM SPRAY

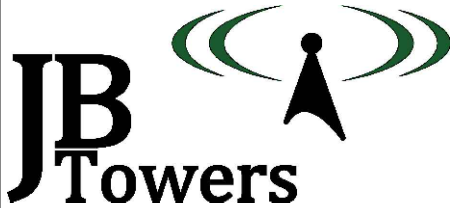

|   |             |               |                |                 |                 |
|---|-------------|---------------|----------------|-----------------|-----------------|
|   |             |               |                |                 |                 |
|   |             |               |                |                 |                 |
|   |             |               |                |                 |                 |
|   |             |               |                |                 |                 |
| 01   | FIRST ISSUE |               |                | AM              | 12/10/18        |
| REV   | REV         |               |                | BY              | DATE            |
| SCALE AS SHOWN<br>WHEN PRINTED AT A3                                                                                     |             | DRAWN<br>DATE | AM<br>12/10/18 | CHECKED<br>DATE | MP<br>12/10/18  |
|   |             |               |                | APPROVED        | JBT<br>12/10/18 |
| ALL DIMENSIONS IN mm UNLESS OTHERWISE STATED.<br>THIS DRAWING TO BE READ IN CONJUNCTION WITH<br>OTHER RELEVANT DRAWINGS. |             |               |                |                 |                 |

|            |
|------------|
| TITLE      |
| PARTS LIST |

|                                                                  |                |           |
|------------------------------------------------------------------|----------------|-----------|
| SITE ADDRESS                                                     |                |           |
| THE PLAYING FIELD<br>GREEN LANE<br>BURBAGE<br>BUXTON<br>SK17 9DG |                |           |
| ARQIVA REF.<br>140357                                            | DRG No.<br>303 | REV<br>01 |

ALL SCALES AS SHOWN WHEN PRINTED AT A3



ALL SCALES AS SHOWN WHEN PRINTED AT A3