
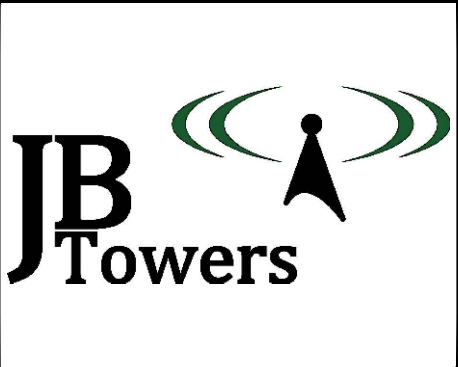


DRAWING ISSUE SHEET

[illegible]

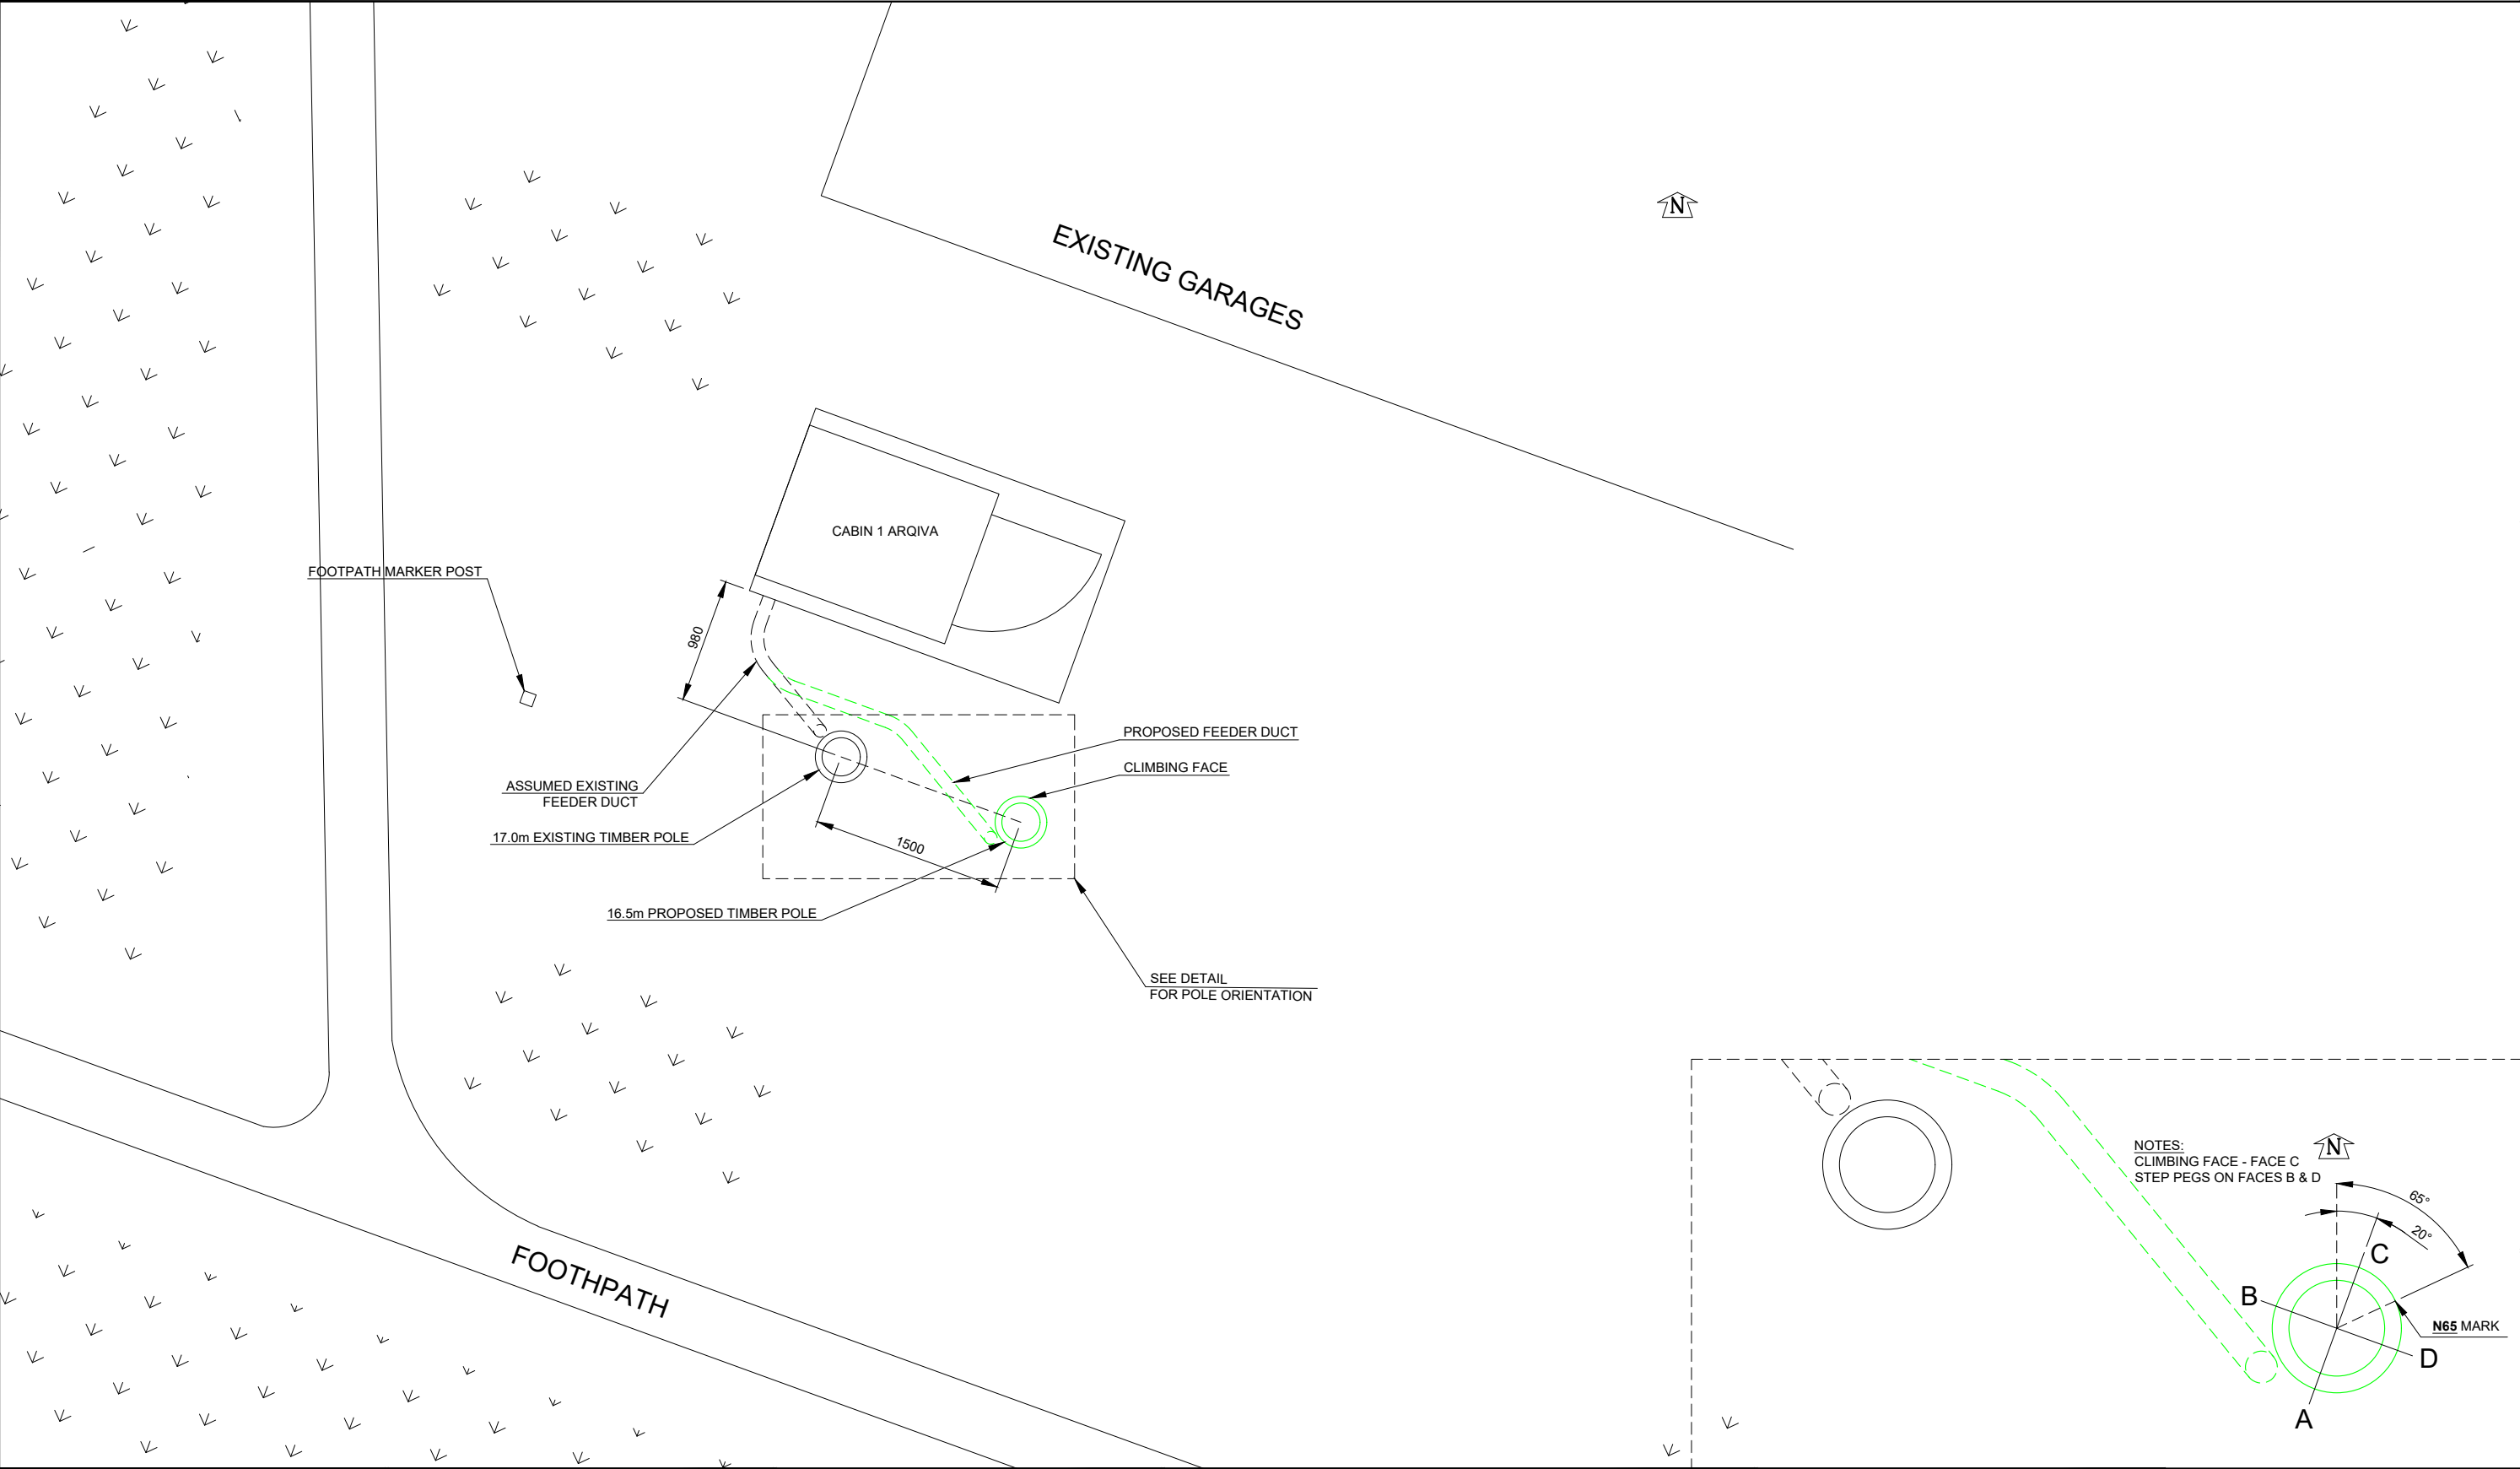


02	CUSTOMER COMMENTS				AM	18/10/18
01	FIRST ISSUE				AM	10/10/18
REV	REV				BY	DATE
SCALE AS SHOWN		DRAWN	AM	CHECKED	MP	APPROVED JBT
WHEN PRINTED AT A3		DATE	10/10/18	DATE	10/10/18	DATE 10/10/18
ALL DIMENSIONS IN mm UNLESS OTHERWISE STATED.						THIS DRAWING TO BE READ IN CONJUNCTION WITH OTHER RELEVANT DRAWINGS.

TITLE

COLDEAN

SITE PLAN

SITE ADDRESS		
THE MEADS COLDEAN BRIGHTON EAST SUSSEX BN1 9BA		
ARQIVA REF. 140357	DRG No. 100	REV 02

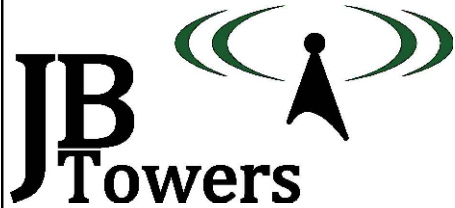

02	CUSTOMER COMMENTS			AM	18/10/18
01	FIRST ISSUE			AM	10/10/18
REV	REV			BY	DATE
SCALE AS SHOWN WHEN PRINTED AT A3		DRAWN	AM	CHECKED	MP
		DATE	10/10/18	DATE	10/10/18
APPROVED					
JBT					
DATE 10/10/18					
ALL DIMENSIONS IN mm UNLESS OTHERWISE STATED. THIS DRAWING TO BE READ IN CONJUNCTION WITH OTHER RELEVANT DRAWINGS.					



TITLE
COLDEAN
GENERAL ARRANGEMENT
SHEET 1 OF 3

SITE ADDRESS
THE MEADS
COLDEAN
BRIGHTON
EAST SUSSEX
BN1 9BA

ARQIVA REF.
140357

DRG No.
200

REV
02

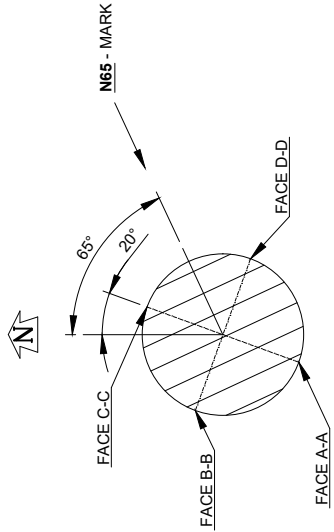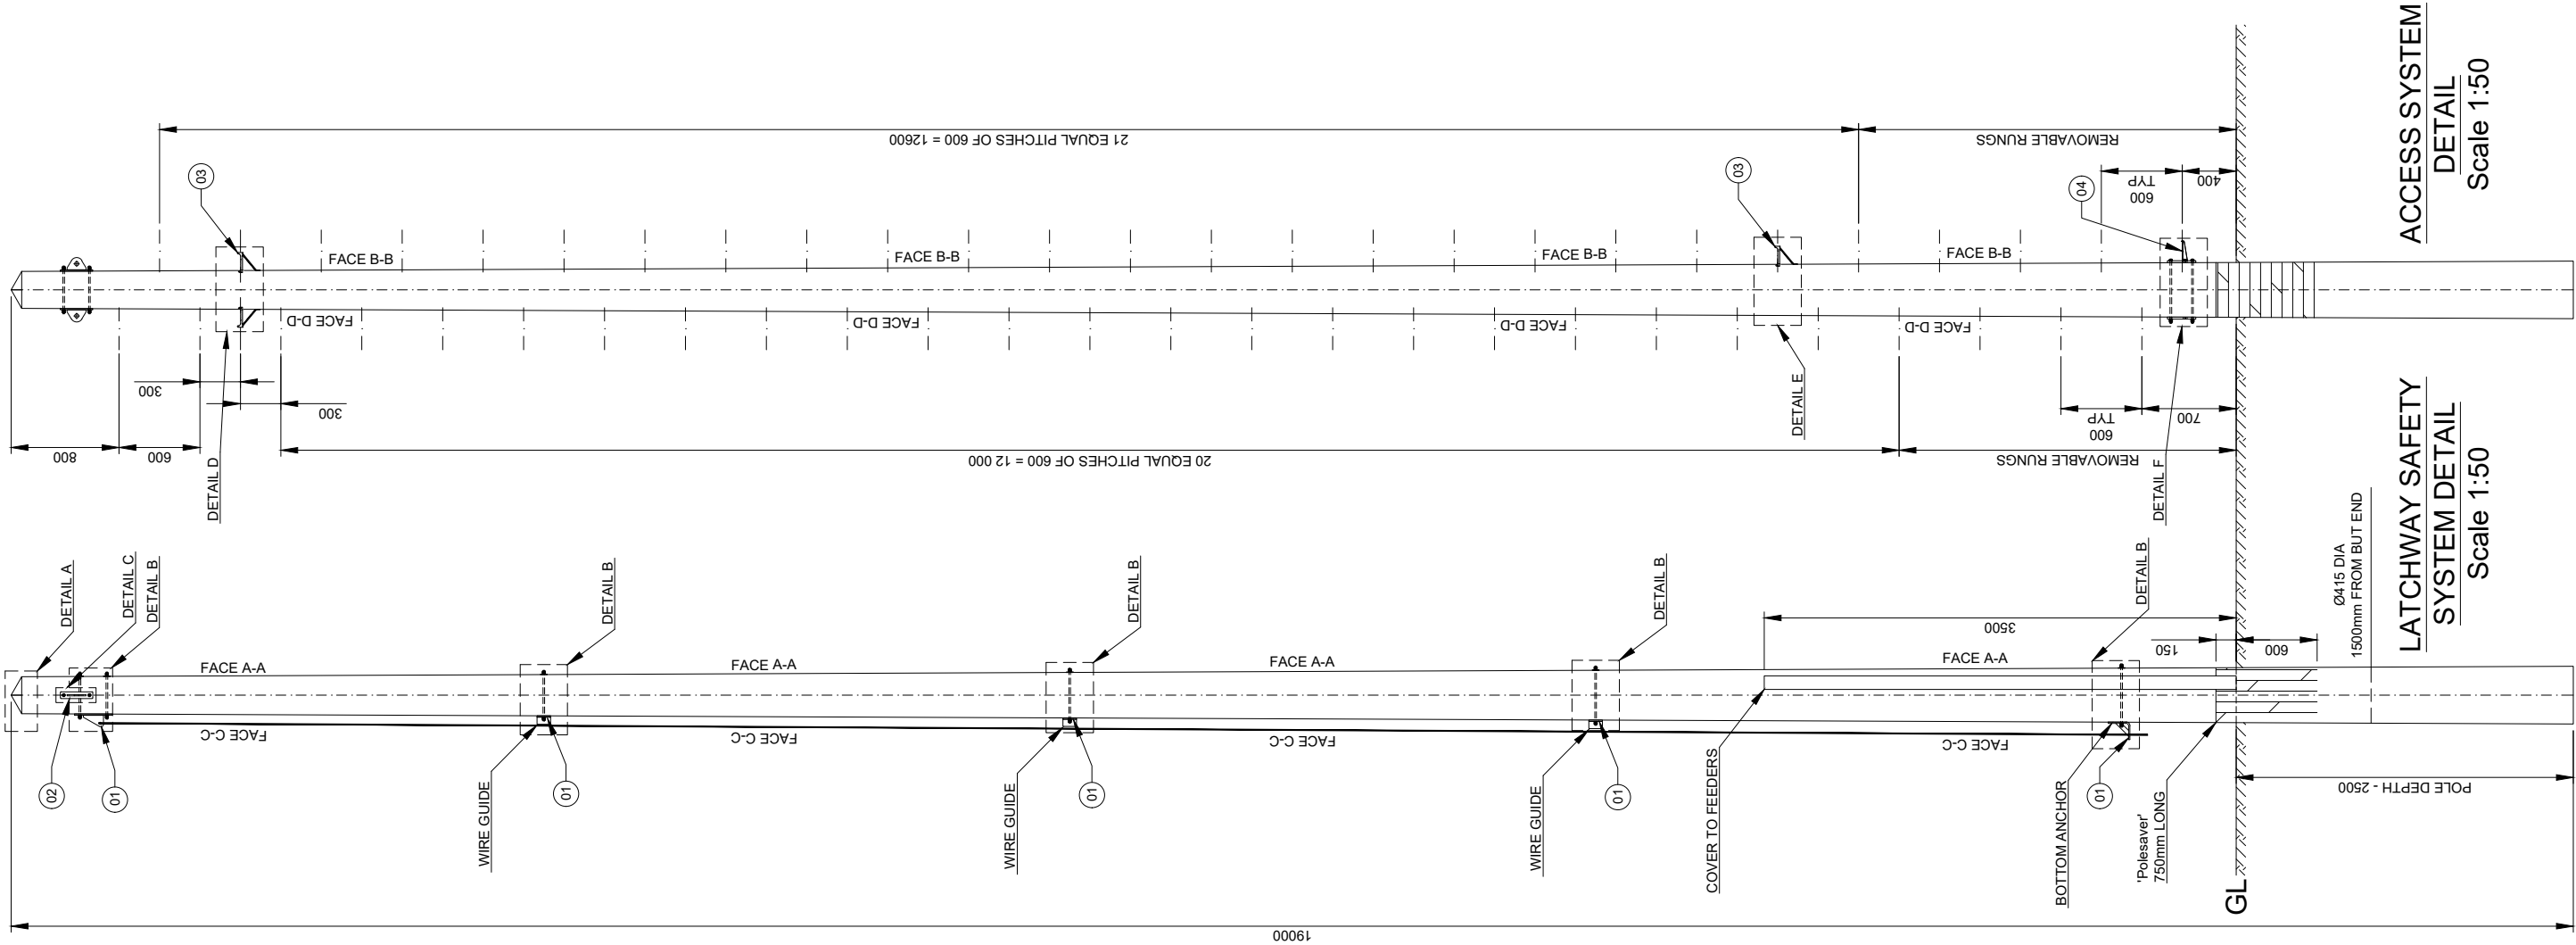

POLE ORIENTATION
Scale 1:20

NOTES

1. SEE DRAWING 304 FOR PARTS LIST
2. ALL BOLTS TO BE CUT ON SITE TO EXTEND MAX 10mm BEYOND THE NUT WHEN TIGHTENED UNO.
3. ALL SITE DRILLED HOLE/CUT ENDS TO BE TREATED WITH METAFUX 70-40 ZINC PASTE FOLLOWED BY 1 COAT OF 7-42 ZINC ALU OR 70-16 ALUMINIUM SPRAY

TIMBER POLE





1. POLE TO BE SUPPLIED IN ACCORDANCE WITH BS EN14229 & SHALL HAVE MIN. CHARACTERISTIC BENDING STRENGTH OF 30N/mm² & MIN. YOUNGS MODULUS (PARALLEL TO GRAIN) OF 10KN/mm².
2. MARKINGS ON FINISHED POLE SHALL BE AT 4m FROM BUT AND COMPLY WITH BS EN 14229 UNO
3. AS FAR AS PRACTICABLE ALL CUTTING, SCARFING & DRILLING TO BE DONE BEFORE CREOSOTING. IF NOT ALL CUT, DRILLED & SCARFED SURFACES TO BE COATED WITH A MIXTURE OF CREOSOTE & TAR.
4. POLE TO BE PRESSURE IMPREGNATED WITH CREOSOTE IN ACCORDANCE WITH BS EN 14229
5. MINIMUM DIAMETERS
TOP - Ø212mm
BOTTOM - Ø430mm
6. 19.0m LONG POLE TO BE SOURCED BY TRIMMING 20m LONG POLE BY 1.0m AT THE TOP

PLANTING

1. CAT SCANNER IS TO BE USED IN ORDER TO CONFIRM THE POSITIONS OF BURIED SERVICES.
2. 'Perma-Soil Stabiliser' OR A SIMILAR APPROVED SHOULD BE USED IN ACCORDANCE WITH THE MANUFACTURER'S RECOMMENDATION.
3. ANY MATERIAL USED FOR BACK-FILLING IS TO BE OF EQUAL OF BETTER QUALITY THAN THE EXCAVATED MATERIAL.
4. ALL BACK-FILLING MATERIAL IS TO BE PLACED AND COMPACTED IN 150mm THICK LAYERS.
5. TIMBER POLE TO BE PLANTED WITH N65 MARKING AT 3.5m FROM BUT FACING 65° FROM NORTH (CLOCKWISE)

ACCESS SYSTEM
DETAIL
Scale 1:50

LATCHWAY SAFETY
SYSTEM DETAIL
Scale 1:50

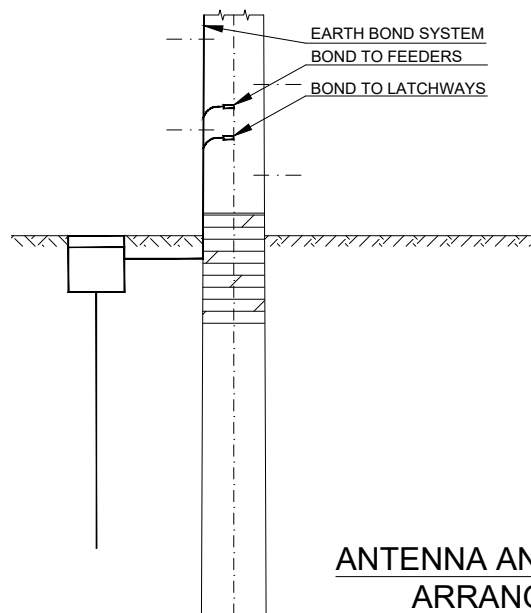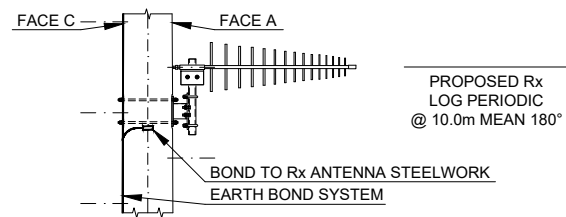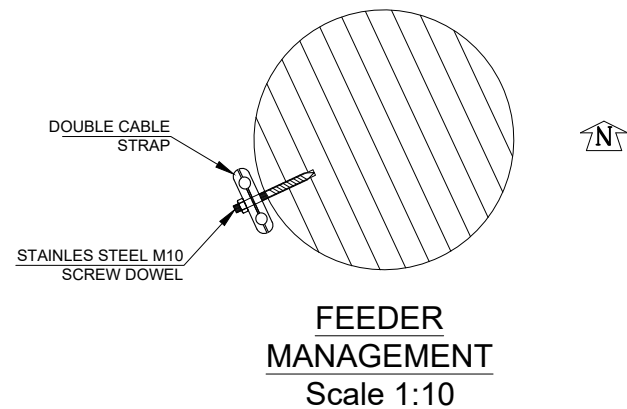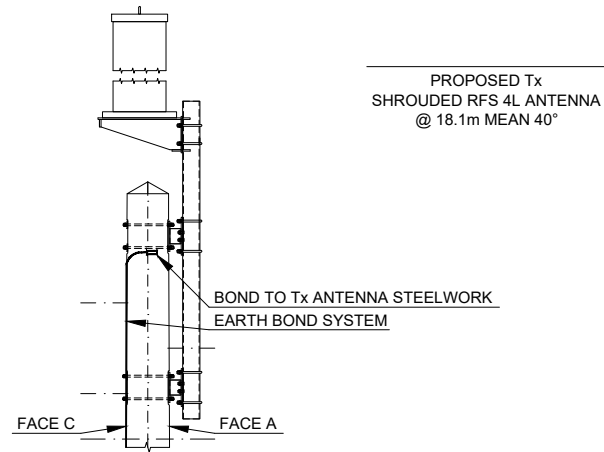

NOTES

1. AS FAR AS IS PRACTICABLE ALL CUTTING SCARFING AND DRILLING TO BE DONE BEFORE CREOSOTING. WHERE THIS IS NOT POSSIBLE ALL CUT, DRILLED, AND SCARFED SURFACES TO BE COATED WITH A MIXTURE OF CREOSOTE AND TAR

FEEDERS

1. SUPPLY OF FEEDERS BY OTHERS
LCF78-50 TO Tx ANTENNA &
LDF12-50 TO Rx ANTENNA
2. FEEDERS FIXED AT 1000mm CENTRES


EARTHING

1. CONNECT EARTH BOND TO NEW EARTHING SYSTEM
2. MAXIMUM VALUE FOR GROUND RESISTANCE TO BE 10 OHMS
3. CABLE OR TAPE TO BE FIXED TO POLE AT 1000mm CENTRES
4. EARTHING SHOULD COMPLY WITH ARQIVA'S DOCUMENT BOS147

ALL SCALES AS SHOWN WHEN PRINTED AT A3




ALL SCALES AS SHOWN WHEN PRINTED AT A3

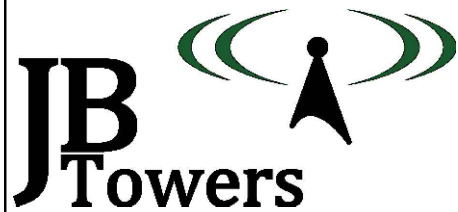


01	FIRST ISSUE			AM	10/10/18
REV	REV			BY	DATE
SCALE AS SHOWN WHEN PRINTED AT A3		DRAWN DATE	AM 10/10/18	CHECKED DATE	MP 10/10/18
				APPROVED	JB DATE 10/10/18
ALL DIMENSIONS IN mm UNLESS OTHERWISE STATED. THIS DRAWING TO BE READ IN CONJUNCTION WITH OTHER RELEVANT DRAWINGS.					

TITLE		SITE ADDRESS	
COLDEAN		THE MEADS COLDEAN BRIGHTON EAST SUSSEX BN1 9BA	
GENERAL ARRANGEMENT SHEET 2 OF 3		ARQIVA REF. 140357	DRG No. 200
		REV 01	

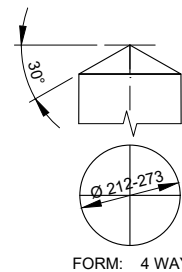


NOTES:
 1. A SINGLE COAT OF TIMBER COMPATIBLE BITUMINOUS PAINT (E.G. BIRD BRAND BLACK BITUMINOUS PAINT OR SIMILAR APPROVED PRODUCT) TO BE APPLIED TO THE UPPER SURFACES AT THE TOP OF THE POLE.
 2. PAINT TO BE APPLIED ON SITE JUST BEFORE ERECTION
 FORM: 4 WAY PYRAMID / CONE


DETAIL A - TIMBER POLE TOP
 Scale 1:20

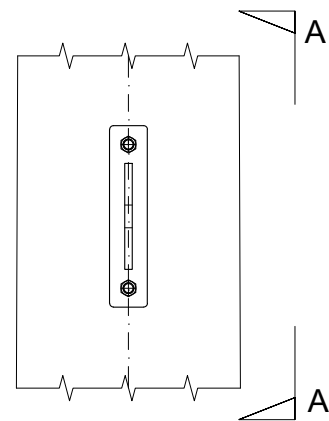


DETAIL C - FALL ARREST ATTACHMENT POINT
 Scale 1:10

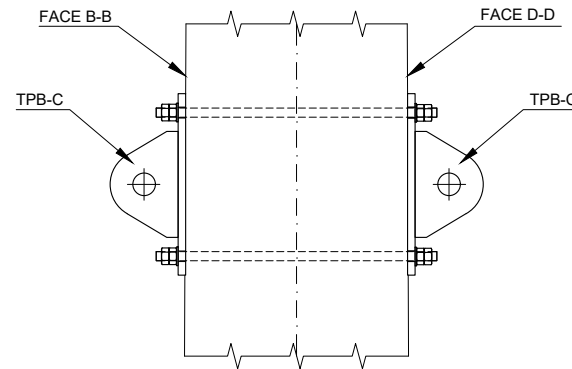


VIEW A-A
 Scale 1:10

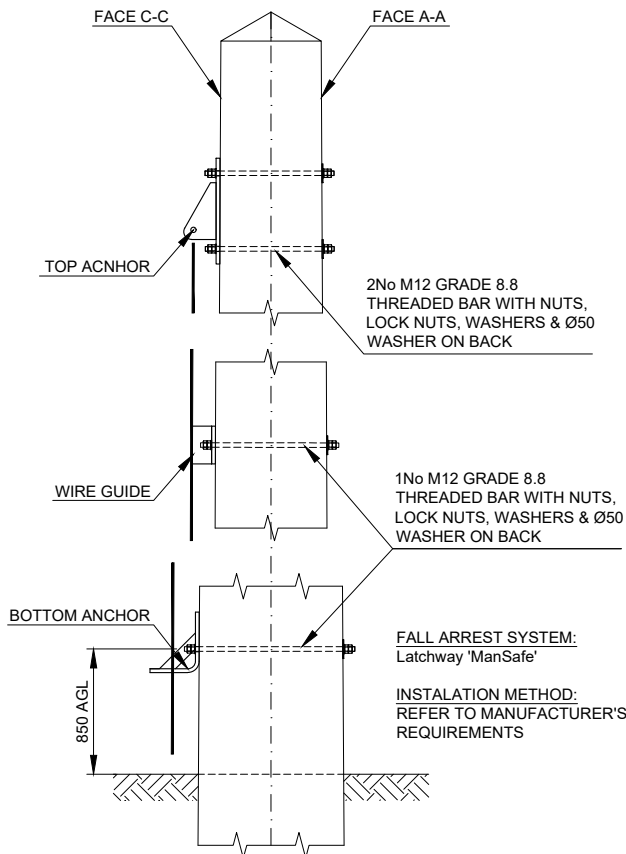

DETAIL B - FALL ARREST SYSTEM
 Scale 1:20

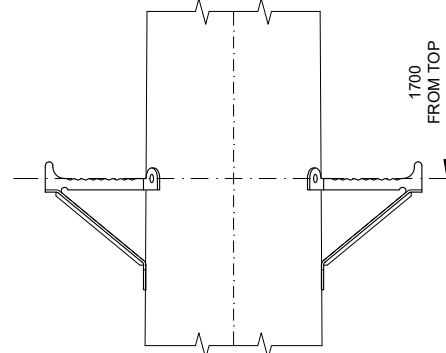


DETAIL D - ANTENNA ACCESS CLIMBING STEP
 Scale 1:10

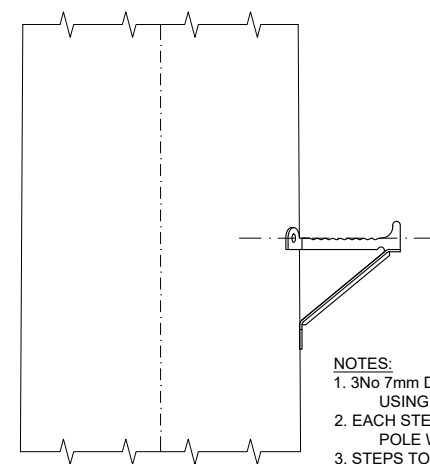

DETAIL E - PERMANENT CLIMBING STEPS
 Scale 1:10

NOTES:
 1. 3No 7mm DIA 70mm LONG PILOT HOLES TO BE DRILLED USING THE STEP AS A TEMPLATE
 2. EACH STEP SHOULD BE FIXED TO THE TIMBER POLE WITH 3No 10mm COACH SCREWS 75mm LONG
 3. STEPS TO BE INSTALLED ON FACES B-B & D-D ONLY

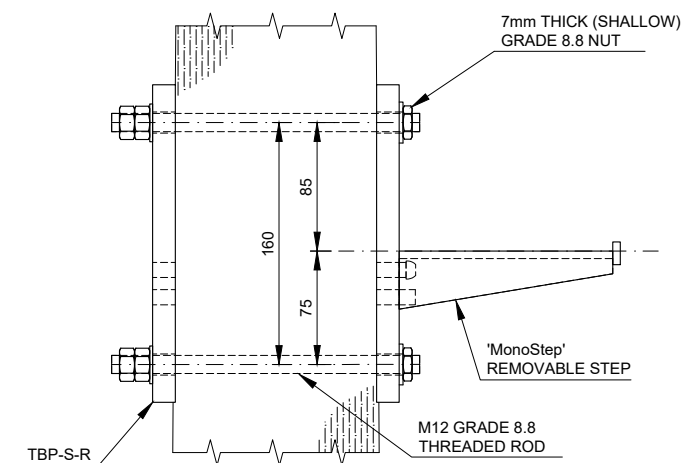


DETAIL F - REMOVABLE CLIMBING STEPS
 Scale 1:5

ALL SCALES AS SHOWN WHEN PRINTED AT A3



ALL SCALES AS SHOWN WHEN PRINTED AT A3

			<table border="1"> <tr> <td>01</td> <td>FIRST ISSUE</td> <td>AM</td> <td>10/10/18</td> </tr> <tr> <td>REV</td> <td>REV</td> <td>BY</td> <td>DATE</td> </tr> </table>				01	FIRST ISSUE	AM	10/10/18	REV	REV	BY	DATE	<table border="1"> <tr> <td>SCALE AS SHOWN</td> <td>DRAWN</td> <td>AM</td> <td>CHECKED</td> <td>MP</td> <td>APPROVED</td> <td>JBT</td> </tr> <tr> <td>WHEN PRINTED AT A3</td> <td>DATE</td> <td>10/10/18</td> <td>DATE</td> <td>10/10/18</td> <td>DATE</td> <td>10/10/18</td> </tr> </table>		SCALE AS SHOWN	DRAWN	AM	CHECKED	MP	APPROVED	JBT	WHEN PRINTED AT A3	DATE	10/10/18	DATE	10/10/18	DATE	10/10/18	<table border="1"> <tr> <td colspan="3">TITLE</td> </tr> <tr> <td colspan="3">COLDEAN</td> </tr> <tr> <td colspan="3">GENERAL ARRANGEMENT SHEET 3 OF 3</td> </tr> </table>		TITLE			COLDEAN			GENERAL ARRANGEMENT SHEET 3 OF 3			<table border="1"> <tr> <td colspan="3">SITE ADDRESS</td> </tr> <tr> <td colspan="3">THE MEADS COLDEAN BRIGHTON EAST SUSSEX BN1 9BA</td> </tr> </table>			SITE ADDRESS			THE MEADS COLDEAN BRIGHTON EAST SUSSEX BN1 9BA		
			01	FIRST ISSUE	AM	10/10/18	
			REV	REV	BY	DATE	
			SCALE AS SHOWN	DRAWN	AM	CHECKED	MP	APPROVED	JBT	
WHEN PRINTED AT A3	DATE	10/10/18	DATE	10/10/18	DATE	10/10/18	
TITLE	
COLDEAN	
GENERAL ARRANGEMENT SHEET 3 OF 3	
SITE ADDRESS	
THE MEADS COLDEAN BRIGHTON EAST SUSSEX BN1 9BA	
<table border="1"> <tr> <td>ALL DIMENSIONS IN mm UNLESS OTHERWISE STATED. THIS DRAWING TO BE READ IN CONJUNCTION WITH OTHER RELEVANT DRAWINGS.</td> </tr> </table>				ALL DIMENSIONS IN mm UNLESS OTHERWISE STATED. THIS DRAWING TO BE READ IN CONJUNCTION WITH OTHER RELEVANT DRAWINGS.	<table border="1"> <tr> <td>ARQIVA REF. 140357</td> <td>DRG No. 200</td> <td>REV 01</td> </tr> </table>		ARQIVA REF. 140357	DRG No. 200	REV 01	
ALL DIMENSIONS IN mm UNLESS OTHERWISE STATED. THIS DRAWING TO BE READ IN CONJUNCTION WITH OTHER RELEVANT DRAWINGS.	
ARQIVA REF. 140357	DRG No. 200	REV 01	

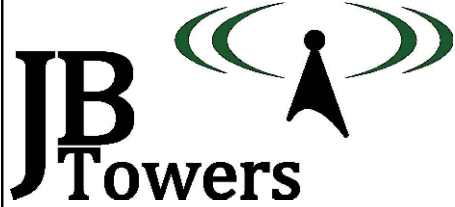

02	CUSTOMER COMMENTS			AM	18/10/18
01	FIRST ISSUE			AM	10/10/18
REV	REV			BY	DATE
SCALE AS SHOWN WHEN PRINTED AT A3		DRAWN	AM	CHECKED	MP
		DATE	10/10/18	DATE	10/10/18
APPROVED					
JBT					
DATE 10/10/18					
ALL DIMENSIONS IN mm UNLESS OTHERWISE STATED. THIS DRAWING TO BE READ IN CONJUNCTION WITH OTHER RELEVANT DRAWINGS.					


TITLE
COLDEAN
TIMBER POLE HOLE SET OUT
SHEET 1 OF 2

SITE ADDRESS
THE MEADS
COLDEAN
BRIGHTON
EAST SUSSEX
BN1 9BA

ARQIVA REF.
140357

DRG No.
201


REV
02

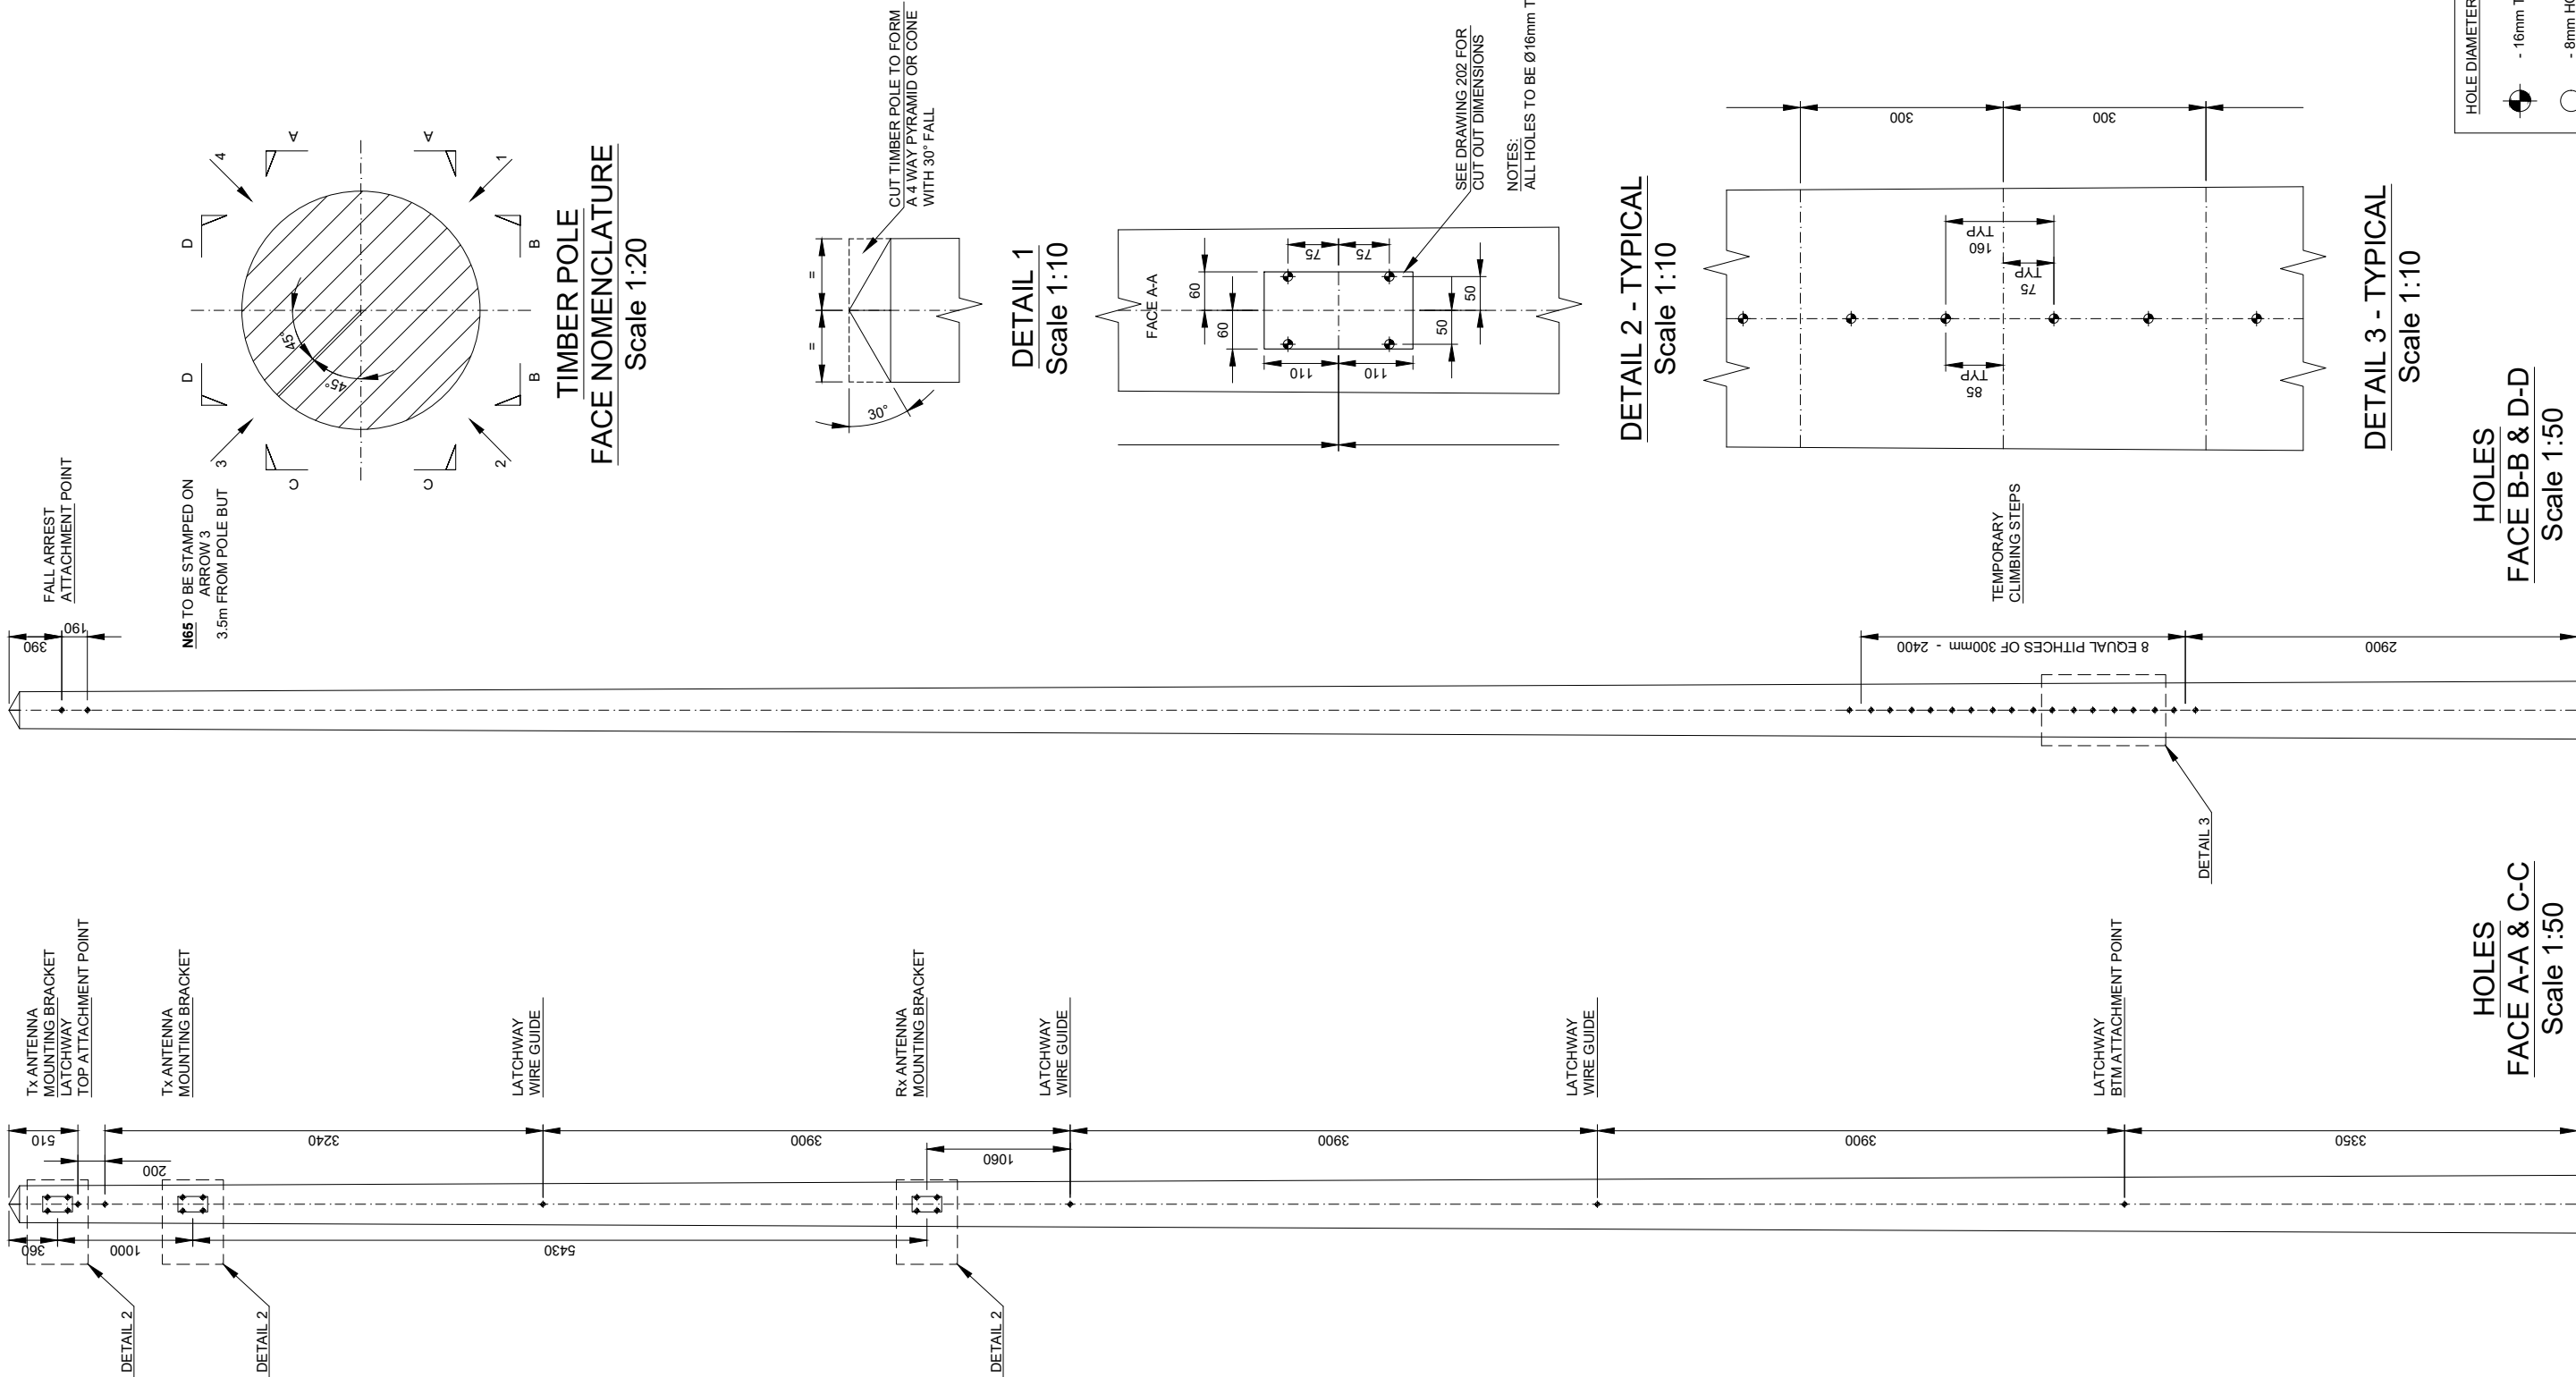

ALL SCALES AS SHOWN WHEN PRINTED AT A3



ALL SCALES AS SHOWN WHEN PRINTED AT A3

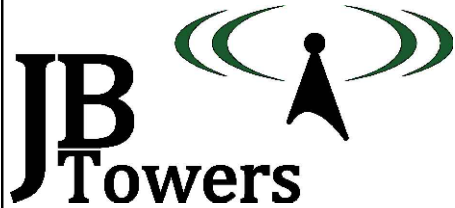

02	CUSTOMER COMMENTS			AM	18/10/18
01	FIRST ISSUE			AM	10/10/18
REV	REV			BY	DATE
SCALE AS SHOWN WHEN PRINTED AT A3		DRAWN	AM	CHECKED	MP
		DATE	10/10/18	DATE	10/10/18
		APPROVED		JBT	
		DATE		10/10/18	
ALL DIMENSIONS IN mm UNLESS OTHERWISE STATED. THIS DRAWING TO BE READ IN CONJUNCTION WITH OTHER RELEVANT DRAWINGS.					

TITLE

COLDEAN

TIMBER POLE HOLE SET OUT
SHEET 2 OF 2


SITE ADDRESS

THE MEADS
COLDEAN
BRIGHTON
EAST SUSSEX
BN1 9BA

ARQIVA REF.
140357


DRG No.
201

REV
02

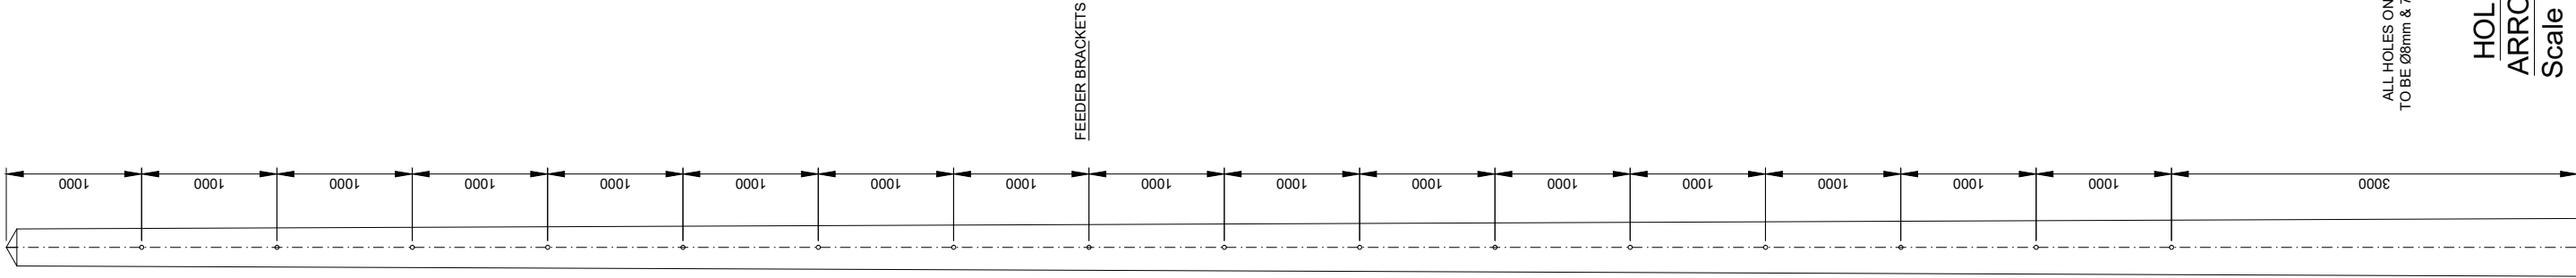

ALL HOLES ON ARROW 1
TO BE Ø8mm & 70mm LONG

HOLES
ARROW 1
Scale 1:50

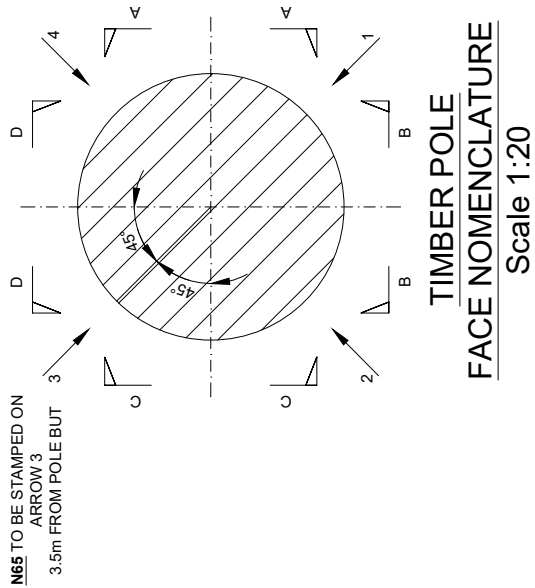


N65 TO BE STAMPED ON
ARROW 3
3.5m FROM POLE BUT



ALL SCALES AS SHOWN WHEN PRINTED AT A3

ALL SCALES AS SHOWN WHEN PRINTED AT A3

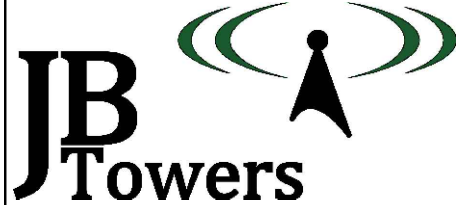


01	FIRST ISSUE			AM	10/10/18
REV	REV			BY	DATE
SCALE AS SHOWN		DRAWN	AM	CHECKED	MP
WHEN PRINTED AT A3		DATE	10/10/18	DATE	10/10/18
		APPROVED	JBT	DATE	10/10/18
ALL DIMENSIONS IN mm UNLESS OTHERWISE STATED. THIS DRAWING TO BE READ IN CONJUNCTION WITH OTHER RELEVANT DRAWINGS.					

TITLE

COLDEAN


TIMBER POLE CUT OUT
DETAIL

SITE ADDRESS		
THE MEADS COLDEAN BRIGHTON EAST SUSSEX BN1 9BA		
ARQIVA REF. 140357	DRG No. 202	REV 01

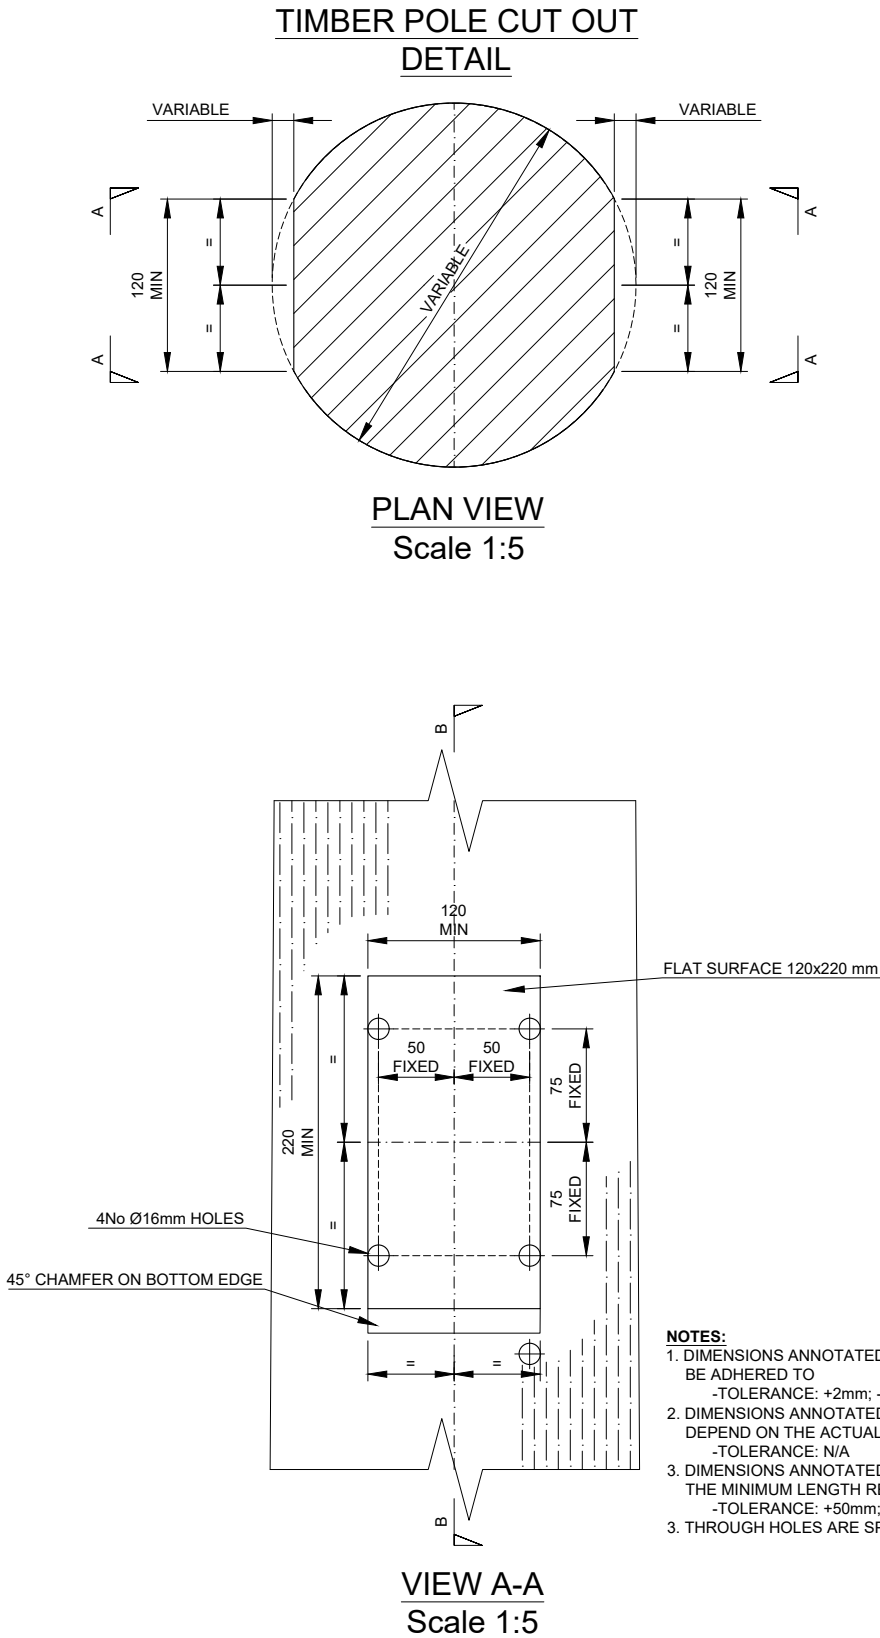


ALL SCALES AS SHOWN WHEN PRINTED AT A3

ALL SCALES AS SHOWN WHEN PRINTED AT A3

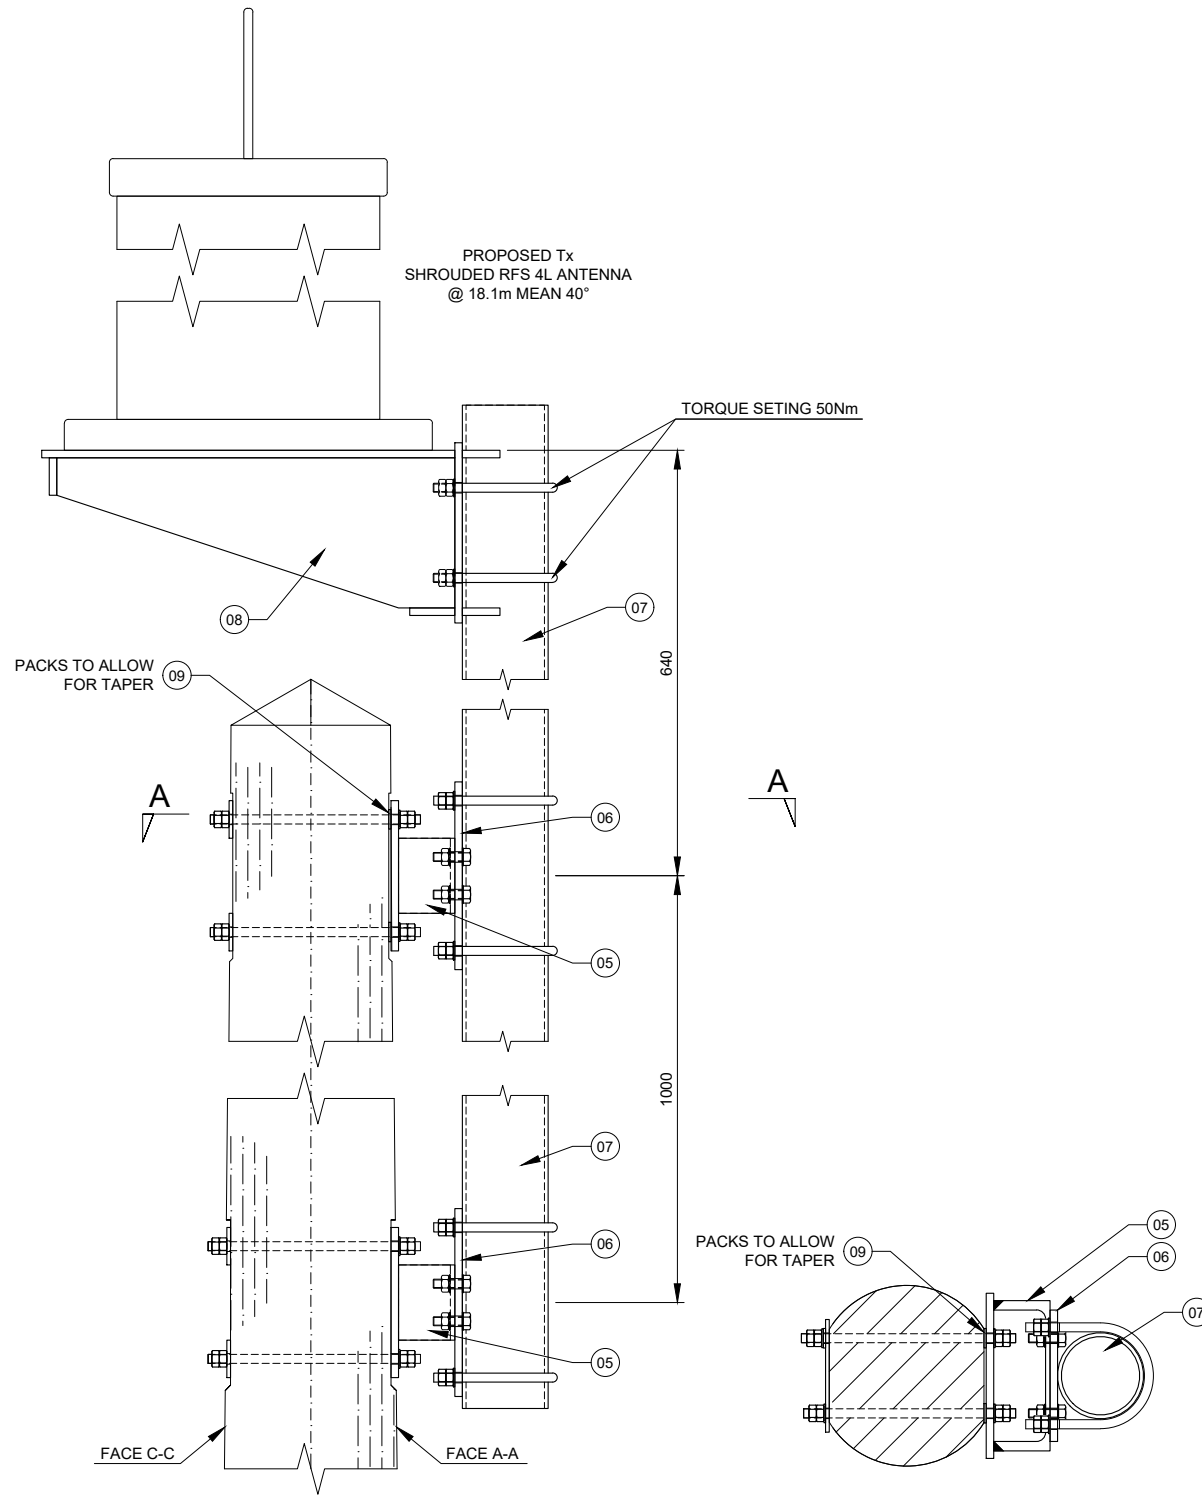

DETAIL F - Tx ANTENNA MOUNT
Scale 1:10

SECTION A-A
Scale 1:10

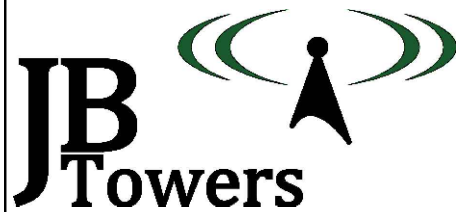

01	FIRST ISSUE				AM	10/10/18
REV	REV				BY	DATE
SCALE AS SHOWN WHEN PRINTED AT A3		DRAWN	AM	CHECKED	MP	APPROVED JBT
		DATE	10/10/18	DATE	10/10/18	DATE 10/10/18
ALL DIMENSIONS IN mm UNLESS OTHERWISE STATED. THIS DRAWING TO BE READ IN CONJUNCTION WITH OTHER RELEVANT DRAWINGS.						


TITLE
ANTENNA MOUNT
DETAIL F

SITE ADDRESS
THE MEADS
COLDEAN
BRIGHTON
EAST SUSSEX
BN1 9BA


ARQIVA REF.
140357

DRG No.
203

REV
01

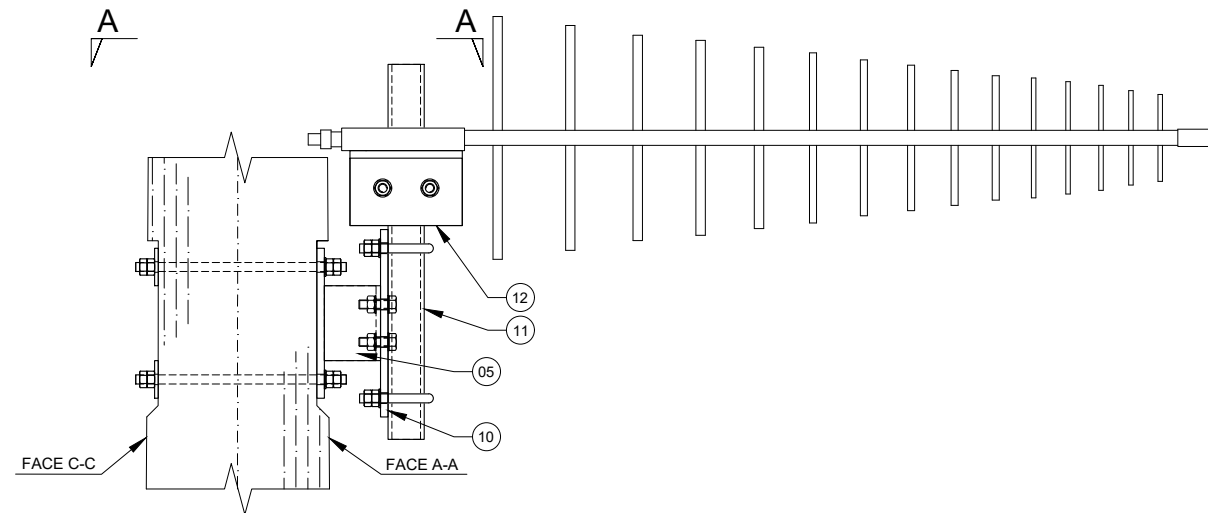

DETAIL G - Rx ANTENNA MOUNT
Scale 1:10

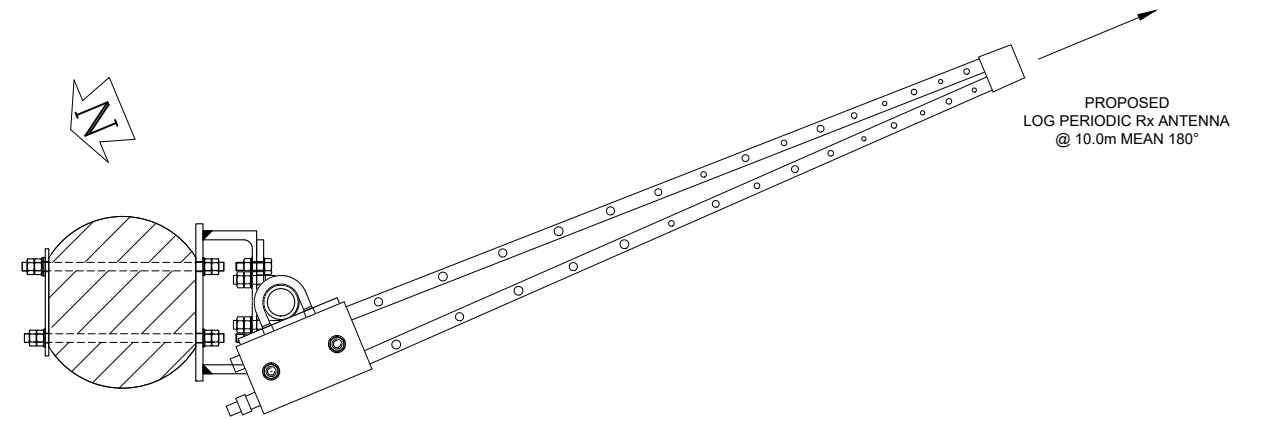


VIEW A-A
Scale 1:10



ALL SCALES AS SHOWN WHEN PRINTED AT A3


ALL SCALES AS SHOWN WHEN PRINTED AT A3

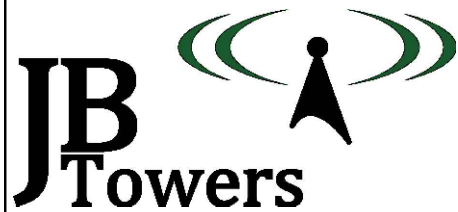

01	FIRST ISSUE				AM	10/10/18
REV	REV				BY	DATE
SCALE AS SHOWN WHEN PRINTED AT A3		DRAWN	AM	CHECKED	MP	APPROVED JBT
		DATE	10/10/18	DATE	10/10/18	DATE 10/10/18
ALL DIMENSIONS IN mm UNLESS OTHERWISE STATED. THIS DRAWING TO BE READ IN CONJUNCTION WITH OTHER RELEVANT DRAWINGS.						


TITLE
ANTENNA MOUNT
DETAIL G

SITE ADDRESS		
THE MEADS COLDEAN BRIGHTON EAST SUSSEX BN1 9BA		
ARQIVA REF. 140357	DRG No. 204	REV 01

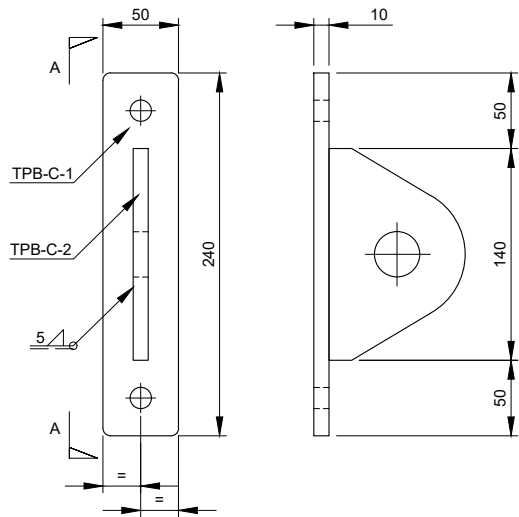

PART TPB-C
Scale 1:5

VIEW A-A
Scale 1:5

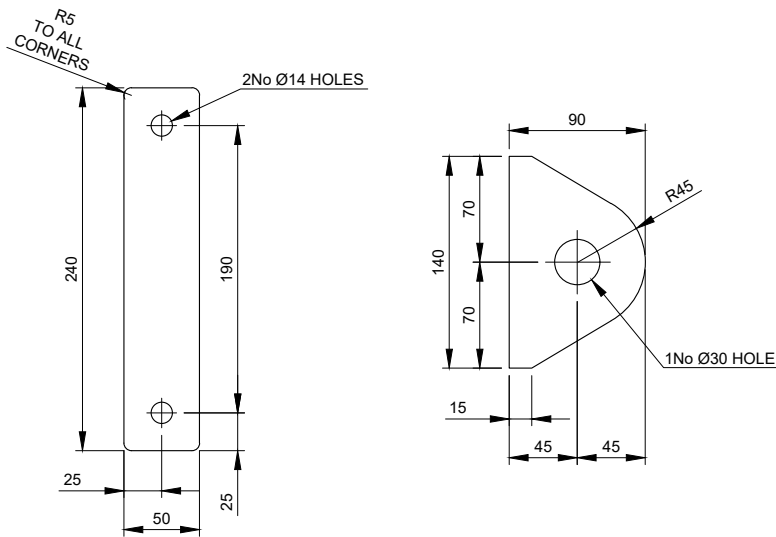


TPB-C-1 - 10mm THICK
Scale 1:5

TPB-C-2 - 10mm THICK
Scale 1:5

Parts list for TPB-C

Item	Part	Quantity	Part description	Length	Material	Weight
01	TPB-C-1	1	240x50x10mm	N/A	S275J0	0.94 kg
02	TPB-C-2	1	140x90x10mm	N/A	S275J0	0.99 kg
03	STUDS	1	M12 STUDDING	360mm	GRADE 8.8	0.32 kg
Total Weight:						2.25 kg

- All steel hot dip galvanized
- Each STUD to be supplied with 4 Full Nuts, 2 Flat Washers and 2 Spring Washers
- For fabrtication notes see drawing 304

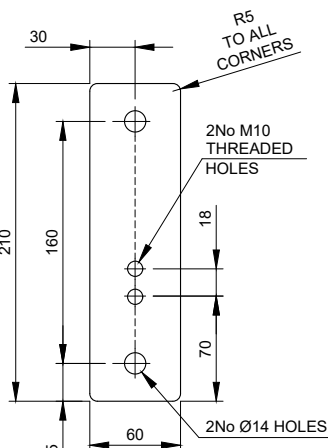


PART TPS-R
Scale 1:5

Parts list for TPS-R

Item	Part	Quantity	Part description	Length	Material	Weight
01	TPS-R	2	210x60x15mm	N/A	S275J0	1.48 kg
02	STUDS	2	M12 STUDDING	500mm	GRADE 8.8	0.44 kg
03	NUT-S	2	M12 SHALLOW NUT	N/A	GRADE 8.8	-
04	NUT	4	M12 NUT	N/A	GRADE 8.8	-
03	WSH	4	M12 WASHER	N/A	GRADE 8.8	-
Total Weight:						3.40 kg

- All steel hot dip galvanized
- For fabrtication notes see drawing 304

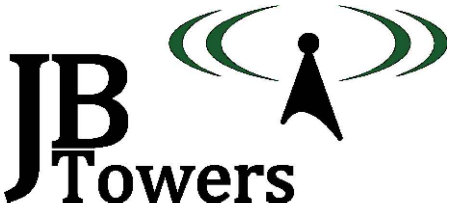

01	FIRST ISSUE	AM	10/10/18
REV	REV	BY	DATE
SCALE AS SHOWN WHEN PRINTED AT A3	DRAWN DATE 10/10/18	CHECKED DATE 10/10/18	APPROVED DATE 10/10/18
ALL DIMENSIONS IN mm UNLESS OTHERWISE STATED. THIS DRAWING TO BE READ IN CONJUNCTION WITH OTHER RELEVANT DRAWINGS.			

TITLE
ATTACHMENT POINT &
TEMPORARY STEP DETAILS
PARTS: TPB-C; TPS-R

SITE ADDRESS
THE MEADS
COLDEAN
BRIGHTON
EAST SUSSEX
BN1 9BA

ARQIVA REF.
140357


DRG No.
300

REV
01

ALL SCALES AS SHOWN WHEN PRINTED AT A3




ALL SCALES AS SHOWN WHEN PRINTED AT A3

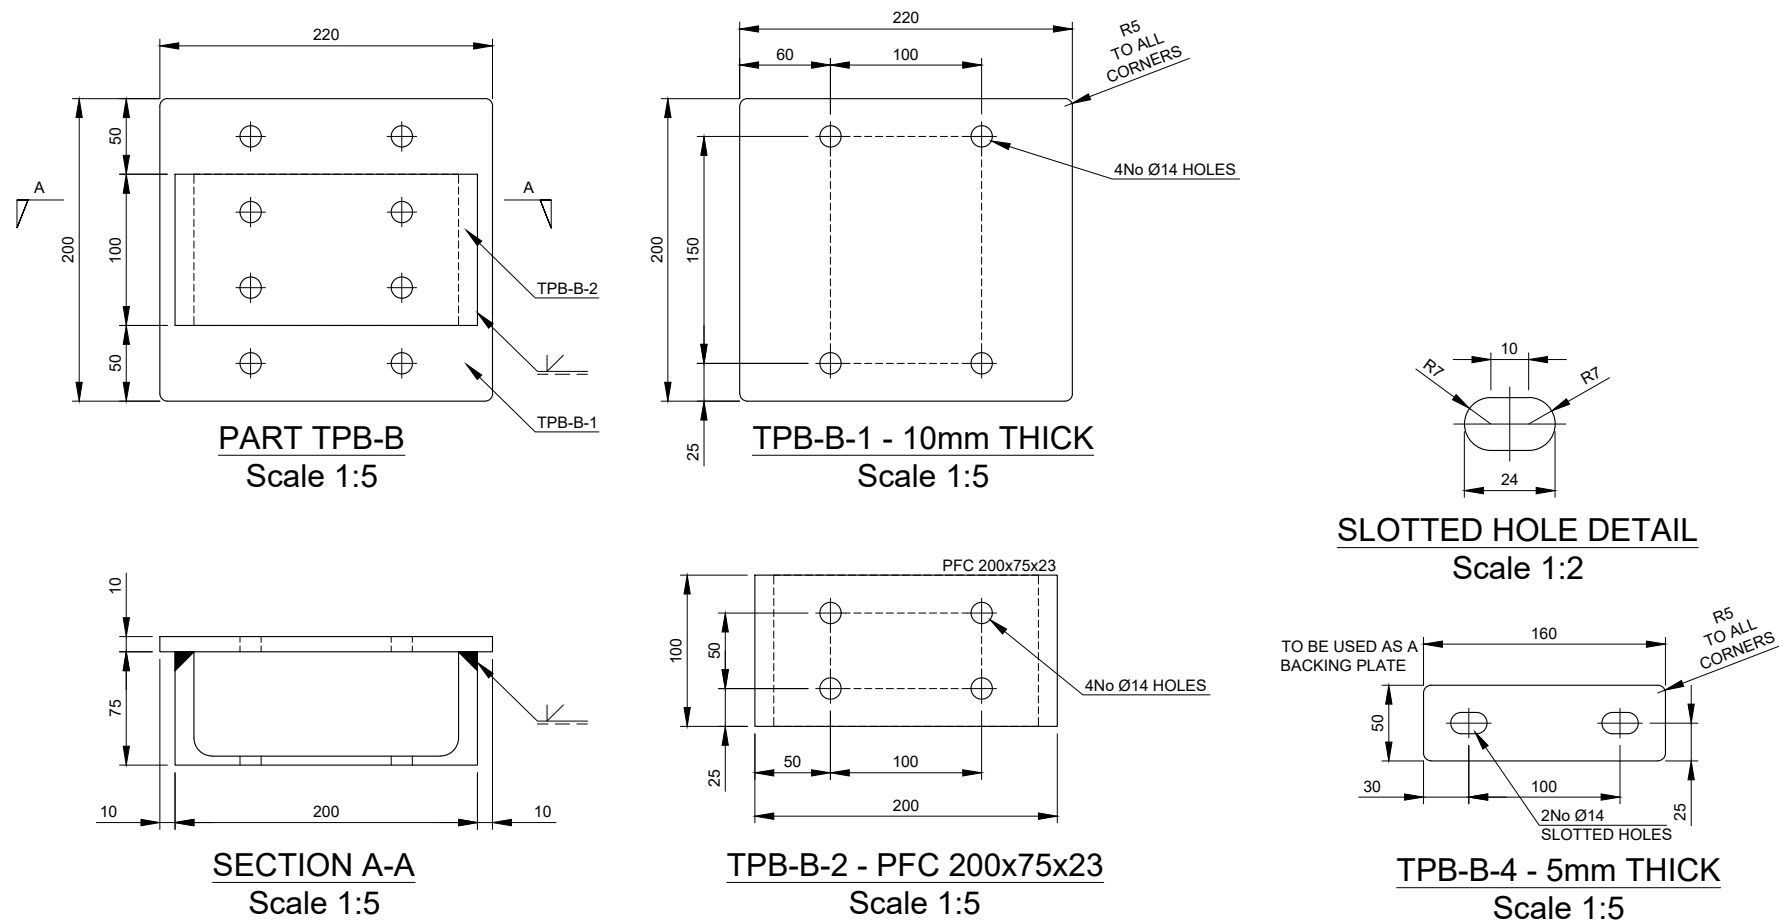

Parts list for TPB-B

Item	Part	Quantity	Part description	Length	Material	Weight
01	TPB-B-1	1	220x200x10mm	N/A	S275J0	3.45 kg
02	TPB-B-2	1	PFC 200x75x23	100mm	S275J0	2.30 kg
03	TPB-B-4	2	160x50x5mm	N/A	S275J0	0.31 kg
04	STUDS	4	M12 STUDDING	400mm	GRADE 8.8	0.35 kg
Total Weight:						7.46 kg

- All steel hot dip galvanized
- Each STUD & U-BOLT to be supplied with 4 Full Nuts, 2 Flat Washers and 2 Spring Washers
- Each BOLT to be supplied with 1 Full Nut, 1 Form E FLat Washer and 1 Spring Washer
- For fabrtrication notes see drawing 304

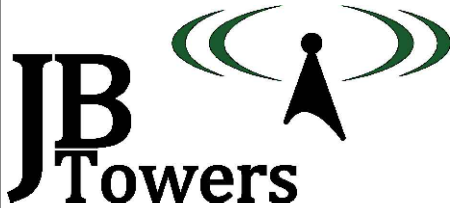

01	FIRST ISSUE	AM	10/10/18
REV	REV	BY	DATE
SCALE AS SHOWN WHEN PRINTED AT A3	DRAWN DATE 10/10/18	CHECKED DATE 10/10/18	APPROVED DATE 10/10/18
ALL DIMENSIONS IN mm UNLESS OTHERWISE STATED. THIS DRAWING TO BE READ IN CONJUNCTION WITH OTHER RELEVANT DRAWINGS.			

TITLE
STEELWORK BRACKET
PART: TPB-B

SITE ADDRESS
THE MEADS
COLDEAN
BRIGHTON
EAST SUSSEX
BN1 9BA

ARQIVA REF.
140357


DRG No.
301

REV
01

ALL SCALES AS SHOWN WHEN PRINTED AT A3




ALL SCALES AS SHOWN WHEN PRINTED AT A3

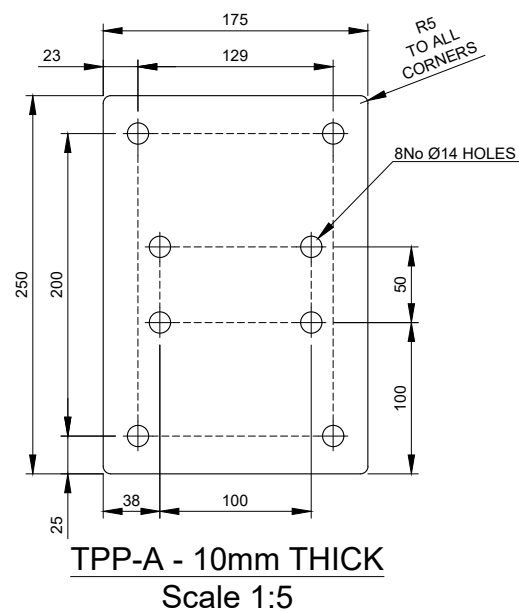

Parts list for TPP-A

Item	Part	Quantity	Part description	Length	Material	Weight
01	TPP-A	1	250x175x10mm	N/A	S275J0	3.45 kg
02	BOLT	4	M12 45mm LONG (2D+6)	45mm	GRADE 8.8	-
03	U-BOLT	2	M12 U-BOLT FOR CHS 114.3mm	N/A	GRADE 8.8	-
Total Weight:						3.45 kg


- All steel hot dip galvanized
- Each STUD & U-BOLT to be supplied with 4 Full Nuts, 2 Flat Washers and 2 Spring Washers
- Each BOLT to be supplied with 1 Full Nut, 1 Form E FLat Washer and 1 Spring Washer
- For fabrtrication notes see drawing 304

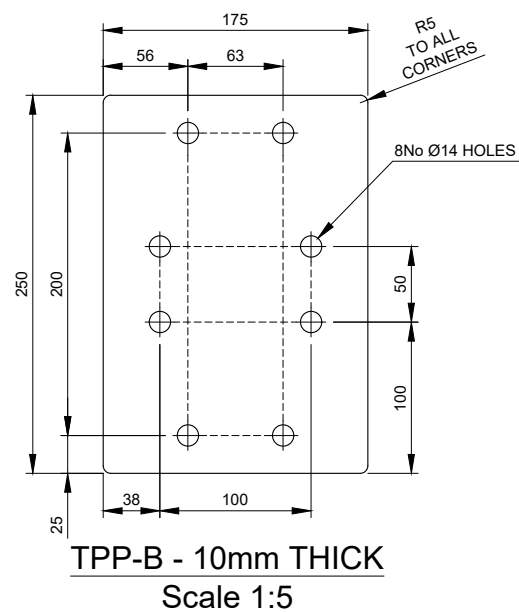

Parts list for TPP-B

Item	Part	Quantity	Part description	Length	Material	Weight
01	TPP-B	1	250x175x10mm	N/A	S275J0	3.45 kg
02	BOLT	4	M12 45mm LONG (2D+6)	45mm	GRADE 8.8	-
03	U-BOLT	2	M12 U-BOLT FOR CHS 48.3mm	N/A	GRADE 8.8	-
Total Weight:						3.45 kg


- All steel hot dip galvanized
- Each STUD & U-BOLT to be supplied with 4 Full Nuts, 2 Flat Washers and 2 Spring Washers
- Each BOLT to be supplied with 1 Full Nut, 1 Form E FLat Washer and 1 Spring Washer
- For fabrtrication notes see drawing 304

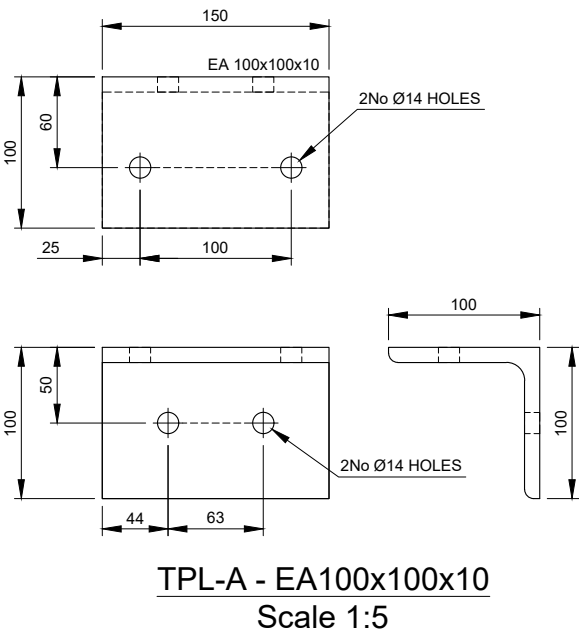

Parts list for TPL-A

Item	Part	Quantity	Part description	Length	Material	Weight
01	TPL-A	1	EA100x100x10	150mm	S275J0	2.25 kg
02	BOLT	2	M12 55mm LONG SET BOLT	55mm	GRADE 8.8	-
03	U-BOLT	1	M12 U-BOLT FOR CHS 48.3mm	N/A	GRADE 8.8	-
Total Weight:						2.25 kg

- All steel hot dip galvanized
- Each STUD & U-BOLT to be supplied with 4 Full Nuts, 2 Flat Washers and 2 Spring Washers
- Each BOLT to be supplied with 1 Full Nut, 1 Form E FLat Washer and 1 Spring Washer
- For fabrtrication notes see drawing 304

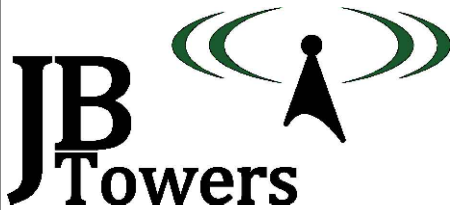

01	FIRST ISSUE	AM	10/10/18
REV	REV	BY	DATE
SCALE AS SHOWN WHEN PRINTED AT A3	DRAWN DATE	AM 10/10/18	CHECKED DATE
ALL DIMENSIONS IN mm UNLESS OTHERWISE STATED. THIS DRAWING TO BE READ IN CONJUNCTION WITH OTHER RELEVANT DRAWINGS.			

TITLE
INTERFACE PLATES &
Rx MOUNT
PARTS: TPP-A; TPP-B; TPL-A






SITE ADDRESS
THE MEADS
COLDEAN
BRIGHTON
EAST SUSSEX
BN1 9BA

ARQIVA REF.
140357
DRG No.
302
REV
01

ALL SCALES AS SHOWN WHEN PRINTED AT A3



ALL SCALES AS SHOWN WHEN PRINTED AT A3

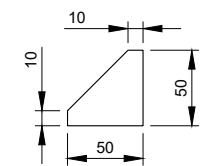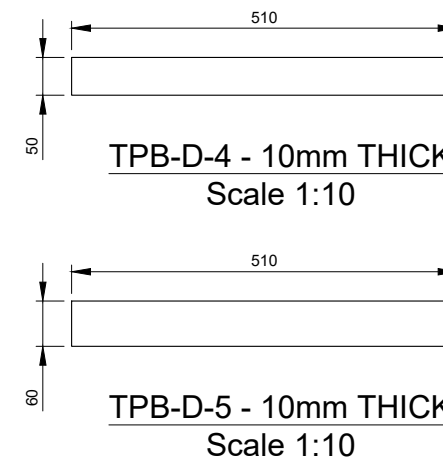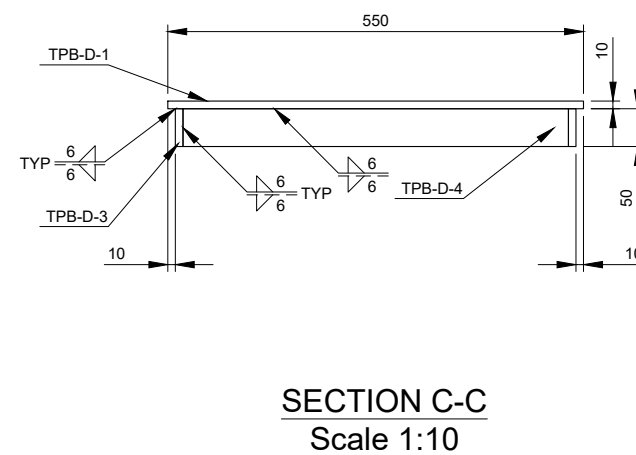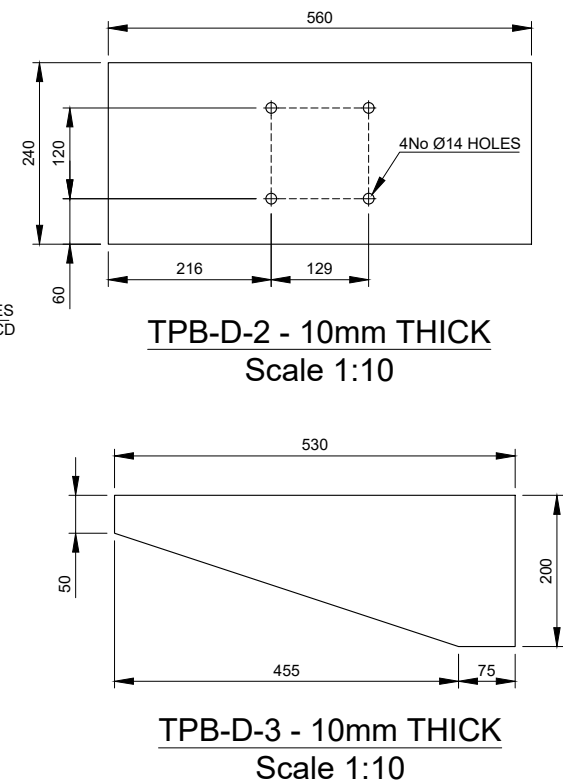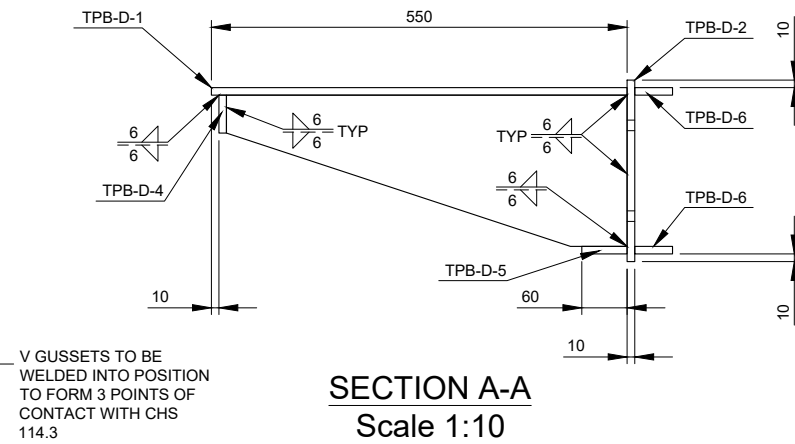

Item	Part	Quantity	Part description	Length	Material	Weight
01	TPB-D-1	1	550x550x10mm	N/A	S275J0	23.75 kg
02	TPB-D-2	1	560x240x10mm	N/A	S275J0	10.55 kg
03	TPB-D-3	2	530x200x10mm	N/A	S275J0	8.32 kg
04	TPB-D-4	1	510x50x10mm	N/A	S275J0	2.00 kg
05	TPB-D-5	1	510x60x10mm	N/A	S275J0	2.40 kg
06	TPB-D-6	4	50x50x10mm	N/A	S275J0	0.20 kg
07	U-BOLT	2	M12 U-BOLT FOR CHS 114.3mm	N/A	GRADE 8.8	-
- All steel hot dip galvanized					Total Weight:	56.14 kg

- All steel hot dip galvanized
- Each U-BOLT to be supplied with 4 Full Nuts, 2 Flat Washers and 2 Spring Washers
- All welded joints to be pickle tight
- For fabrication notes see drawing 304

Total Weight:

Weight:	56.14 kg
---------	----------



01	FIRST ISSUE		AM	10/10/18	
REV	REV		BY	DAT	
SCALE AS SHOWN WHEN PRINTED AT A3	DRAWN AM DATE 10/10/18	CHECKED MP DATE 10/10/18	APPROVED JB DATE 10/10/18		
ALL DIMENSIONS IN mm UNLESS OTHERWISE STATED. THIS DRAWING TO BE READ IN CONJUNCTION WITH OTHER RELEVANT DRAWINGS.					

PART: TPB-D

THE MEADS
COLDEAN
BRIGHTON
EAST SUSSEX
BN1 9BA

ARQIVA REF.
140357


DRG No.
303[illegible]

Item	Part	Drawing	Quantity	Part description	Length	Material	Weight
01	01	200	1	3 MAN LATCHWAY SYSTEM & 3No. WIRE GUIDES FOR FACE MOUNTED MONOPOLE	16500	N/A	-
02	TPB-C	300	2	FALL ARREST ATTACHMENT POINT	N/A	S275J0	4.50 kg
03	03	301	44	PERMANENT BT STEP c/w 3No 10x75mm ZINC-PLATED COACH SCREWS	N/A	S275J0	12.90 kg
04	TPS-R	300	9	'MonoStep' ASSEMBLY	N/A	S275J0	30.60 kg
05	TPB-B	301	3	MOUNTING BRACKET	N/A	S275J0	22.38 kg
06	TPP-A	302	2	PLATE A INTERFACE	N/A	S275J0	6.90 kg
07	07	203	1	CHS 114.3x5mm	2100mm	S355J2H	28.35 kg
08	TPB-D	303	1	MOUNTING BRACKET ASSEMBLY	N/A	S275J0	56.14 kg
09	09	203	12	M12 WASHER	N/A	GRADE 8.8	-
10	TPP-B	302	1	PLATE B INTERFACE	N/A	S275J0	3.45 kg
11	11	204	1	CHS 48.3x5mm	500mm	S355J2H	2.70 kg
12	TPL-A	302	1	Rx MOUNT - EA100x100x10	150mm	S275J0	2.25 kg
13	13	200	1	FEEDER COVER - 2/CG/100	3500mm	UV RESISTANT PLASTIC	-
14	14	200	16	FEEDER CLAMP - 2/FCD/028	N/A	POLYPROPYLENE	-
15	15	200	16	M10 SCREW DOWELS WTH M10 NUT	100mm	STAINLESS STEEL	-
16	16	200	1	PoleSaver	750mm	N/A	-
17	17	200	8	M12 STUD + 4No NUTS + 2No FLAT WASHERS + 1No Ø50mm WASHER (FOR FALL ARREST SYSTEM)	470mm	GRADE 8.8	3.35 kg
Total Weight:						173.52 kg	

- All steel hot dip galvanized
- All U-BOLTS to be FLA supply, each Supplied with 4 Full Nuts, 2 Flat Washers and 2 Spring Washers

NOTES:

1. WELDING TO BE IN ACCORDANCE WITH BS EN 1011-1:2009
2. LINEAR DIMS TO BE WITHIN ±1mm;
3. ANGULAR TOLERANCES TO BE WITHIN 0.5°
4. WELDING SYMBOLS ARE IN ACCORDANCE WITH BS EN 22553:1995
5. ALL PROFILE EDGES TO BE DRESSED AND SHARP CORNERS REMOVED
6. ALL WELD SIZES ARE FINAL SIZES
7. ALL WELDED JOINTS ARE TO BE PICKLE TIGHT
8. ALL STEELWORK TO BE BS EN 10025 GRADE S275 J0 UNO & 9. HOT DIPPED GALVANISED TO BS EN ISO 1461. (ALL HOLLOW SECTIONS TO BE GRADE S355 J0H)
10. ALL STEEL IS TO BE SUPPLIED IN ACCORDANCE WITH EN 1090 TO EXECUTION CLASS 2
11. ALL NON PRE-LOADED BOLTS TO BE COMPLIANT STRUCTURAL BOLTS TO BS EN ISO 15048 PARTS 1&2.
12. STEELWORK COMPONENTS SHALL BE HOT DIP GALVANISED TO ACHIEVE A "VERY HIGH" DURABILITY FOR AN ENVIRONMENT CATEGORY CODE C4 FROM TABLE 1 IN BS EN ISO 14713
13. BOLTS AND NUTS SHALL BE SUPPLIED IN ACCORDANCE WITH BS 7371, SPUN GALVANISED IN ACCORDANCE WITH ISO 10684, THE NUTS RE-TAPPED AFTER GALVANISING, AND THE THREADS TREATED WITH GREASE.
14. ALL BOLTS TO BE CUT ON SITE TO EXTEND MAX 10mm BEYOND THE NUT WHEN TIGHTENED UNO.
15. ALL SITE DRILLED HOLE/CUT ENDS TO BE TREATED WITH METAFLUX 70-40 ZINC PASTE FOLLOWED BY 1 COAT OF 7-42 ZINC ALU OR 70-16 ALUMINIUM SPRAY

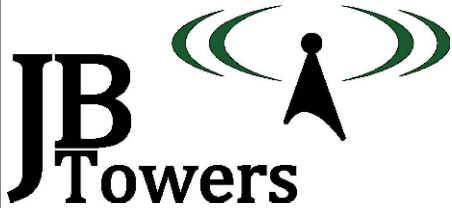

01	FIRST ISSUE	AM	10/10/18
REV	REV	BY	DATE
SCALE AS SHOWN WHEN PRINTED AT A3	DRAWN AM DATE 10/10/18	CHECKED MP DATE 10/10/18	APPROVED JBT DATE 10/10/18
ALL DIMENSIONS IN mm UNLESS OTHERWISE STATED. THIS DRAWING TO BE READ IN CONJUNCTION WITH OTHER RELEVANT DRAWINGS.			

TITLE
PARTS LIST

SITE ADDRESS		
THE MEADS COLDEAN BRIGHTON EAST SUSSEX BN1 9BA		
ARQIVA REF. 140357	DRG No. 304	REV 01

ALL SCALES AS SHOWN WHEN PRINTED AT A3



ALL SCALES AS SHOWN WHEN PRINTED AT A3