
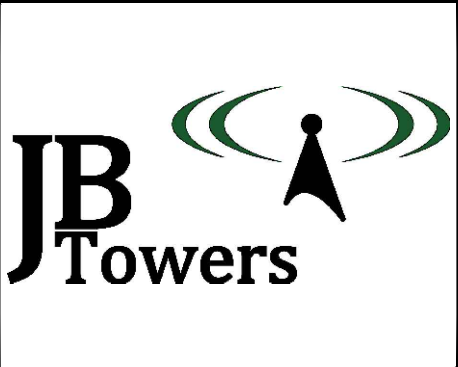
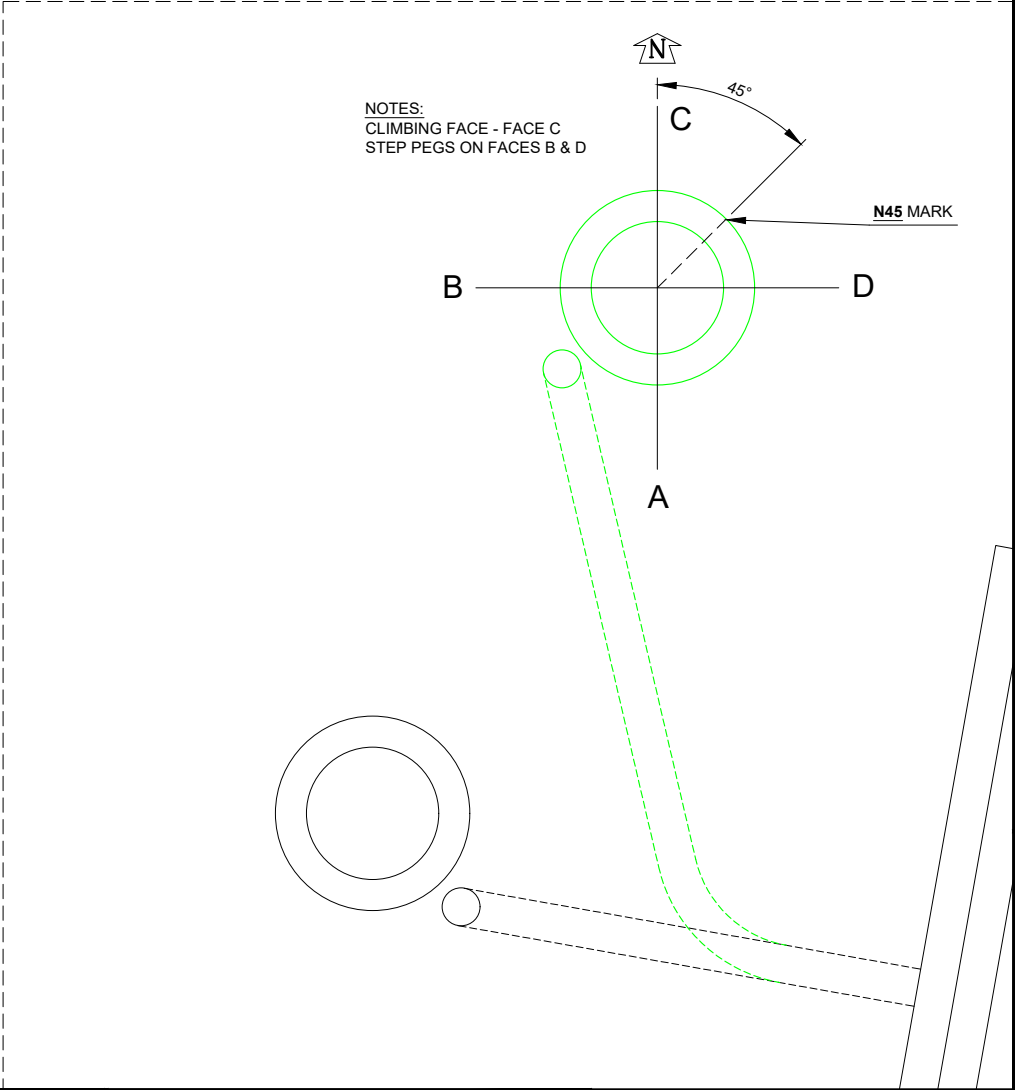


DRAWING ISSUE SHEET

[illegible]

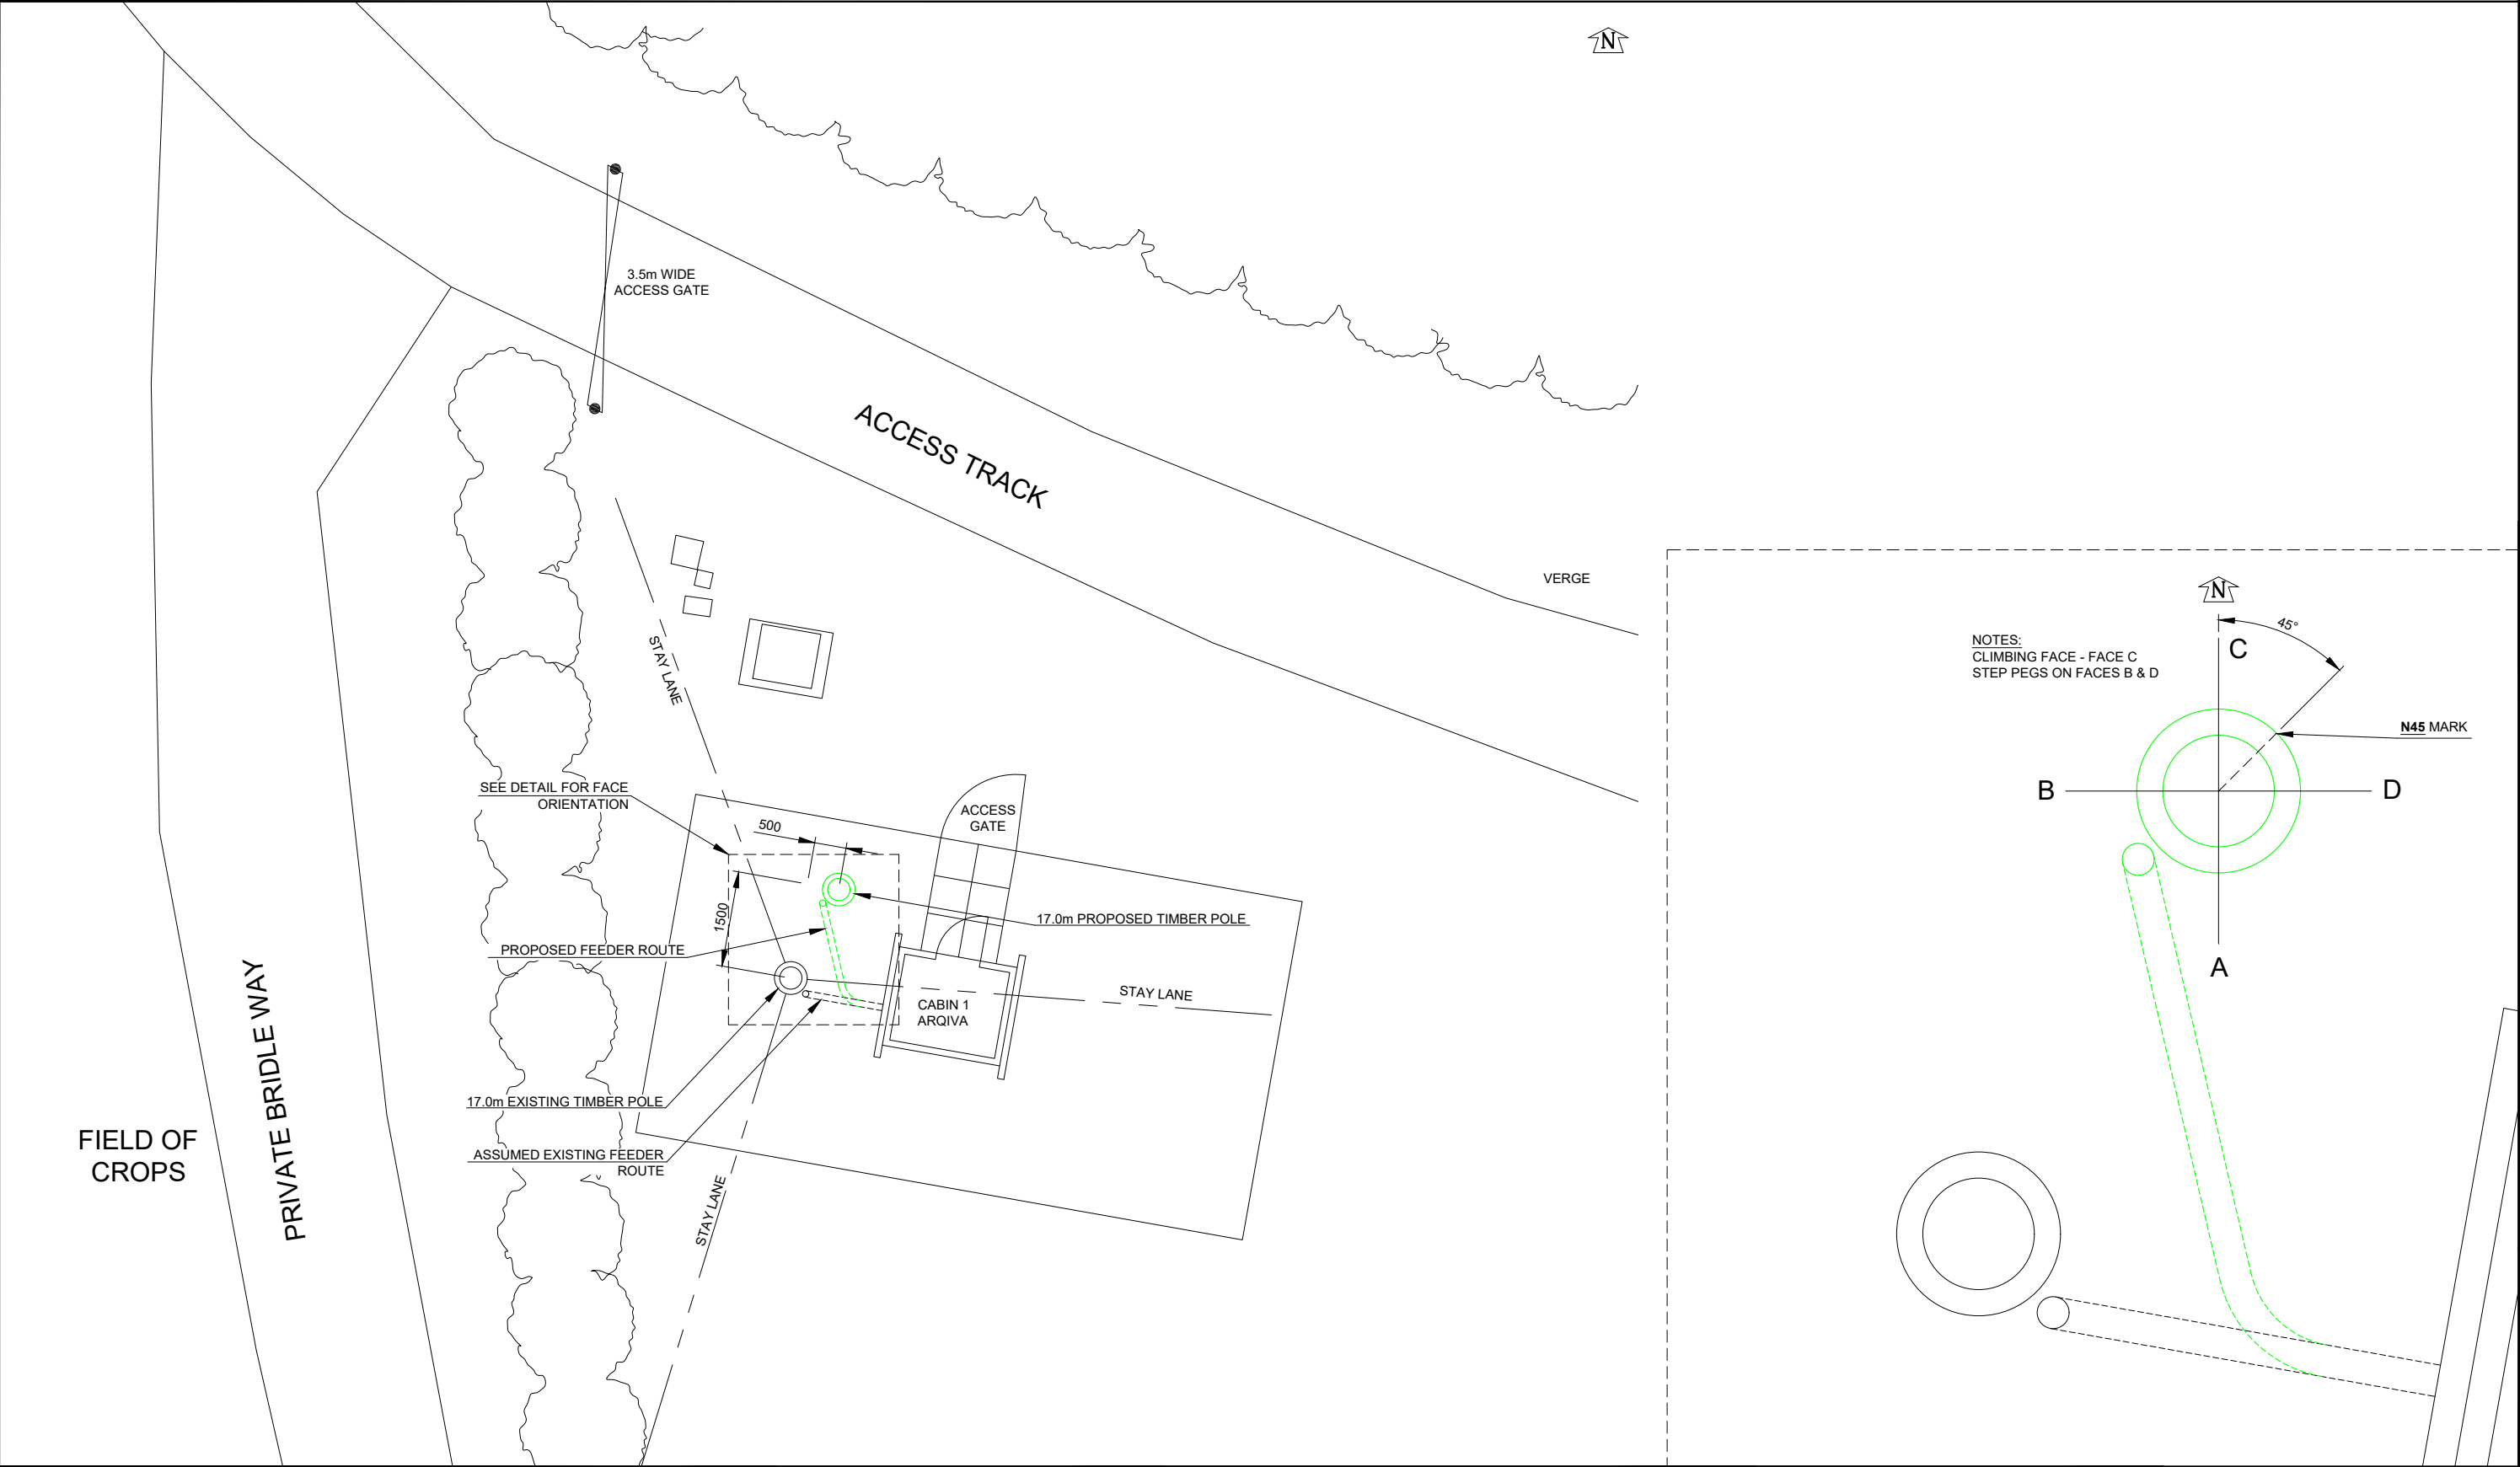


01	FIRST ISSUE				AM	23/10/18
REV	REV				BY	DATE
SCALE AS SHOWN		DRAWN	AM	CHECKED	MP	APPROVED JBT
WHEN PRINTED AT A3		DATE	23/10/18	DATE	23/10/18	DATE 23/10/18
ALL DIMENSIONS IN mm UNLESS OTHERWISE STATED.						THIS DRAWING TO BE READ IN CONJUNCTION WITH OTHER RELEVANT DRAWINGS.

TITLE
LULWORTH
SITE PLAN

SITE ADDRESS WINDFRITH DROVE WEST LULWORTH DORSET BH20 5PX		
ARQIVA REF. 141118	DRG No. 100	REV 01

ALL SCALES AS SHOWN WHEN PRINTED AT A3

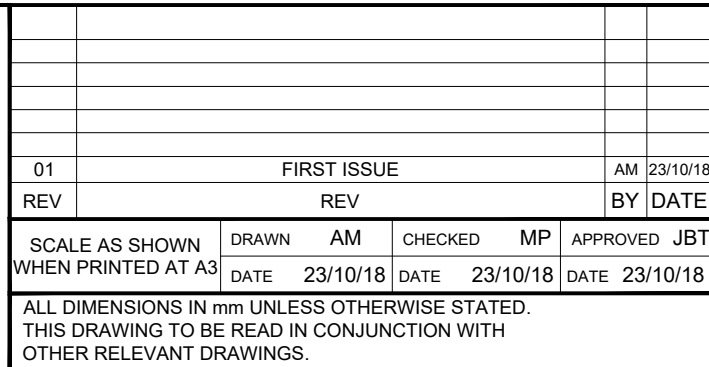

SITE ADDRESS


WINDFRITH DROVE
WEST LULWORTH
DORSET
BH20 5PX

DRG No.
200

1. SEE DRAWING 303 FOR PARTS LIST
2. ALL BOLTS TO BE CUT ON SITE TO EXTEND MAX 10mm BEYOND THE NUT WHEN TIGHTENED UNO.
3. ALL SITE DRILLED HOLE/CUT ENDS TO BE TREATED WITH METAFUX 70-40 ZINC PASTE FOLLOWED BY 1 COAT OF 7-42 ZINC ALU OR 70-16 ALUMINIUM SPRAY




1. POLE TO BE SUPPLIED IN ACCORDANCE WITH BS EN14229 & SHALL HAVE MIN. CHARACTERISTIC BENDING STRENGTH OF 30N/mm² & MIN. YOUNG'S MODULUS (PARALLEL TO GRAIN) OF 10KN/mm².
2. MARKINGS ON FINISHED POLE SHALL BE AT 4m FROM BUT AND COMPLY WITH BS EN 14229 UNO
3. AS FAR AS PRACTICABLE ALL CUTTING, SCARPING & DRILLING TO BE DONE BEFORE CREOSOTING. IF NOT ALL CUT, DRILLED & SCARFED SURFACES TO BE COATED WITH A MIXTURE OF CREOSOTE & TAR.
4. POLE TO BE PRESSURE IMPREGNATED WITH CREOSOTE IN ACCORDANCE WITH BS EN 14229
5. MINIMUM DIAMETERS
TOP - Ø200mm
BOTTOM - Ø430mm
6. 19.5m LONG POLE TO BE SOURCED BY TRIMMING 20m LONG POLE BY 0.5m AT THE TOP

1. CAT SCANNER IS TO BE USED IN ORDER TO CONFIRM THE POSITIONS OF BURIED SERVICES.
2. 'Penna-Soil Stabiliser' OR A SIMILAR APPROVED SHOULD BE USED IN ACCORDANCE WITH THE MANUFACTURER'S RECOMMENDATION.
3. ANY MATERIAL USED FOR BACK-FILLING IS TO BE OF EQUAL OR BETTER QUALITY THAN THE EXCAVATED MATERIAL.
4. ALL BACK-FILLING MATERIAL IS TO BE PLACED AND COMPACTED IN 150mm THICK LAYERS.
5. TIMBER POLE TO BE PLANTED WITH **N45** MARKING AT 3.5m FROM BUT FACING 45° FROM NORTH (CLOCKWISE)

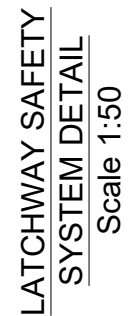

ALL SCALES AS SHOWN WHEN PRINTED AT A3

ALL SCALES AS SHOWN WHEN PRINTED AT A3

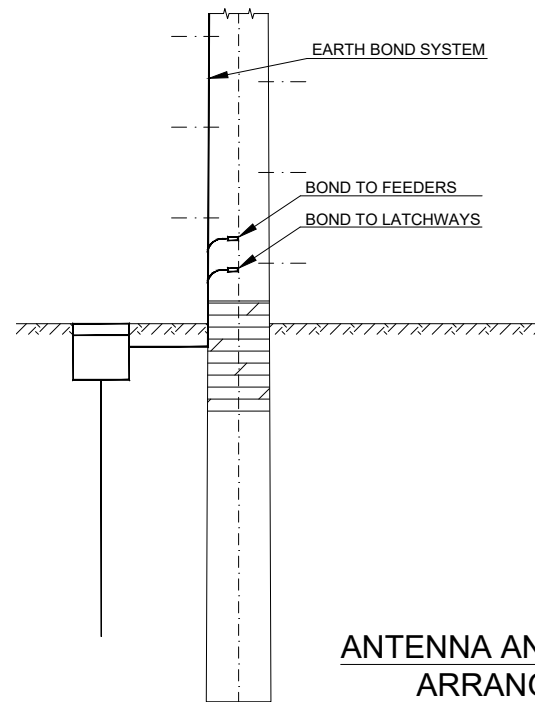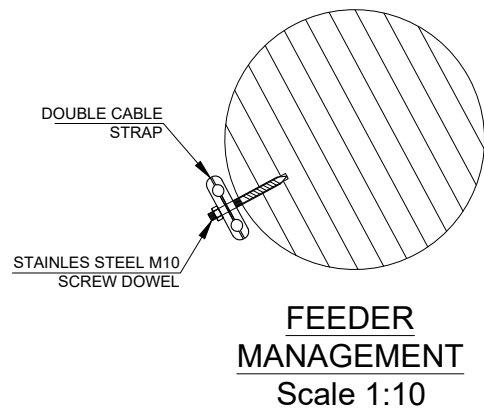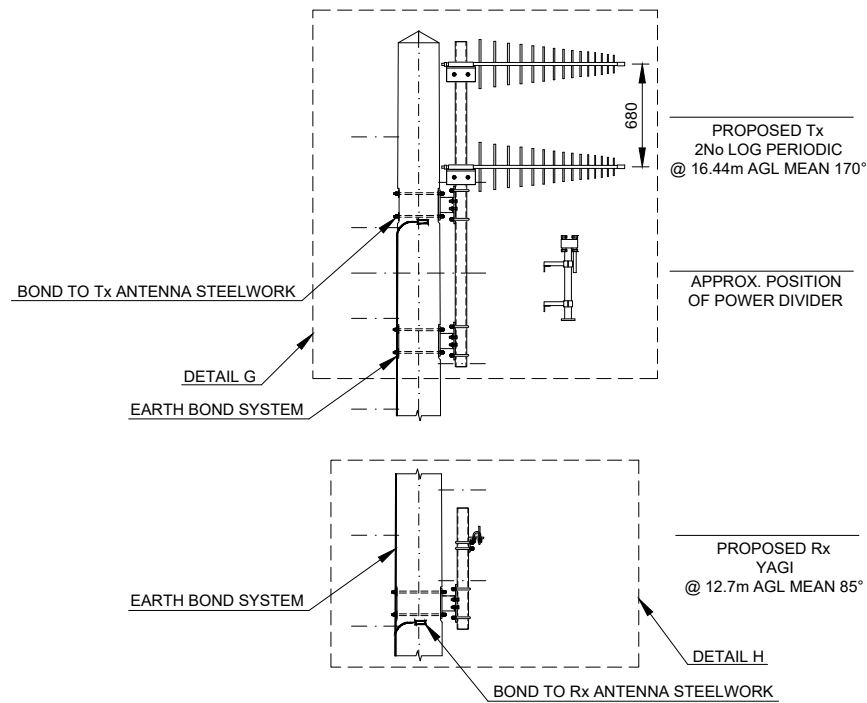

NOTES


1. AS FAR AS IS PRACTICABLE ALL CUTTING SCARFING AND DRILLING TO BE DONE BEFORE CREOSOTING. WHERE THIS IS NOT POSSIBLE ALL CUT, DRILLED, AND SCARFED SURFACES TO BE COATED WITH A MIXTURE OF CREOSOTE AND TAR

FEEDERS

1. SUPPLY OF FEEDERS BY OTHERS
LCF78-50 TO Tx ANTENNA &
LCF12-50 TO Rx ANTENNA
2. FEEDERS FIXED AT 1000mm CENTRES

EARTHING

1. CONNECT EARTH BOND TO NEW EARTHING SYSTEM
2. MAXIMUM VALUE FOR GROUND RESISTANCE TO BE 10 OHMS
3. CABLE OR TAPE TO BE FIXED TO POLE AT 1000mm CENTRES
4. EARTHING SHOULD COMPLY WITH ARQIVA'S DOCUMENT BOS147

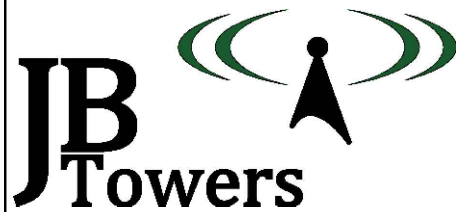


01	FIRST ISSUE	AM	23/10/18
REV	REV	BY	DATE
SCALE AS SHOWN WHEN PRINTED AT A3	DRAWN DATE 23/10/18	CHECKED DATE 23/10/18	APPROVED DATE 23/10/18
ALL DIMENSIONS IN mm UNLESS OTHERWISE STATED. THIS DRAWING TO BE READ IN CONJUNCTION WITH OTHER RELEVANT DRAWINGS.			

TITLE		SITE ADDRESS	
LULWORTH		WINDFRITH DROVE WEST LULWORTH DORSET BH20 5PX	
GENERAL ARRANGEMENT SHEET 2 OF 3		ARQIVA REF. 141118	DRG No. 200
			REV 01

ALL SCALES AS SHOWN WHEN PRINTED AT A3




ALL SCALES AS SHOWN WHEN PRINTED AT A3

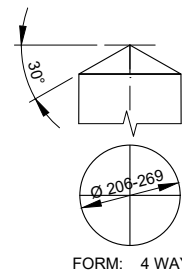


NOTES:
 1. A SINGLE COAT OF TIMBER COMPATIBLE BITUMINOUS PAINT (E.G. BIRD BRAND BLACK BITUMINOUS PAINT OR SIMILAR APPROVED PRODUCT) TO BE APPLIED TO THE UPPER SURFACES AT THE TOP OF THE POLE.
 2. PAINT TO BE APPLIED ON SITE JUST BEFORE ERECTION
 FORM: 4 WAY PYRAMID / CONE


DETAIL A - TIMBER POLE TOP
 Scale 1:20

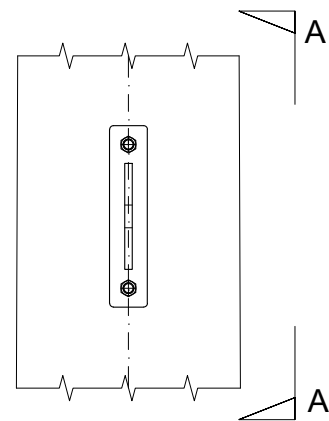


DETAIL C - FALL ARREST ATTACHMENT POINT
 Scale 1:10

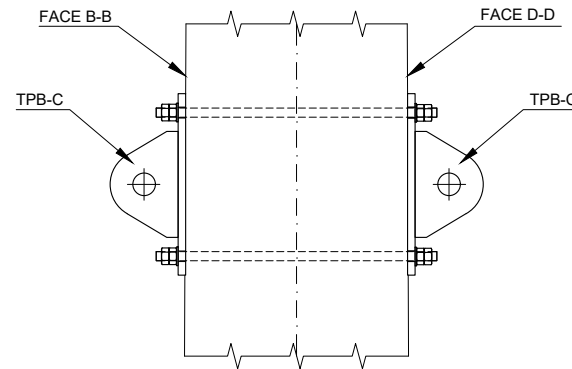


VIEW A-A
 Scale 1:10

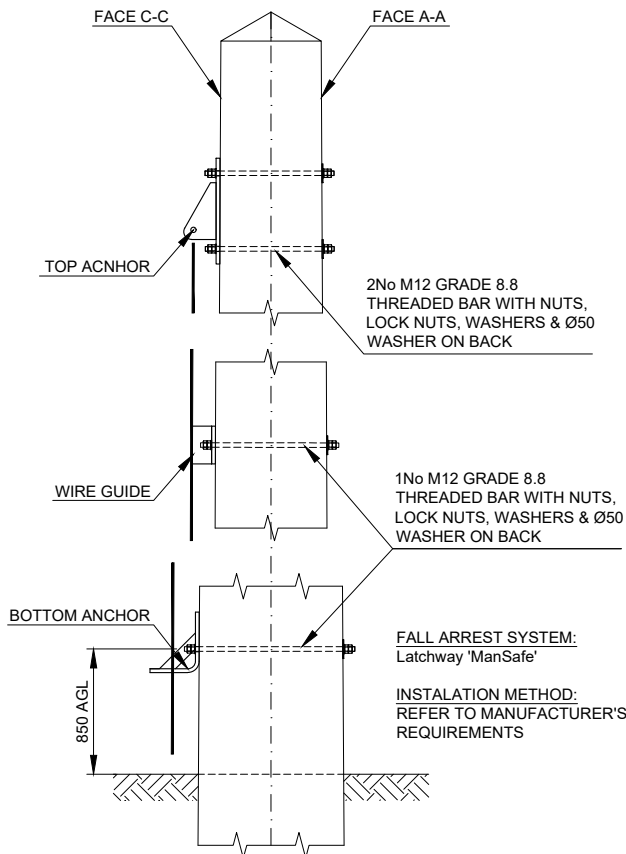

DETAIL B - FALL ARREST SYSTEM
 Scale 1:20

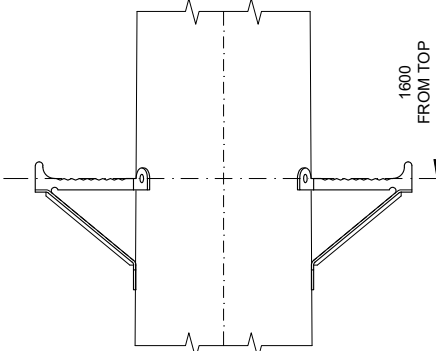


DETAIL D - ANTENNA ACCESS CLIMBING STEP
 Scale 1:10

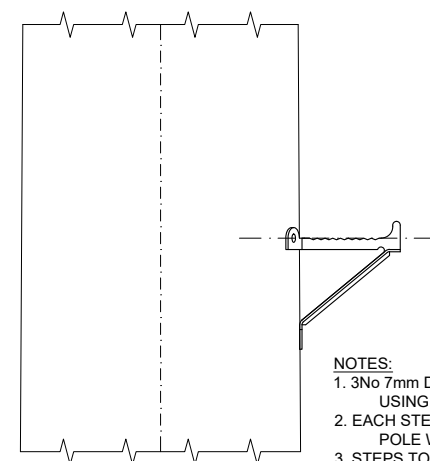

DETAIL E - PERMANENT CLIMBING STEPS
 Scale 1:10

NOTES:
 1. 3No 7mm DIA 70mm LONG PILOT HOLES TO BE DRILLED USING THE STEP AS A TEMPLATE
 2. EACH STEP SHOULD BE FIXED TO THE TIMBER POLE WITH 3No 10mm COACH SCREWS 75mm LONG
 3. STEPS TO BE INSTALLED ON FACES B-B & D-D ONLY

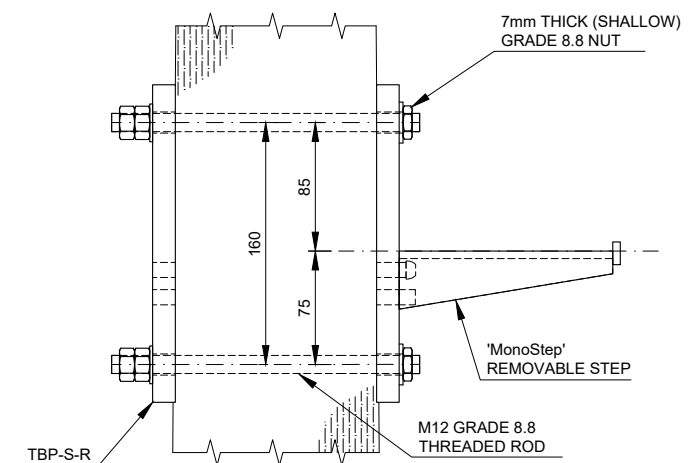


DETAIL F - REMOVABLE CLIMBING STEPS
 Scale 1:5

ALL SCALES AS SHOWN WHEN PRINTED AT A3



ALL SCALES AS SHOWN WHEN PRINTED AT A3

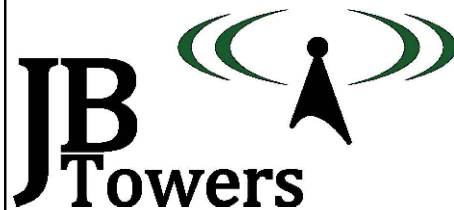


01	FIRST ISSUE	AM	23/10/18
REV	REV	BY	DATE
SCALE AS SHOWN WHEN PRINTED AT A3	DRAWN AM	CHECKED MP	APPROVED JBT
DATE 23/10/18	DATE 23/10/18	DATE 23/10/18	DATE 23/10/18
ALL DIMENSIONS IN mm UNLESS OTHERWISE STATED. THIS DRAWING TO BE READ IN CONJUNCTION WITH OTHER RELEVANT DRAWINGS.			

TITLE
 LULWORTH
 GENERAL ARRANGEMENT
 SHEET 3 OF 3

SITE ADDRESS
 WINDFRITH DROVE
 WEST LULWORTH
 DORSET
 BH20 5PX

ARQIVA REF. 141118
 DRG No. 200
 REV 01

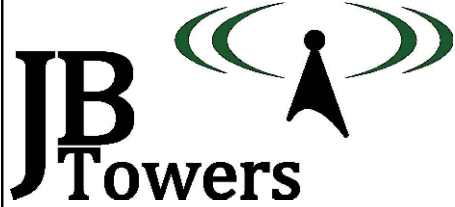

01	FIRST ISSUE			AM	23/10/18
REV	REV			BY	DATE
SCALE AS SHOWN		DRAWN	AM	CHECKED	MP
WHEN PRINTED AT A3		DATE	23/10/18	DATE	23/10/18
		DATE	23/10/18	DATE	23/10/18
ALL DIMENSIONS IN mm UNLESS OTHERWISE STATED. THIS DRAWING TO BE READ IN CONJUNCTION WITH OTHER RELEVANT DRAWINGS.					

TITLE

LULWORTH

TIMBER POLE HOLE SET OUT

SHEET 1 OF 2

SITE ADDRESS

WINDFRITH DROVE

WEST LULWORTH

DORSET

BH20 5PX

ARQIVA REF.


141118

DRG No.


201

REV

01

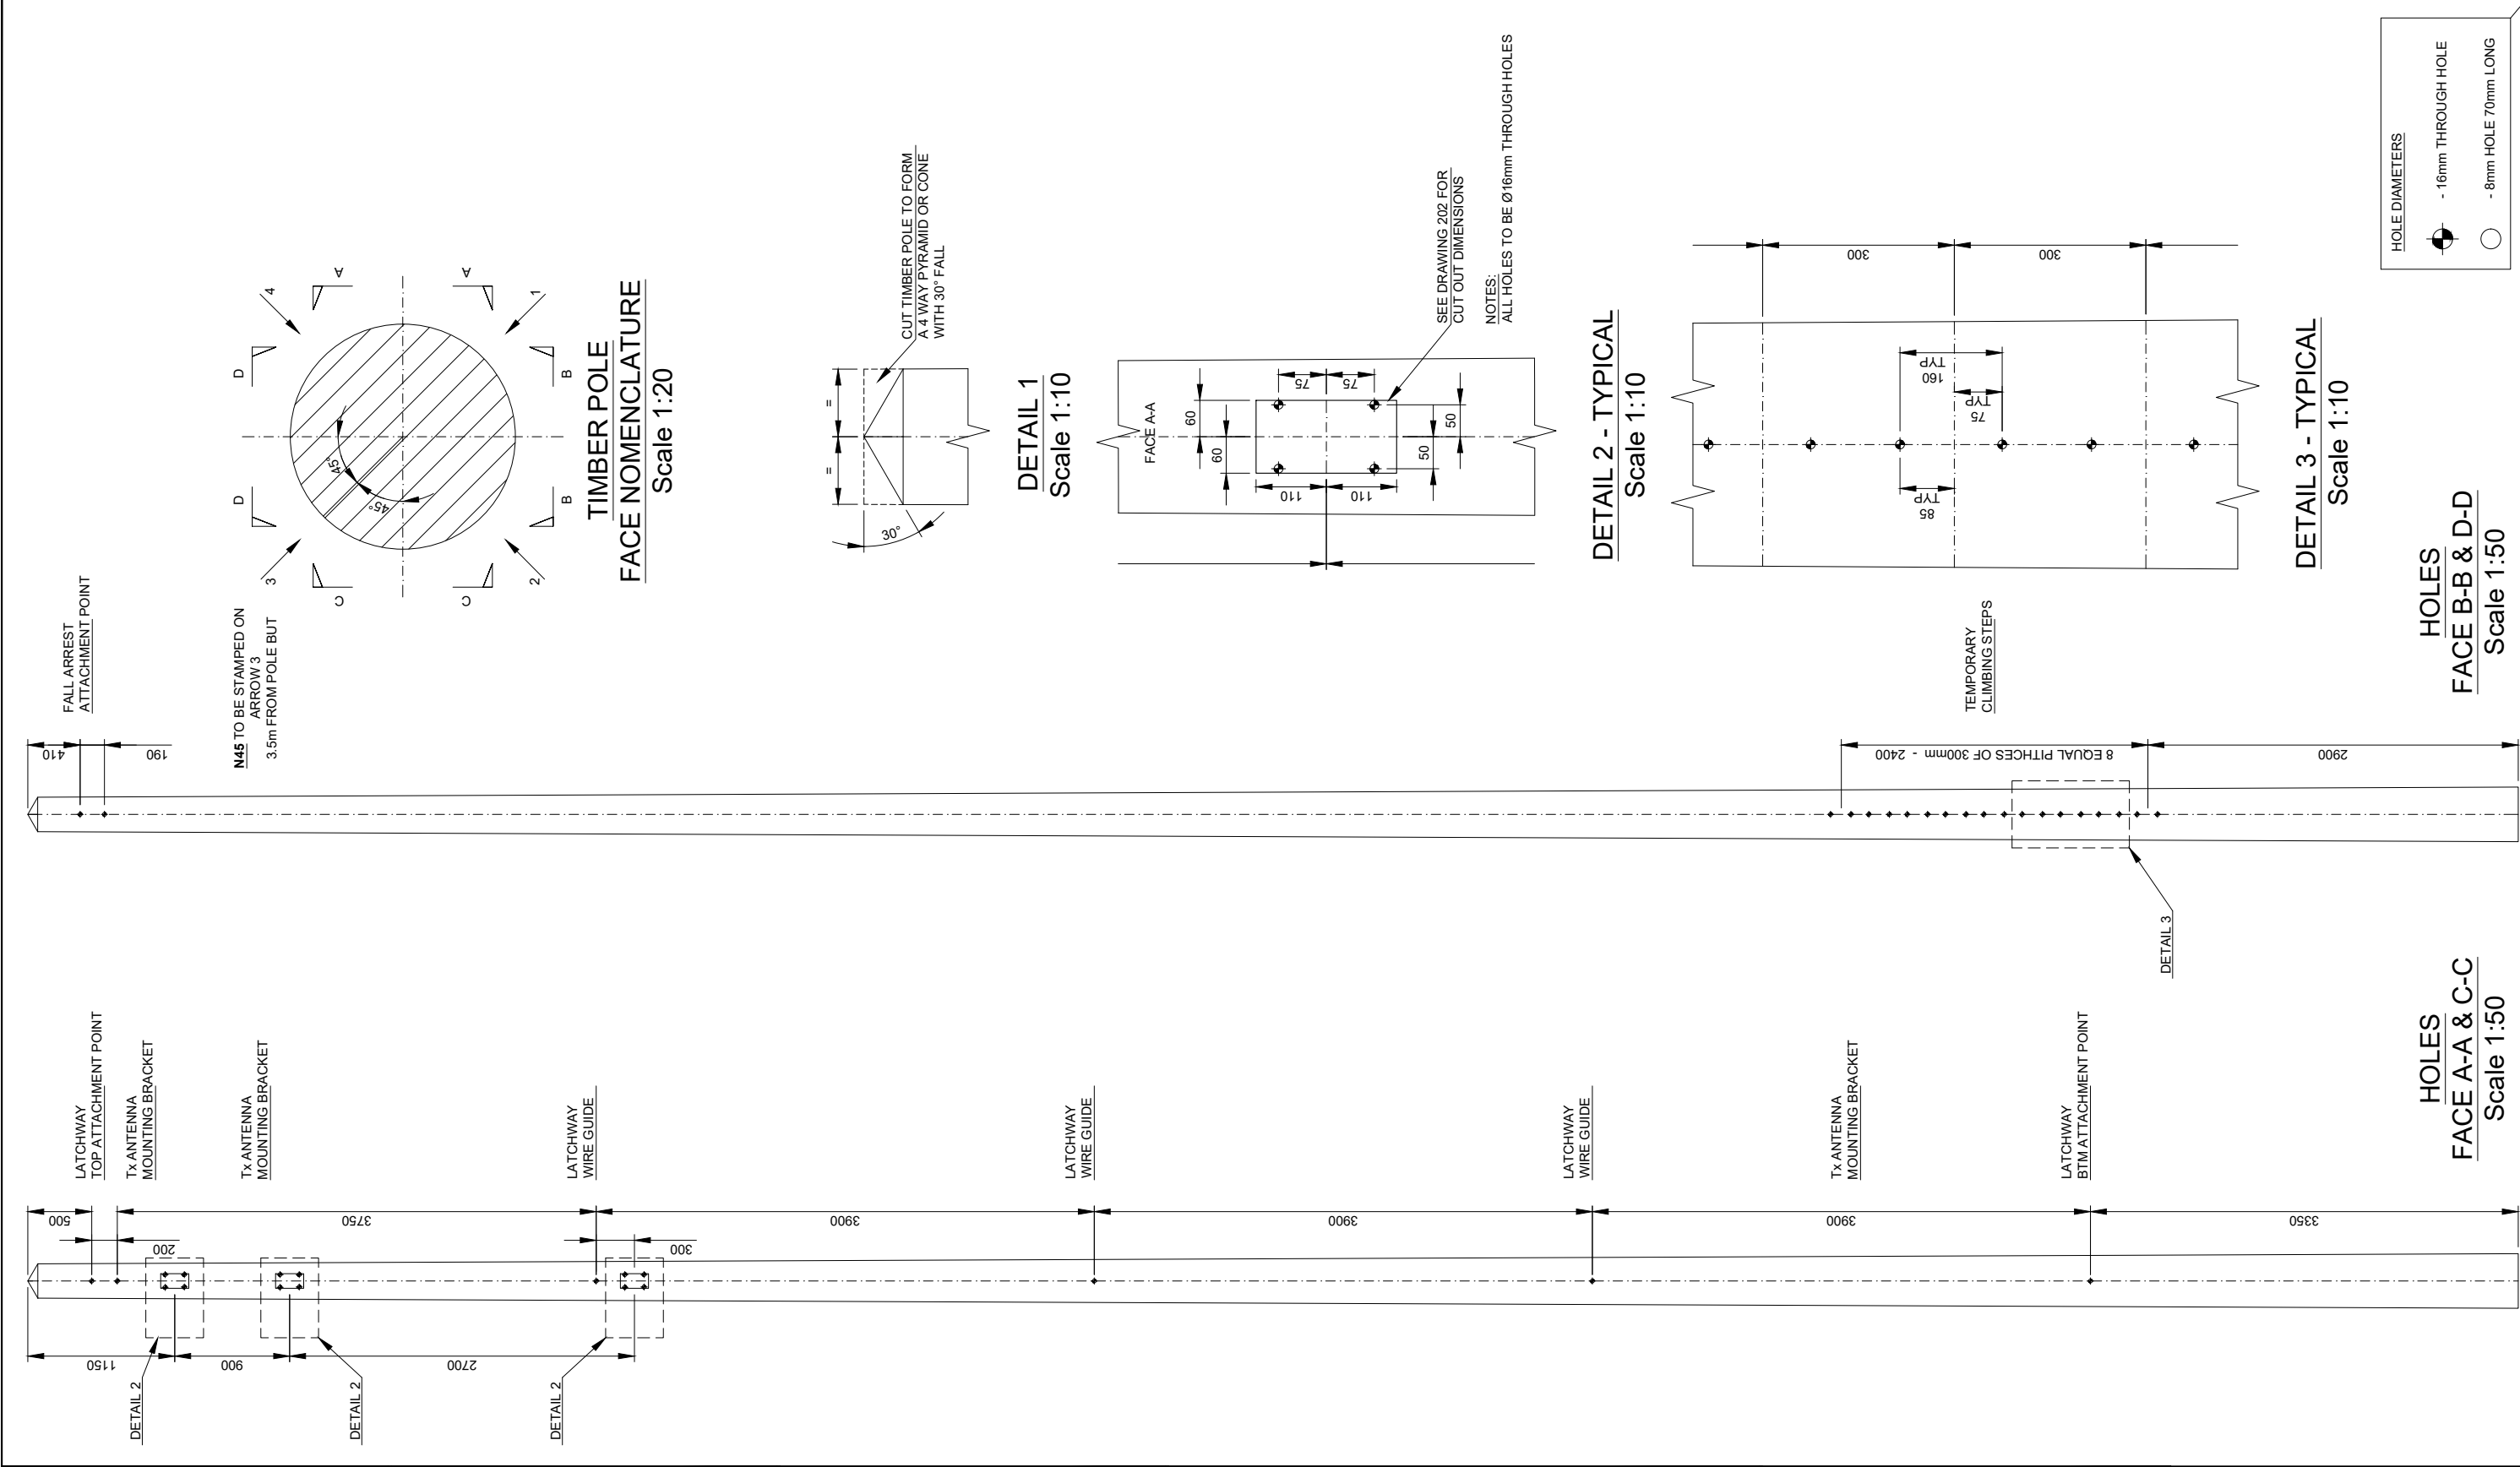



ALL SCALES AS SHOWN WHEN PRINTED AT A3

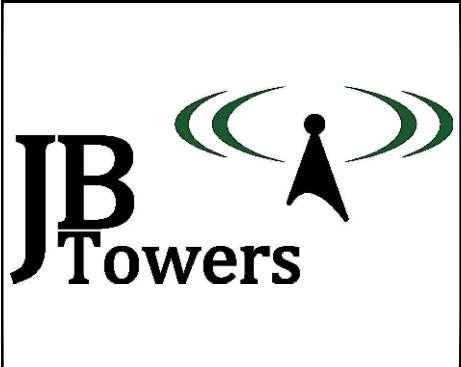


01	FIRST ISSUE			AM	23/10/18
REV	REV			BY	DATE
SCALE AS SHOWN		DRAWN	AM	CHECKED	MP
WHEN PRINTED AT A3		DATE	23/10/18	DATE	23/10/18
		DATE	23/10/18	DATE	23/10/18
ALL DIMENSIONS IN mm UNLESS OTHERWISE STATED. THIS DRAWING TO BE READ IN CONJUNCTION WITH OTHER RELEVANT DRAWINGS.					

TITLE
LULWORTH
TIMBER POLE HOLE SET OUT
SHEET 2 OF 2

SITE ADDRESS		
WINDFRITH DROVE WEST LULWORTH DORSET BH20 5PX		
ARQIVA REF. 141118	DRG No. 201	REV 01

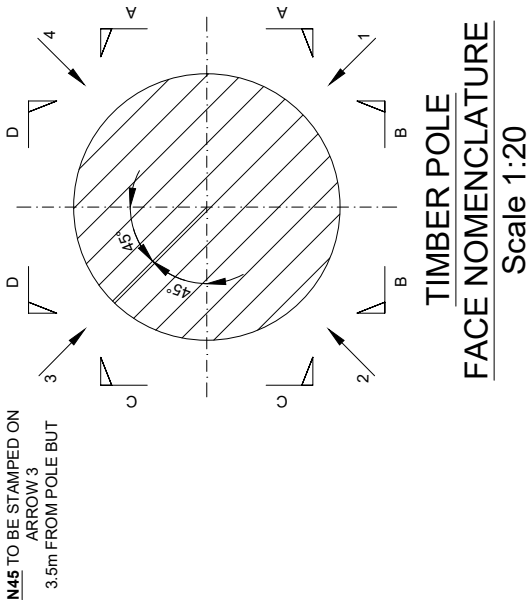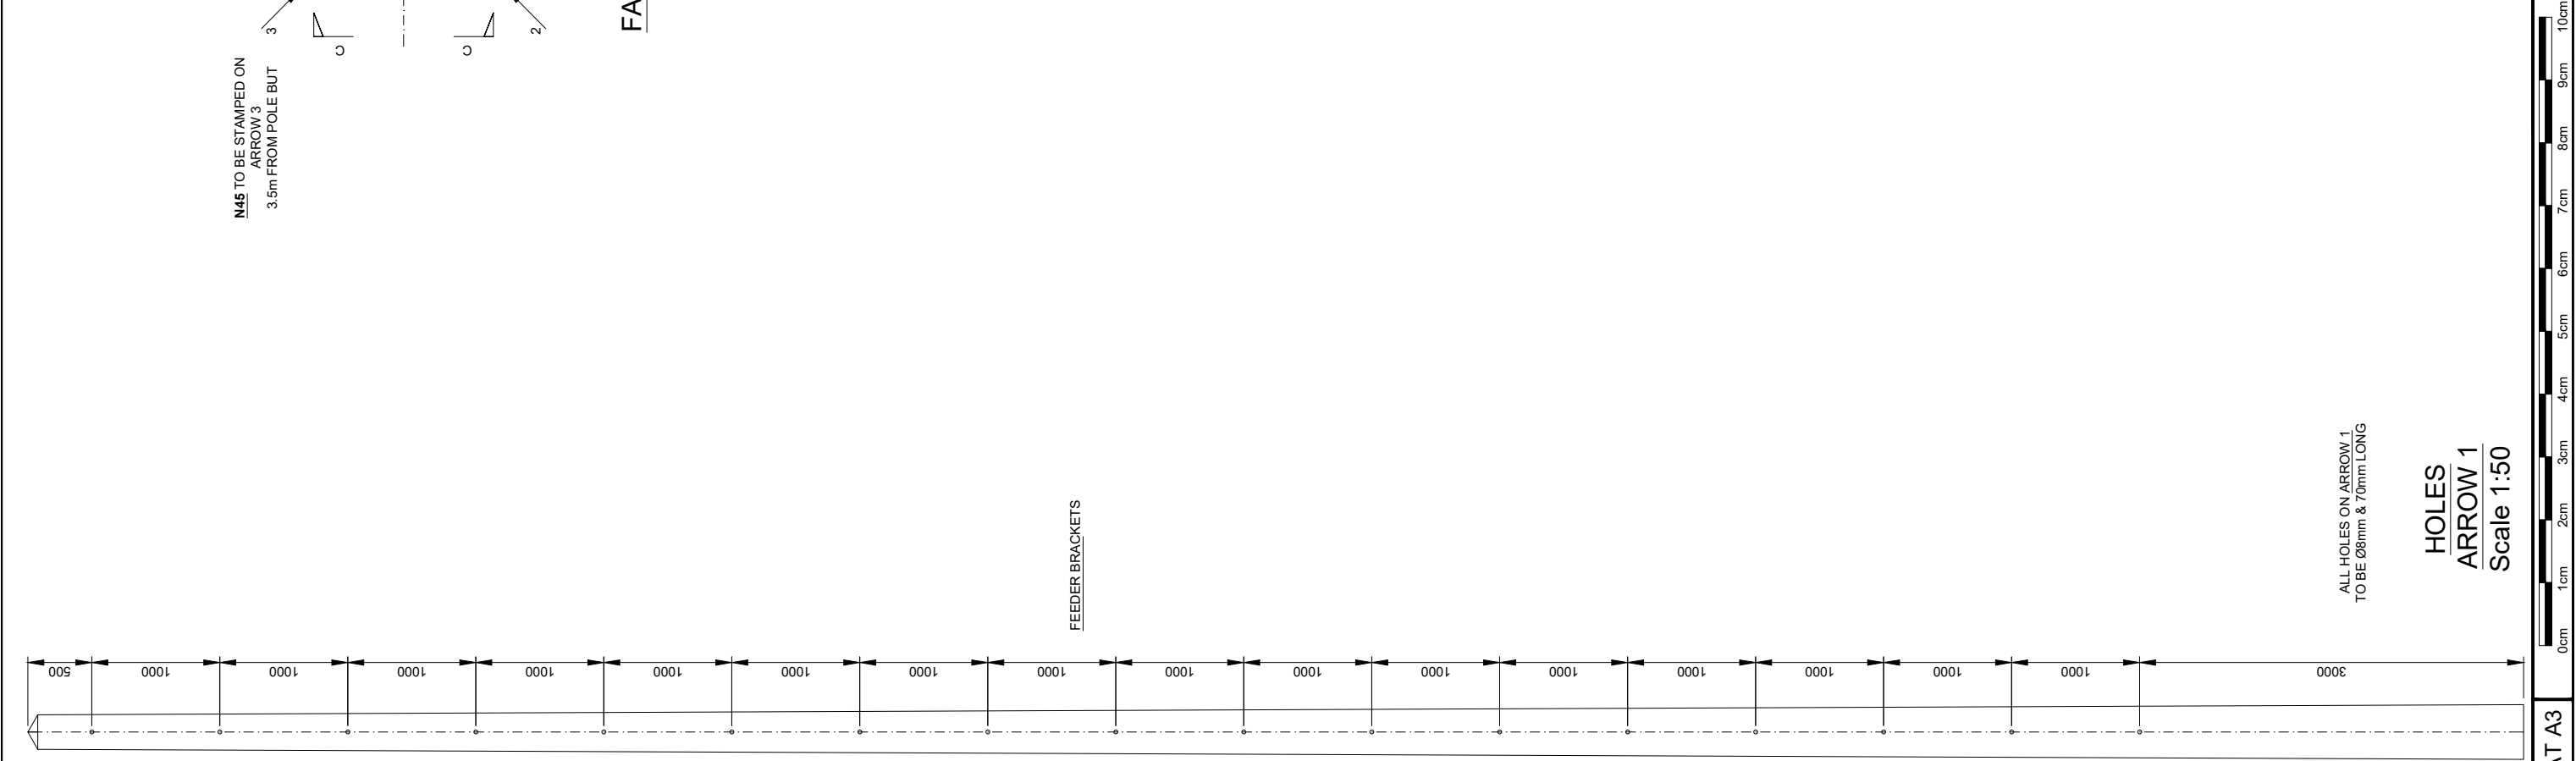

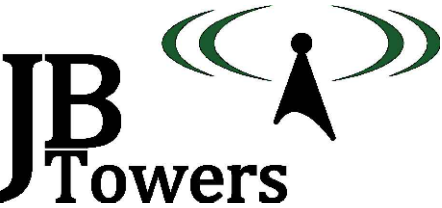

01	FIRST ISSUE							AM	23/10/18
REV	REV							BY	DATE
SCALE AS SHOWN WHEN PRINTED AT A3		DRAWN	AM	CHECKED	MP	APPROVED		JBT	
		DATE	23/10/18	DATE	23/10/18	DATE		23/10/18	
ALL DIMENSIONS IN mm UNLESS OTHERWISE STATED. THIS DRAWING TO BE READ IN CONJUNCTION WITH OTHER RELEVANT DRAWINGS.									


TITLE

LULWORTH


TIMBER POLE CUT OUT
DETAIL

SITE ADDRESS		
WINDFRITH DROVE WEST LULWORTH DORSET BH20 5PX		
ARQIVA REF. 141118	DRG No. 202	REV 01


TIMBER POLE CUT OUT
DETAIL

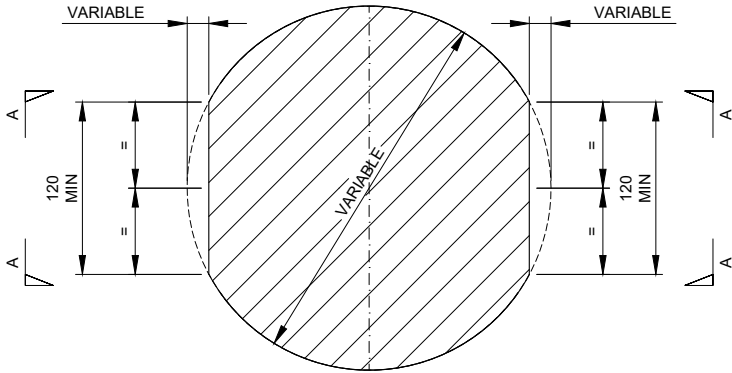

PLAN VIEW
Scale 1:5

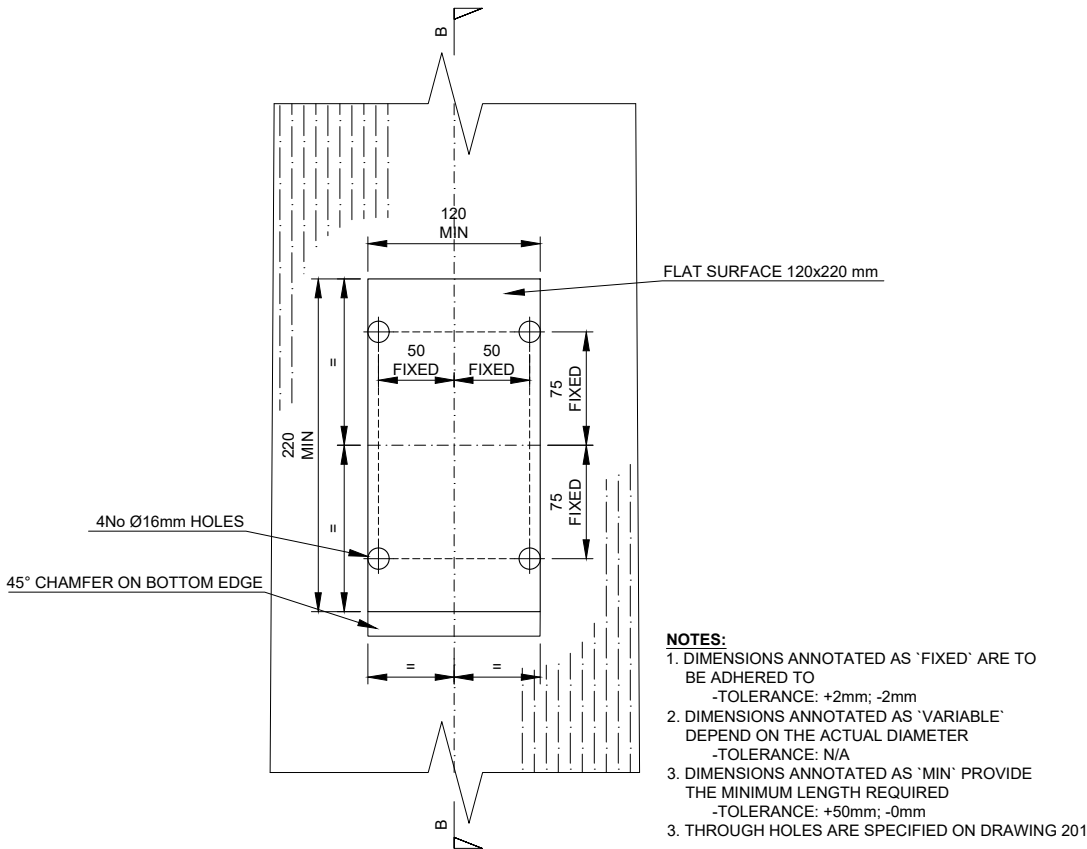

VIEW A-A
Scale 1:5

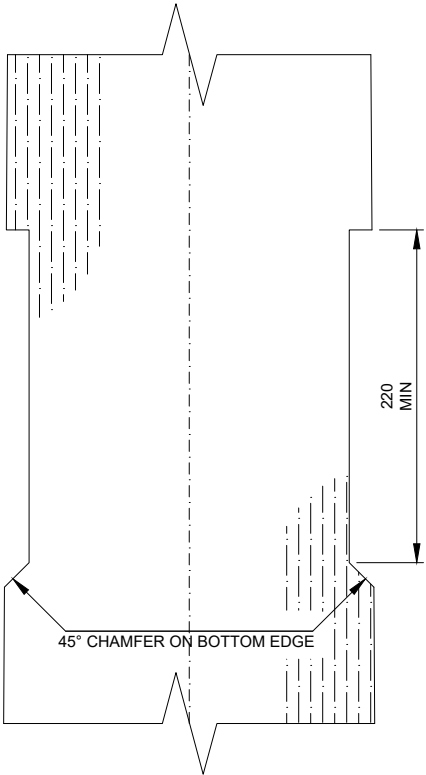


VIEW B-B
Scale 1:5

- NOTES:
- DIMENSIONS ANNOTATED AS 'FIXED' ARE TO BE ADHERED TO
-TOLERANCE: +2mm; -2mm
 - DIMENSIONS ANNOTATED AS 'VARIABLE' DEPEND ON THE ACTUAL DIAMETER
-TOLERANCE: N/A
 - DIMENSIONS ANNOTATED AS 'MIN' PROVIDE THE MINIMUM LENGTH REQUIRED
-TOLERANCE: +50mm; -0mm
 - THROUGH HOLES ARE SPECIFIED ON DRAWING 201

ALL SCALES AS SHOWN WHEN PRINTED AT A3



ALL SCALES AS SHOWN WHEN PRINTED AT A3

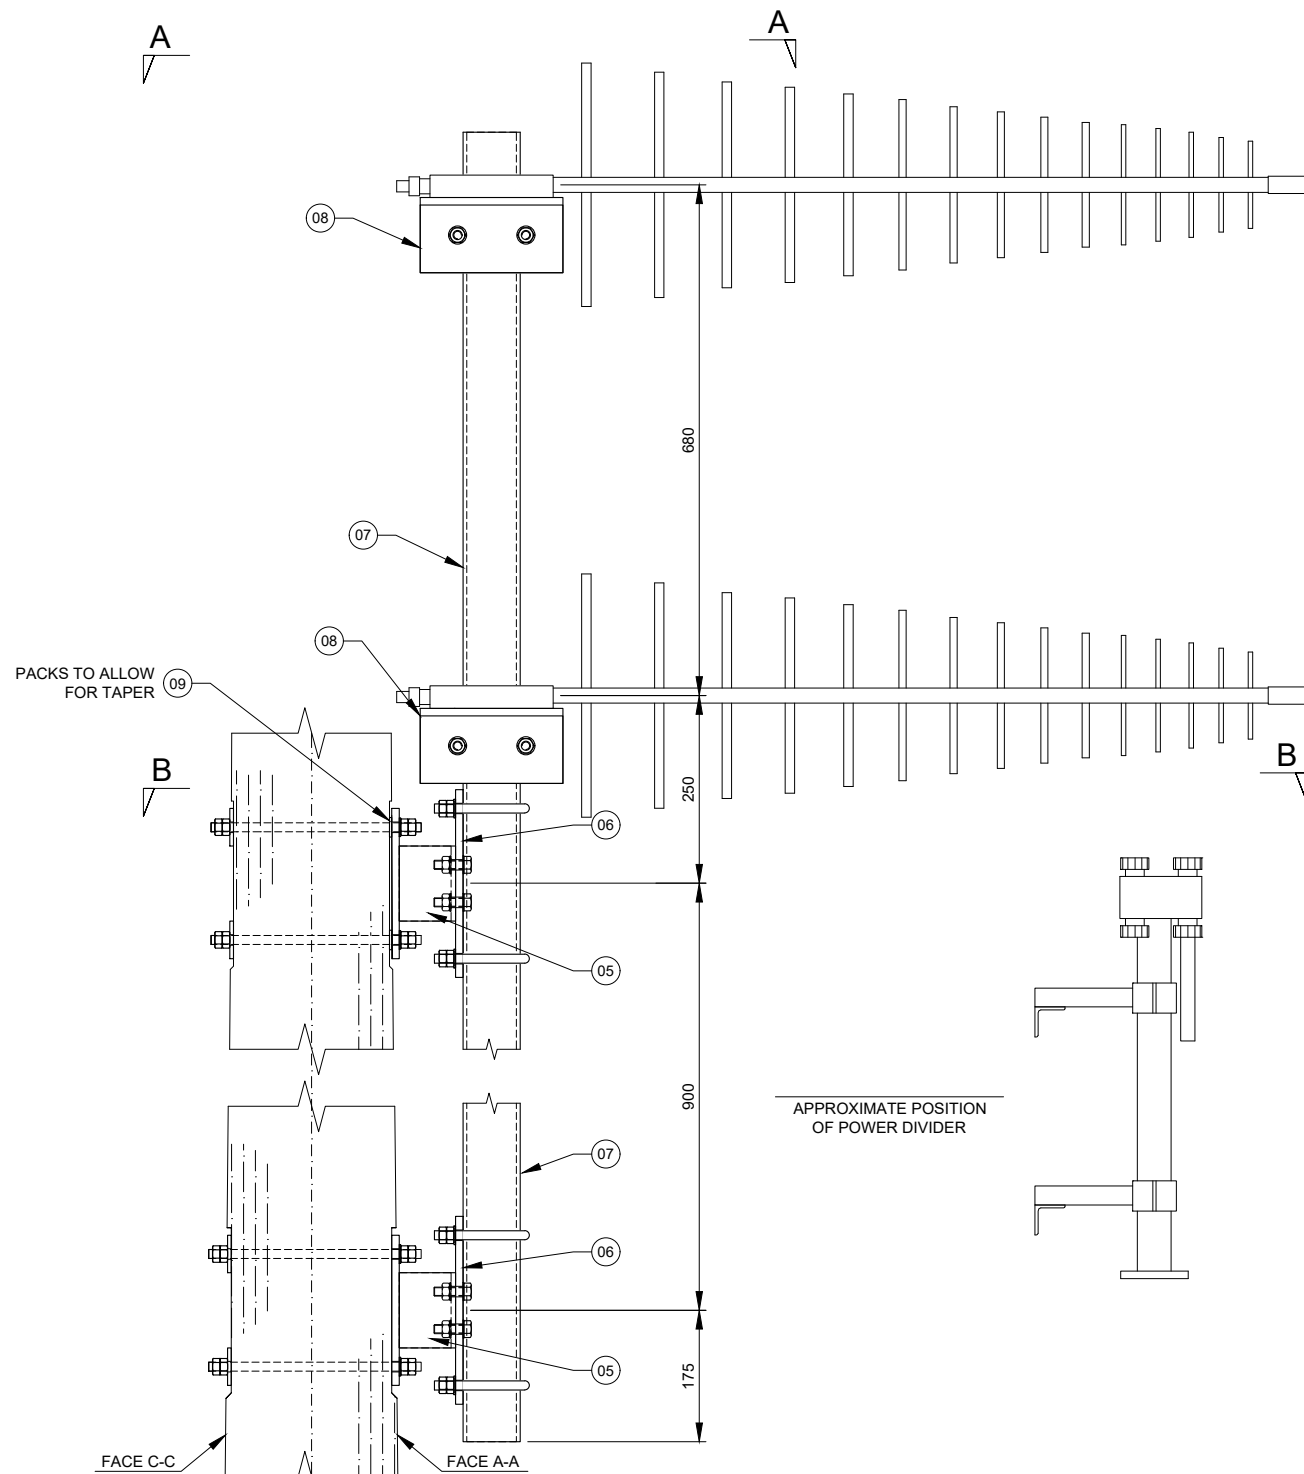


PACKS TO ALLOW FOR TAPER

APPROXIMATE POSITION OF POWER DIVIDER


FACE C-C

FACE A-A

DETAIL G - Tx ANTENNA MOUNT
Scale 1:10


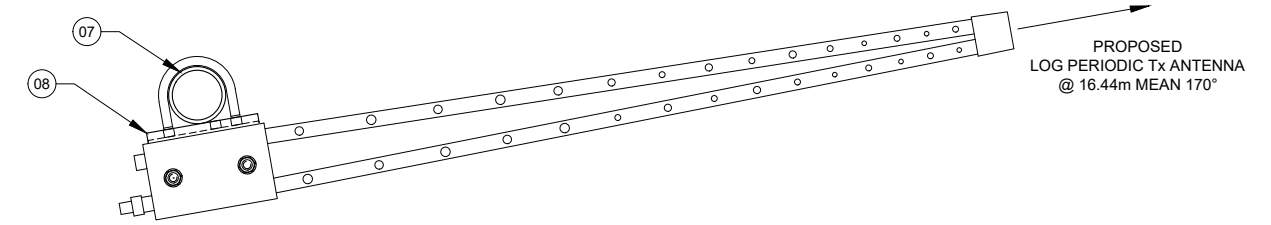


SECTION A-A
Scale 1:10

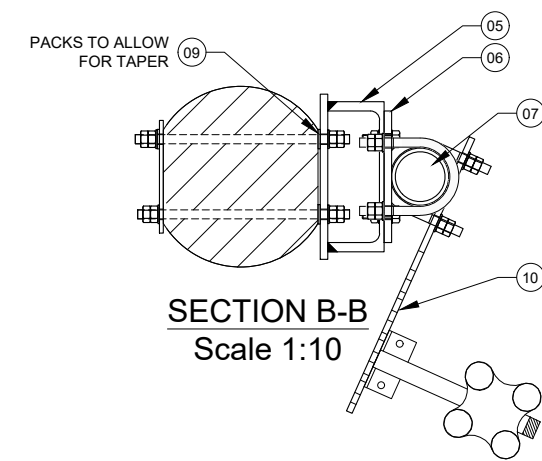

SECTION B-B
Scale 1:10

PROPOSED LOG PERIODIC Tx ANTENNA @ 16.44m MEAN 170°

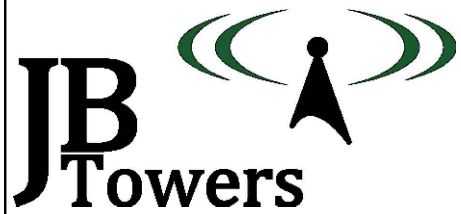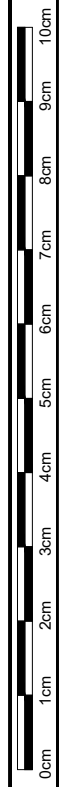

01	FIRST ISSUE			AM	23/10/18
REV	REV			BY	DATE
SCALE AS SHOWN WHEN PRINTED AT A3		DRAWN	AM	CHECKED	MP
		DATE	23/10/18	DATE	23/10/18
		APPROVED	JBT		
		DATE	23/10/18		


ALL DIMENSIONS IN mm UNLESS OTHERWISE STATED.
THIS DRAWING TO BE READ IN CONJUNCTION WITH OTHER RELEVANT DRAWINGS.

TITLE
Tx ANTENNA MOUNT
DETAIL G


SITE ADDRESS
WINDFRITH DROVE
WEST LULWORTH
DORSET
BH20 5PX

ARQIVA REF. 141118	DRG No. 203	REV 01
-----------------------	----------------	-----------

ALL SCALES AS SHOWN WHEN PRINTED AT A3

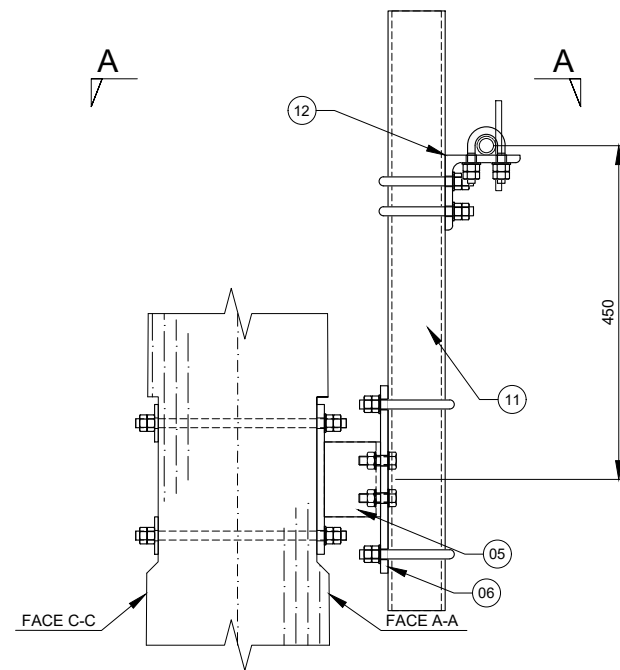

DETAIL H - Rx ANTENNA MOUNT
Scale 1:10

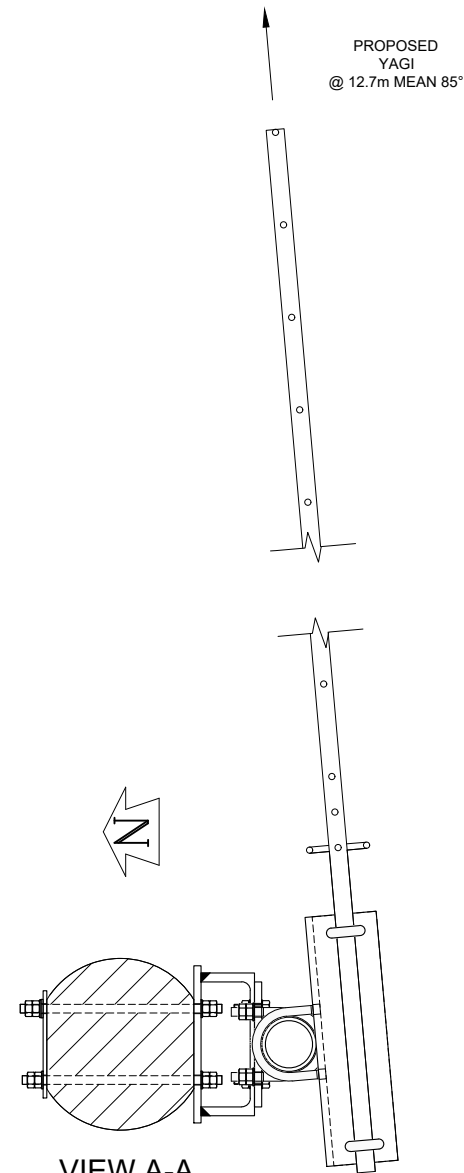


VIEW A-A
Scale 1:10

ALL SCALES AS SHOWN WHEN PRINTED AT A3



ALL SCALES AS SHOWN WHEN PRINTED AT A3

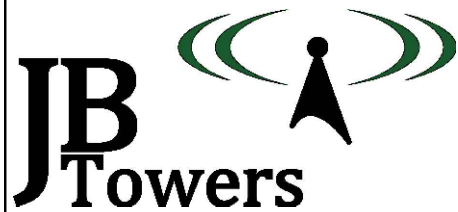


chalcroft
construction built on teamwork

arqiva


01	FIRST ISSUE	AM	23/10/18
REV	REV	BY	DATE
SCALE AS SHOWN WHEN PRINTED AT A3	DRAWN DATE 23/10/18	CHECKED DATE 23/10/18	APPROVED DATE 23/10/18
ALL DIMENSIONS IN mm UNLESS OTHERWISE STATED. THIS DRAWING TO BE READ IN CONJUNCTION WITH OTHER RELEVANT DRAWINGS.			

TITLE	Rx ANTENNA MOUNT		SITE ADDRESS	
DETAIL H			WINDFRITH DROVE WEST LULWORTH DORSET BH20 5PX	
ARQIVA REF. 141118	DRG No. 204	REV 01		

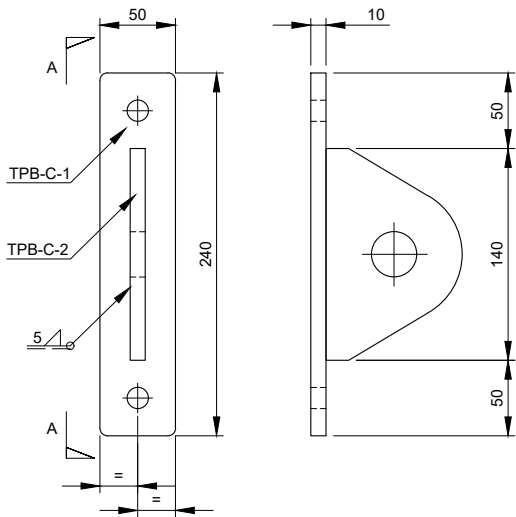

PART TPB-C
Scale 1:5

VIEW A-A
Scale 1:5

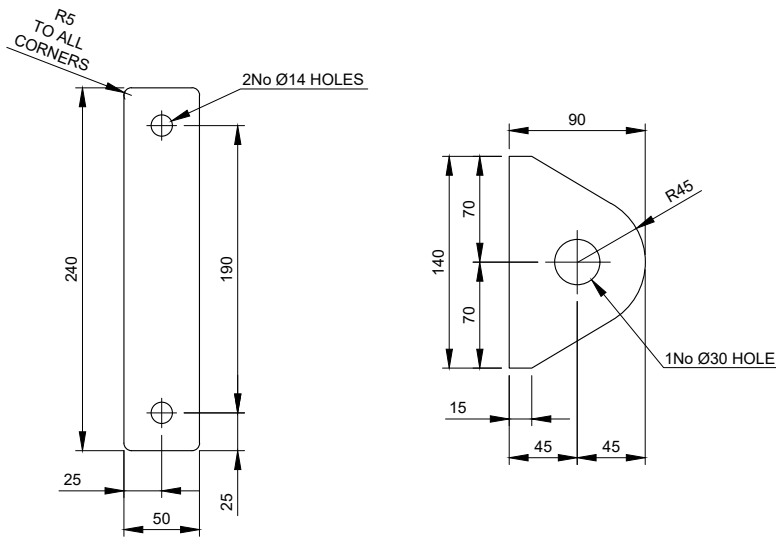


TPB-C-1 - 10mm THICK
Scale 1:5

TPB-C-2 - 10mm THICK
Scale 1:5

Parts list for TPB-C

Item	Part	Quantity	Part description	Length	Material	Weight
01	TPB-C-1	1	240x50x10mm	N/A	S275J0	0.94 kg
02	TPB-C-2	1	140x90x10mm	N/A	S275J0	0.99 kg
03	STUDS	1	M12 STUDDING	350mm	GRADE 8.8	0.31 kg
Total Weight:						2.24 kg

- All steel hot dip galvanized
- Each STUD to be supplied with 4 Full Nuts, 2 Flat Washers and 2 Spring Washers
- For fabrctation notes see drawing 303

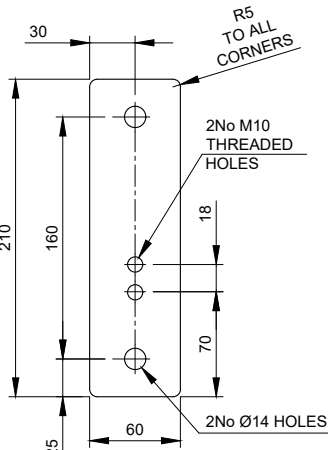


PART TPS-R
Scale 1:5

Parts list for TPS-R

Item	Part	Quantity	Part description	Length	Material	Weight
01	TPS-R	2	210x60x15mm	N/A	S275J0	1.48 kg
02	STUDS	2	M12 STUDDING	500mm	GRADE 8.8	0.44 kg
03	NUT-S	2	M12 SHALLOW NUT	N/A	GRADE 8.8	-
04	NUT	4	M12 NUT	N/A	GRADE 8.8	-
03	WSH	4	M12 WASHER	N/A	GRADE 8.8	-
Total Weight:						3.84 kg

- All steel hot dip galvanized
- For fabrctation notes see drawing 303

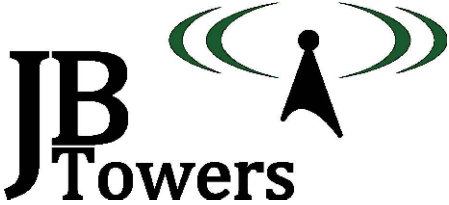

01	FIRST ISSUE	AM	23/10/18
REV	REV	BY	DATE
SCALE AS SHOWN WHEN PRINTED AT A3	DRAWN DATE 23/10/18	CHECKED DATE 23/10/18	APPROVED DATE 23/10/18
ALL DIMENSIONS IN mm UNLESS OTHERWISE STATED. THIS DRAWING TO BE READ IN CONJUNCTION WITH OTHER RELEVANT DRAWINGS.			

TITLE
ATTACHMENT POINT &
TEMPORARY STEP DETAILS
PARTS: TPB-C; TPS-R

SITE ADDRESS
WINDFRITH DROVE
WEST LULWORTH
DORSET
BH20 5PX

ARQIVA REF.
141118
DRG No.
300
REV
01

ALL SCALES AS SHOWN WHEN PRINTED AT A3









ALL SCALES AS SHOWN WHEN PRINTED AT A3

01	FIRST ISSUE			AM	23/10/18
REV	REV			BY	DATE
SCALE AS SHOWN WHEN PRINTED AT A3		DRAWN DATE 23/10/18	AM DATE 23/10/18	CHECKED DATE 23/10/18	MP DATE 23/10/18
		APPROVED		JBT	
ALL DIMENSIONS IN mm UNLESS OTHERWISE STATED. THIS DRAWING TO BE READ IN CONJUNCTION WITH OTHER RELEVANT DRAWINGS.					

TITLE
STEELWORK BRACKET
PART: TPB-B

SITE ADDRESS
WINDFRITH DROVE
WEST LULWORTH
DORSET
BH20 5PX

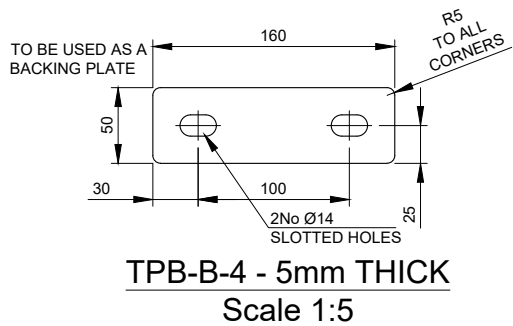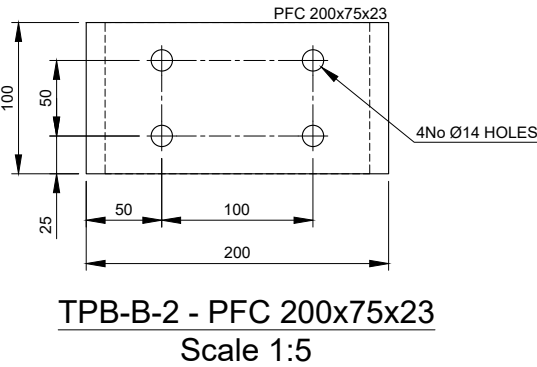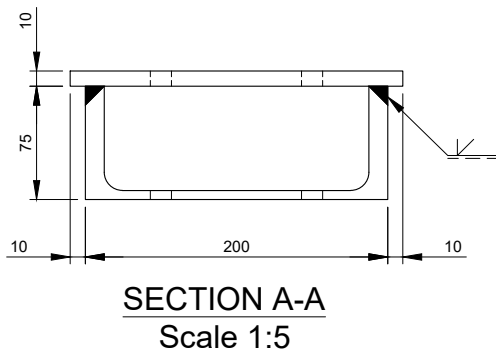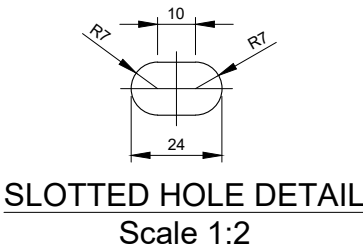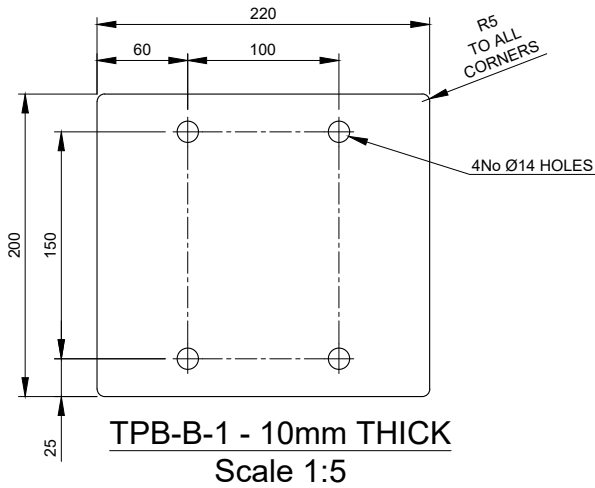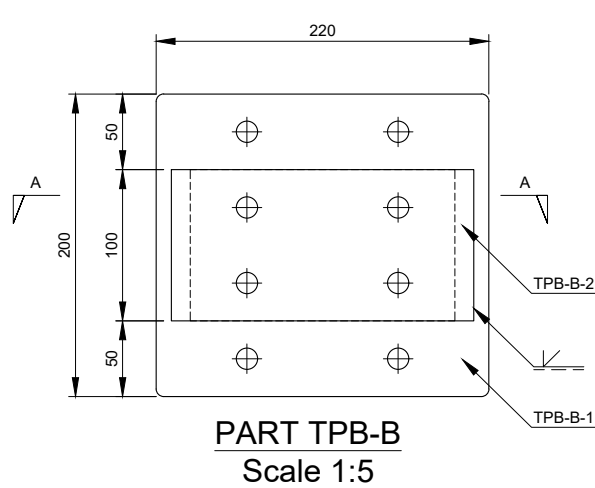

Parts list for TPB-B

Item	Part	Quantity	Part description	Length	Material	Weight
01	TPB-B-1	1	220x200x10mm	N/A	S275J0	3.45 kg
02	TPB-B-2	1	PFC 200x75x23	100mm	S275J0	2.30 kg
03	TPB-B-4	2	160x50x5mm	N/A	S275J0	0.31 kg
04	STUDS	4	M12 STUDDING	400mm	GRADE 8.8	0.35 kg

- All steel hot dip galvanized
- Each STUD & U-BOLT to be supplied with 4 Full Nuts, 2 Flat Washers and 2 Spring Washers
- Each BOLT to be supplied with 1 Full Nut, 1 Form E Flat Washer and 1 Spring Washer
- For fabrication notes see drawing 303


Total Weight: 7.77 kg

Item	Part	Drawing	Quantity	Part description	Length	Material	Weight
01	01	200	1	3 MAN LATCHWAY SYSTEM & 3No. WIRE GUIDES FOR FACE MOUNTED MONOPOLE	17000	N/A	-
02	TPB-C	300	2	FALL ARREST ATTACHMENT POINT	N/A	S275J0	4.48 kg
03	03	200	46	PERMANENT BT STEP c/w 3No 10x75mm ZINC-PLATED COACH SCREWS	N/A	S275J0	13.80 kg
04	TPS-R	300	9	'MonoStep' ASSEMBLY	N/A	S275J0	34.56 kg
05	TPB-B	301	3	MOUNTING BRACKET	N/A	S275J0	23.31 kg
06	TPP-A	302	3	PLATE A INTERFACE	N/A	S275J0	10.35 kg
07	07	203	1	CHS 76.1x5mm	2150mm	S355J2H	18.86 kg
08	TPL-A	302	2	LOG MOUNTING BRACKET	150mm	S275J0	4.50 kg
09	09	203	12	M12 WASHER	N/A	GRADE 8.8	-
10	TPA-PD	302	2	POWER DIVIDER STRAP	N/A	S275J0	2.52 kg
11	11	204	1	CHS 76.1x5mm	800mm	S355J2H	7.02 kg
12	TPY-A	302	1	YAGI MOUNTING BRACKET	350mm	S275J0	5.25 kg
13	13	200	1	FEEDER COVER - 2/CG/100	3500mm	UV RESISTANT PLASTIC	-
14	14	200	17	FEEDER CLAMP - 2/FCD/028	N/A	POLYPROPYLENE	-
15	15	200	17	M10 SCREW DOWELS WTH M10 NUT	100mm	STAINLESS STEEL	-
16	16	200	1	PoleSaver	750mm	N/A	-
17	17	200	8	M12 STUD + 4No NUTS + 2No FLAT WASHERS + 1No Ø50mm WASHER (FOR FALL ARREST SYSTEM)	500mm	GRADE 8.8	3.56 kg
Total Weight:							128.21 kg

- All steel hot dip galvanized
- All U-BOLTS to be FLA supply, each Supplied with 4 Full Nuts, 2 Flat Washers and 2 Spring Washers

NOTES:

1. WELDING TO BE IN ACCORDANCE WITH BS EN 1011-1:2009
2. LINEAR DIMS TO BE WITHIN ±1mm;
3. ANGULAR TOLERANCES TO BE WITHIN 0.5°
4. WELDING SYMBOLS ARE IN ACCORDANCE WITH BS EN 22553:1995
5. ALL PROFILE EDGES TO BE DRESSED AND SHARP CORNERS REMOVED
6. ALL WELD SIZES ARE FINAL SIZES
7. ALL WELDED JOINTS ARE TO BE PICKLE TIGHT
8. ALL STEELWORK TO BE BS EN 10025 GRADE S275 J0 UNO & 9. HOT DIPPED GALVANISED TO BS EN ISO 1461. (ALL HOLLOW SECTIONS TO BE GRADE S355 J0H)
10. ALL STEEL IS TO BE SUPPLIED IN ACCORDANCE WITH EN 1090 TO EXECUTION CLASS 2
11. ALL NON PRE-LOADED BOLTS TO BE COMPLIANT STRUCTURAL BOLTS TO BS EN ISO 15048 PARTS 1&2.
12. STEELWORK COMPONENTS SHALL BE HOT DIP GALVANISED TO ACHIEVE A "VERY HIGH" DURABILITY FOR AN ENVIRONMENT CATEGORY CODE C4 FROM TABLE 1 IN BS EN ISO 14713
13. BOLTS AND NUTS SHALL BE SUPPLIED IN ACCORDANCE WITH BS 7371, SPUN GALVANISED IN ACCORDANCE WITH ISO 10684, THE NUTS RE-TAPPED AFTER GALVANISING, AND THE THREADS TREATED WITH GREASE.
14. ALL BOLTS TO BE CUT ON SITE TO EXTEND MAX 10mm BEYOND THE NUT WHEN TIGHTENED UNO.
15. ALL SITE DRILLED HOLE/CUT ENDS TO BE TREATED WITH METAFLUX 70-40 ZINC PASTE FOLLOWED BY 1 COAT OF 7-42 ZINC ALU OR 70-16 ALUMINIUM SPRAY

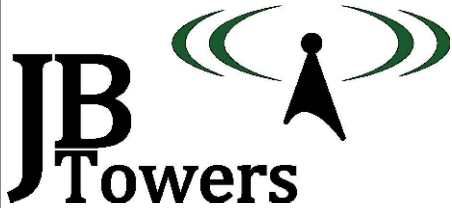

01	FIRST ISSUE					AM	23/10/18
REV	REV					BY	DATE
SCALE AS SHOWN WHEN PRINTED AT A3		DRAWN	AM	CHECKED	MP	APPROVED	JBT
		DATE	23/10/18	DATE	23/10/18	DATE	23/10/18
ALL DIMENSIONS IN mm UNLESS OTHERWISE STATED. THIS DRAWING TO BE READ IN CONJUNCTION WITH OTHER RELEVANT DRAWINGS.							

TITLE
PARTS LIST

SITE ADDRESS
WINDFRITH DROVE
WEST LULWORTH
DORSET
BH20 5PX

ARQIVA REF.
141118

DRG No.
303

REV
01

ALL SCALES AS SHOWN WHEN PRINTED AT A3



ALL SCALES AS SHOWN WHEN PRINTED AT A3