



DRAWING ISSUE SHEET

[illegible]

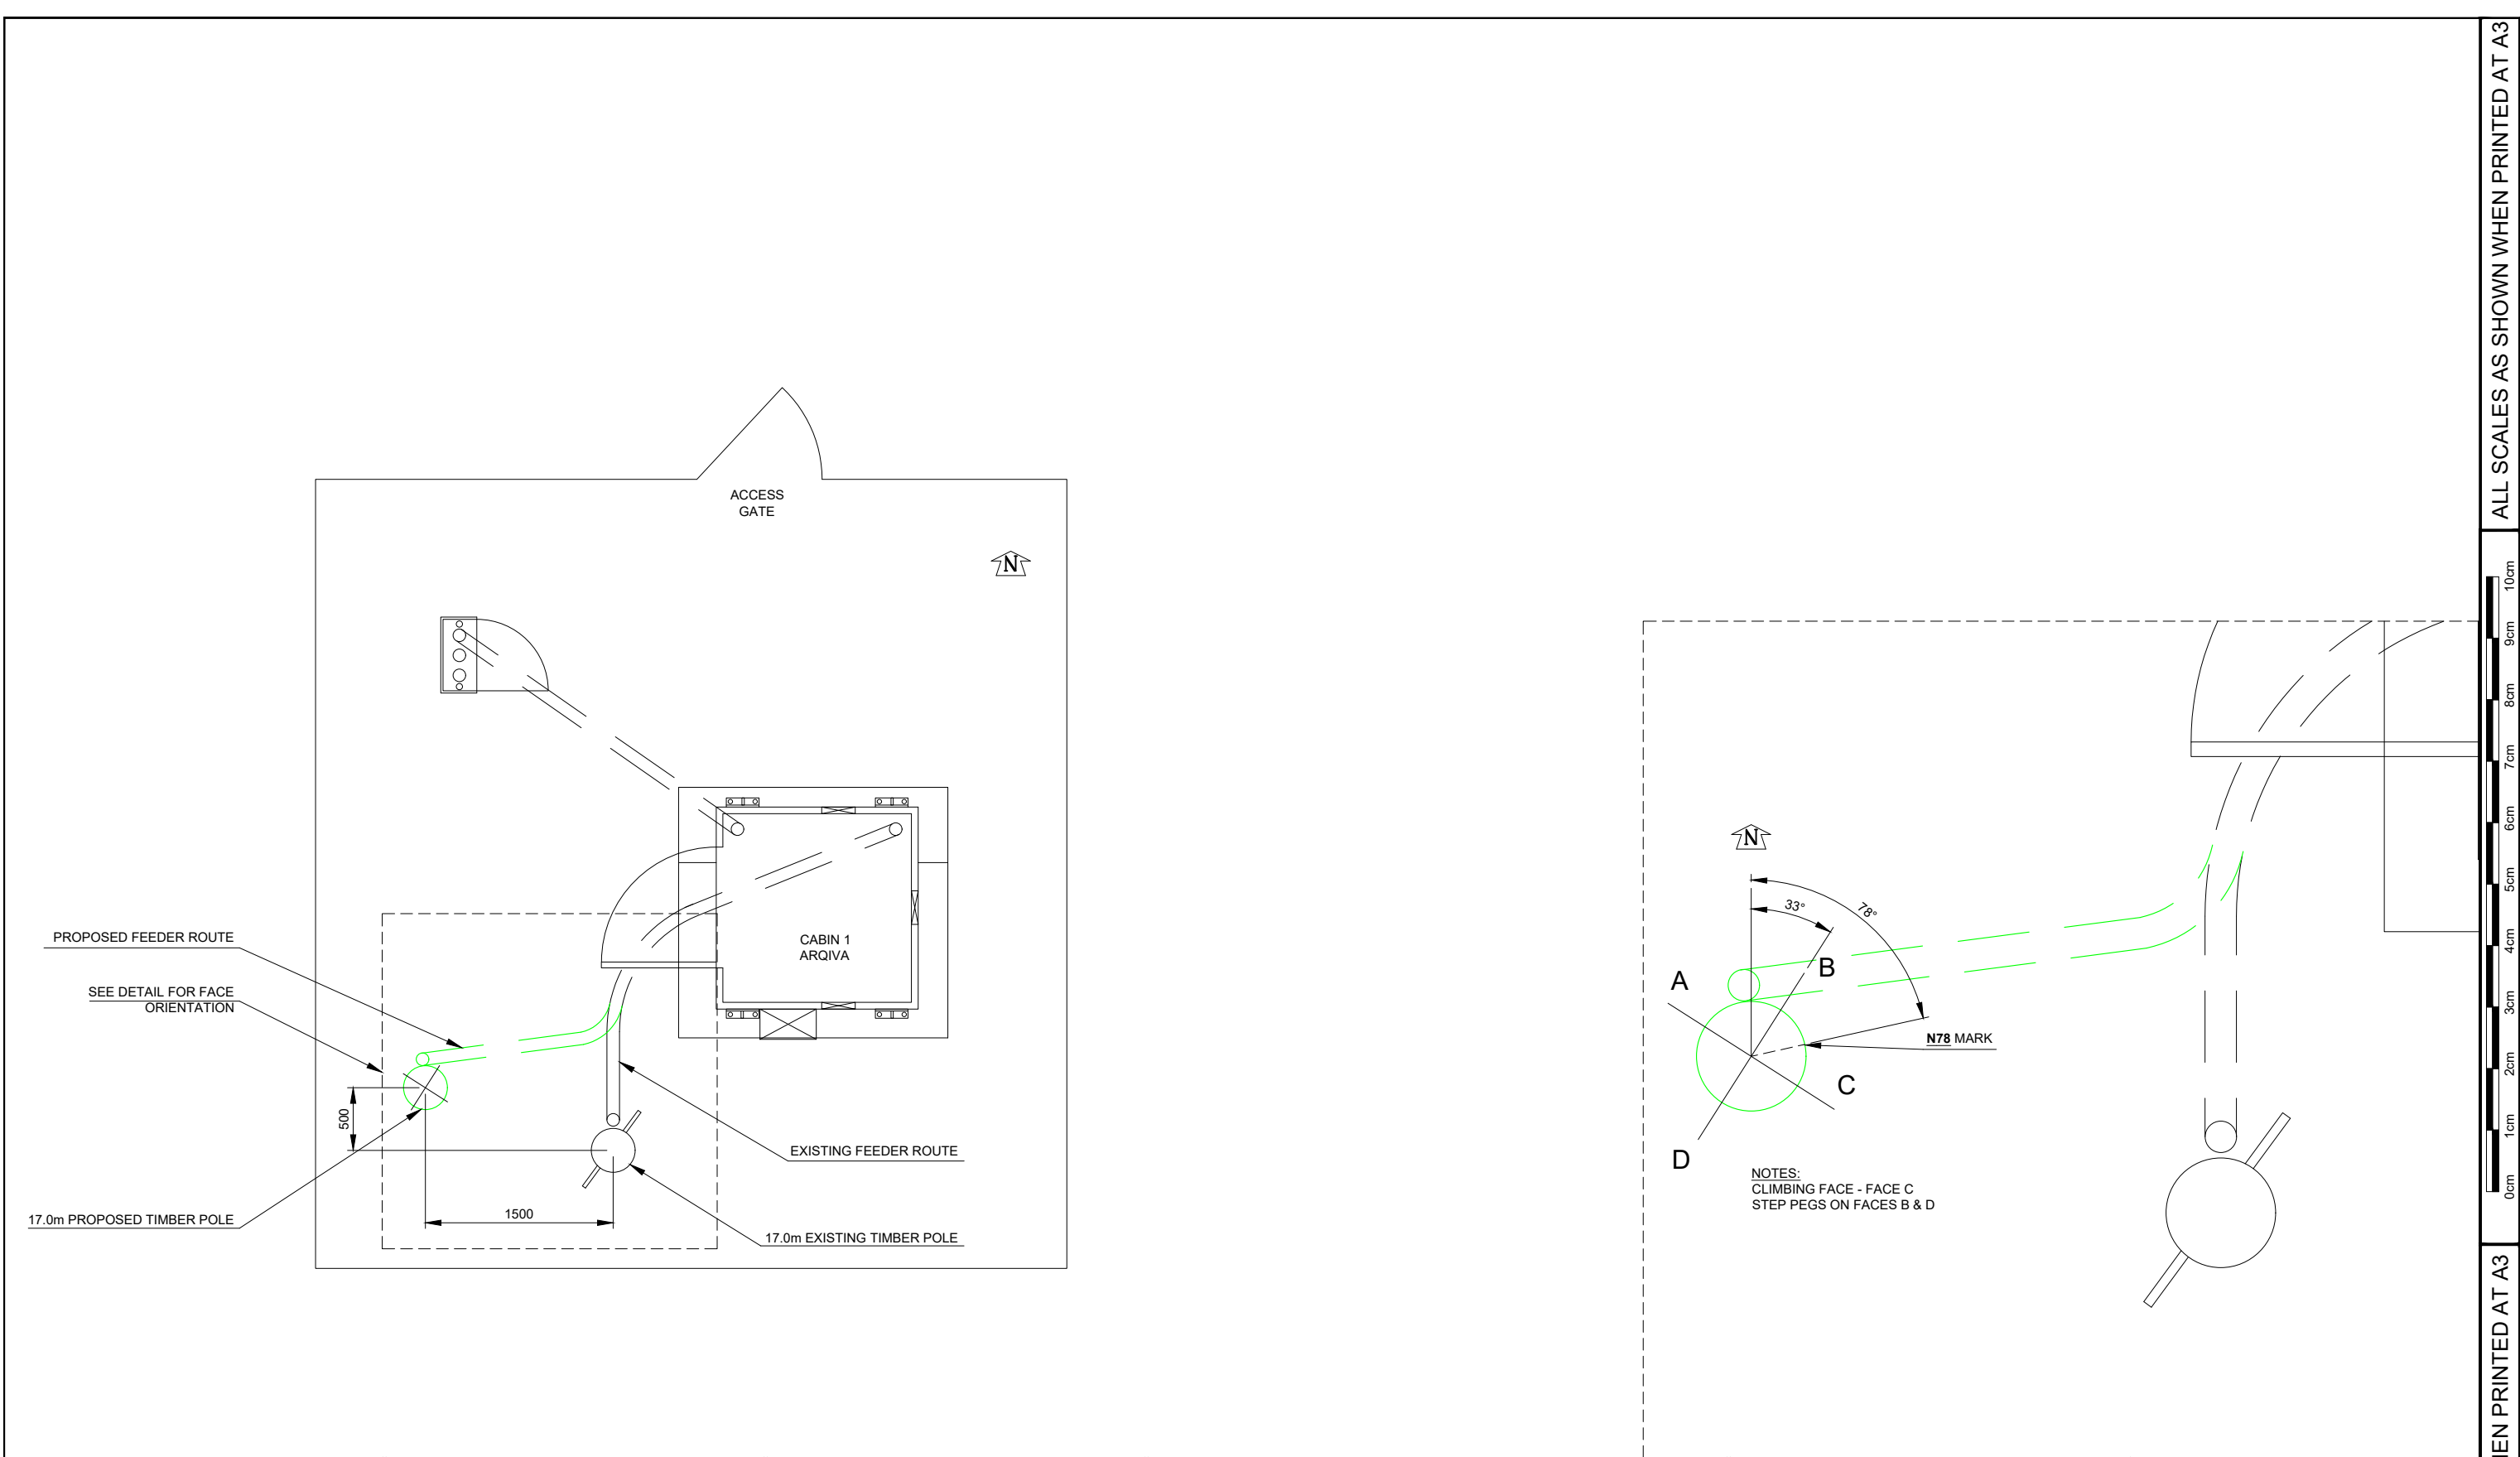

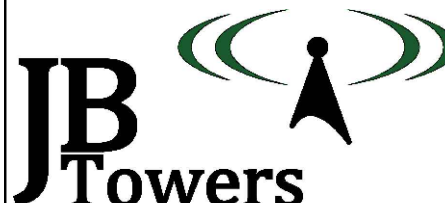

01	FIRST ISSUE	AM	19/11/18
REV	REV	BY	DATE
SCALE AS SHOWN WHEN PRINTED AT A3	DRAWN DATE 19/11/18	CHECKED DATE 19/11/18	MP DATE 19/11/18
APPROVED JBT DATE 19/11/18			
ALL DIMENSIONS IN mm UNLESS OTHERWISE STATED. THIS DRAWING TO BE READ IN CONJUNCTION WITH OTHER RELEVANT DRAWINGS.			

TITLE
SKIRMETT
SITE PLAN


SITE ADDRESS
VALENTINE FARM
SHOGMOOR LANE
SKIRMETT
HENLEY-ON-THAMES
RG9 6TD

ARQIVA REF.
141568

DRG No.
100

REV
01

ALL SCALES AS SHOWN WHEN PRINTED AT A3

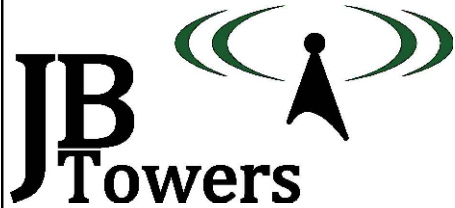

01	FIRST ISSUE			AM	19/11/18
REV	REV			BY	DATE
SCALE AS SHOWN		DRAWN	AM	CHECKED	MP
WHEN PRINTED AT A3		DATE	19/11/18	DATE	19/11/18
		DATE	19/11/18	DATE	19/11/18
ALL DIMENSIONS IN mm UNLESS OTHERWISE STATED. THIS DRAWING TO BE READ IN CONJUNCTION WITH OTHER RELEVANT DRAWINGS.					



TITLE

SKIRMETT

GENERAL ARRANGEMENT

SHEET 1 OF 3

SITE ADDRESS		
VALENTINE FARM SHOGMOOR LANE SKIRMETT HENLEY-ON-THAMES RG9 6TD		
ARQIVA REF. 141568	DRG No. 200	REV 01

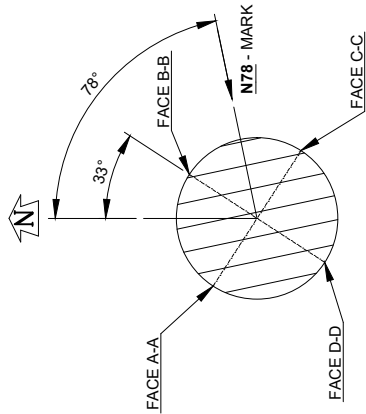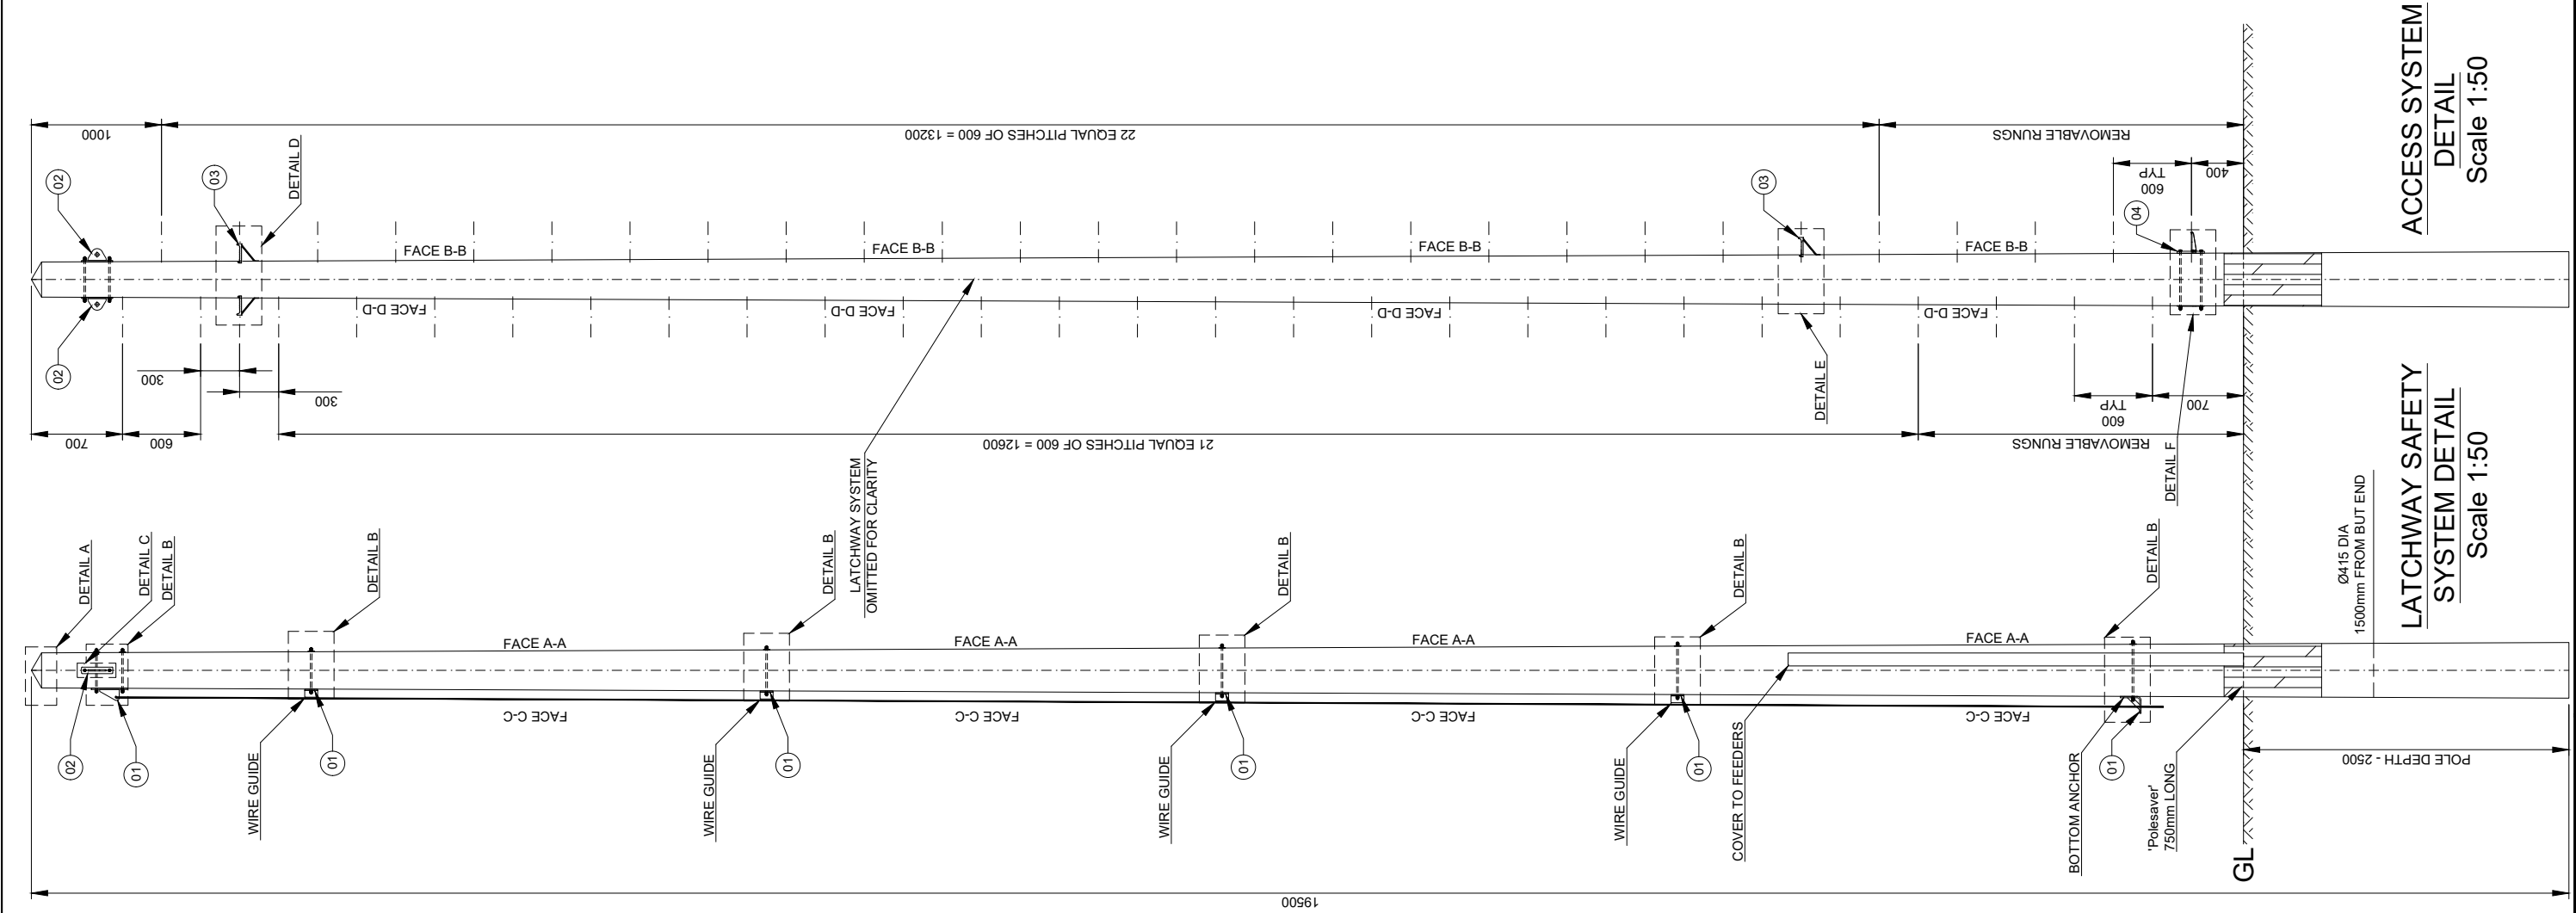

POLE ORIENTATION

NOTES

- SEE DRAWING 304 FOR PARTS LIST
- ALL BOLTS TO BE CUT ON SITE TO EXTEND MAX 10mm BEYOND THE NUT WHEN TIGHTENED UNO.
- ALL SITE DRILLED HOLE/CUT ENDS TO BE TREATED WITH METAFUX 70-40 ZINC PASTE FOLLOWED BY 1 COAT OF 7-42 ZINC ALU OR 70-16 ALUMINIUM SPRAY

TIMBER POLE


- POLE TO BE SUPPLIED IN ACCORDANCE WITH BS EN14229 & SHALL HAVE MIN. CHARACTERISTIC BENDING STRENGTH OF 30N/mm² & MIN. YOUNGS MODULUS (PARALLEL TO GRAIN) OF 10KN/mm².
- MARKINGS ON FINISHED POLE SHALL BE AT 4m FROM BUT AND COMPLY WITH BS EN 14229 UNO
- AS FAR AS PRACTICABLE ALL CUTTING, SCARFING & DRILLING TO BE DONE BEFORE CREOSOTING. IF NOT ALL CUT, DRILLED & SCARFED SURFACES TO BE COATED WITH A MIXTURE OF CREOSOTE & TAR.
- POLE TO BE PRESSURE IMPREGNATED WITH CREOSOTE IN ACCORDANCE WITH BS EN 14229
- MINIMUM DIAMETERS
TOP - Ø206mm
BOTTOM - Ø425mm
- 19.5m LONG POLE TO BE SOURCED BY TRIMMING 20m LONG POLE BY 0.5m AT THE TOP


PLANTING

- CAT SCANNER IS TO BE USED IN ORDER TO CONFIRM THE POSITIONS OF BURIED SERVICES.
- 'Perma-Soil Stabiliser' OR A SIMILAR APPROVED SHOULD BE USED IN ACCORDANCE WITH THE MANUFACTURER'S RECOMMENDATION.
- ANY MATERIAL USED FOR BACK-FILLING IS TO BE OF EQUAL OR BETTER QUALITY THAN THE EXCAVATED MATERIAL.
- ALL BACK-FILLING MATERIAL IS TO BE PLACED AND COMPACTED IN 150mm THICK LAYERS.
- TIMBER POLE TO BE PLANTED WITH N78 MARKING AT 4m FROM BUT FACING 78° FROM NORTH (CLOCKWISE)

ACCESS SYSTEM
DETAIL
Scale 1:50


LATCHWAY SAFETY
SYSTEM DETAIL
Scale 1:50

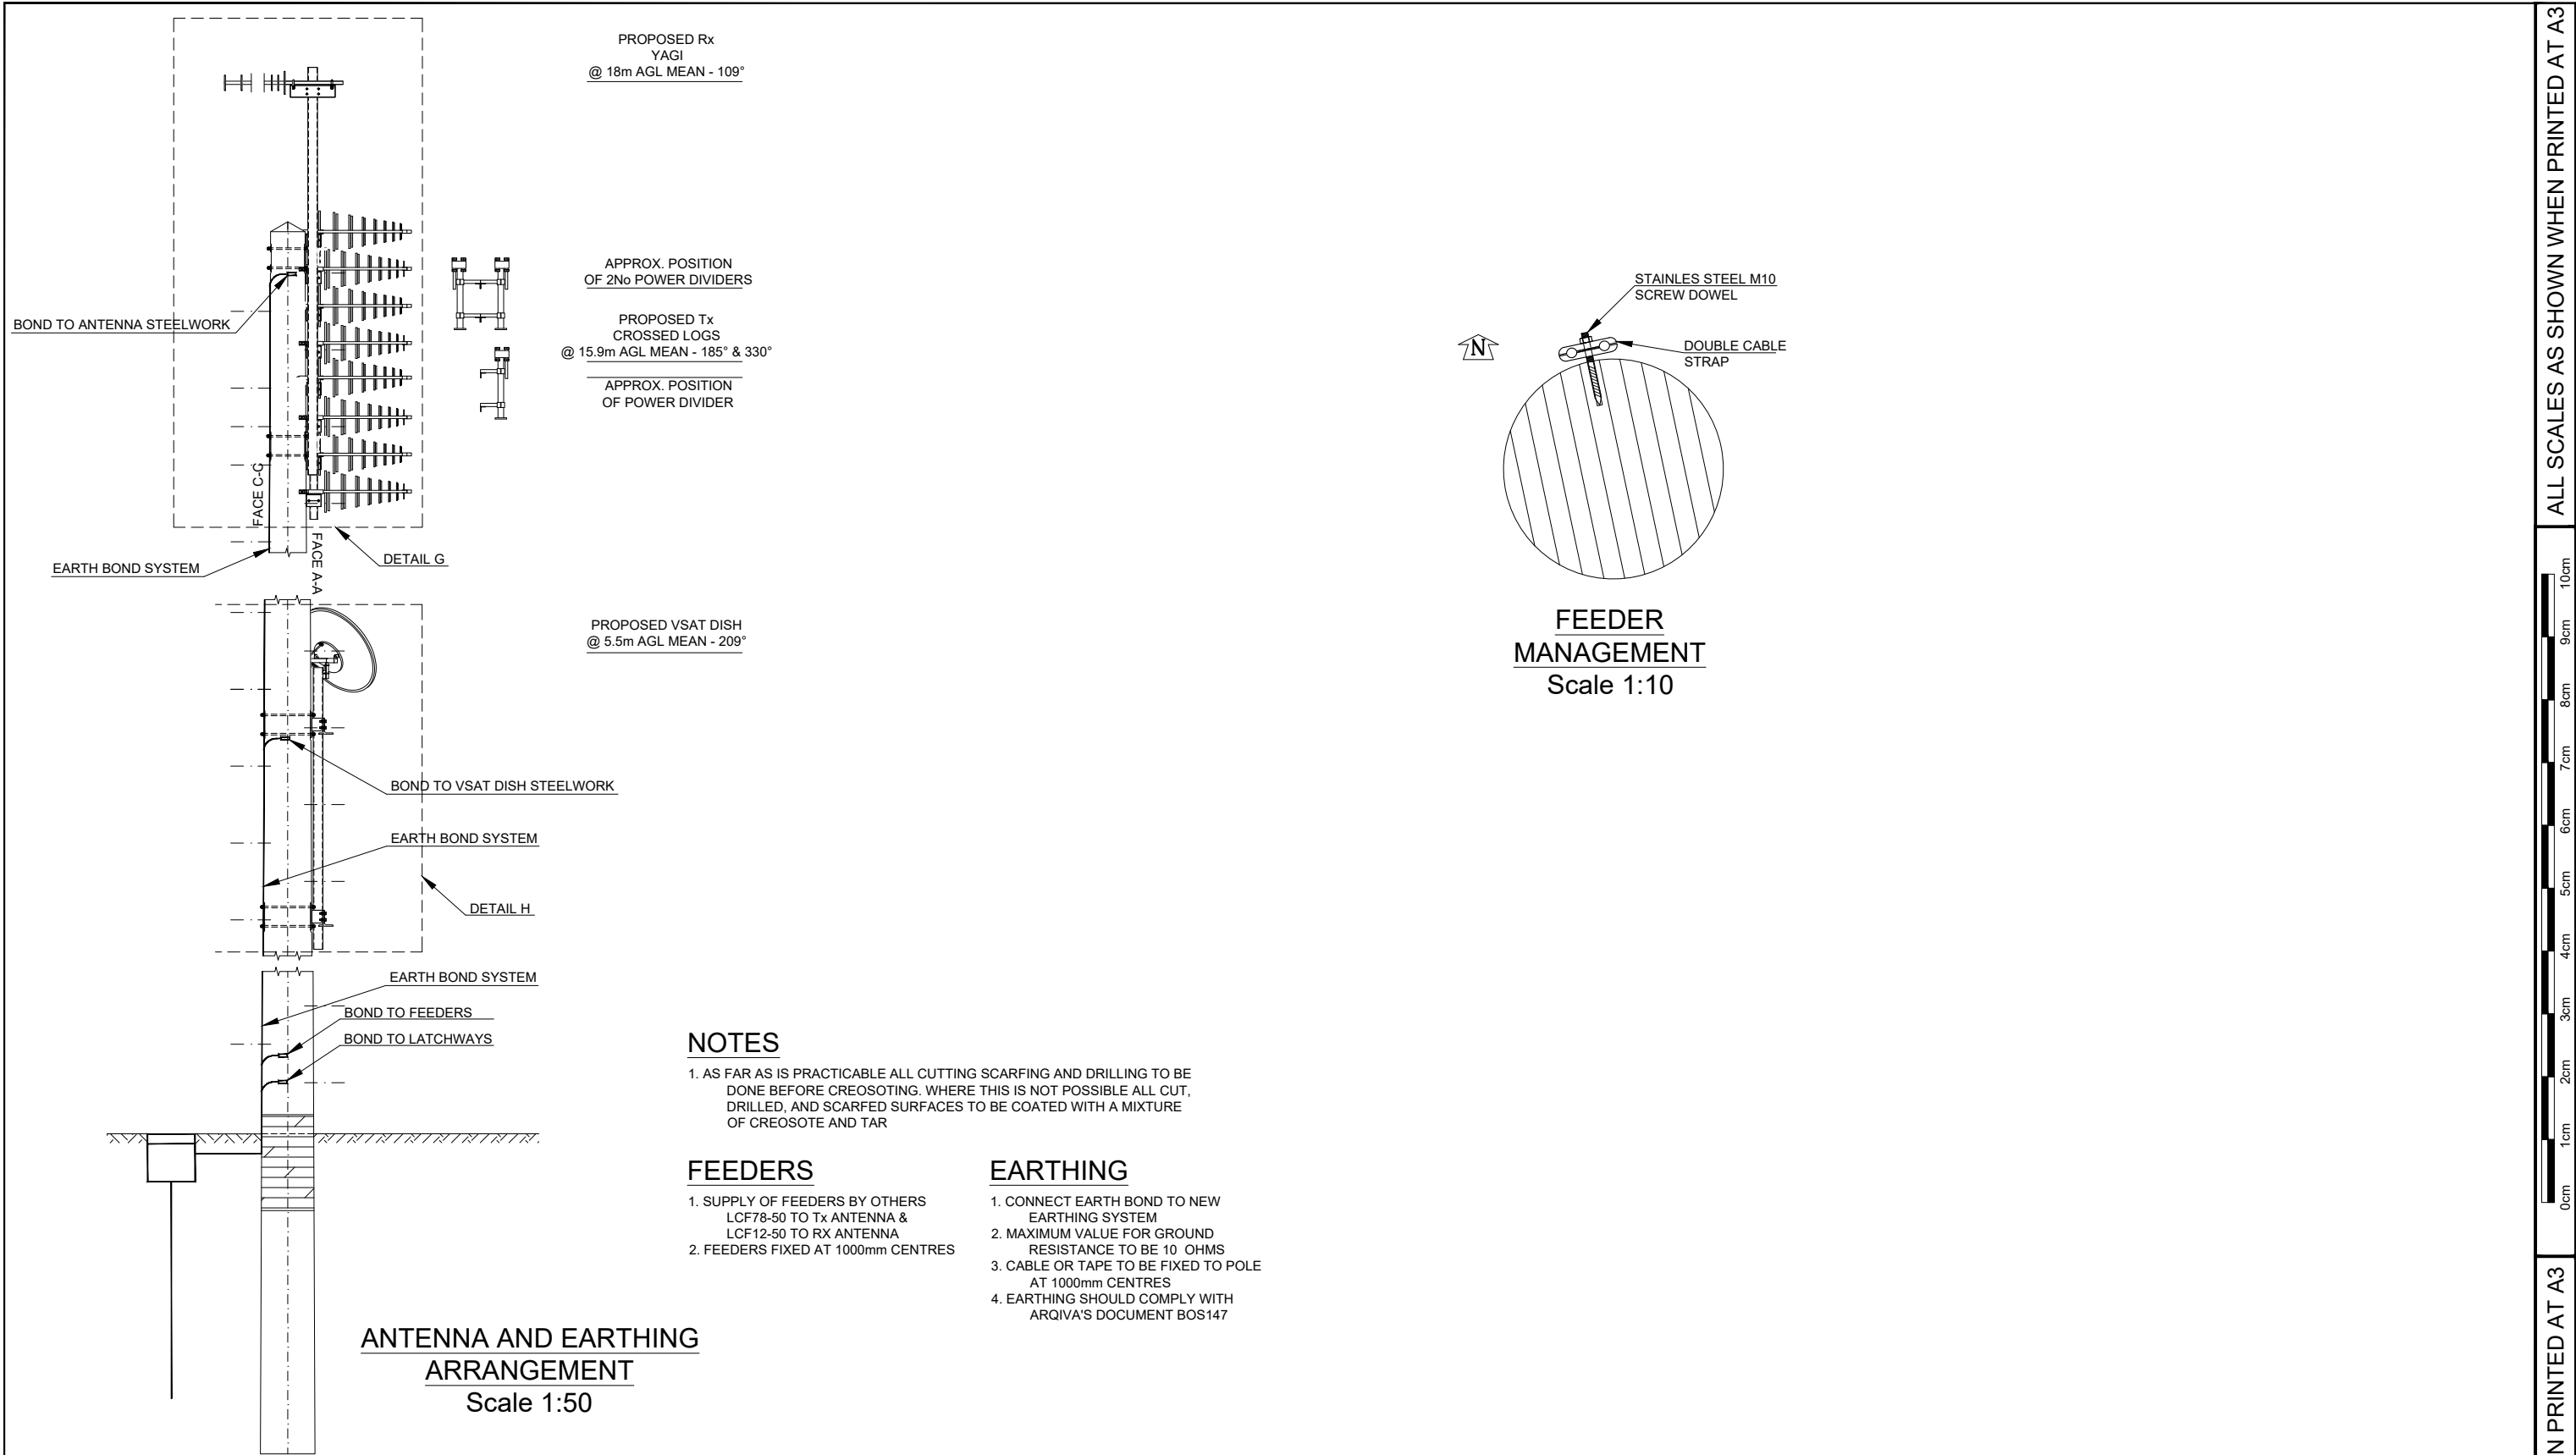

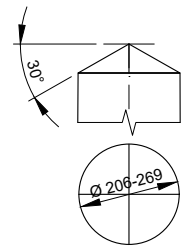


- NOTES:
1. A SINGLE COAT OF TIMBER COMPATIBLE BITUMINOUS PAINT (E.G. BIRD BRAND BLACK BITUMINOUS PAINT OR SIMILAR APPROVED PRODUCT) TO BE APPLIED TO THE UPPER SURFACES AT THE TOP OF THE POLE.
 2. PAINT TO BE APPLIED ON SITE JUST BEFORE ERECTION
- FORM: 4 WAY PYRAMID / CONE


DETAIL A - TIMBER POLE TOP
Scale 1:20

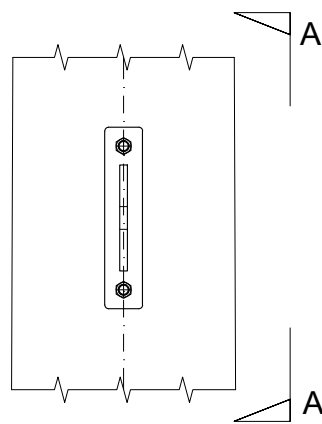


DETAIL C - FALL ARREST
ATTACHMENT POINT
Scale 1:10

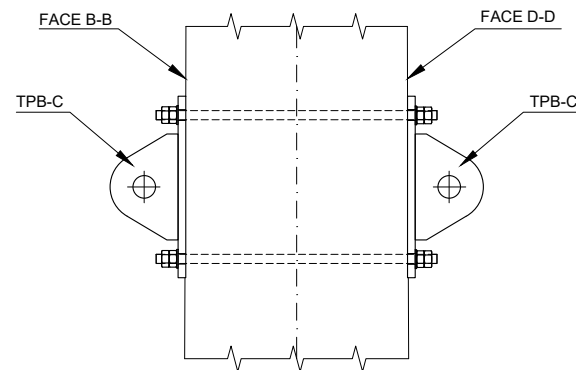

VIEW A-A
Scale 1:10

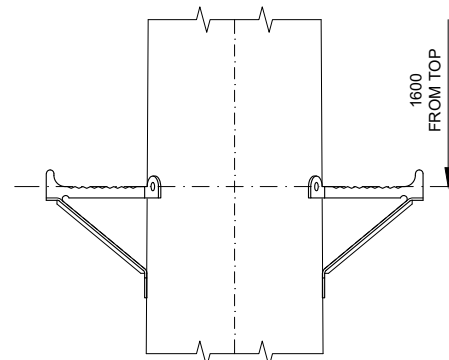


DETAIL D - ANTENNA
ACCESS CLIMBING STEP
Scale 1:10

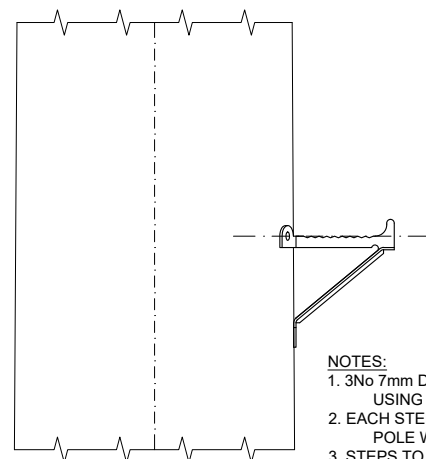


DETAIL E - PERMANENT
CLIMBING STEPS
Scale 1:10


- NOTES:
1. 3No 7mm DIA 70mm LONG PILOT HOLES TO BE DRILLED USING THE STEP AS A TEMPLATE
 2. EACH STEP SHOULD BE FIXED TO THE TIMBER POLE WITH 3No 10mm COACH SCREWS 75mm LONG
 3. STEPS TO BE INSTALLED ON FACES B-B & D-D ONLY

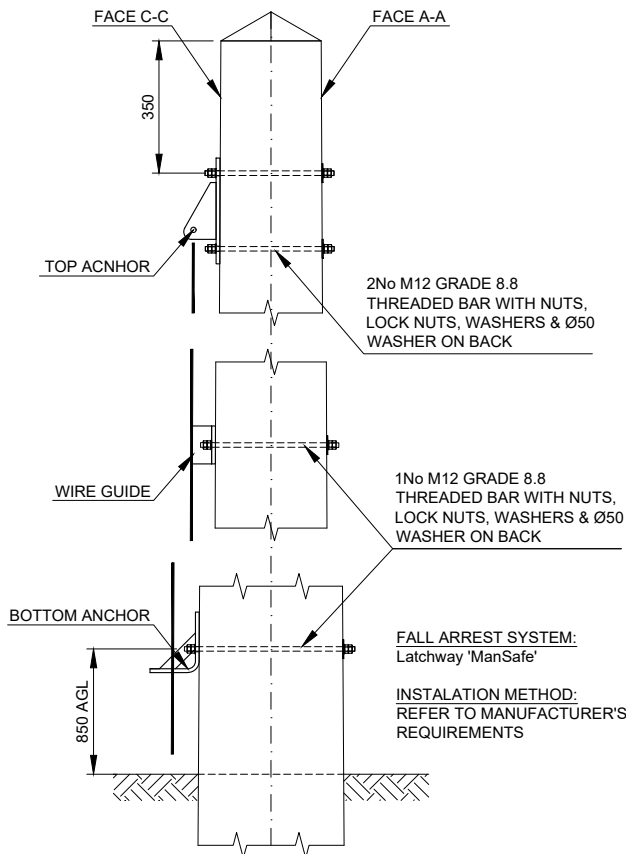

DETAIL B - FALL ARREST SYSTEM
Scale 1:20

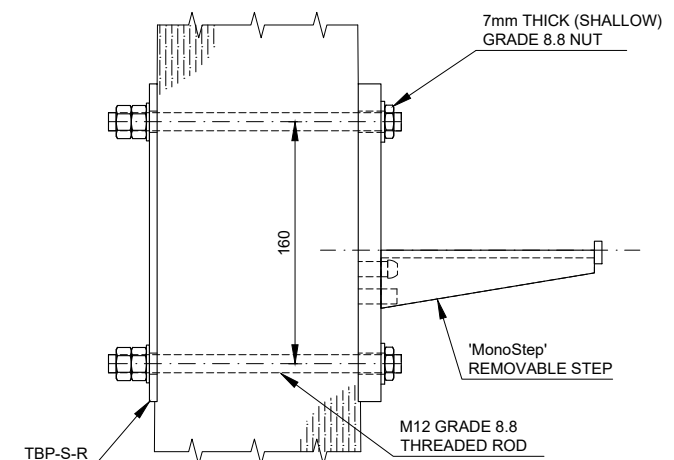

DETAIL F - REMOVABLE
CLIMBING STEPS
Scale 1:5

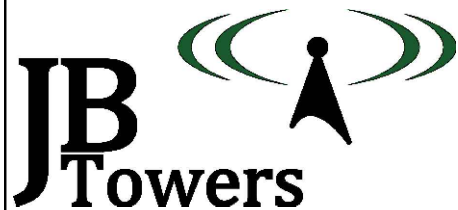


01	FIRST ISSUE	AM	19/11/18
REV	REV	BY	DATE
SCALE AS SHOWN WHEN PRINTED AT A3	DRAWN DATE 19/11/18	CHECKED DATE 19/11/18	APPROVED DATE 19/11/18
ALL DIMENSIONS IN mm UNLESS OTHERWISE STATED. THIS DRAWING TO BE READ IN CONJUNCTION WITH OTHER RELEVANT DRAWINGS.			

TITLE		SITE ADDRESS	
SKIRMETT		VALENTINE FARM SHOGMOOR LANE SKIRMETT HENLEY-ON-THAMES RG9 6TD	
GENERAL ARRANGEMENT SHEET 3 OF 3		ARQIVA REF. 141568	DRG No. 200 REV 01

ALL SCALES AS SHOWN WHEN PRINTED AT A3



ALL SCALES AS SHOWN WHEN PRINTED AT A3

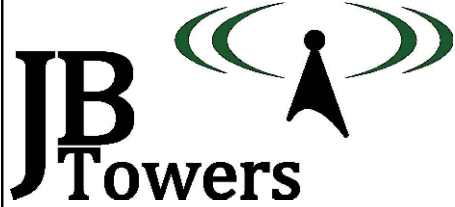

01	FIRST ISSUE			AM	19/11/18
REV	REV			BY	DATE
SCALE AS SHOWN		DRAWN	AM	CHECKED	MP
WHEN PRINTED AT A3		DATE	19/11/18	DATE	19/11/18
		APPROVED	JBT	DATE	19/11/18
ALL DIMENSIONS IN mm UNLESS OTHERWISE STATED. THIS DRAWING TO BE READ IN CONJUNCTION WITH OTHER RELEVANT DRAWINGS.					


TITLE
SKIRMETT
TIMBER POLE HOLE SET OUT
SHEET 1 OF 2

SITE ADDRESS
VALENTINE FARM
SHOGMOOR LANE
SKIRMETT
HENLEY-ON-THAMES
RG9 6TD

ARQIVA REF.
141568

DRG No.
201


REV
01

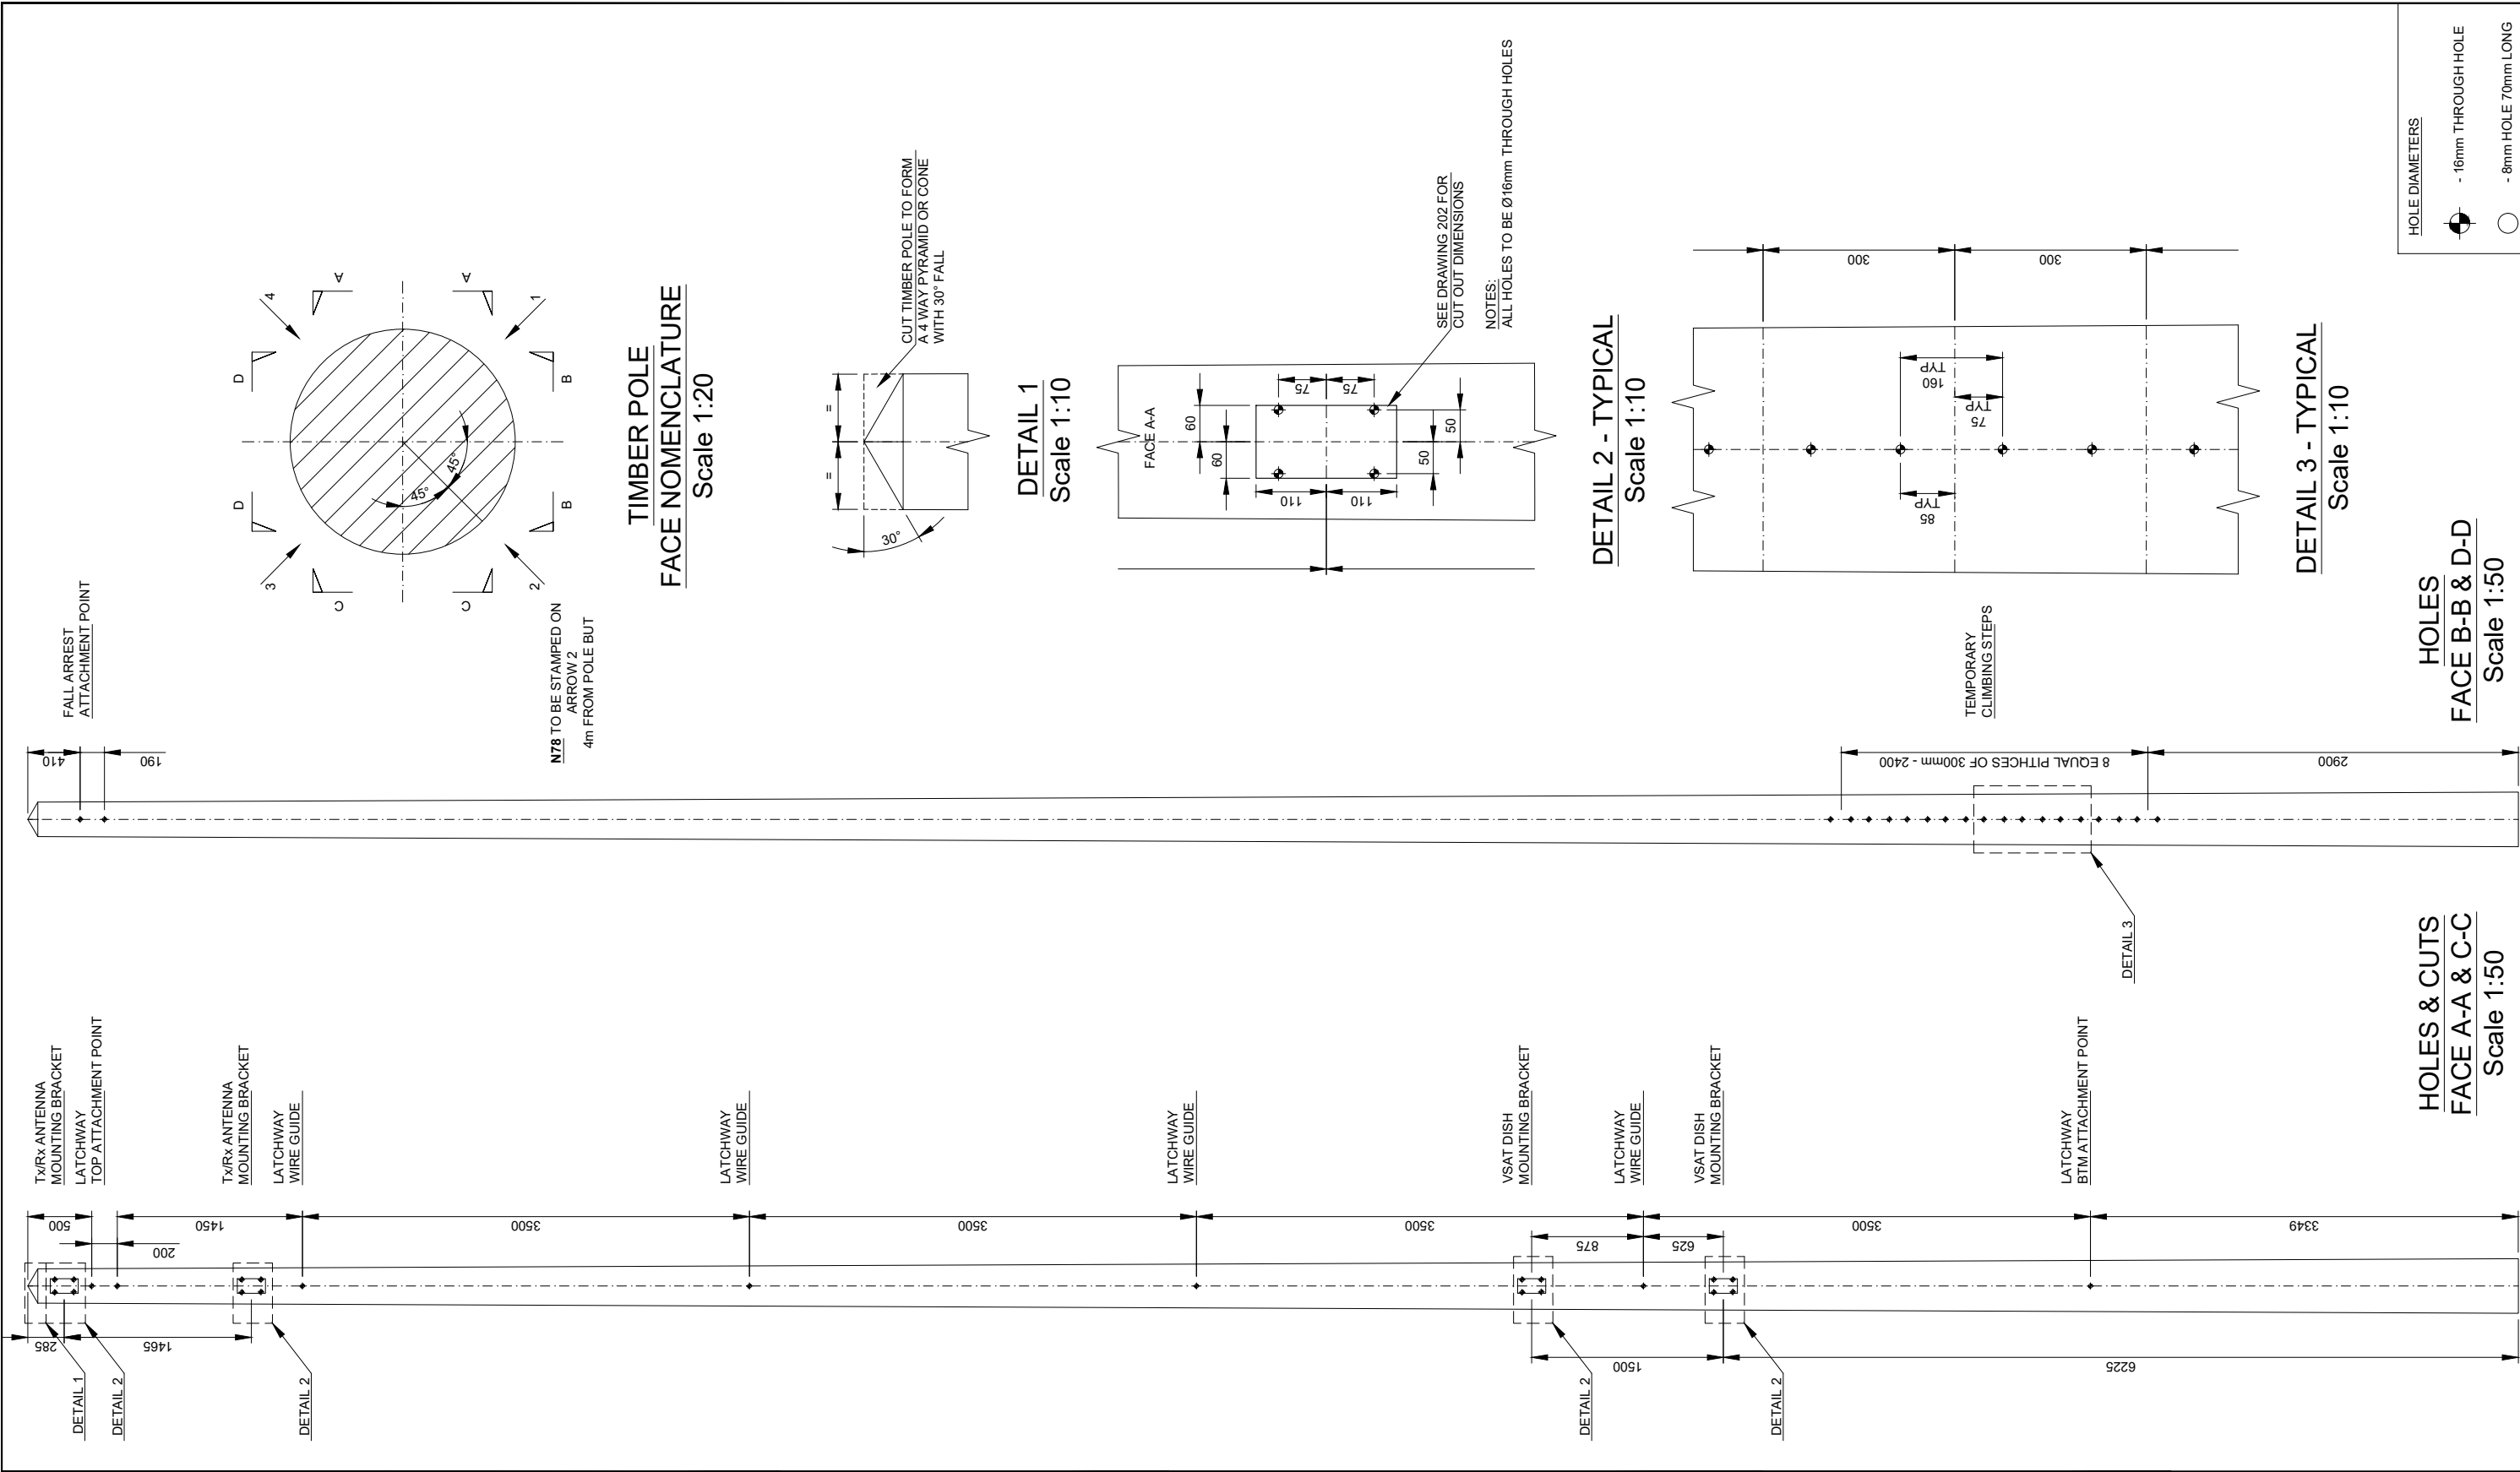

ALL SCALES AS SHOWN WHEN PRINTED AT A3





ALL SCALES AS SHOWN WHEN PRINTED AT A3

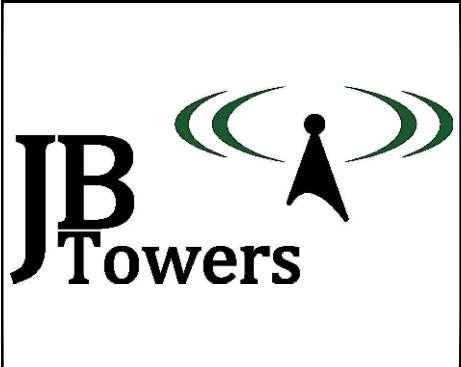


01	FIRST ISSUE			AM	19/11/18
REV	REV			BY	DATE
SCALE AS SHOWN		DRAWN	AM	CHECKED	MP
WHEN PRINTED AT A3		DATE	19/11/18	DATE	19/11/18
		DATE	19/11/18	DATE	19/11/18
ALL DIMENSIONS IN mm UNLESS OTHERWISE STATED. THIS DRAWING TO BE READ IN CONJUNCTION WITH OTHER RELEVANT DRAWINGS.					

TITLE
SKIRMETT
TIMBER POLE HOLE SET OUT
SHEET 2 OF 2

SITE ADDRESS		
VALENTINE FARM		
SHOGMOOR LANE		
SKIRMETT		
HENLEY-ON-THAMES		
RG9 6TD		
ARQIVA REF.	DRG No.	REV
141568	201	01

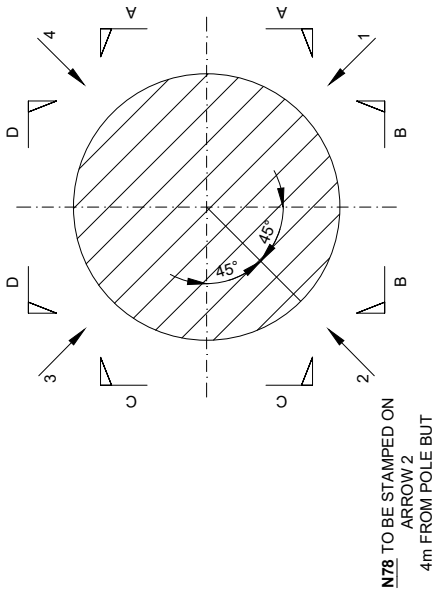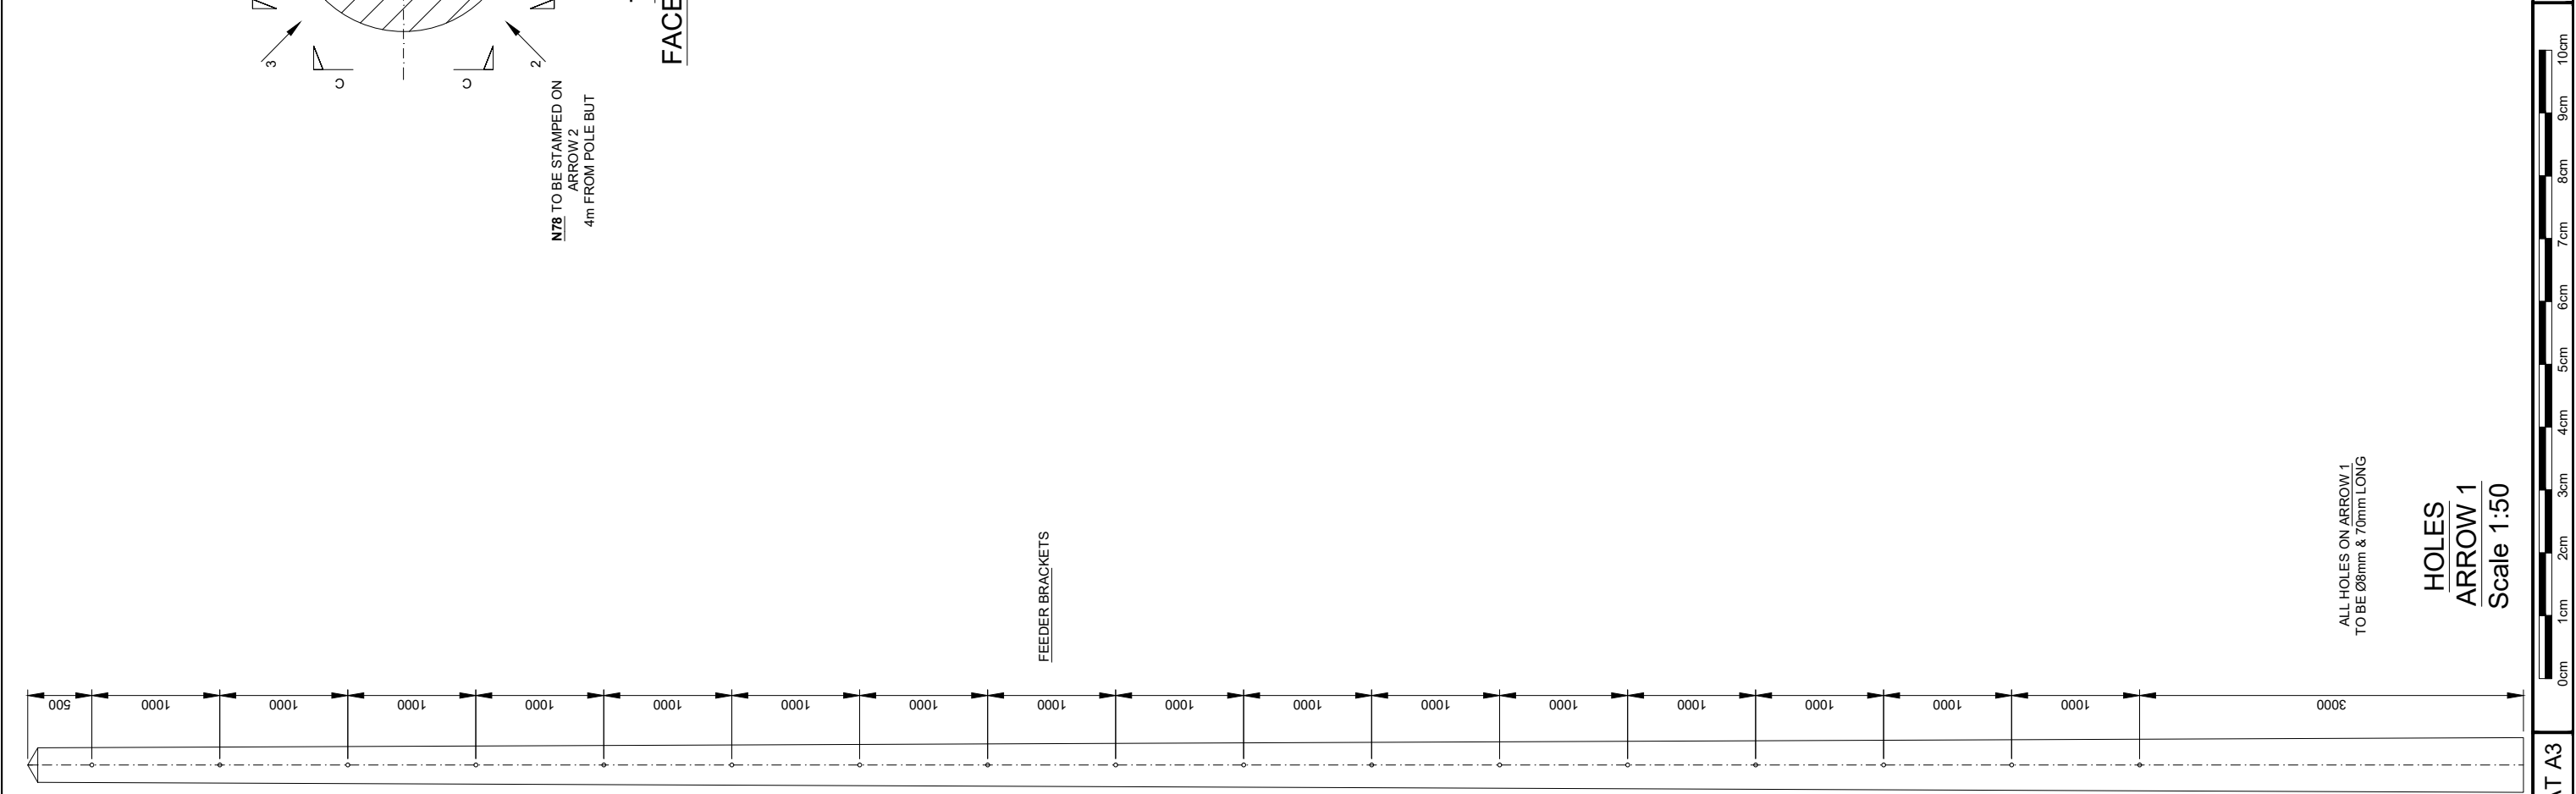


TIMBER POLE
FACE NOMENCLATURE
Scale 1:20

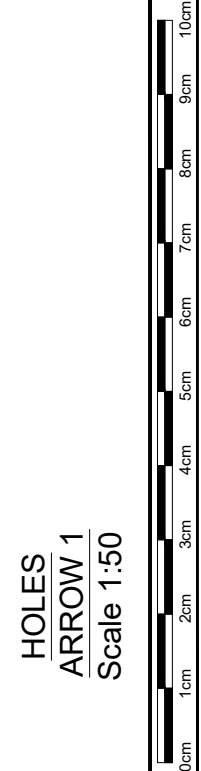

HOLE DIAMETERS
- 16mm THROUGH HOLE
- 8mm HOLE 70mm LONG

ALL SCALES AS SHOWN WHEN PRINTED AT A3

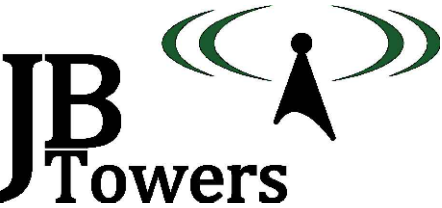

01	FIRST ISSUE			AM	19/11/18
REV	REV			BY	DATE
SCALE AS SHOWN		DRAWN	AM	CHECKED	MP
WHEN PRINTED AT A3		DATE	19/11/18	DATE	19/11/18
		APPROVED	JBT	DATE	19/11/18
ALL DIMENSIONS IN mm UNLESS OTHERWISE STATED. THIS DRAWING TO BE READ IN CONJUNCTION WITH OTHER RELEVANT DRAWINGS.					

TITLE

SKIRMETT

TIMBER POLE CUT OUT
DETAIL


SITE ADDRESS

VALENTINE FARM
SHOGMOOR LANE
SKIRMETT
HENLEY-ON-THAMES
RG9 6TD

ARQIVA REF.
141568


DRG No.
202

REV
01

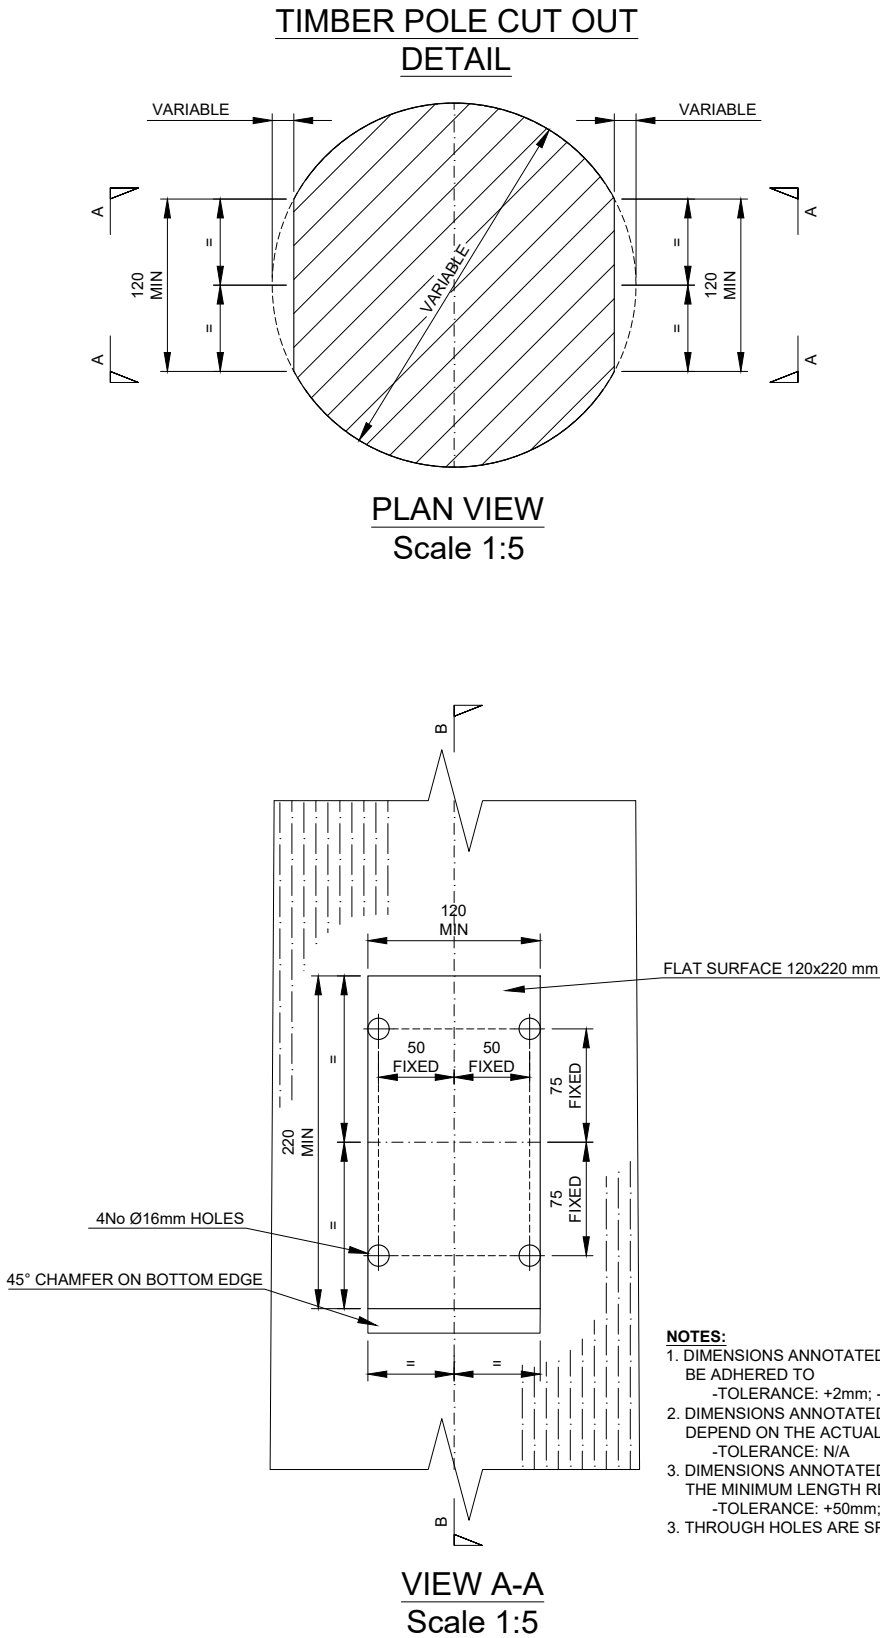


ALL SCALES AS SHOWN WHEN PRINTED AT A3


ALL SCALES AS SHOWN WHEN PRINTED AT A3

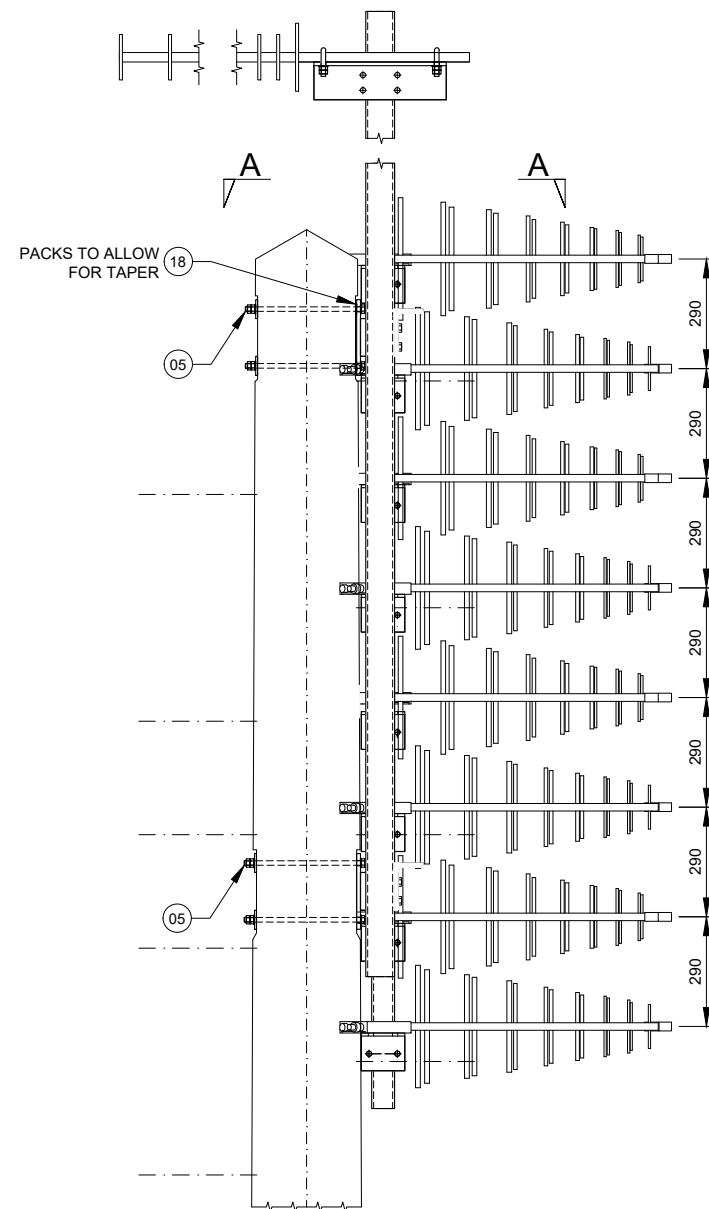


DETAIL G - Rx & Tx ANTENNA MOUNTS
Scale 1:20

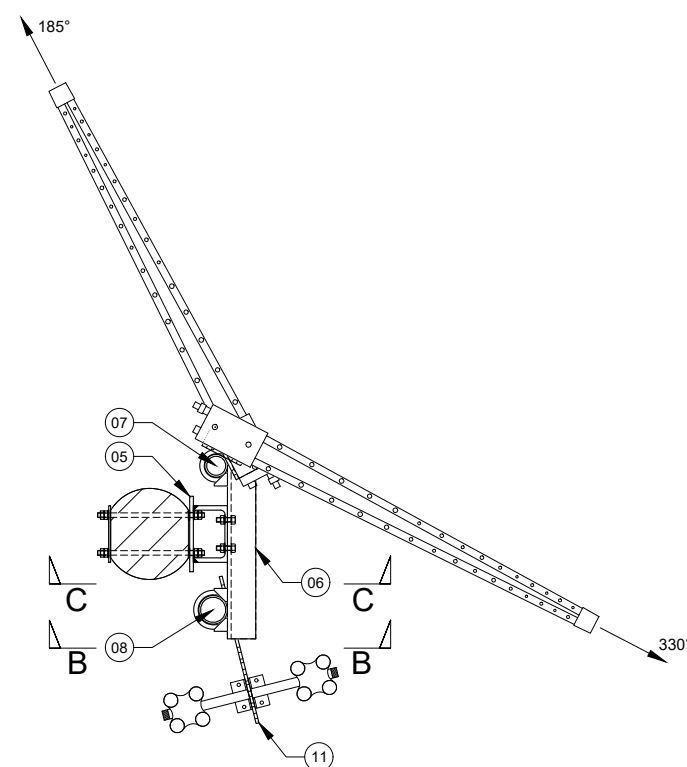

SECTION A-A
Scale 1:20

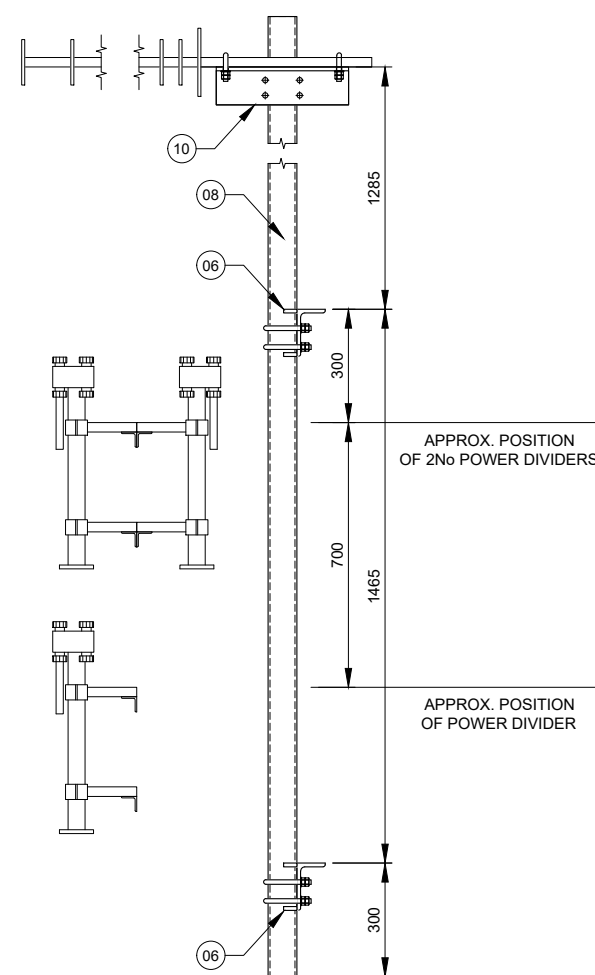

VIEW B-B
Scale 1:20

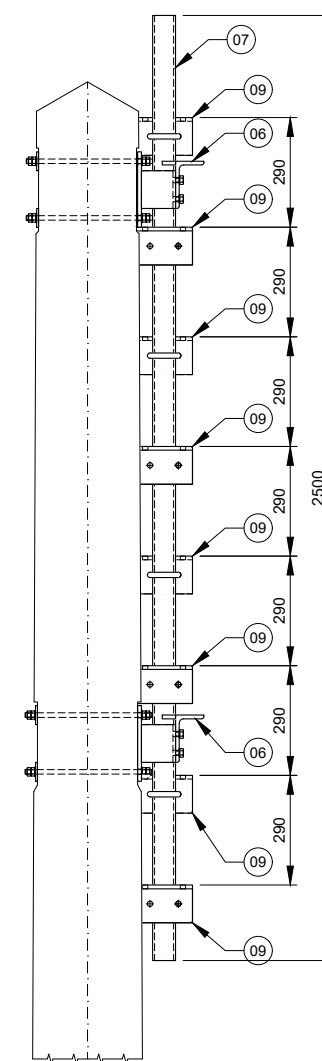


SECTION C-C
Scale 1:20



ALL SCALES AS SHOWN WHEN PRINTED AT A3

ALL SCALES AS SHOWN WHEN PRINTED AT A3

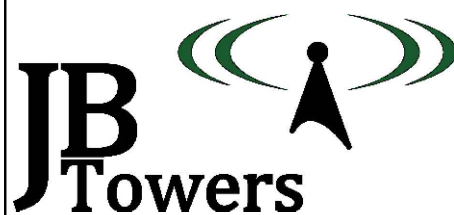

01	FIRST ISSUE	AM	19/11/18
REV	REV	BY	DATE
SCALE AS SHOWN WHEN PRINTED AT A3	DRAWN DATE 19/11/18	CHECKED DATE 19/11/18	APPROVED DATE 19/11/18
ALL DIMENSIONS IN mm UNLESS OTHERWISE STATED. THIS DRAWING TO BE READ IN CONJUNCTION WITH OTHER RELEVANT DRAWINGS.			


TITLE
ANTENNA MOUNT
DETAIL G

SITE ADDRESS
VALENTINE FARM
SHOGMOOR LANE
SKIRMETT
HENLEY-ON-THAMES
RG9 6TD

ARQIVA REF.
141568

DRG No.
203

REV
01

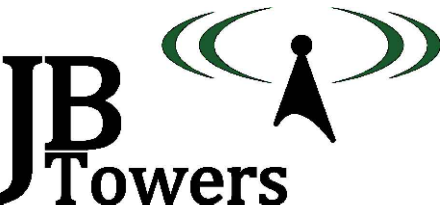

01	FIRST ISSUE			AM	19/11/18
REV	REV			BY	DATE
SCALE AS SHOWN		DRAWN	AM	CHECKED	MP
WHEN PRINTED AT A3		DATE	19/11/18	DATE	19/11/18
				APPROVED	JBT
				DATE	19/11/18
ALL DIMENSIONS IN mm UNLESS OTHERWISE STATED. THIS DRAWING TO BE READ IN CONJUNCTION WITH OTHER RELEVANT DRAWINGS.					


TITLE
ANTENNA MOUNT
DETAIL H

SITE ADDRESS
VALENTINE FARM
SHOGMOOR LANE
SKIRMETT
HENLEY-ON-THAMES
RG9 6TD


ARQIVA REF.
141568

DRG No.
204

REV
01

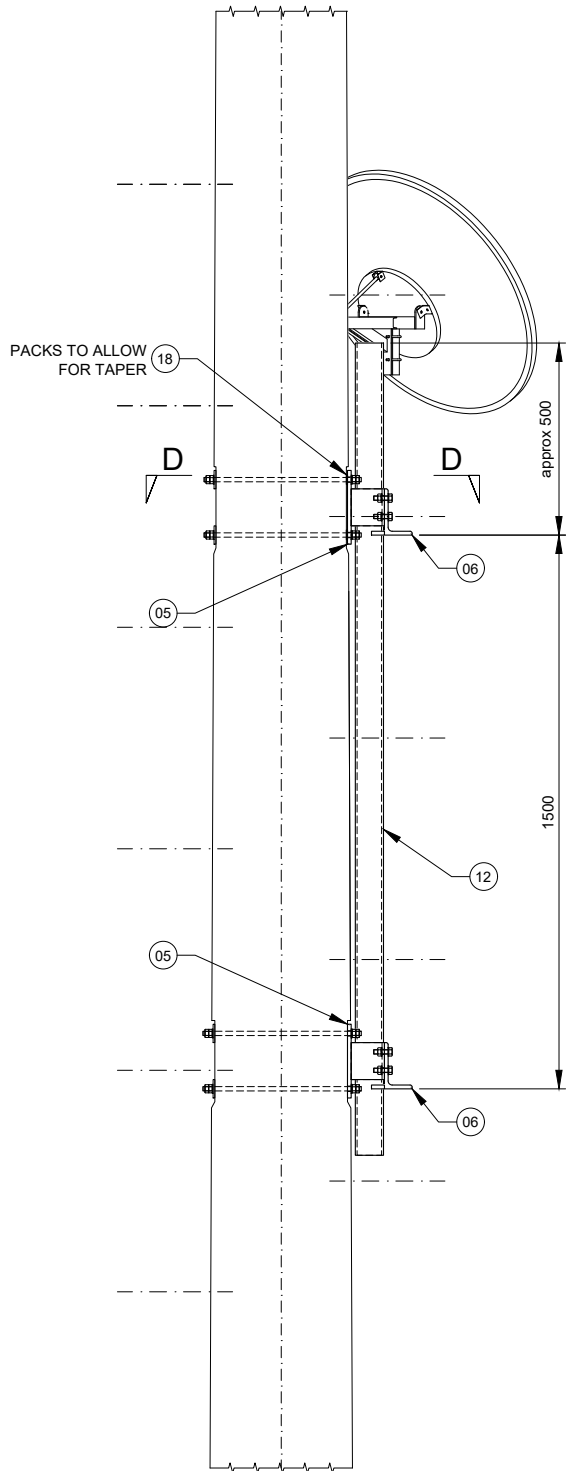

DETAIL H - VSAT DISH MOUNT
Scale 1:20

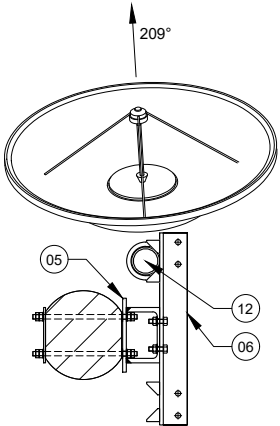


SECTION D-D
Scale 1:20




ALL SCALES AS SHOWN WHEN PRINTED AT A3

ALL SCALES AS SHOWN WHEN PRINTED AT A3

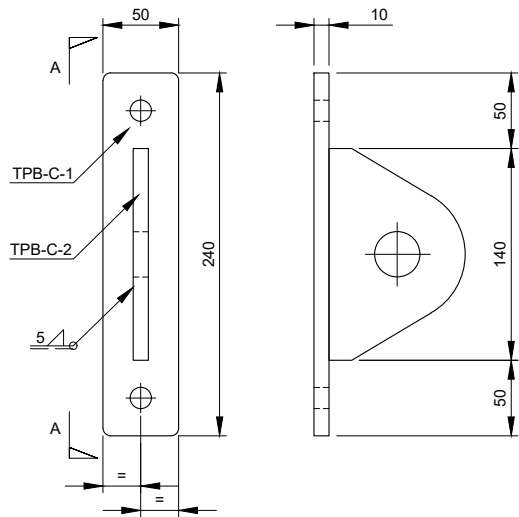

PART TPB-C
Scale 1:5

VIEW A-A
Scale 1:5

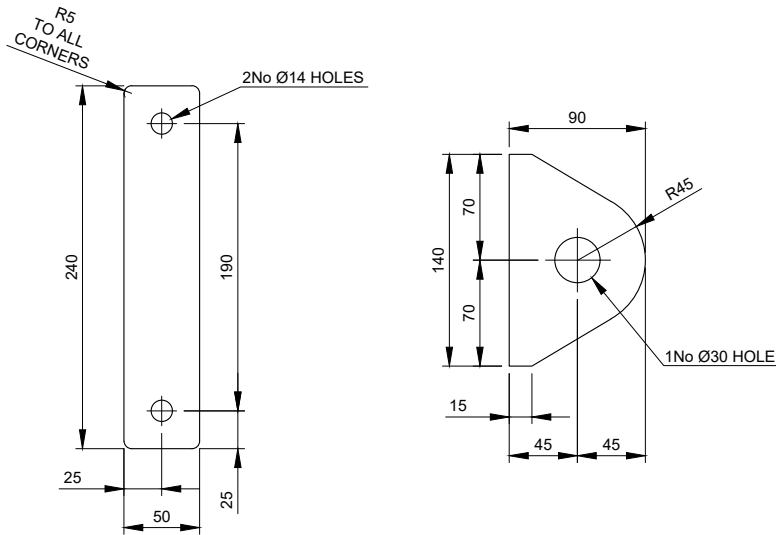


TPB-C-1 - 10mm THICK
Scale 1:5

TPB-C-2 - 10mm THICK
Scale 1:5

Parts list for TPB-C


Item	Part	Quantity	Part description	Length	Material	Weight
01	TPB-C-1	1	240x50x10mm	N/A	S275J0	0.94 kg
02	TPB-C-2	1	140x90x10mm	N/A	S275J0	0.99 kg
03	STUDS	1	M12 STUDDING	350mm	GRADE 8.8	0.31 kg
Total Weight:						2.24 kg

- All steel hot dip galvanized
- Each STUD to be supplied with 4 Full Nuts, 2 Flat Washers and 2 Spring Washers
- For fabrication notes see drawing 304

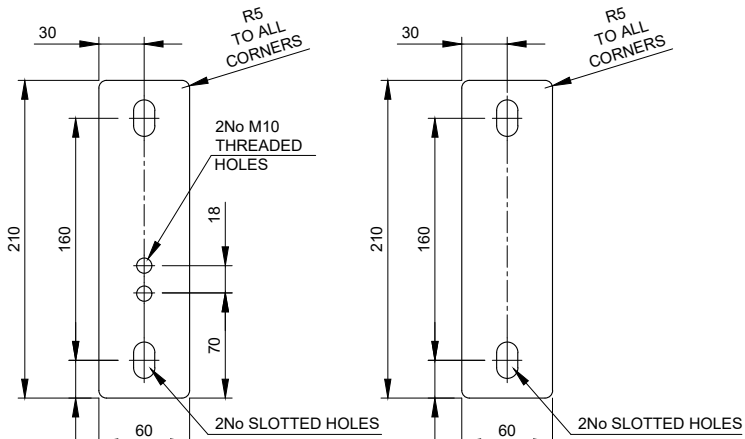

PART TPS-R-1
Scale 1:5

PART TPS-R-2
Scale 1:5

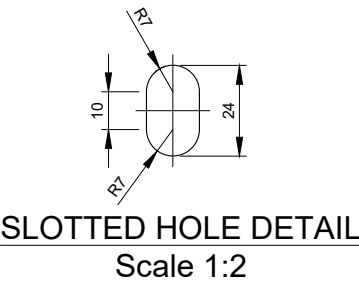


SLOTTED HOLE DETAIL
Scale 1:2

Parts list for TPS-R

Item	Part	Quantity	Part description	Length	Material	Weight
01	TPS-R-1	1	210x60x15mm	N/A	S275J0	1.48 kg
02	TPS-R-2	1	210x60x5mm	N/A	S275J0	0.49 kg
03	STUDS	2	M12 STUDDING	500mm	GRADE 8.8	0.44 kg
04	NUT-S	2	M12 SHALLOW NUT	N/A	GRADE 8.8	-
05	NUT	4	M12 NUT	N/A	GRADE 8.8	-
06	WSH	4	M12 WASHER	N/A	GRADE 8.8	-
Total Weight:						2.85 kg

- All steel hot dip galvanized
- For fabrication notes see drawing 304

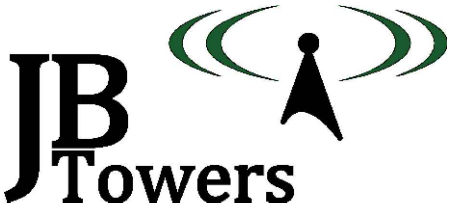

01	FIRST ISSUE	AM	19/11/18
REV	REV	BY	DATE
SCALE AS SHOWN WHEN PRINTED AT A3	DRAWN DATE 19/11/18	CHECKED DATE 19/11/18	APPROVED DATE 19/11/18
ALL DIMENSIONS IN mm UNLESS OTHERWISE STATED. THIS DRAWING TO BE READ IN CONJUNCTION WITH OTHER RELEVANT DRAWINGS.			

TITLE
ATTACHMENT POINT &
TEMPORARY STEP DETAILS
PARTS: TPB-C; TPS-R

SITE ADDRESS
VALENTINE FARM
SHOGMOOR LANE
SKIRMETT
HENLEY-ON-THAMES
RG9 6TD

ARQIVA REF.
141568







DRG No.
300

REV
01

ALL SCALES AS SHOWN WHEN PRINTED AT A3





ALL SCALES AS SHOWN WHEN PRINTED AT A3

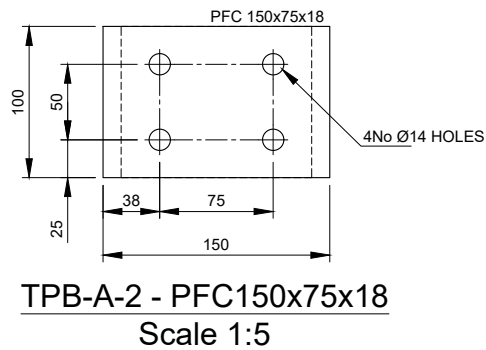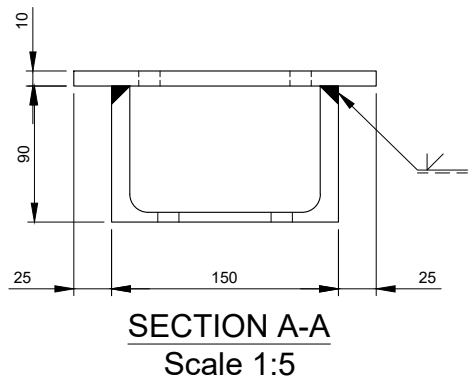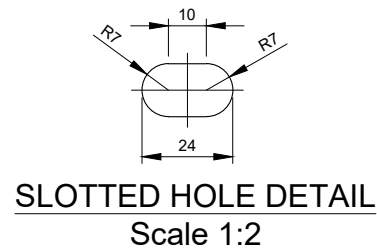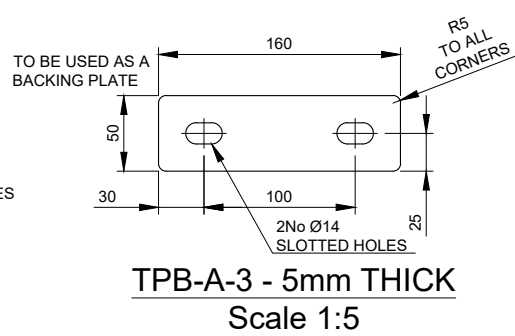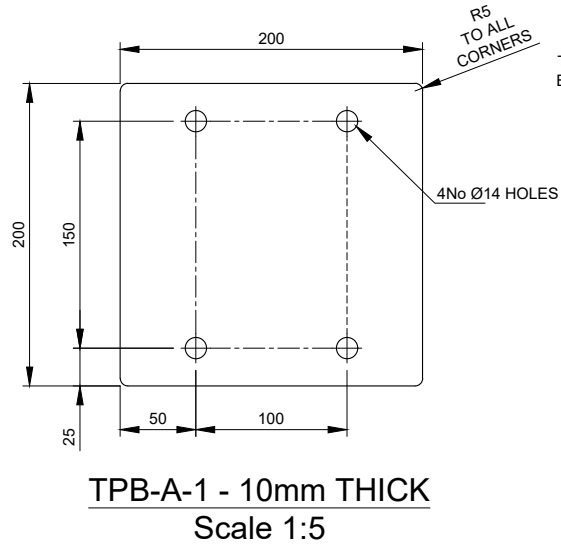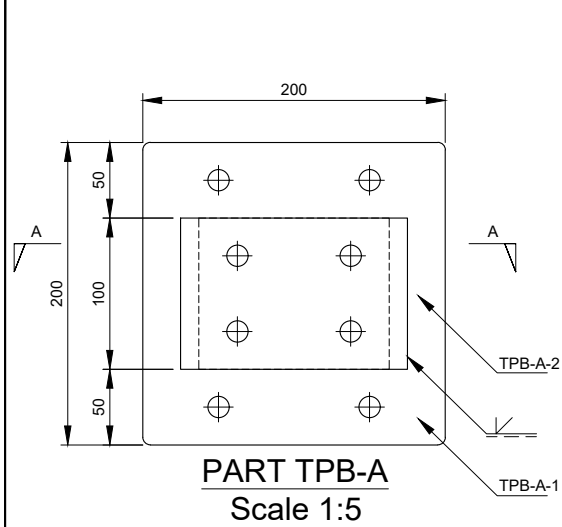

Parts list for TPB-A

Item	Part	Quantity	Part description	Length	Material	Weight
01	TPB-A-1	1	200x200x10mm	N/A	S275J0	3.14 kg
02	TPB-A-2	1	PFC 150x75x18	100mm	S275J0	1.79 kg
03	TPB-A-3	2	160x50x5mm	N/A	S275J0	0.31 kg
04	STUDS	4	M12 STUDDING	450mm	GRADE 8.8	0.34 kg
					Total Weight:	6.60 kg

- All steel hot dip galvanized
- Each STUD to be supplied with 4 Full Nuts, 2 Flat Washers and 2 Spring Washers
- For fabrtrication notes see drawing 304

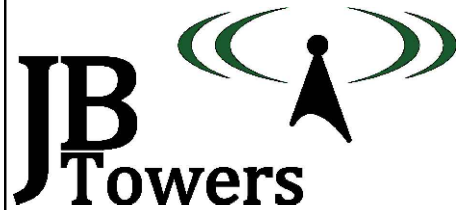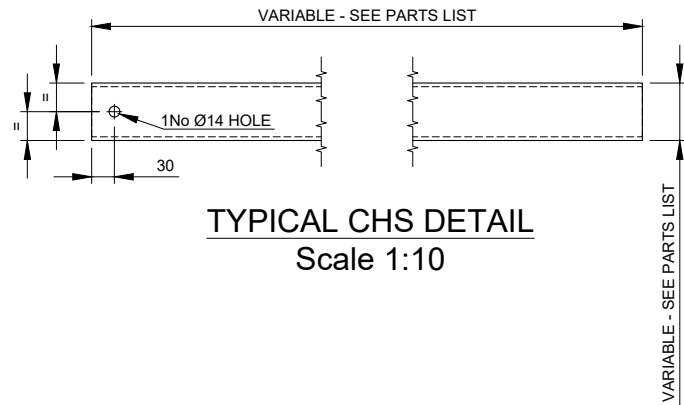

01	FIRST ISSUE	AM	23/05/18
REV	REV	BY	DATE
SCALE AS SHOWN	DRAWN	CHECKED	APPROVED
WHEN PRINTED AT A3	AM	MP	JBT
DATE	19/11/18	DATE	19/11/18
DATE	19/11/18	DATE	19/11/18
ALL DIMENSIONS IN mm UNLESS OTHERWISE STATED. THIS DRAWING TO BE READ IN CONJUNCTION WITH OTHER RELEVANT DRAWINGS.			

TITLE
ANTENNA MOUNTING
BRACKET & TYP CHS DETAIL
PART: TPB-A


SITE ADDRESS
VALENTINE FARM
SHOGMOOR LANE
SKIRMETT
HENLEY-ON-THAMES
RG9 6TD

ARQIVA REF.
141568
DRG No.
301
REV
01

ALL SCALES AS SHOWN WHEN PRINTED AT A3



ALL SCALES AS SHOWN WHEN PRINTED AT A3

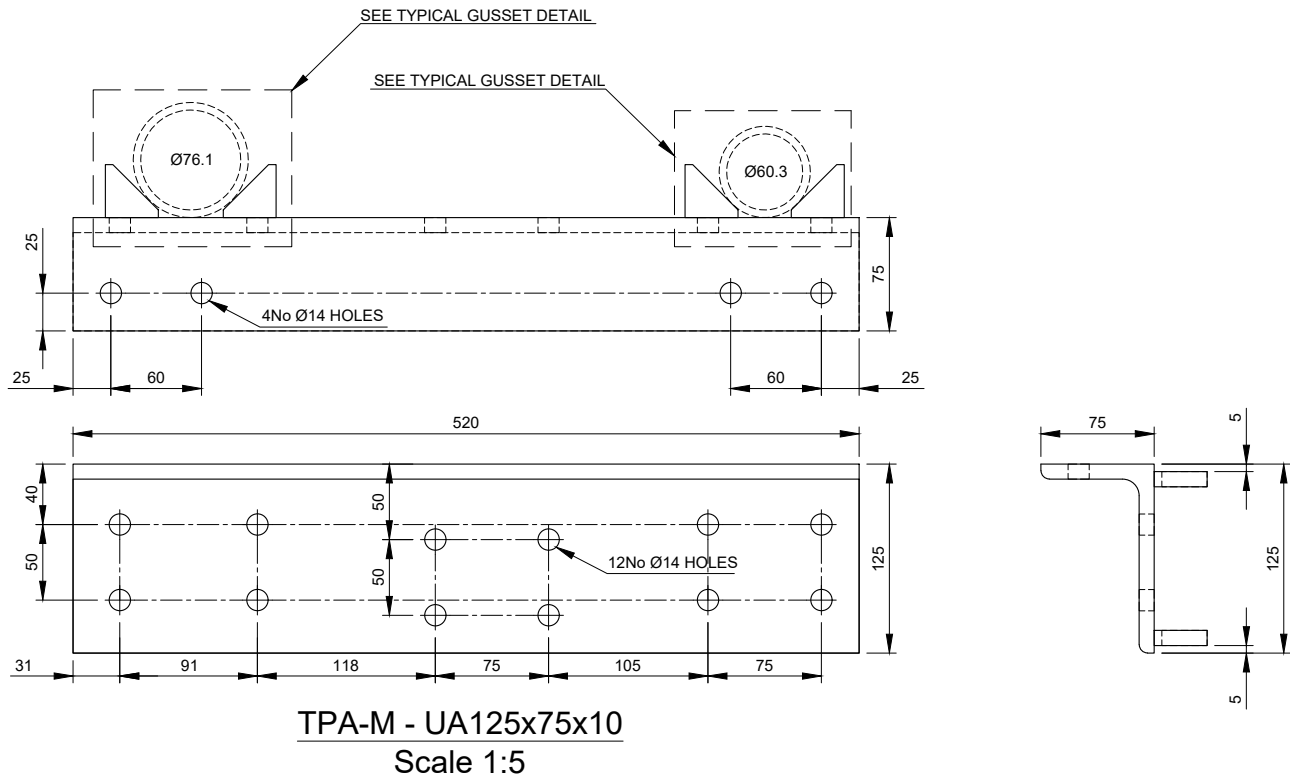


TPA-M - UA125x75x10
Scale 1:5


Parts list for TPA-M

Item	Part	Quantity	Part description	Length	Material	Weight
01	TPA-M	1	UA125x75x10 C/W GUSSETS	520mm	S275J0	7.80 kg
02	U-BOLT	2	M12 U-BOLT FOR CHS 60.3mm	N/A	GRADE 8.8	-
03	U-BOLT	2	M12 U-BOLT FOR CHS 76.1mm	N/A	GRADE 8.8	-
03	BOLT	4	M12x45 (2D+6) BOLT	N/A	GRADE 8.8	-
Total Weight:						5.25 kg

- All steel hot dip galvanized
- Each STUD & U-BOLT to be supplied with 4 Full Nuts, 2 Flat Washers and 2 Spring Washers
- Each BOLT to be supplied with 1 Full Nut, 1 Form E FLat Washer and 1 Spring Washer
- For fabrtrication notes see drawing 304

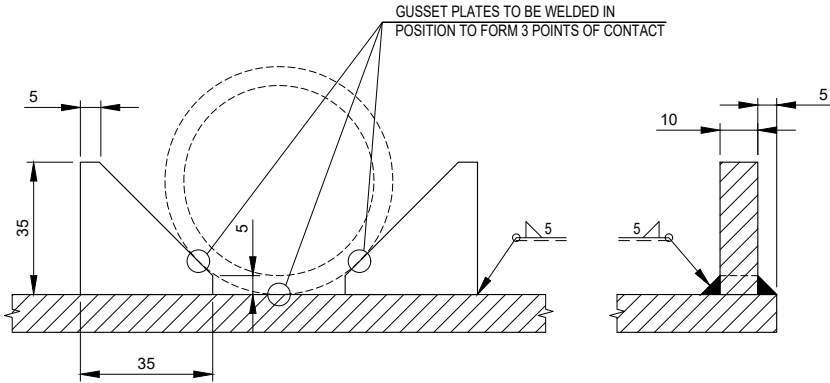

TYPICAL GUSSET PLATE DETAIL
Scale 1:2

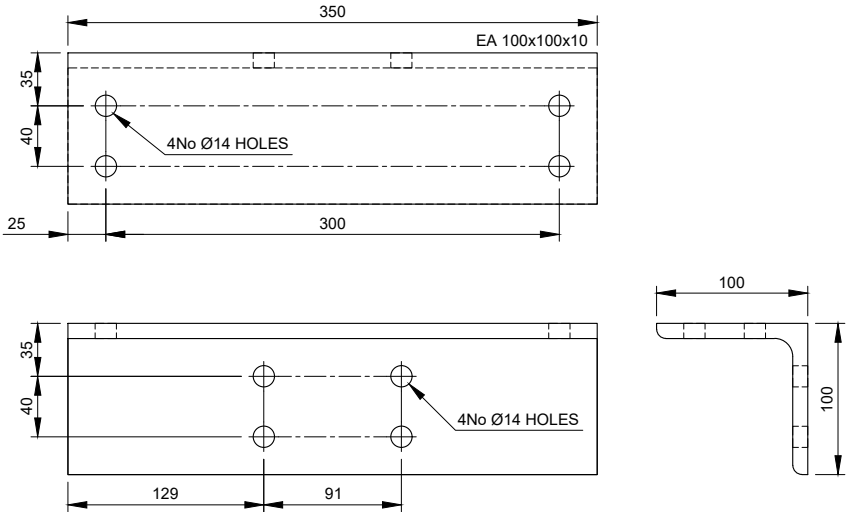


TPY-A - EA100x100x10
Scale 1:5

Parts list for TPY-A

Item	Part	Quantity	Part description	Length	Material	Weight
01	TPY-A	1	EA100x100x10	350mm	S275J0	5.25 kg
02	U-BOLT	2	M12 U-BOLT FOR CHS 25mm	N/A	GRADE 8.8	-
03	U-BOLT	2	M12 U-BOLT FOR CHS 76.1mm	N/A	GRADE 8.8	-
Total Weight:						5.25 kg

- All steel hot dip galvanized
- Each STUD & U-BOLT to be supplied with 4 Full Nuts, 2 Flat Washers and 2 Spring Washers
- Each BOLT to be supplied with 1 Full Nut, 1 Form E FLat Washer and 1 Spring Washer
- For fabrtrication notes see drawing 304

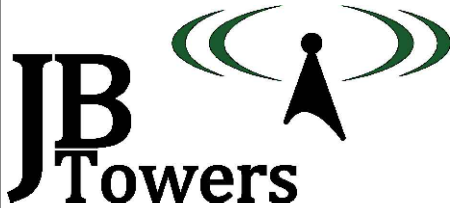

01	FIRST ISSUE	AM	19/11/18
REV	REV	BY	DATE
SCALE AS SHOWN WHEN PRINTED AT A3	DRAWN DATE	AM 19/11/18	CHECKED DATE
MP 19/11/18	APPROVED DATE	JBT 19/11/18	
ALL DIMENSIONS IN mm UNLESS OTHERWISE STATED. THIS DRAWING TO BE READ IN CONJUNCTION WITH OTHER RELEVANT DRAWINGS.			

TITLE
ANTENNA MOUNTING
BRACKETS

PARTS: TPA-M; TPY-A

SITE ADDRESS
VALENTINE FARM
SHOGMOOR LANE
SKIRMETT
HENLEY-ON-THAMES
RG9 6TD

ARQIVA REF.
141568


DRG No.
302

REV
01

ALL SCALES AS SHOWN WHEN PRINTED AT A3



ALL SCALES AS SHOWN WHEN PRINTED AT A3

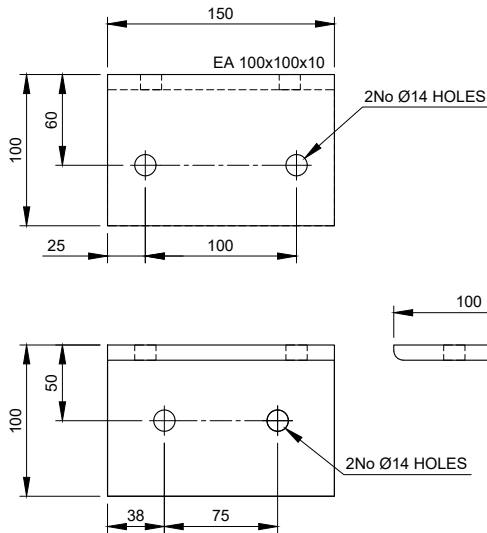


TPL-A - EA100x100x10
Scale 1:5

Parts list for TPL-A

Item	Part	Quantity	Part description	Length	Material	Weight
01	TPL-A	1	EA100x100x10	150mm	S275J0	2.25 kg
02	BOLT	2	M12 55mm LONG SET BOLT	55mm	GRADE 8.8	-
03	U-BOLT	1	M12 U-BOLT FOR CHS 60.3mm	N/A	GRADE 8.8	-
Total Weight:						2.25 kg

- All steel hot dip galvanized
- Each STUD & U-BOLT to be supplied with 4 Full Nuts, 2 Flat Washers and 2 Spring Washers
- Each BOLT to be supplied with 1 Full Nut, 1 Form E FLat Washer and 1 Spring Washer
- For fabrctication notes see drawing 304

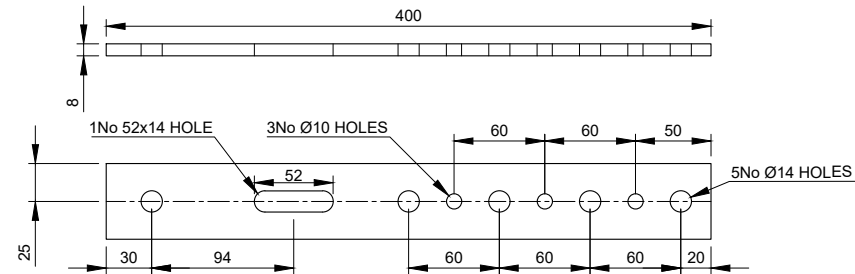


TPA-PD - 8mm THICK
Scale 1:5

Parts list for TPA-PD

Item	Part	Quantity	Part description	Length	Material	Weight
01	TPA-PD	1	400x50x8mm	N/A	S275J0	1.26 kg
02	U-BOLT	1	M12 U-BOLT FOR CHS 76.1mm	N/A	GRADE 8.8	-
Total Weight:						1.26 kg

- All steel hot dip galvanized
- Each U-BOLT to be supplied with 4 Full Nuts, 2 Flat Washers and 2 Spring Washers
- For fabrctication notes see drawing 304

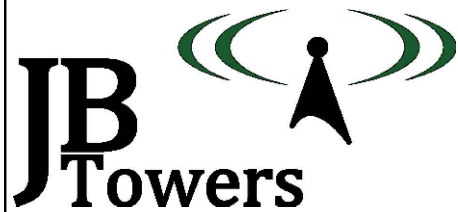

01	FIRST ISSUE	AM	19/11/18
REV	REV	BY	DATE
SCALE AS SHOWN	DRAWN	CHECKED	APPROVED
WHEN PRINTED AT A3	DATE	DATE	DATE
19/11/18	19/11/18	19/11/18	19/11/18
ALL DIMENSIONS IN mm UNLESS OTHERWISE STATED. THIS DRAWING TO BE READ IN CONJUNCTION WITH OTHER RELEVANT DRAWINGS.			

TITLE		SITE ADDRESS	
LOG MOUNTING BRACKET & POWER DIVIDER STRAP		VALENTINE FARM SHOGMOOR LANE SKIRMETT HENLEY-ON-THAMES RG9 6TD	
PART: TPL-A; TPA-PD		ARQIVA REF. 141568	DRG No. 303
			REV 01

ALL SCALES AS SHOWN WHEN PRINTED AT A3



ALL SCALES AS SHOWN WHEN PRINTED AT A3

Item	Part	Drawing	Quantity	Part description	Length	Material	Weight
01	01	200	1	3 MAN LATCHWAY SYSTEM & 3No. WIRE GUIDES FOR FACE MOUNTED MONOPOLE	17000	N/A	-
02	TPB-C	300	2	FALL ARREST ATTACHMENT POINT	N/A	S275J0	4.48 kg
03	03	200	46	PERMANENT BT STEP c/w 3No 10x75mm ZINC-PLATED COACH SCREWS	N/A	S275J0	13.80 kg
04	TPS-R	300	9	'MonoStep' ASSEMBLY	N/A	S275J0	25.65 kg
05	TPB-A	301	4	MOUNTING BRACKET	N/A	S275J0	26.40 kg
06	TPA-M	302	4	ANTENNA MOUNTING BRACKET	N/A	S275J0	21.00 kg
07	07	203	1	CHS 60.3x5mm	2500mm	S355J2H	17.05 kg
08	08	203	1	CHS 76.1x5mm	3200mm	S355J2H	26.10 kg
09	TPL-A	303	8	LOG MOUNTING BRACKET	N/A	S275J0	18.00 kg
10	TPY-A	302	1	YAGI MOUNTING BRACKET	350mm	S275J0	5.25 kg
11	TPA-PD	303	6	POWER DIVIDER STRAP	N/A	S275J0	7.56 kg
12	12	204	1	CHS 76.1x5mm	2200mm	S355J2H	19.30 kg
13	13	200	1	FEEDER COVER - 2/CG/100	3500mm	UV RESISTANT PLASTIC	-
14	14	200	17	FEEDER CLAMP - 2/FCD/028	N/A	POLYPROPYLENE	-
15	15	200	17	M10 SCREW DOWELS WTH M10 NUT	100mm	STAINLESS STEEL	-
16	16	200	1	PoleSaver	750mm	N/A	-
17	17	200	8	M12 STUD + 4No NUTS + 2No FLAT WASHERS + 1No Ø50mm WASHER (FOR FALL ARREST SYSTEM)	500mm	GRADE 8.8	3.56 kg
18	18	-	24	M12 WASHER	N/A	GRADE 8.8	-


- All steel hot dip galvanized

- All U-BOLTS to be FLA supply, each Supplied with 4 Full Nuts, 2 Flat Washers and 2 Spring Washers

Total Weight: 188.15 kg

NOTES:

1. WELDING TO BE IN ACCORDANCE WITH BS EN 1011-1:2009
2. LINEAR DIMS TO BE WITHIN ±1mm;
3. ANGULAR TOLERANCES TO BE WITHIN 0.5°
4. WELDING SYMBOLS ARE IN ACCORDANCE WITH BS EN 22553:1995
5. ALL PROFILE EDGES TO BE DRESSED AND SHARP CORNERS REMOVED
6. ALL WELD SIZES ARE FINAL SIZES
7. ALL WELDED JOINTS ARE TO BE PICKLE TIGHT
8. ALL STEELWORK TO BE BS EN 10025 GRADE S275 J0 UNO & HOT DIPPED GALVANISED TO BS EN ISO 1461. (ALL HOLLOW SECTIONS TO BE GRADE S355 J0H)
9. ALL STEEL IS TO BE SUPPLIED IN ACCORDANCE WITH EN 1090 TO EXECUTION CLASS 2
10. ALL NON PRE-LOADED BOLTS TO BE COMPLIANT STRUCTURAL BOLTS TO BS EN ISO 15048 PARTS 1&2.
11. STEELWORK COMPONENTS SHALL BE HOT DIP GALVANISED TO ACHIEVE A "VERY HIGH" DURABILITY FOR AN ENVIRONMENT CATEGORY CODE C4 FROM TABLE 1 IN BS EN ISO 14713
12. BOLTS AND NUTS SHALL BE SUPPLIED IN ACCORDANCE WITH BS 7371, SPUN GALVANISED IN ACCORDANCE WITH ISO 10684, THE NUTS RE-TAPPED AFTER GALVANISING, AND THE THREADS TREATED WITH GREASE.
13. ALL BOLTS TO BE CUT ON SITE TO EXTEND MAX 10mm BEYOND THE NUT WHEN TIGHTENED UNO.
14. ALL SITE DRILLED HOLE/CUT ENDS TO BE TREATED WITH METAFLUX 70-40 ZINC PASTE FOLLOWED BY 1 COAT OF 7-42 ZINC ALU OR 70-16 ALUMINIUM SPRAY

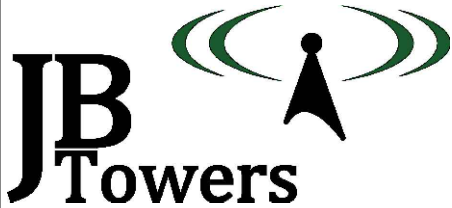

01	FIRST ISSUE	AM	19/11/18
REV	REV	BY	DATE
SCALE AS SHOWN WHEN PRINTED AT A3	DRAWN AM DATE 19/11/18	CHECKED MP DATE 19/11/18	APPROVED JBT DATE 19/11/18
ALL DIMENSIONS IN mm UNLESS OTHERWISE STATED. THIS DRAWING TO BE READ IN CONJUNCTION WITH OTHER RELEVANT DRAWINGS.			

TITLE
PARTS LIST

SITE ADDRESS		
VALENTINE FARM SHOGMOOR LANE SKIRMETT HENLEY-ON-THAMES RG9 6TD		
ARQIVA REF. 141568	DRG No. 304	REV 01

ALL SCALES AS SHOWN WHEN PRINTED AT A3



ALL SCALES AS SHOWN WHEN PRINTED AT A3