


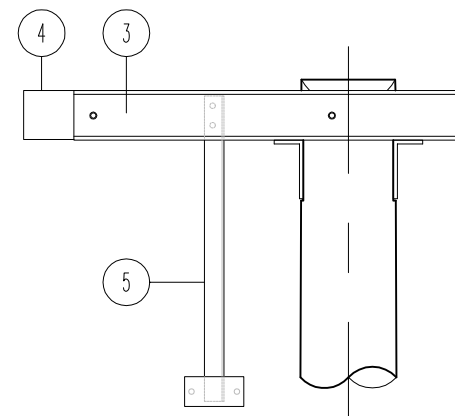
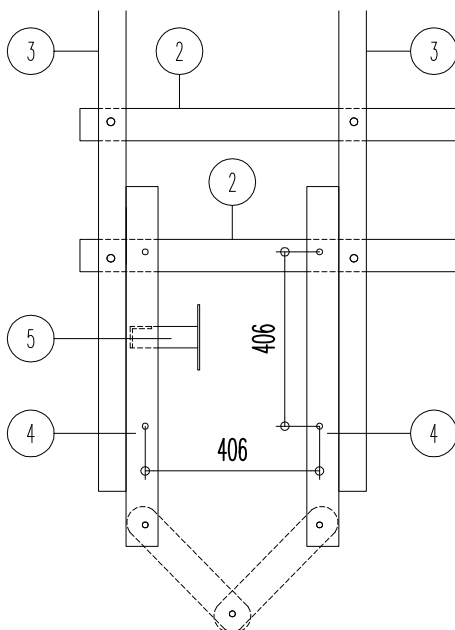
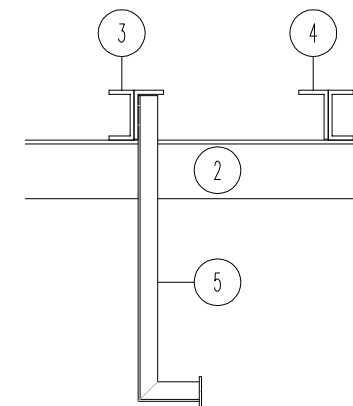


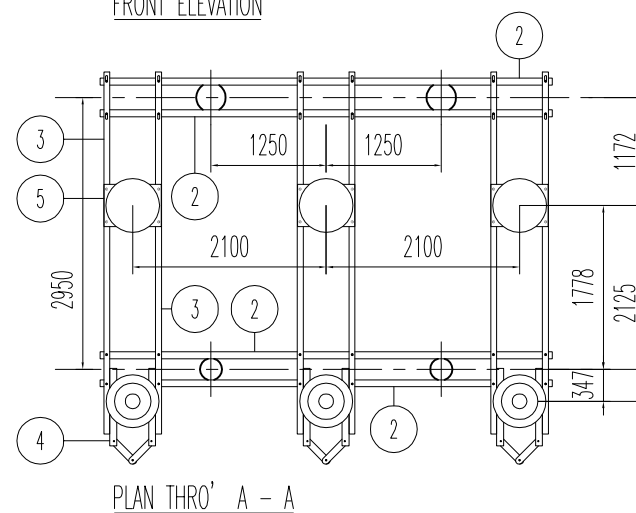

PART DETAIL OF SIDE ELEVATION
AT CHANNEL SUPPORT ENDS

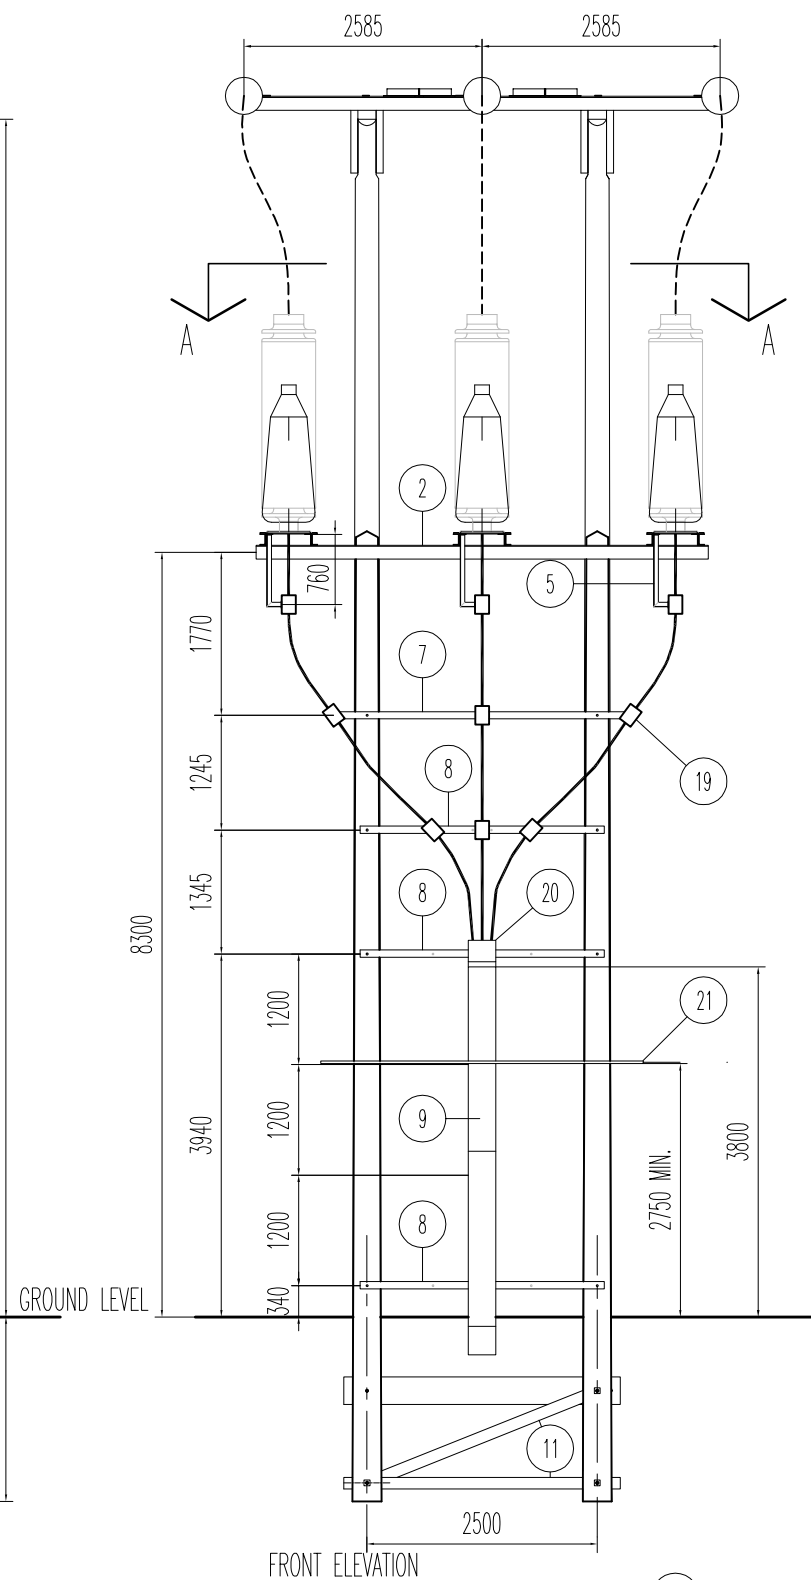

PART DETAIL OF PLAN AT CHANNEL SUPPORT ENDS
CABLE SEALING ENDS OMITTED

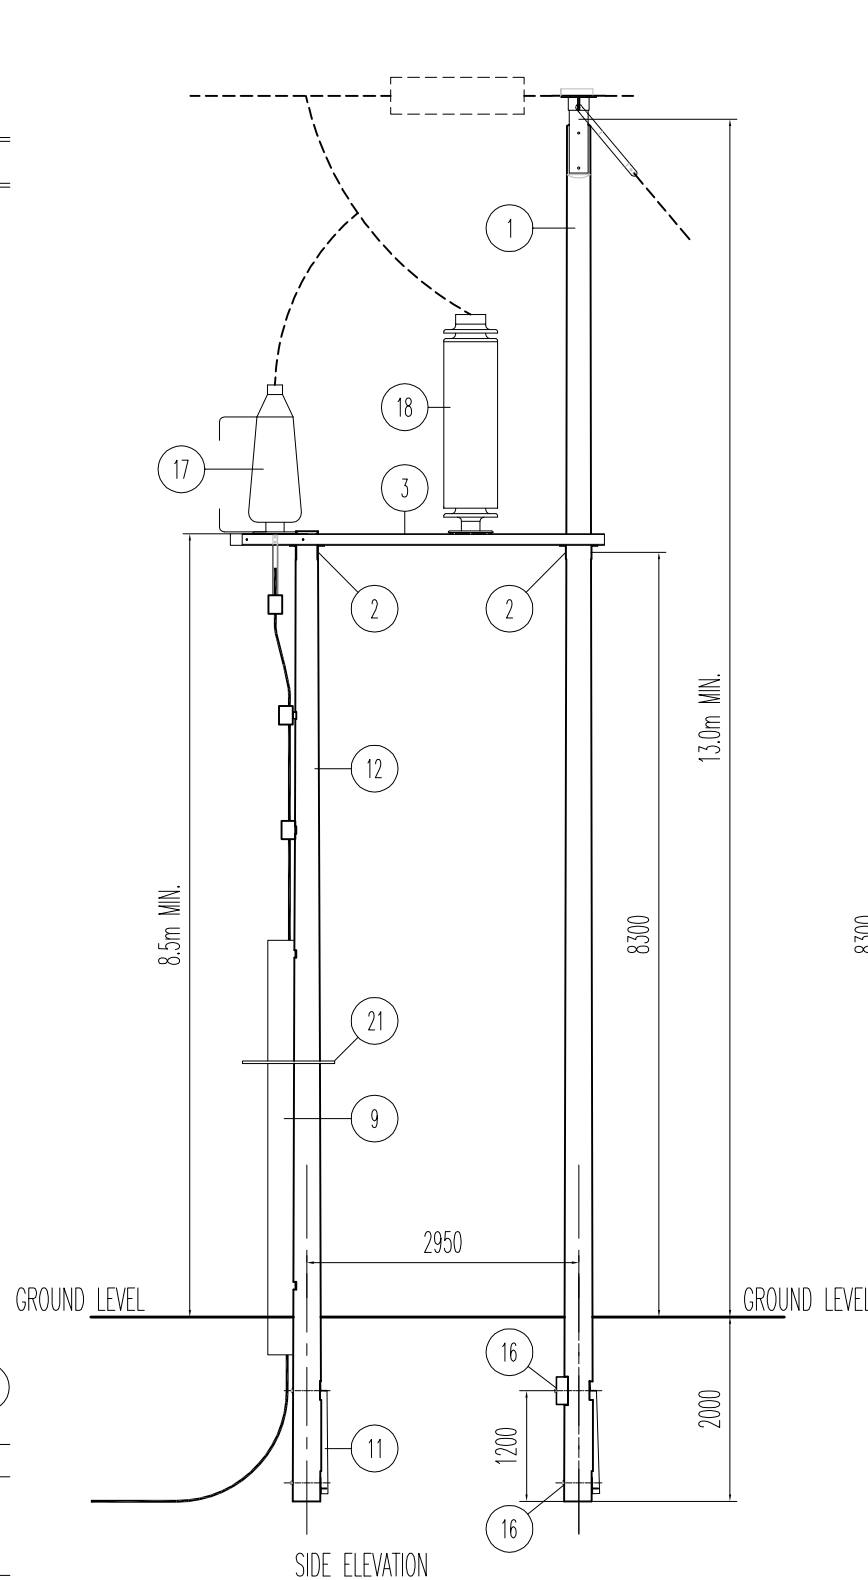

PART DETAIL OF FRONT ELEVATION

No.	ITEM	ENATS STANDARD DRG No. OR BS REF	No. OF	REMARKS
1	TERMINAL 'H' POLE	435013	1	SEE NOTES
2	CROSSARM CABLE TERM	439545	4	
3	CHANNEL SUPPORTS	439547	6	
4	SEALING END SUPPORT	439548	3 SETS	IN HANDED PAIRS
5	CABLE CLEAT SUPPORT	439549	3	
6	SURGE DIVERTER SUPPORT PLATE	439550	3	
7	CABLE SUPPORT CROSSARM 'A'	439551	1	
8	CABLE SUPPORT CROSSARM 'B'	439552	3	
9	132kV CABLE GUARD	439553	2	
10	CABLE BACKBOARD	435018	1	
11	'A' POLE FOUNDATION BRACE	439545	2	
12	CABLE TERMINAL AUX. POLE	435005	2	
13	M12 x 50 BOLT	ENAT 43 - 95	6	
14	M16 x 50 BOLT	ENAT 43 - 95	54	
15	M20 x 375 BOLT	ENAT 43 - 95	14	
16	SQUARE CURVED WASHER	439605	3	
17	132kV SEALING END		3	SEE NOTES
18	132kV SURGE DIVERTER		3	
19	SINGLE CABLE CLEAT		9	
20	TREFOIL CABLE CLEAT		4	
21	ANTI-CLIMBING DEVICE	ENAT 43 - 90	-	

NOTES

ITEM 1 TO INCLUDE ALL ITEMS FROM 435013 EXCEPT Nos. 2, 23, 24 & 25.

ITEM 17 132kV SEALING END TO INCLUDE ARCING HORNS AND EARTH END ATTACHMENT PLATES

ALL DIMENSIONS IN MILLIMETRES UNLESS OTHERWISE STATED.



ENATS Drawing No. 435015

General Arrangement Pole Mounted Cable Termination - Boat Crossarm