




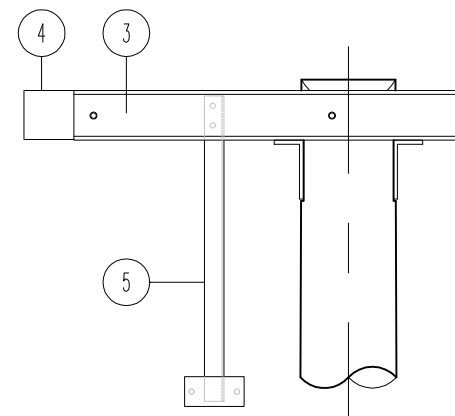


PART DETAIL OF SIDE ELEVATION
AT CHANNEL SUPPORT ENDS

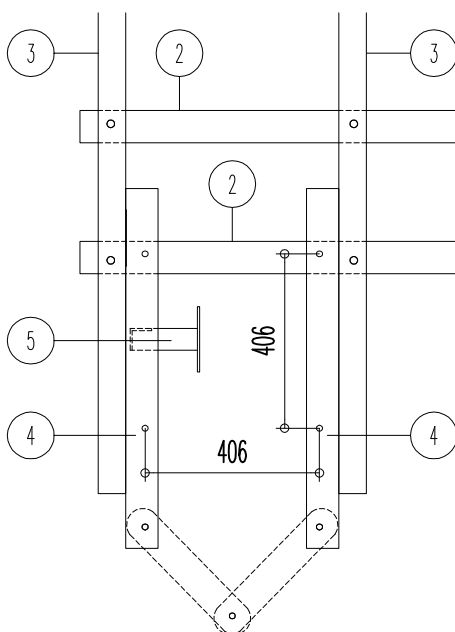


PART DETAIL OF PLAN AT CHANNEL SUPPORT ENDS
CABLE SEALING ENDS OMITTED

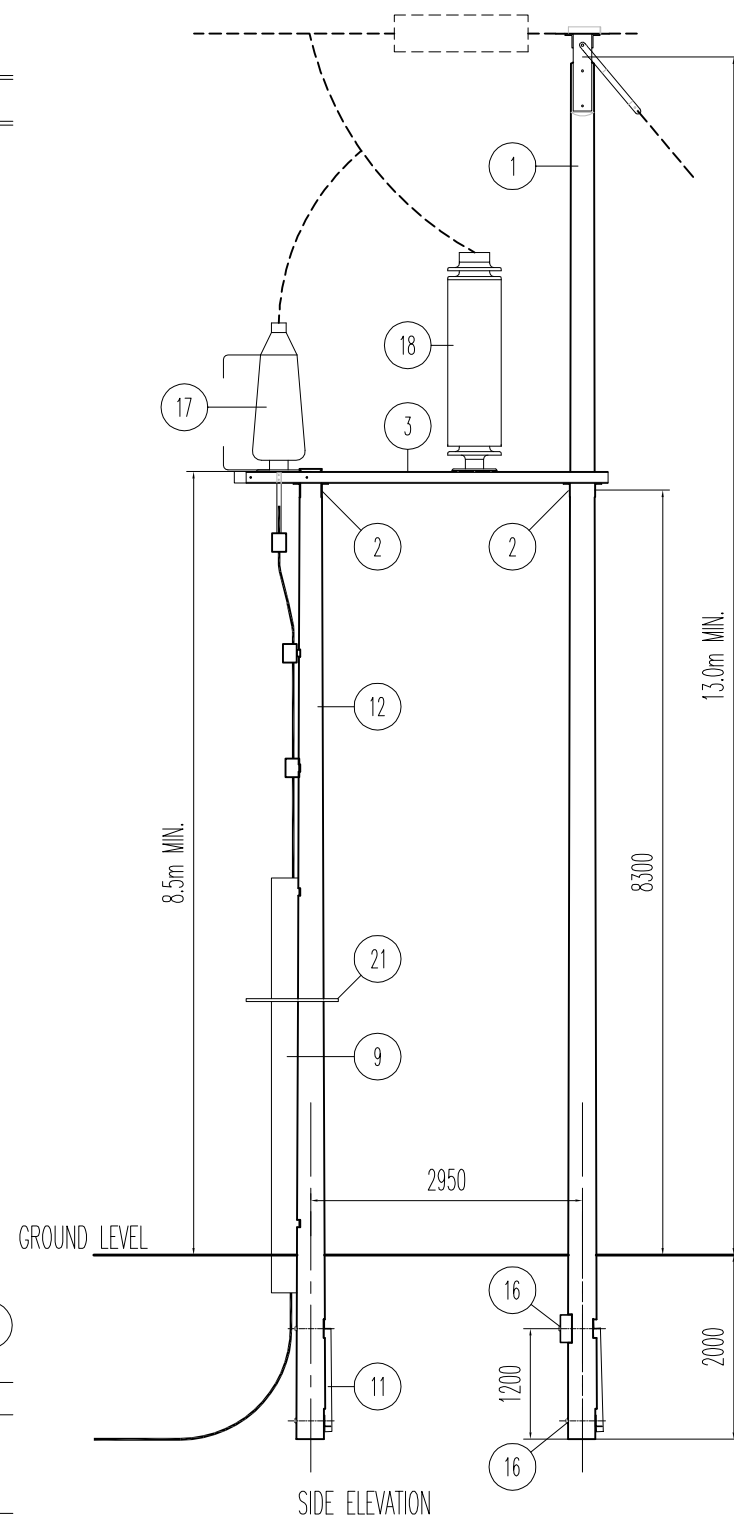


SIDE ELEVATION

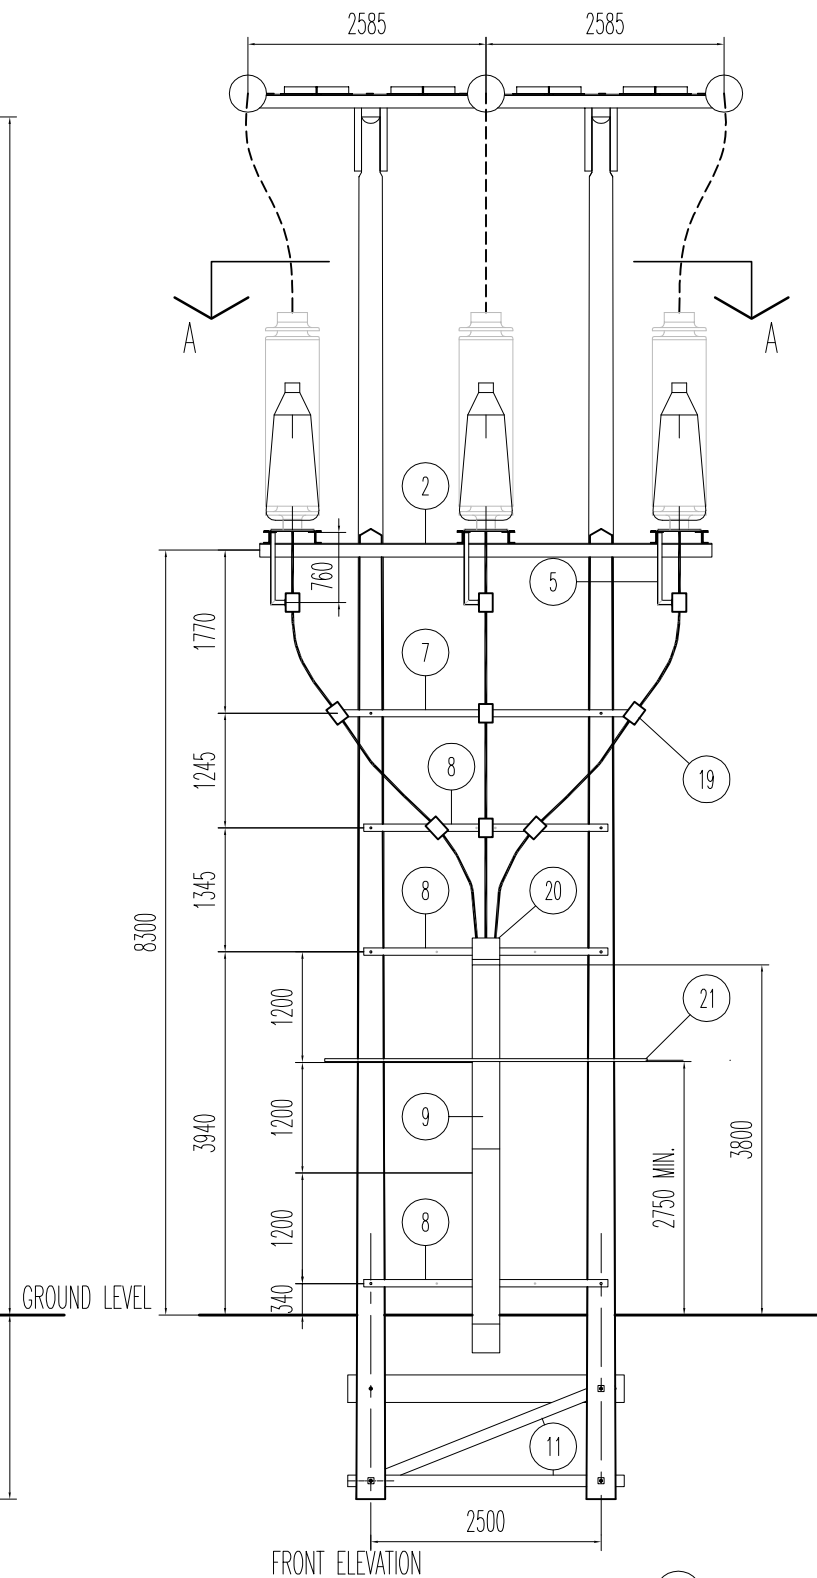

FRONT ELEVATION

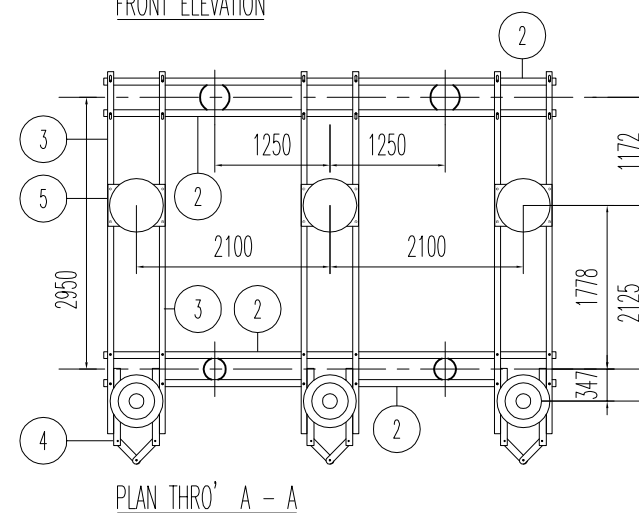

PLAN THRO' A - A

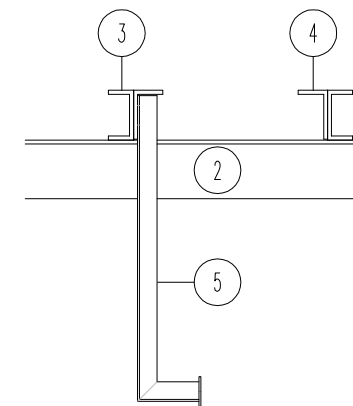

PART DETAIL OF FRONT ELEVATION

No.	ITEM	ENATS STANDARD DRG No. OR BS REF	No. OF	REMARKS
1	TERMINAL 'H' POLE	435014	1	SEE NOTES
2	CROSSARM CABLE TERM	439545	4	
3	CHANNEL SUPPORTS	439547	6	
4	SEALING END SUPPORT	439548	3 SETS	IN HANDED PAIRS
5	CABLE CLEAT SUPPORT	439549	3	
6	SURGE DIVERTER SUPPORT PLATE	439550	3	
7	CABLE SUPPORT CROSSARM 'A'	439551	1	
8	CABLE SUPPORT CROSSARM 'B'	439552	3	
9	132kV CABLE GUARD	439553	2	
10	CABLE BACKBOARD	435018	1	
11	'A' POLE FOUNDATION BRACE	439545	2	
12	CABLE TERMINAL AUX. POLE	435005	2	
13	M12 x 50 BOLT	ENAT 43 - 95	6	
14	M16 x 50 BOLT	ENAT 43 - 95	54	
15	M20 x 375 BOLT	ENAT 43 - 95	14	
16	SQUARE CURVED WASHER	439605	3	
17	132kV SEALING END		3	SEE NOTES
18	132kV SURGE DIVERTER		3	
19	SINGLE CABLE CLEAT		9	
20	TREFOIL CABLE CLEAT		4	
21	ANTI-CLIMBING DEVICE	ENAT 43 - 90	-	

NOTES

ITEM 1 TO INCLUDE ALL ITEMS FROM 435014 EXCEPT Nos. 2, 23, 24 & 25.

ITEM 17 132kV SEALING END TO INCLUDE ARCING HORNS AND EARTH END ATTACHMENT PLATES

ALL DIMENSIONS IN MILLIMETRES UNLESS OTHERWISE STATED.