


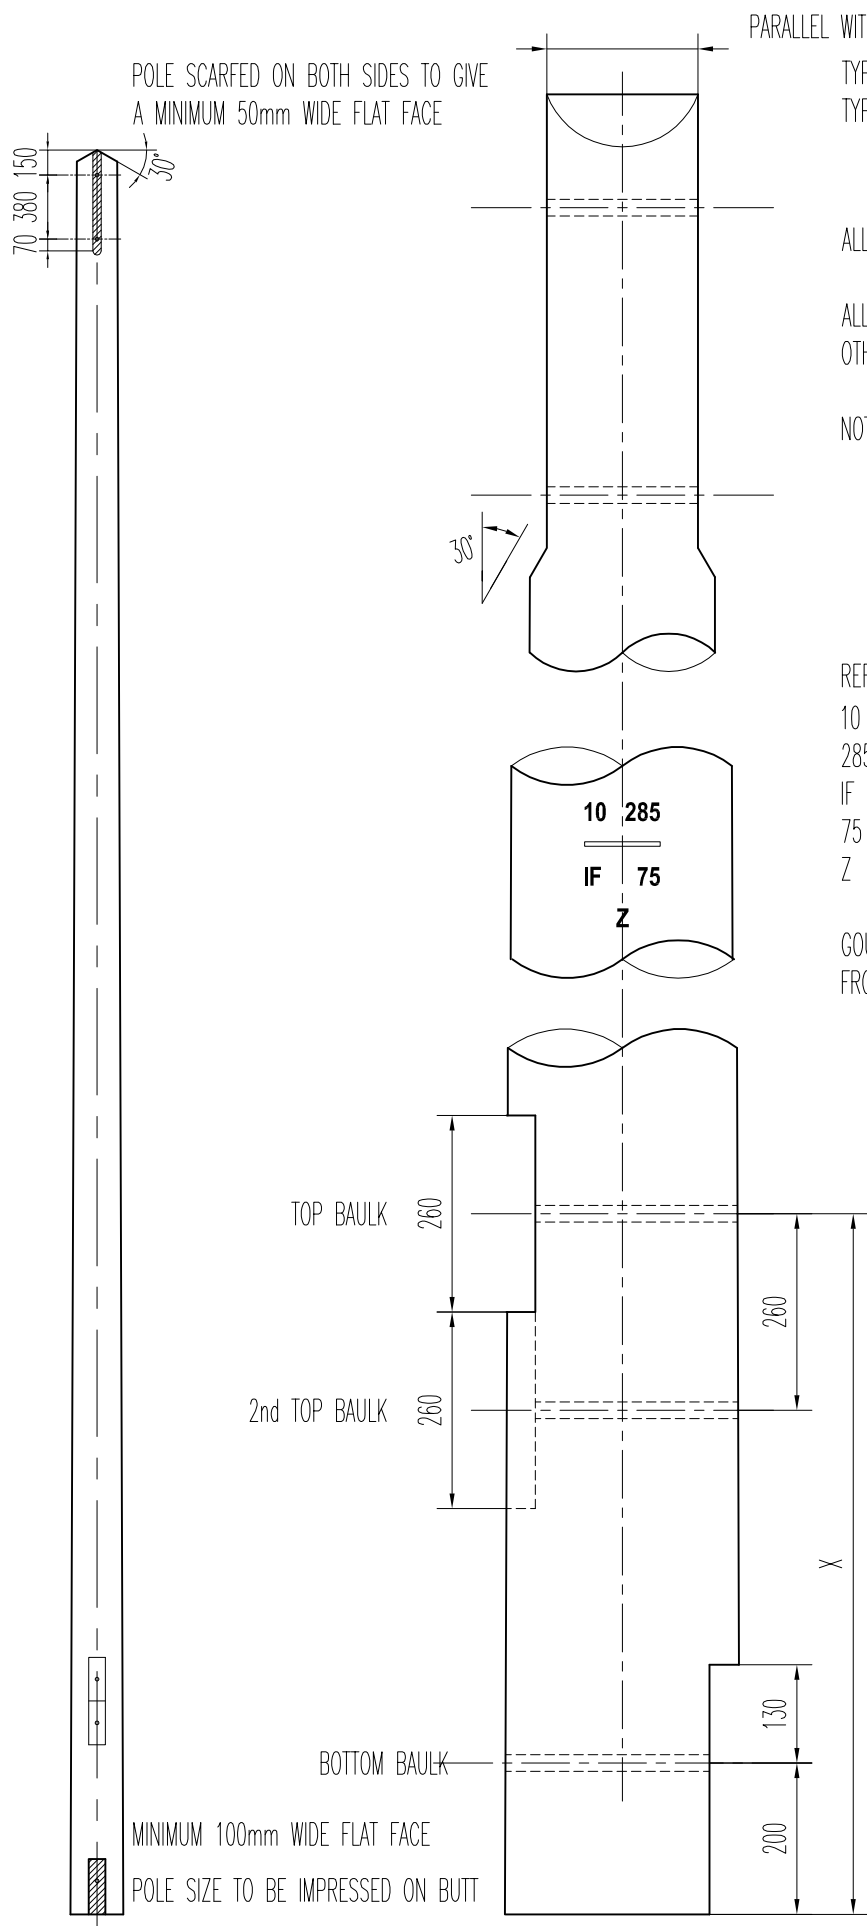

TYPE 1. 140-200mm NORMAL SPAN INTERMEDIATE
TYPE 2. 200-280mm SECTION AND LONG SPAN INTERMEDIATE

ALL DRILLINGS 22mm DIAMETER

ALL DIMENSIONS IN MILLIMETRES EXCEPT WHERE OTHERWISE STATED.

NOTE: STAYED SECTION POLE PLANTING DEPTH 2.0m

REFERENCE

10 - POLE LENGTH (m)
285 - POLE DIAMETER 1.5m FROM BUTT
IF - IMPORTED FIR
75 - YEAR OF CREOSOTING
Z - SUPPLIERS NAME OR MARK

GOUGE MARK 6mm WIDE x 6mm DEEP AND 3m FROM POLE BUTT.

PLANTING DEPTH (m)	FOUNDATION TYPES A & C	FOUNDATION TYPES B & D
	Dim. (m)	Dim. (m)
2.0	1.4	1.5
2.25	1.65	1.75
2.5	1.9	2.0
2.75	2.15	2.25
3.0	2.4	2.5

BAULK SCARFINGS CARRIED OUT ONLY WHEN SPECIFIED



ENATS Drawing No. 435002

Scarfig and Drilling - Single Intermediate and Section Poles