


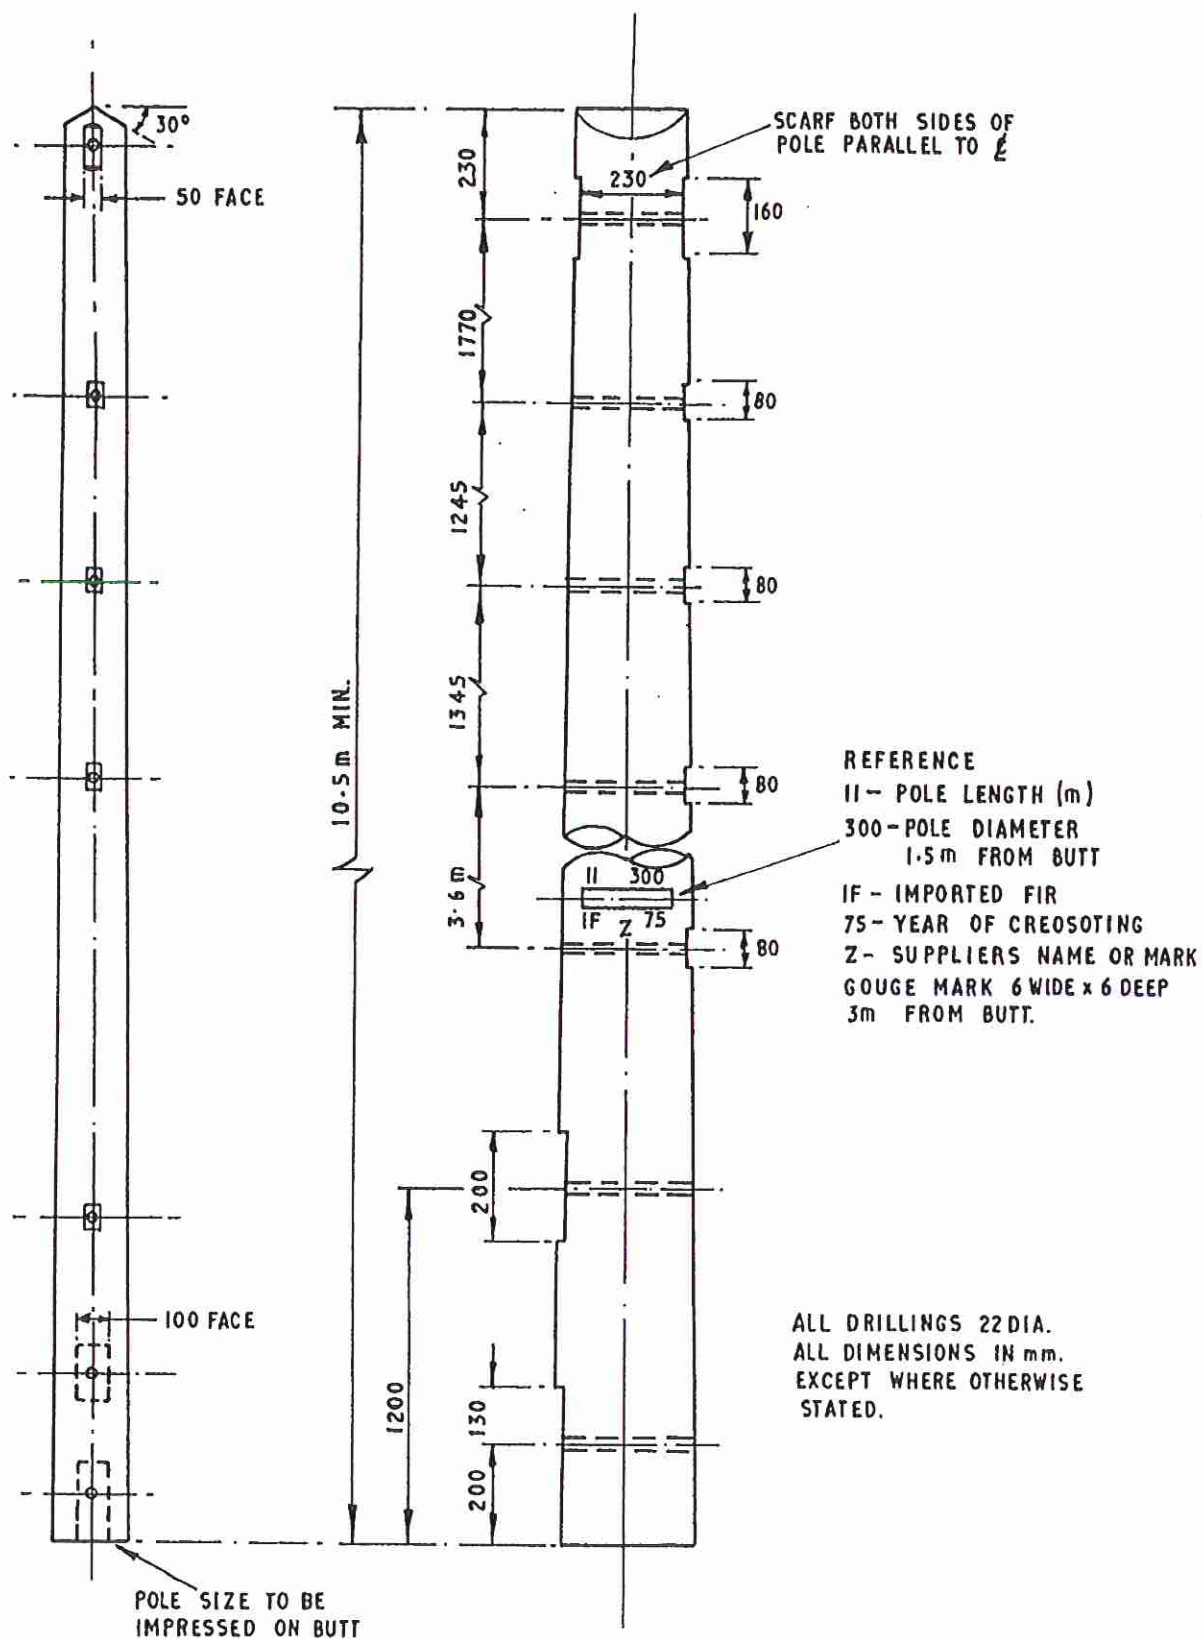

ESI Drawing No. 435005

Fig. 5 — Scarfing and drilling — cable terminal structure auxiliary pole