



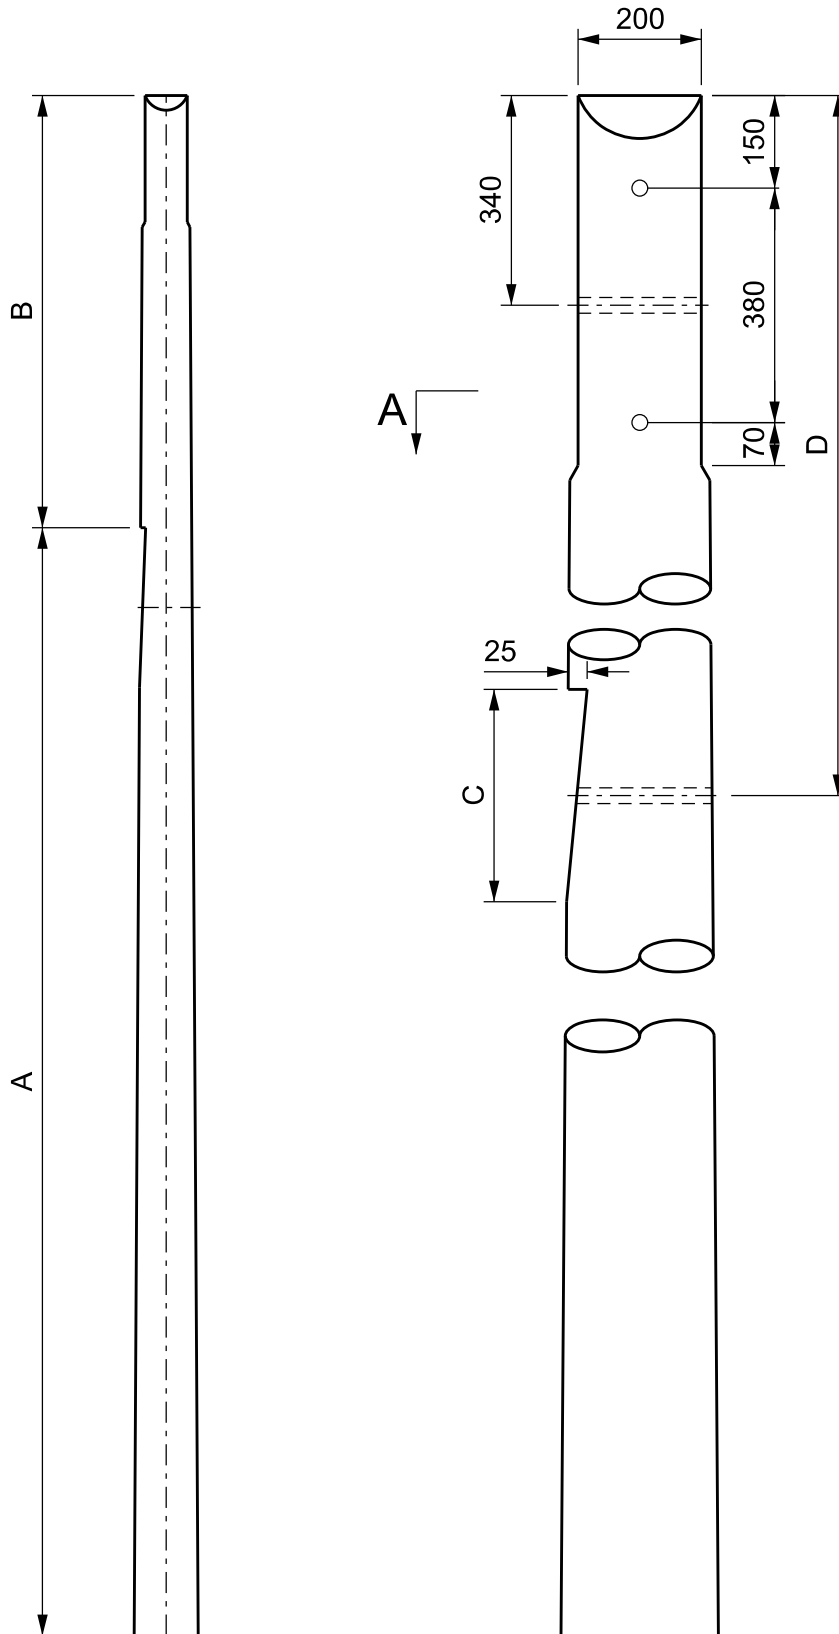

All drillings 22mm diameter

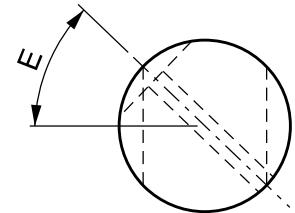

View on A-A
Orientation of scarfing
for strut pole

Description	Base Dia.	Top Dia.	A	B	C	D	E
15m extra stout	375	220	12806	2194	489	2444	44°
16m extra stout	390	220	13919	2081	695	2331	29°
17m extra stout	415	220	14949	2052	757	2302	23°

All dimensions in millimetres except where otherwise stated.

DRAWING STATUS	FOR APPROVAL	✓
	FOR TENDER	
	FOR CONSTRUCTION	
	AS BUILT	



THIS DRAWING AND ANY INFORMATION OR DESCRIPTIVE MATTER SET OUT HEREON ARE THE CONFIDENTIAL AND COPYRIGHT PROPERTY OF ELECTRICITY NORTH WEST LIMITED AND MUST NOT BE DISCLOSED, LOANED, COPIED OR USED FOR ANY PURPOSE WITHOUT WRITTEN PERMISSION.						
NOT TO BE SCALED. UNLESS OTHERWISE STATED DIMENSIONS ARE IN MILLIMETRES.						
REV	AMENDMENTS	DWN	CHKD	APP.	DATE	



ELECTRICITY NORTH WEST
WHITEBIRK DEPOT
WHITEBIRK DRIVE
BLACKBURN
BB1 3HT

TERMINAL WOODPOLE
PIECE SMALL DETAIL

DRAWN	L.B.	SCALE	N.T.S.	SITE NAME	ULVERSTON
CHECKED (LSTC)	D.C.	DATE	15-9-14	DWG NO	18-14073-21
APPROVED (ENW)		SHEET SIZE	A4	REV	A