


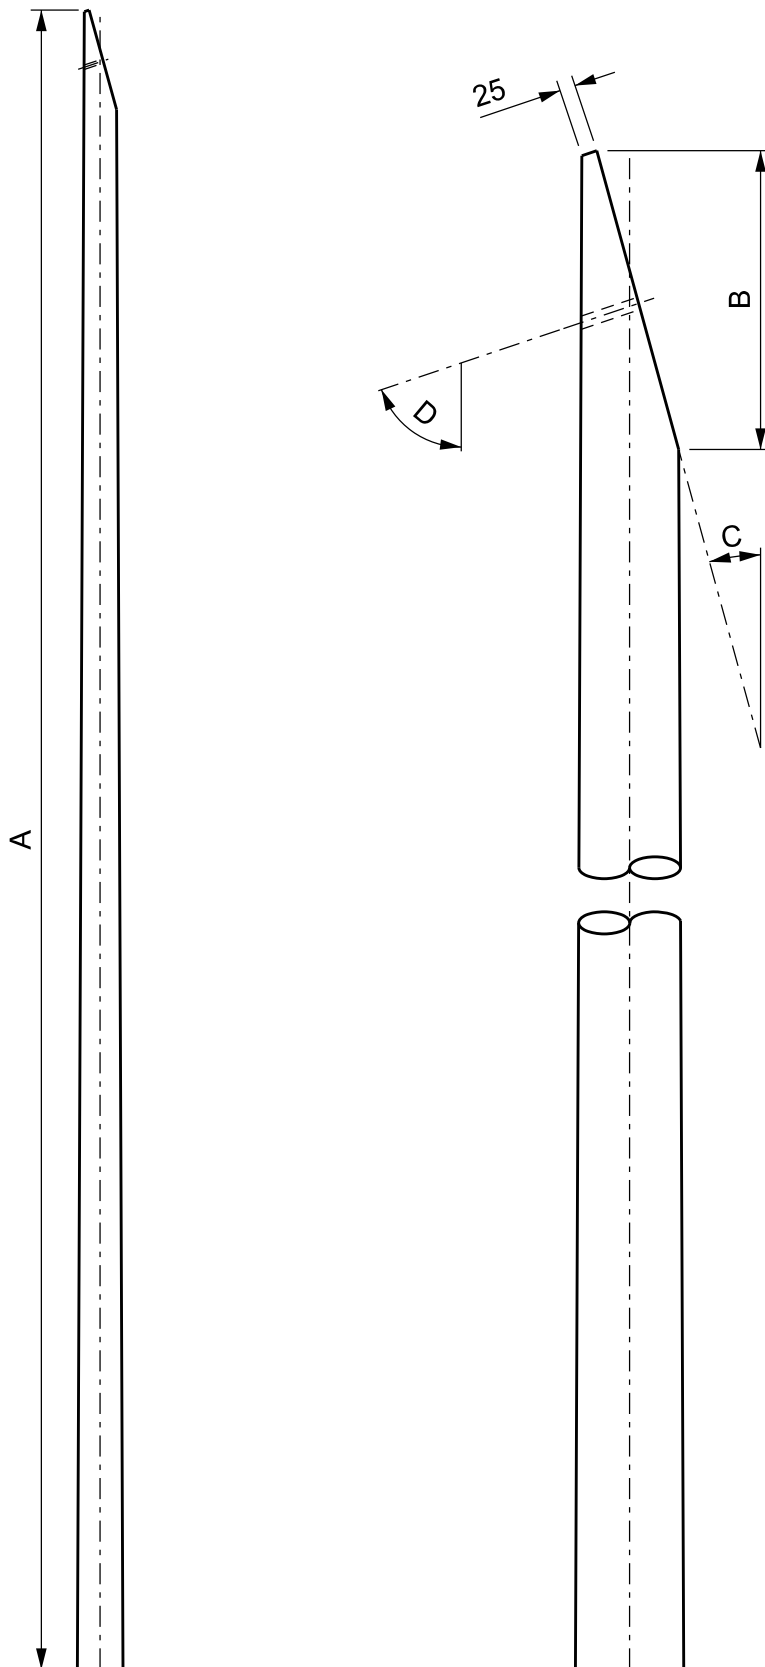

All drillings 22mm diameter

Description	Base Dia.	Top Dia.	A	B	C	D
12m medium	250	150	11852	473	15°	71°
13m stout	320	195	12914	673	15°	73°
14m stout	335	195	13905	737	13°	74°

All dimensions in millimetres except where otherwise stated.

DRAWING STATUS	FOR APPROVAL	✓
	FOR TENDER	
	FOR CONSTRUCTION	
	AS BUILT	



THIS DRAWING AND ANY INFORMATION OR DESCRIPTIVE MATTER SET OUT HEREON ARE THE CONFIDENTIAL AND COPYRIGHT PROPERTY OF ELECTRICITY NORTH WEST LIMITED AND MUST NOT BE DISCLOSED, LOANED, COPIED OR USED FOR ANY PURPOSE WITHOUT WRITTEN PERMISSION.						
NOT TO BE SCALED. UNLESS OTHERWISE STATED DIMENSIONS ARE IN MILLIMETRES.						
REV	AMENDMENTS	DWN	CHKD	APP.	DATE	



ELECTRICITY NORTH WEST
WHITEBIRK DEPOT
WHITEBIRK DRIVE
BLACKBURN
BB1 3HT

STRUT POLE
PIECE SMALL DETAIL

DRAWN	L.B.	SCALE	N.T.S.	SITE NAME	ULVERSTON		
CHECKED (LSTC)	D.C.	DATE	15-9-14	DWG NO	18-14073-22	REV	A
APPROVED (ENW)		SHEET SIZE	A4				