


DESCRIPTION POLE REFERENCE & NOTES REVISED						
REV	B	DATE	04-11-13	BY	SP	CHKD MJ
						APPD MJ

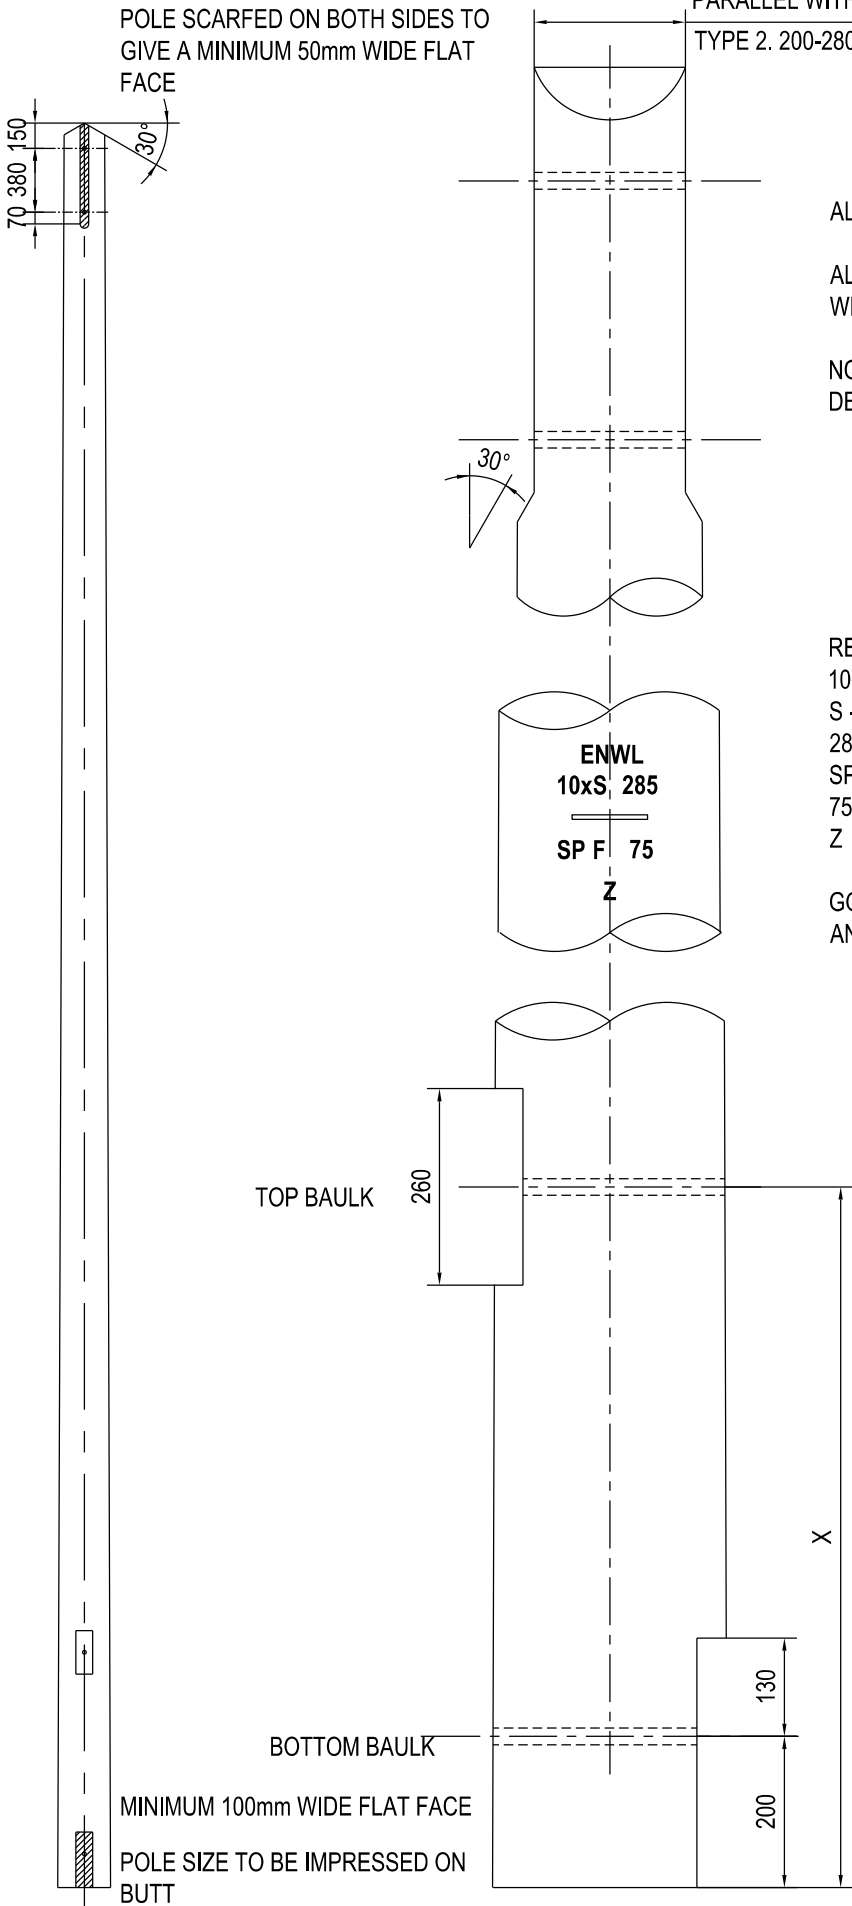

PARALLEL WITHIN LIMITS OF
TYPE 2. 200-280mm LONG SPAN INTERMEDIATE

ALL DRILLINGS 22mm DIAMETER

ALL DIMENSIONS IN MILLIMETRES EXCEPT
WHERE OTHERWISE STATED.

NOTE: STAYED SECTION POLE PLANTING
DEPTH 2.0m

REFERENCE
10 - POLE LENGTH (m)
S - CLASS OF POLE
285 - POLE DIAMETER 1.5m FROM BUTT
SP F - SCOTS PINE (FROM FINLAND)
75 - YEAR OF CREOSOTING
Z - SUPPLIERS NAME OR MARK

GOUGE MARK 6mm WIDE x 6mm DEEP
AND 3m FROM POLE BUTT.

PLANTING DEPTH (m)	FOUNDATION TYPE C
	Dim X(m)
2.2	1.6
2.4	1.8
2.8	2.2

TO BE READ IN CONJUNCTION WITH
FOUNDATION DRG No. 16_13228_115 &
POLE SCHEDULE 02_13228_02

BASED UPON ENATS Drawing No. 435002
AND GENERALLY IN ACCORDANCE
WITH ENW ES400W2

LS Transmission Consultancy Limited makes no warranties, express or implied, that compliance with this drawing, or any other document issued by LSTC, would in itself be sufficient to ensure safe systems of work or operation. Users are reminded of their own duties under health and safety legislation.



LSTC

LSTC North:
Yorkshire House
York Road
Little Driffield
East Yorkshire
YO25 5XA
Tel 01377 253617
Fax 01377 259555

LSTC South:
Bourne House
Office 21
475 Godstone Road
Whyteleafe
Surrey
CR3 0BL
Tel 01883 621114

CLIENT



PROJECT

WHITEBRK DRIVE
WHITEBRK
BLACKBURN
BB1 3HT
Tel: 01254 688917

KIRKBY - ORRELL

TITLE

**Scarfig and Drilling - Single
Intermediate Poles
with Backfill Type Foundations**

SCALE

NTS
(UNLESS OTHERWISE STATED)

DESIGNED

A4

DATE

31-10-13

CHECKED

MJ

DRAWN

SP

APPROVED

MJ

ORIGINAL SIZE

A4

DRAWING NUMBER

18_13228_172

REV

B