


DESCRIPTION POLE REFERENCE & NOTES REVISED						
REV	B	DATE	05-10-13	BY	SP	CHKD MJ APPD MJ

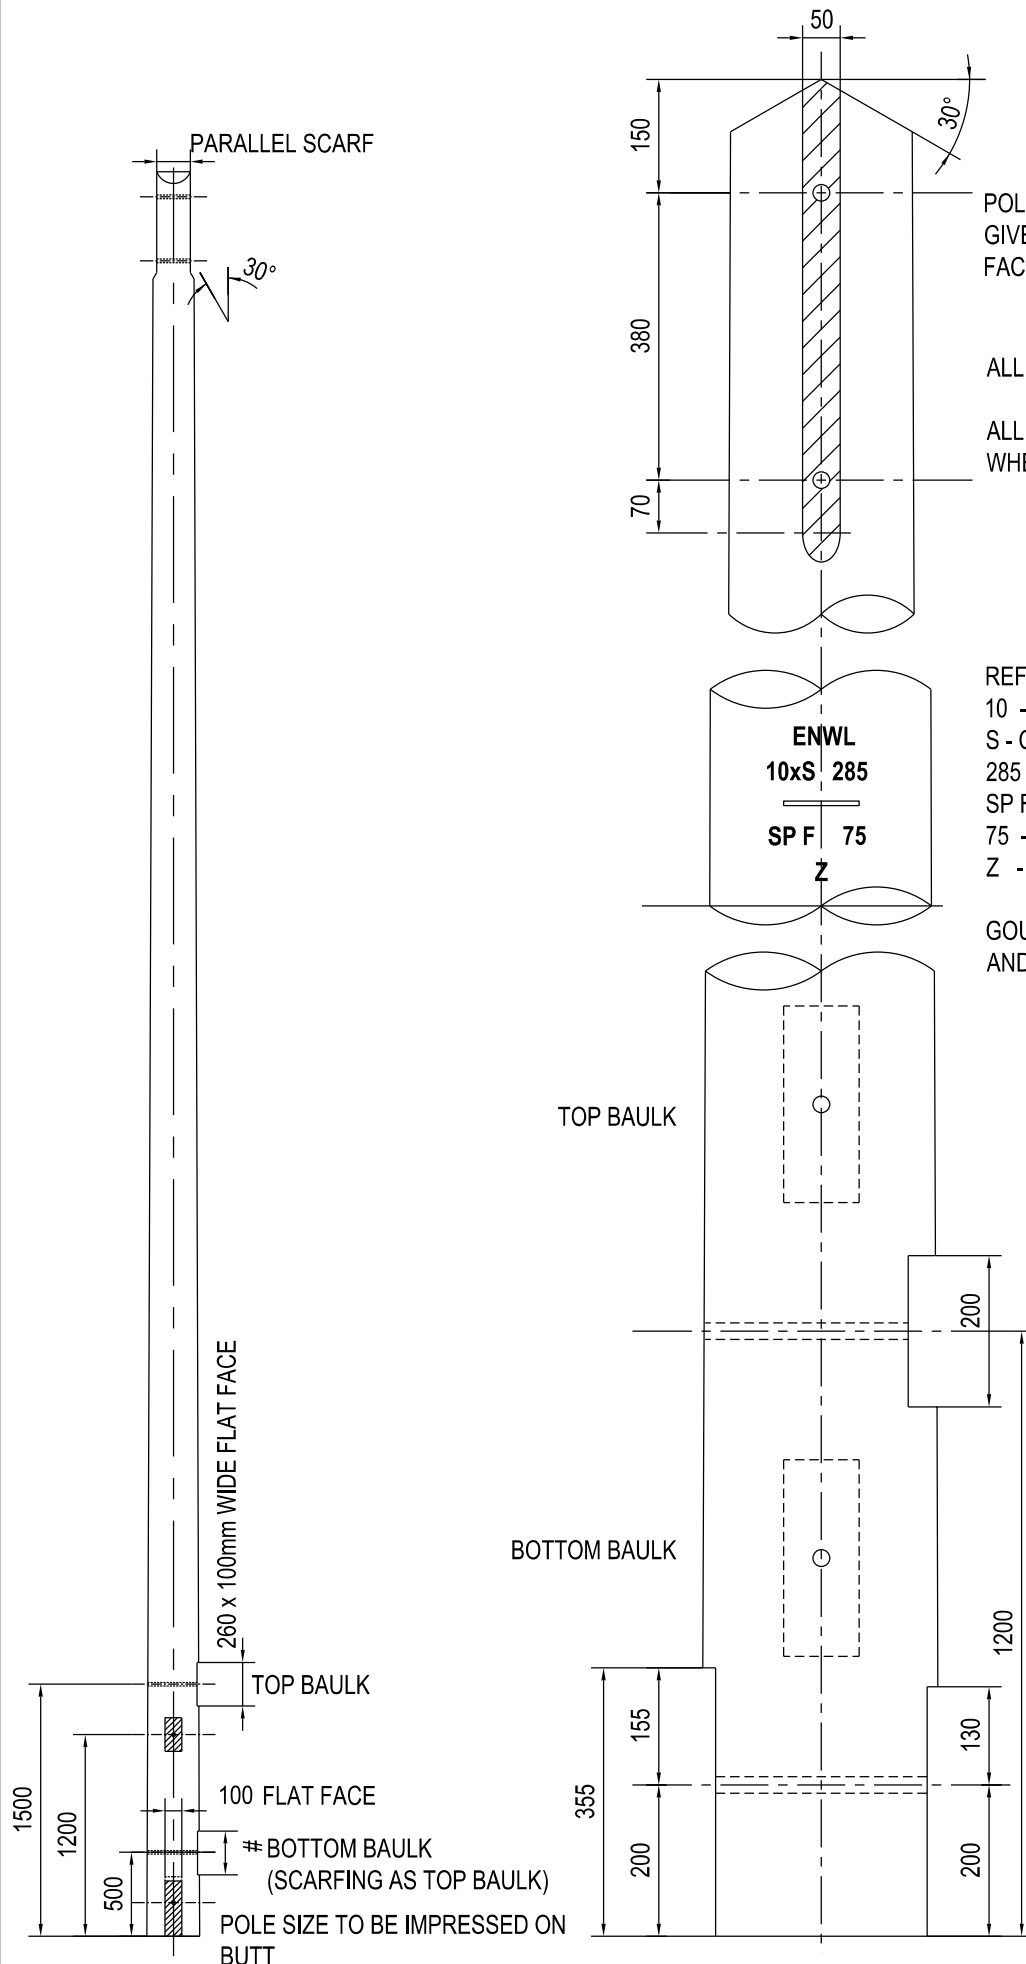

POLE SCARFED ON BOTH SIDES TO GIVE A MINIMUM 50mm WIDE FLAT FACE

ALL DRILLINGS 22mm DIAMETER

ALL DIMENSIONS IN MILLIMETRES EXCEPT WHERE OTHERWISE STATED.

REFERENCE

10 - POLE LENGTH (m)
S - CLASS OF POLE
285 - POLE DIAMETER 1.5m FROM BUTT
SP F - SCOTTS PINE (FROM FINLAND)
75 - YEAR OF CREOSOTING
Z - SUPPLIERS NAME OR MARK

GOUGE MARK 6mm WIDE x 6mm DEEP AND 3m FROM POLE BUTT.

TO BE READ IN CONJUNCTION WITH FOUNDATION DRG No. 16.13228.115 & POLE SCHEDULE 02.13228.02

Based upon ENATS Drawing No. 435003 AND GENERALLY IN ACCORDANCE WITH ENW ES400W2

LS Transmission Consultancy Limited makes no warranties, express or implied, that compliance with this drawing, or any other document issued by LSTC, would in itself be sufficient to ensure safe systems of work or operation. Users are reminded of their own duties under health and safety legislation.

LSTC

LSTC North:
Yorkshire House
York Road
Little Driffield
East Yorkshire
YO25 5XA
Tel 01377 253617
Fax 01377 259555

LSTC South:
Bourne House
Office 21
475 Godstone Road
Whyteleafe
Surrey
CR3 0BL
Tel 01883 621114

CLIENT

Electricity north west

WHITEBRK DRIVE
WHITEBRK
BLACKBURN
BB1 3HT
Tel: 01254 688917

PROJECT

KIRKBY - ORRELL

TITLE

Scarfig and Drilling - 'H' Type Intermediate and Section Poles with Backfill Type Foundations

SCALE	NTS (UNLESS OTHERWISE STATED)	DESIGNED	A4
DATE	31-10-13	CHECKED	MJ
DRAWN	SP	APPROVED	MJ
ORIGINAL SIZE	A4	DRAWING NUMBER	18_13228_173
		REV	B