


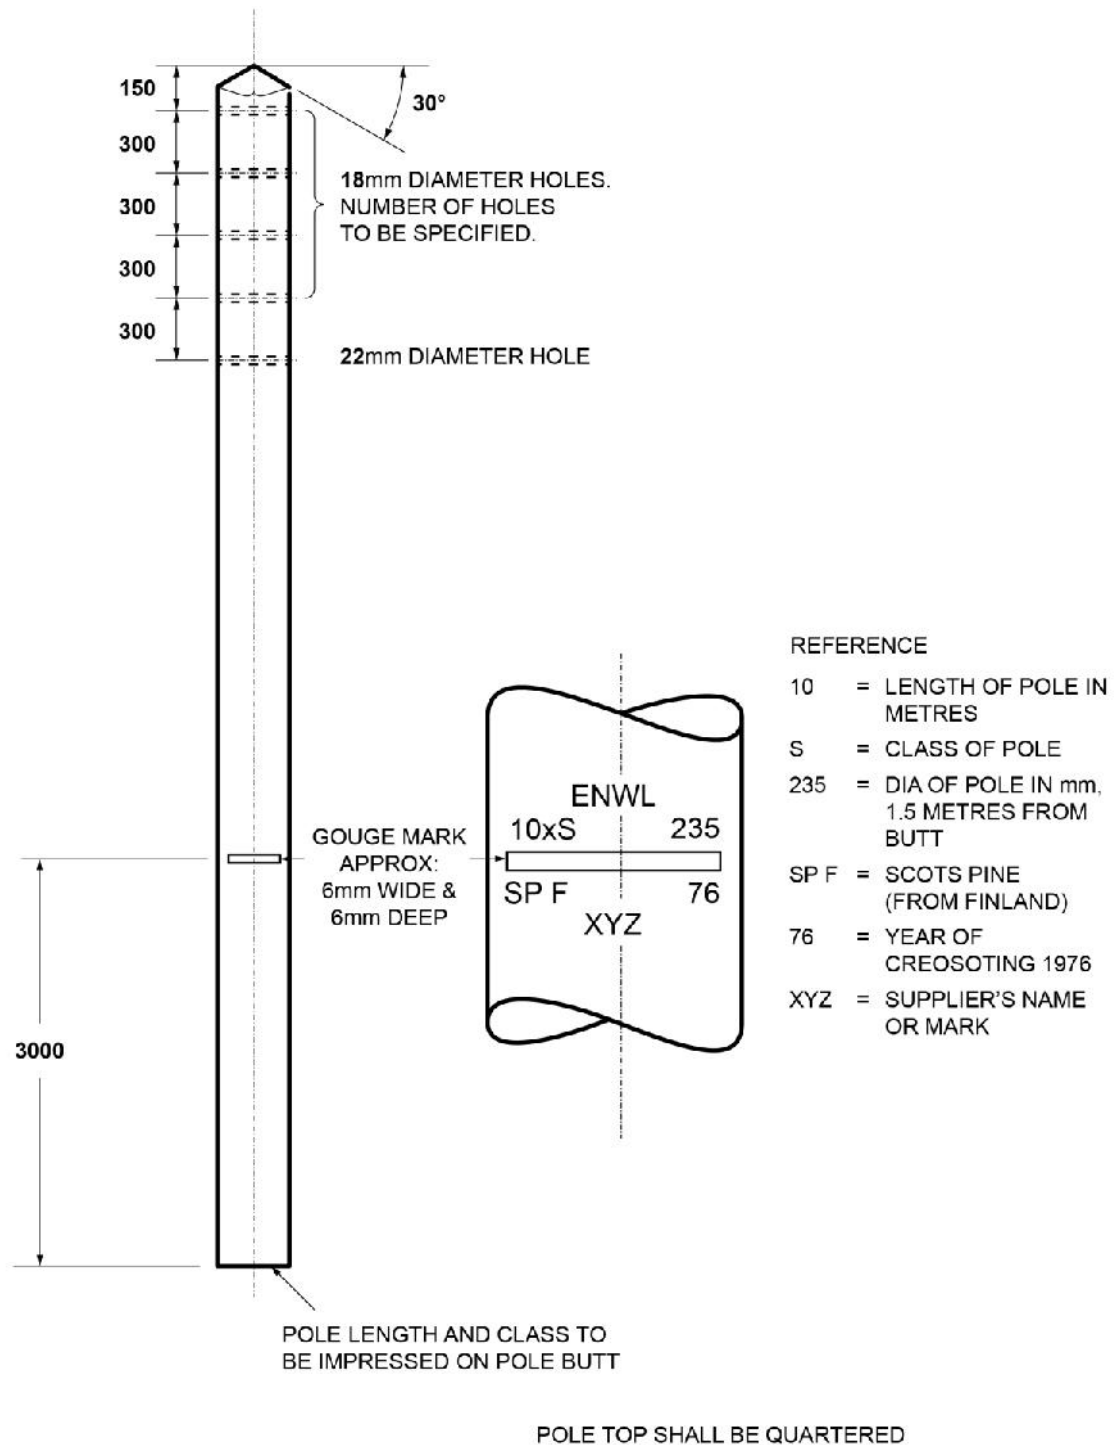

WOOD POLE FABRICATION
(LV BARE-WIRE)

Change information for this issue
N/A

Appears in
ES400W2

electricity
north west

I-400W2-FAB-004 Iss 4 sht 1 of 1

Scale: nts Auth: DMT Date: 20/01/2012