


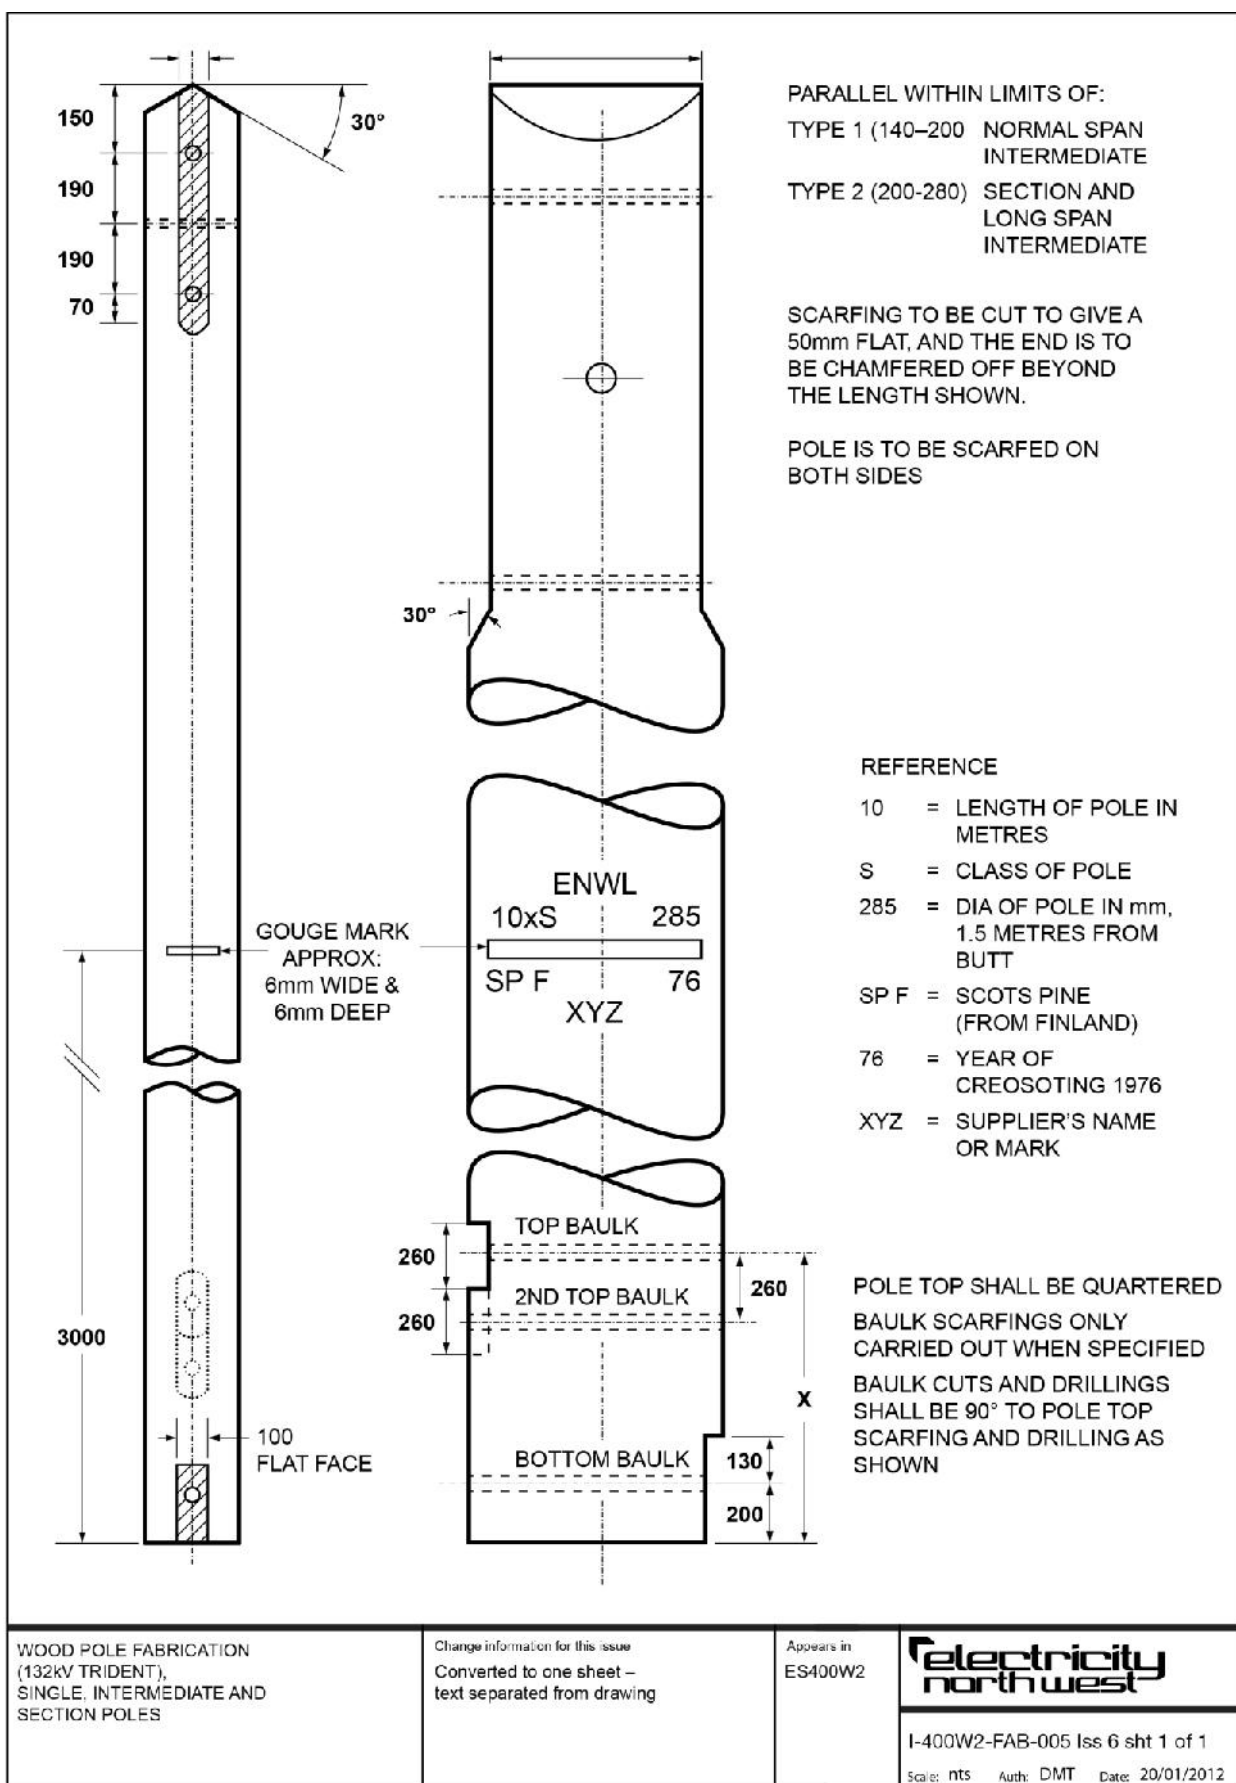

NOTES ON DRAWING I-400W2-FAB-005

1. Foundation blocks shall be selected and ordered separately.
2. The pole butt shall be cut at right angles to the vertical axis of the pole.
3. All cutting, drilling and scarfing shall be done using a template prior to preservation treatment.
4. All holes shall be 22mm diameter and drilled at right angles to the vertical centre line of the pole.
5. Pole size and grade shall be impressed on the butt.
6. To accommodate wood blocks, the scarfing shall be cut to provide a 100mm face.
7. Planting depth:

PLANTING DEPTH * m	FOUNDATION TYPES	
	A&C	B&D
	DIM X m	DIM X m
2.00	1.4	1.5
2.25	1.65	1.75
2.5	1.9	2.0
2.75	2.15	2.25
3.0	2.4	2.5
*STAYED SECTION POLE PLANTING DEPTH = 2.0 m.		