


POLE No. 435004A
REPLACES 435004 ON
GA DRG. ENATS 435013

ALL DRILLINGS ARE Ø22mm
UNLESS NOTED OTHERWISE

REFERENCE:


15.0 - POLE LENGTH (m)
375 - POLE Ø 1.5m FROM BUTT
IF - IMPORTED FIR
14 - YEAR OF CREOSOTING
XYZ - SUPPLIER'S MARK

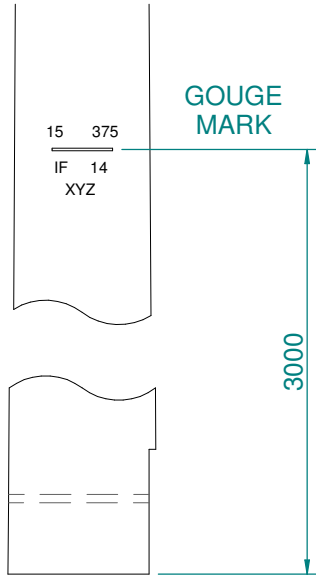

GENERAL NOTES:

- ALL DIMENSIONS ARE IN MILLIMETRES (mm) UNLESS NOTED OTHERWISE.
- WOOD POLE SCARFING AND DRILLING DETAILS ARE DISPLAYED FOR 2 OF 3 DIFFERENT TYPES OF WOOD POLE REQUIRED FOR 6-POLE TERMINAL STRUCTURE. FOR THIRD WOOD POLE TYPE, SEE ENATS DRAWING No. 435005.

IMPORTANT NOTE:
REMOVE TOP 500mm FROM 11.0m POLE SUPPLIED
TO LEAVE 10.5m OVERALL POLE LENGTH BEFORE
DRILLING AND SCARFING IS PERFORMED

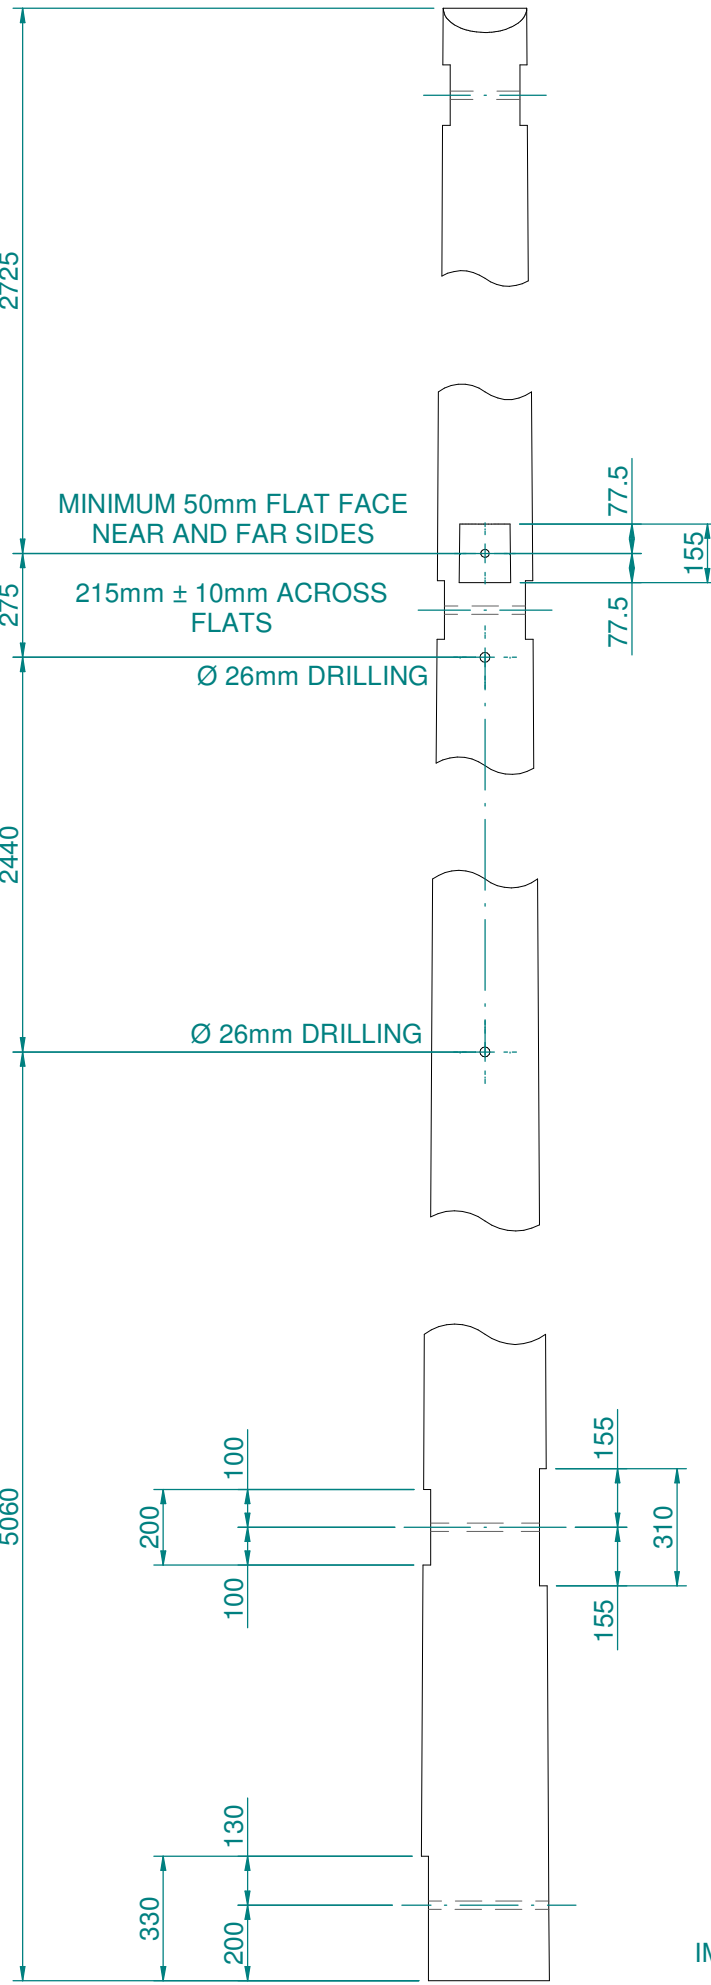


POLE SIZE TO BE
IMPRESSED ON BUTT

DISCONNECTER SUPPORT POLE


ALL DRILLINGS ARE Ø22mm
UNLESS NOTED OTHERWISE

REFERENCE:

11.0 - POLE LENGTH (m)
320 - POLE Ø 1.5m FROM BUTT
IF - IMPORTED FIR
14 - YEAR OF CREOSOTING
XYZ - SUPPLIER'S MARK

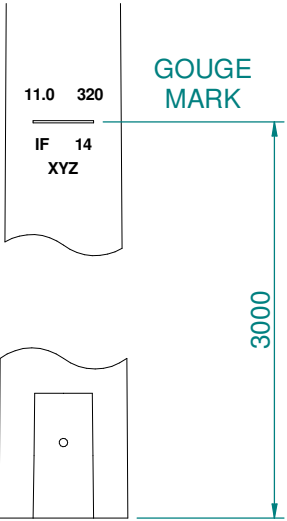

IF IN DOUBT ASK ENGINEER / DESIGN OFFICE

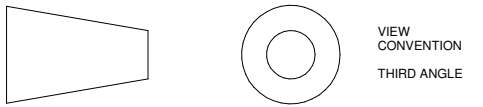

THIS DRAWING IS THE EXCLUSIVE PROPERTY OF LSTC LTD THE CONTENTS OF THE DRAWING MUST BE TREATED AS STRICTLY CONFIDENTIAL AND MUST NOT BE DISCLOSED TO ANY THIRD PARTY WITHOUT LSTC LTD WRITTEN CONSENT. USE ONLY FOR THE PURPOSE FOR WHICH IT WAS LOANED. NO COPYING OR REPRODUCING. RETURN ON REQUEST.

LS TRANSMISSION CONSULTANCY LIMITED MAKES NO WARRANTIES, EXPRESS OR IMPLIED, THAT COMPLIANCE WITH THIS DRAWING, OR ANY OTHER DOCUMENT ISSUED BY LSTC, WOULD IN ITSELF BE SUFFICIENT TO ENSURE SAFE SYSTEMS OF WORK OR OPERATION. USERS ARE REMINDED OF THEIR OWN DUTIES UNDER HEALTH AND SAFETY LEGISLATION.

CLIENT



PROJECT

LYNEHAM P.V. FARM

TITLE

WOOD POLE SCARFING DRAWING
FOR NEW WOOD POLES
REQUIRED FOR 6-POLE TERMINAL STRUCTURE

SCALE
1:20

TOTAL No. OF
SHEETS
1

DESIGNED
IS

DATE
09/09/2015

CHECKED
RF

DRAWN
MA

APPROVED
GY

ORIGINAL
SIZE
A2

DRAWING NUMBER
18_15098_10

REV
A



LSTC North:

Yorkshire House
York Road
Little Driffield
East Yorkshire
YO25 5XA
Tel 01377 253617
Fax 01377 259555

LSTC South:

Bourne House
Office 21
475 Godstone
Road
Whyteleafe
Surrey
CR3 0BL
Tel 01883 621114