
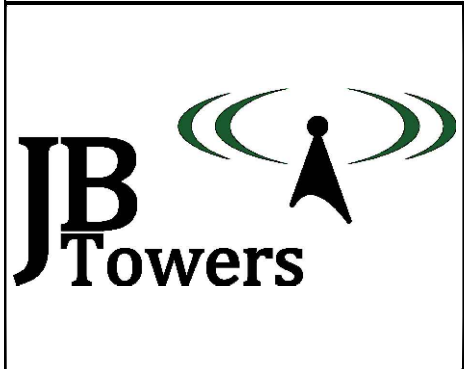


DRAWING ISSUE SHEET

[illegible]

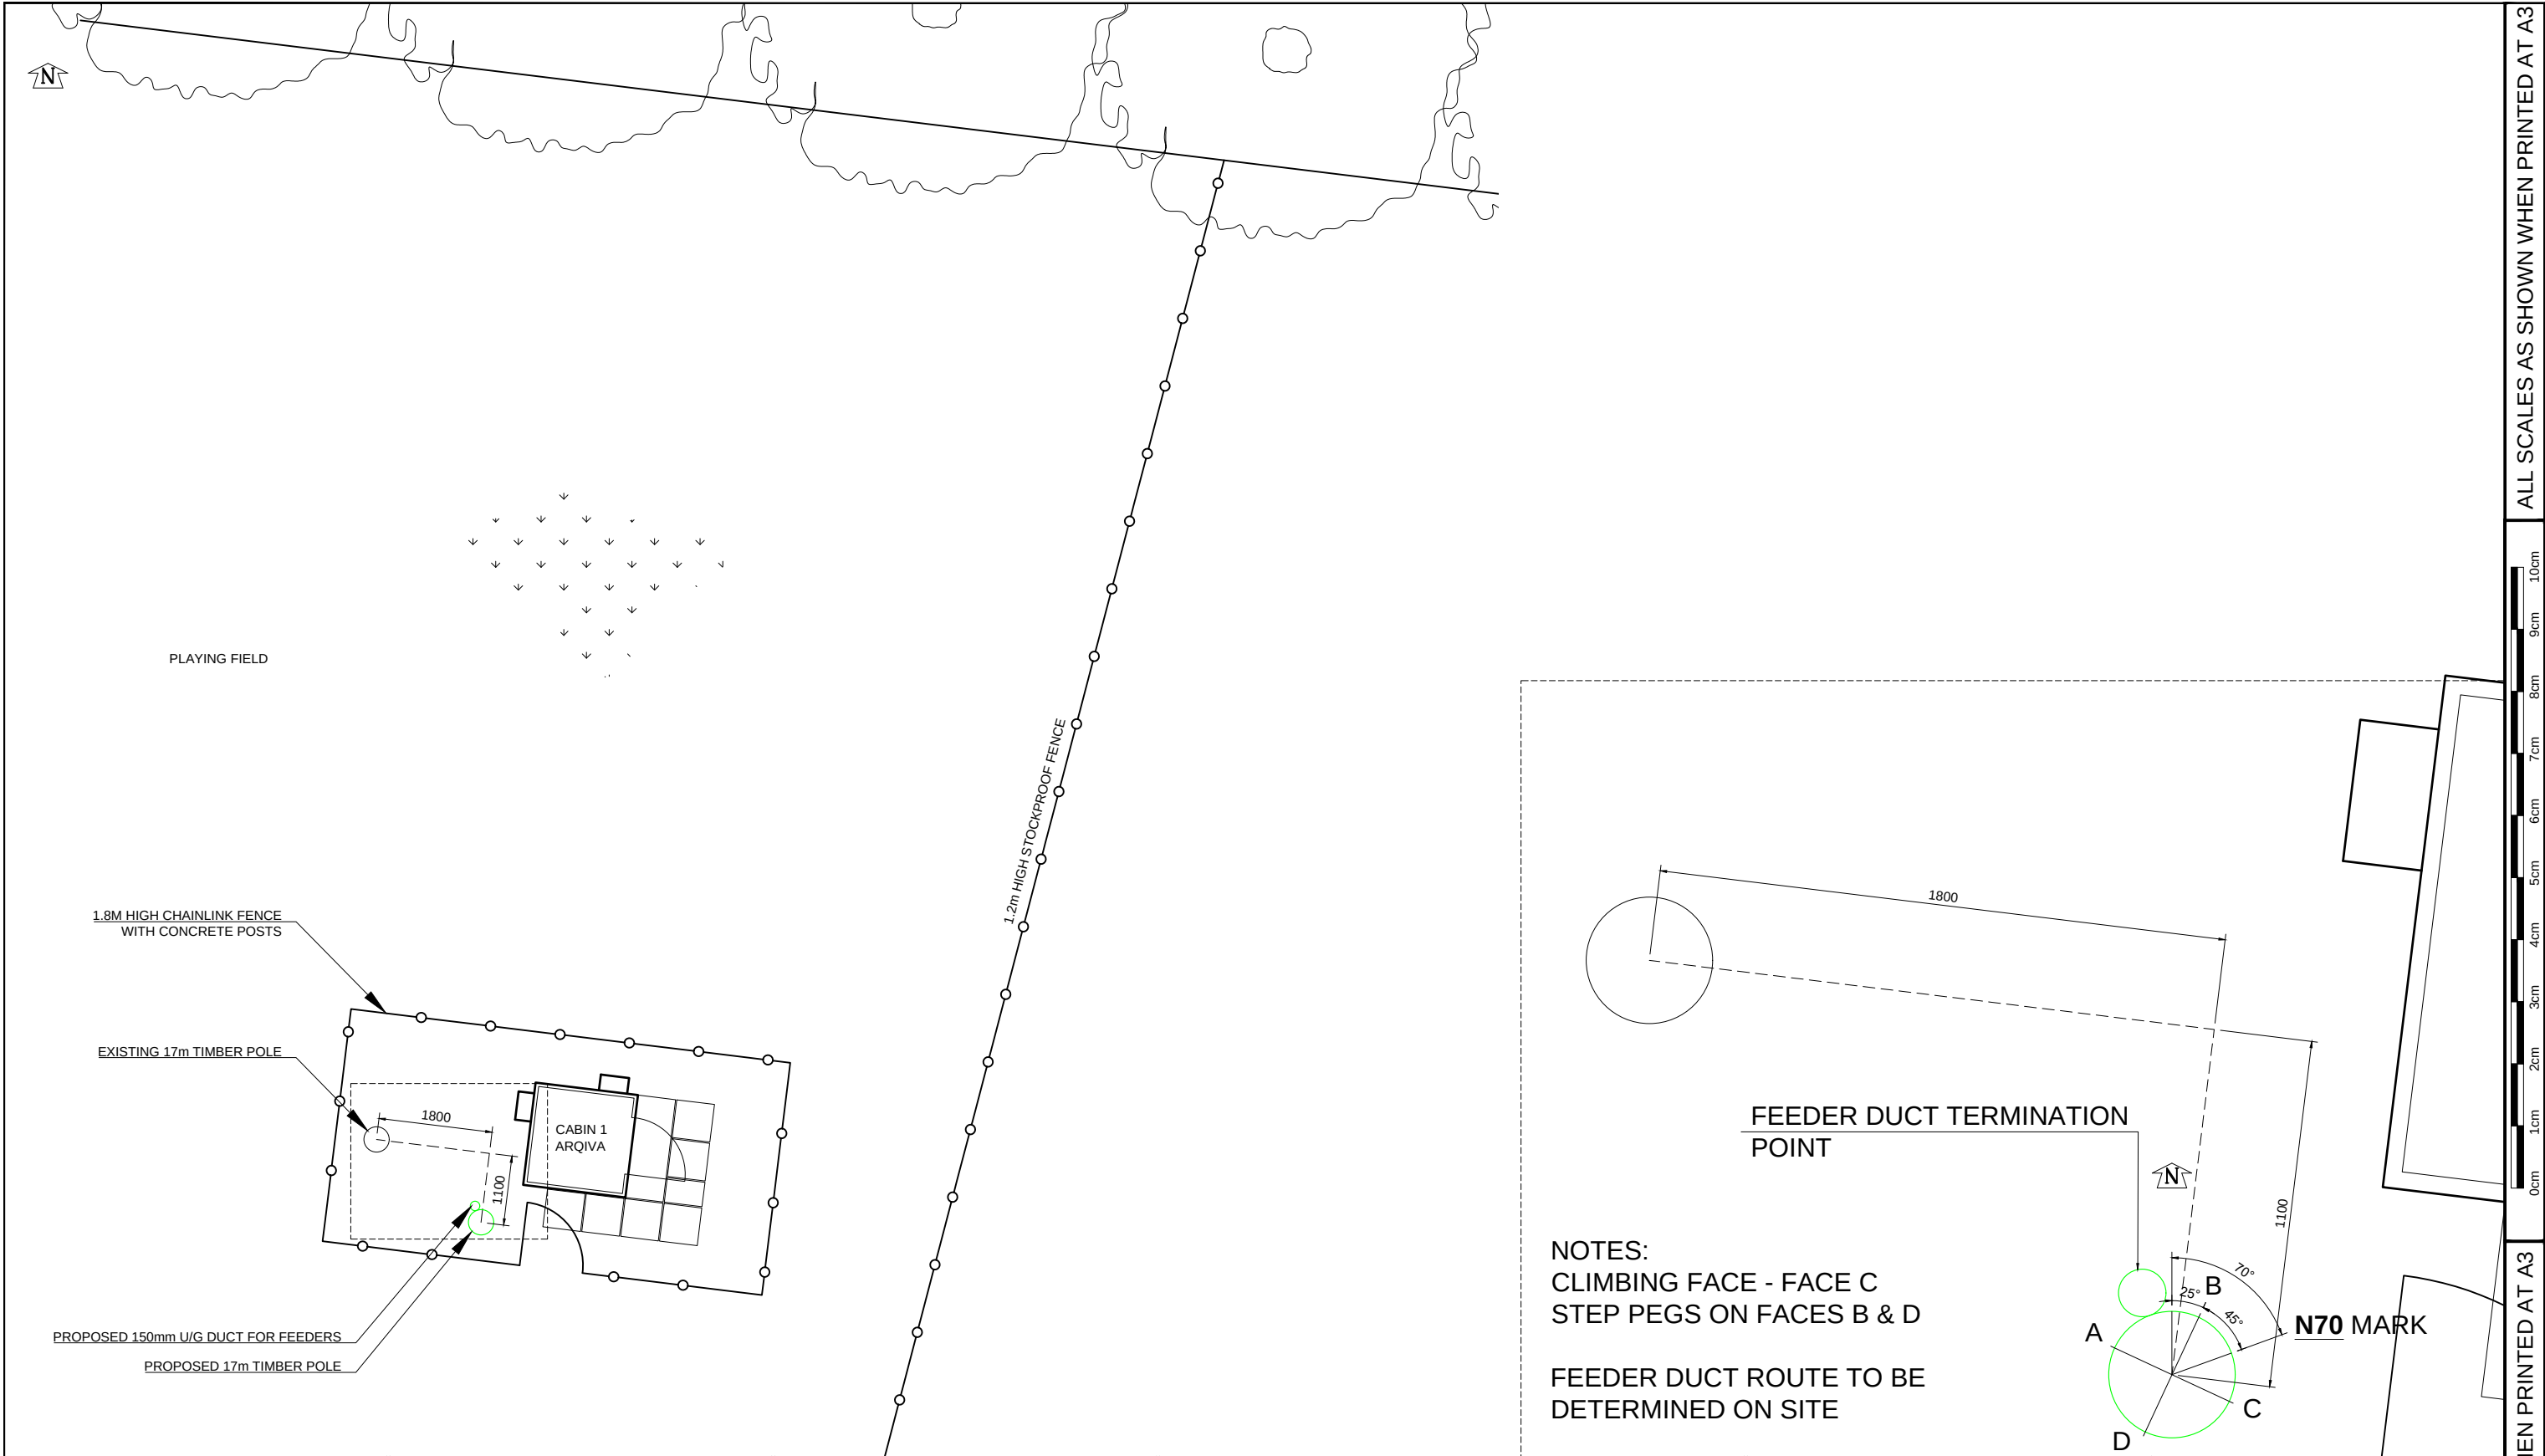


01	FIRST ISSUE			AM	14/02/20
REV	REV			BY	DATE
SCALE AS SHOWN		DRAWN	AM	CHECKED	MP
WHEN PRINTED AT A3		DATE	14/02/20	DATE	14/02/20
				APPROVED	JBT
				DATE	14/02/20
ALL DIMENSIONS IN mm UNLESS OTHERWISE STATED. THIS DRAWING TO BE READ IN CONJUNCTION WITH OTHER RELEVANT DRAWINGS.					

TITLE
BOW STREET
SITE PLAN

SITE ADDRESS		
TIRYMYNACH		
COMMUNITY COUNCIL		
PLAYING FIELDS		
ABERYSTWTH		
CEREDIGION		
SY24 5BW		
ARQIVA REF.	DRG No.	REV
140234	100	01

ALL SCALES AS SHOWN WHEN PRINTED AT A3

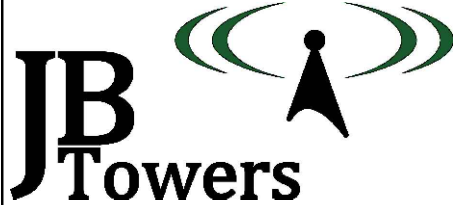

02	PERMANENT STEPS REARRANGED			AM	24/02/20
01	FIRST ISSUE			AM	14/02/20
REV	REV			BY	DATE
SCALE AS SHOWN WHEN PRINTED AT A3		DRAWN	AM	CHECKED	MP
		DATE	14/02/20	DATE	14/02/20
				APPROVED	JBT
				DATE	14/02/20
ALL DIMENSIONS IN mm UNLESS OTHERWISE STATED. THIS DRAWING TO BE READ IN CONJUNCTION WITH OTHER RELEVANT DRAWINGS.					

TITLE

BOW STREET

GENERAL ARRANGEMENT

SHEET 1 OF 3

SITE ADDRESS

TIRYMYNACH

COMMUNITY COUNCIL

PLAYING FIELDS

ABERYSTWTH

CEREDIGION

SY24 5BW

ARQIVA REF.



140234

DRG No.

200

REV

02

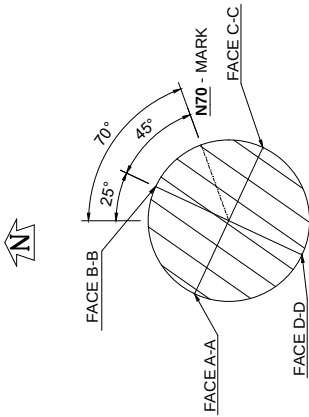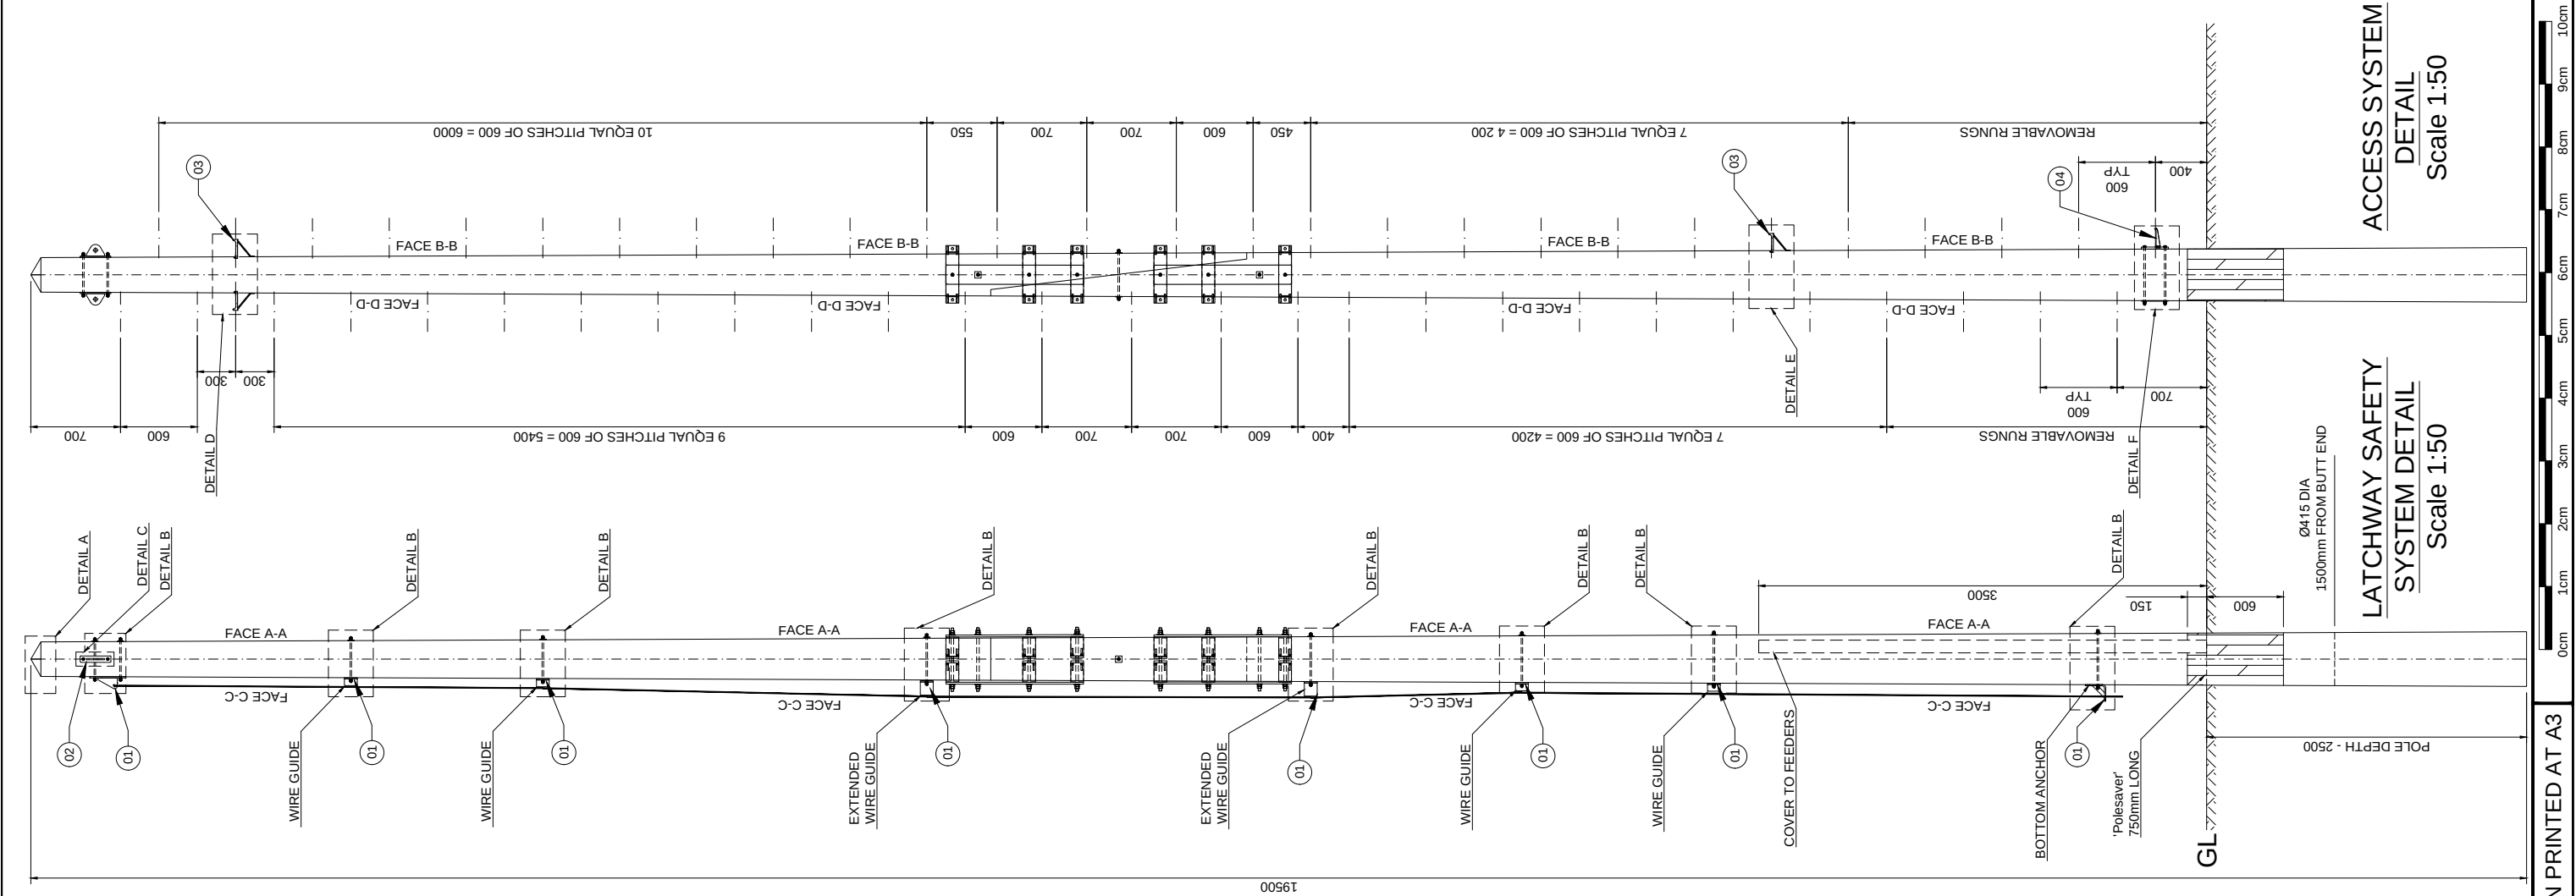

POLE ORIENTATION

Scale 1:20

NOTES

1. SEE DRAWING 305 FOR PARTS LIST
2. ALL BOLTS TO BE CUT ON SITE TO EXTEND MAX 10mm BEYOND THE NUT WHEN TIGHTENED UNO.
3. ALL SITE DRILLED HOLE/CUT ENDS TO BE TREATED WITH METALUX 70-40 ZINC PASTE FOLLOWED BY 1 COAT OF 7-42 ZINC ALU OR 70-16 ALUMINIUM SPRAY

TIMBER POLE

1. POLE TO BE SUPPLIED IN ACCORDANCE WITH BS EN14229 & SHALL HAVE MIN. CHARACTERISTIC BENDING STRENGTH OF 30N/mm2 & MIN. YOUNGS MODULUS (PARALLEL TO GRAIN) OF 10kN/mm2.
2. MARKINGS ON FINISHED POLE SHALL BE AT 4m FROM BUTT AND COMPLY WITH BS EN 14229 UNO
3. AS FAR AS PRACTICABLE ALL CUTTING, SCARFING & DRILLING TO BE DONE BEFORE CREOSOTING. IF NOT ALL CUT, DRILLED & SCARFED SURFACES TO BE COATED WITH A MIXTURE OF CREOSOTE & TAR.
4. POLE TO BE PRESSURE IMPREGNATED WITH CREOSOTE IN ACCORDANCE WITH BS EN 14229
5. MINIMUM DIAMETERS
TOP - Ø205mm
BOTTOM - Ø430mm
6. 19.5m LONG POLE TO BE SOURCED BY TRIMMING 20m LONG POLE BY 0.5m AT THE TOP

SPLICE CONNECTION

1. THE CONTACT SURFACES AND ALL THROUGH HOLES OF THE TIMBER POLE SPLICE ARE TO BE TREATED LIBERALLY WITH SINGLE COAT OF TIMBER COMPATIBLE BITUMINOUS PAINT (E.G. BIRD BRAND BLACK BITUMINOUS PAINT OR SIMILAR APPROVED PRODUCT).
2. PAINT TO BE APPLIED JUST BEFORE SPLICING THE TWO PARTS
3. ANY DISTURBED SURFACES SHALL HAVE THEIR WATERPROOFING REPAIRED WITH SINGLE COAT OF TIMBER COMPATIBLE BITUMINOUS PAINT (E.G. BIRD BRAND BLACK BITUMINOUS PAINT OR SIMILAR APPROVED PRODUCT).

PLANTING

1. CAT SCANNER IS TO BE USED IN ORDER TO CONFIRM THE POSITIONS OF BURIED SERVICES.
2. 'Pema-Soil Stabiliser' OR A SIMILAR APPROVED SHOULD BE USED IN ACCORDANCE WITH THE MANUFACTURER'S RECOMMENDATION.
3. ANY MATERIAL USED FOR BACK-FILLING IS TO BE OF EQUAL OR BETTER QUALITY THAN THE EXCAVATED MATERIAL.
4. ALL BACK-FILLING MATERIAL IS TO BE PLACED AND COMPACTED IN 150mm THICK LAYERS.
5. TIMBER POLE TO BE PLANTED WITH N70 MARKING AT 3.5m FROM BUTT FACING 70° FROM NORTH (CLOCKWISE)

ACCESS SYSTEM


DETAIL

Scale 1:50

LATCHWAY SAFETY

SYSTEM DETAIL

Scale 1:50

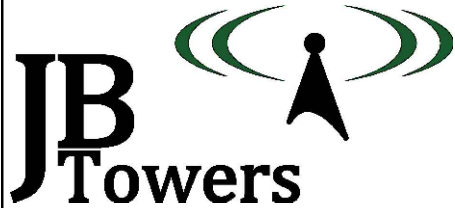

01	FIRST ISSUE						AM	14/02/20	
REV	REV						BY	DATE	
SCALE AS SHOWN		DRAWN	AM	CHECKED	MP	APPROVED		JBT	
WHEN PRINTED AT A3		DATE	14/02/20	DATE	14/02/20	DATE		14/02/20	
ALL DIMENSIONS IN mm UNLESS OTHERWISE STATED. THIS DRAWING TO BE READ IN CONJUNCTION WITH OTHER RELEVANT DRAWINGS.									

TITLE

BOW STREET

GENERAL ARRANGEMENT

SHEET 2 OF 3

SITE ADDRESS

TIRYMYNACH

COMMUNITY COUNCIL

PLAYING FIELDS

ABERYSTWTH

CEREDIGION

SY24 5BW

ARQIVA REF.


140234

DRG No.

200

REV


01

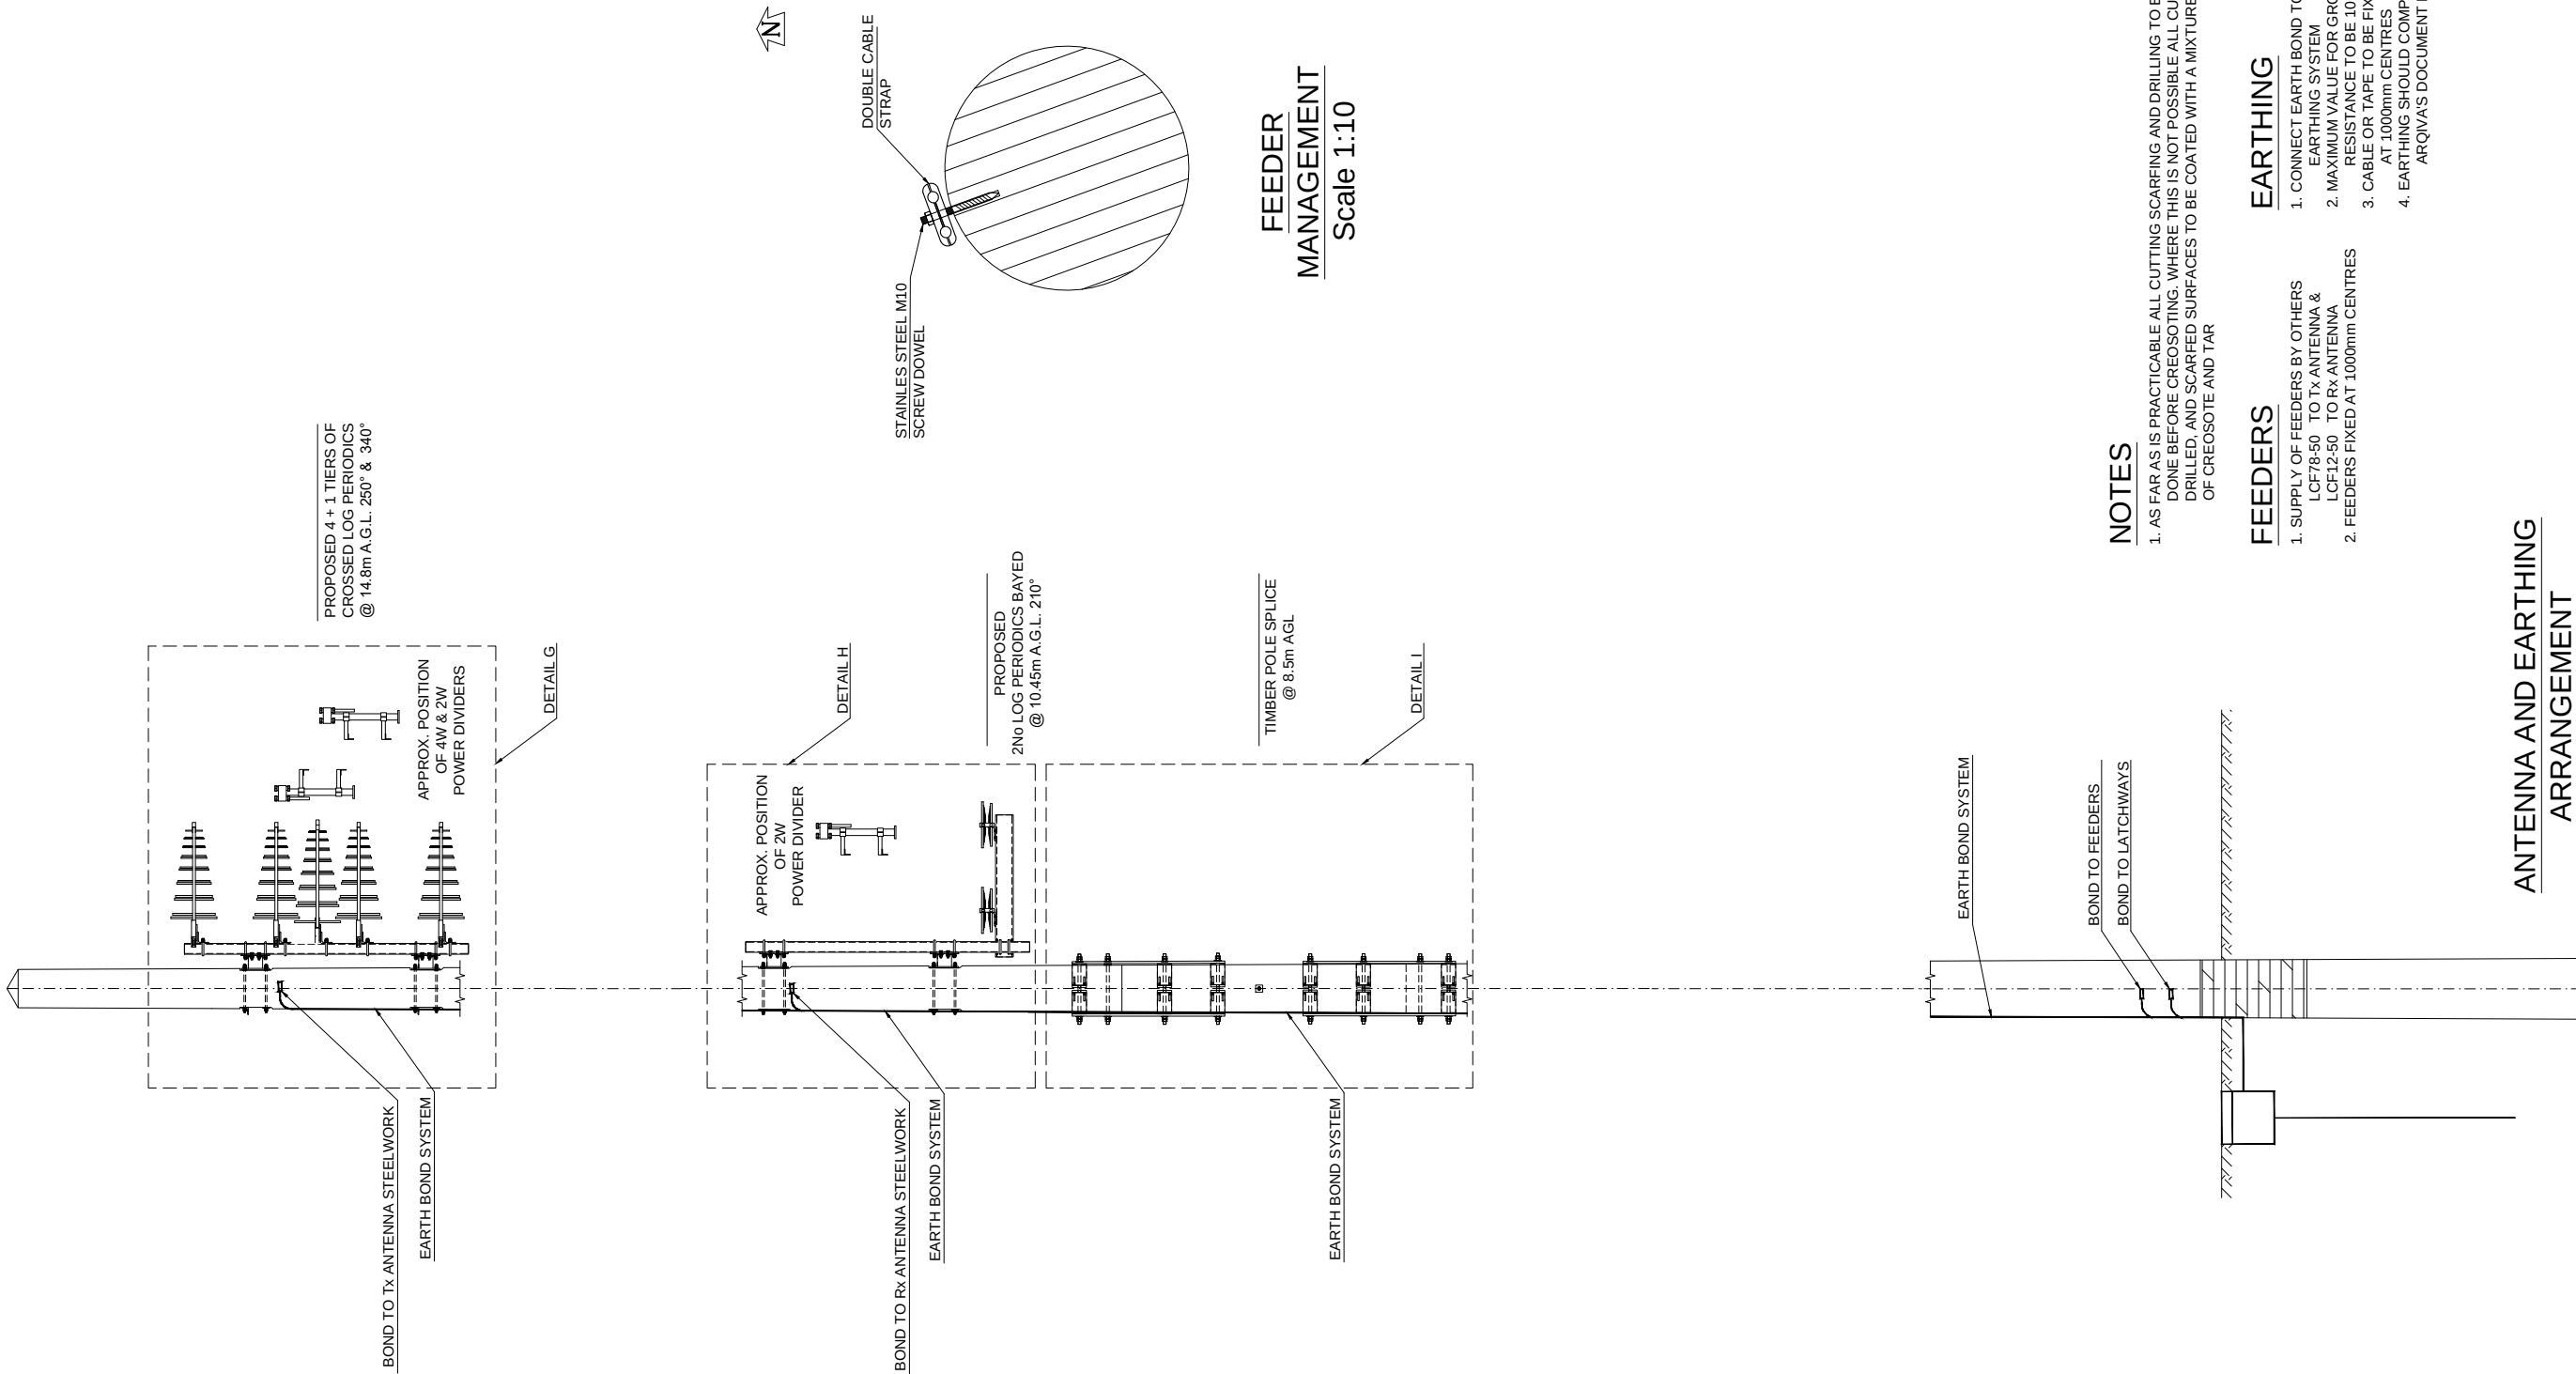

ALL SCALES AS SHOWN WHEN PRINTED AT A3




ALL SCALES AS SHOWN WHEN PRINTED AT A3

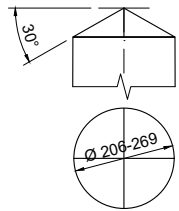


- NOTES:
1. A SINGLE COAT OF TIMBER COMPATIBLE BITUMINOUS PAINT (E.G. BIRD BRAND BLACK BITUMINOUS PAINT OR SIMILAR APPROVED PRODUCT) TO BE APPLIED TO THE UPPER SURFACES AT THE TOP OF THE POLE.
 2. PAINT TO BE APPLIED ON SITE JUST BEFORE ERECTION
- FORM: 4 WAY PYRAMID / CONE


DETAIL A - TIMBER POLE TOP
Scale 1:20

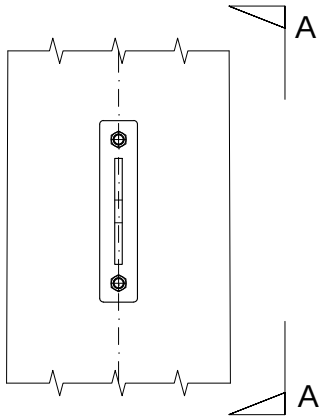


DETAIL C - FALL ARREST
ATTACHMENT POINT
Scale 1:10

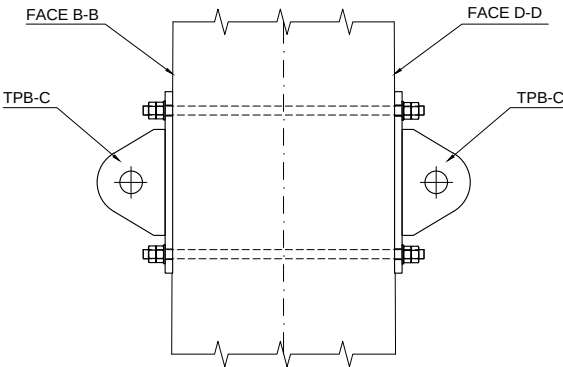

VIEW A-A
Scale 1:10

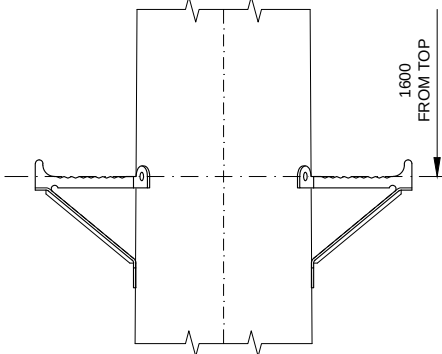


DETAIL D - ANTENNA
ACCESS CLIMBING STEP
Scale 1:10

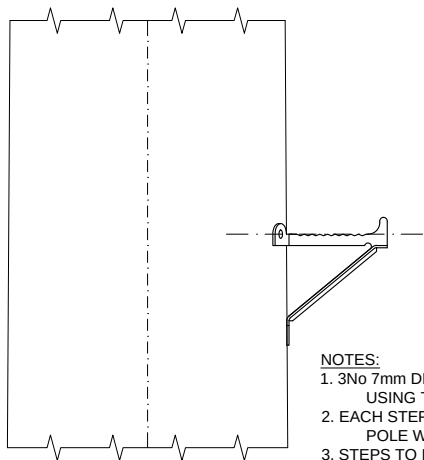


DETAIL E - PERMANENT
CLIMBING STEPS
Scale 1:10


- NOTES:
1. 3No 7mm DIA 70mm LONG PILOT HOLES TO BE DRILLED USING THE STEP AS A TEMPLATE
 2. EACH STEP SHOULD BE FIXED TO THE TIMBER POLE WITH 3No 10mm COACH SCREWS 75mm LONG
 3. STEPS TO BE INSTALLED ON FACES B-B & D-D ONLY

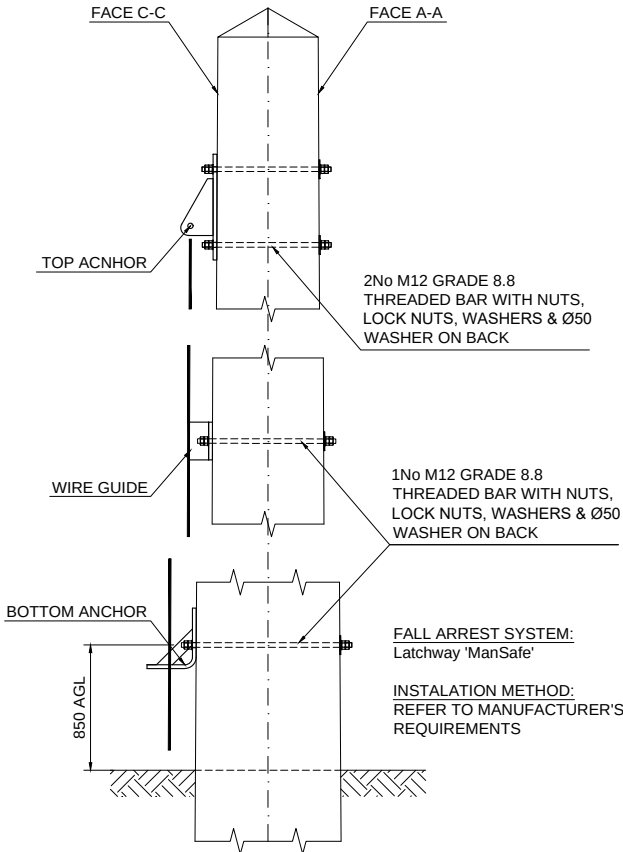

DETAIL B - FALL ARREST SYSTEM
Scale 1:20

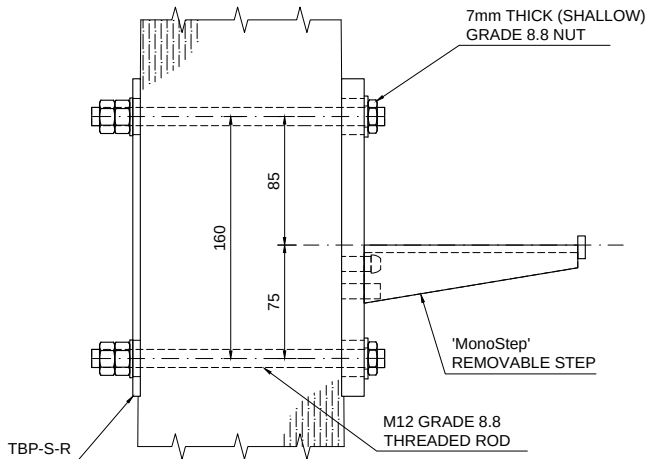

DETAIL F - REMOVABLE
CLIMBING STEPS
Scale 1:5

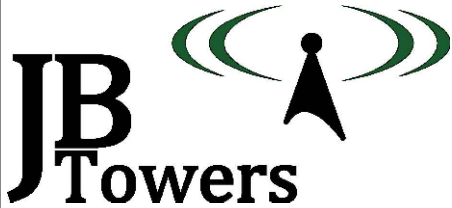

01	FIRST ISSUE	AM	14/02/20
REV	REV	BY	DATE
SCALE AS SHOWN WHEN PRINTED AT A3	DRAWN DATE	AM 14/02/20	CHECKED DATE
	MP 14/02/20	APPROVED DATE	JBT 14/02/20
ALL DIMENSIONS IN mm UNLESS OTHERWISE STATED. THIS DRAWING TO BE READ IN CONJUNCTION WITH OTHER RELEVANT DRAWINGS.			

TITLE
BOW STREET
GENERAL ARRANGEMENT
SHEET 3 OF 3

SITE ADDRESS
TIRYMYNACH
COMMUNITY COUNCIL
PLAYING FIELDS
ABERYSTWTH
CEREDIGION
SY24 5BW

ARQIVA REF.
140234


DRG No.
200

REV
01

ALL SCALES AS SHOWN WHEN PRINTED AT A3



ALL SCALES AS SHOWN WHEN PRINTED AT A3

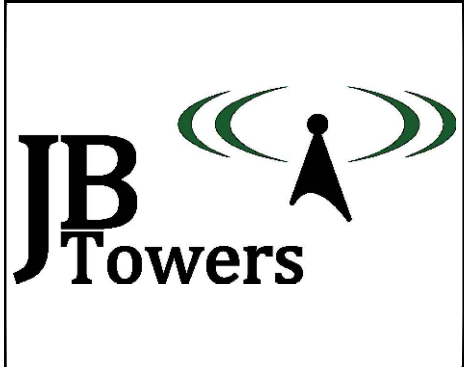

01	FIRST ISSUE							AM	14/02/20
REV	REV							BY	DATE
SCALE AS SHOWN WHEN PRINTED AT A3		DRAWN AM		CHECKED MP		APPROVED JBT			
		DATE 14/02/20		DATE 14/02/20		DATE 14/02/20			
ALL DIMENSIONS IN mm UNLESS OTHERWISE STATED. THIS DRAWING TO BE READ IN CONJUNCTION WITH OTHER RELEVANT DRAWINGS.									

TITLE


BOW STREET


TIMBER POLE HOLE SET OUT

SHEET 1 OF 2

SITE ADDRESS
TIRYMYNACH
COMMUNITY COUNCIL
PLAYING FIELDS
ABERYSTWTH
CEREDIGION
SY24 5BW

ARQIVA REF. 140234	DRG No. 201	REV 01
-----------------------	----------------	-----------

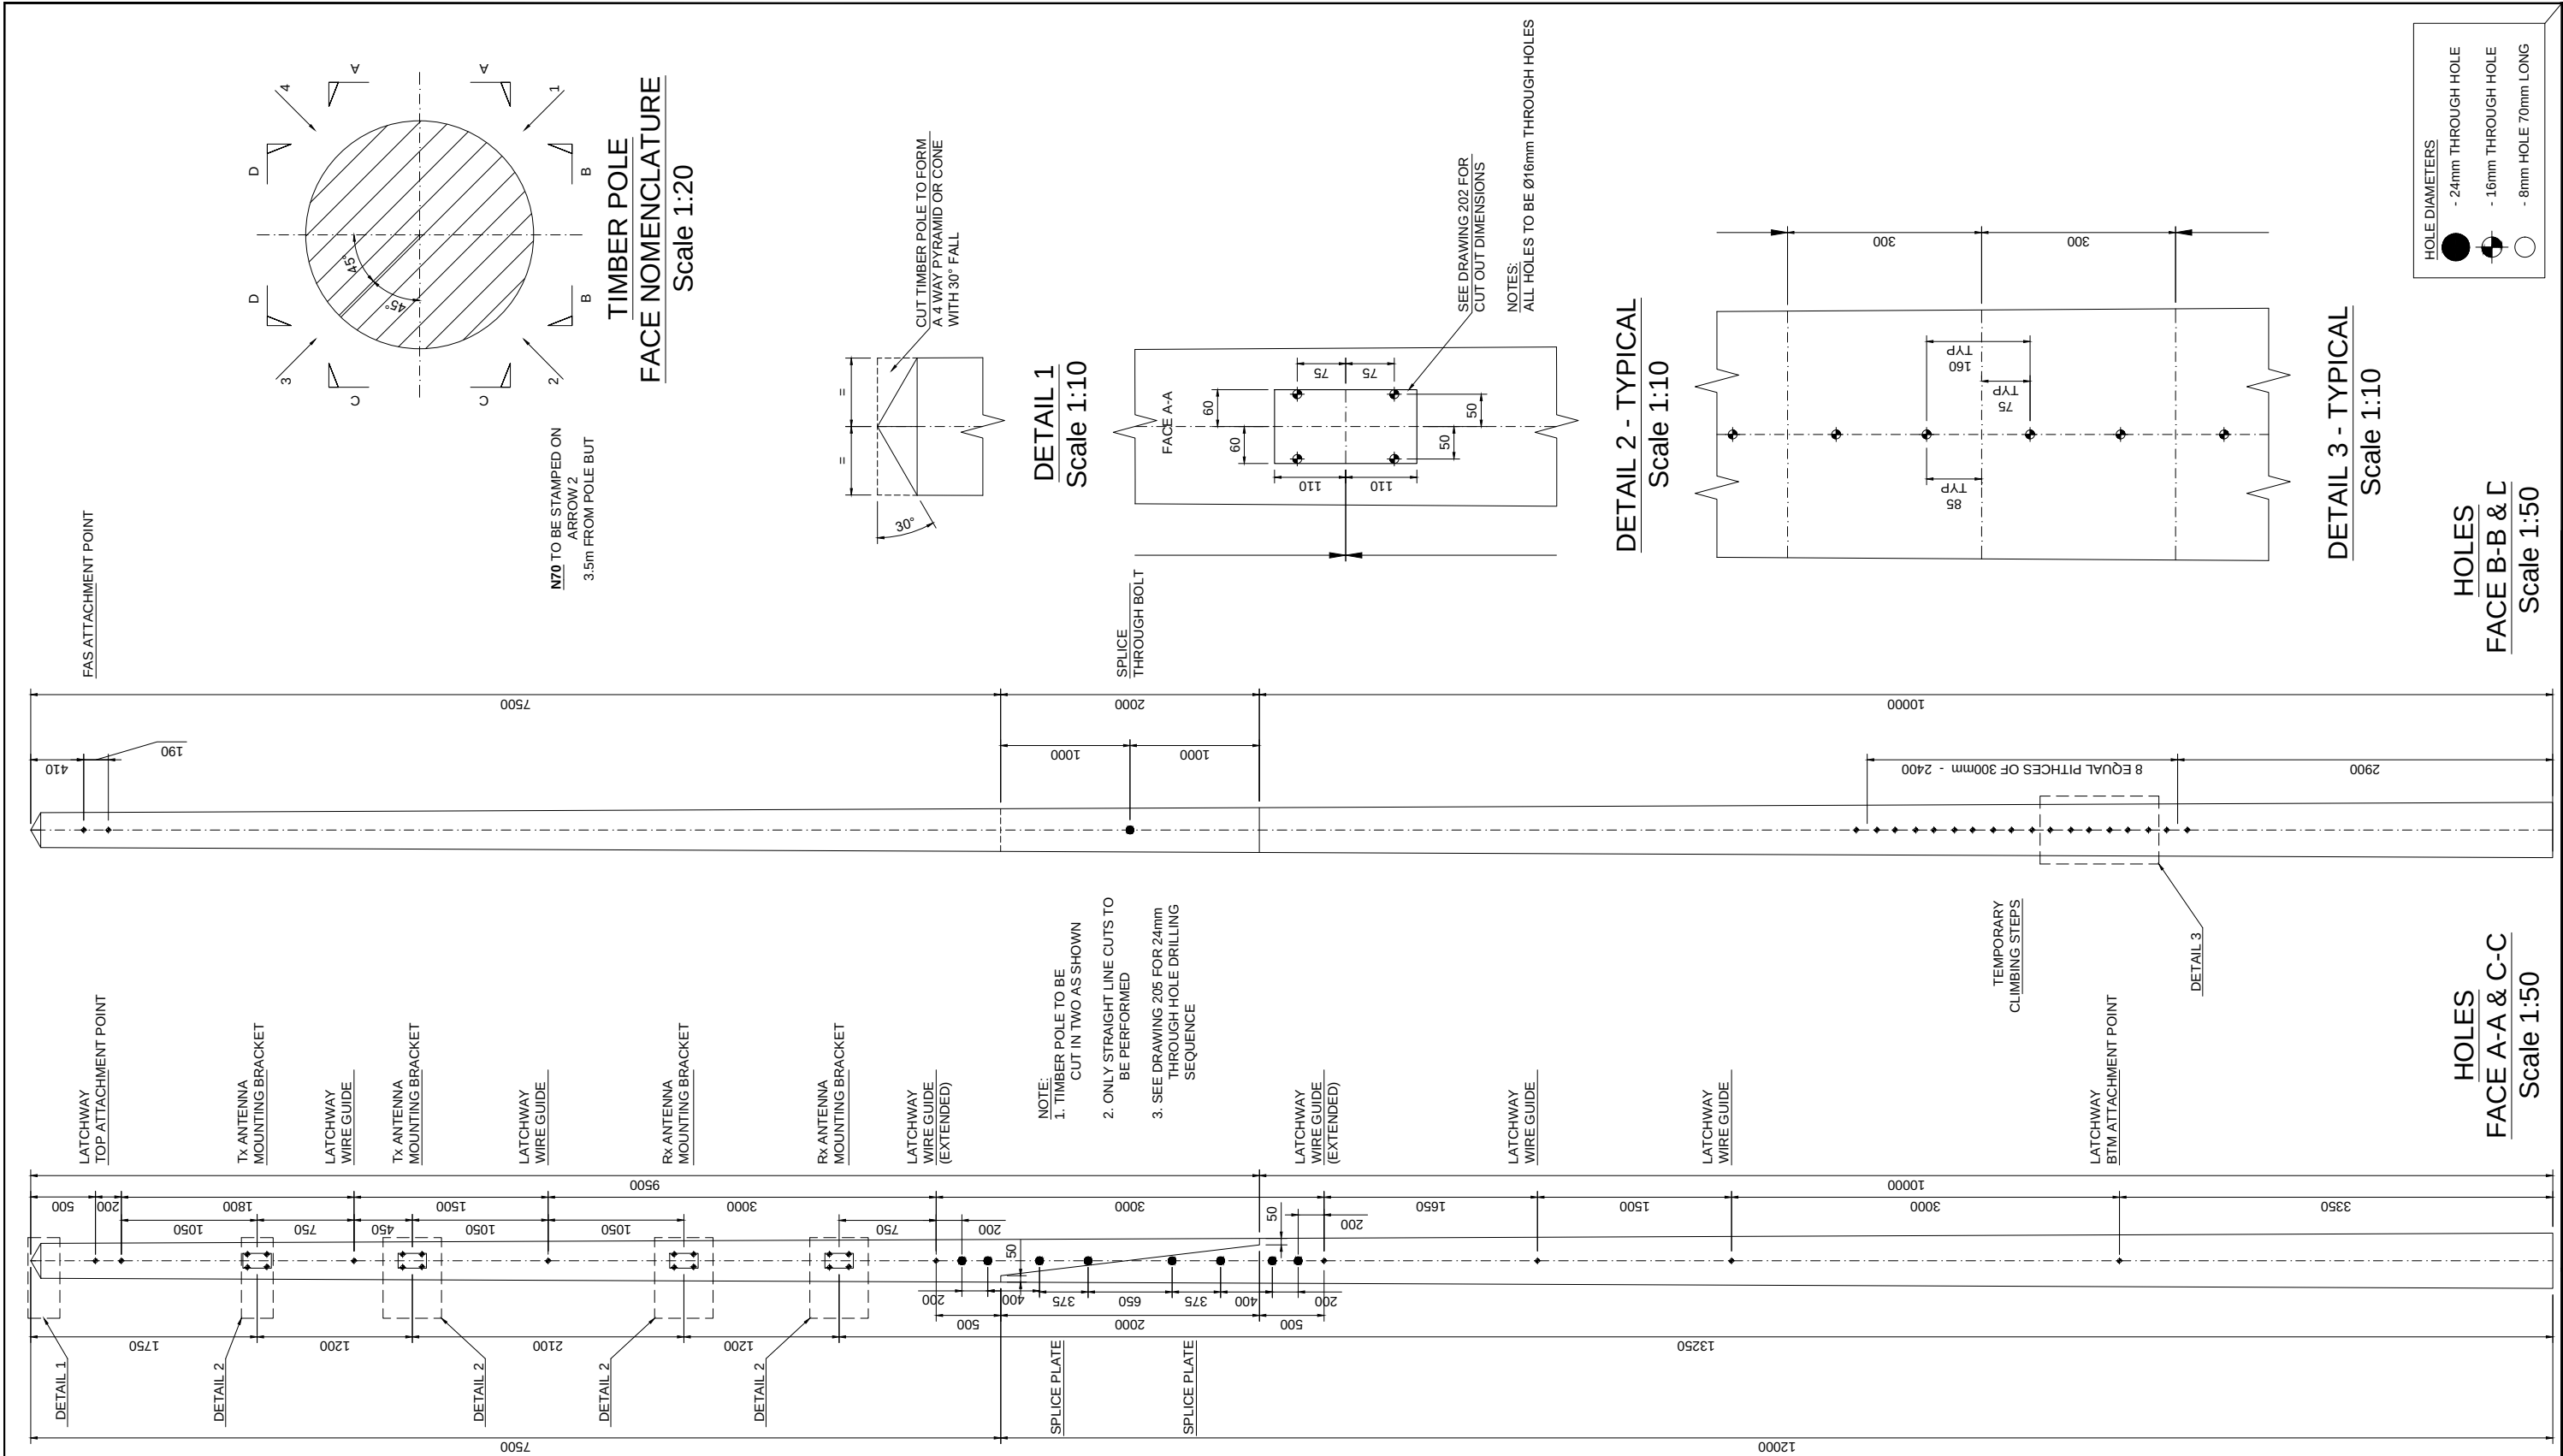DRG No.
201REV
01

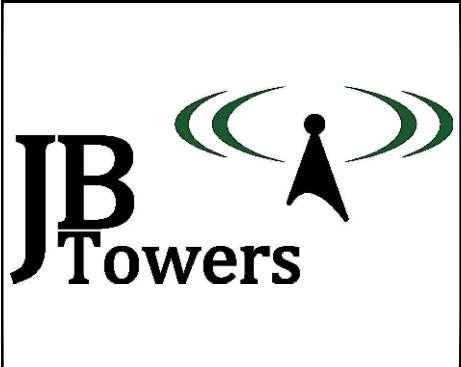

01	FIRST ISSUE			AM	14/02/20
REV	REV			BY	DATE
SCALE AS SHOWN		DRAWN	AM	CHECKED	MP
WHEN PRINTED AT A3		DATE	14/02/20	DATE	14/02/20
		APPROVED	JBT	DATE	14/02/20
ALL DIMENSIONS IN mm UNLESS OTHERWISE STATED. THIS DRAWING TO BE READ IN CONJUNCTION WITH OTHER RELEVANT DRAWINGS.					

TITLE

BOW STREET

TIMBER POLE HOLE SET OUT

SHEET 2 OF 2

SITE ADDRESS

TIRYMYNACH

COMMUNITY COUNCIL

PLAYING FIELDS

ABERYSTWTH

CEREDIGION

SY24 5BW

ARQIVA REF.


140234

DRG No.


201

REV

01

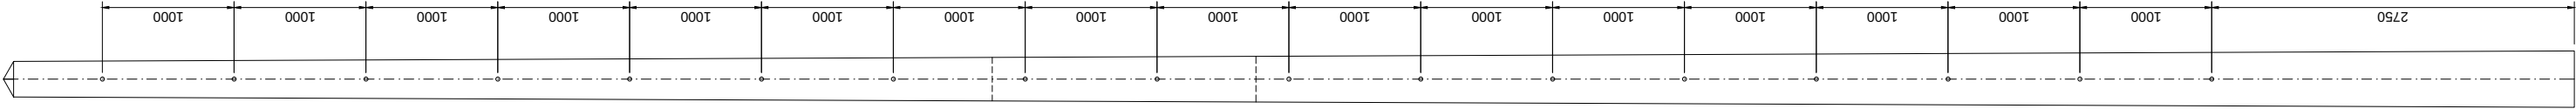

FEEDER BRACKETS

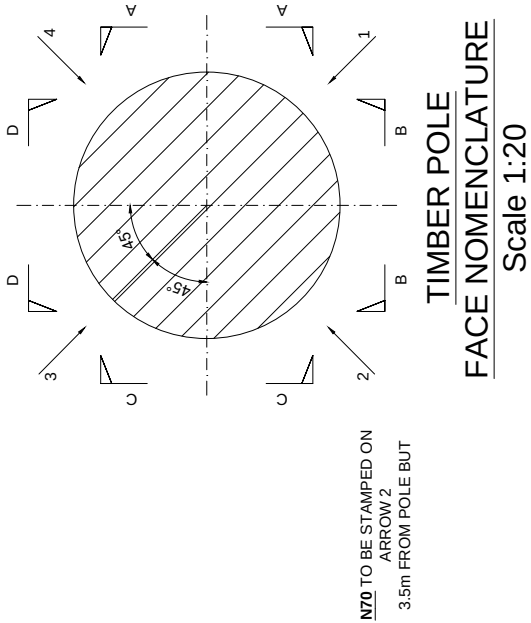

ALL HOLES ON ARROW 1
TO BE Ø8mm & 70mm LONG

HOLES
ARROW 1
Scale 1:50



ALL SCALES AS SHOWN WHEN PRINTED AT A3

ALL SCALES AS SHOWN WHEN PRINTED AT A3

01	FIRST ISSUE					AM	14/02/20
REV	REV					BY	DATE
SCALE AS SHOWN WHEN PRINTED AT A3		DRAWN	AM	CHECKED	MP	APPROVED	JBT
		DATE	14/02/20	DATE	14/02/20	DATE	14/02/20
ALL DIMENSIONS IN mm UNLESS OTHERWISE STATED. THIS DRAWING TO BE READ IN CONJUNCTION WITH OTHER RELEVANT DRAWINGS.							

TITLE

BOW STREET

TIMBER POLE CUT OUT
DETAIL


SITE ADDRESS


TIRYMYNACH
COMMUNITY COUNCIL
PLAYING FIELDS
ABERYSTWTH
CEREDIGION
SY24 5BW

ARQIVA REF.
140234


DRG No.
202

REV
01

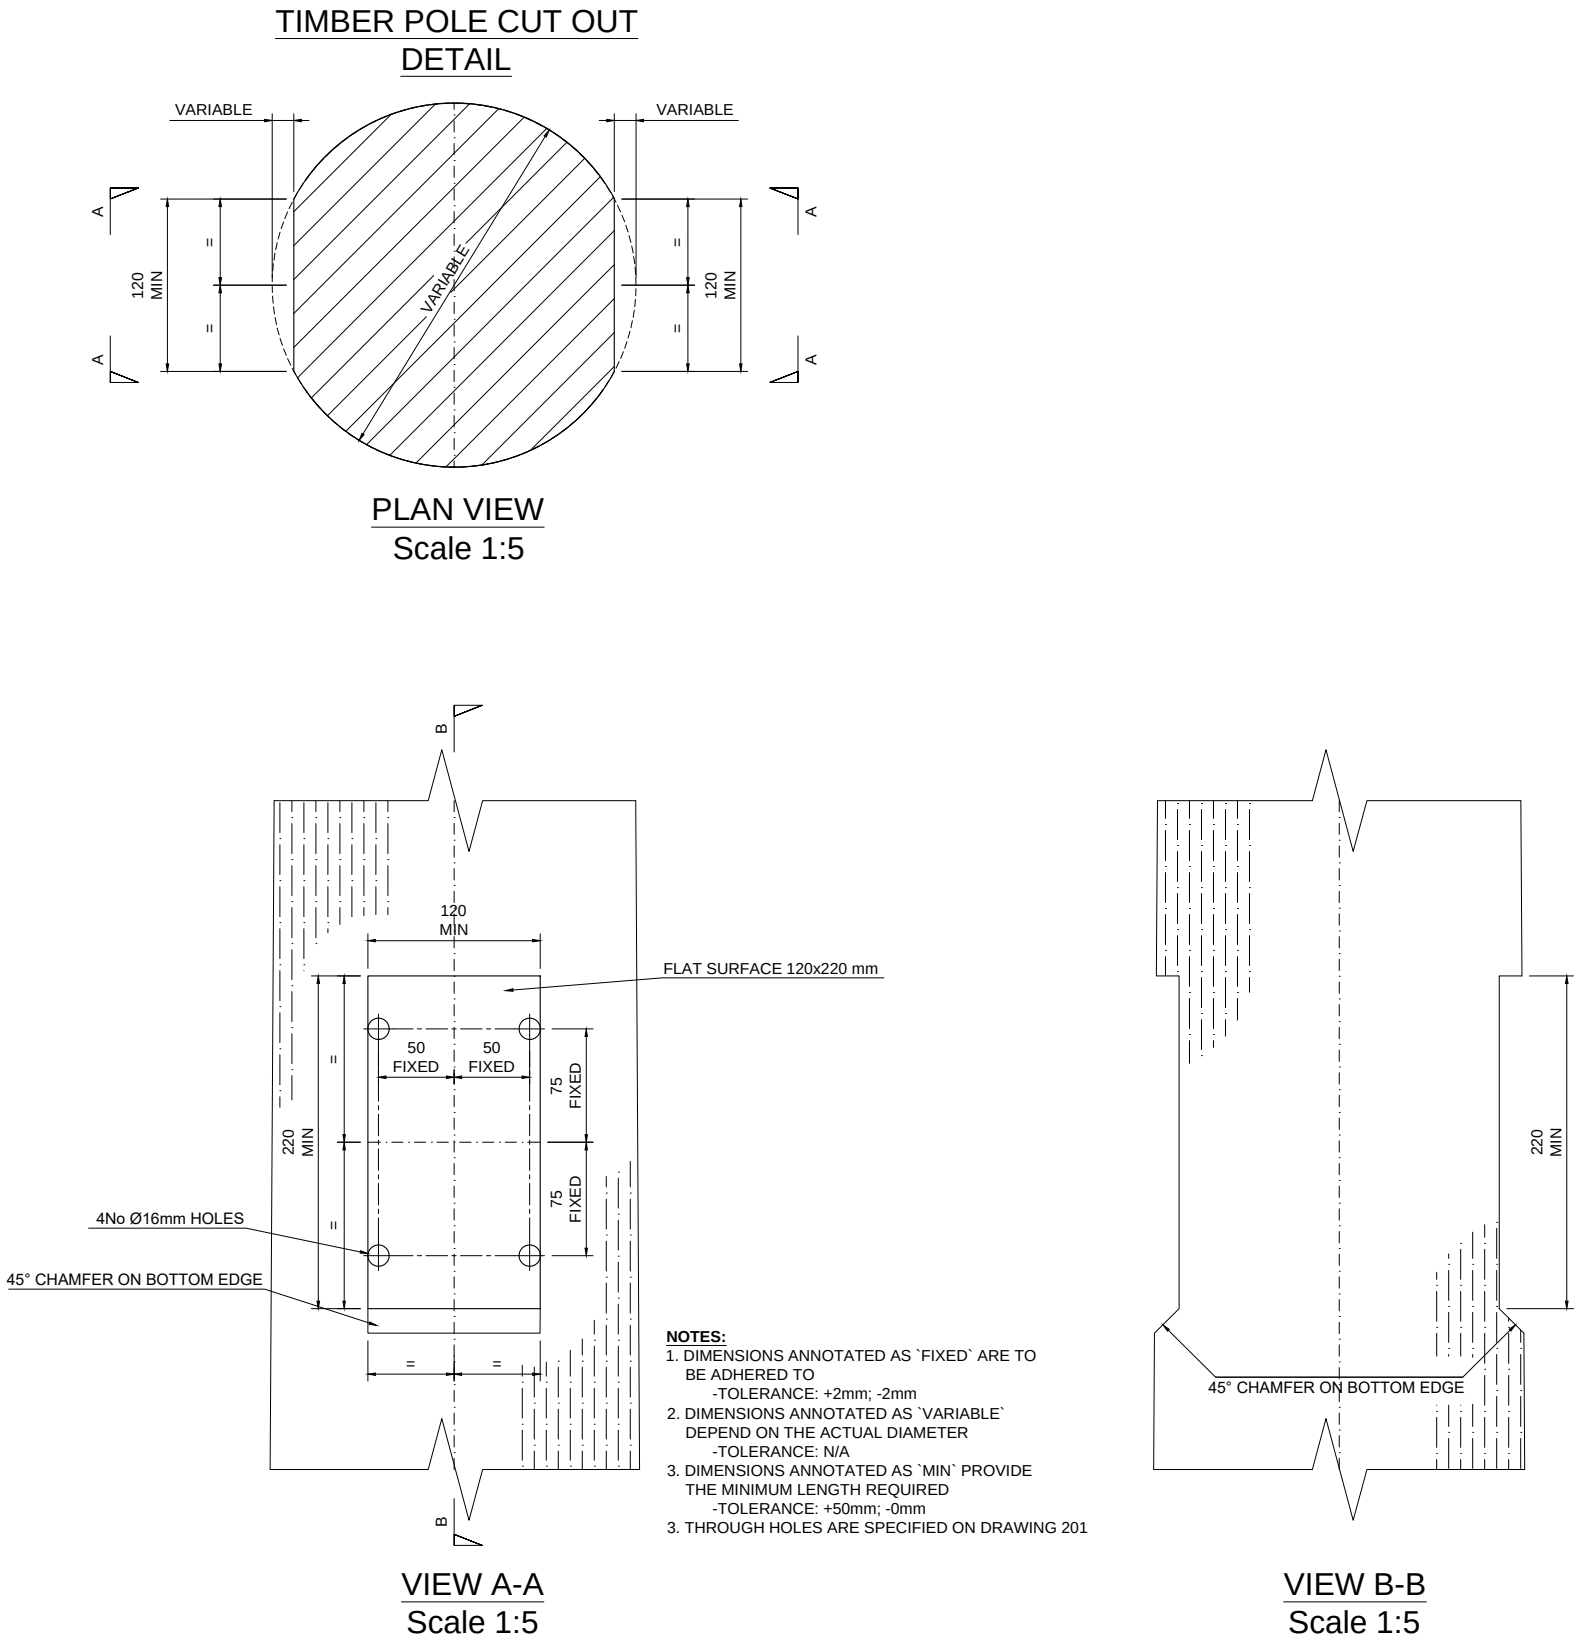


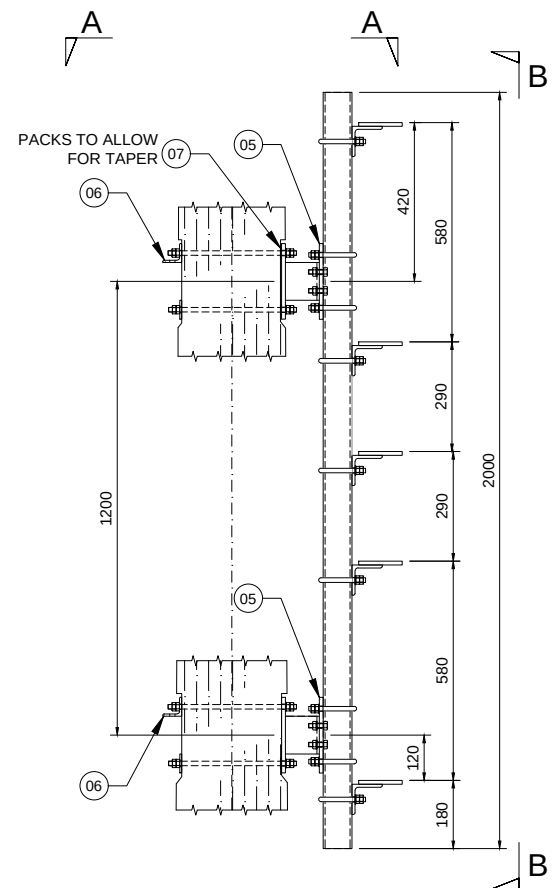

DETAIL G - Tx ANTENNA MOUNT
Scale 1:20

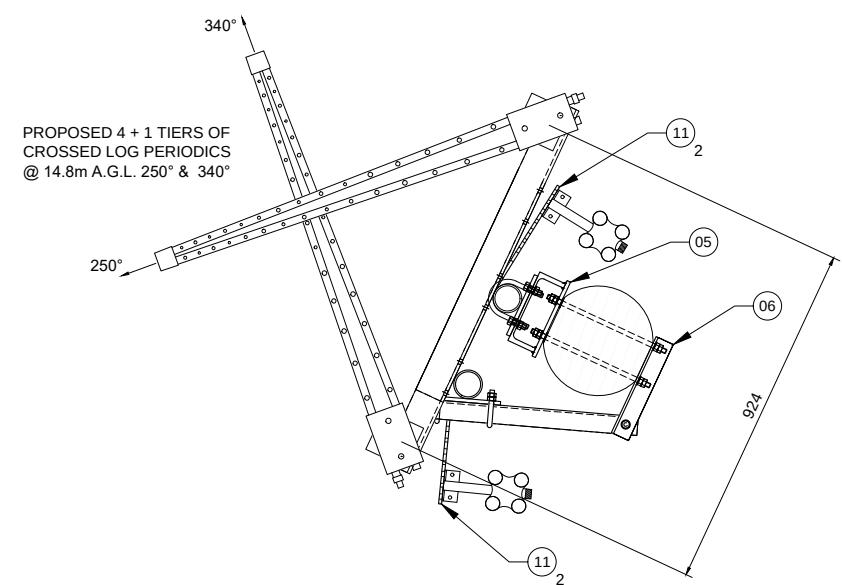


SECTION A-A
Scale 1:20

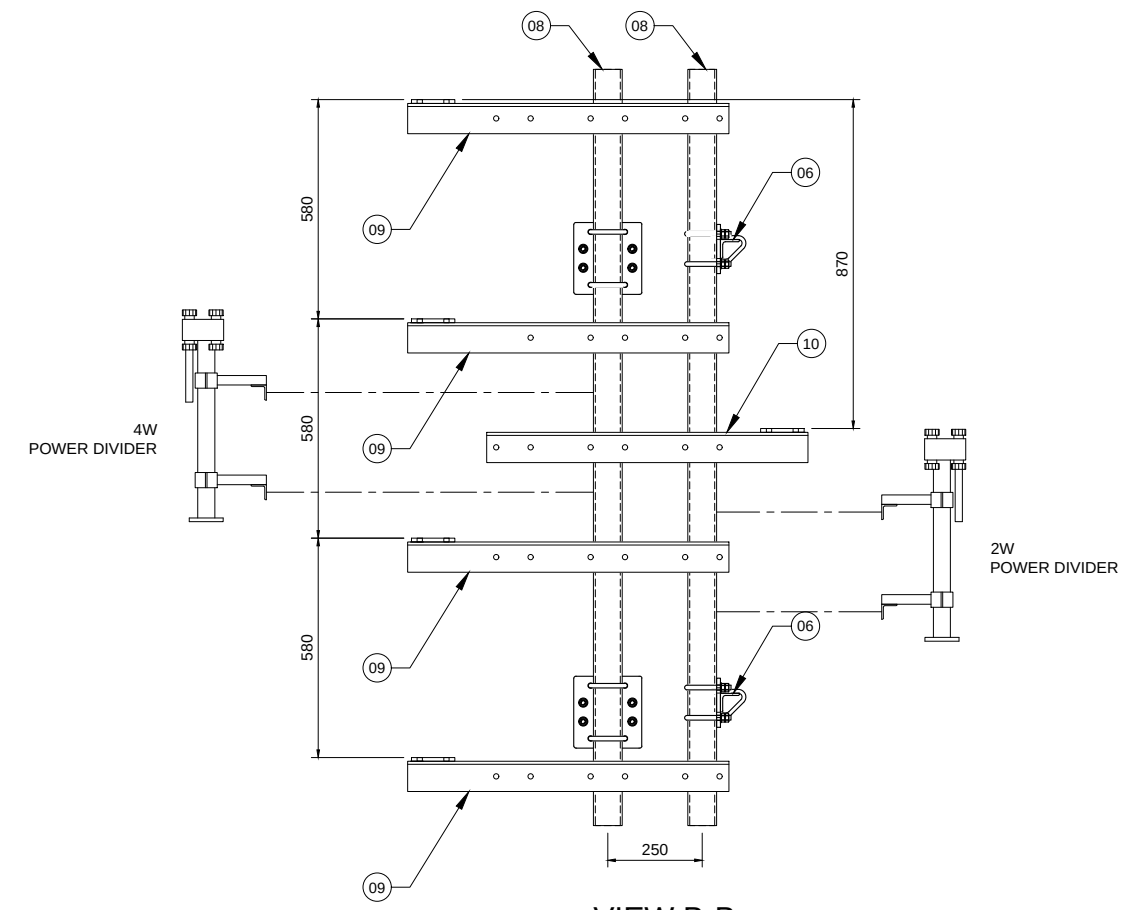

VIEW B-B
Scale 1:20

NOTE:
ALL M12 U-BOLTS TO BE
TIGHTENED TO 50Nm

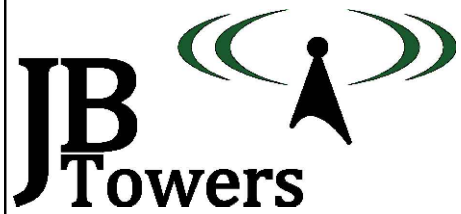


01	FIRST ISSUE			AM	14/02/20
REV	REV			BY	DATE
SCALE AS SHOWN		DRAWN	AM	CHECKED	MP
WHEN PRINTED AT A3		DATE	14/02/20	DATE	14/02/20
APPROVED		JBT			
ALL DIMENSIONS IN mm UNLESS OTHERWISE STATED. THIS DRAWING TO BE READ IN CONJUNCTION WITH OTHER RELEVANT DRAWINGS.					

TITLE
Tx ANTENNA MOUNT
DETAIL G


SITE ADDRESS		
TIRYMYNACH COMMUNITY COUNCIL PLAYING FIELDS ABERYSTWTH CEREDIGION SY24 5BW		
ARQIVA REF. 140234	DRG No. 203	REV 01

ALL SCALES AS SHOWN WHEN PRINTED AT A3



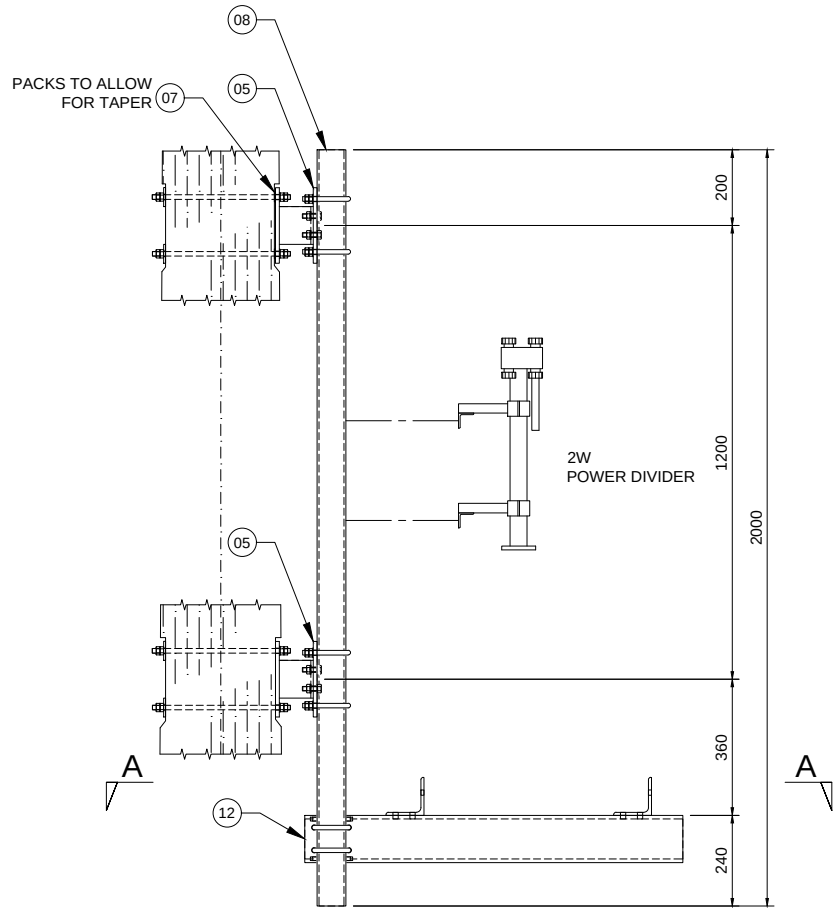


DETAIL H - Rx ANTENNA MOUNT
Scale 1:20

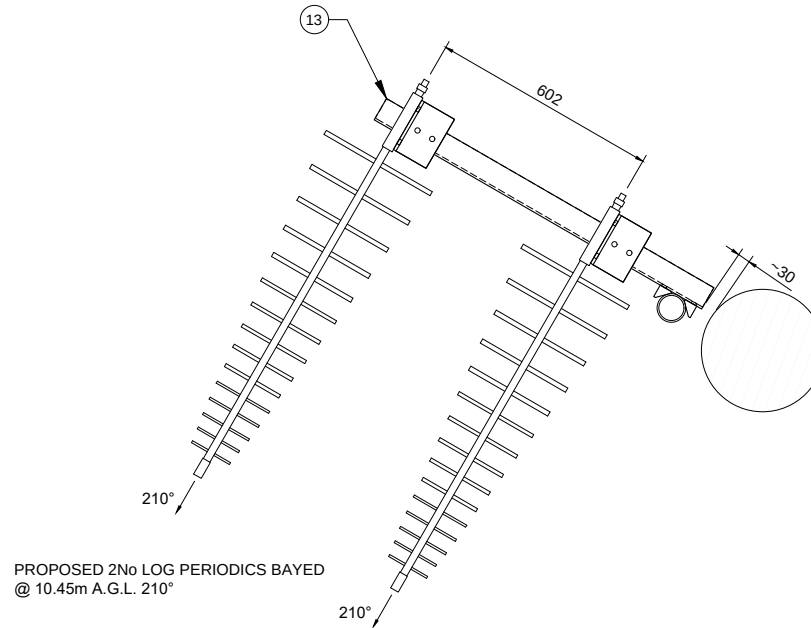

SECTION A-A
Scale 1:20

NOTE:
ALL M12 U-BOLTS TO BE
TIGHTENED TO 50Nm

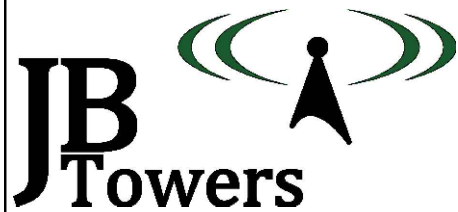


01	FIRST ISSUE			AM	14/02/20
REV	REV			BY	DATE
SCALE AS SHOWN WHEN PRINTED AT A3		DRAWN	AM	CHECKED	MP
		DATE	14/02/20	DATE	14/02/20
		APPROVED			
		JBT			
		DATE			
		14/02/20			
ALL DIMENSIONS IN mm UNLESS OTHERWISE STATED. THIS DRAWING TO BE READ IN CONJUNCTION WITH OTHER RELEVANT DRAWINGS.					

TITLE		SITE ADDRESS		
Rx ANTENNA MOUNT		TIRYMYNACH		
DETAIL H		COMMUNITY COUNCIL		
		PLAYING FIELDS		
		ABERYSTWTH		
		CEREDIGION		
		SY24 5BW		
ARQIVA REF.		DRG No.	REV	
140234		204	01	



ALL SCALES AS SHOWN WHEN PRINTED AT A3



ALL SCALES AS SHOWN WHEN PRINTED AT A3

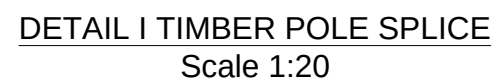


- ALL M16 BOLTS TO BE TIGHTENED TO 90Nm
- ALL SITE DRILLED HOLE/CUT ENDS TO BE TREATED WITH
METAFLUX 70-40 ZINC PASTE FOLLOWED BY 1 COAT OF
7-42 ZINC ALU OR 70-16 ALUMINIUM SPRAY

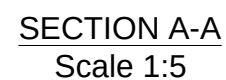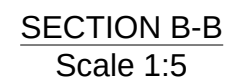


- WORK SEQUENCE (PRIOR TO POLE BEING SENT TO SITE):**
1. LOCATION OF COLLARS TO BE MARKED ON POLE AND POLE OD AT THESE LOCATIONS TO BE MEASURED AND USED TO INFORM THE FABRICATION OF THE STEEL COLLARS.
(COLLAR HOLES FOR THE THROUGH BOLTS ARE TO BE DRILLED LATER)
 2. HOLES IN POLE FOR ALL COLLAR THROUGH BOLTS TO BE DRILLED.
 3. SPLICE JOINT TO BE CUT IN POLE.
 4. POLE TO BE PRESSURE IMPREGNATED WITH CREOSOTE.
 5. POLE SECTIONS TO BE OFFERED TO ONE ANOTHER AND ONCE IN THE CORRECT POSITION COLLARS 2 SHALL BE INSTALLED TO HOLD THE POLE IN POSITION AND THE CLAMPING BOLTS TORQUED.
 6. THE THROUGH BOLT IN THE CENTRE OF THE SPLICE SHALL BE DRILLED AND THE THROUGH BOLT INSERTED.
 7. THE THROUGH BOLTS FOR COLLARS 1 & 3 SHALL BE INSTALLED AND THE COLLARS OFFERED UP AND THE REQD HOLE LOCATIONS IN THE COLLARS MARKED AND THEN DRILLED.
 8. THESE COLLARS SHALL BE INSTALLED OVER THE THROUGH BOLTS AND THEN THE CLAMPING BOLTS TORQUED.
 9. COLLARS 2 SHALL THEN BE REMOVED AND THE THROUGH BOLTS INSTALLED AND THE COLLARS OFFERED UP AND THE REQD HOLE LOCATIONS IN THE COLLARS MARKED AND THEN DRILLED.
 10. THESE COLLARS SHALL BE INSTALLED OVER THE THROUGH BOLTS AND THEN THE CLAMPING BOLTS TORQUED.
 11. THE VERTICAL PLATES STRAPPING THE COLLARS TOGETHER SHALL THEN BE INSTALLED.
 12. THE FIT OF ALL ELEMENTS OF THE SPLICE SHALL BE CHECKED AND ONCE SATISFACTORY FIT HAS BEEN CONFIRMED THE SPLICE JOINT CAN BE DISASSEMBLED.
 13. ANY DISTURBED SURFACES SHALL HAVE THEIR WATERPROOFING REPAIRED AS PER NOTES ON DRG 200
 14. THE CLAMPING BOLTS USED IN THE CHECK ERECTION SHALL BE DISCARDED AND NEW BOLTS SUPPLIED TO SITE.



01	FIRST ISSUE			AM 14/02/20
REV	REV			BY DAT
SCALE AS SHOWN WHEN PRINTED AT A3	DRAWN AM DATE 14/02/20	CHECKED MP DATE 14/02/20	APPROVED JB DATE 14/02/20	
ALL DIMENSIONS IN mm UNLESS OTHERWISE STATED. THIS DRAWING TO BE READ IN CONJUNCTION WITH OTHER RELEVANT DRAWINGS.				

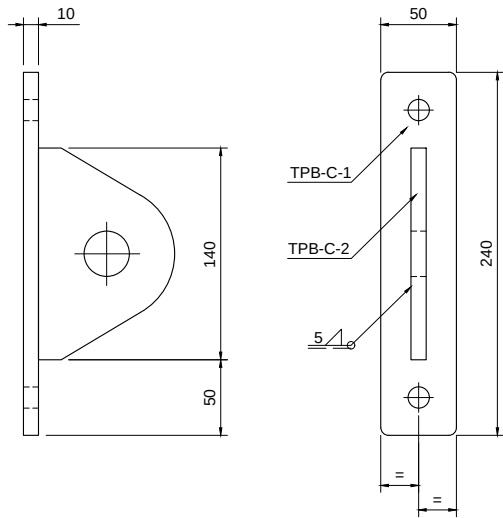

PART TPB-C
Scale 1:5

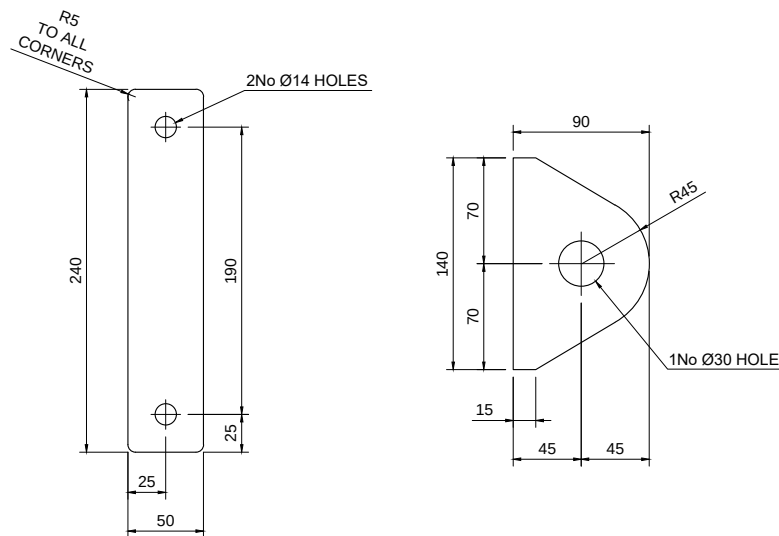


TPB-C-1 - 10mm THICK
Scale 1:5

TPB-C-2 - 10mm THICK
Scale 1:5

Parts list for TPB-C


Item	Part	Quantity	Part description	Length	Material	Weight
01	TPB-C-1	1	Plate 240x50x10mm	N/A	S275J0	0.94 kg
02	TPB-C-2	1	Plate 140x90x10mm	N/A	S275J0	0.99 kg
03	STUDS	1	M12 STUDDING	350mm	GRADE 8.8	0.31 kg
Total Weight:						2.24 kg

- All steel hot dip galvanized
- Each STUD to be supplied with 4 Full Nuts, 2 Flat Washers and 2 Spring Washers
- For fabrication notes see drawing 305

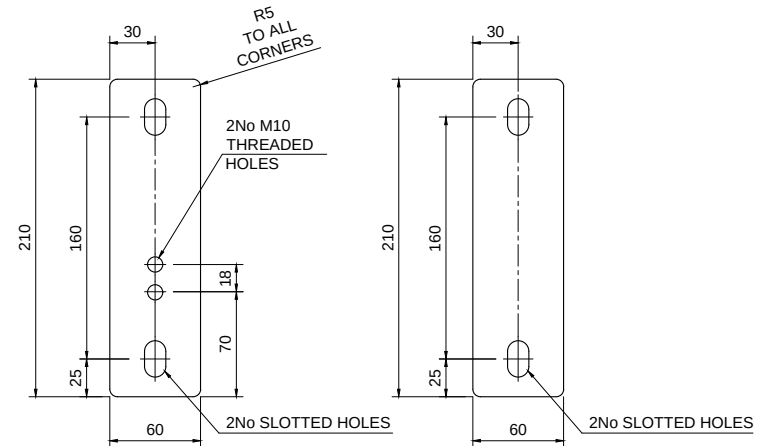

PART TPS-R-1
Scale 1:5

PART TPS-R-2
Scale 1:5

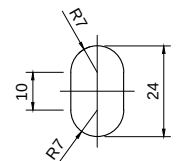


SLOTTED HOLE DETAIL
Scale 1:2

Parts list for TPS-R

Item	Part	Quantity	Part description	Length	Material	Weight
01	TPS-R-1	1	210x60x15mm	N/A	S275J0	1.48 kg
02	TPS-R-2	1	210x60x5mm	N/A	S275J0	0.49 kg
03	STUDS	2	M12 STUDDING	500mm	GRADE 8.8	0.44 kg
04	NUT-S	2	M12 SHALLOW NUT	N/A	GRADE 8.8	-
05	NUT	4	M12 NUT	N/A	GRADE 8.8	-
06	WSH	4	M12 WASHER	N/A	GRADE 8.8	-
Total Weight:						2.85 kg

- All steel hot dip galvanized
- For fabrication notes see drawing 305

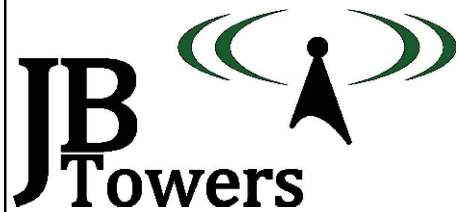



01	FIRST ISSUE	AM	14/02/20
REV	REV	BY	DATE
SCALE AS SHOWN WHEN PRINTED AT A3	DRAWN DATE 14/02/20	CHECKED DATE 14/02/20	APPROVED DATE 14/02/20
ALL DIMENSIONS IN mm UNLESS OTHERWISE STATED. THIS DRAWING TO BE READ IN CONJUNCTION WITH OTHER RELEVANT DRAWINGS.			

TITLE ATTACHMENT POINT & TEMPORARY STEP DETAILS PARTS: TPB-C; TPS-R		SITE ADDRESS TIRYMYNACH COMMUNITY COUNCIL PLAYING FIELDS ABERYSTWTH CEREDIGION SY24 5BW	
ARQIVA REF. 140234		DRG No. 300	REV 01


ALL SCALES AS SHOWN WHEN PRINTED AT A3




ALL SCALES AS SHOWN WHEN PRINTED AT A3

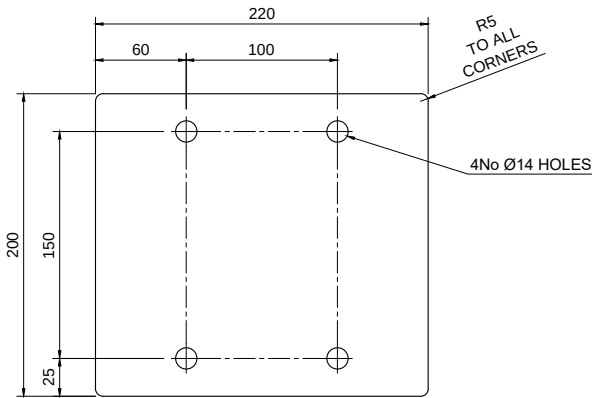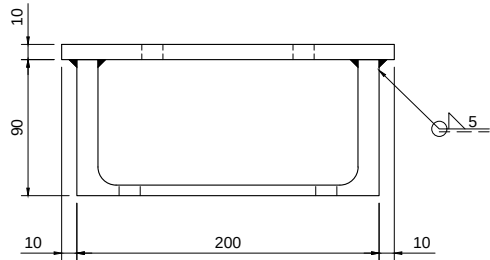


TPB-B-1 - 10mm THICK
Scale 1:5

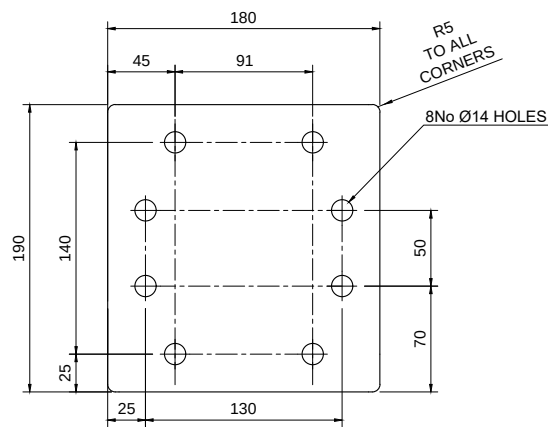


TPB-B-5 - 10mm THICK
Scale 1:5

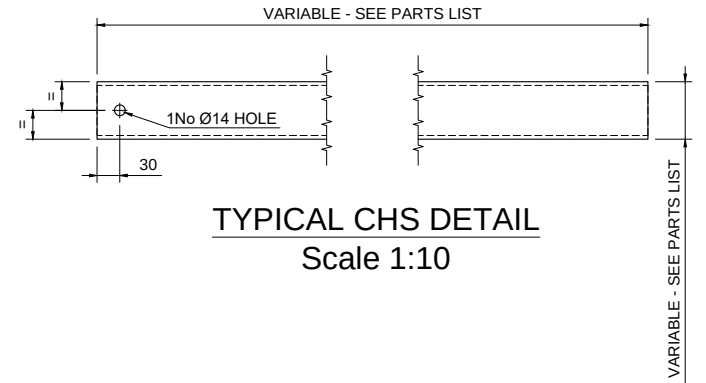


TYPICAL CHS DETAIL
Scale 1:10

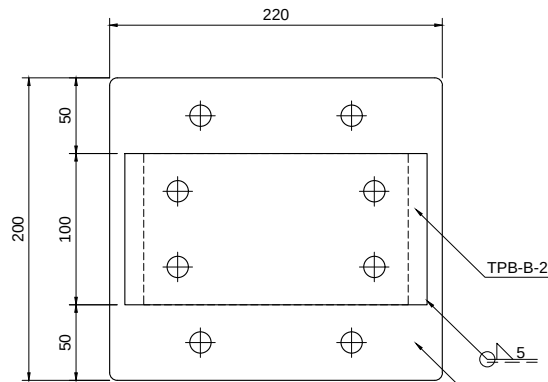

PART TPB-B
Scale 1:5

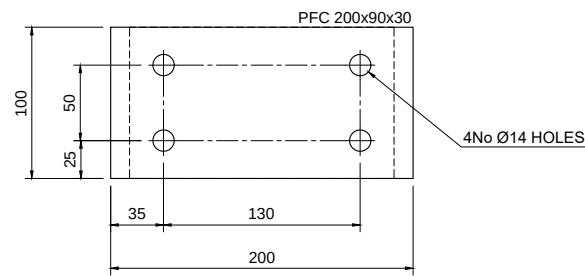

TPB-B-2 - PFC 200x90x30
Scale 1:5

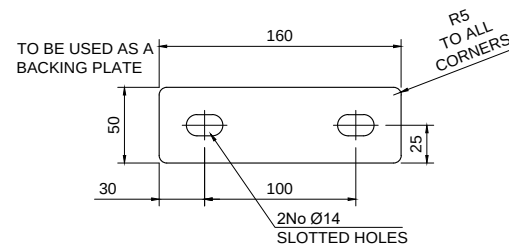


TPB-B-4 - 5mm THICK
Scale 1:5


Parts list for TPB-B

Item	Part	Quantity	Part description	Length	Material	Weight
01	TPB-B-1	1	Plate 220x200x10mm	N/A	S275J0	3.45 kg
02	TPB-B-2	1	PFC 200x90x30	100mm	S275J0	3.00 kg
03	TPB-B-4	2	Plate 160x50x5mm	N/A	S275J0	0.31 kg
04	TPB-B-5	1	Plate 190x180x10mm	N/A	S275J0	2.70 kg
05	STUDS	4	M12 STUDDING	450mm	GRADE 8.8	0.39 kg
06	BOLT	4	M12 45mm LONG (2D+6)	45mm	GRADE 8.8	-
07	U-BOLT	2	M12 U-BOLT FOR CHS 76.1	N/A	GRADE 8.8	-
Total Weight:						11.02 kg

- All steel hot dip galvanized
- Each STUD & U-BOLT to be supplied with 4 Full Nuts, 2 Flat Washers and 2 Spring Washers
- Each BOLT to be supplied with 1 Full Nut, 1 Form E FLat Washer and 1 Spring Washer
- For fabrication notes see drawing 305

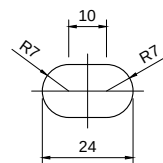

SLOTTED HOLE DETAIL
Scale 1:2

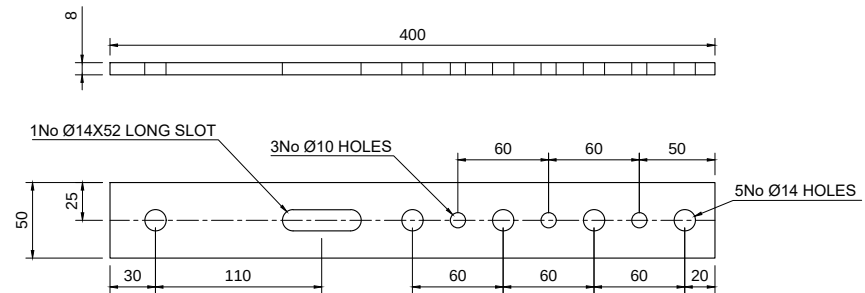


TPA-PD - 8mm THICK
Scale 1:5

Parts list for TPA-PD

Item	Part	Quantity	Part description	Length	Material	Weight
01	TPA-PD	1	Plate 400x50x8mm	N/A	S275J0	1.26 kg
02	U-BOLT	1	M12 U-BOLT FOR CHS 76.1mm	N/A	GRADE 8.8	-
Total Weight:						1.26 kg

- All steel hot dip galvanized
- Each U-BOLT to be supplied with 4 Full Nuts, 2 Flat Washers and 2 Spring Washers
- For fabrication notes see drawing 305

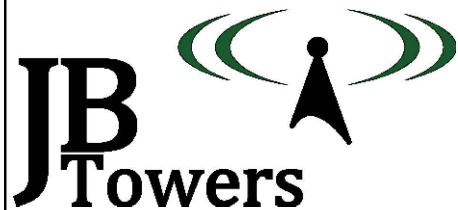

01	FIRST ISSUE	AM	14/02/20
REV	REV	BY	DATE
SCALE AS SHOWN WHEN PRINTED AT A3	DRAWN DATE	AM 14/02/20	CHECKED DATE
MP 14/02/20	APPROVED DATE	JBT 14/02/20	
ALL DIMENSIONS IN mm UNLESS OTHERWISE STATED. THIS DRAWING TO BE READ IN CONJUNCTION WITH OTHER RELEVANT DRAWINGS.			

TITLE
STEELWORK BRACKET;
POWER DIVIDER STRAP;
TYPICAL CHS DETAIL
PARTS: TPB-B; TPA-PD


SITE ADDRESS
TIRYMYNACH
COMMUNITY COUNCIL
PLAYING FIELDS
ABERYSTWTH
CEREDIGION
SY24 5BW

ARQIVA REF. 140234	DRG No. 301	REV 01
-----------------------	----------------	-----------

ALL SCALES AS SHOWN WHEN PRINTED AT A3



ALL SCALES AS SHOWN WHEN PRINTED AT A3

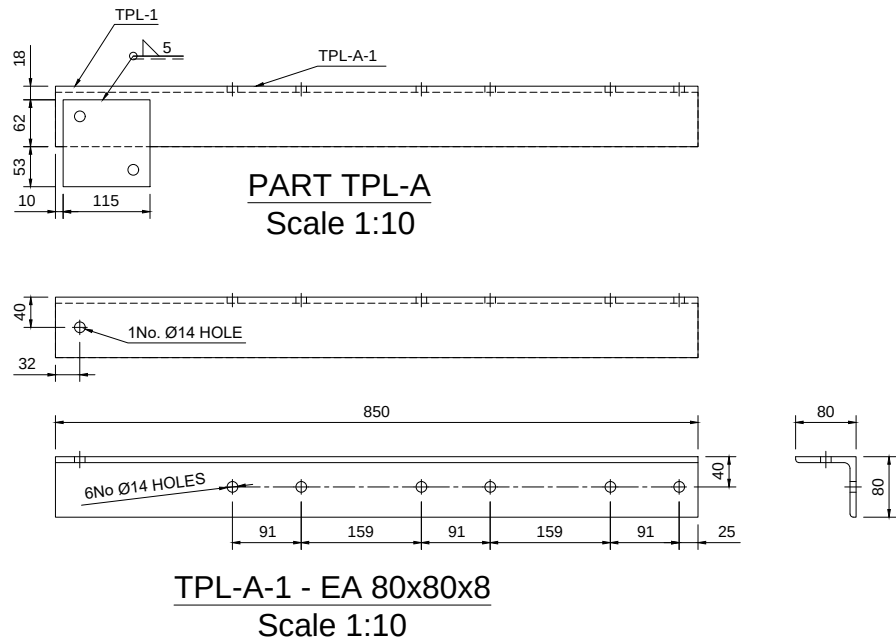


TPL-A-1 - EA 80x80x8
Scale 1:10

Parts list for TPL-A

Item	Part	Quantity	Part description	Length	Material	Weight
01	TPL-A-1	1	EA 80x80x8	850mm	S275J0	8.20 kg
02	TPL-1	1	Plate 115x115x10mm	N/A	S275J0	1.10 kg
03	U-BOLT	2	M12 U-BOLT FOR CHS 76.1mm	N/A	GRADE 8.8	-
Total Weight:						9.30 kg

- All steel hot dip galvanized
- Each U-BOLT to be supplied with 4 Full Nuts, 2 Flat Washers and 2 Spring Washers
- For fabrication notes see drawing 305

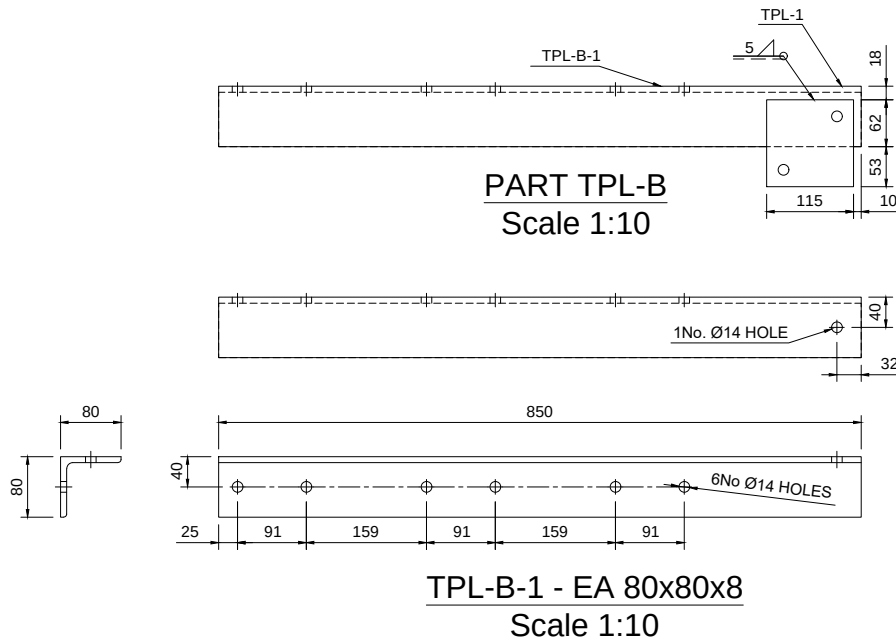


TPL-B-1 - EA 80x80x8
Scale 1:10


Parts list for TPL-B

Item	Part	Quantity	Part description	Length	Material	Weight
01	TPL-B-1	1	EA 80x80x8	850mm	S275J0	8.20 kg
02	TPL-1	1	Plate 115x115x10mm	N/A	S275J0	1.10 kg
03	U-BOLT	2	M12 U-BOLT FOR CHS 76.1mm	N/A	GRADE 8.8	-
Total Weight:						9.30 kg

- All steel hot dip galvanized
- Each U-BOLT to be supplied with 4 Full Nuts, 2 Flat Washers and 2 Spring Washers
- For fabrication notes see drawing 305

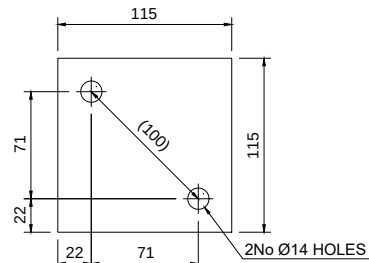

PART TPL-1 - 10mm THICK
Scale 1:5

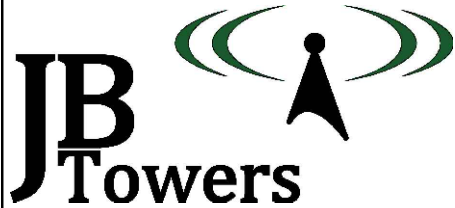

01	FIRST ISSUE	AM	14/02/20
REV	REV	BY	DATE
SCALE AS SHOWN WHEN PRINTED AT A3	DRAWN DATE	AM 14/02/20	CHECKED DATE
ALL DIMENSIONS IN mm UNLESS OTHERWISE STATED. THIS DRAWING TO BE READ IN CONJUNCTION WITH OTHER RELEVANT DRAWINGS.			

TITLE
LOG MOUNTING BRACKETS
PARTS: TPL-A; TPL-B


SITE ADDRESS
TIRYMYNACH
COMMUNITY COUNCIL
PLAYING FIELDS
ABERYSTWTH
CEREDIGION
SY24 5BW

ARQIVA REF.
140234
DRG No.
302
REV
01


ALL SCALES AS SHOWN WHEN PRINTED AT A3




ALL SCALES AS SHOWN WHEN PRINTED AT A3

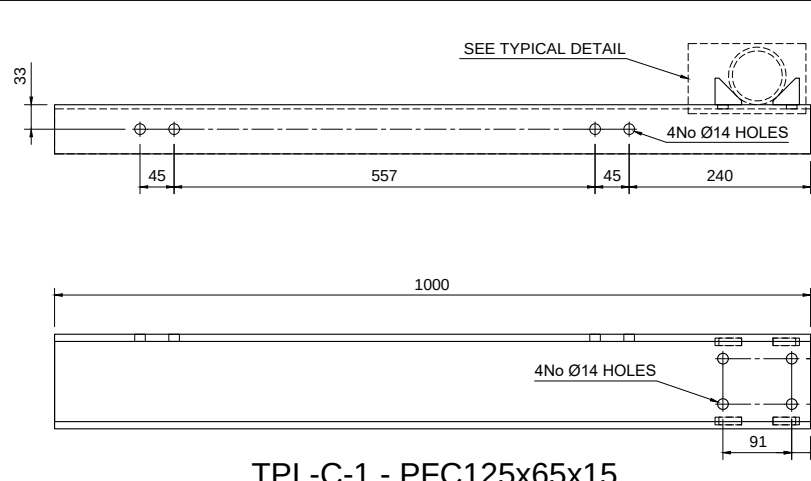


TPL-C-1 - PFC125x65x15
Scale 1:10

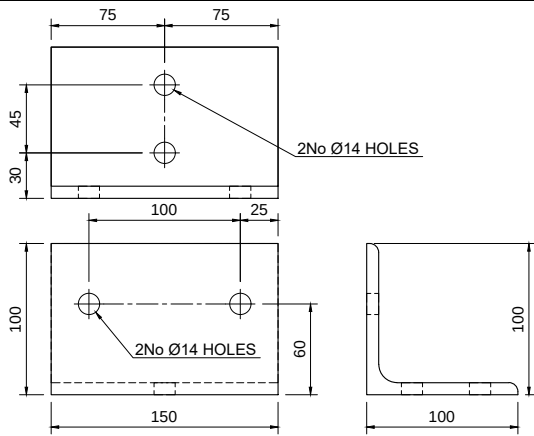


TPL-C-2 - EA100x100x8
Scale 1:5

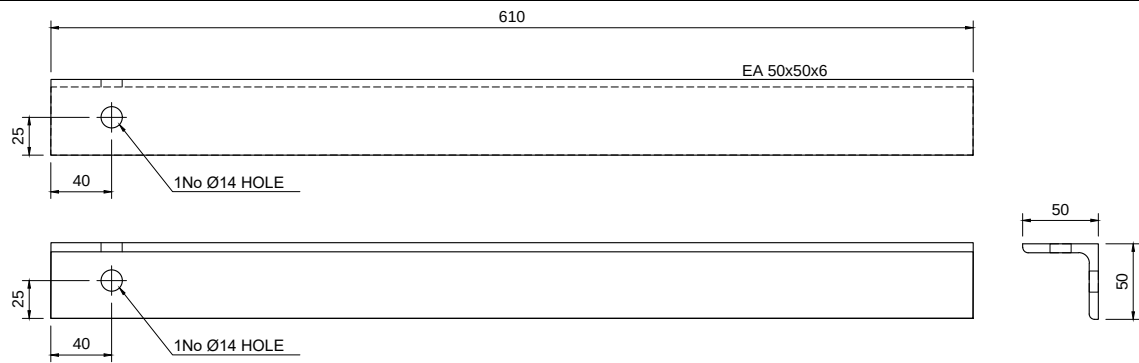

TPA-BR-1 - EA50x50x6
Scale 1:5

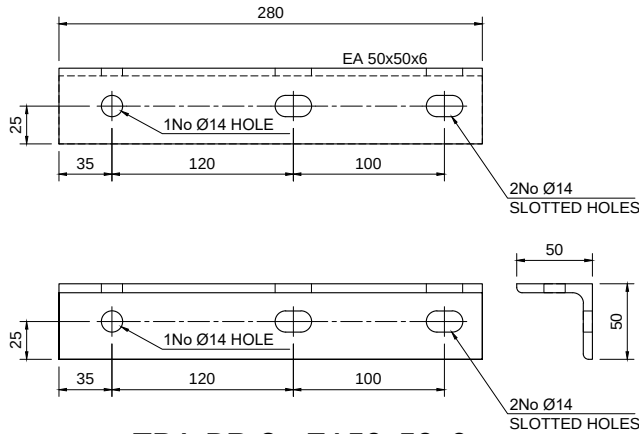

TPA-BR-2 - EA50x50x6
Scale 1:5

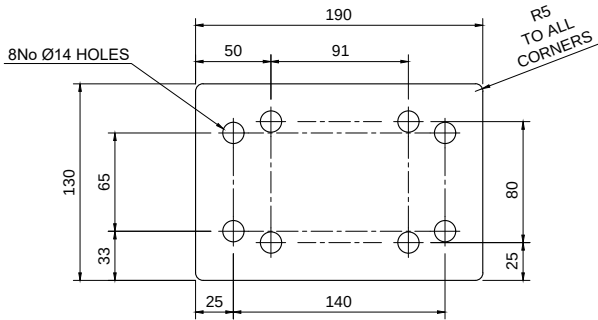


TPB-BR-3 - 10mm THICK
Scale 1:5

Parts list for TPL-C

Item	Part	Quantity	Part description	Length	Material	Weight
01	TPL-C-1	1	PFC125x65x15	1000mm	S275J0	15.00 kg
02	TPL-C-2	1	EA100x100x8	150mm	S275J0	1.90 kg
03	U-BOLT	2	M12 U-BOLT FOR CHS 76.1mm	N/A	GRADE 8.8	-
03	BOLT	4	M12 40mm SET BOLT	N/A	GRADE 8.8	-
Total Weight:						16.90 kg

- All steel hot dip galvanized
- Each U-BOLT to be supplied with 4 Full Nuts, 2 Flat Washers and 2 Spring Washers
- Each BOLT to be supplied with 1 Full Nut, 1 Form E FLat Washer and 1 Spring Washer
- For fabrication notes see drawing 305

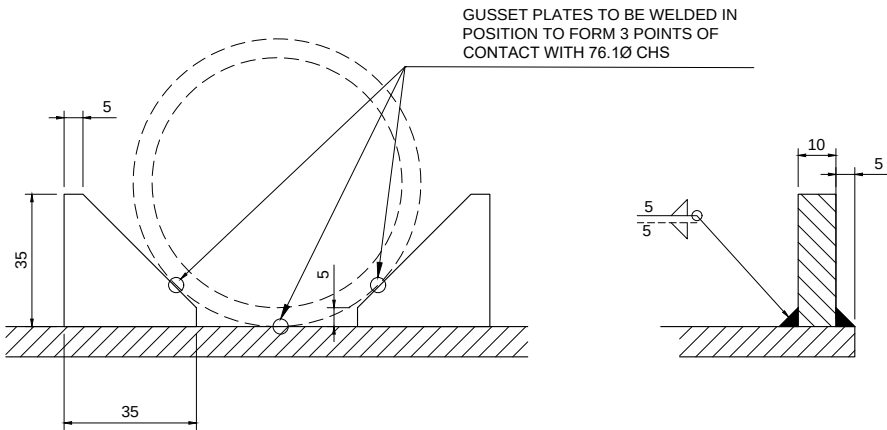


TYPICAL GUSSET PLATE DETAIL
Scale 1:2


Parts list for TPA-BR

Item	Part	Quantity	Part description	Length	Material	Weight
01	TPB-BR-1	1	EA 50x50x6	280mm	S275J0	1.25 kg
02	TPB-BR-2	1	EA 50x50x6	610mm	S275J0	2.80 kg
03	TPB-BR-3	1	130x190x10mm	N/A	S275J0	1.95 kg
04	BOLT	1	M12 SET BOLT - 30mm LONG	N/A	GRADE 8.8	-
05	N-BOLT	2	M12 N-BOLT FOR EA 50x50x6	N/A	GRADE 8.8	-
06	U-BOLT	2	M12 U-BOLT FOR CHS 76.1mm	N/A	GRADE 8.8	-
Total Weight:						6.00 kg

- All steel hot dip galvanized
- Each BOLT to be supplied with 1 Full Nut, 1 Form E FLat Washer and 1 Spring Washer
- Each STUD & U-BOLT to be supplied with 4 Full Nuts, 2 Flat Washers and 2 Spring Washers
- For fabrication notes see drawing 305

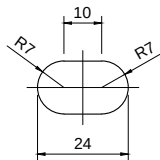

SLOTTED HOLE DETAIL
Scale 1:2

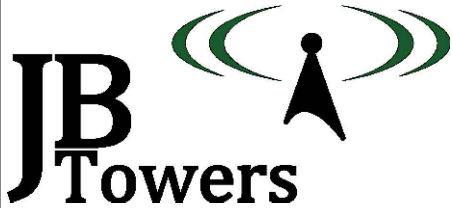

01	FIRST ISSUE	AM	14/02/20
REV	REV	BY	DATE
SCALE AS SHOWN WHEN PRINTED AT A3	DRAWN DATE	AM 14/02/20	CHECKED DATE
MP 14/02/20			
APPROVED DATE			
JBT 14/02/20			
ALL DIMENSIONS IN mm UNLESS OTHERWISE STATED. THIS DRAWING TO BE READ IN CONJUNCTION WITH OTHER RELEVANT DRAWINGS.			

TITLE
LOG MOUNT; BRACING KIT
PARTS: TPL-C; TPA-BR


SITE ADDRESS
TIRYMYNACH
COMMUNITY COUNCIL
PLAYING FIELDS
ABERYSTWTH
CEREDIGION
SY24 5BW

ARQIVA REF.
140234
DRG No.
303
REV
01



ALL SCALES AS SHOWN WHEN PRINTED AT A3




ALL SCALES AS SHOWN WHEN PRINTED AT A3

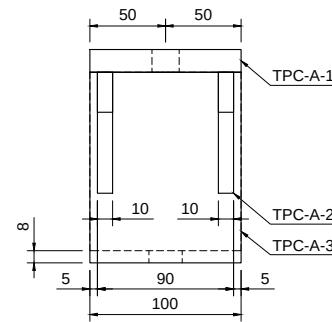


TPC-A
Scale 1:5

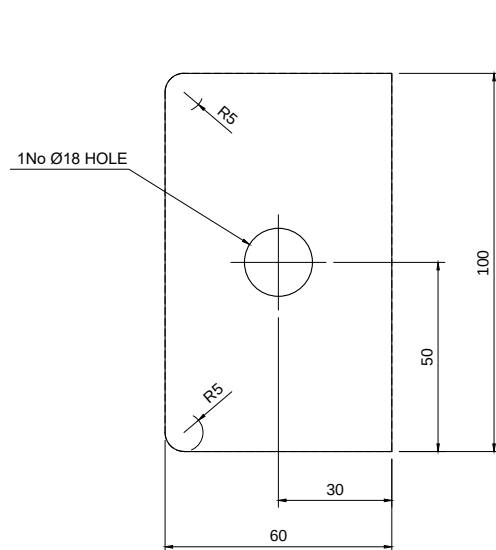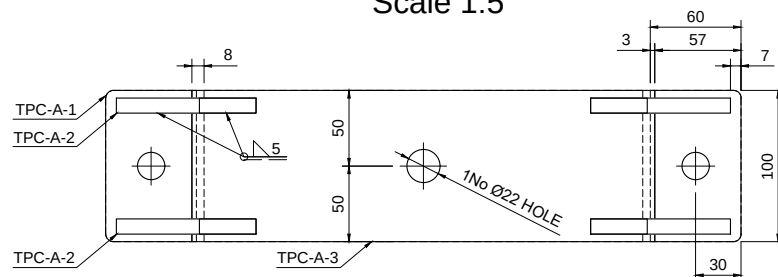

TPC-A-1 - 15mm THICK
Scale 1:2

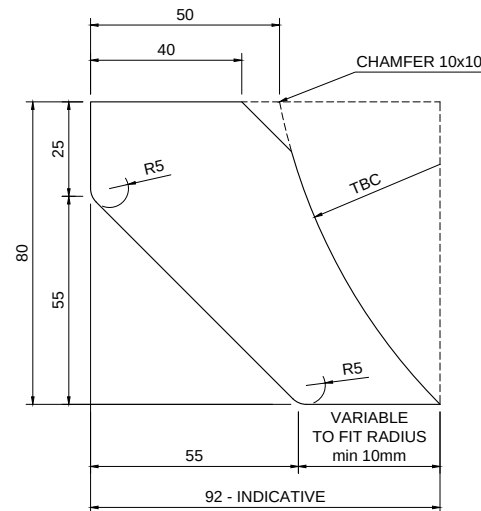

TPC-A-2 - 10mm THICK
Scale 1:2

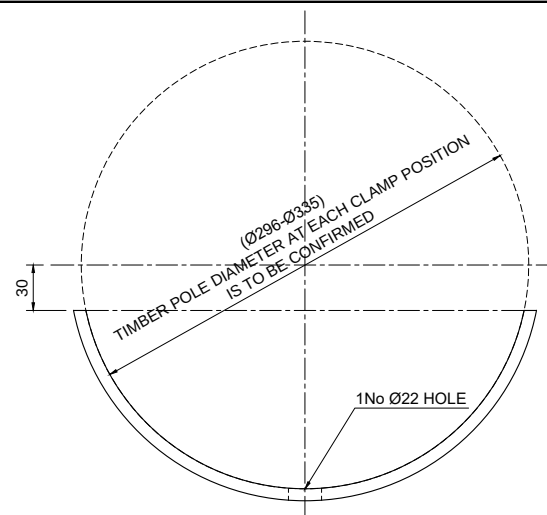


TPC-A-3 - 100x8mm PLATE
Scale 1:5

Parts list for TPC-A - 1No COLLAR (6No COLLARS REQUIRED)

Item	Part	Quantity	Part description	Length	Material	Weight
01	TPC-A-1	4	PLATE 100x60x15mm	TBC	S275J0	0.71 kg
02	TPC-A-2	8	PLATE 80x50x10mm	N/A	S275J0	0.30 kg
03	TPC-A-3	2	PLATE 100mm WIDE & 8mm THICK	N/A	S275J0	3.00 kg
04	NUT	2	M16 - HALF NUT	N/A	GRADE 8.8	-
05	BOLT	2	M16 100mm LONG SET BOLT	N/A	GRADE 8.8	-
- All steel hot dip galvanized					Total Weight:	11.24 kg

- All steel hot dip galvanized
- Each BOLT to be supplied with 1 Full Nut, 1 Form E FLat Washer and 1 Spring Washer
- For fabrication notes see drawing 305

Total Weight:

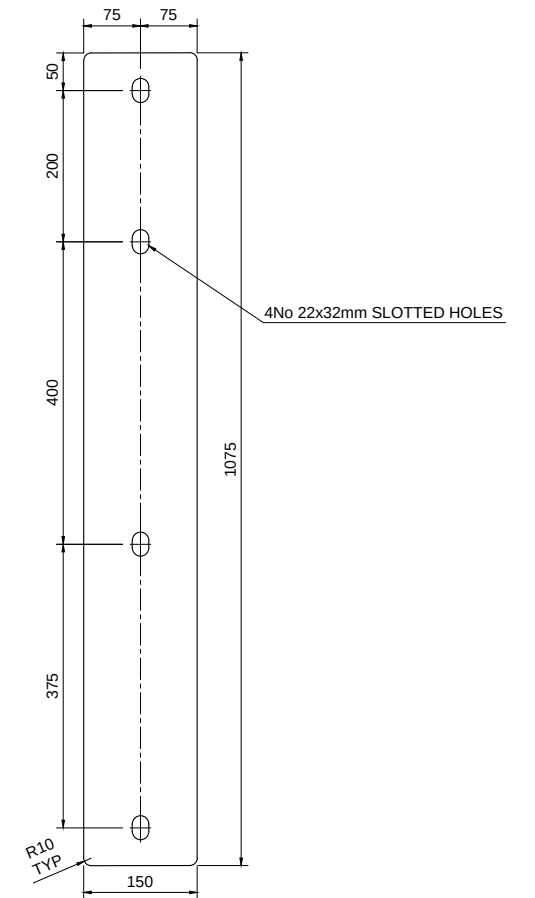


TPC-B - 15mm THICK
Scale 1:10

Parts list for TPC-B - 1No SET OF 2No INTERFACE PLATES (2No SETS REQUIRED)

Item	Part	Quantity	Part description	Length	Material	Weight
01	TPC-B	2	PLATE 1075x150x15mm	N/A	S275J0	19.00 kg
02	STUD	4	M20 STUD	500mm	GRADE 8.8	1.25 kg
03	SQ-WSH	6	M20 50x50x3mm SQUARE WASHER	N/A	GRADE 8.8	-
- All steel hot dip galvanized					Total Weight:	43.00 kg

- All steel hot dip galvanized
 - Each STUD to be supplied with 2 Full Nuts, 2 Half Nuts, 2 Flat Washers and 2 Spring Washers
 - For fabrication notes see drawing 305
- Total W

Total Weight:	
---------------	--

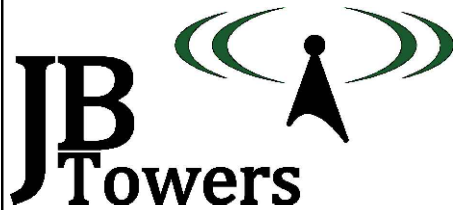

argiva

01	FIRST ISSUE		AM	14/02/20	
REV	REV		BY	DAT	
SCALE AS SHOWN WHEN PRINTED AT A3	DRAWN AM DATE 14/02/20	CHECKED MP DATE 14/02/20	APPROVED JB DATE 14/02/20		
ALL DIMENSIONS IN mm UNLESS OTHERWISE STATED. THIS DRAWING TO BE READ IN CONJUNCTION WITH OTHER RELEVANT DRAWINGS.					

TITLE

SPLICE COLLAR; INTERFACE
PLATES

PARTS: TPC-A; TPC-B

SITE ADDRESS

TIRYMYNACH
COMMUNITY COUNCIL
PLAYING FIELDS
ABERYSTWTH
CEREDIGION
SY24 5BW

ARQIVA REF.
140234

DRG No.
304

ALL SCALES AS SHOWN WHEN PRINTED AT A3

ALL SCALES AS SHOWN WHEN PRINTED AT A3




NOTE:
2No. EXTENDED WIRE GUIDES - PART NO. 35397-00
4No. REGULAR WIRE GUIDES - PART NO. 30050-00

Item	Part	Drawing	Quantity	Part description	Length	Material	Weight
01	01	200	1	3 MAN LATCHWAY SYSTEM & *6No. WIRE GUIDES FOR FACE MOUNTED MONOPOLE (see notes)	17000	N/A	-
02	TPB-C	300	2	FALL ARREST ATTACHMENT POINT	N/A	S275J0	4.48 kg
03	03	200	46	PERMANENT BT STEP c/w 3No 10x75mm ZINC-PLATED COACH SCREWS	N/A	S275J0	13.80 kg
04	TPS-R	300	9	'MonoStep' ASSEMBLY	N/A	S275J0	25.65 kg
05	TPB-B	301	4	MOUNTING BRACKET	N/A	S275J0	44.08 kg
06	TPA-BR	303	2	BRACING KIT	N/A	S275J0	12.00 kg
07	07	203/4	24	M12 WASHER	N/A	GRADE 8.8	-
08	08	203/4	3	CHS 76.1x5mm	2000mm	S355J2H	52.70 kg
09	TPL-A	302	4	LOG MOUNTING BRACKET	850mm	S275J0	37.20 kg
10	TPL-B	302	1	LOG MOUNTING BRACKET	850mm	S275J0	9.30 kg
11	TPA-PD	301	6	POWER DIVIDER STRAP	N/A	S275J0	7.60 kg
12	TPL-C	303	1	LOG MOUNTING BRACKET	1000mm	S275J0	16.90 kg
13	TPC-A	304	6	TIMBER POLE SPLICE COLLAR	N/A	S275J0	67.44 kg
14	TPC-B	304	2	TIMBER POLE SPLICE INTERFACE PLATE	N/A	S275J0	86.00 kg
15	15	205	1	M20 STUD C/W 4No NUTS & 2No SQ WSH	450mm	GRADE 8.8	1.11 kg
16	16	200	1	FEEDER COVER - 2/CG/100	3500mm	UV RESISTANT PLASTIC	-
17	17	200	17	FEEDER CLAMP - 2/FCD/028	N/A	POLYPROPYLENE	-
18	18	200	17	M10 SCREW DOWELS WTH M10 NUT	100mm	STAINLESS STEEL	-
19	19	200	1	PoleSaver	750mm	N/A	-
20	20	200	9	M12 STUD + 4No NUTS + 2No FLAT WASHERS + 1No Ø50mm WASHER (FOR FALL ARREST SYSTEM)	500mm	GRADE 8.8	-
Total Weight:							378.26 kg

- All steel hot dip galvanized
- All U-BOLTS to be FLA supply, each Supplied with 4 Full Nuts, 2 Flat Washers and 2 Spring Washers

NOTES:

1. WELDING TO BE IN ACCORDANCE WITH BS EN 1011-1:2009
2. LINEAR DIMS TO BE WITHIN ±1mm;
3. ANGULAR TOLERANCES TO BE WITHIN 0.5°
4. WELDING SYMBOLS ARE IN ACCORDANCE WITH BS EN 22553:1995
5. ALL PROFILE EDGES TO BE DRESSED AND SHARP CORNERS REMOVED
6. ALL WELD SIZES ARE FINAL SIZES
7. ALL WELDED JOINTS ARE TO BE PICKLE TIGHT
8. ALL STEELWORK TO BE BS EN 10025 GRADE S275 J0 UNO, HOT DIPPED GALVANISED TO BS EN ISO 1461. (ALL HOLLOW SECTIONS TO BE GRADE S355 J0H)
9. ALL STEEL IS TO BE SUPPLIED IN ACCORDANCE WITH EN 1090 TO EXECUTION CLASS 2
10. ALL NON PRE-LOADED BOLTS TO BE COMPLIANT STRUCTURAL BOLTS TO BS EN ISO 15048 PARTS 1&2.
11. STEELWORK COMPONENTS SHALL BE HOT DIP GALVANISED TO ACHIEVE A "VERY HIGH" DURABILITY FOR AN ENVIRONMENT CATEGORY CODE C4 FROM TABLE 1 IN BS EN ISO 14713
12. BOLTS AND NUTS SHALL BE SUPPLIED IN ACCORDANCE WITH BS 7371, SPUN GALVANISED IN ACCORDANCE WITH ISO 10684, THE NUTS RE-TAPPED AFTER GALVANISING, AND THE THREADS TREATED WITH GREASE.
13. ALL BOLTS TO BE CUT ON SITE TO EXTEND MAX 10mm BEYOND THE NUT WHEN TIGHTENED UNO.
14. ALL SITE DRILLED HOLE/CUT ENDS TO BE TREATED WITH METAFLUX 70-40 ZINC PASTE FOLLOWED BY 1 COAT OF 7-42 ZINC ALU OR 70-16 ALUMINIUM SPRAY

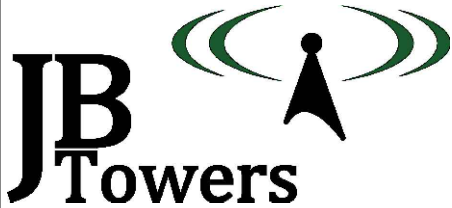

01	FIRST ISSUE	AM	14/02/20
REV	REV	BY	DATE
SCALE AS SHOWN WHEN PRINTED AT A3	DRAWN AM DATE 14/02/20	CHECKED MP DATE 14/02/20	APPROVED JBT DATE 14/02/20
ALL DIMENSIONS IN mm UNLESS OTHERWISE STATED. THIS DRAWING TO BE READ IN CONJUNCTION WITH OTHER RELEVANT DRAWINGS.			

TITLE
PARTS LIST

SITE ADDRESS
TIRYMYNACH
COMMUNITY COUNCIL
PLAYING FIELDS
ABERYSTWTH
CEREDIGION
SY24 5BW

ARQIVA REF.
140234


DRG No.
305

REV
01


ALL SCALES AS SHOWN WHEN PRINTED AT A3




ALL SCALES AS SHOWN WHEN PRINTED AT A3

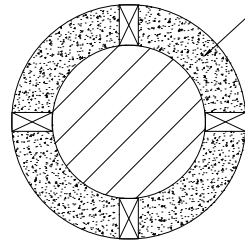

INSTALLATION
PLAN VIEW
Scale 1:20

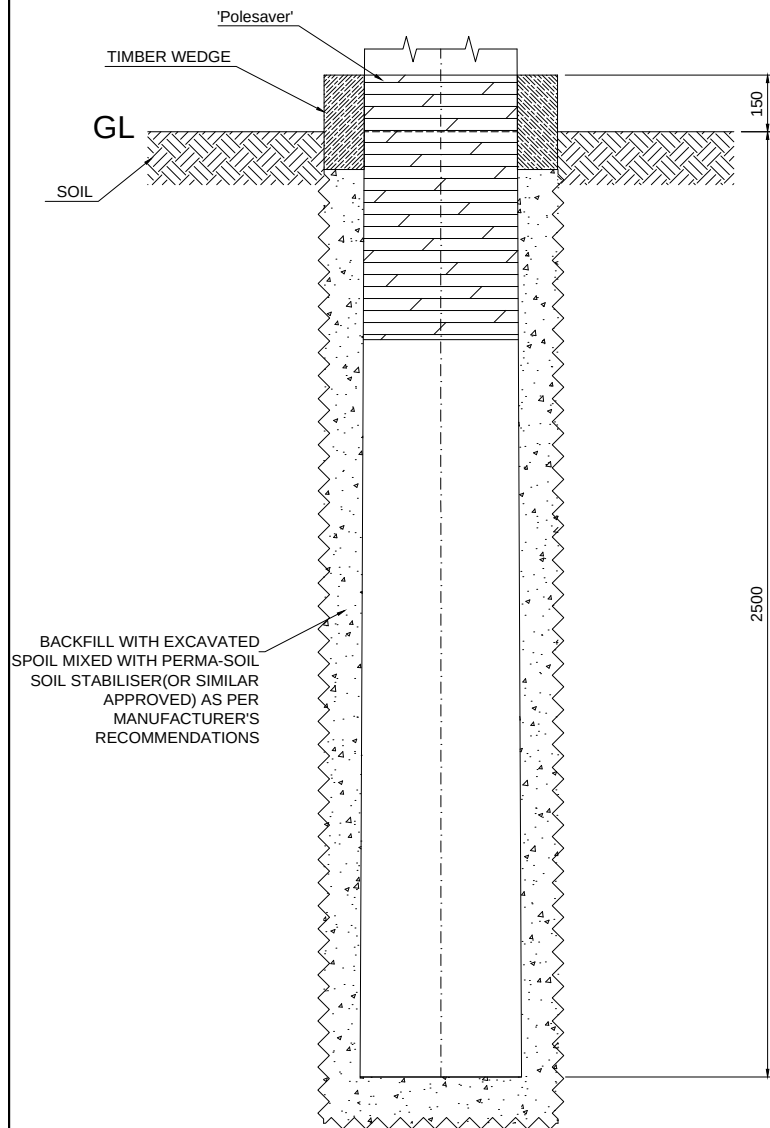


INSTALLATION
ELEVATION
Scale 1:20

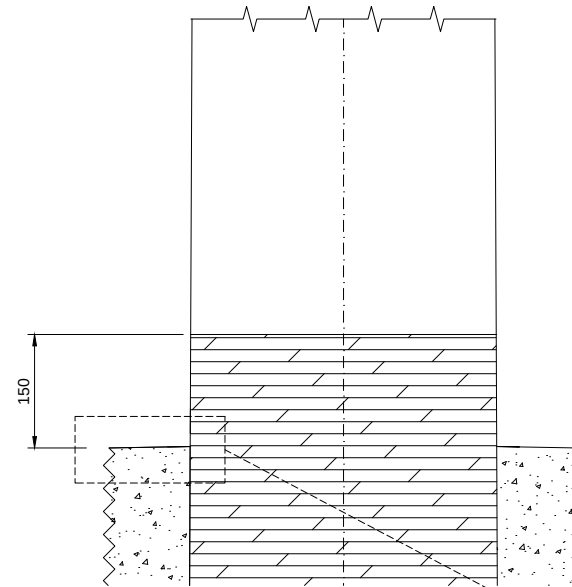


WATER PROOFING
Scale 1:10

TIMBER POLE INSTALLATION:

1. REFER TO DRG 200 FOR TIMBER POLE ORIENTATION.
2. ANY OVERDIG AT BASE OF HOLE TO BE FILLED WITH EXCAVATED SPOIL MIXED WITH PERMA-SOIL STABILISER .
3. POLE TO BE WRAPPED IN 'POLESAVER' AND INSTALLED AND LEVELED IN OPENING. TIMBERS TO BE USED TO HOLD POLE IN POSITION & THEN ANNULUS FILLED WITH EXCAVATED SPOIL MIXED WITH PERMA-SOIL SOIL STABILISER.
4. REMOVE TIMBER WEDGES ONCE BACKFILL HAS ALMOST REACHED UNDERSIDE OF WEDGES & CONTINUE TO BACKFILL TO GL.
5. ALL BACK-FILL MATERIAL TO BE PLACED AND COMPACTED IN 150mm THICK LAYERS.

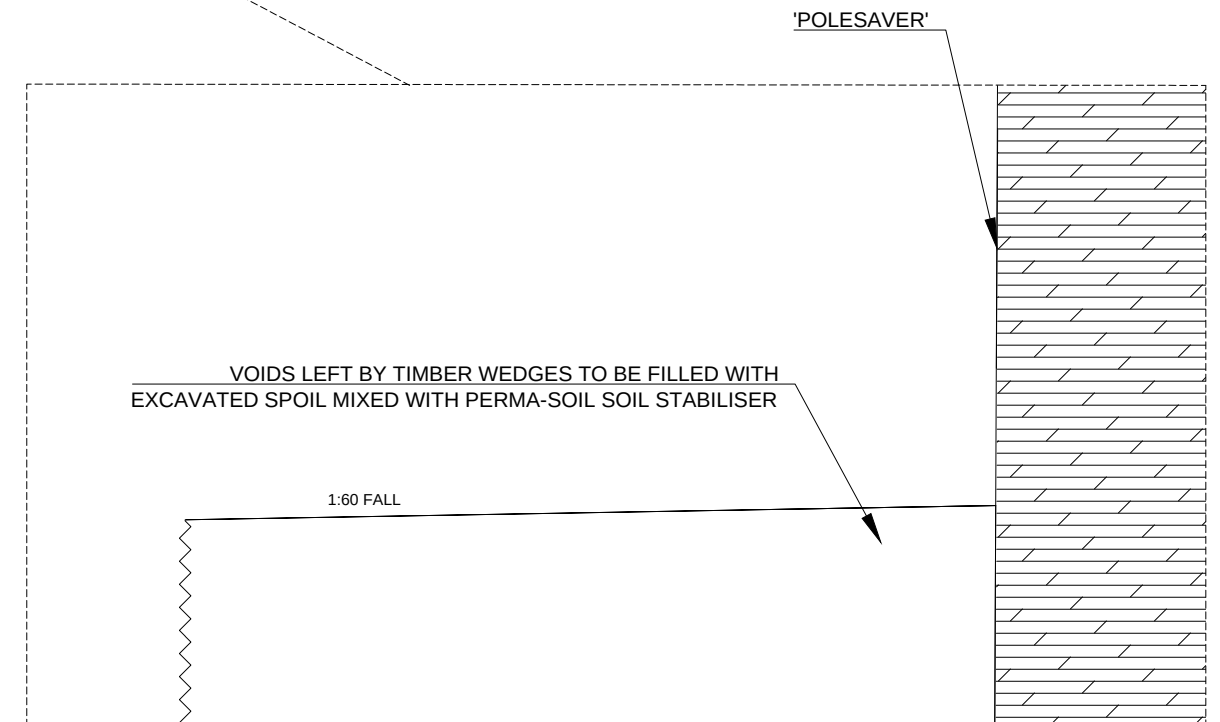

ENLARGED DETAIL
Scale 1:1

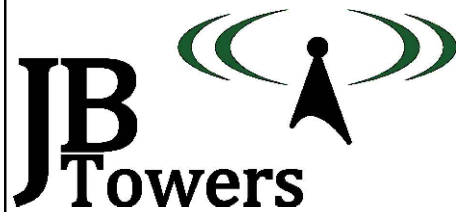

01	FIRST ISSUE	AM	14/02/20
REV	REV	BY	DATE
SCALE AS SHOWN WHEN PRINTED AT A3	DRAWN DATE 14/02/20	CHECKED DATE 14/02/20	APPROVED DATE 14/02/20
ALL DIMENSIONS IN mm UNLESS OTHERWISE STATED. THIS DRAWING TO BE READ IN CONJUNCTION WITH OTHER RELEVANT DRAWINGS.			

TITLE

FOUNDATION DETAILS

SITE ADDRESS

TIRYMYNACH
COMMUNITY COUNCIL
PLAYING FIELDS
ABERYSTWTH
CEREDIGION
SY24 5BW

ARQIVA REF.
140234

DRG No.
400

REV
01

ALL SCALES AS SHOWN WHEN PRINTED AT A3



ALL SCALES AS SHOWN WHEN PRINTED AT A3