
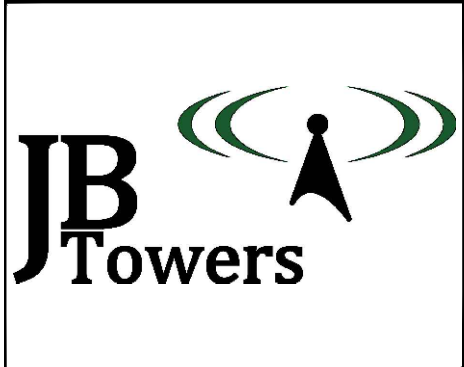


DRAWING ISSUE SHEET

[illegible]

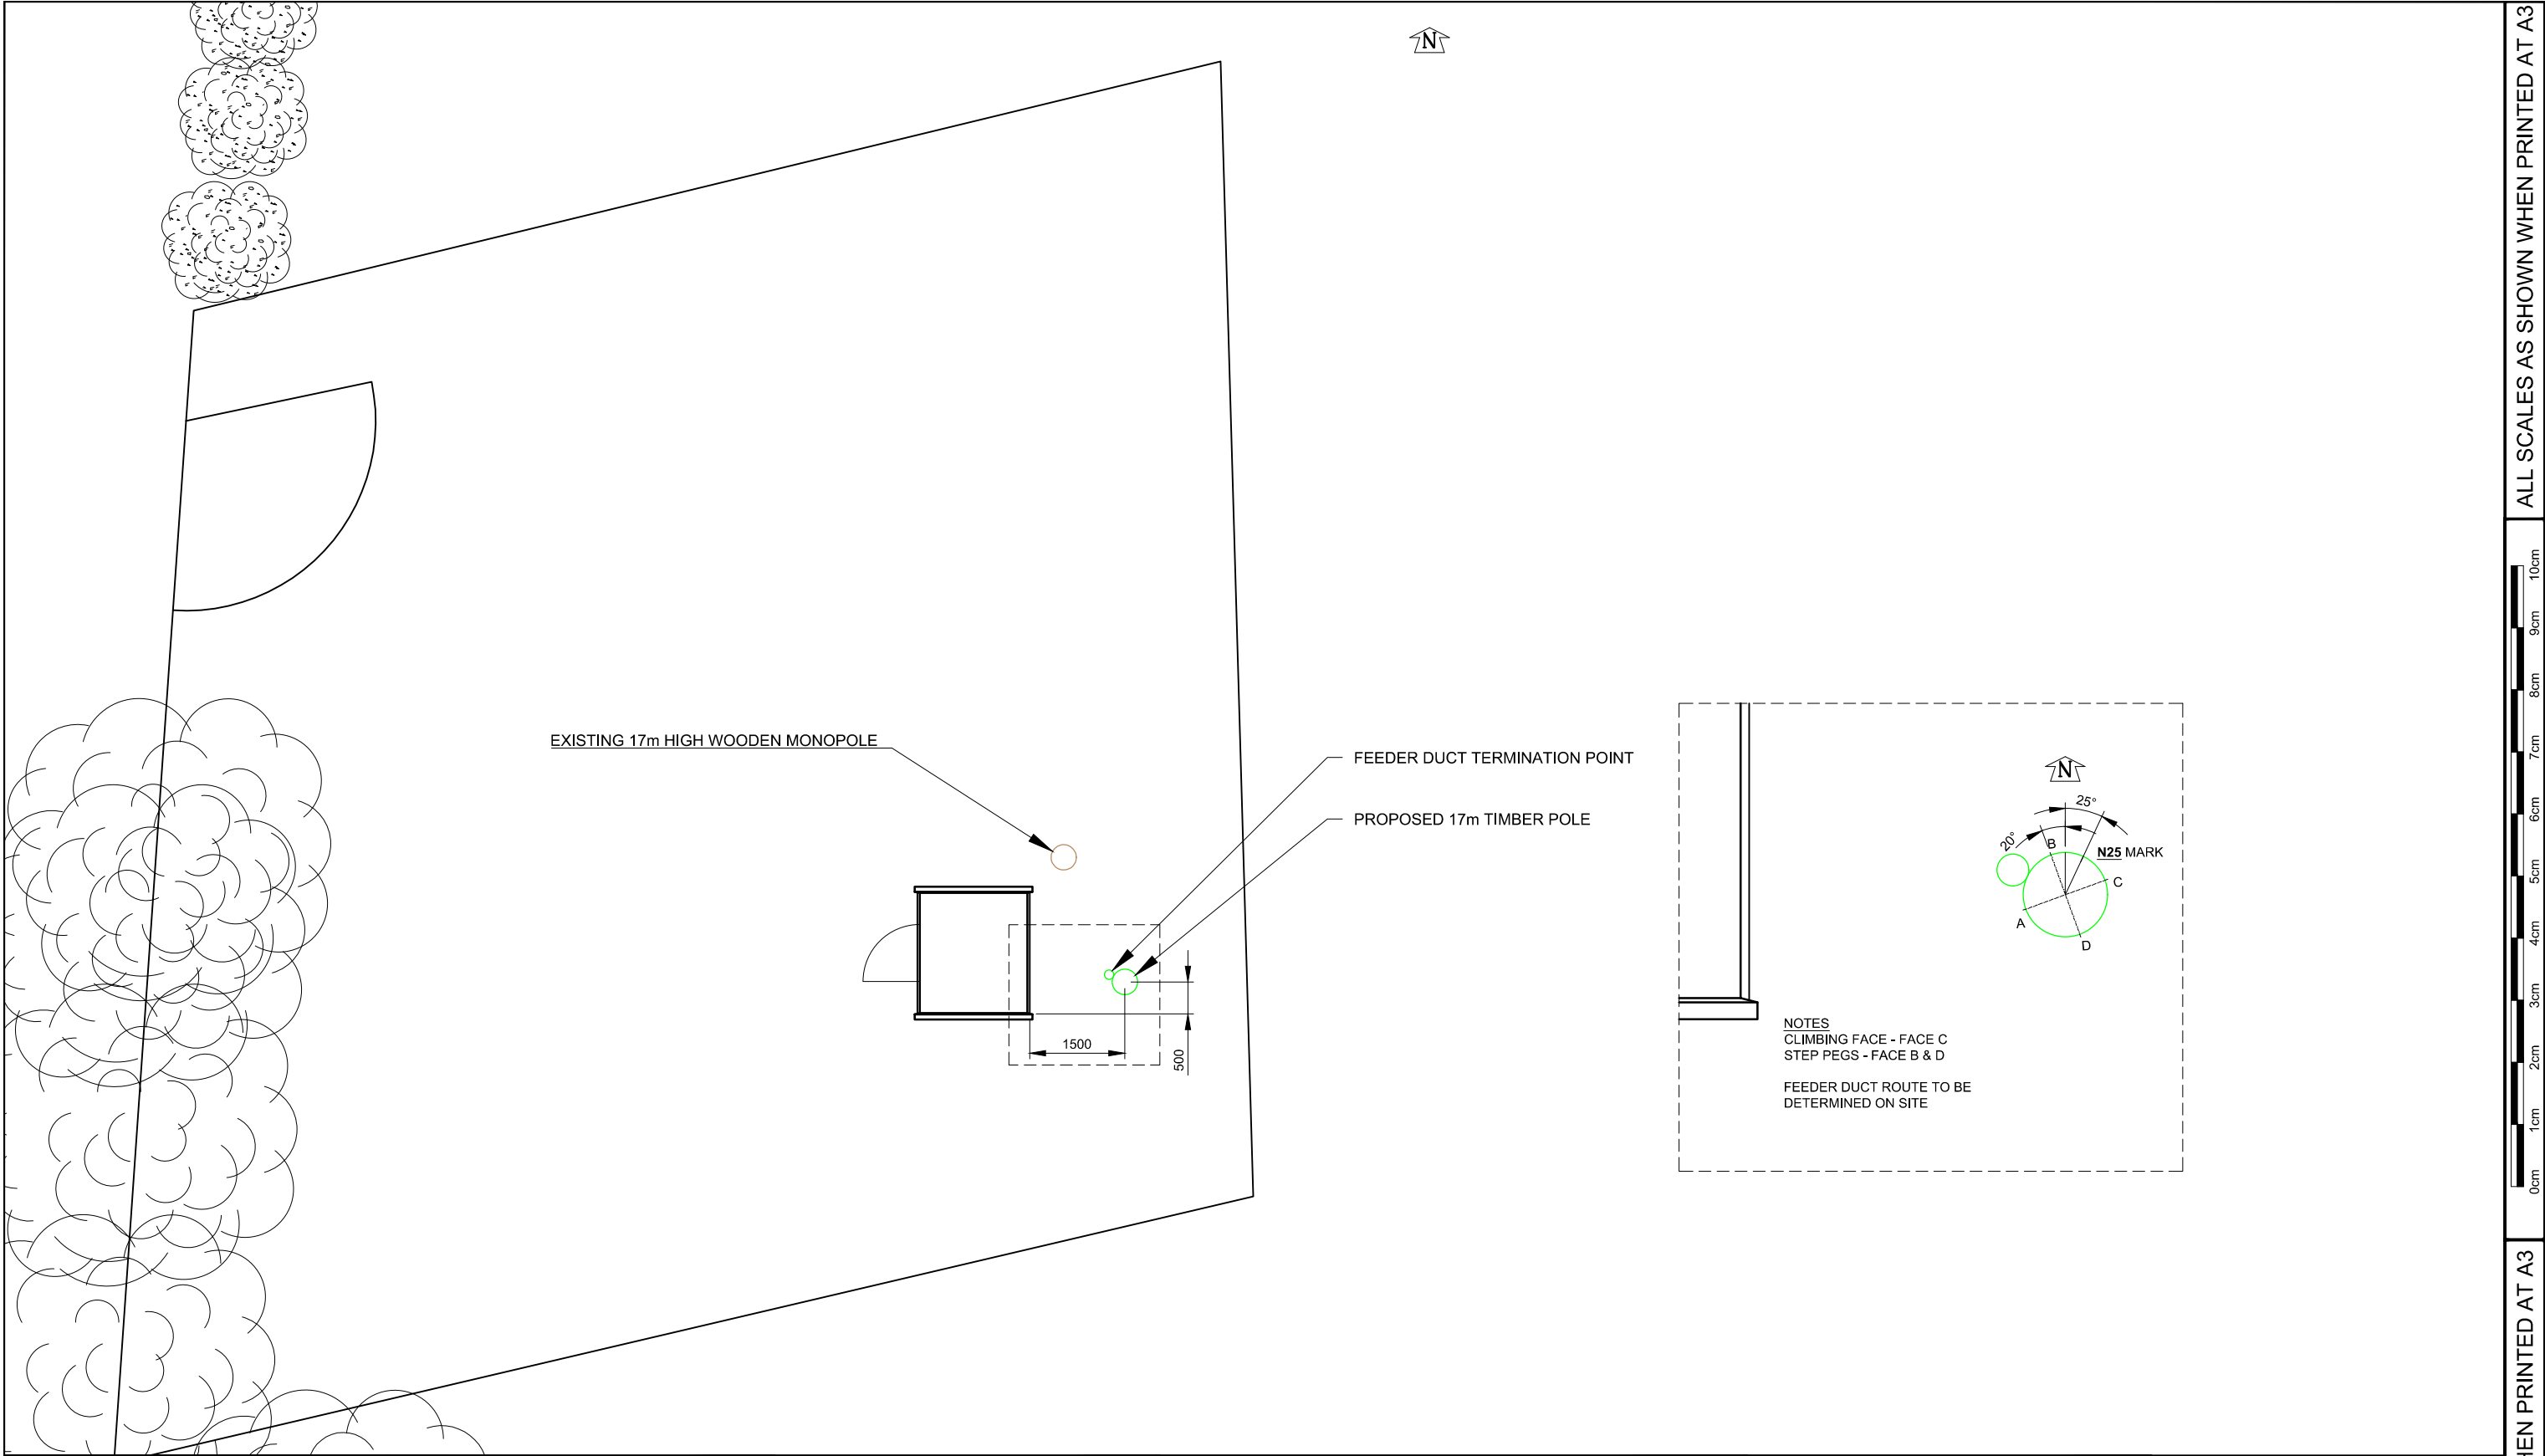


01	FIRST ISSUE			AM	15/05/20
REV	REV			BY	DATE
SCALE AS SHOWN WHEN PRINTED AT A3		DRAWN AM DATE 15/05/20	CHECKED MP DATE 15/05/20	APPROVED JBT DATE 15/05/20	
ALL DIMENSIONS IN mm UNLESS OTHERWISE STATED. THIS DRAWING TO BE READ IN CONJUNCTION WITH OTHER RELEVANT DRAWINGS.					

TITLE
CEMAES
SITE PLAN

SITE ADDRESS		
CARROG FARM LLANBADRIG ISLE OF ANGLESEY LL67 0LB		
ARQIVA REF. 140365	DRG No. 100	REV 01

ALL SCALES AS SHOWN WHEN PRINTED AT A3

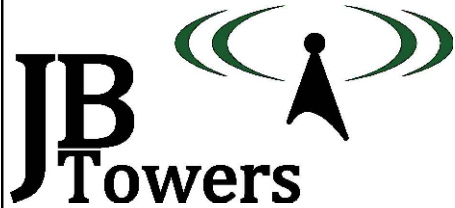

01	FIRST ISSUE			AM	15/05/20
REV	REV			BY	DATE
SCALE AS SHOWN		DRAWN	AM	CHECKED	MP
WHEN PRINTED AT A3		DATE	15/05/20	DATE	15/05/20
		APPROVED	JBT	DATE	15/05/20
ALL DIMENSIONS IN mm UNLESS OTHERWISE STATED. THIS DRAWING TO BE READ IN CONJUNCTION WITH OTHER RELEVANT DRAWINGS.					

TITLE

CEMAES

GENERAL ARRANGEMENT

SHEET 1 OF 3

SITE ADDRESS

CARROG FARM

LLANBADRIG

ISLE OF ANGLESEY

LL67 0LB

ARQIVA REF.



140365

DRG No.

200

REV

01

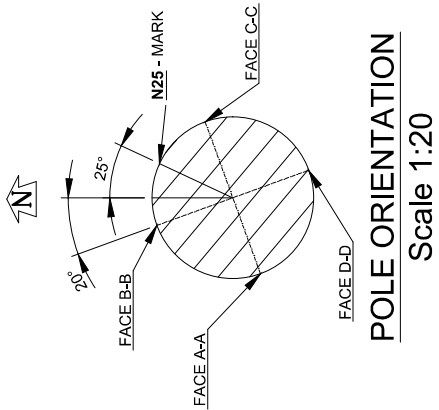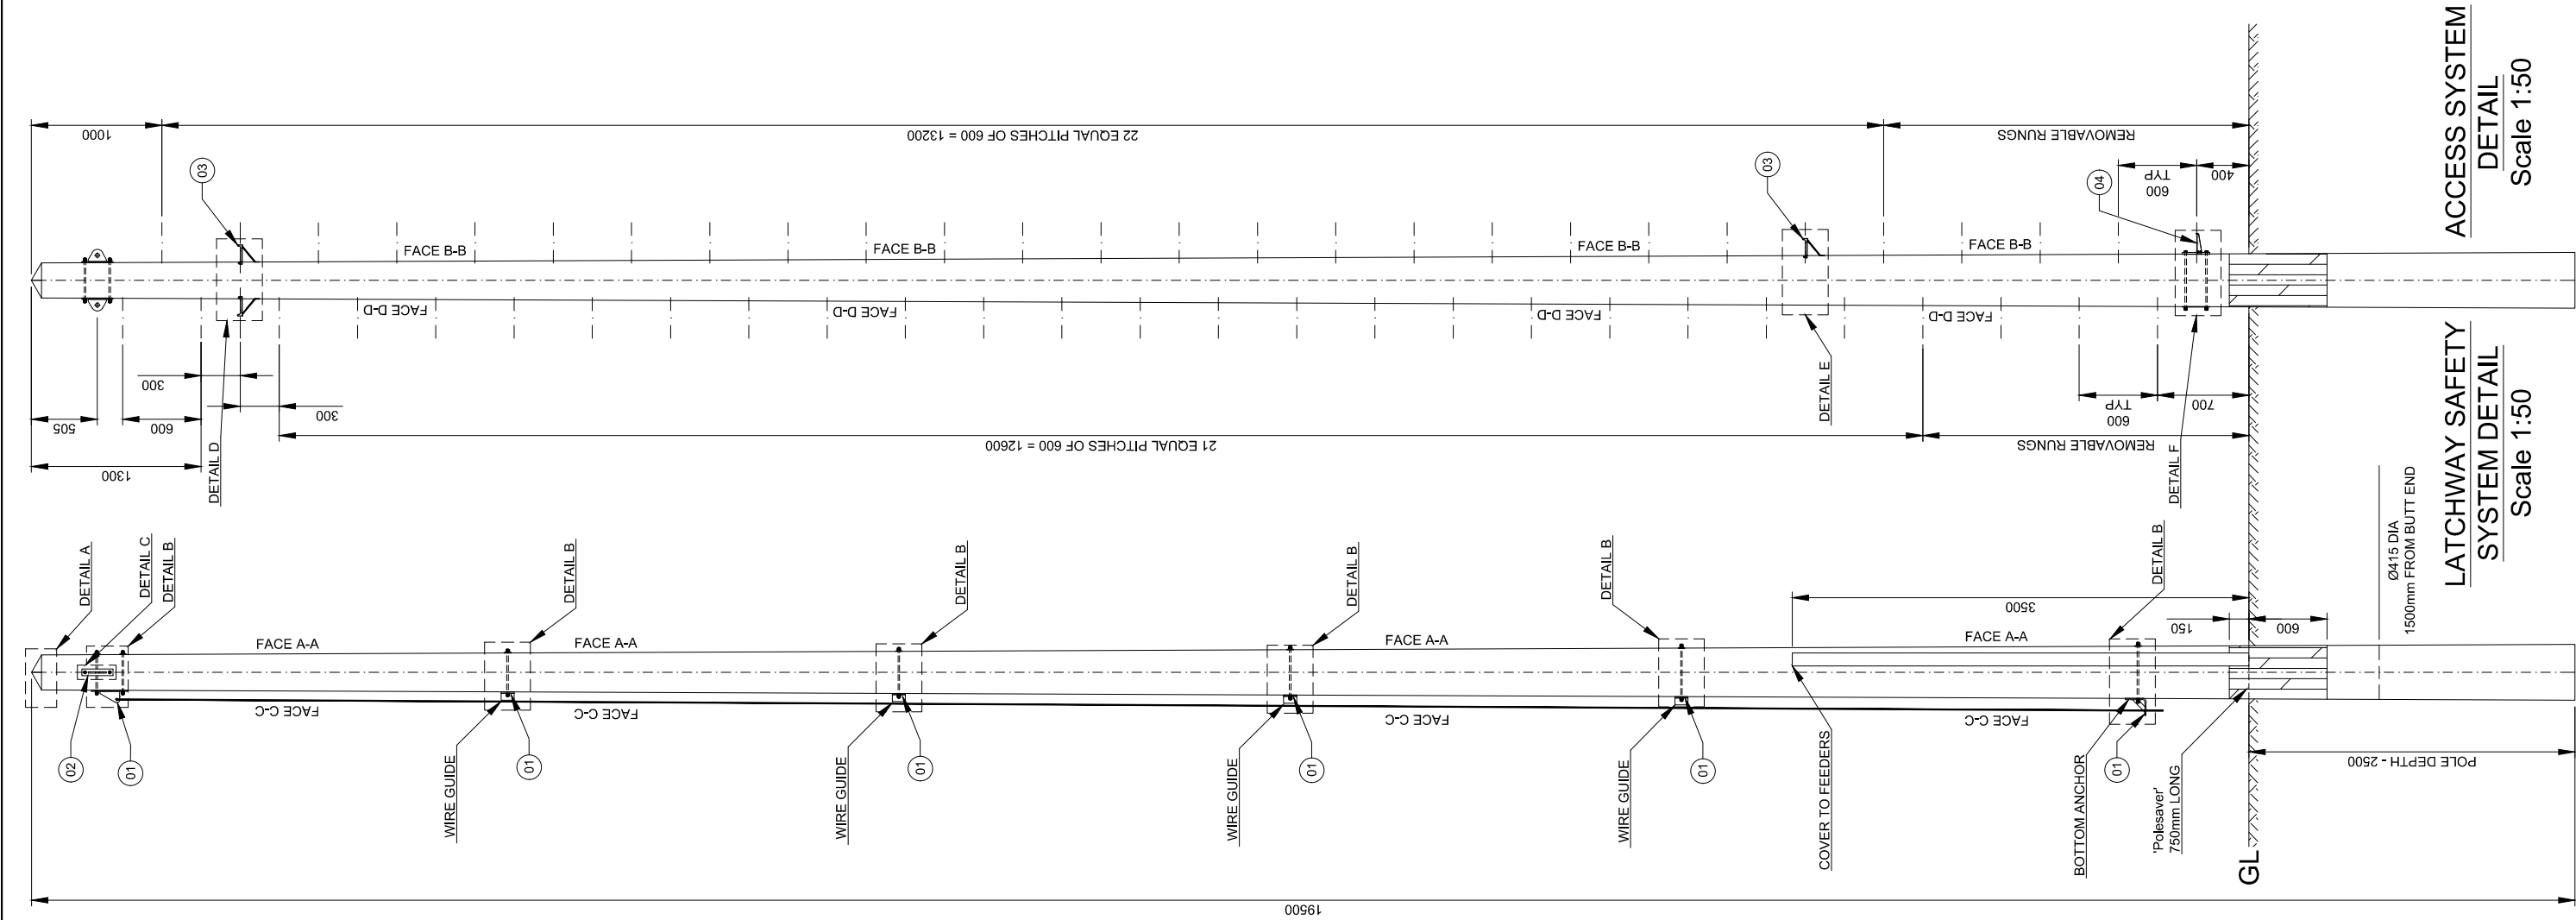

NOTES

1. SEE DRAWING 303 FOR PARTS LIST
2. ALL BOLTS TO BE CUT ON SITE TO EXTEND MAX 10mm BEYOND THE NUT WHEN TIGHTENED UNO.
3. ALL SITE DRILLED HOLE/CUT ENDS TO BE TREATED WITH METALUX 70-40 ZINC PASTE FOLLOWED BY 1 COAT OF 7-42 ZINC ALU OR 70-16 ALUMINIUM SPRAY

TIMBER POLE

1. POLE TO BE SUPPLIED IN ACCORDANCE WITH BS EN14229 & SHALL HAVE MIN. CHARACTERISTIC BENDING STRENGTH OF 30N/mm2 & MIN. YOUNGS MODULUS (PARALLEL TO GRAIN) OF 10kN/mm2.
2. MARKINGS ON FINISHED POLE SHALL BE AT 4m FROM BUTT AND COMPLY WITH BS EN 14229 UNO
3. AS FAR AS PRACTICABLE ALL CUTTING, SCARFING & DRILLING TO BE DONE BEFORE CREOSOTING. IF NOT ALL CUT, DRILLED & SCARFED SURFACES TO BE COATED WITH A MIXTURE OF CREOSOTE & TAR.
4. POLE TO BE PRESSURE IMPREGNATED WITH CREOSOTE IN ACCORDANCE WITH BS EN 14229
5. MINIMUM DIAMETERS
TOP - Ø205mm
BOTTOM - Ø430mm
6. 19.5m LONG POLE TO BE SOURCED BY TRIMMING 20m LONG POLE BY 0.5m AT THE TOP

PLANTING


1. CAT SCANNER IS TO BE USED IN ORDER TO CONFIRM THE POSITIONS OF BURIED SERVICES.
2. TIMBER POLE TO BE PLANTED WITH **N25** MARKING AT 3.5m FROM BUT FACING 25° FROM NORTH (CLOCKWISE)
3. SEE DRAWING 400 FOR FOUNDATION DETAILS

ACCESS SYSTEM
DETAIL
Scale 1:50

LATCHWAY SAFETY
SYSTEM DETAIL
Scale 1:50

ALL SCALES AS SHOWN WHEN PRINTED AT A3

ALL SCALES AS SHOWN WHEN PRINTED AT A3

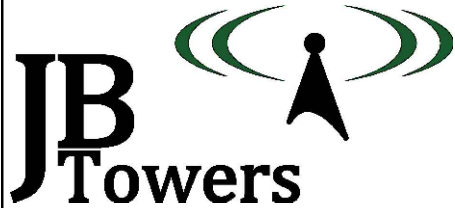

01	FIRST ISSUE			AM	15/05/20
REV	REV			BY	DATE
SCALE AS SHOWN		DRAWN	AM	CHECKED	MP
WHEN PRINTED AT A3		DATE	15/05/20	DATE	15/05/20
		APPROVED		JBT	
		DATE		15/05/20	
ALL DIMENSIONS IN mm UNLESS OTHERWISE STATED. THIS DRAWING TO BE READ IN CONJUNCTION WITH OTHER RELEVANT DRAWINGS.					

TITLE

CEMAES

GENERAL ARRANGEMENT

SHEET 2 OF 3

SITE ADDRESS

CARROG FARM

LLANBADRIG

ISLE OF ANGLESEY

LL67 0LB

ARQIVA REF.



140365

DRG No.

200

REV

01

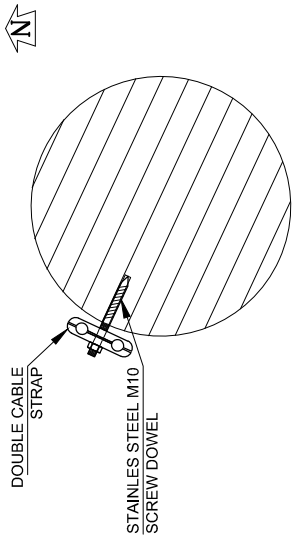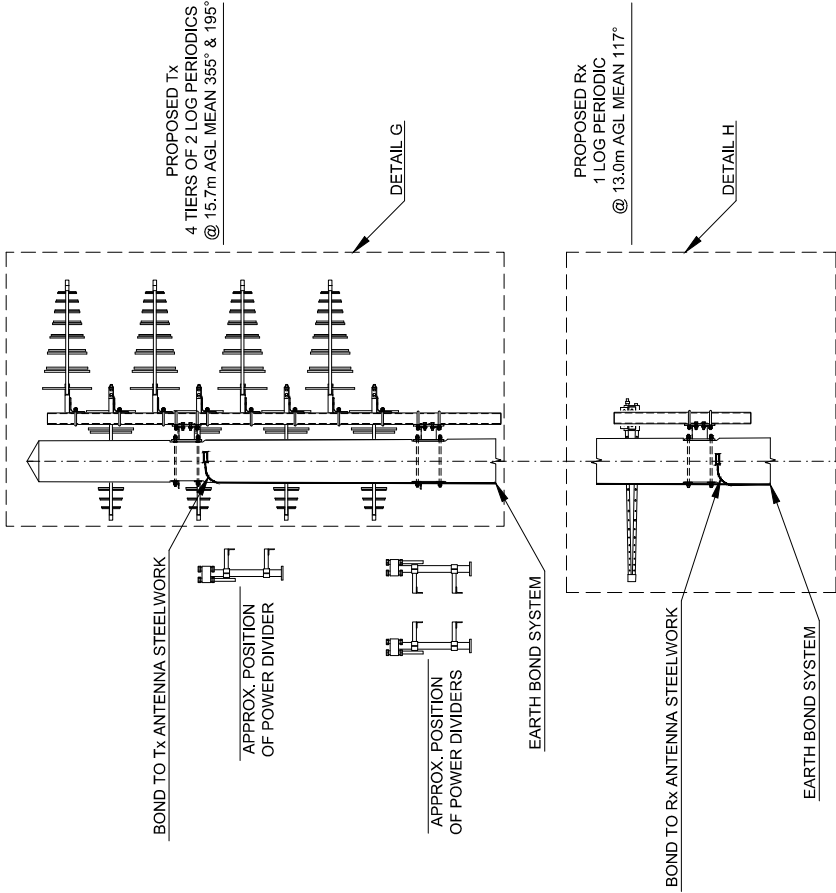

FEEDER
MANAGEMENT

Scale 1:10

NOTES

1. AS FAR AS IS PRACTICABLE ALL CUTTING SCARFING AND DRILLING TO BE DONE BEFORE CREOSOTING. WHERE THIS IS NOT POSSIBLE ALL CUT, DRILLED, AND SCARFED SURFACES TO BE COATED WITH A MIXTURE OF CREOSOTE AND TAR

FEEDERS


1. SUPPLY OF FEEDERS BY OTHERS
LCF7/8-50 TO Tx ANTENNA &
LCF12-50 TO Rx ANTENNA
2. FEEDERS FIXED AT 1000mm CENTRES

EARTHING


1. CONNECT EARTH BOND TO NEW
EARTHING SYSTEM
2. MAXIMUM VALUE FOR GROUND
RESISTANCE TO BE 10 OHMS
3. CABLE OR TAPE TO BE FIXED TO POLE
AT 1000mm CENTRES
4. EARTHING SHOULD COMPLY WITH
ARQIVA'S DOCUMENT BOS147

ANTENNA AND EARTHING
ARRANGEMENT

Scale 1:50

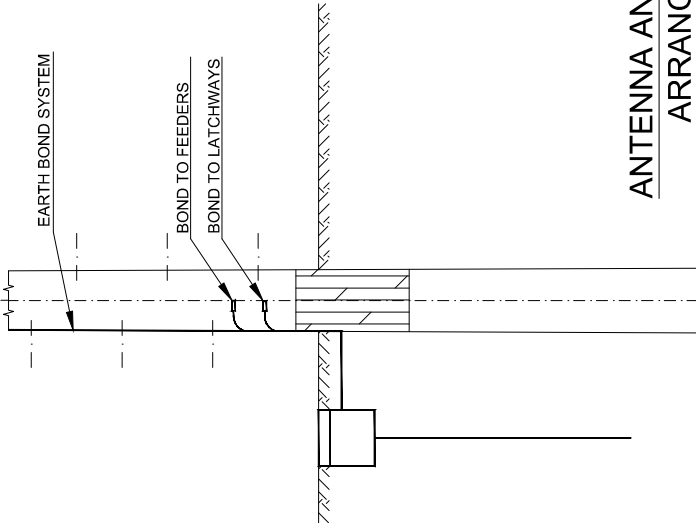


ALL SCALES AS SHOWN WHEN PRINTED AT A3

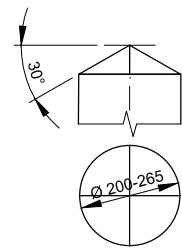


- NOTES:
1. A SINGLE COAT OF TIMBER COMPATIBLE BITUMINOUS PAINT (E.G. BIRD BRAND BLACK BITUMINOUS PAINT OR SIMILAR APPROVED PRODUCT) TO BE APPLIED TO THE UPPER SURFACES AT THE TOP OF THE POLE.
 2. PAINT TO BE APPLIED ON SITE JUST BEFORE ERECTION
- FORM: 4 WAY PYRAMID / CONE


DETAIL A - TIMBER POLE TOP
Scale 1:20

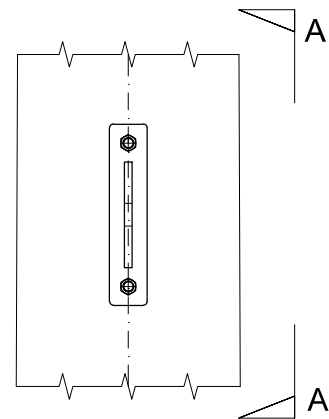


DETAIL C - FALL ARREST
ATTACHMENT POINT
Scale 1:10

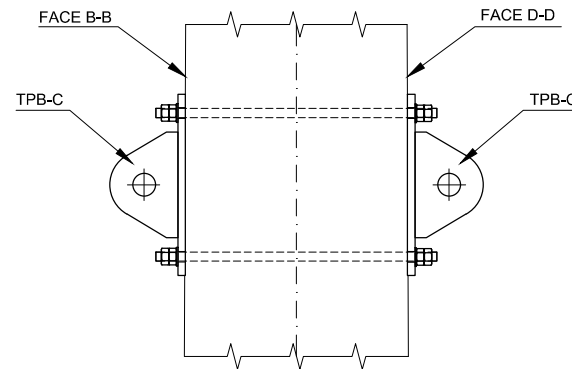


VIEW A-A
Scale 1:10

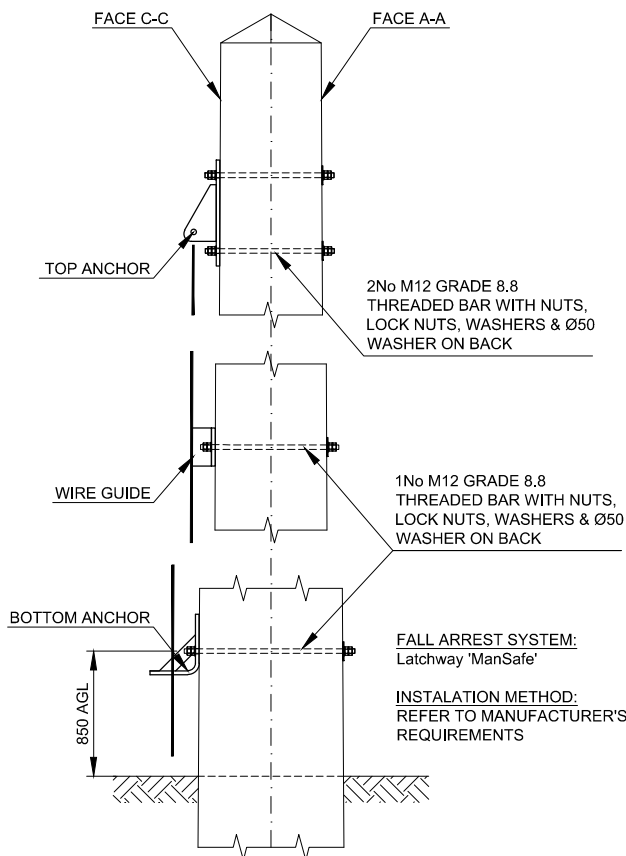


DETAIL B - FALL ARREST SYSTEM
Scale 1:20

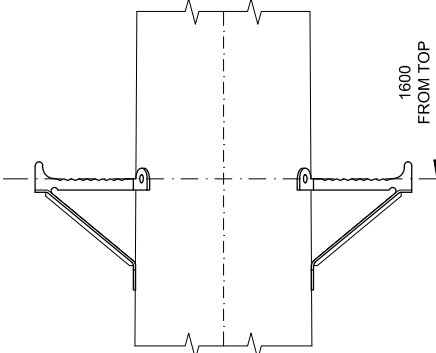


DETAIL D - ANTENNA
ACCESS CLIMBING STEP
Scale 1:10

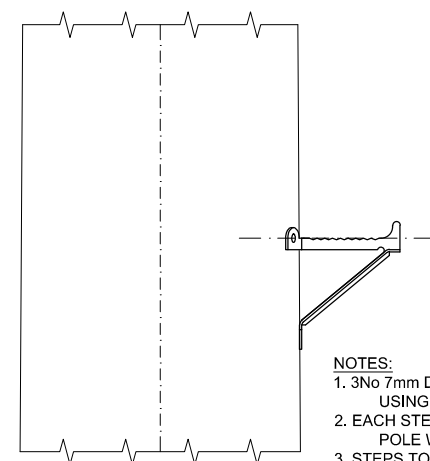

DETAIL E - PERMANENT
CLIMBING STEPS
Scale 1:10

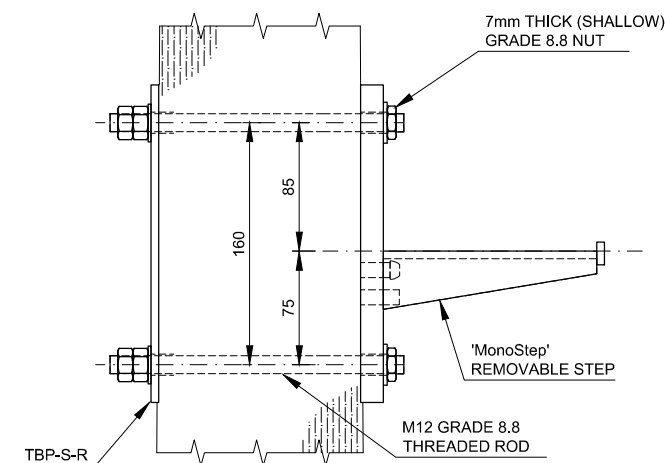

DETAIL F - REMOVABLE
CLIMBING STEPS
Scale 1:5

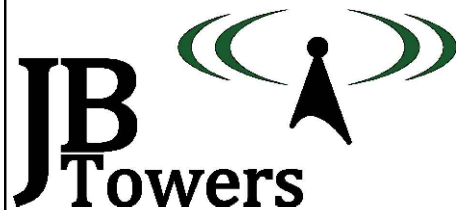

01	FIRST ISSUE	AM	15/05/20
REV	REV	BY	DATE
SCALE AS SHOWN WHEN PRINTED AT A3	DRAWN DATE 15/05/20	CHECKED DATE 15/05/20	APPROVED DATE 15/05/20
ALL DIMENSIONS IN mm UNLESS OTHERWISE STATED. THIS DRAWING TO BE READ IN CONJUNCTION WITH OTHER RELEVANT DRAWINGS.			

TITLE
CEMAES
GENERAL ARRANGEMENT
SHEET 3 OF 3


SITE ADDRESS
CARROG FARM
LLANBADRIG
ISLE OF ANGLESEY
LL67 0LB

ARQIVA REF.
140365
DRG No.
200
REV
01

ALL SCALES AS SHOWN WHEN PRINTED AT A3



ALL SCALES AS SHOWN WHEN PRINTED AT A3

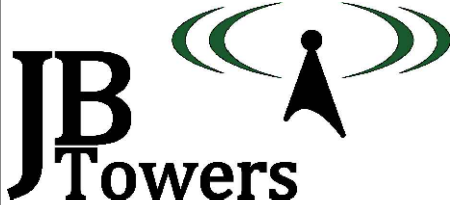

01	FIRST ISSUE			AM	15/05/20
REV	REV			BY	DATE
SCALE AS SHOWN		DRAWN	AM	CHECKED	MP
WHEN PRINTED AT A3		DATE	15/05/20	DATE	15/05/20
		APPROVED	JBT	DATE	15/05/20
ALL DIMENSIONS IN mm UNLESS OTHERWISE STATED. THIS DRAWING TO BE READ IN CONJUNCTION WITH OTHER RELEVANT DRAWINGS.					

TITLE

CEMAES

TIMBER POLE HOLE SET OUT

SHEET 1 OF 2

SITE ADDRESS

CARROG FARM

LLANBADRIG

ISLE OF ANGLESEY

LL67 0LB

ARQIVA REF.




140365

DRG No.

201


REV

01

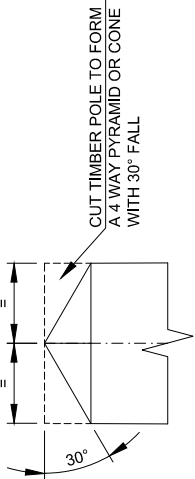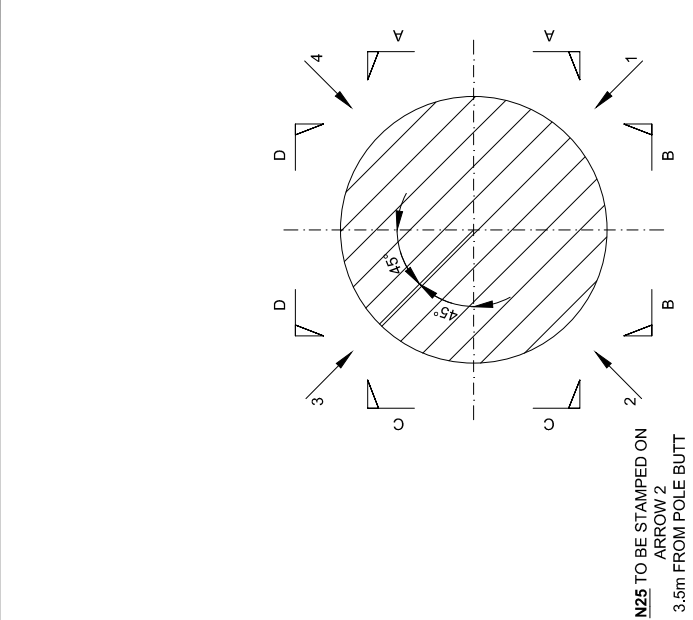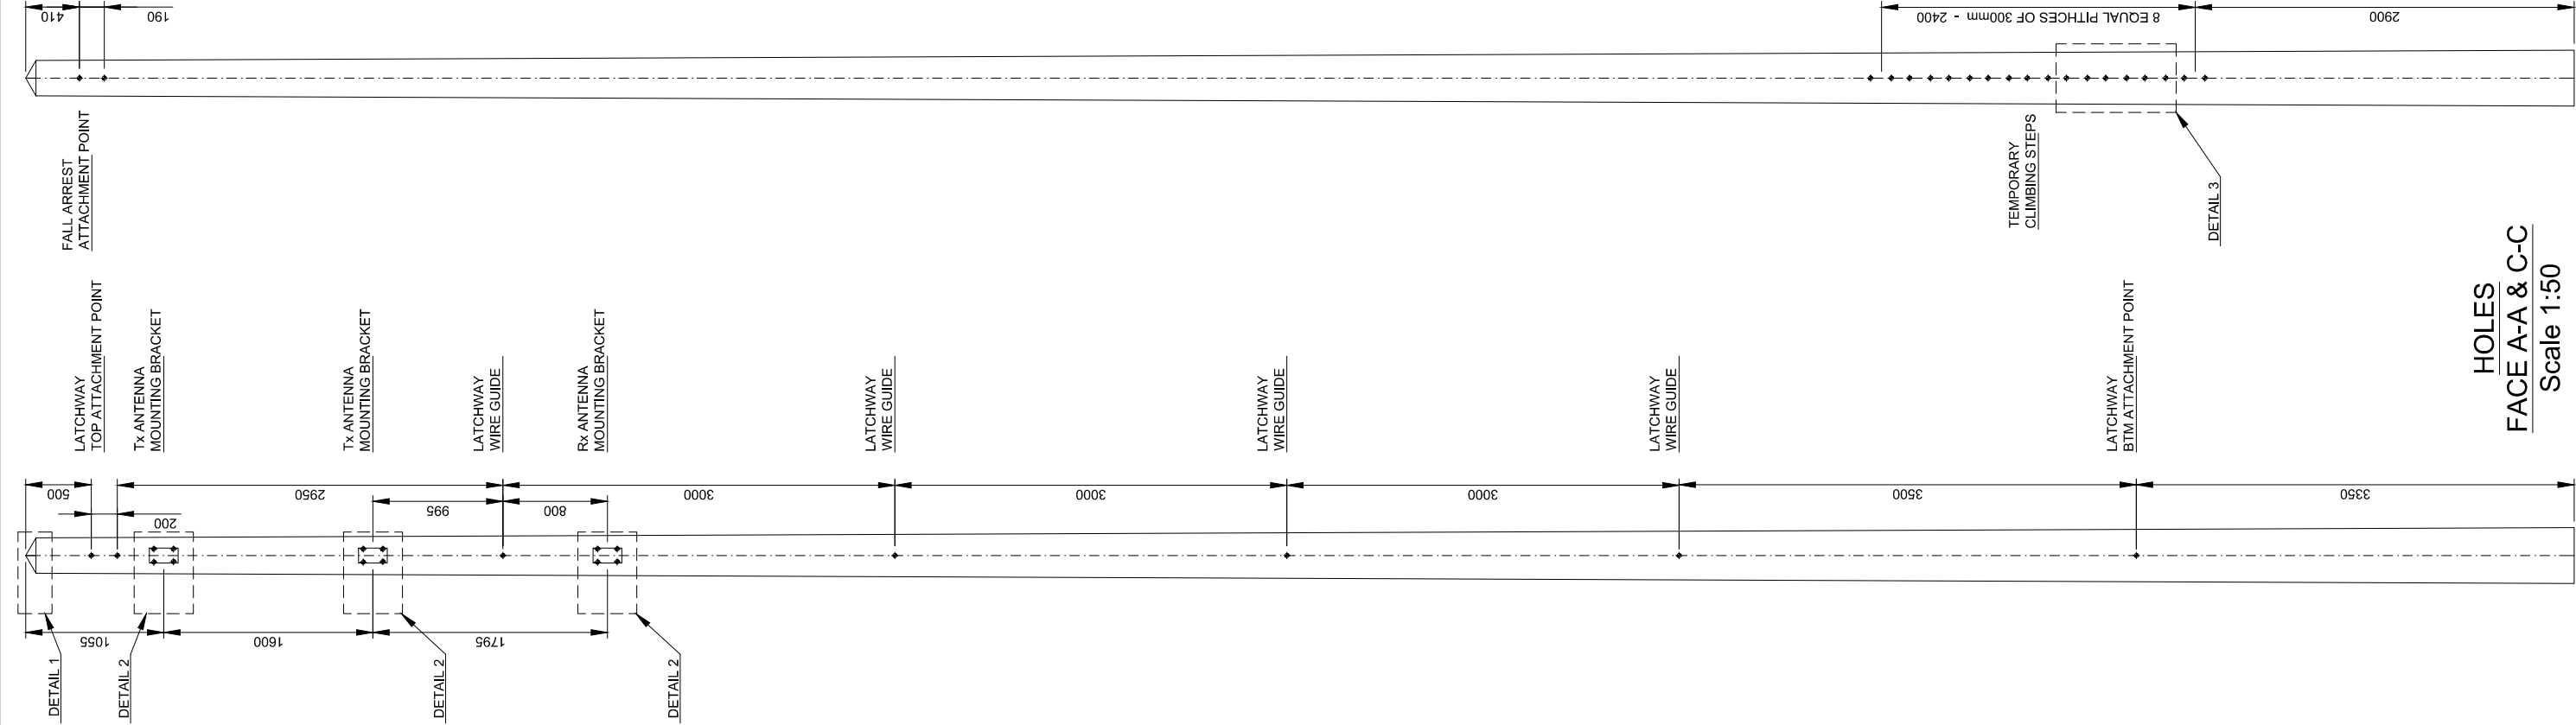


DETAIL 1

Scale 1:10

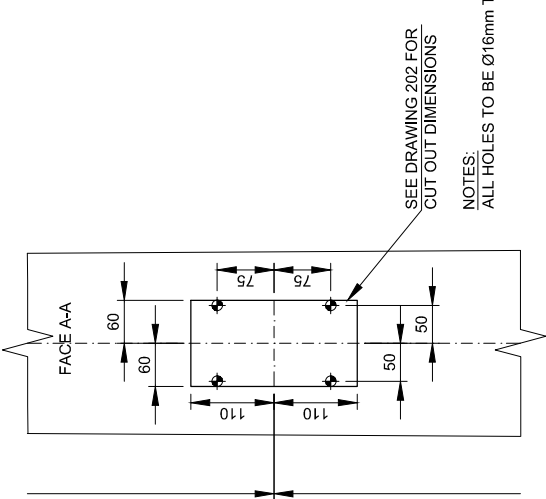

DETAIL 2 - TYPICAL

Scale 1:10

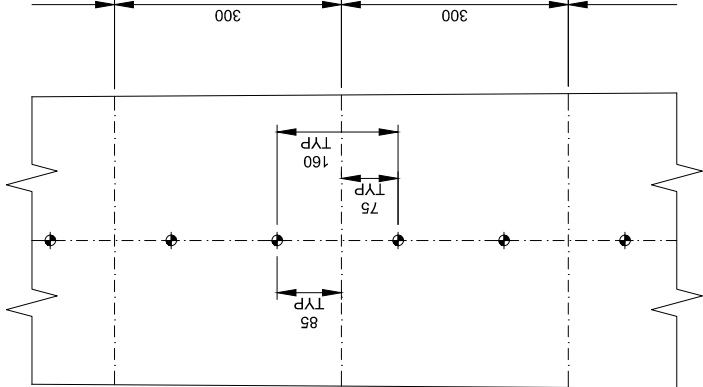

DETAIL 3 - TYPICAL

Scale 1:10

HOLES


FACE B-B & D-D

Scale 1:50

HOLES


FACE A-A & C-C

Scale 1:50

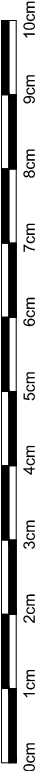

ALL SCALES AS SHOWN WHEN PRINTED AT A3

ALL SCALES AS SHOWN WHEN PRINTED AT A3

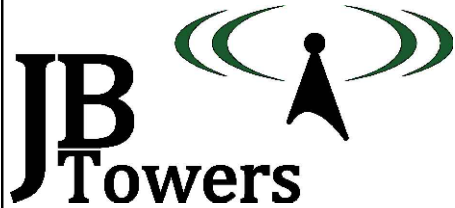

01	FIRST ISSUE			AM	15/05/20
REV	REV			BY	DATE
SCALE AS SHOWN		DRAWN	AM	CHECKED	MP
WHEN PRINTED AT A3		DATE	15/05/20	DATE	15/05/20
		DATE	15/05/20	DATE	15/05/20
ALL DIMENSIONS IN mm UNLESS OTHERWISE STATED. THIS DRAWING TO BE READ IN CONJUNCTION WITH OTHER RELEVANT DRAWINGS.					

TITLE

CEMAES

TIMBER POLE HOLE SET OUT

SHEET 2 OF 2

SITE ADDRESS

CARROG FARM

LLANBADRIG

ISLE OF ANGLESEY

LL67 0LB

ARQIVA REF.



140365

DRG No.

201

REV


01

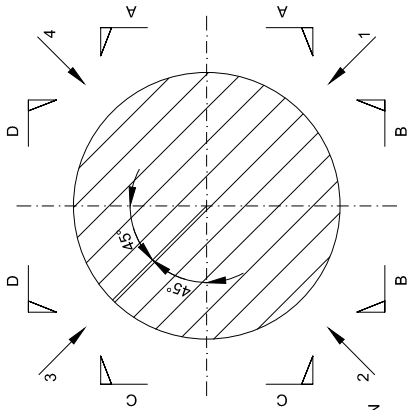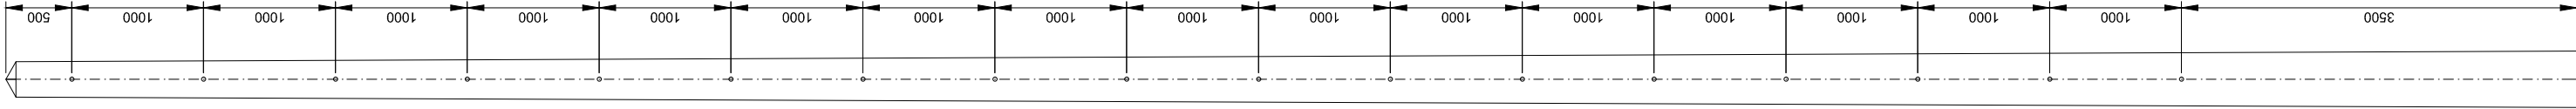

N25 TO BE STAMPED ON
ARROW 2
3.5m FROM POLE BUTT

ALL HOLES ON ARROW 1
TO BE Ø8mm & 70mm LONG

HOLES
ARROW 1
Scale 1:50

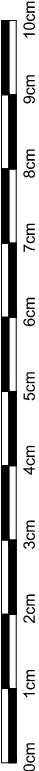

ALL SCALES AS SHOWN WHEN PRINTED AT A3

ALL SCALES AS SHOWN WHEN PRINTED AT A3


HOLE DIAMETERS



01	FIRST ISSUE							AM	15/05/20
REV	REV							BY	DATE
SCALE AS SHOWN		DRAWN	AM	CHECKED	MP	APPROVED		JBT	
WHEN PRINTED AT A3		DATE	15/05/20	DATE	15/05/20	DATE		15/05/20	
ALL DIMENSIONS IN mm UNLESS OTHERWISE STATED. THIS DRAWING TO BE READ IN CONJUNCTION WITH OTHER RELEVANT DRAWINGS.									

TITLE
CEMAES
TIMBER POLE CUT OUT
DETAIL

SITE ADDRESS
CARROG FARM
LLANBADRIG
ISLE OF ANGLESEY
LL67 0LB

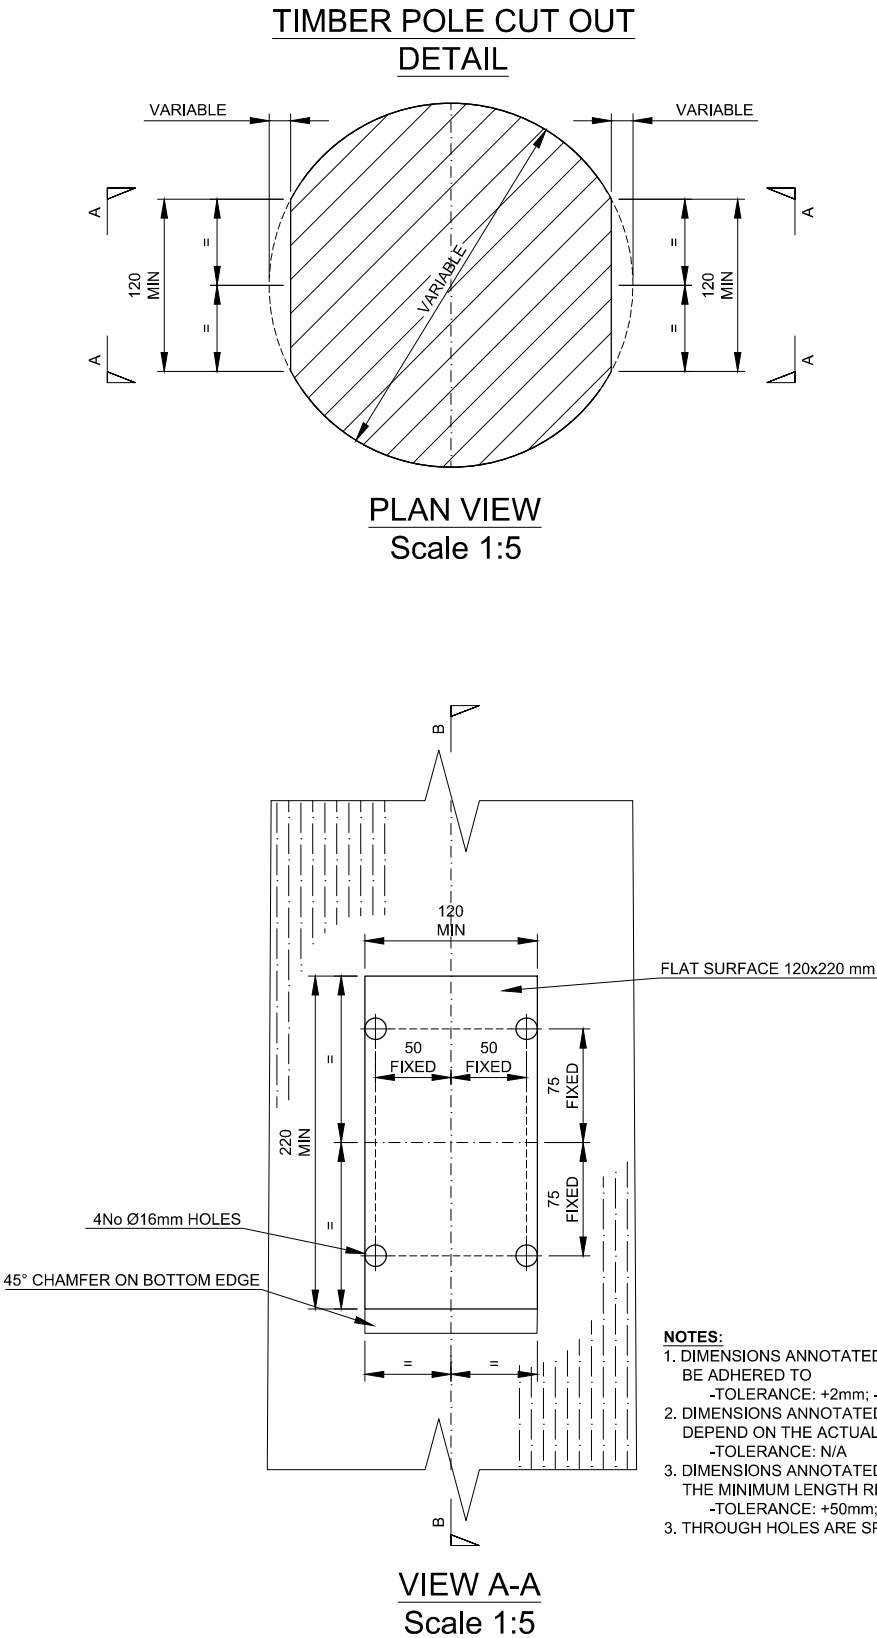




DETAIL G - Tx ANTENNA MOUNT
Scale 1:20




SECTION B-E
Scale 1:20

POSITION OF POWER
DIVIDER
TO BE DETERMINED
ON SITE

POSITION OF POWER
DIVIDERS
TO BE DETERMINED
ON SITE

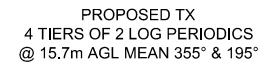

SECTION A-A
Scale 1:20

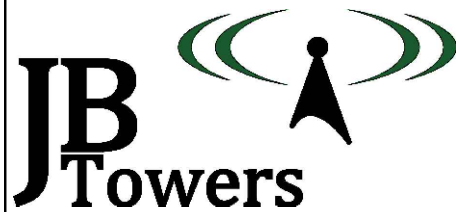

01	FIRST ISSUE			AM	15/05/20
REV	REV			BY	DATE
SCALE AS SHOWN WHEN PRINTED AT A3		DRAWN AM DATE 15/05/20	CHECKED MP DATE 15/05/20	APPROVED JB DATE 15/05/20	
ALL DIMENSIONS IN mm UNLESS OTHERWISE STATED. THIS DRAWING TO BE READ IN CONJUNCTION WITH OTHER RELEVANT DRAWINGS.					

TITLE

CEMAES

Tx ANTENNA MOUNT


DETAIL G

SITE ADDRESS


CARROG FARM
LLANBADRIG
ISLE OF ANGLESEY
LL67 0LB

ARQIVA REF.
140365

DRG No.
203REV
01

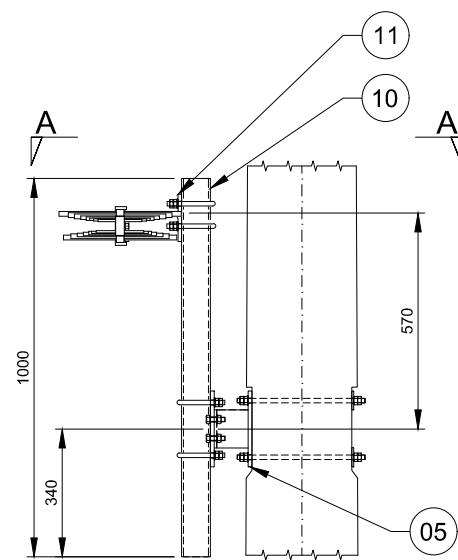

DETAIL H - Rx ANTENNA MOUNT
Scale 1:20

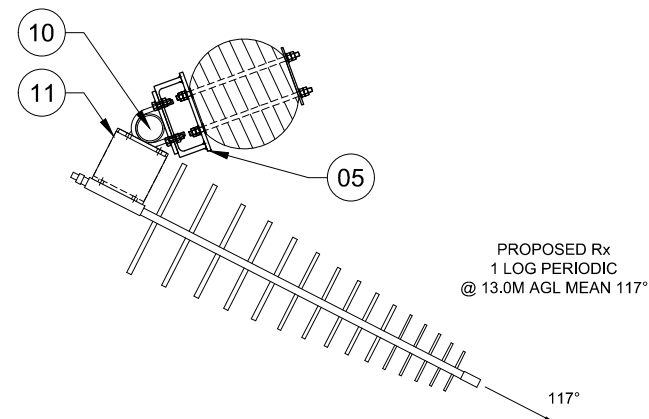


SECTION A-A
Scale 1:20

ALL SCALES AS SHOWN WHEN PRINTED AT A3



ALL SCALES AS SHOWN WHEN PRINTED AT A3

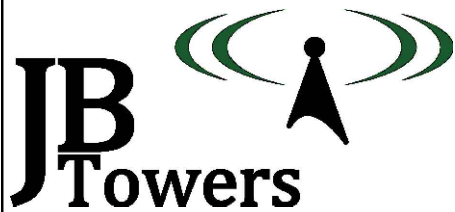

01	FIRST ISSUE				AM	15/05/20
REV	REV				BY	DATE
SCALE AS SHOWN		DRAWN	AM	CHECKED	MP	APPROVED JBT
WHEN PRINTED AT A3		DATE	15/05/20	DATE	15/05/20	DATE 15/05/20
ALL DIMENSIONS IN mm UNLESS OTHERWISE STATED. THIS DRAWING TO BE READ IN CONJUNCTION WITH OTHER RELEVANT DRAWINGS.						


TITLE
CEMAES
Rx ANTENNA MOUNT
DETAIL H

SITE ADDRESS
CARROG FARM
LLANBADRIG
ISLE OF ANGLESEY
LL67 0LB


ARQIVA REF.
140365

DRG No.
204

REV
01

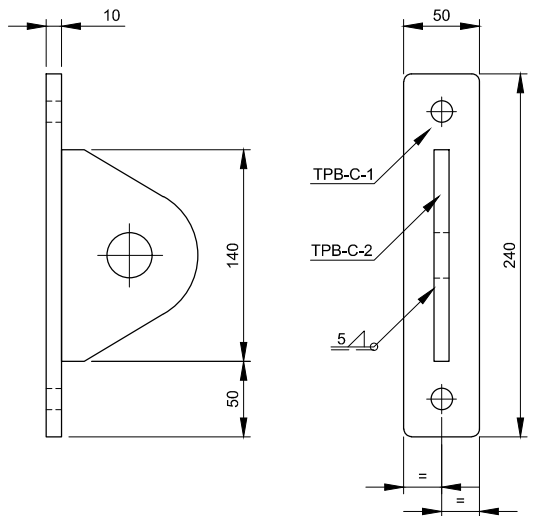

PART TPB-C
Scale 1:5

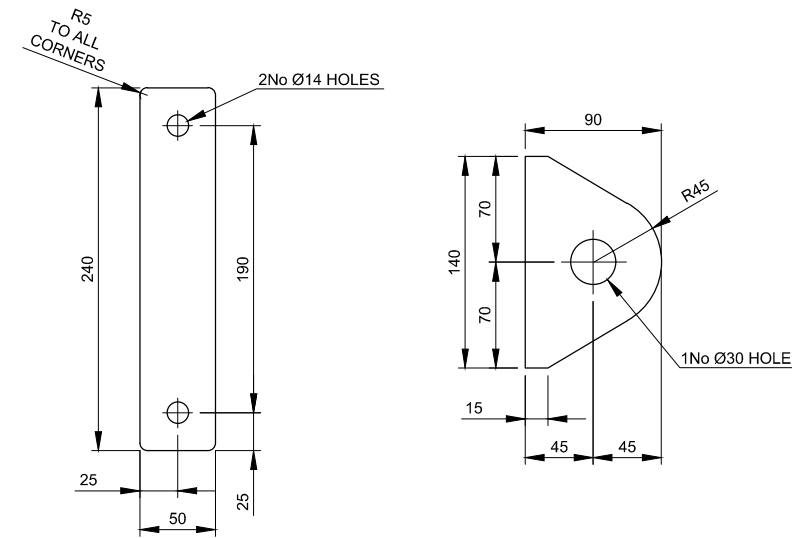


TPB-C-1 - 10mm THICK
Scale 1:5

TPB-C-2 - 10mm THICK
Scale 1:5


Parts list for TPB-C

Item	Part	Quantity	Part description	Length	Material	Weight
01	TPB-C-1	1	Plate 240x50x10mm	N/A	S275J0	0.94 kg
02	TPB-C-2	1	Plate 140x90x10mm	N/A	S275J0	0.99 kg
03	STUDS	1	M12 STUDDING	350mm	GRADE 8.8	0.31 kg
Total Weight:						2.24 kg

- All steel hot dip galvanized
- Each STUD to be supplied with 4 Full Nuts, 2 Flat Washers and 2 Spring Washers
- For fabrication notes see drawing 303

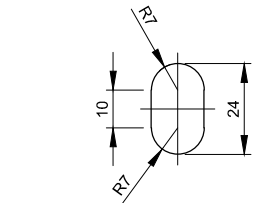

SLOTTED HOLE DETAIL
Scale 1:2

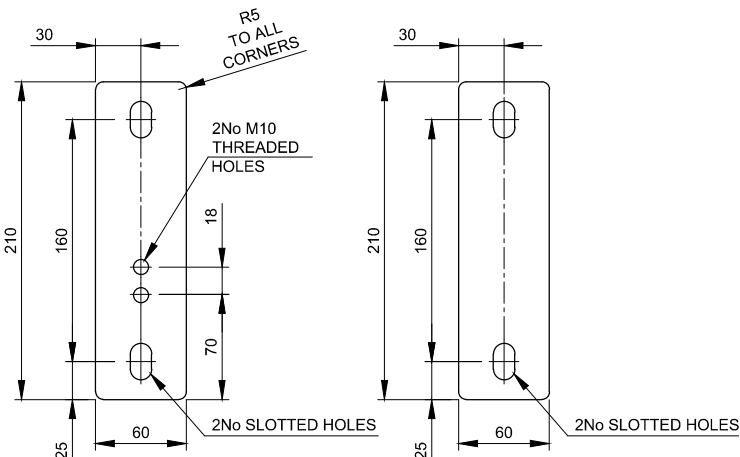


PART TPS-R-1
Scale 1:5

PART TPS-R-2
Scale 1:5

Parts list for TPS-R

Item	Part	Quantity	Part description	Length	Material	Weight
01	TPS-R-1	1	Plate 210x60x15mm	N/A	S275J0	1.48 kg
02	TPS-R-2	1	Plate 210x60x5mm	N/A	S275J0	0.49 kg
03	STUDS	2	M12 STUDDING	500mm	GRADE 8.8	0.44 kg
04	NUT-S	2	M12 SHALLOW NUT	N/A	GRADE 8.8	-
05	NUT	4	M12 NUT	N/A	GRADE 8.8	-
06	WSH	4	M12 WASHER	N/A	GRADE 8.8	-
Total Weight:						2.41 kg

- All steel hot dip galvanized
- For fabrication notes see drawing 303

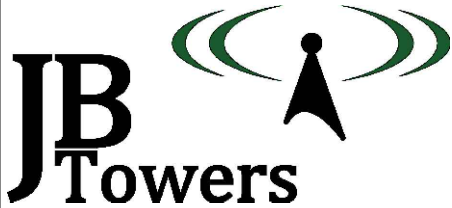

01	FIRST ISSUE	AM	15/05/20
REV	REV	BY	DATE
SCALE AS SHOWN WHEN PRINTED AT A3	DRAWN DATE 15/05/20	CHECKED DATE 15/05/20	APPROVED DATE 15/05/20
ALL DIMENSIONS IN mm UNLESS OTHERWISE STATED. THIS DRAWING TO BE READ IN CONJUNCTION WITH OTHER RELEVANT DRAWINGS.			



TITLE
CEMAES
ATTACHMENT POINT &
TEMPORARY STEP DETAILS
PARTS: TPB-C; TPS-R

SITE ADDRESS
CARROG FARM
LLANBADRIG
ISLE OF ANGLESEY
LL67 0LB
ARQIVA REF.
140365
DRG No.
300
REV
01


ALL SCALES AS SHOWN WHEN PRINTED AT A3




ALL SCALES AS SHOWN WHEN PRINTED AT A3

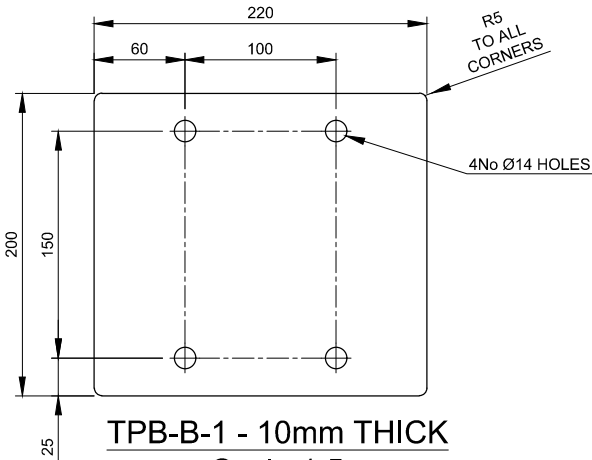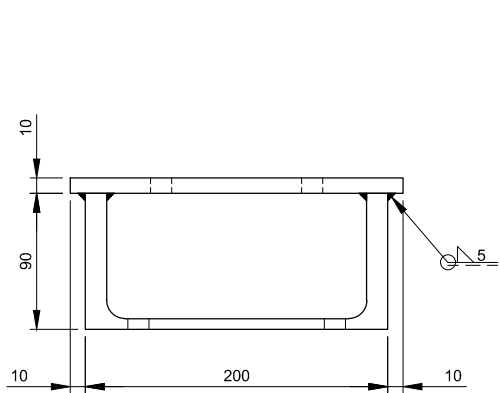


TPB-B-1 - 10mm THICK
Scale 1:5

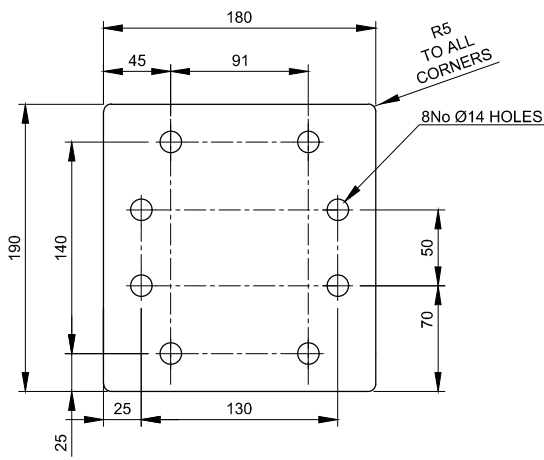


TPB-B-5 - 10mm THICK
Scale 1:5

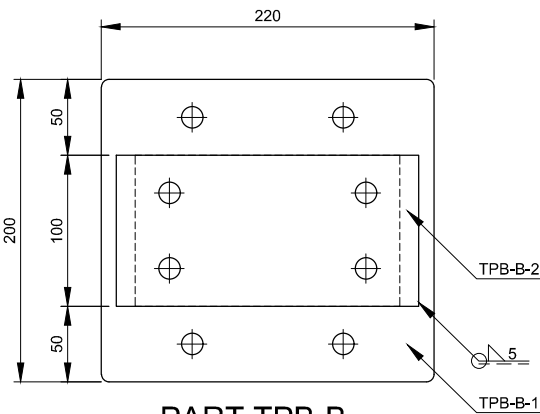


PART TPB-B
Scale 1:5

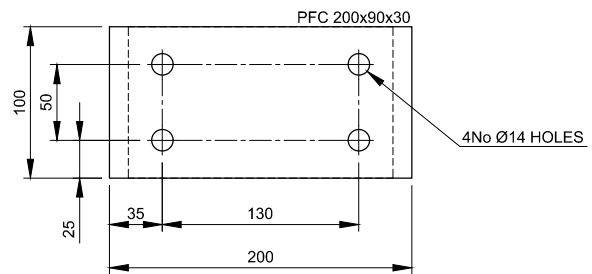

TPB-B-2 - PFC 200x90x30
Scale 1:5

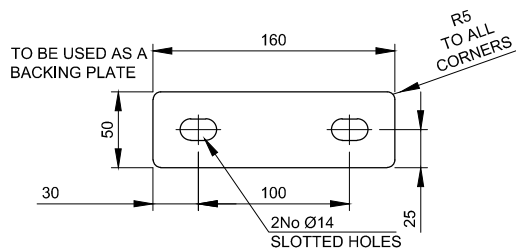

TPB-B-4 - 5mm THICK
Scale 1:5

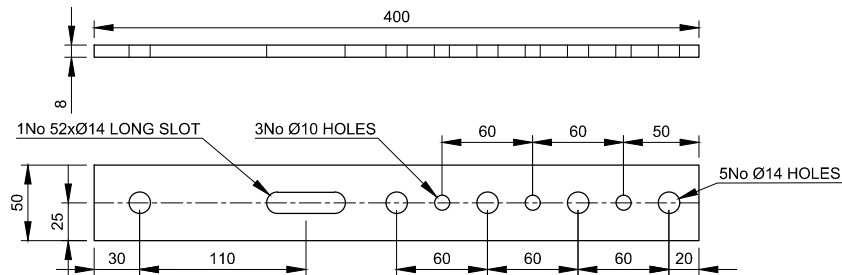


TPA-PD - 8mm THICK
Scale 1:5

Parts list for TPB-B

Item	Part	Quantity	Part description	Length	Material	Weight
01	TPB-B-1	1	Plate 220x200x10mm	N/A	S275J0	3.45 kg
02	TPB-B-2	1	PFC 200x90x30	100mm	S275J0	3.00 kg
03	TPB-B-4	2	Plate 160x50x5mm	N/A	S275J0	0.31 kg
04	TPB-B-5	1	Plate 190x180x10mm	N/A	S275J0	2.70 kg
05	STUDS	4	M12 STUDDING	450mm	GRADE 8.8	0.39 kg
06	BOLT	4	M12 45mm LONG (2D+6)	45mm	GRADE 8.8	-
07	U-BOLT	2	M12 U-BOLT FOR CHS 76.1	N/A	GRADE 8.8	-

- All steel hot dip galvanized
- Each STUD & U-BOLT to be supplied with 4 Full Nuts, 2 Flat Washers and 2 Spring Washers
- Each BOLT to be supplied with 1 Full Nut, 1 Form E FLat Washer and 1 Spring Washer
- For fabrication notes see drawing 303

Total Weight: 11.33 kg

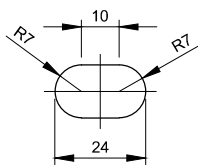


SLOTTED HOLE DETAIL
Scale 1:2

Parts list for TPA-PD

Item	Part	Quantity	Part description	Length	Material	Weight
01	TPA-PD	1	400x50x8mm	N/A	S275J0	1.26 kg
02	U-BOLT	1	M12 U-BOLT FOR CHS 76.1mm	N/A	GRADE 8.8	-

Total Weight: 1.26 kg

- All steel hot dip galvanized
- Each U-BOLT to be supplied with 4 Full Nuts, 2 Flat Washers and 2 Spring Washers
- For fabrication notes see drawing 303

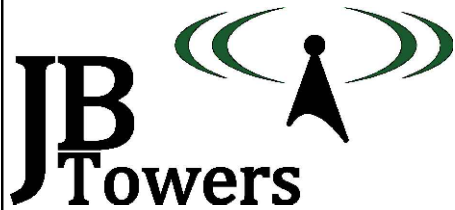

01	FIRST ISSUE	AM	15/05/20
REV	REV	BY	DATE
SCALE AS SHOWN WHEN PRINTED AT A3	DRAWN DATE	AM 15/05/20	CHECKED DATE
MP 15/05/20	APPROVED DATE	JBT 15/05/20	
ALL DIMENSIONS IN mm UNLESS OTHERWISE STATED. THIS DRAWING TO BE READ IN CONJUNCTION WITH OTHER RELEVANT DRAWINGS.			

TITLE

CEMAES

STEELWORK BRACKET,
POWER DIVIDER STRAP

PARTS: TPB-B, TPA-PD

SITE ADDRESS

CARROG FARM
LLANBADRIG
ISLE OF ANGLESEY
LL67 0LB

ARQIVA REF.
140365


DRG No.
301

REV
01


ALL SCALES AS SHOWN WHEN PRINTED AT A3



ALL SCALES AS SHOWN WHEN PRINTED AT A3

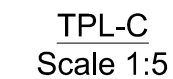


- All steel hot dip galvanized
- Each U-BOLT to be supplied with 4 Full Nuts, 2 Flat Washers and 2 Spring Washers
- For fabrication notes see drawing 303

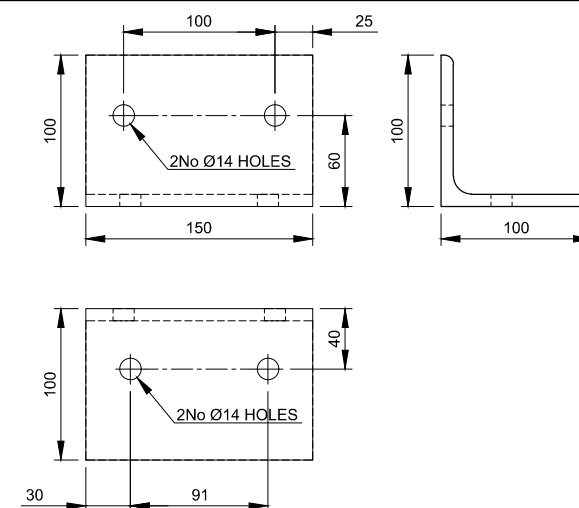


TPL-D - EA100x100x8
Scale 1:5

Item	Part	Quantity	Part description	Length	Material	Weight
01	TPL-D	1	EA100x100x8	150mm	S275J0	1.90 kg
02	U-BOLT	1	M12 U-BOLT FOR CHS 76.1mm	N/A	GRADE 8.8	-
- All steel hot dip galvanized					Total Weight:	1.90 kg

- All steel hot dip galvanized
- Each U-BOLT to be supplied with 4 Full Nuts, 2 Flat Washers and 2 Spring Washers
- For fabrication notes see drawing 303

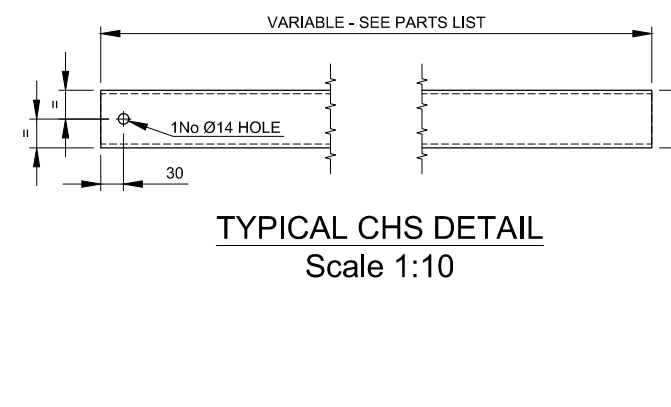

TYPICAL CHS DETAIL
Scale 1:10

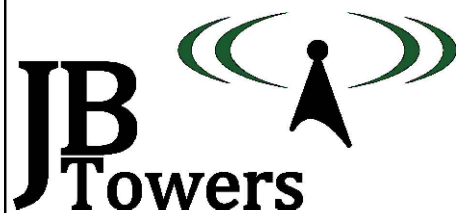

01	FIRST ISSUE		AM	15/05/20	
REV	REV		BY	DAT	
SCALE AS SHOWN WHEN PRINTED AT A3	DRAWN AM DATE 15/05/20	CHECKED MP DATE 15/05/20	APPROVED JB DATE 15/05/20		
ALL DIMENSIONS IN mm UNLESS OTHERWISE STATED. THIS DRAWING TO BE READ IN CONJUNCTION WITH OTHER RELEVANT DRAWINGS.					

CEMAES

LOG MOUNTS & TYPICAL CHS DETAIL


PARTS: TPL-C; TPL-D

CARROG FARM
LLANBADRIG
ISLE OF ANGLESEY
LL67 0LB

ARQIVA REF.
140365

DRG No.
302REV
01

ALL SCALES AS SHOWN WHEN PRINTED AT A3

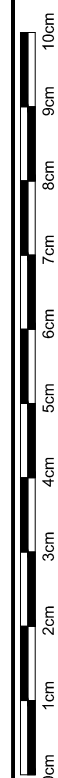


ALL SCALES AS SHOWN WHEN PRINTED AT A3

Item	Part	Drawing	Quantity	Part description	Length	Material	Weight
01	01	200	1	3 MAN LATCHWAY SYSTEM & *5No. WIRE GUIDES FOR FACE MOUNTED MONOPOLE (SEE NOTES)	17000	N/A	-
02	TPB-C	300	2	FALL ARREST ATTACHMENT POINT	N/A	S275J0	4.50 kg
03	03	200	46	PERMANENT BT STEP c/w 3No 10x75mm ZINC-PLATED COACH SCREWS	N/A	S275J0	13.80 kg
04	TPS-R	300	9	'MonoStep' ASSEMBLY	N/A	S275J0	21.70 kg
05	TPB-B	301	3	MOUNTING BRACKET	N/A	S275J0	34.00 kg
06	06	203	12	M12 WASHER	N/A	GRADE 8.8	-
07	07	203	1	CHS 76.1x5mm	3000mm	S355J2H	26.50 kg
08	TPL-D	302	8	LOG MOUNTING BRACKET	150mm	S275J0	15.20 kg
09	TPA-PD	301	6	POWER DIVIDER STRAP	N/A	S275J0	7.60 kg
10	10	204	1	CHS 76.1x5mm	1000mm	S355J2H	8.80 kg
11	TPL-C	302	1	LOG MOUNTING BRACKET	150mm	S275J0	3.25 kg
12	12	200	7	M12 STUD + 4No NUTS + 2No FLAT WASHERS + 1No Ø50mm WASHER (FOR FALL ARREST SYSTEM)	500mm	GRADE 8.8	3.20 kg
13	13	200	1	FEEDER COVER - 2/CG/100	3500mm	UV RESISTANT PLASTIC	-
14	14	200	17	FEEDER CLAMP - 2/FCD/028	N/A	POLYPROPYLENE	-
15	15	200	17	M10 SCREW DOWELS WTH M10 NUT	100mm	STAINLESS STEEL	-
Total Weight:							138.55 kg

- All steel hot dip galvanized
- All U-BOLTS to be FLA supply, each Supplied with 4 Full Nuts, 2 Flat Washers and 2 Spring Washers

NOTES:

1. WELDING TO BE IN ACCORDANCE WITH BS EN 1011-1:2009
2. LINEAR DIMS TO BE WITHIN ±1mm;
3. ANGULAR TOLERANCES TO BE WITHIN 0.5°
4. WELDING SYMBOLS ARE IN ACCORDANCE WITH BS EN 22553:1995
5. ALL PROFILE EDGES TO BE DRESSED AND SHARP CORNERS REMOVED
6. ALL WELD SIZES ARE FINAL SIZES
7. ALL WELDED JOINTS ARE TO BE PICKLE TIGHT
8. ALL STEELWORK TO BE BS EN 10025 GRADE S275 J0 UNO, HOT DIPPED GALVANISED TO BS EN ISO 1461. (ALL HOLLOW SECTIONS TO BE GRADE S355 J0H)
9. ALL STEEL IS TO BE SUPPLIED IN ACCORDANCE WITH EN 1090 TO EXECUTION CLASS 2
10. ALL NON PRE-LOADED BOLTS TO BE COMPLIANT STRUCTURAL BOLTS TO BS EN ISO 15048 PARTS 1&2.
11. STEELWORK COMPONENTS SHALL BE HOT DIP GALVANISED TO ACHIEVE A "VERY HIGH" DURABILITY FOR AN ENVIRONMENT CATEGORY CODE C4 FROM TABLE 1 IN BS EN ISO 14713
12. BOLTS AND NUTS SHALL BE SUPPLIED IN ACCORDANCE WITH BS 7371, SPUN GALVANISED IN ACCORDANCE WITH ISO 10684, THE NUTS RE-TAPPED AFTER GALVANISING, AND THE THREADS TREATED WITH GREASE.
13. ALL BOLTS TO BE CUT ON SITE TO EXTEND MAX 10mm BEYOND THE NUT WHEN TIGHTENED UNO.
14. ALL SITE DRILLED HOLE/CUT ENDS TO BE TREATED WITH METAFLUX 70-40 ZINC PASTE FOLLOWED BY 1 COAT OF 7-42 ZINC ALU OR 70-16 ALUMINIUM SPRAY

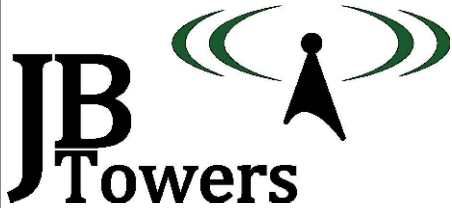

01	FIRST ISSUE			AM	15/05/20
REV	REV			BY	DATE
SCALE AS SHOWN		DRAWN	AM	CHECKED	MP
WHEN PRINTED AT A3		DATE	15/05/20	DATE	15/05/20
APPROVED		JBT			
DATE		15/05/20			
ALL DIMENSIONS IN mm UNLESS OTHERWISE STATED. THIS DRAWING TO BE READ IN CONJUNCTION WITH OTHER RELEVANT DRAWINGS.					

TITLE
CEMAES
PARTS LIST

SITE ADDRESS
CARROG FARM
LLANBADRIG
ISLE OF ANGLESEY
LL67 0LB

ARQIVA REF.
140365


DRG No.
303

REV
01


ALL SCALES AS SHOWN WHEN PRINTED AT A3



ALL SCALES AS SHOWN WHEN PRINTED AT A3

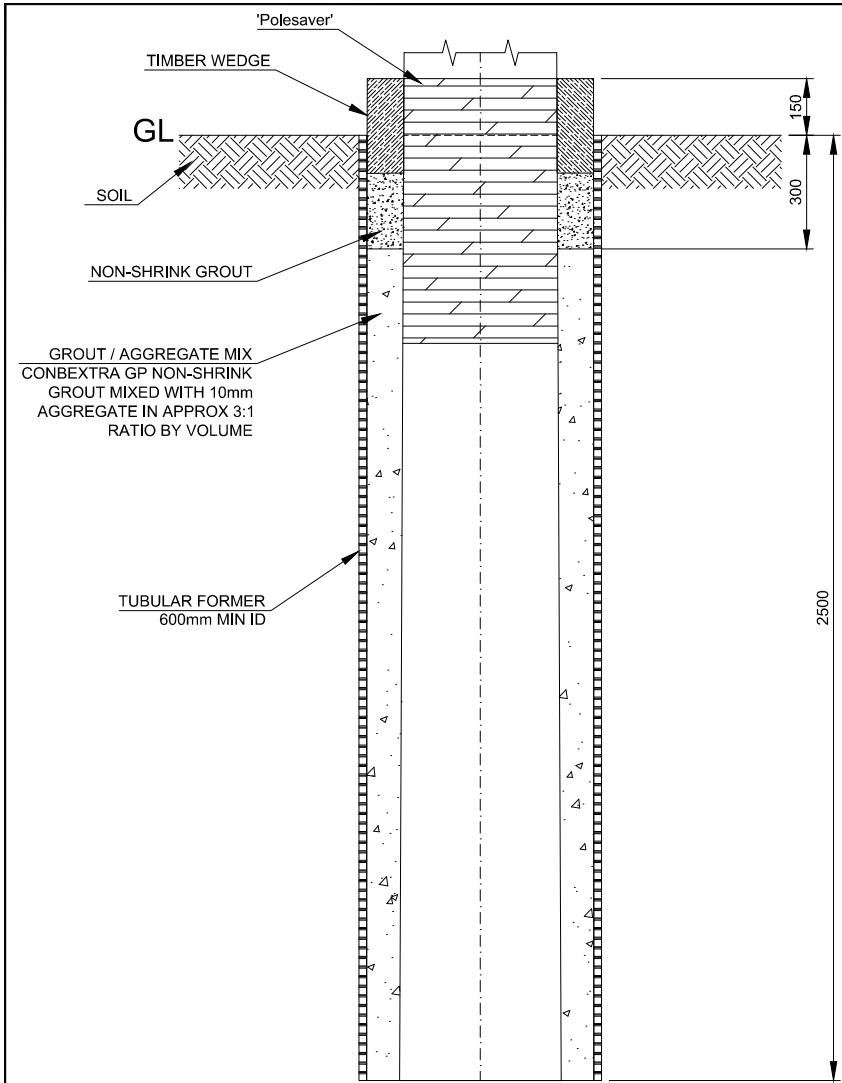


**POROPOSED INSTALLATION
ELEVATION**
Scale 1:20

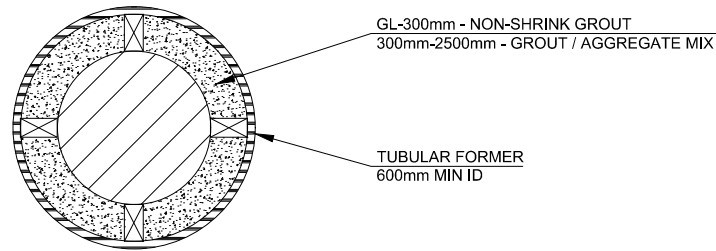


**POROPOSED INSTALLATION
PLAN VIEW**
Scale 1:20

TIMBER POLE INSTALLATION:


1. REFER TO DRAWING 200 FOR TIMBER POLE ORIENTATION
2. HOLE TO BE AUGURED TO REQUIRED DEPTH
3. IF REQUIRED A TUBULAR FORMER IS TO BE INSERTED AND THE ANNULUS BETWEEN THE FORMER AND THE SOIL GROUTED UP
4. POLE TO BE WRAPPED IN 'POLESAVER' AND INSTALLED AND LEVELLED IN OPENING. TIMBERS TO BE USED TO HOLD POLE IN POSITION
5. ANNULUS SHALL BE FILLED WITH GROUT / AGGREGATE MIX TO 300mm BELOW GL
6. TOP 300mm SHALL BE FILLED WITH NON-SHRINK GROUT. A 1:60 FALL SHALL BE FORMED AROUND TIMBER POLE TO ALLOW WATER TO DRAIN AWAY FROM POLE
7. ONCE GROUT HAS CURED REMOVE TIMBER WEDGES AND FILL REMAINING VOIDS WITH NON-SHRINK GROUT

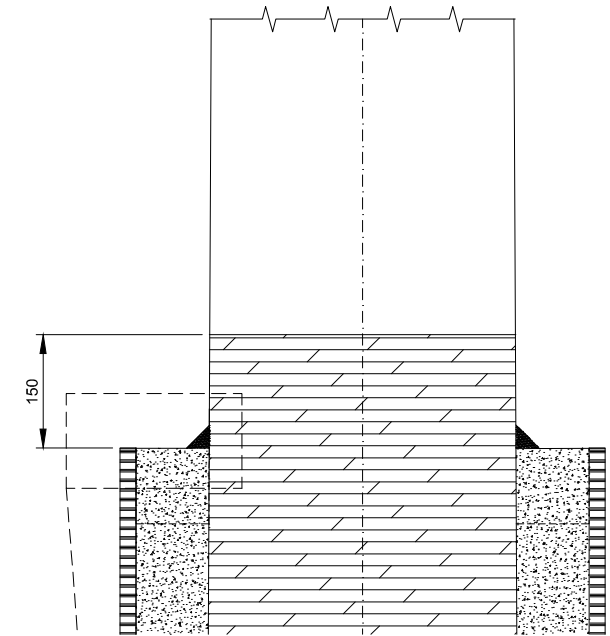

WATER PROOFING
Scale 1:10

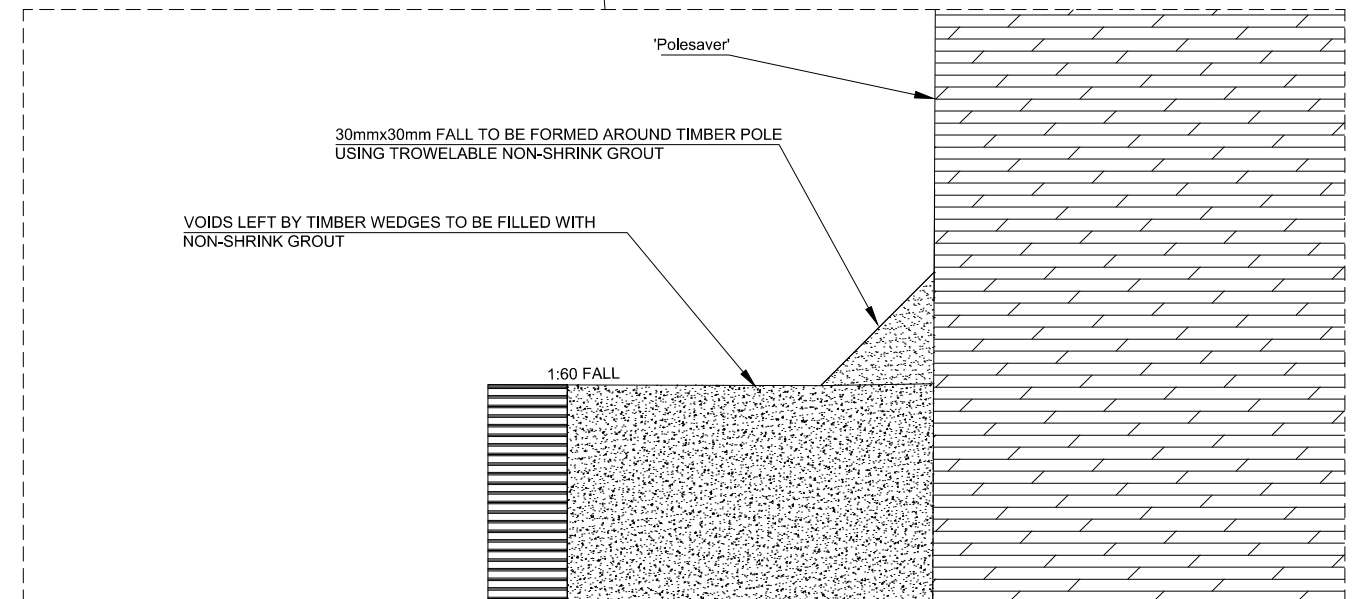

ENLARGED DETAIL
Scale 1:2

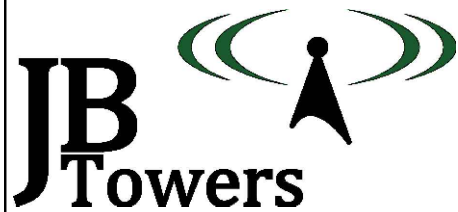

01	FIRST ISSUE	AM	15/05/20
REV	REV	BY	DATE
SCALE AS SHOWN WHEN PRINTED AT A3	DRAWN DATE 15/05/20	CHECKED DATE 15/05/20	APPROVED DATE 15/05/20
ALL DIMENSIONS IN mm UNLESS OTHERWISE STATED. THIS DRAWING TO BE READ IN CONJUNCTION WITH OTHER RELEVANT DRAWINGS.			

TITLE		SITE ADDRESS	
CEMAES		CARROG FARM	
TIMBER POLE FOUNDATION DETAILS		LLANBADRIG	
		ISLE OF ANGLESEY	
		LL67 0LB	
ARQIVA REF. 140365		DRG No. 400	REV 01