
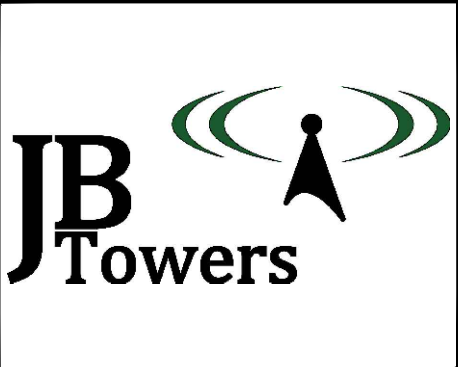
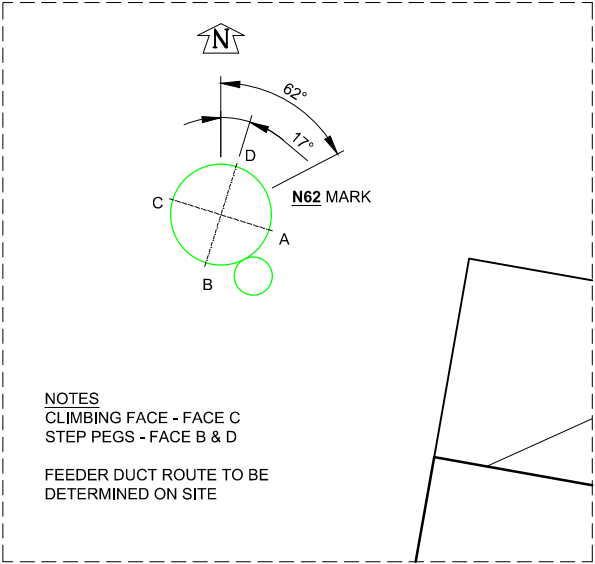


DRAWING ISSUE SHEET

[illegible]

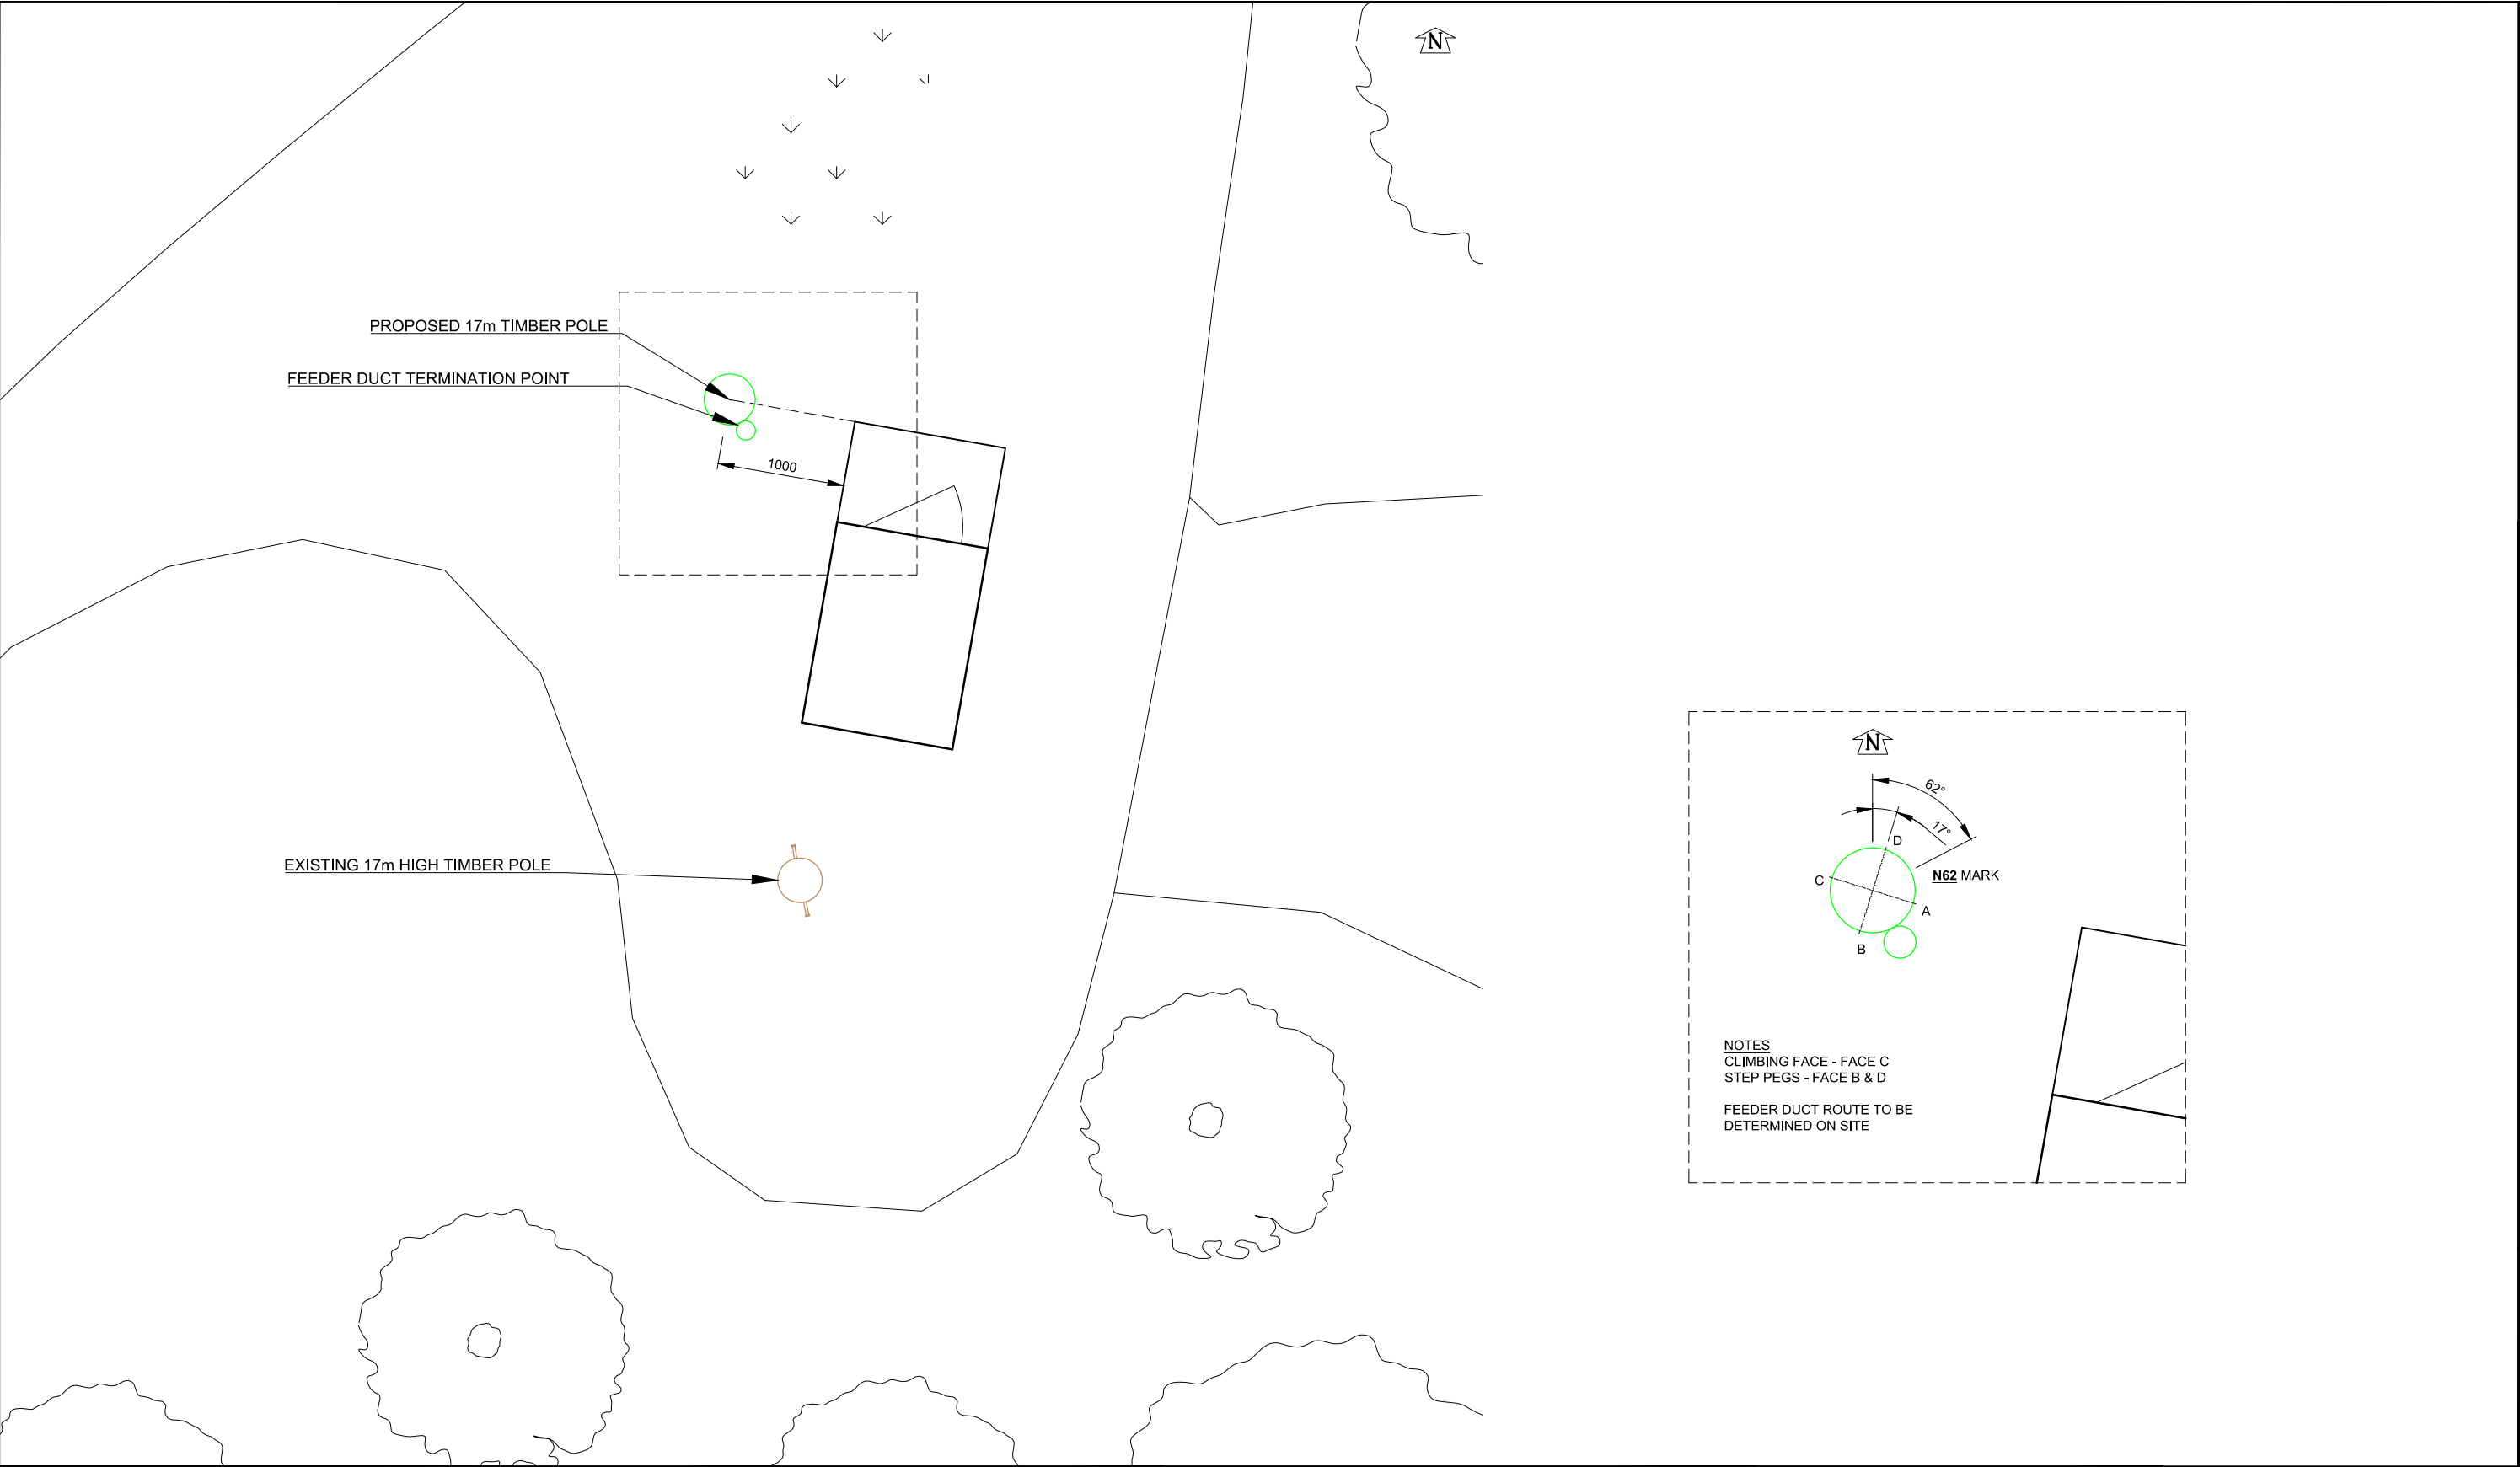


02	REVISED POSITION OF PROPOSED TIMBER POLE			AM	16/11/20
01	FIRST ISSUE			AM	29/05/20
REV	REV			BY	DATE
SCALE AS SHOWN		DRAWN	AM	CHECKED	MP
WHEN PRINTED AT A3		DATE	29/05/20	DATE	29/05/20
		APPROVED	JBT	DATE	29/05/20
ALL DIMENSIONS IN mm UNLESS OTHERWISE STATED. THIS DRAWING TO BE READ IN CONJUNCTION WITH OTHER RELEVANT DRAWINGS.					

TITLE
COED DERW
SITE PLAN

SITE ADDRESS COED DERW MILL STREET BETWS-Y-COED ABERCONWY AND COLWYN LL24 0BB		
ARQIVA REF. 140456	DRG No. 100	REV 02



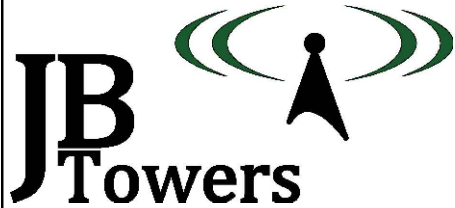

01	FIRST ISSUE			AM	29/05/20
REV	REV			BY	DATE
SCALE AS SHOWN		DRAWN	AM	CHECKED	MP
WHEN PRINTED AT A3		DATE	29/05/20	DATE	29/05/20
		APPROVED	JBT	DATE	29/05/20

ALL DIMENSIONS IN mm UNLESS OTHERWISE STATED.
THIS DRAWING TO BE READ IN CONJUNCTION WITH
OTHER RELEVANT DRAWINGS.



TITLE
COED DERW
GENERAL ARRANGEMENT
SHEET 1 OF 3

SITE ADDRESS
COED DERW
MILL STREET
BETWS-Y-COED
ABERCONWY AND
COLWYN
LL24 0BB

ARQIVA REF.
140456

DRG No.
200

REV
01

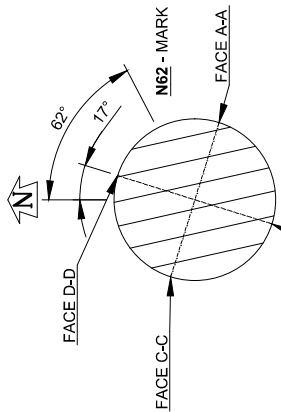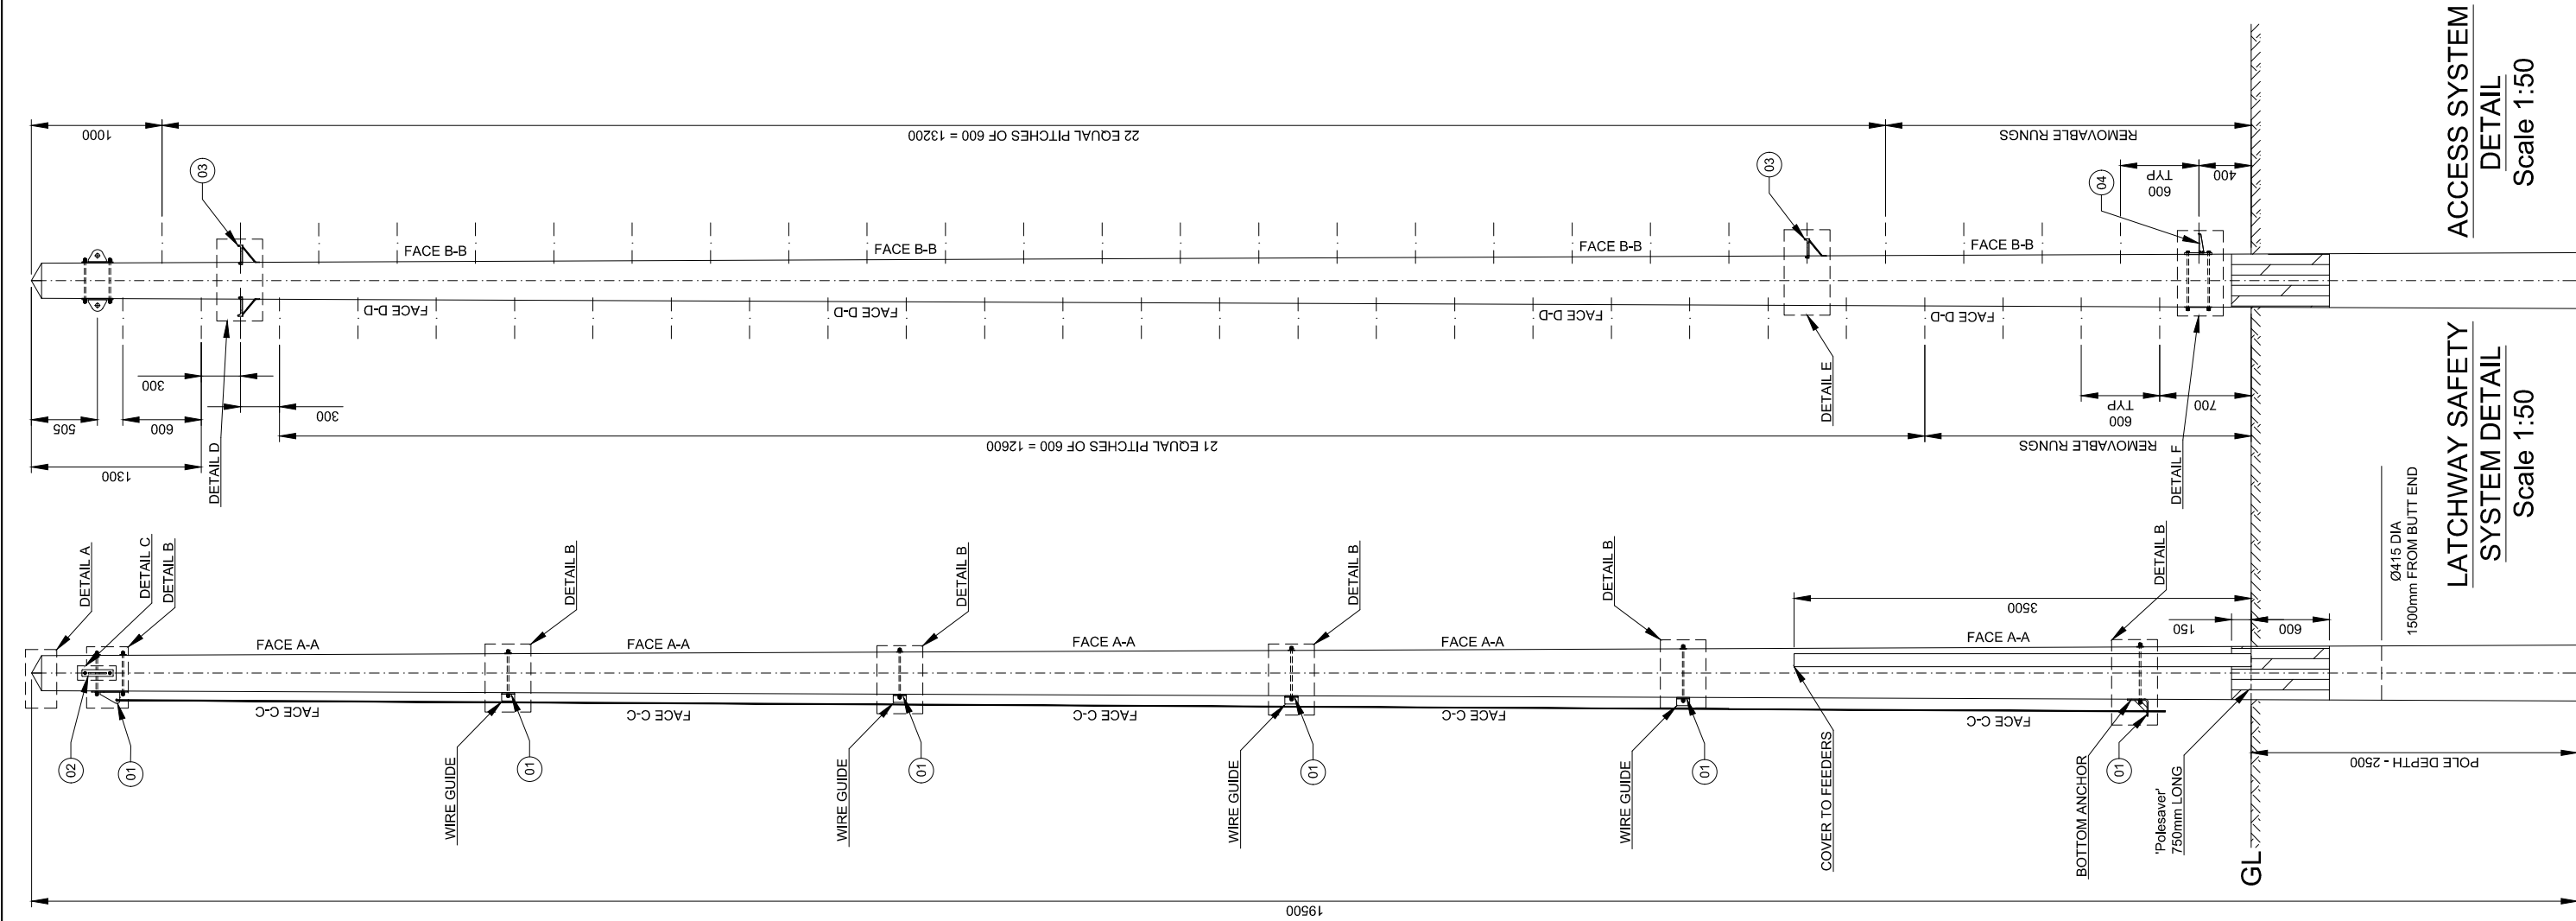

POLE ORIENTATION
Scale 1:20

NOTES

1. SEE DRAWING 305 FOR PARTS LIST
2. ALL BOLTS TO BE CUT ON SITE TO EXTEND MAX 10mm BEYOND THE NUT WHEN TIGHTENED UNO.
3. ALL SITE DRILLED HOLE/CUT ENDS TO BE TREATED WITH METALUX 70-40 ZINC PASTE FOLLOWED BY 1 COAT OF 7-42 ZINC ALU OR 70-16 ALUMINIUM SPRAY

TIMBER POLE

1. POLE TO BE SUPPLIED IN ACCORDANCE WITH BS EN14229 & SHALL HAVE MIN. CHARACTERISTIC BENDING STRENGTH OF 30N/mm2 & MIN. YOUNGS MODULUS (PARALLEL TO GRAIN) OF 10kN/mm2.
2. MARKINGS ON FINISHED POLE SHALL BE AT 4m FROM BUTT AND COMPLY WITH BS EN 14229 UNO
3. AS FAR AS PRACTICABLE ALL CUTTING, SCARFING & DRILLING TO BE DONE BEFORE CREOSOTING. IF NOT ALL CUT, DRILLED & SCARFED SURFACES TO BE COATED WITH A MIXTURE OF CREOSOTE & TAR.
4. POLE TO BE PRESSURE IMPREGNATED WITH CREOSOTE IN ACCORDANCE WITH BS EN 14229
5. MINIMUM DIAMETERS
TOP - Ø205mm
BOTTOM - Ø430mm
6. 19.5m LONG POLE TO BE SOURCED BY TRIMMING 20m LONG POLE BY 0.5m AT THE TOP

PLANTING


1. CAT SCANNER IS TO BE USED IN ORDER TO CONFIRM THE POSITIONS OF BURIED SERVICES.
2. TIMBER POLE TO BE PLANTED WITH N62 MARKING AT 3.5m FROM BUT FACING 62° FROM NORTH (CLOCKWISE)
3. SEE DRAWING 400 FOR FOUNDATION DETAILS

ACCESS SYSTEM
DETAIL
Scale 1:50

LATCHWAY SAFETY
SYSTEM DETAIL
Scale 1:50

ALL SCALES AS SHOWN WHEN PRINTED AT A3

ALL SCALES AS SHOWN WHEN PRINTED AT A3

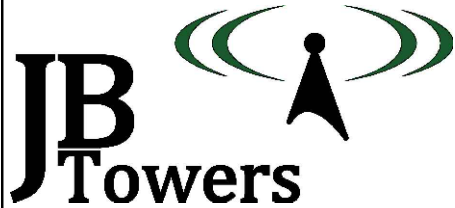

01	FIRST ISSUE			AM	29/05/20
REV	REV			BY	DATE
SCALE AS SHOWN		DRAWN	AM	CHECKED	MP
WHEN PRINTED AT A3		DATE	29/05/20	DATE	29/05/20
		APPROVED	JBT	DATE	29/05/20
ALL DIMENSIONS IN mm UNLESS OTHERWISE STATED. THIS DRAWING TO BE READ IN CONJUNCTION WITH OTHER RELEVANT DRAWINGS.					



TITLE
COED DERW
GENERAL ARRANGEMENT
SHEET 2 OF 3

SITE ADDRESS
COED DERW
MILL STREET
BETWS-Y-COED
ABERCONWY AND
COLWYN
LL24 0BB

ARQIVA REF.
140456

DRG No.
200

REV
01

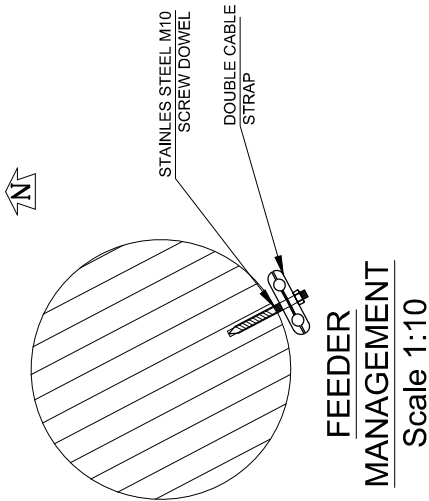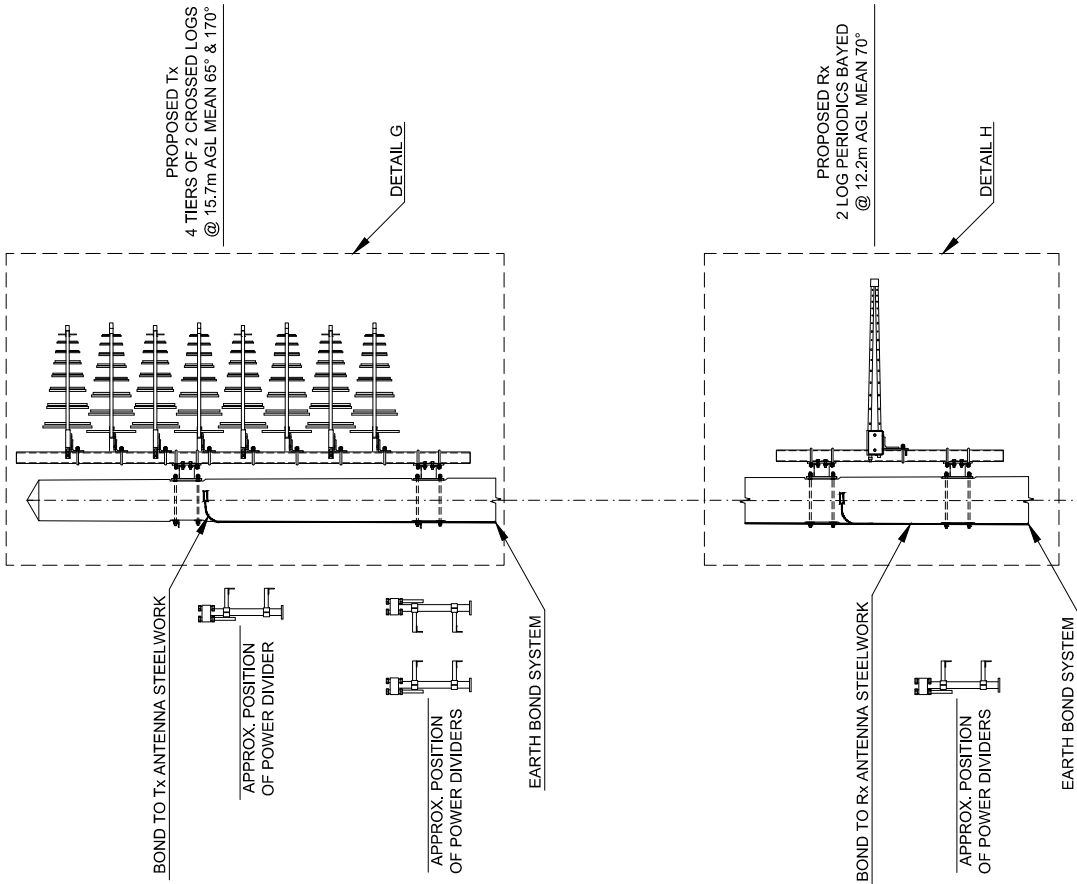

NOTES


1. AS FAR AS IS PRACTICABLE ALL CUTTING SCARFING AND DRILLING TO BE DONE BEFORE CREOSOTING. WHERE THIS IS NOT POSSIBLE ALL CUT, DRILLED, AND SCARFED SURFACES TO BE COATED WITH A MIXTURE OF CREOSOTE AND TAR

FEEDERS

1. SUPPLY OF FEEDERS BY OTHERS
LCF7/8-50 TO Tx ANTENNA &
LCF12-50 TO Rx ANTENNA
2. FEEDERS FIXED AT 1000mm CENTRES

EARTHING


1. CONNECT EARTH BOND TO NEW EARTHING SYSTEM
2. MAXIMUM VALUE FOR GROUND RESISTANCE TO BE 10 OHMS
3. CABLE OR TAPE TO BE FIXED TO POLE AT 1000mm CENTRES
4. EARTHING SHOULD COMPLY WITH ARQIVA'S DOCUMENT BOS147

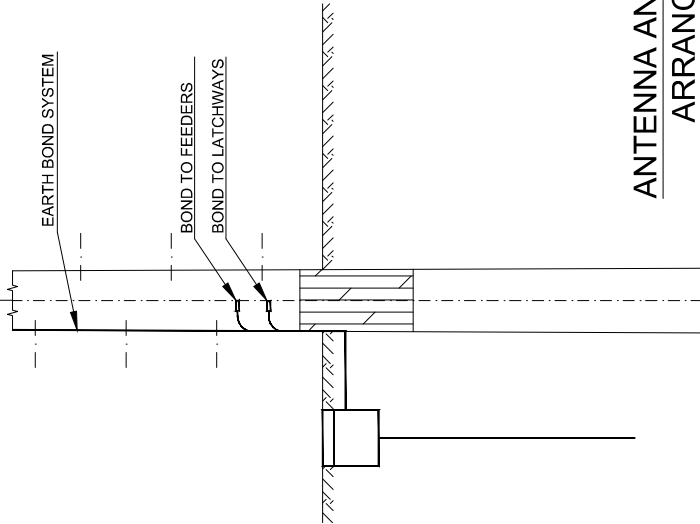

ANTENNA AND EARTHING
ARRANGEMENT
Scale 1:50




ALL SCALES AS SHOWN WHEN PRINTED AT A3

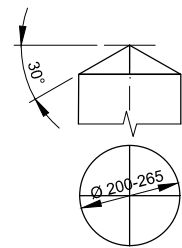


- NOTES:
1. A SINGLE COAT OF TIMBER COMPATIBLE BITUMINOUS PAINT (E.G. BIRD BRAND BLACK BITUMINOUS PAINT OR SIMILAR APPROVED PRODUCT) TO BE APPLIED TO THE UPPER SURFACES AT THE TOP OF THE POLE.
 2. PAINT TO BE APPLIED ON SITE JUST BEFORE ERECTION
- FORM: 4 WAY PYRAMID / CONE


DETAIL A - TIMBER POLE TOP
Scale 1:20

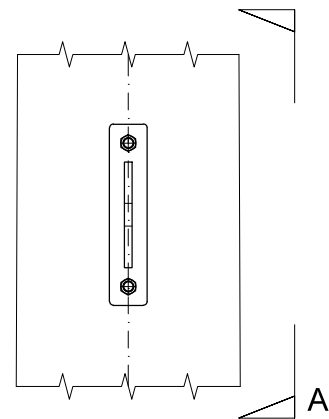


DETAIL C - FALL ARREST
ATTACHMENT POINT
Scale 1:10

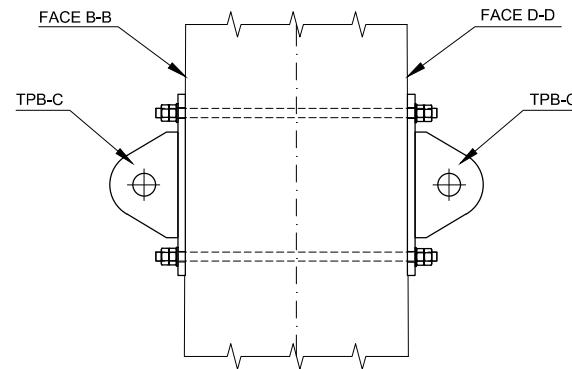


VIEW A-A
Scale 1:10

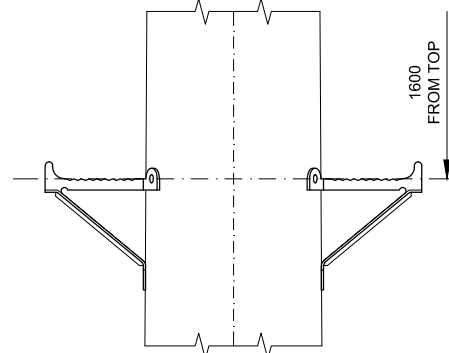


DETAIL D - ANTENNA
ACCESS CLIMBING STEP
Scale 1:10

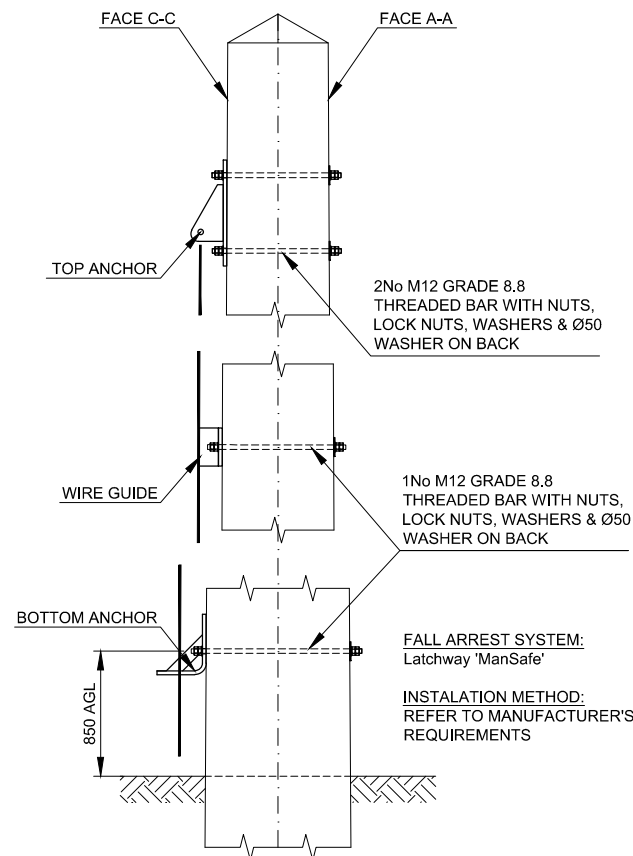


DETAIL B - FALL ARREST SYSTEM
Scale 1:20

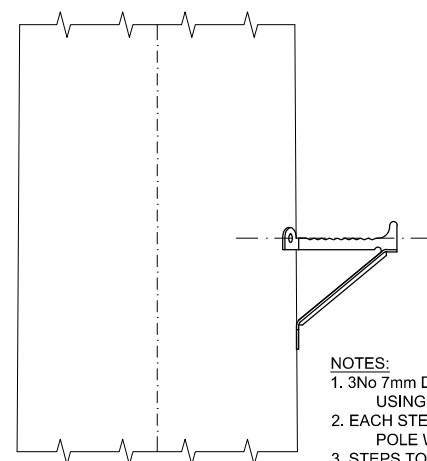

- NOTES:
1. 3No 7mm DIA 70mm LONG PILOT HOLES TO BE DRILLED USING THE STEP AS A TEMPLATE
 2. EACH STEP SHOULD BE FIXED TO THE TIMBER POLE WITH 3No 10mm COACH SCREWS 75mm LONG
 3. STEPS TO BE INSTALLED ON FACES B-B & D-D ONLY

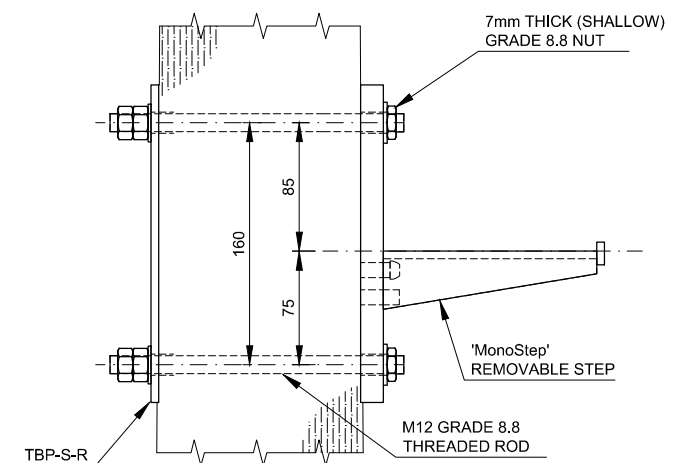

DETAIL F - REMOVABLE
CLIMBING STEPS
Scale 1:5

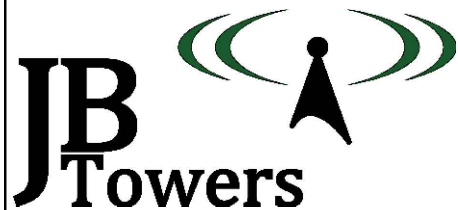

01	FIRST ISSUE			AM	29/05/20
REV	REV			BY	DATE
SCALE AS SHOWN WHEN PRINTED AT A3	DRAWN	AM	CHECKED	MP	APPROVED
	DATE	29/05/20	DATE	29/05/20	DATE
ALL DIMENSIONS IN mm UNLESS OTHERWISE STATED. THIS DRAWING TO BE READ IN CONJUNCTION WITH OTHER RELEVANT DRAWINGS.					

TITLE
COED DERW
GENERAL ARRANGEMENT
SHEET 3 OF 3

SITE ADDRESS
COED DERW
MILL STREET
BETWS-Y-COED
ABERCONWY AND
COLWYN
LL24 0BB

ARQIVA REF.
140456


DRG No.
200

REV
01

ALL SCALES AS SHOWN WHEN PRINTED AT A3



ALL SCALES AS SHOWN WHEN PRINTED AT A3

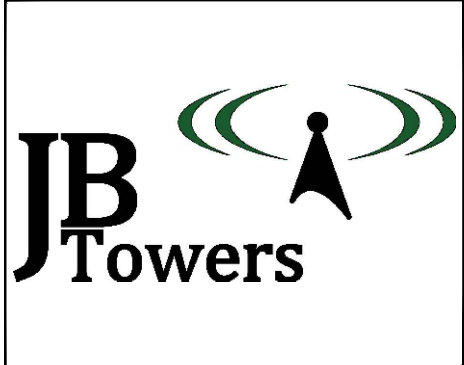

01	FIRST ISSUE							AM	29/05/20
REV	REV							BY	DATE
SCALE AS SHOWN WHEN PRINTED AT A3		DRAWN	AM	CHECKED	MP	APPROVED JBT			
		DATE	29/05/20	DATE	29/05/20	DATE 29/05/20			
ALL DIMENSIONS IN mm UNLESS OTHERWISE STATED. THIS DRAWING TO BE READ IN CONJUNCTION WITH OTHER RELEVANT DRAWINGS.									

TITLE


COED DERW

TIMBER POLE HOLE SET OUT

SHEET 1 OF 2

SITE ADDRESS COED DERW MILL STREET BETWS-Y-COED ABERCONWY AND COLWYN LL24 0BB	DRG 2
---	------------------


ARQIVA REF. 140456	DRG No. 201	REV 01
------------------------------	-----------------------	------------------

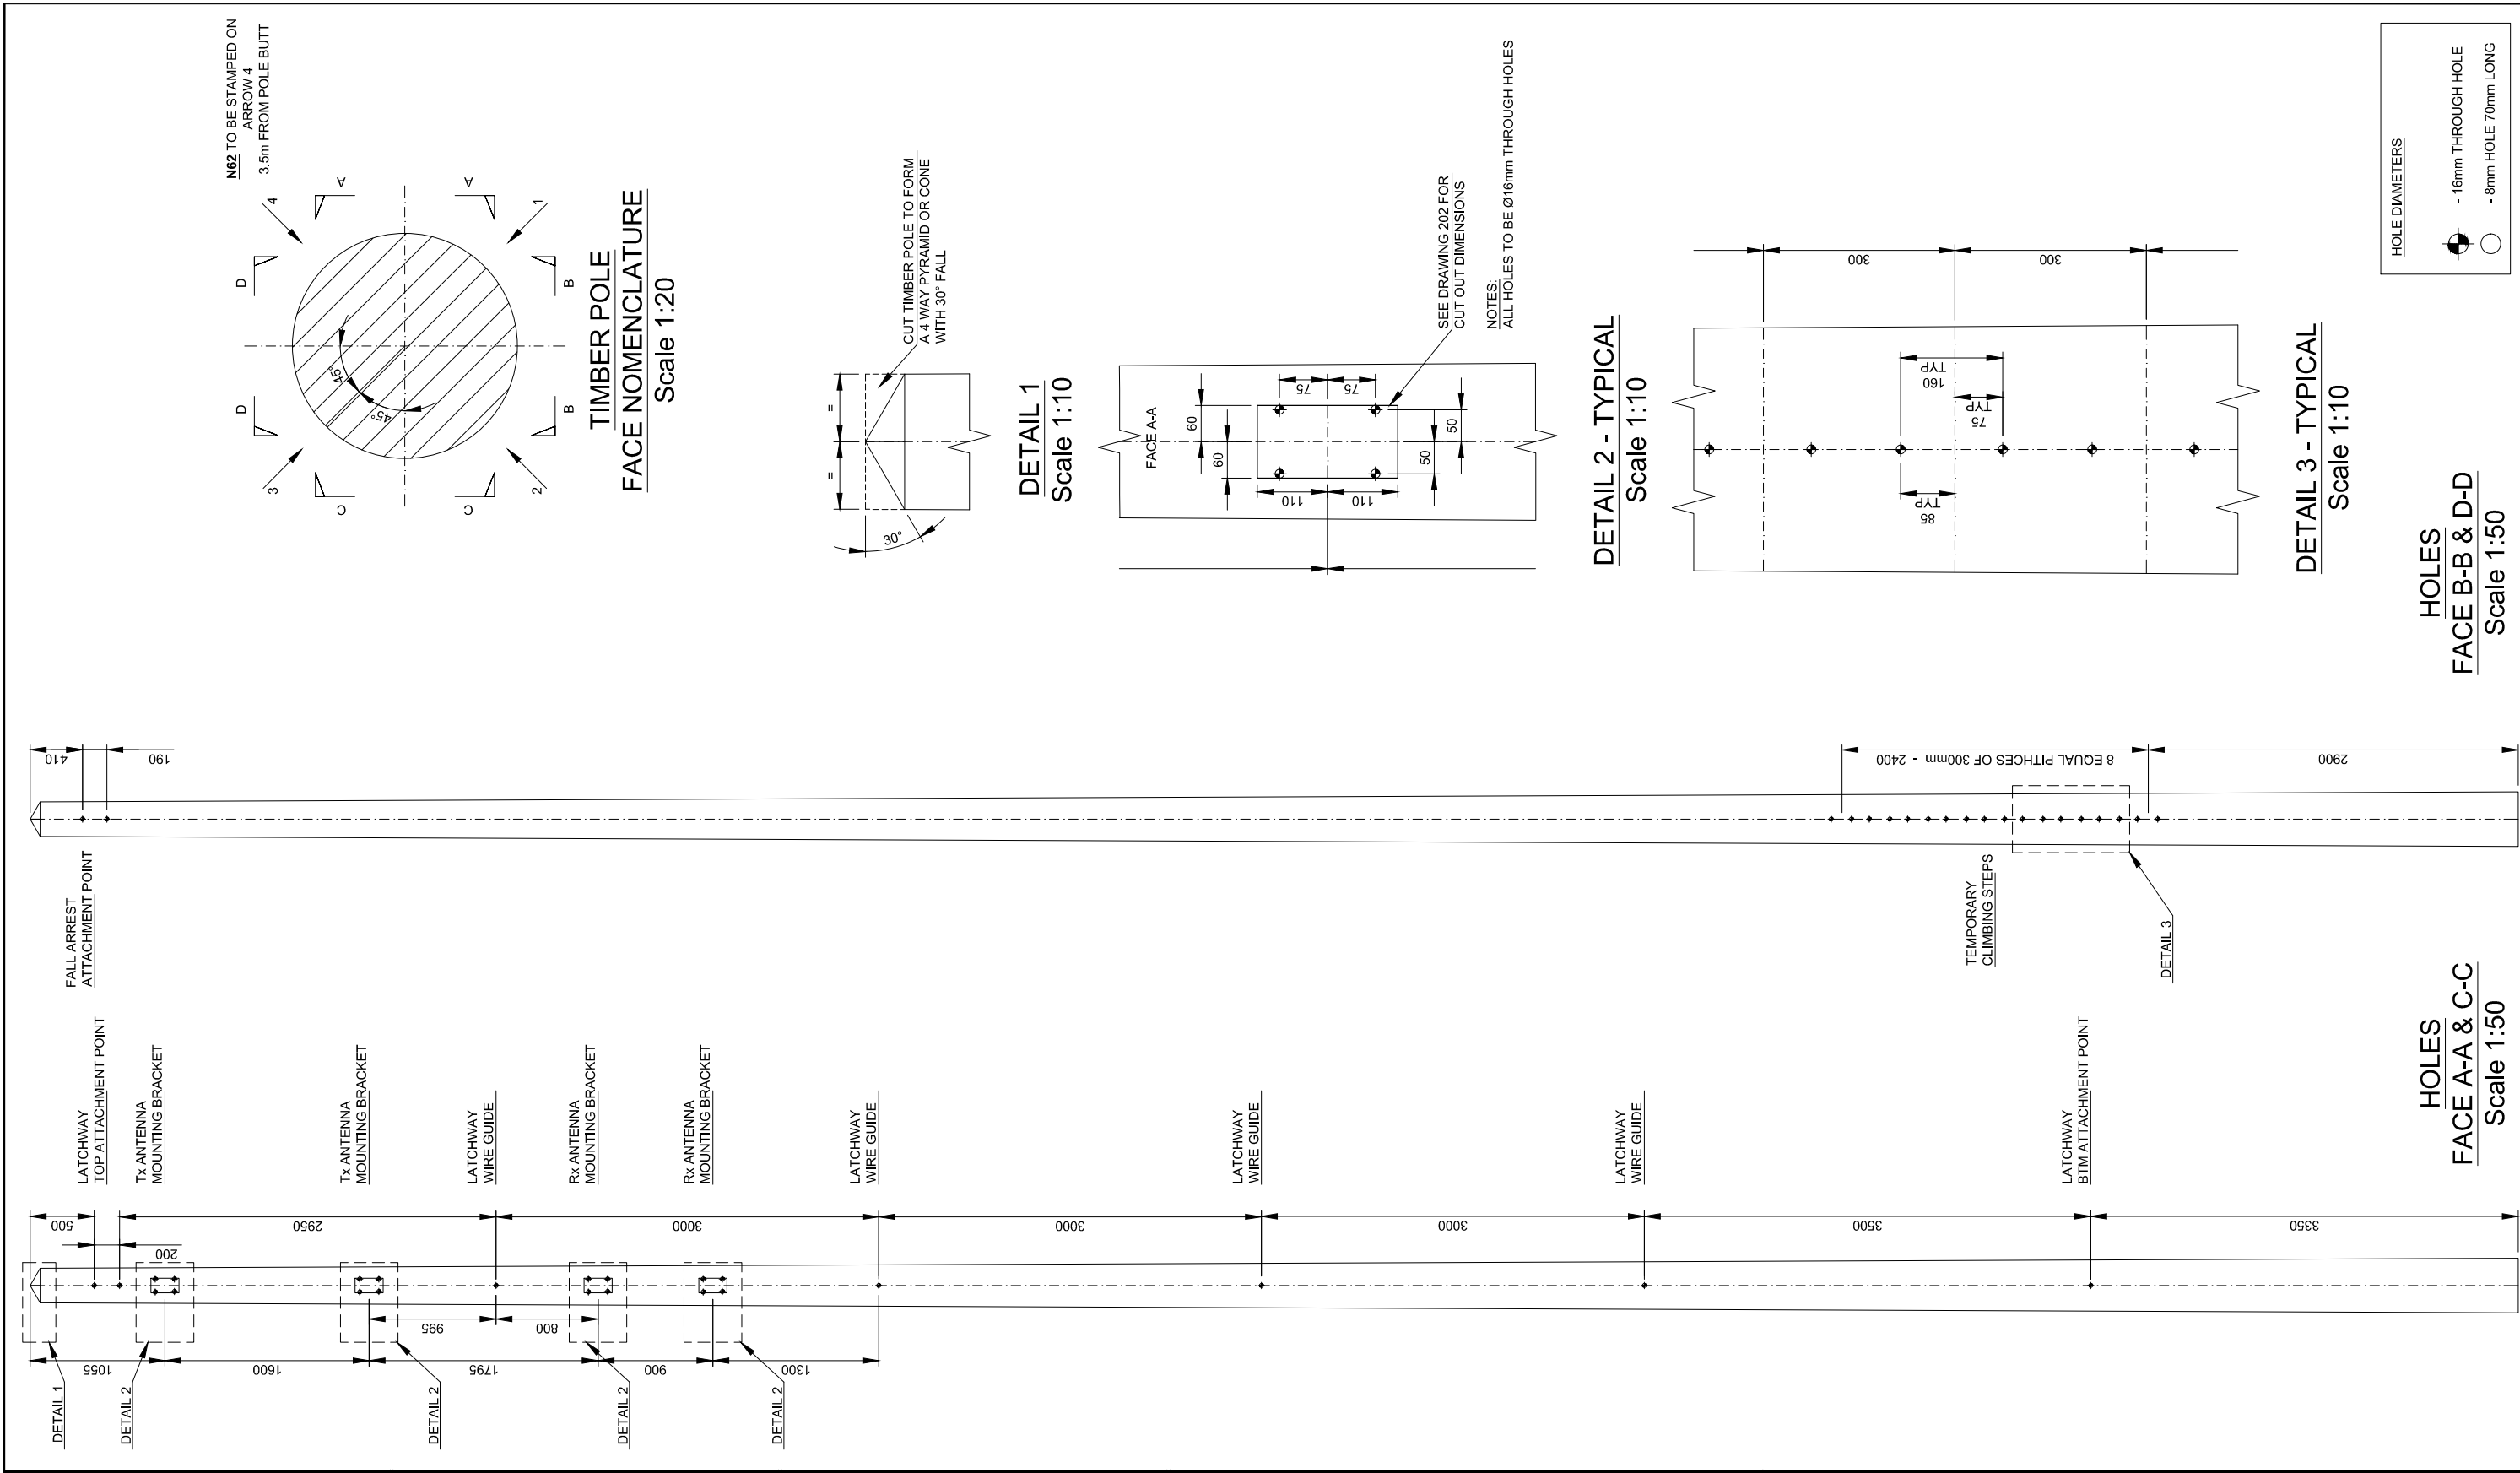

ALL SCALES AS SHOWN WHEN PRINTED AT A3

0cm	1cm	2cm	3cm	4cm	5cm	6cm	7cm	8cm	9cm	10cm
-----	-----	-----	-----	-----	-----	-----	-----	-----	-----	------

ALL SCALES AS SHOWN WHEN PRINTED AT A3

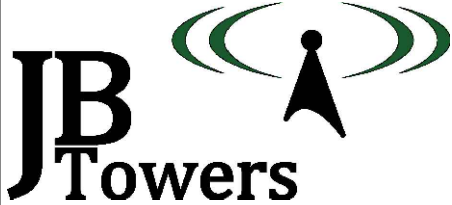

012	DIMENSION AT BUTT END UPDATED			AM	16/11/20
01	FIRST ISSUE			AM	29/05/20
REV	REV			BY	DATE
SCALE AS SHOWN		DRAWN	AM	CHECKED	MP
WHEN PRINTED AT A3		DATE	29/05/20	DATE	29/05/20
		DATE	29/05/20	DATE	29/05/20
ALL DIMENSIONS IN mm UNLESS OTHERWISE STATED. THIS DRAWING TO BE READ IN CONJUNCTION WITH OTHER RELEVANT DRAWINGS.					


TITLE
COED DERW
TIMBER POLE HOLE SET OUT
SHEET 2 OF 2

SITE ADDRESS
COED DERW
MILL STREET
BETWS-Y-COED
ABERCONWY AND
COLWYN
LL24 0BB

ARQIVA REF.
140456

DRG No.
201



REV
02

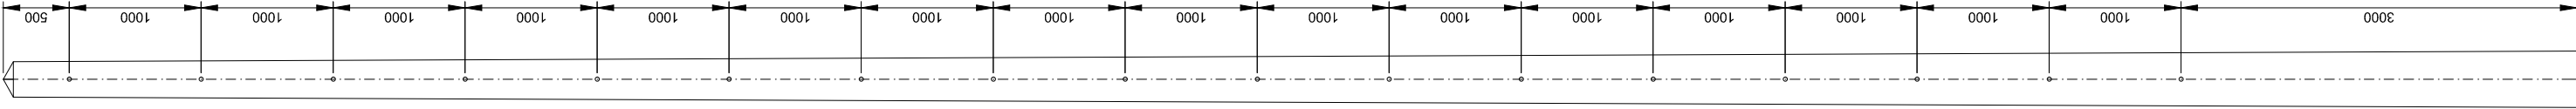

FEEDER BRACKETS

ALL HOLES ON ARROW 1
TO BE Ø8mm & 70mm LONG

HOLES
ARROW 1
Scale 1:50

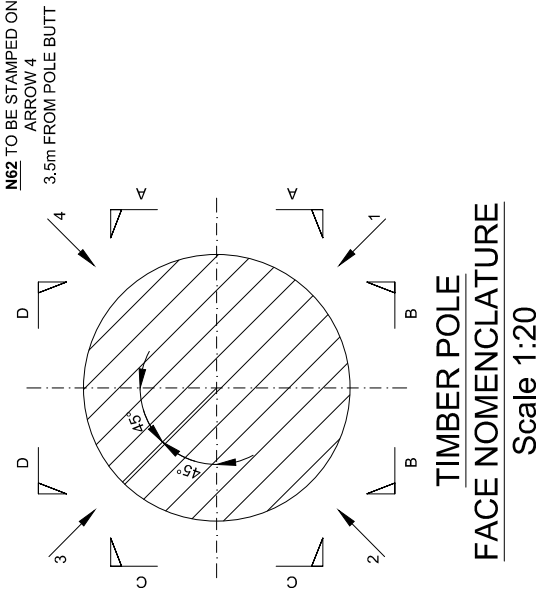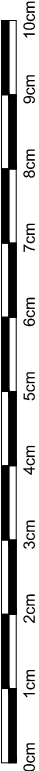

TIMBER POLE
FACE NOMENCLATURE
Scale 1:20



ALL SCALES AS SHOWN WHEN PRINTED AT A3

01	FIRST ISSUE					AM	29/05/20
REV	REV					BY	DATE
SCALE AS SHOWN		DRAWN	AM	CHECKED	MP	APPROVED	JBT
WHEN PRINTED AT A3		DATE	29/05/20	DATE	29/05/20	DATE	29/05/20
ALL DIMENSIONS IN mm UNLESS OTHERWISE STATED. THIS DRAWING TO BE READ IN CONJUNCTION WITH OTHER RELEVANT DRAWINGS.							


TITLE
COED DERW
TIMBER POLE CUT OUT
DETAIL


SITE ADDRESS
COED DERW
MILL STREET
BETWS-Y-COED
ABERCONWY AND
COLWYN
LL24 0BB

ARQIVA REF.
140456

DRG No.
202

REV
01

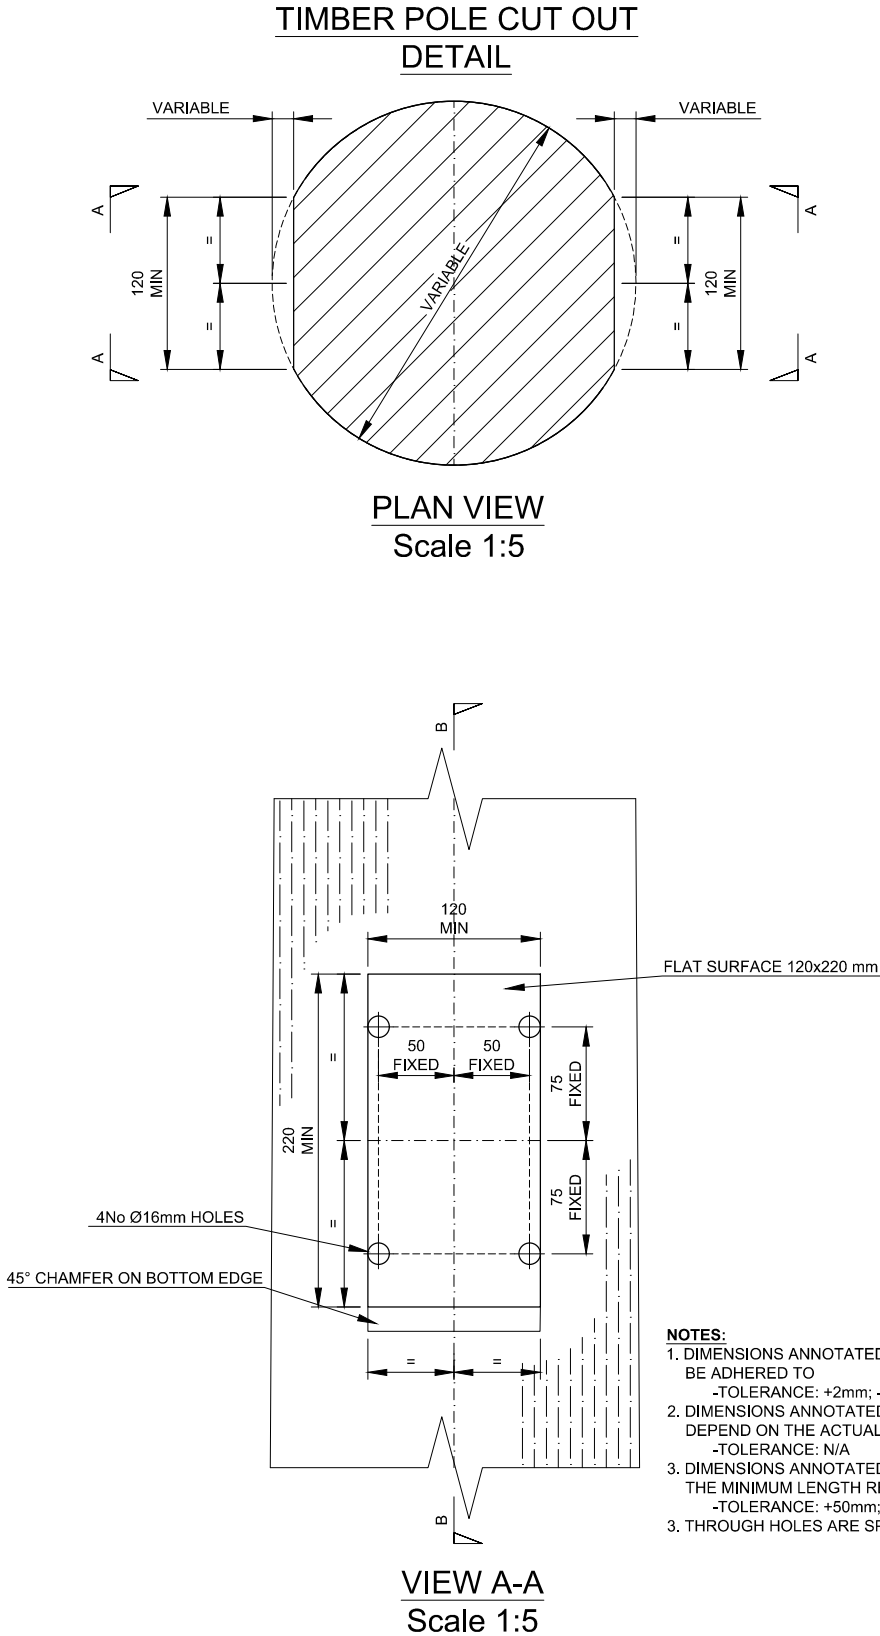


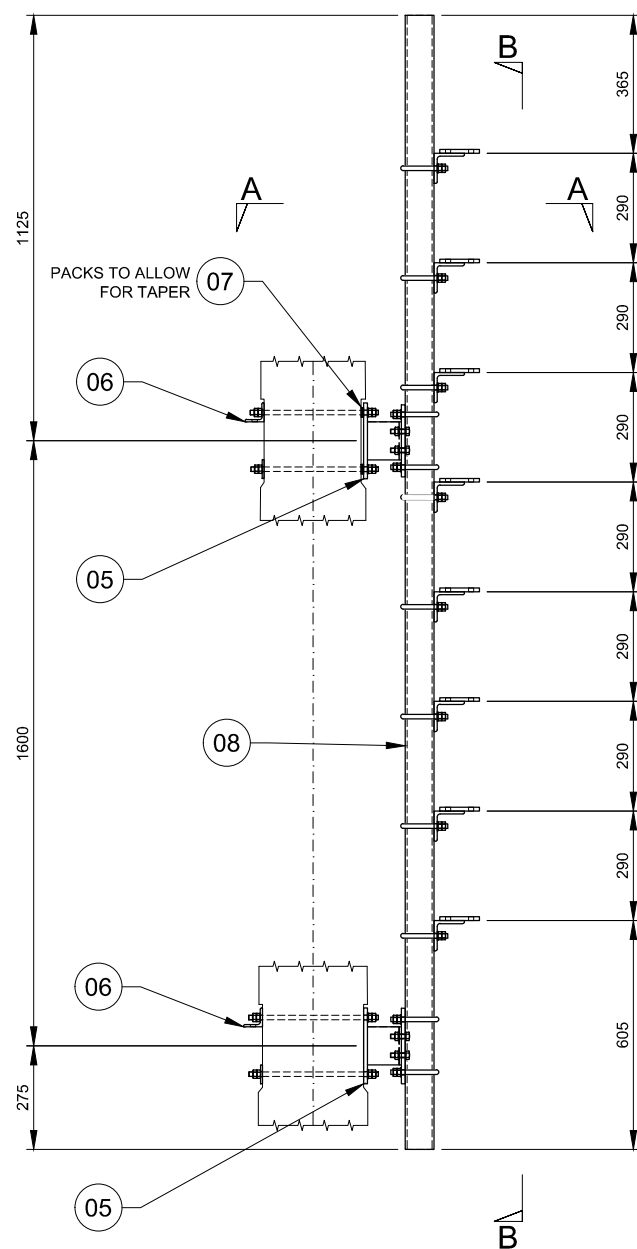


DETAIL G - Tx ANTENNA MOUNT
Scale 1:20

POSITION OF POWER
DIVIDER
TO BE DETERMINED
ON SITE

POSITION OF POWER
DIVIDERS
TO BE DETERMINED
ON SITE

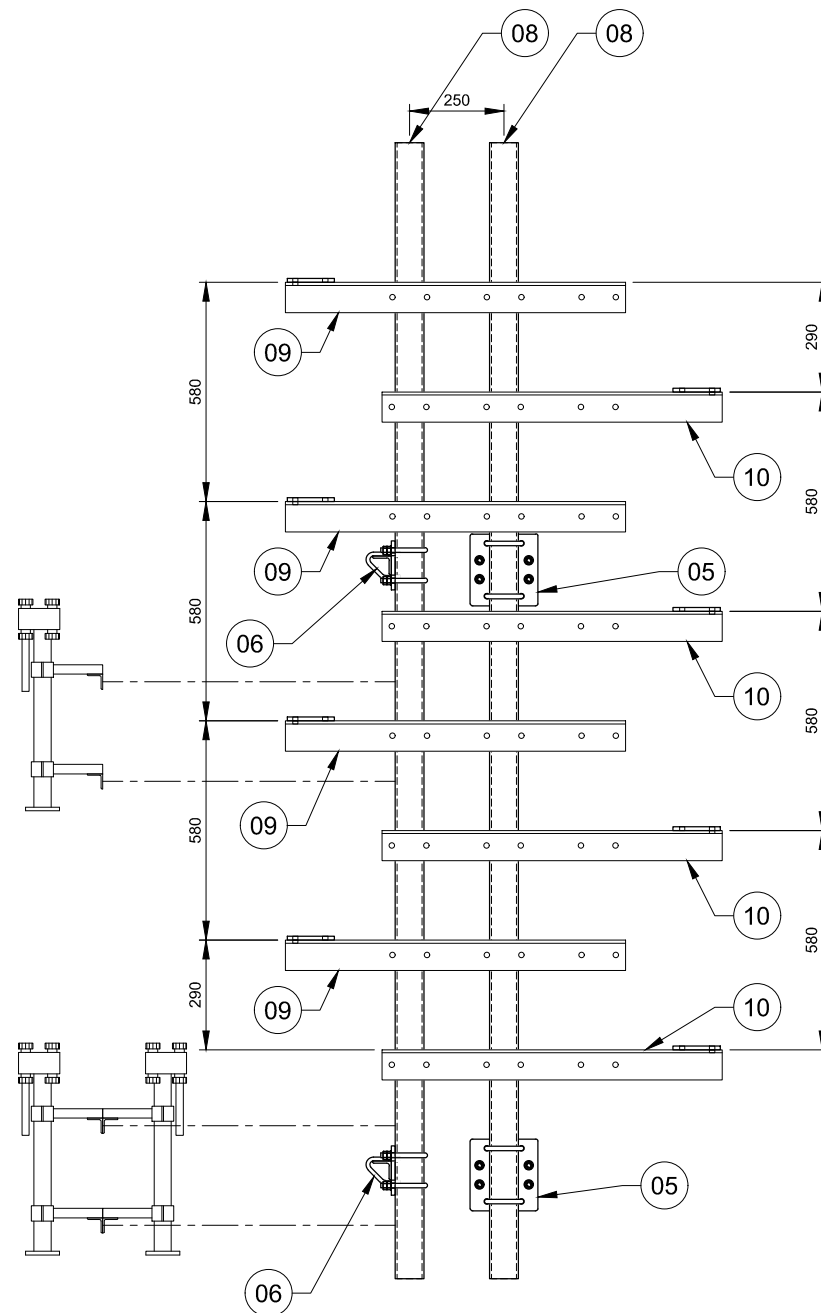


SECTION B-B
Scale 1:20

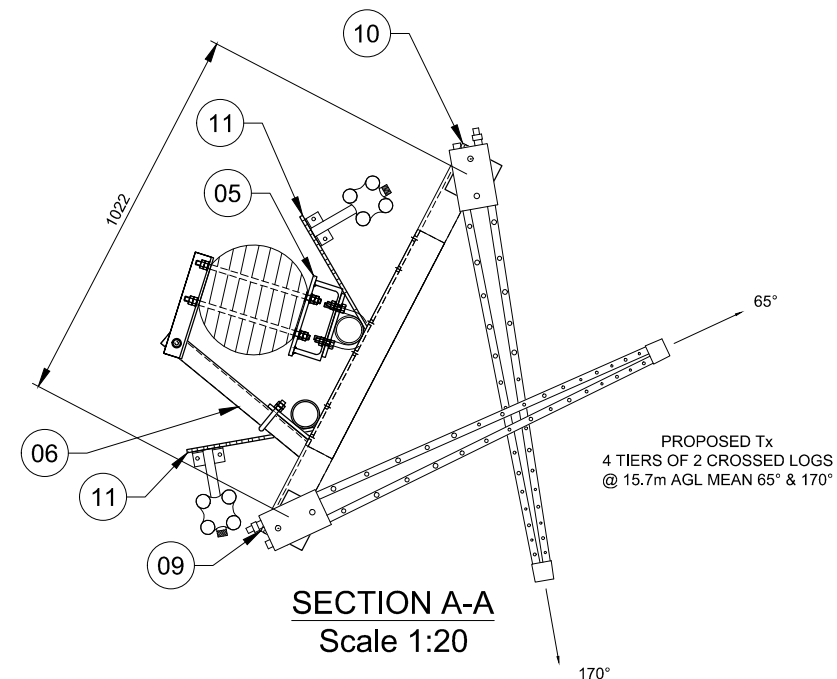

SECTION A-A
Scale 1:20

PROPOSED Tx
4 TIERS OF 2 CROSSED LOGS
@ 15.7m AGL MEAN 65° & 170°

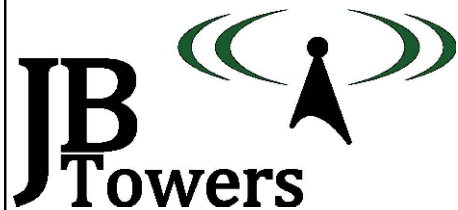

arqiva

02	MINOR UPDATE	AM	16/11/20
01	FIRST ISSUE	AM	29/05/20
REV	REV	BY	DATE
SCALE AS SHOWN WHEN PRINTED AT A3	DRAWN DATE 29/05/20	CHECKED DATE 29/05/20	APPROVED DATE 29/05/20
ALL DIMENSIONS IN mm UNLESS OTHERWISE STATED. THIS DRAWING TO BE READ IN CONJUNCTION WITH OTHER RELEVANT DRAWINGS.			

TITLE

COED DERW

Tx ANTENNA MOUNT

DETAIL G

SITE ADDRESS

COED DERW
MILL STREET
BETWS-Y-COED
ABERCONWY AND
COLWYN
LL24 0BB

ARQIVA REF.
140456


DRG No.
203

REV
02


ALL SCALES AS SHOWN WHEN PRINTED AT A3

ALL SCALES AS SHOWN WHEN PRINTED AT A3


POSITION OF POWER
DIVIDER
TO BE DETERMINED
ON SITE

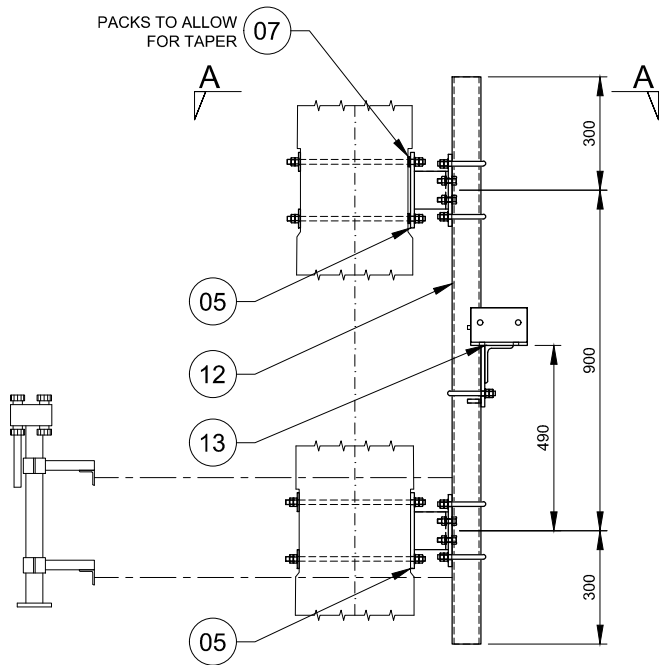

DETAIL H - Rx ANTENNA MOUNT
Scale 1:20

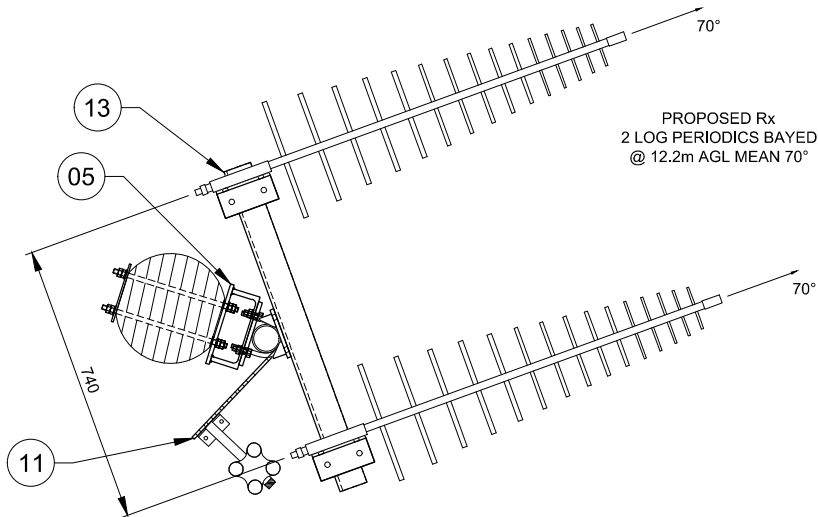

SECTION A-A
Scale 1:20

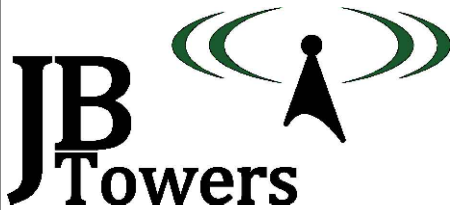

01	FIRST ISSUE	AM	29/05/20
REV	REV	BY	DATE
SCALE AS SHOWN WHEN PRINTED AT A3	DRAWN DATE 29/05/20	CHECKED DATE 29/05/20	APPROVED DATE 29/05/20
ALL DIMENSIONS IN mm UNLESS OTHERWISE STATED. THIS DRAWING TO BE READ IN CONJUNCTION WITH OTHER RELEVANT DRAWINGS.			

TITLE
COED DERW
Rx ANTENNA MOUNT
DETAIL H

SITE ADDRESS
COED DERW
MILL STREET
BETWS-Y-COED
ABERCONWY AND
COLWYN
LL24 0BB

ARQIVA REF.
140456


DRG No.
204

REV
01


ALL SCALES AS SHOWN WHEN PRINTED AT A3



ALL SCALES AS SHOWN WHEN PRINTED AT A3

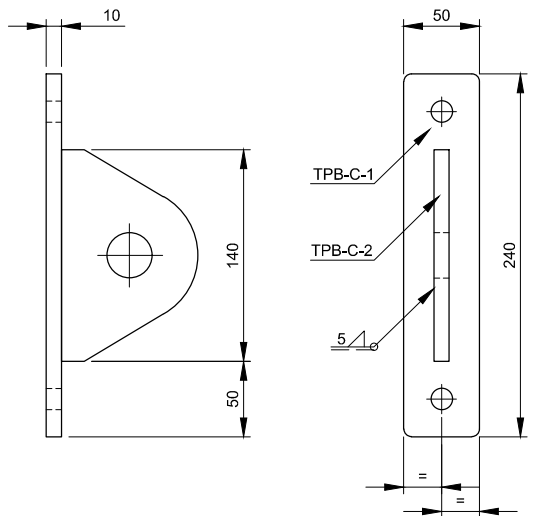

PART TPB-C
Scale 1:5

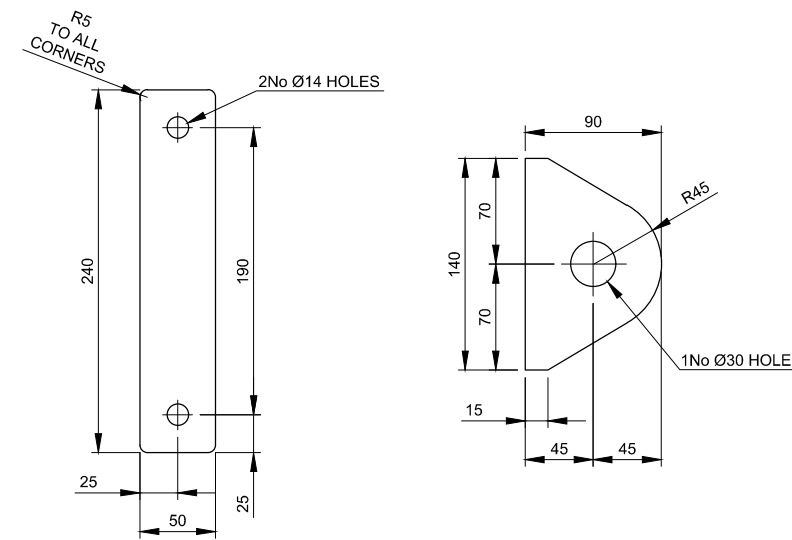


TPB-C-1 - 10mm THICK
Scale 1:5

TPB-C-2 - 10mm THICK
Scale 1:5


Parts list for TPB-C

Item	Part	Quantity	Part description	Length	Material	Weight
01	TPB-C-1	1	Plate 240x50x10mm	N/A	S275J0	0.94 kg
02	TPB-C-2	1	Plate 140x90x10mm	N/A	S275J0	0.99 kg
03	STUDS	1	M12 STUDDING	350mm	GRADE 8.8	0.31 kg
Total Weight:						2.24 kg

- All steel hot dip galvanized
- Each STUD to be supplied with 4 Full Nuts, 2 Flat Washers and 2 Spring Washers
- For fabrication notes see drawing 305

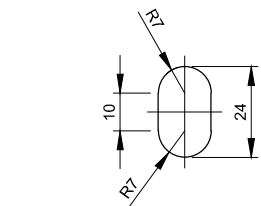

SLOTTED HOLE DETAIL
Scale 1:2

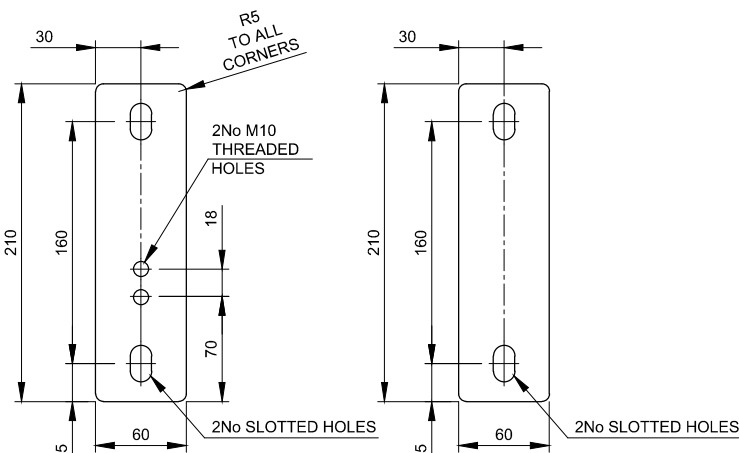


PART TPS-R-1
Scale 1:5

PART TPS-R-2
Scale 1:5

Parts list for TPS-R

Item	Part	Quantity	Part description	Length	Material	Weight
01	TPS-R-1	1	Plate 210x60x15mm	N/A	S275J0	1.48 kg
02	TPS-R-2	1	Plate 210x60x5mm	N/A	S275J0	0.49 kg
03	STUDS	2	M12 STUDDING	500mm	GRADE 8.8	0.44 kg
04	NUT-S	2	M12 SHALLOW NUT	N/A	GRADE 8.8	-
05	NUT	4	M12 NUT	N/A	GRADE 8.8	-
06	WSH	4	M12 WASHER	N/A	GRADE 8.8	-
Total Weight:						2.41 kg

- All steel hot dip galvanized
- For fabrication notes see drawing 305

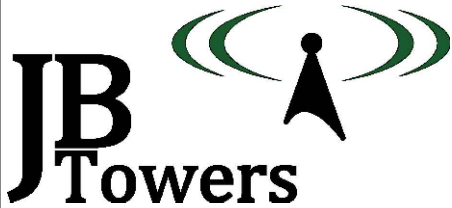

01	FIRST ISSUE					AM	29/05/20
REV	REV					BY	DATE
SCALE AS SHOWN WHEN PRINTED AT A3		DRAWN	AM	CHECKED	MP	APPROVED	JBT
		DATE	29/05/20	DATE	29/05/20	DATE	29/05/20
ALL DIMENSIONS IN mm UNLESS OTHERWISE STATED. THIS DRAWING TO BE READ IN CONJUNCTION WITH OTHER RELEVANT DRAWINGS.							

TITLE
COED DERW
ATTACHMENT POINT &
TEMPORARY STEP DETAILS
PARTS: TPB-C; TPS-R


SITE ADDRESS
COED DERW
MILL STREET
BETWS-Y-COED
ABERCONWY AND
COLWYN
LL24 0BB

ARQIVA REF.
140456
DRG No.
300
REV
01


ALL SCALES AS SHOWN WHEN PRINTED AT A3




ALL SCALES AS SHOWN WHEN PRINTED AT A3

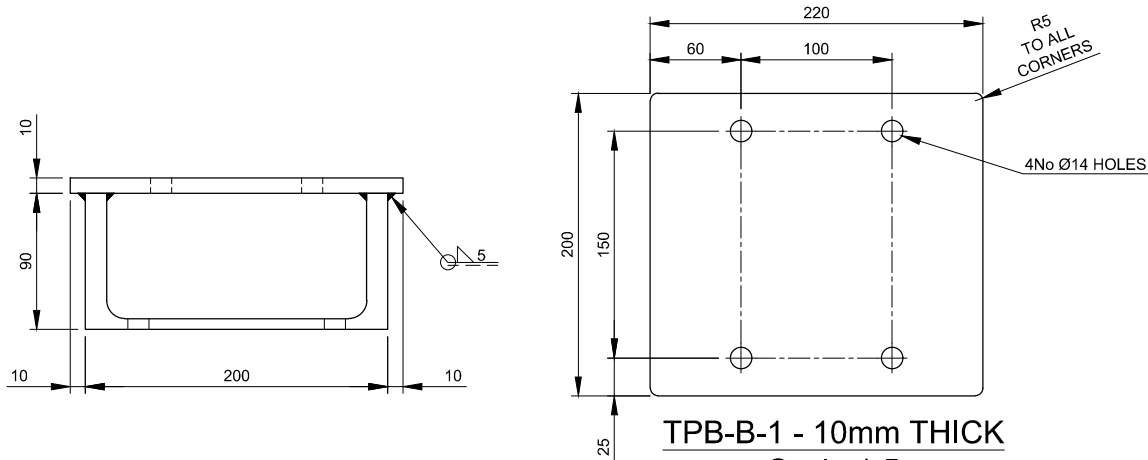


TPB-B-1 - 10mm THICK
Scale 1:5

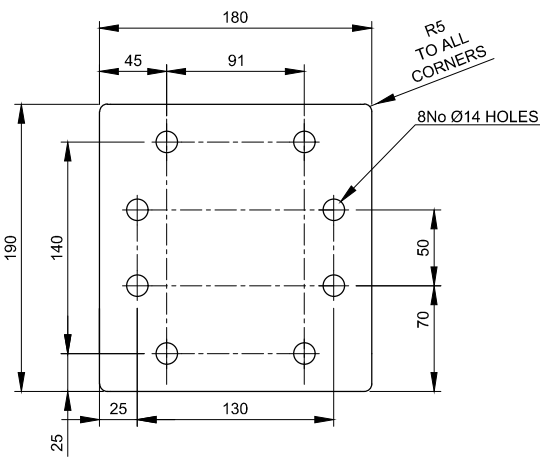


TPB-B-5 - 10mm THICK
Scale 1:5

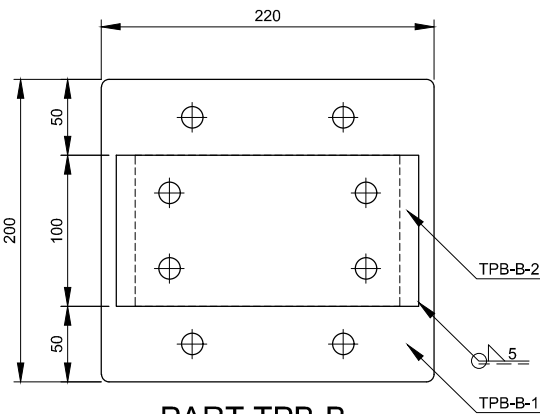


PART TPB-B
Scale 1:5

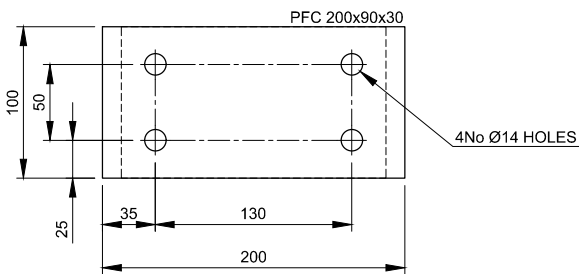

TPB-B-2 - PFC 200x90x30
Scale 1:5

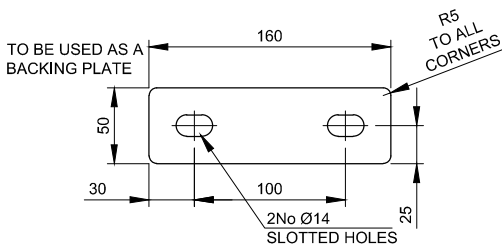

TPB-B-4 - 5mm THICK
Scale 1:5

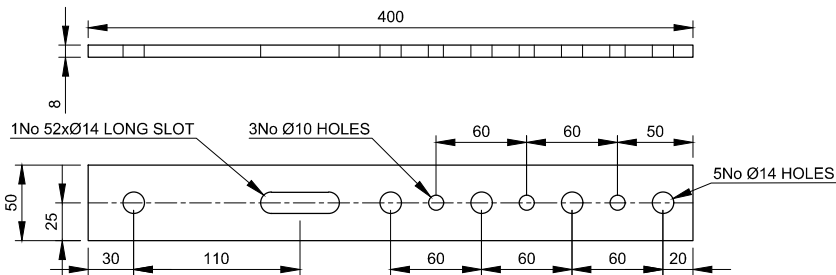


TPA-PD - 8mm THICK
Scale 1:5

Parts list for TPB-B

Item	Part	Quantity	Part description	Length	Material	Weight
01	TPB-B-1	1	Plate 220x200x10mm	N/A	S275J0	3.45 kg
02	TPB-B-2	1	PFC 200x90x30	100mm	S275J0	3.00 kg
03	TPB-B-4	2	Plate 160x50x5mm	N/A	S275J0	0.31 kg
04	TPB-B-5	1	Plate 190x180x10mm	N/A	S275J0	2.70 kg
05	STUDS	4	M12 STUDDING	450mm	GRADE 8.8	0.39 kg
06	BOLT	4	M12 45mm LONG (2D+6)	45mm	GRADE 8.8	-
07	U-BOLT	2	M12 U-BOLT FOR CHS 76.1	N/A	GRADE 8.8	-

- All steel hot dip galvanized
- Each STUD & U-BOLT to be supplied with 4 Full Nuts, 2 Flat Washers and 2 Spring Washers
- Each BOLT to be supplied with 1 Full Nut, 1 Form E FLat Washer and 1 Spring Washer
- For fabrication notes see drawing 305

Total Weight: 11.33 kg

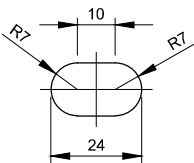


SLOTTED HOLE DETAIL
Scale 1:2

Parts list for TPA-PD

Item	Part	Quantity	Part description	Length	Material	Weight
01	TPA-PD	1	400x50x8mm	N/A	S275J0	1.26 kg
02	U-BOLT	1	M12 U-BOLT FOR CHS 76.1mm	N/A	GRADE 8.8	-

Total Weight: 1.26 kg

- All steel hot dip galvanized
- Each U-BOLT to be supplied with 4 Full Nuts, 2 Flat Washers and 2 Spring Washers
- For fabrication notes see drawing 305

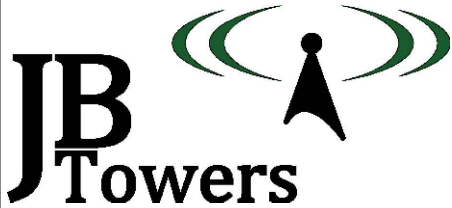

01	FIRST ISSUE	AM	29/05/20
REV	REV	BY	DATE
SCALE AS SHOWN WHEN PRINTED AT A3	DRAWN DATE	AM 29/05/20	CHECKED DATE
MP	APPROVED	JBT	DATE
DATE	29/05/20	DATE	29/05/20
DATE	29/05/20	DATE	29/05/20
ALL DIMENSIONS IN mm UNLESS OTHERWISE STATED. THIS DRAWING TO BE READ IN CONJUNCTION WITH OTHER RELEVANT DRAWINGS.			

TITLE

COED DERW

STEELWORK BRACKET,
POWER DIVIDER STRAP

PARTS: TPB-B, TPA-PD

SITE ADDRESS

COED DERW
MILL STREET
BETWS-Y-COED
ABERCONWY AND
COLWYN
LL24 0BB

ARQIVA REF.
140456


DRG No.
301

REV
01

ALL SCALES AS SHOWN WHEN PRINTED AT A3




ALL SCALES AS SHOWN WHEN PRINTED AT A3

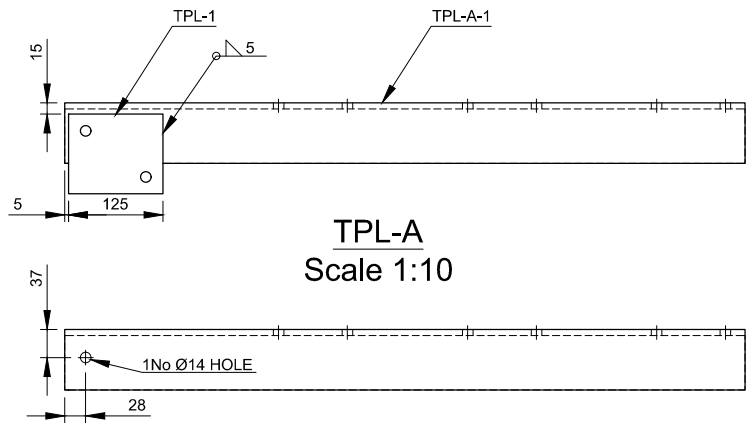

TPL-A
Scale 1:10


TPL-A-1 - EA 80x80x8
Scale 1:10

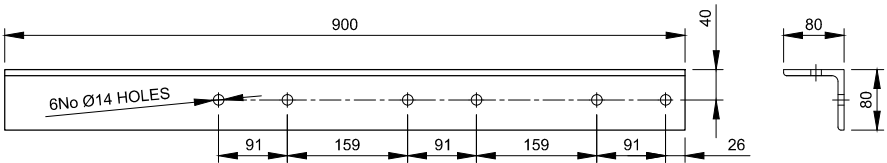

Parts list for TPL-A


Item	Part	Quantity	Part description	Length	Material	Weight
01	TPL-A-1	1	EA 80x80x8	900mm	S275J0	8.70 kg
02	TPL-1	1	Plate 125x105x10	N/A	S275J0	1.00 kg
03	U-BOLT	2	M12 U-BOLT FOR CHS 76.1mm	N/A	GRADE 8.8	-
Total Weight:						9.70 kg

- All steel hot dip galvanized
- Each U-BOLT to be supplied with 4 Full Nuts, 2 Flat Washers and 2 Spring Washers
- For fabrication notes see drawing 305

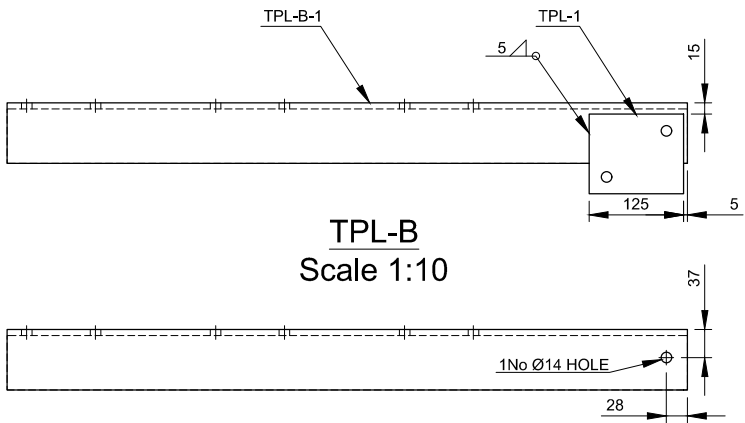

TPL-B
Scale 1:10


TPL-B-1 - EA 80x80x8
Scale 1:10

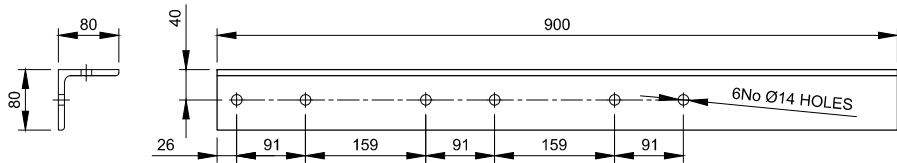


Parts list for TPL-B

Item	Part	Quantity	Part description	Length	Material	Weight
01	TPL-B-1	1	EA 80x80x8	900mm	S275J0	8.70 kg
02	TPL-1	1	Plate 125x105x10	N/A	S275J0	1.00 kg
03	U-BOLT	2	M12 U-BOLT FOR CHS 76.1mm	N/A	GRADE 8.8	-
Total Weight:						9.70 kg

- All steel hot dip galvanized
- Each U-BOLT to be supplied with 4 Full Nuts, 2 Flat Washers and 2 Spring Washers
- For fabrication notes see drawing 305

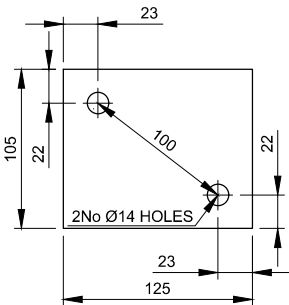

TPL-1 - 10mm THICK
Scale 1:5

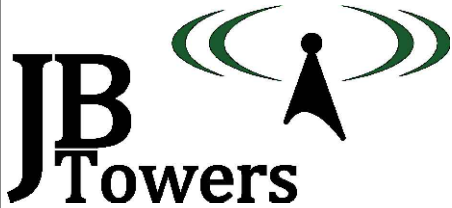


01	FIRST ISSUE	AM	29/05/20
REV	REV	BY	DATE
SCALE AS SHOWN	DRAWN	CHECKED	APPROVED
WHEN PRINTED AT A3	DATE	DATE	DATE
ALL DIMENSIONS IN mm UNLESS OTHERWISE STATED. THIS DRAWING TO BE READ IN CONJUNCTION WITH OTHER RELEVANT DRAWINGS.			


TITLE
COED DERW
LOG MOUNTS
PARTS: TPL-A; TPL-B

SITE ADDRESS
COED DERW
MILL STREET
BETWS-Y-COED
ABERCONWY AND
COLWYN
LL24 0BB


ARQIVA REF.
140456
DRG No.
302
REV
01

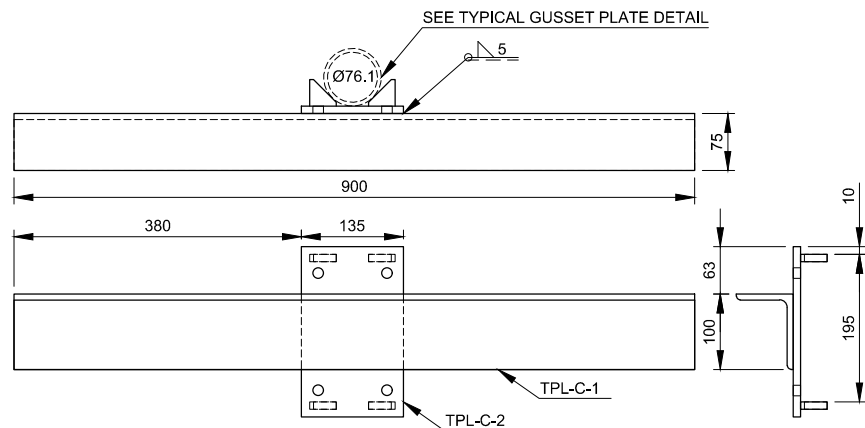

TPL-C - UA100x75x8
Scale 1:10

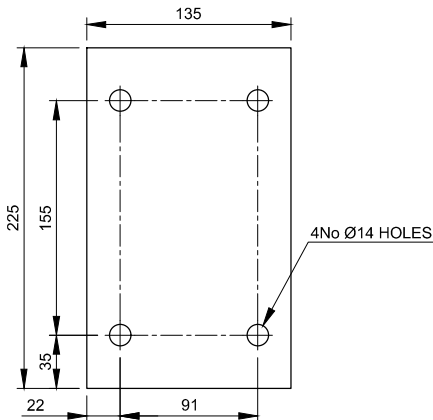

TPL-C-2 - 10mm THICK
Scale 1:5

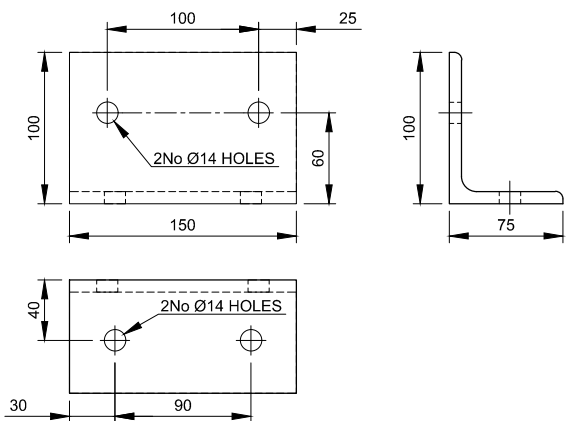


TPL-C-3 - UA100x75x8
Scale 1:5

Parts list for TPL-C


Item	Part	Quantity	Part description	Length	Material	Weight
01	TPL-C-1	1	UA100x75x8	900mm	S275J0	9.60 kg
02	TPL-C-2	1	PLATE 225x135x10mm C/W GUSSETS	N/A	S275J0	2.40 kg
03	TPL-C-3	2	UA100x75x8	150mm	S275J0	1.60 kg
04	U-BOLT	2	M12 U-BOLT FOR CHS 76.1mm	N/A	GRADE 8.8	-
05	N-BOLT	2	M12 N-BOLT FOR UA100x75 (C=90mm)	N/A	GRADE 8.8	-

Total Weight: 15.40 kg

- All steel hot dip galvanized
- Each STUD & U-BOLT to be supplied with 4 Full Nuts, 2 Flat Washers and 2 Spring Washers
- Each BOLT to be supplied with 1 Full Nut, 1 Form E FLat Washer and 1 Spring Washer
- For fabrication notes see drawing 305

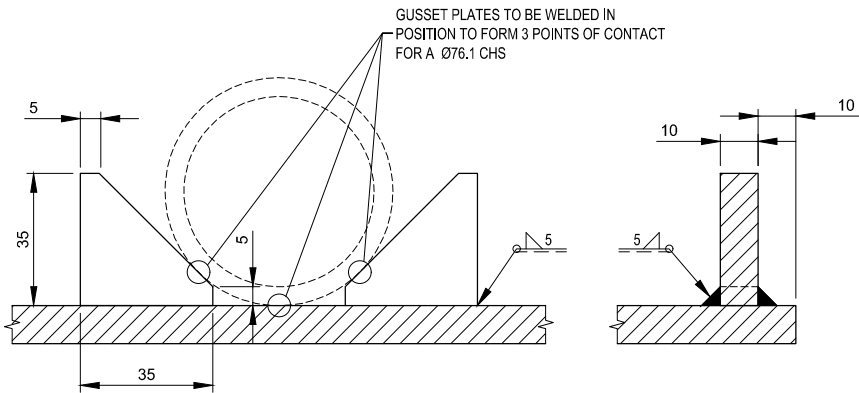

TYPICAL GUSSET PLATE DETAIL
Scale 1:2

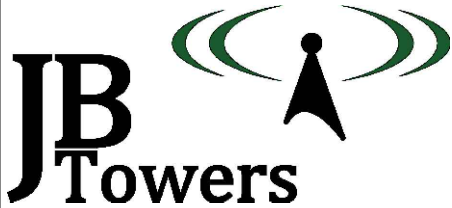

01	FIRST ISSUE			AM	29/05/20
REV	REV			BY	DATE
SCALE AS SHOWN WHEN PRINTED AT A3		DRAWN AM DATE 29/05/20	CHECKED MP DATE 29/05/20	APPROVED JBT DATE 29/05/20	
ALL DIMENSIONS IN mm UNLESS OTHERWISE STATED. THIS DRAWING TO BE READ IN CONJUNCTION WITH OTHER RELEVANT DRAWINGS.					

TITLE
COED DERW
LOG MOUNT
PART: TPL-C

SITE ADDRESS
COED DERW
MILL STREET
BETWS-Y-COED
ABERCONWY AND
COLWYN
LL24 0BB

ARQIVA REF.
140456


DRG No.
303

REV
01



ALL SCALES AS SHOWN WHEN PRINTED AT A3




ALL SCALES AS SHOWN WHEN PRINTED AT A3

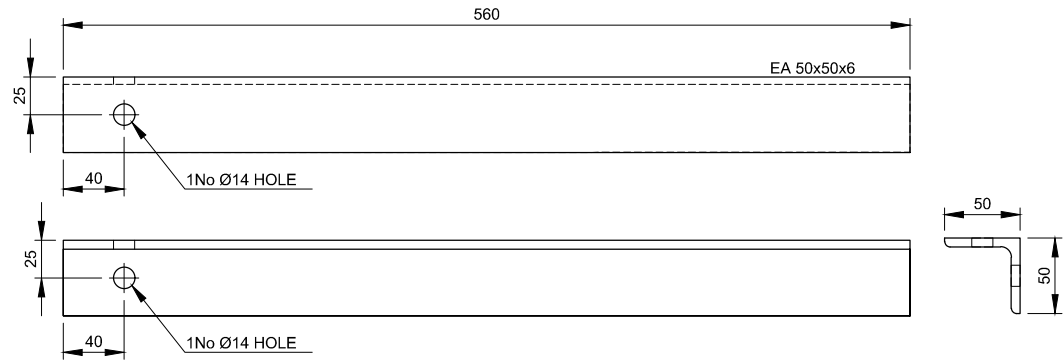


TPB-BR-1 - EA50x50x6
Scale 1:5

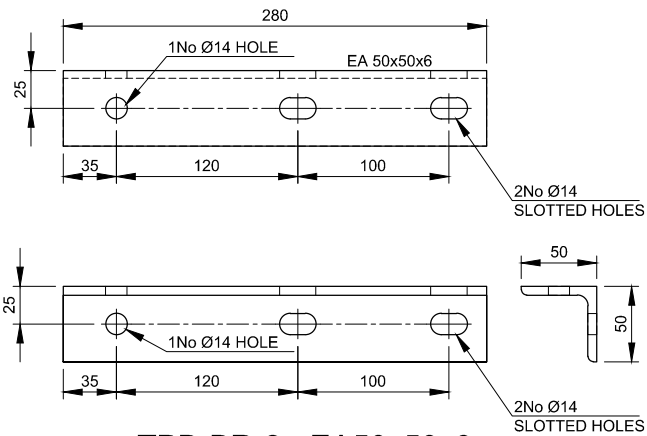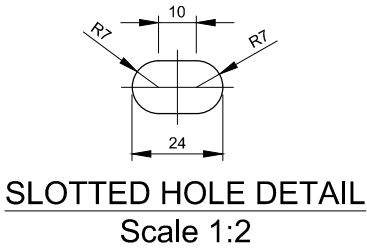

TPB-BR-2 - EA50x50x6
Scale 1:5

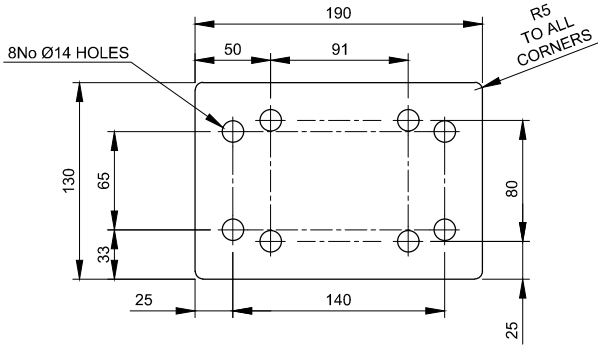

TPB-BR-3 - 10mm THICK
Scale 1:5

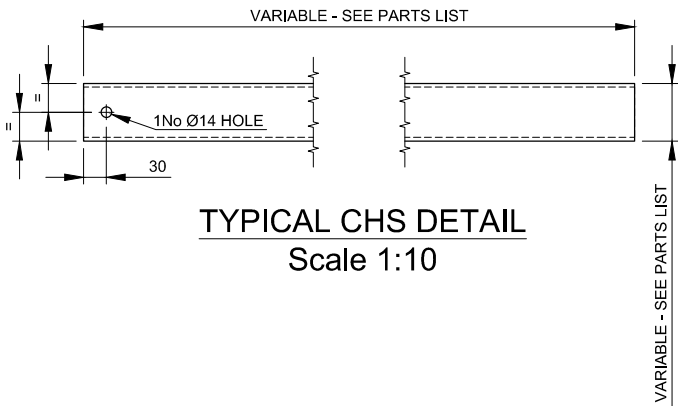


TYPICAL CHS DETAIL
Scale 1:10

Parts list for TPB-BR

Item	Part	Quantity	Part description	Length	Material	Weight
01	TPB-BR-1	1	EA 50x50x6	280mm	S275J0	1.25 kg
02	TPB-BR-2	1	EA 50x50x6	560mm	S275J0	2.50 kg
03	TPB-BR-3	1	Plate 130x190x10mm	N/A	S275J0	1.95 kg
04	BOLT	1	M12 SET BOLT - 30mm LONG	N/A	GRADE 8.8	-
05	N-BOLT	2	M12 N-BOLT FOR EA 50x50x6	N/A	GRADE 8.8	-
06	U-BOLT	2	M12 U-BOLT FOR CHS 76.1mm	N/A	GRADE 8.8	-
Total Weight:						5.70 kg

- All steel hot dip galvanized
- Each BOLT to be supplied with 1 Full Nut, 1 Form E FLat Washer and 1 Spring Washer
- Each STUD & U-BOLT to be supplied with 4 Full Nuts, 2 Flat Washers and 2 Spring Washers
- For fabrication notes see drawing 305

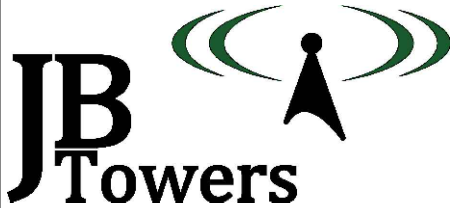

01	FIRST ISSUE			AM	29/05/20	
REV	REV			BY	DATE	
SCALE AS SHOWN	DRAWN	AM	CHECKED	MP	APPROVED	JBT
WHEN PRINTED AT A3	DATE	29/05/20	DATE	29/05/20	DATE	29/05/20
ALL DIMENSIONS IN mm UNLESS OTHERWISE STATED. THIS DRAWING TO BE READ IN CONJUNCTION WITH OTHER RELEVANT DRAWINGS.						

TITLE
COED DERW
BRACING ARM & TYPICAL
CHS DETAIL
PART: TPB-BR

SITE ADDRESS
COED DERW
MILL STREET
BETWS-Y-COED
ABERCONWY AND
COLWYN
LL24 0BB

ARQIVA REF.
140456
DRG No.
304
REV
01

ALL SCALES AS SHOWN WHEN PRINTED AT A3




ALL SCALES AS SHOWN WHEN PRINTED AT A3

Item	Part	Drawing	Quantity	Part description	Length	Material	Weight
01	01	200	1	3 MAN LATCHWAY SYSTEM & 4No. WIRE GUIDES FOR FACE MOUNTED MONOPOLE	17000	N/A	-
02	TPB-C	300	2	FALL ARREST ATTACHMENT POINT	N/A	S275J0	4.50 kg
03	03	200	46	PERMANENT BT STEP c/w 3No 10x75mm ZINC-PLATED COACH SCREWS	N/A	S275J0	14.40 kg
04	TPS-R	300	9	'MonoStep' ASSEMBLY	N/A	S275J0	21.70 kg
05	TPB-B	301	4	MOUNTING BRACKET	N/A	S275J0	45.30 kg
06	TPB-BR	304	2	BRACING ARM	N/A	S275J0	11.40 kg
07	07	203	12	M12 WASHER	N/A	GRADE 8.8	-
08	08	203	2	CHS 76.1x5mm	3000mm	S355J2H	52.60 kg
09	TPL-A	302	4	LOG MOUNTING BRACKET	900mm	S275J0	38.80 kg
10	TPL-B	302	4	LOG MOUNTING BRACKET	900mm	S275J0	38.80 kg
11	TPA-PD	301	8	POWER DIVIDER STRAP	N/A	S275J0	10.10 kg
12	12	204	1	CHS 76.1x5mm	1500mm	S355J2H	13.20 kg
13	TPL-C	303	1	LOG MOUNTING BRACKET	N/A	S275J0	15.40 kg
14	14	200	1	PoleSaver	750mm	N/A	-
15	15	200	7	M12 STUD + 4No NUTS + 2No FLAT WASHERS + 1No Ø50mm WASHER (FOR FALL ARREST SYSTEM)	500mm	GRADE 8.8	3.10 kg
16	16	200	1	FEEDER COVER - 2/CG/100	3500mm	UV RESISTANT PLASTIC	-
17	17	200	17	FEEDER CLAMP - 2/FCD/028	N/A	POLYPROPYLENE	-
18	18	200	17	M10 SCREW DOWELS WTH M10 NUT	100mm	STAINLESS STEEL	-
Total Weight:							269.30 kg

- All steel hot dip galvanized
- All U-BOLTS to be FLA supply, each Supplied with 4 Full Nuts, 2 Flat Washers and 2 Spring Washers

NOTES:

1. WELDING TO BE IN ACCORDANCE WITH BS EN 1011-1:2009
2. LINEAR DIMS TO BE WITHIN ±1mm;
3. ANGULAR TOLERANCES TO BE WITHIN 0.5°
4. WELDING SYMBOLS ARE IN ACCORDANCE WITH BS EN 22553:1995
5. ALL PROFILE EDGES TO BE DRESSED AND SHARP CORNERS REMOVED
6. ALL WELD SIZES ARE FINAL SIZES
7. ALL WELDED JOINTS ARE TO BE PICKLE TIGHT
8. ALL STEELWORK TO BE BS EN 10025 GRADE S275 J0 UNO, HOT DIPPED GALVANISED TO BS EN ISO 1461. (ALL HOLLOW SECTIONS TO BE GRADE S355 J0H)
9. ALL STEEL IS TO BE SUPPLIED IN ACCORDANCE WITH EN 1090 TO EXECUTION CLASS 2
10. ALL NON PRE-LOADED BOLTS TO BE COMPLIANT STRUCTURAL BOLTS TO BS EN ISO 15048 PARTS 1&2.
11. STEELWORK COMPONENTS SHALL BE HOT DIP GALVANISED TO ACHIEVE A "VERY HIGH" DURABILITY FOR AN ENVIRONMENT CATEGORY CODE C4 FROM TABLE 1 IN BS EN ISO 14713
12. BOLTS AND NUTS SHALL BE SUPPLIED IN ACCORDANCE WITH BS 7371, SPUN GALVANISED IN ACCORDANCE WITH ISO 10684, THE NUTS RE-TAPPED AFTER GALVANISING, AND THE THREADS TREATED WITH GREASE.
13. ALL BOLTS TO BE CUT ON SITE TO EXTEND MAX 10mm BEYOND THE NUT WHEN TIGHTENED UNO.
14. ALL SITE DRILLED HOLE/CUT ENDS TO BE TREATED WITH METAFLUX 70-40 ZINC PASTE FOLLOWED BY 1 COAT OF 7-42 ZINC ALU OR 70-16 ALUMINIUM SPRAY

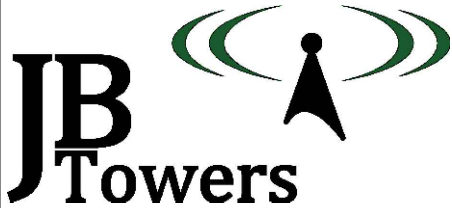

01	FIRST ISSUE					AM	29/05/20
REV	REV					BY	DATE
SCALE AS SHOWN		DRAWN	AM	CHECKED	MP	APPROVED	JBT
WHEN PRINTED AT A3		DATE	29/05/20	DATE	29/05/20	DATE	29/05/20
ALL DIMENSIONS IN mm UNLESS OTHERWISE STATED. THIS DRAWING TO BE READ IN CONJUNCTION WITH OTHER RELEVANT DRAWINGS.							

TITLE

COED DERW

PARTS LIST

SITE ADDRESS

COED DERW

MILL STREET

BETWS-Y-COED

ABERCONWY AND

COLWYN

LL24 0BB

ARQIVA REF.

140456

DRG No.

305



REV

01




ALL SCALES AS SHOWN WHEN PRINTED AT A3



ALL SCALES AS SHOWN WHEN PRINTED AT A3

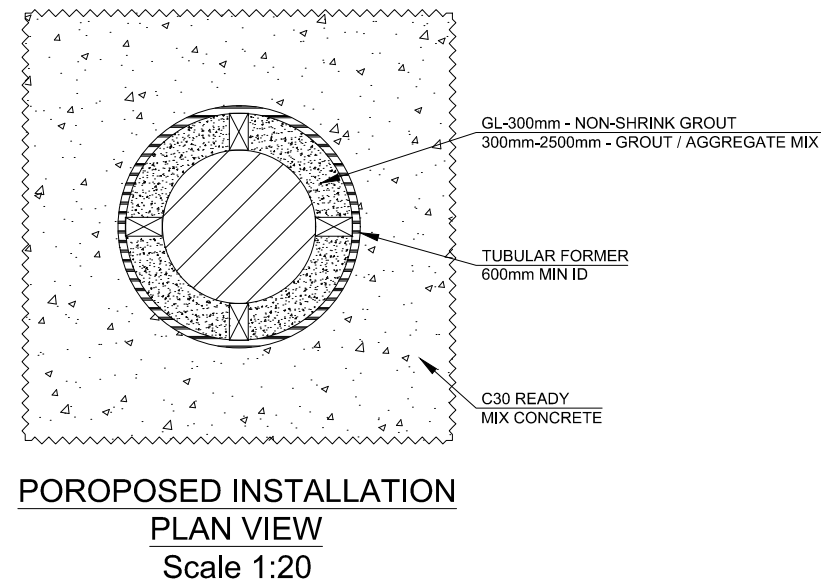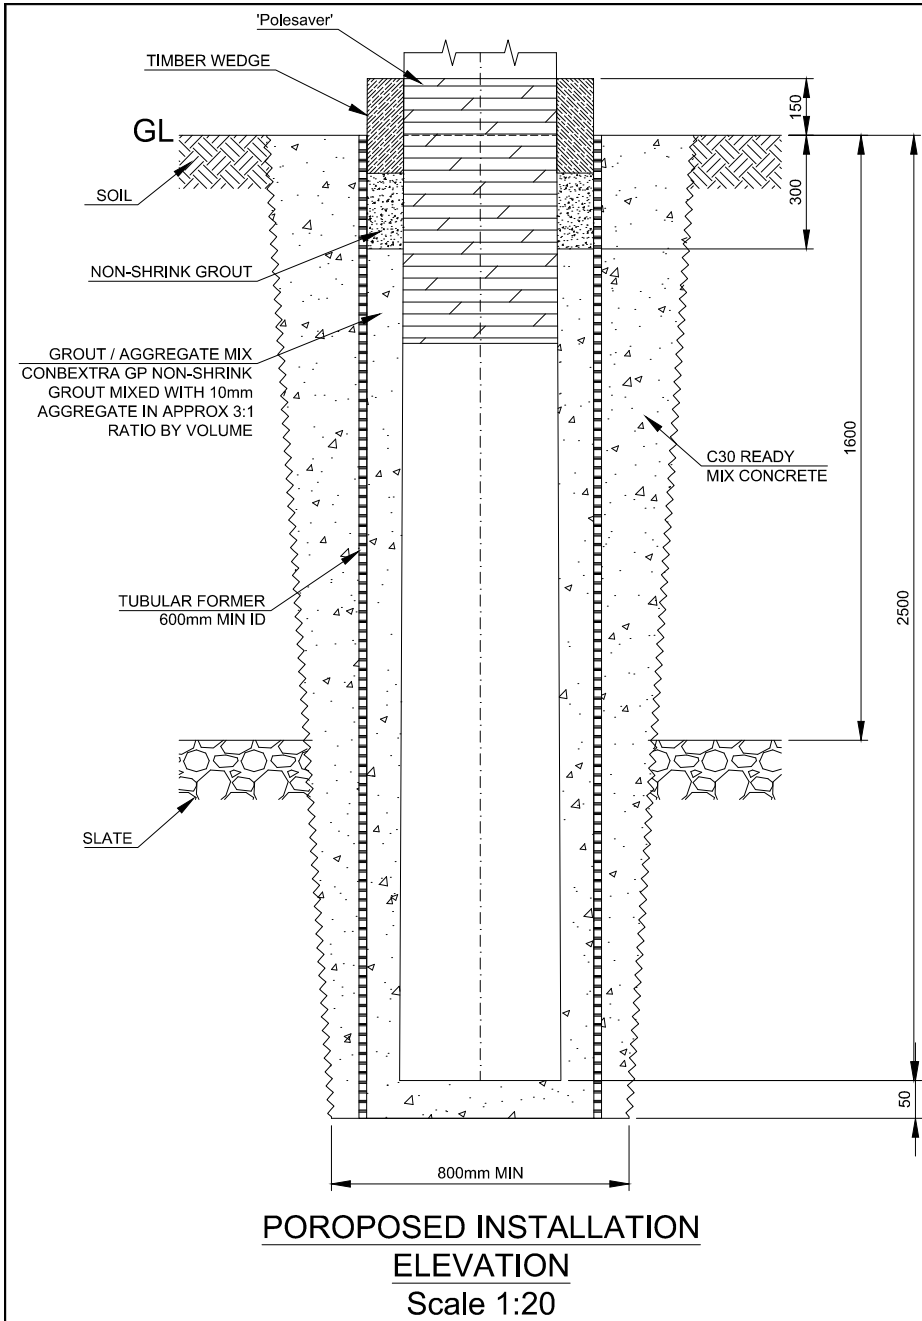

- TIMBER POLE INSTALLATION:**
1. REFER TO DRAWING 200 FOR TIMBER POLE ORIENTATION
 2. EXCAVATE A HOLE MIN. 800mm SQUARE TO A DEPTH OF 2500mm
 3. INSERT FORMER WITH APPROPRIATE SUPPORT TO ENSURE IT HOLDS ITS SHAPE
 4. POUR CONCRETE AROUND OUTSIDE OF BASE OF FORMER UPTO ~0.5m FROM BASE OF HOLE & PLACE 50mm OF GROUT / AGGREGATE MIX INSIDE BASE OF FORMER. CONCRETE MIX TO ACHIEVE MIN STRENGTH OF 15 N/mm2 AFTER 2 DAYS & MIN 30 N/mm2 AFTER 28 DAYS
 5. REMAINDER OF CONCRETE TO BE POURED THE FOLLOWING DAY
 6. POLE TO BE WRAPPED IN 'POLESAVER' AND INSTALLED AND LEVELLED IN OPENING. TIMBERS TO BE USED TO HOLD POLE IN POSITION. POLE TO BE INSTALLED MIN OF 2 DAYS AFTER INITIAL CONCRETE POUR
 7. ANNULUS SHALL BE FILLED WITH GROUT / AGGREGATE MIX TO 300mm BELOW GL
 8. TOP 300mm SHALL BE FILLED WITH NON-SHRINK GROUT. A 1:60 FALL SHALL BE FORMED AROUND TIMBER POLE TO ALLOW WATER TO DRAIN AWAY FROM POLE
 9. ONCE GROUT HAS CURED REMOVE TIMBER WEDGES AND FILL REMAINING VOIDS WITH NON-SHRINK GROUT

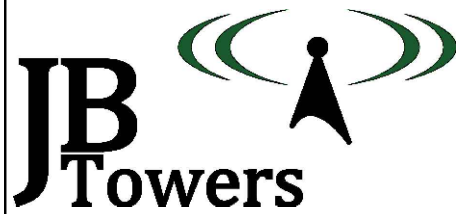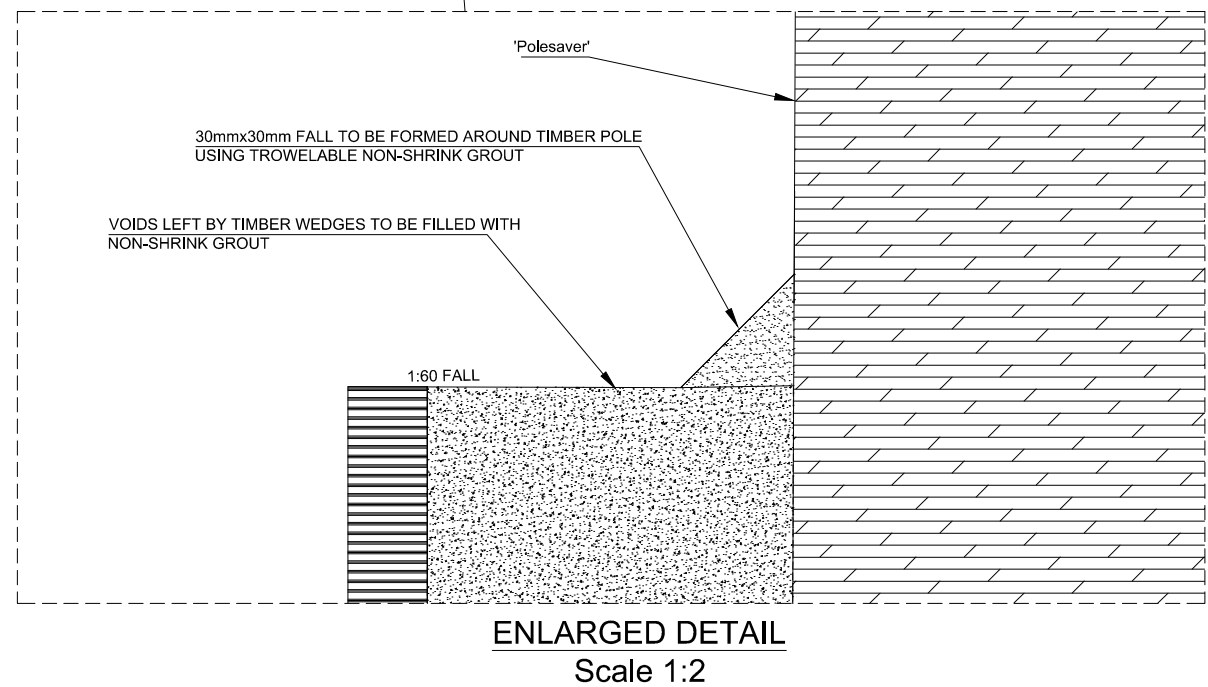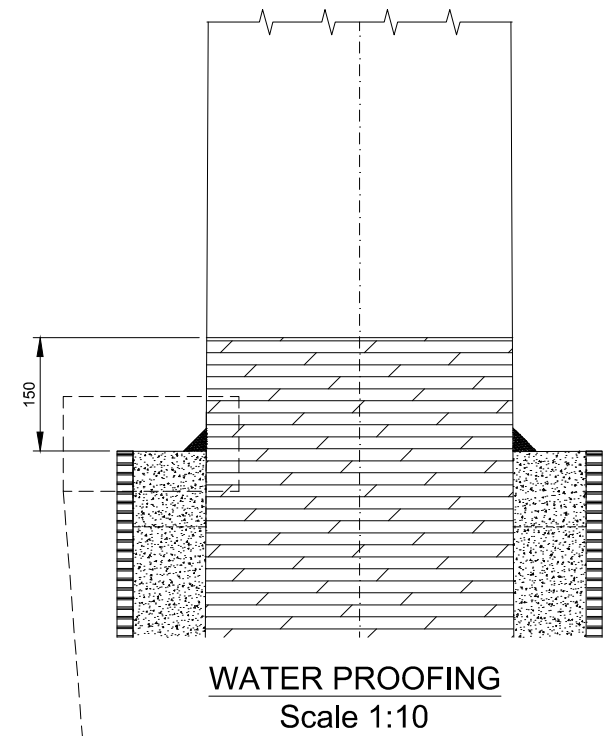

01	FIRST ISSUE					AM	29/05/20
REV	REV					BY	DATE
SCALE AS SHOWN WHEN PRINTED AT A3		DRAWN	AM	CHECKED	MP	APPROVED	JBT
		DATE	29/05/20	DATE	29/05/20	DATE	29/05/20
ALL DIMENSIONS IN mm UNLESS OTHERWISE STATED. THIS DRAWING TO BE READ IN CONJUNCTION WITH OTHER RELEVANT DRAWINGS.							

TITLE		SITE ADDRESS		
COED DERW		COED DERW		
TIMBER POLE FOUNDATION DETAILS		MILL STREET		
		BETWS-Y-COED		
		ABERCONWY AND		
		LL24 0BB		
ARQIVA REF.		DRG No.	REV	
140456		400	01	

ALL SCALES AS SHOWN WHEN PRINTED AT A3