
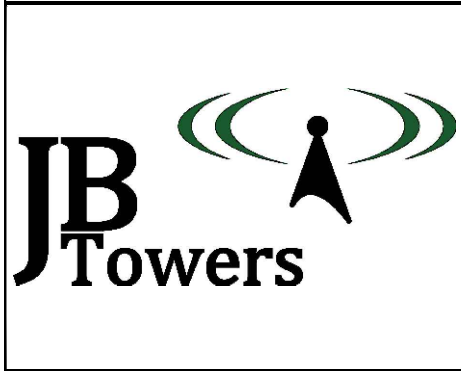


DRAWING ISSUE SHEET

[illegible]

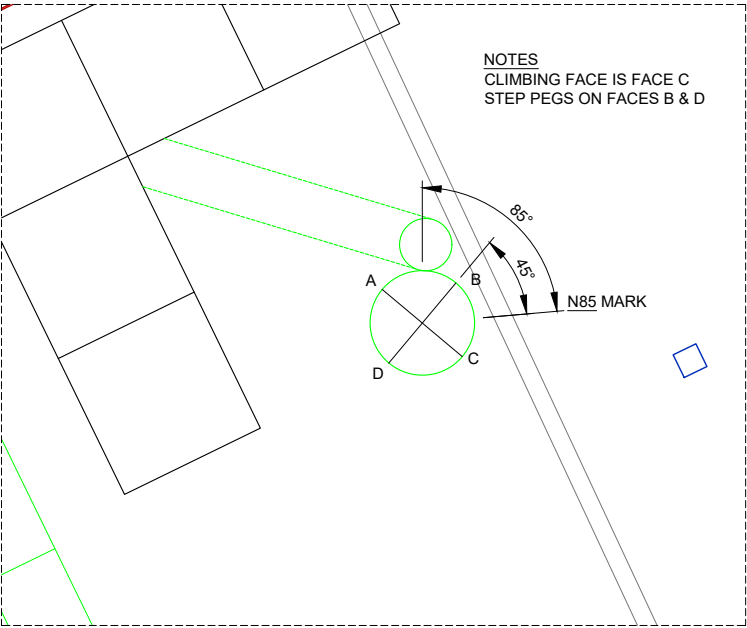


01	FIRST ISSUE				TT	20/06/19
REV	REV				BY	DATE
SCALE AS SHOWN		DRAWN	AM	CHECKED	MP	APPROVED JBT
WHEN PRINTED AT A3		DATE	20/06/19	DATE	20/06/19	DATE 20/06/19
ALL DIMENSIONS IN mm UNLESS OTHERWISE STATED.						THIS DRAWING TO BE READ IN CONJUNCTION WITH OTHER RELEVANT DRAWINGS.

TITLE
FERRYSIDE
SITE PLAN

SITE ADDRESS
TRI PEN HAD ROAD
DYFED
CARMARTHENSHIRE
SA17 5UR

ARQIVA REF. 140665	DRG No. 100	REV 01
-----------------------	----------------	-----------

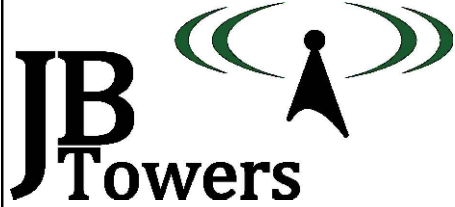

01	FIRST ISSUE			TT	20/06/19
REV	REV			BY	DATE
SCALE AS SHOWN		DRAWN	AM	CHECKED	MP
WHEN PRINTED AT A3		DATE	20/06/19	DATE	20/06/19
		APPROVED		JBT	
ALL DIMENSIONS IN mm UNLESS OTHERWISE STATED. THIS DRAWING TO BE READ IN CONJUNCTION WITH OTHER RELEVANT DRAWINGS.					

TITLE

FERRYSIDE

GENERAL ARRANGEMENT

SHEET 1 OF 3

SITE ADDRESS

TRI PEN HAD ROAD

DYFED

CARMARTHENSHIRE

SA17 5UR

ARQIVA REF.



140665

DRG No.

200

REV

01

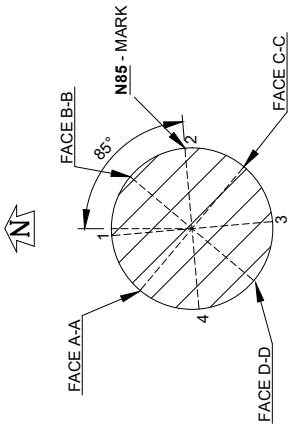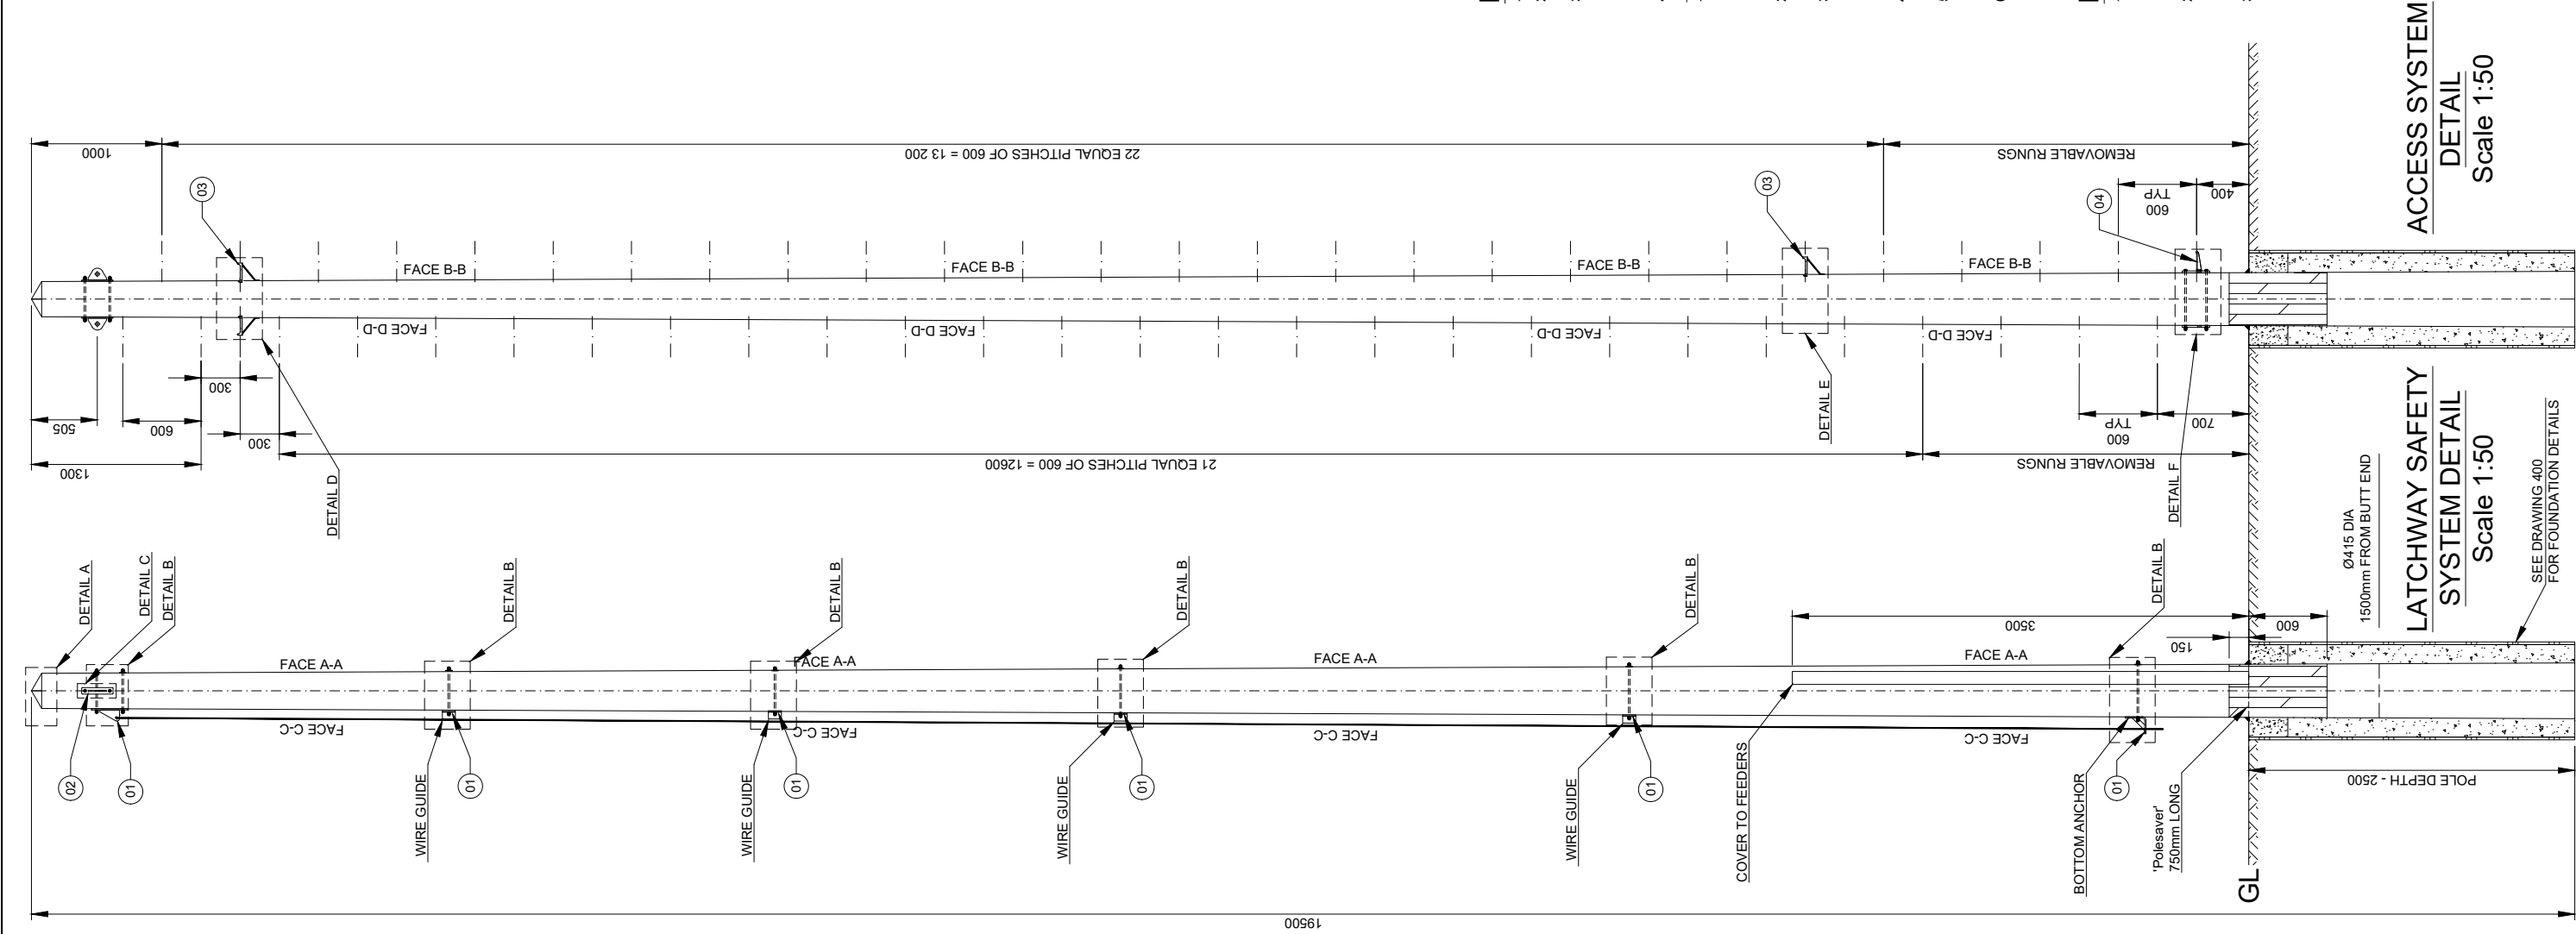

NOTES

- SEE DRAWING 305 FOR PARTS LIST
- ALL BOLTS TO BE CUT ON SITE TO EXTEND MAX 10mm BEYOND THE NUT WHEN TIGHTENED UNO.
- ALL SITE DRILLED HOLE/CUT ENDS TO BE TREATED WITH METAFUX 70-40 ZINC PASTE FOLLOWED BY 1 COAT OF 7-42 ZINC ALU OR 70-16 ALUMINIUM SPRAY

TIMBER POLE

- POLE TO BE SUPPLIED IN ACCORDANCE WITH BS EN14229 & SHALL HAVE MIN. CHARACTERISTIC BENDING STRENGTH OF 30N/mm² & MIN. YOUNGS MODULUS (PARALLEL TO GRAIN) OF 10KN/mm².
- MARKINGS ON FINISHED POLE SHALL BE AT 4m FROM BUTT AND COMPLY WITH BS EN 14229 UNO
- AS FAR AS PRACTICABLE ALL CUTTING, SCARFING & DRILLING TO BE DONE BEFORE CREOSOTING. IF NOT ALL CUT, DRILLED & SCARFED SURFACES TO BE COATED WITH A MIXTURE OF CREOSOTE & TAR.
- POLE TO BE PRESSURE IMPREGNATED WITH CREOSOTE IN ACCORDANCE WITH BS EN 14229
- MINIMUM DIAMETERS
TOP - Ø206mm
BOTTOM - Ø430mm
- 19.5m LONG POLE TO BE SOURCED BY TRIMMING 20m LONG POLE BY 0.5m AT THE TOP

PLANTING

- CAT SCANNER IS TO BE USED IN ORDER TO CONFIRM THE POSITIONS OF BURIED SERVICES.
- TIMBER POLE TO BE PLANTED WITH N85 MARKING AT 3.5m FROM BUTT FACING 85° FROM NORTH (CLOCKWISE)
- SEE DRAWING 400 FOR FOUNDATION DETAILS

0cm 1cm 2cm 3cm 4cm 5cm 6cm 7cm 8cm 9cm 10cm

ALL SCALES AS SHOWN WHEN PRINTED AT A3

ALL SCALES AS SHOWN WHEN PRINTED AT A3

01	FIRST ISSUE			TT	20/06/19
REV	REV			BY	DATE
SCALE AS SHOWN WHEN PRINTED AT A3		DRAWN AM DATE 20/06/19	CHECKED MP DATE 20/06/19	APPROVED JBT DATE 20/06/19	
ALL DIMENSIONS IN mm UNLESS OTHERWISE STATED. THIS DRAWING TO BE READ IN CONJUNCTION WITH OTHER RELEVANT DRAWINGS.					

TITLE

FERRYSIDE

GENERAL ARRANGEMENT

SHEET 2 OF 3

SITE ADDRESS

TRI PEN HAD ROAD

DYFED

CARMARTHENSHIRE

SA17 5UR

ARQIVA REF.






140665

DRG No.

200

REV

01

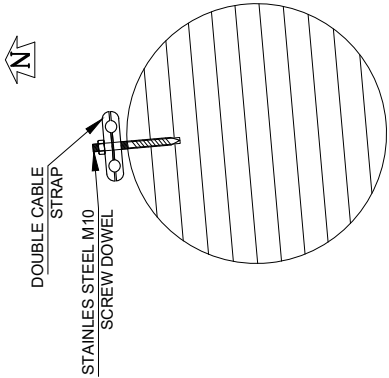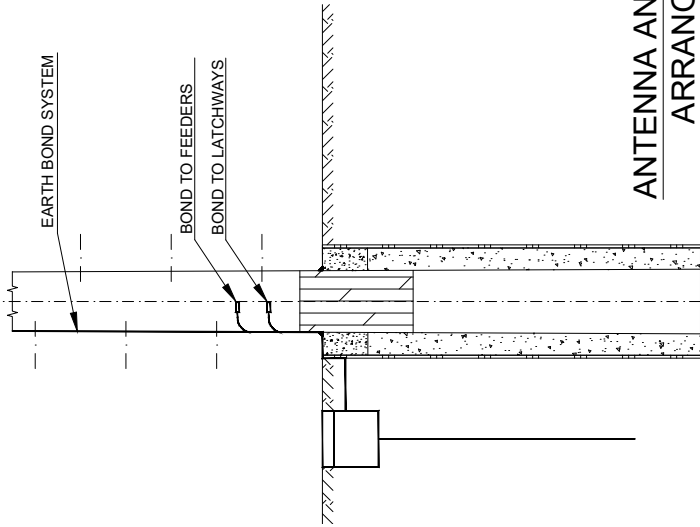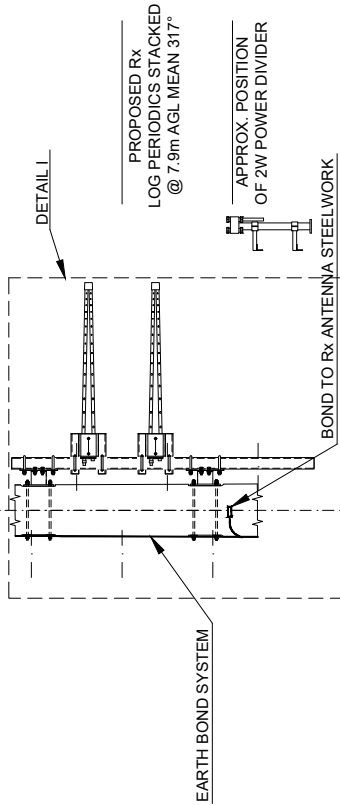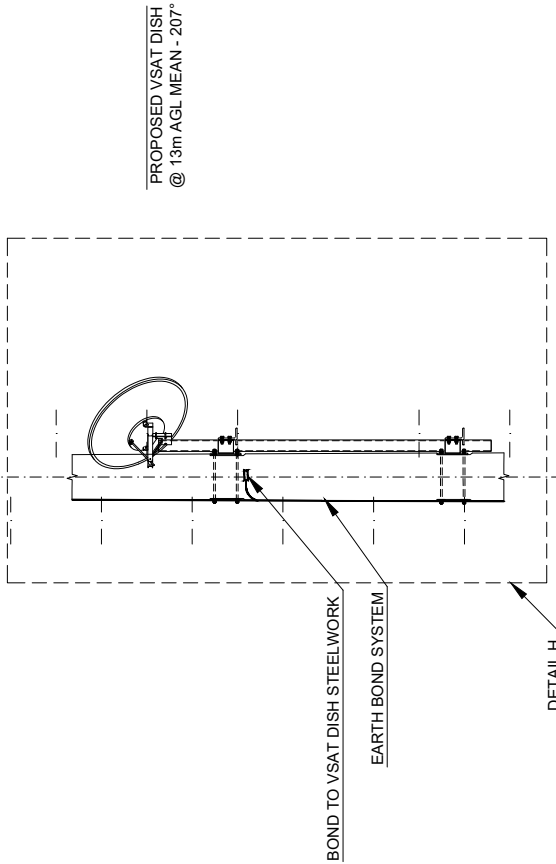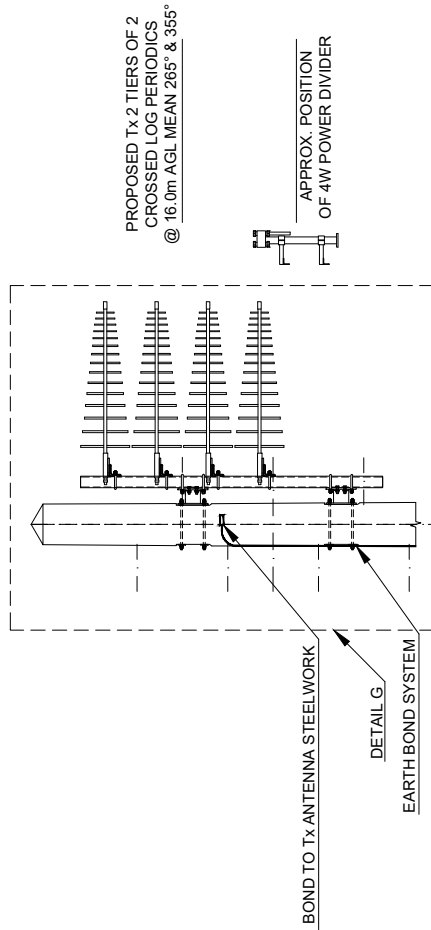

FEEDER
MANAGEMENT

Scale 1:10

NOTES

1. AS FAR AS IS PRACTICABLE ALL CUTTING SCARFING AND DRILLING TO BE
DONE BEFORE CREOSOTING. WHERE THIS IS NOT POSSIBLE ALL CUT,
DRILLED, AND SCARFED SURFACES TO BE COATED WITH A MIXTURE
OF CREOSOTE AND TAR

FEEDERS


1. SUPPLY OF FEEDERS BY OTHERS
LCF78-50 TO Tx ANTENNA &
LCF12-50 TO Rx ANTENNA
UNKNOWN TO VSAT DISH
(ARQIVA TO CONFIRM)
2. FEEDERS FIXED AT 1000mm CENTRES

EARTHING

1. CONNECT EARTH BOND TO NEW
EARTHING SYSTEM
2. MAXIMUM VALUE FOR GROUND
RESISTANCE TO BE 10 OHMS
3. CABLE OR TAPE TO BE FIXED TO POLE
AT 1000mm CENTRES
4. EARTHING SHOULD COMPLY WITH
ARQIVA'S DOCUMENT BOS147


ANTENNA AND EARTHING
ARRANGEMENT

Scale 1:50

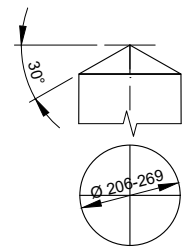


- NOTES:
1. A SINGLE COAT OF TIMBER COMPATIBLE BITUMINOUS PAINT (E.G. BIRD BRAND BLACK BITUMINOUS PAINT OR SIMILAR APPROVED PRODUCT) TO BE APPLIED TO THE UPPER SURFACES AT THE TOP OF THE POLE.
 2. PAINT TO BE APPLIED ON SITE JUST BEFORE ERECTION
- FORM: 4 WAY PYRAMID / CONE


DETAIL A - TIMBER POLE TOP
Scale 1:20

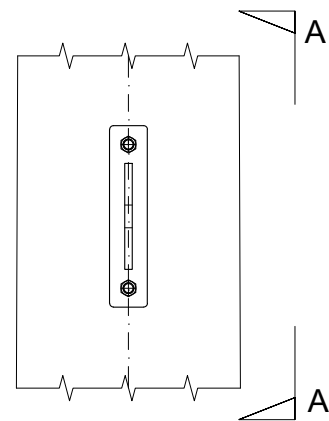


DETAIL C - FALL ARREST
ATTACHMENT POINT
Scale 1:10

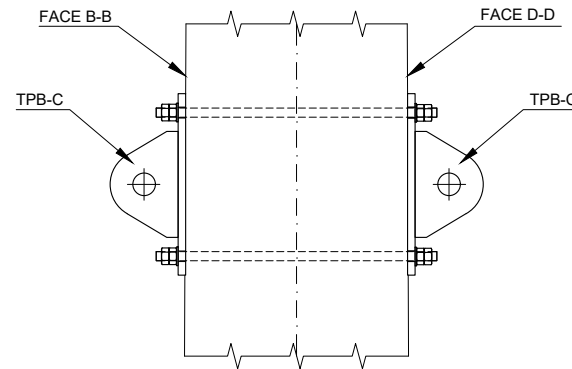


VIEW A-A
Scale 1:10

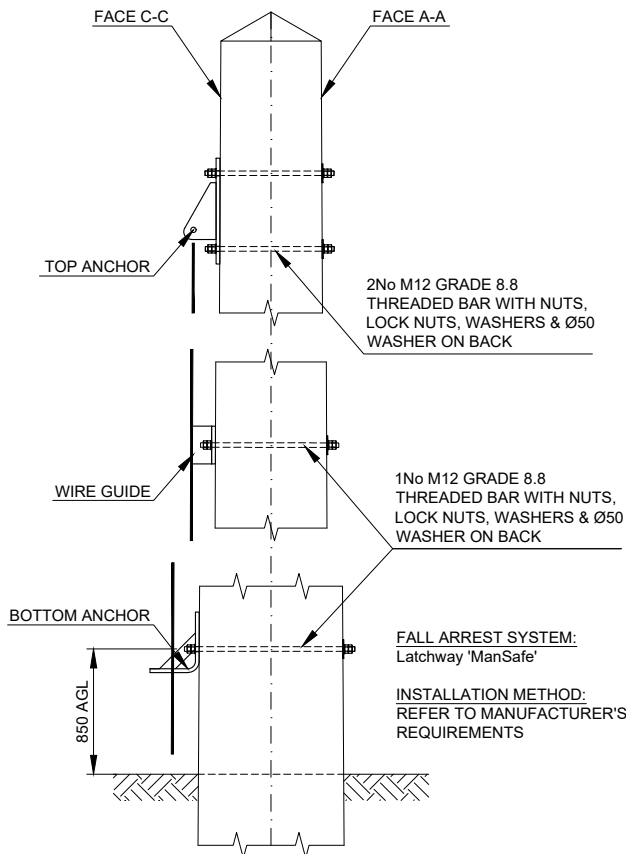

DETAIL B - FALL ARREST SYSTEM
Scale 1:20

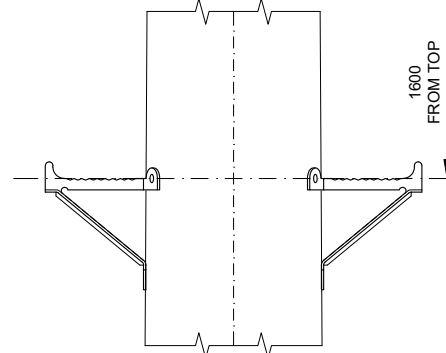


DETAIL D - ANTENNA
ACCESS CLIMBING STEP
Scale 1:10

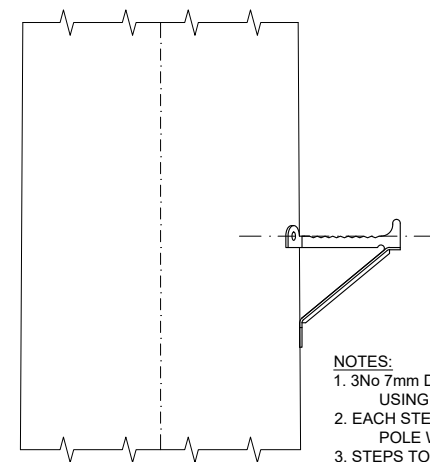


DETAIL E - PERMANENT
CLIMBING STEPS
Scale 1:10

- NOTES:
1. 3No 7mm DIA 70mm LONG PILOT HOLES TO BE DRILLED USING THE STEP AS A TEMPLATE
 2. EACH STEP SHOULD BE FIXED TO THE TIMBER POLE WITH 3No 10mm COACH SCREWS 75mm LONG
 3. STEPS TO BE INSTALLED ON FACES B-B & D-D ONLY

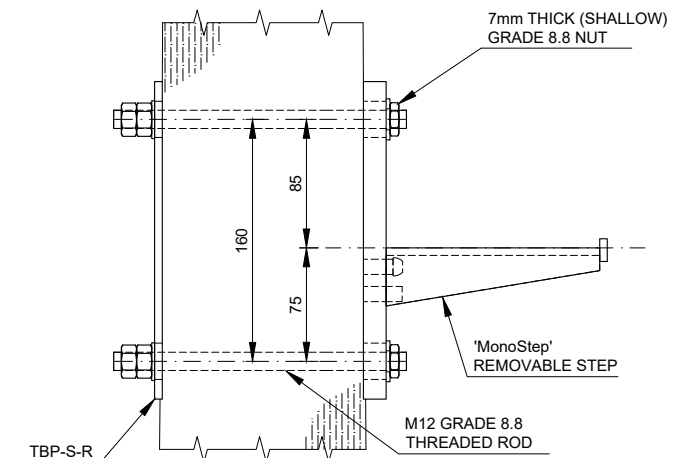

DETAIL F - REMOVABLE
CLIMBING STEPS
Scale 1:5

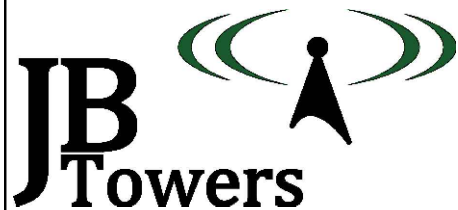

01	FIRST ISSUE	TT	20/06/19
REV	REV	BY	DATE
SCALE AS SHOWN WHEN PRINTED AT A3	DRAWN AM DATE 20/06/19	CHECKED MP DATE 20/06/19	APPROVED JBT DATE 20/06/19
ALL DIMENSIONS IN mm UNLESS OTHERWISE STATED. THIS DRAWING TO BE READ IN CONJUNCTION WITH OTHER RELEVANT DRAWINGS.			

TITLE
FERRYSIDE
GENERAL ARRANGEMENT
SHEET 3 OF 3


SITE ADDRESS
TRI PEN HAD ROAD
DYFED
CARMARTHENSHIRE
SA17 5UR

ARQIVA REF.
140665
DRG No.
200
REV
01

ALL SCALES AS SHOWN WHEN PRINTED AT A3



ALL SCALES AS SHOWN WHEN PRINTED AT A3

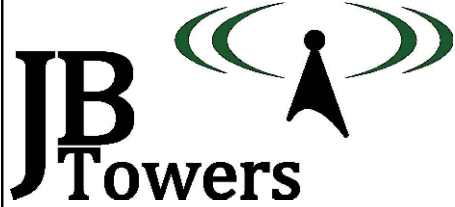

01	FIRST ISSUE			TT	20/06/19
REV	REV			BY	DATE
SCALE AS SHOWN WHEN PRINTED AT A3		DRAWN AM	CHECKED MP	APPROVED	JBT
		DATE 20/06/19	DATE 20/06/19	DATE 20/06/19	
ALL DIMENSIONS IN mm UNLESS OTHERWISE STATED. THIS DRAWING TO BE READ IN CONJUNCTION WITH OTHER RELEVANT DRAWINGS.					

TITLE

FERRYSIDE

TIMBER POLE HOLE SET OUT

SHEET 1 OF 2

SITE ADDRESS

TRI PEN HAD ROAD

DYFED

CARMARTHENSHIRE

SA17 5UR

ARQIVA REF.


140665

DRG No.

201

REV


01

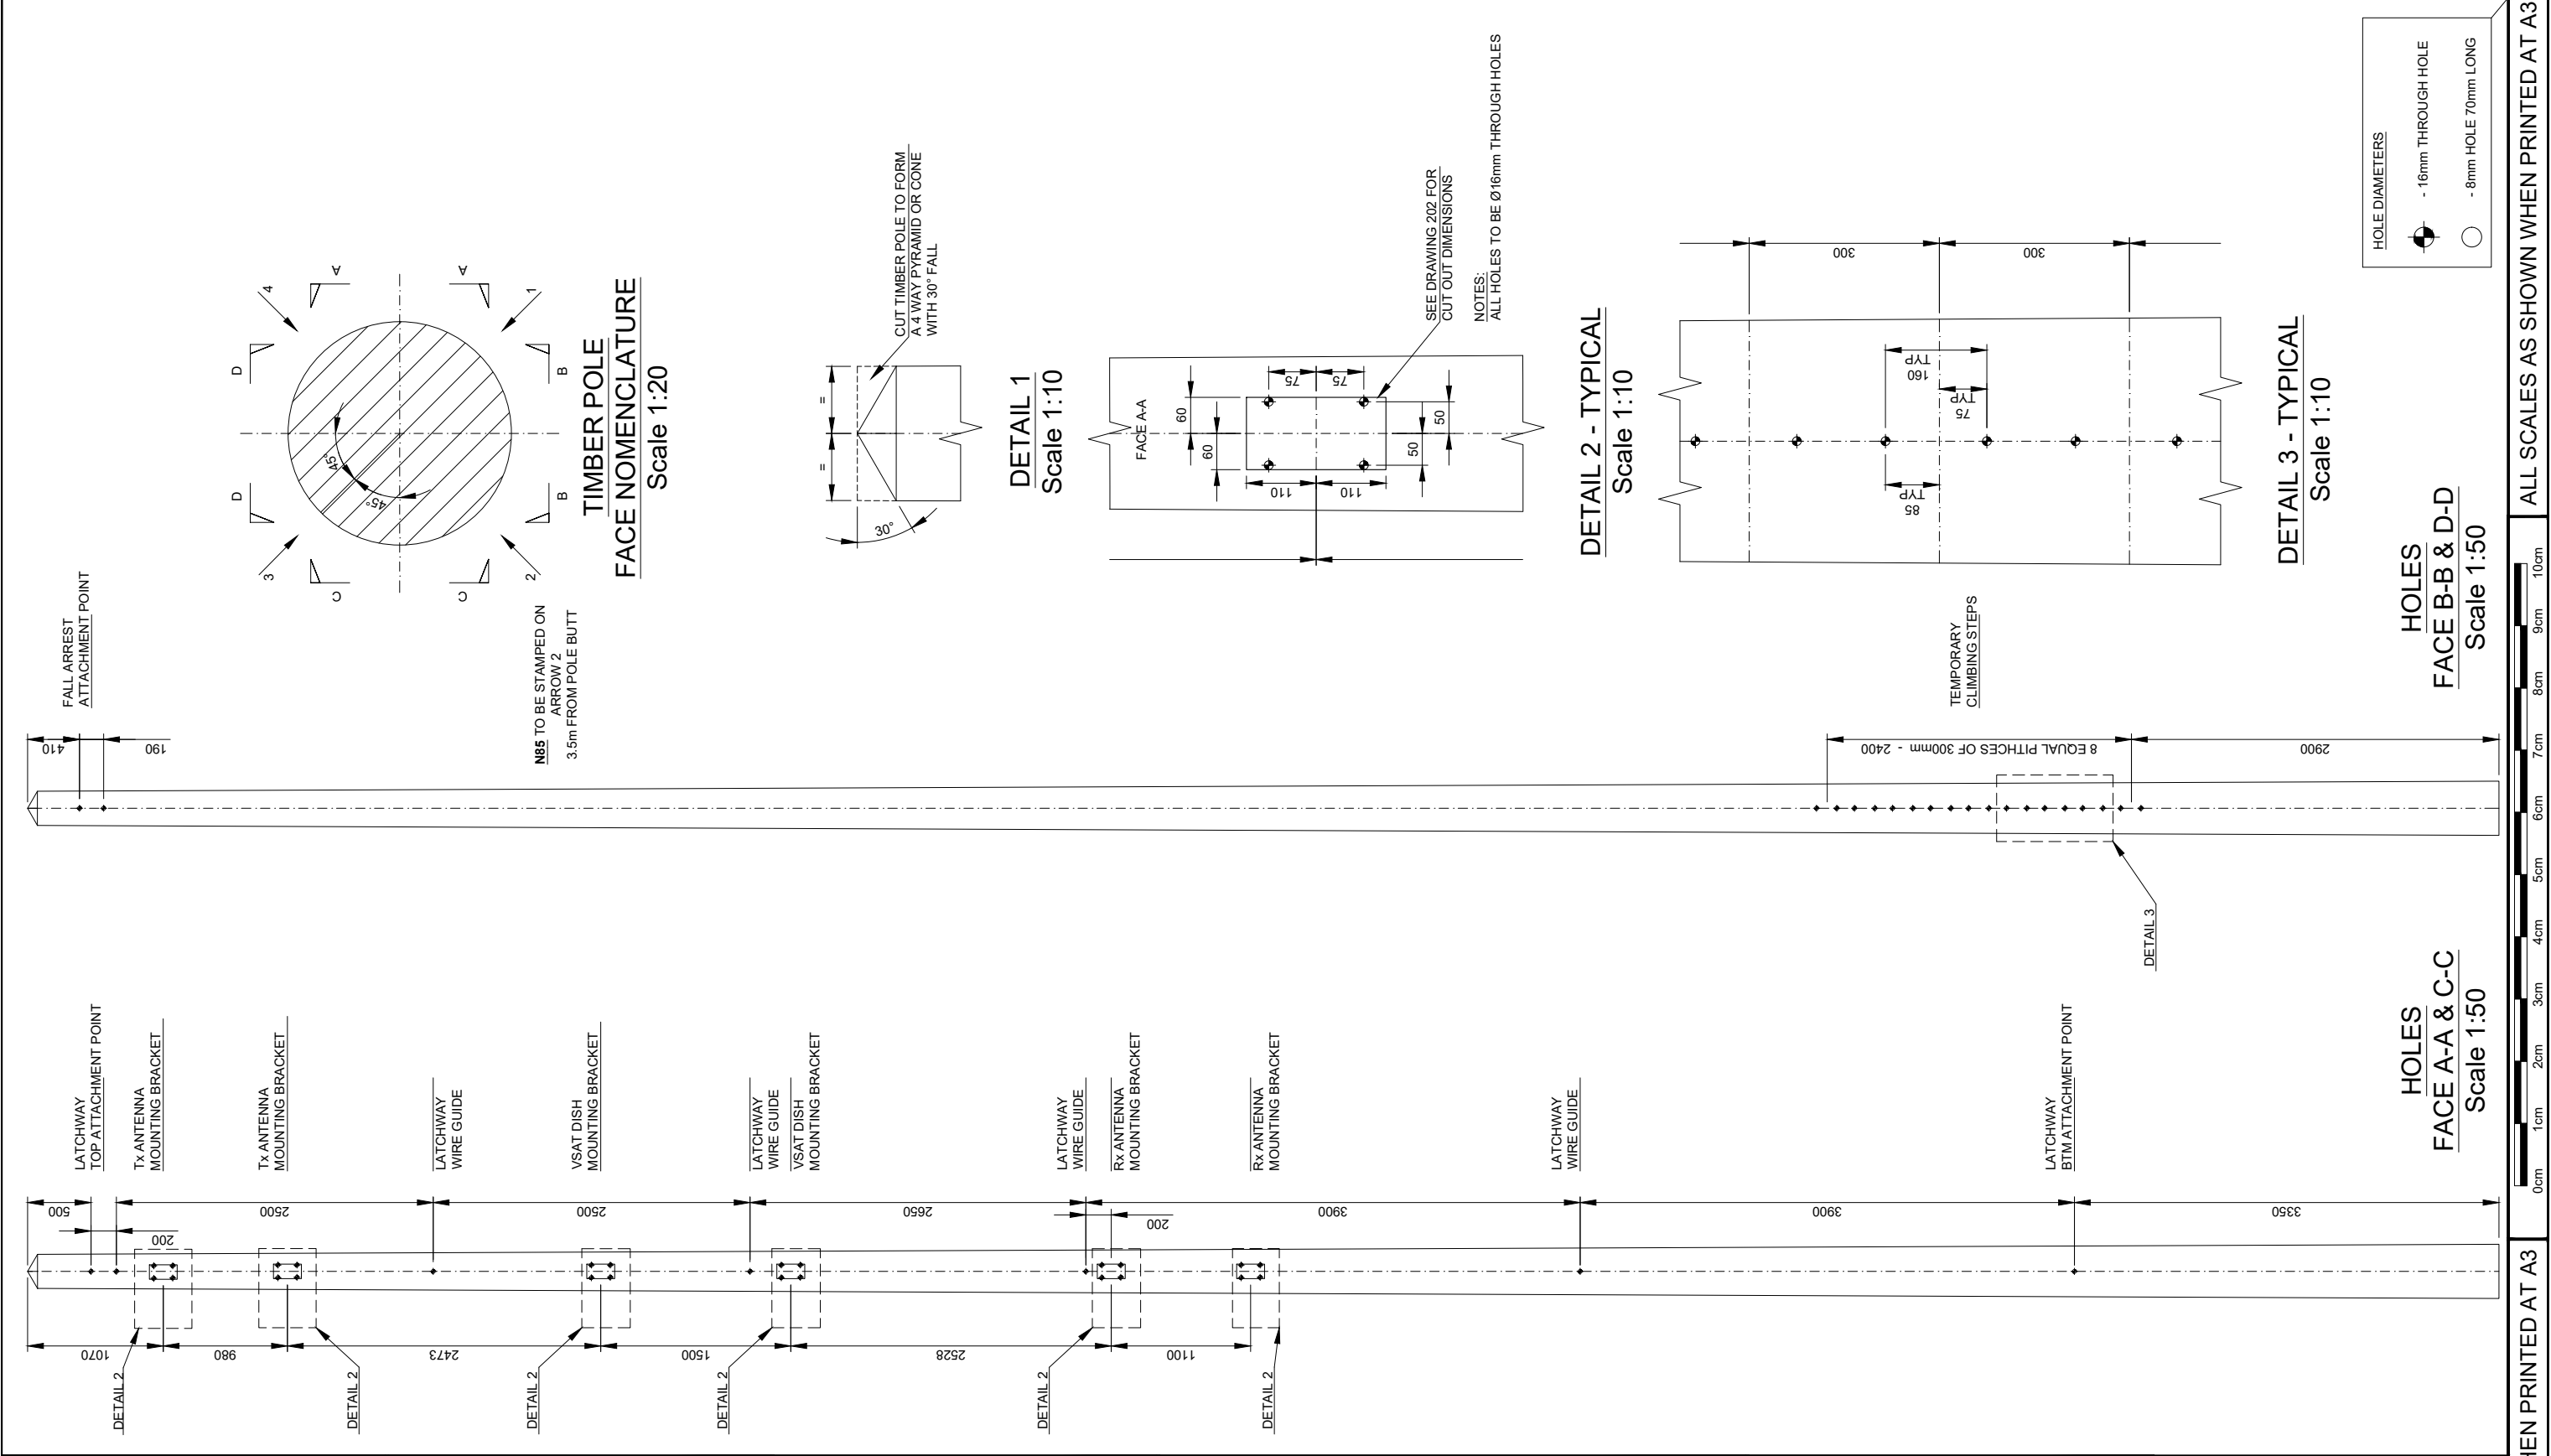

ALL SCALES AS SHOWN WHEN PRINTED AT A3



ALL SCALES AS SHOWN WHEN PRINTED AT A3

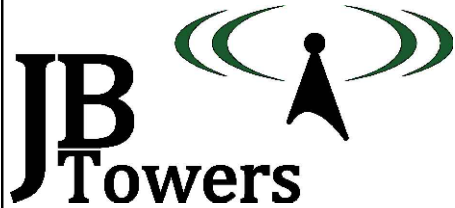

01	FIRST ISSUE			TT	20/06/19
REV	REV			BY	DATE
SCALE AS SHOWN		DRAWN	AM	CHECKED	MP
WHEN PRINTED AT A3		DATE	20/06/19	DATE	20/06/19
		APPROVED		JBT	
		DATE		20/06/19	
ALL DIMENSIONS IN mm UNLESS OTHERWISE STATED. THIS DRAWING TO BE READ IN CONJUNCTION WITH OTHER RELEVANT DRAWINGS.					

TITLE

FERRYSIDE

TIMBER POLE HOLE SET OUT

SHEET 2 OF 2

SITE ADDRESS

TRI PEN HAD ROAD

DYFED

CARMARTHENSHIRE

SA17 5UR

ARQIVA REF.



140665

DRG No.

201

REV

01

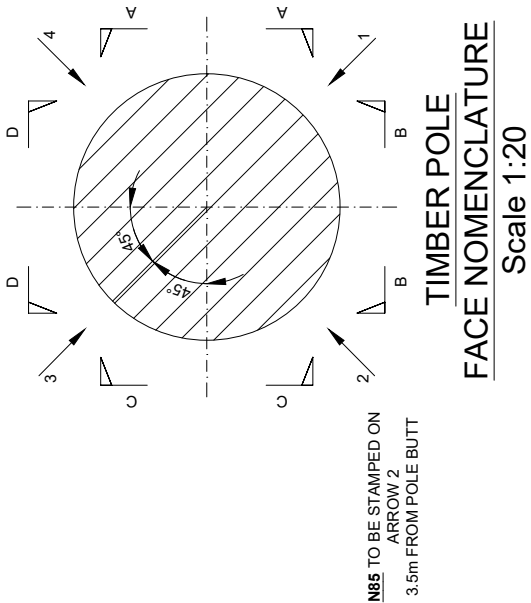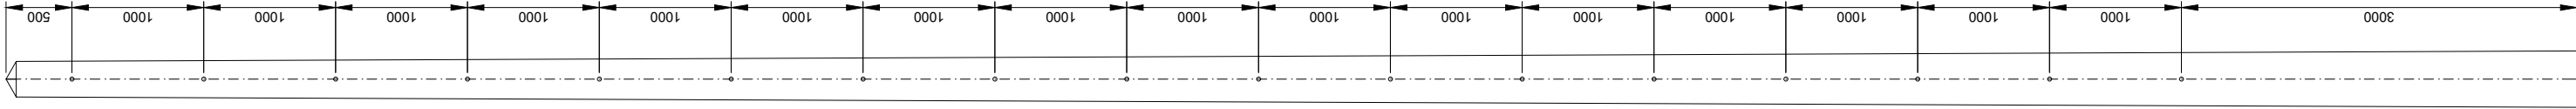

FEEDER BRACKETS

ALL HOLES ON ARROW 1
TO BE Ø8mm & 70mm LONG

HOLES
ARROW 1
Scale 1:50



ALL SCALES AS SHOWN WHEN PRINTED AT A3

ALL SCALES AS SHOWN WHEN PRINTED AT A3

01	FIRST ISSUE			TT	20/06/19
REV	REV			BY	DATE
SCALE AS SHOWN WHEN PRINTED AT A3		DRAWN AM DATE 20/06/19	CHECKED MP DATE 20/06/19	APPROVED JBT DATE 20/06/19	
ALL DIMENSIONS IN mm UNLESS OTHERWISE STATED. THIS DRAWING TO BE READ IN CONJUNCTION WITH OTHER RELEVANT DRAWINGS.					

TITLE


FERRYSIDE

TIMBER POLE CUT OUT
DETAIL

SITE ADDRESS

TRI PEN HAD ROAD
DYFED
CARMARTHENSHIRE
SA17 5UR

ARQIVA REF. 140665	DRG No. 202	REV 01
-----------------------	----------------	-----------

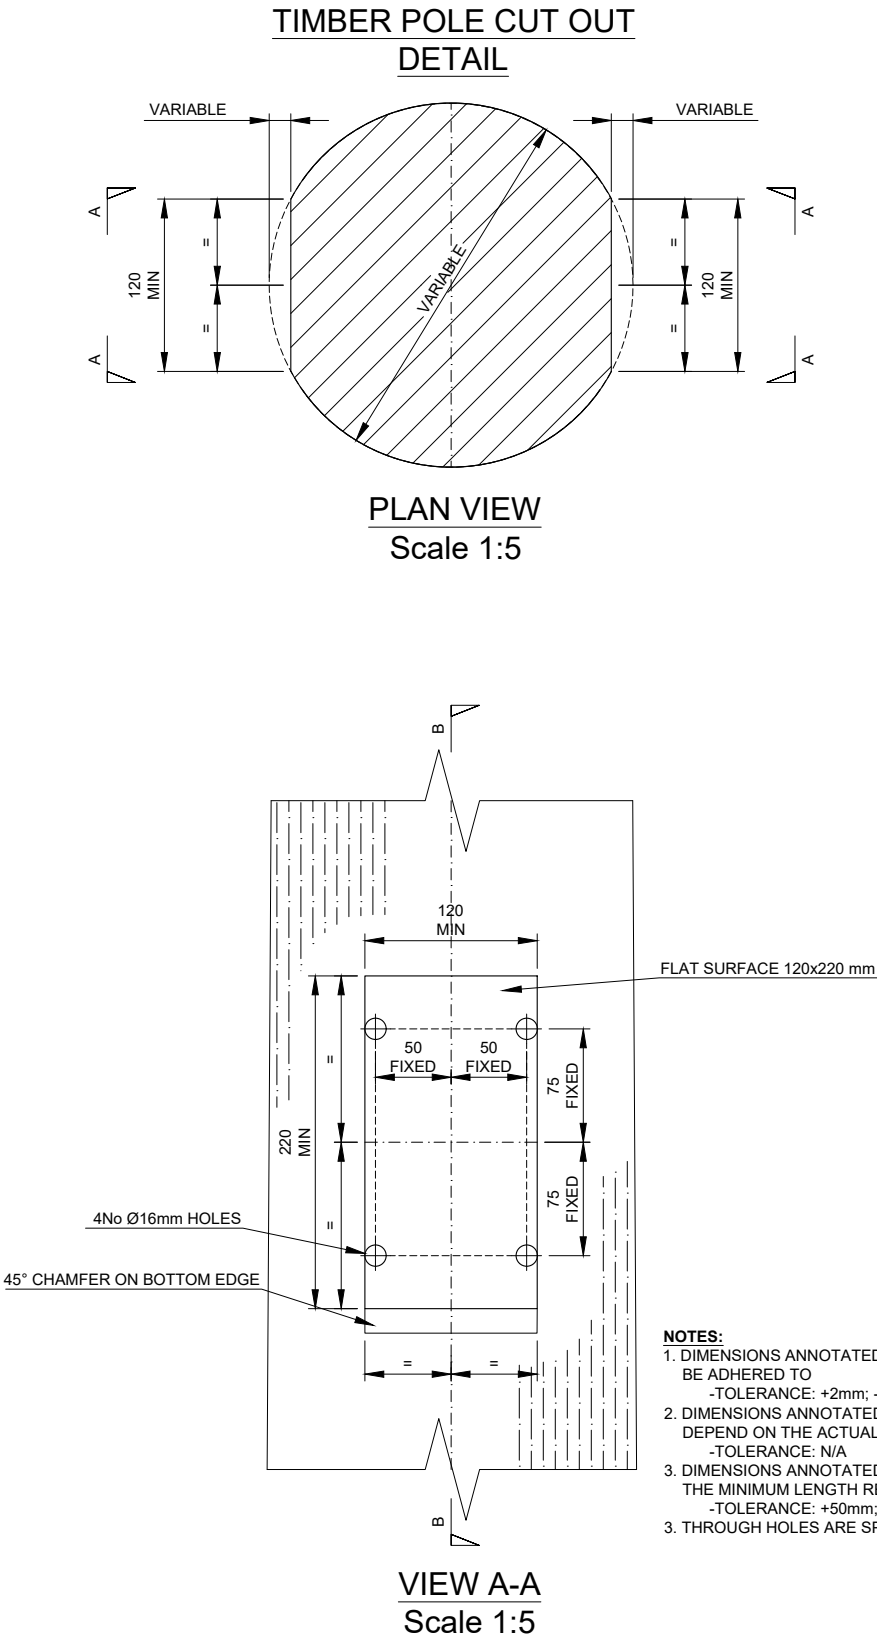

A

B

A

980

340

340

340

518

275

PACKS TO ALLOW
FOR TAPER

FACE C-C

FACE A-A

DETAIL G - Tx ANTENNA MOUNT

Scale 1:10

PROPOSED 2 TIER OF 2
CROSSED LOG PERIODIC
Tx ANTENNA @ 16.0m
MEAN 265° & 355°

VIEW A-A


Scale 1:20

VIEW A-A

Scale 1:20

VIEW B-B

Scale 1:20

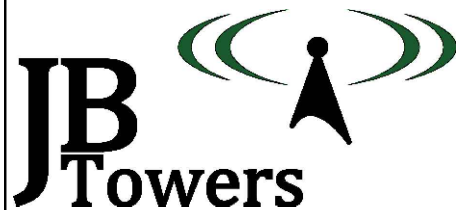APPROXIMATE
POSITION
OF 4W POWER
DIVIDER

arqiva

01	FIRST ISSUE	TT	20/06/19
REV	REV	BY	DATE
SCALE AS SHOWN WHEN PRINTED AT A3	DRAWN AM DATE 20/06/19	CHECKED MP DATE 20/06/19	APPROVED JBT DATE 20/06/19
ALL DIMENSIONS IN mm UNLESS OTHERWISE STATED. THIS DRAWING TO BE READ IN CONJUNCTION WITH OTHER RELEVANT DRAWINGS.			

TITLE

Tx ANTENNA MOUNT

DETAIL G


SITE ADDRESS

TRI PEN HAD ROAD
DYFED
CARMARTHENSHIRE
SA17 5URARQIVA REF.
140665DRG No.
203REV
01

ALL SCALES AS SHOWN WHEN PRINTED AT A3





ALL SCALES AS SHOWN WHEN PRINTED AT A3

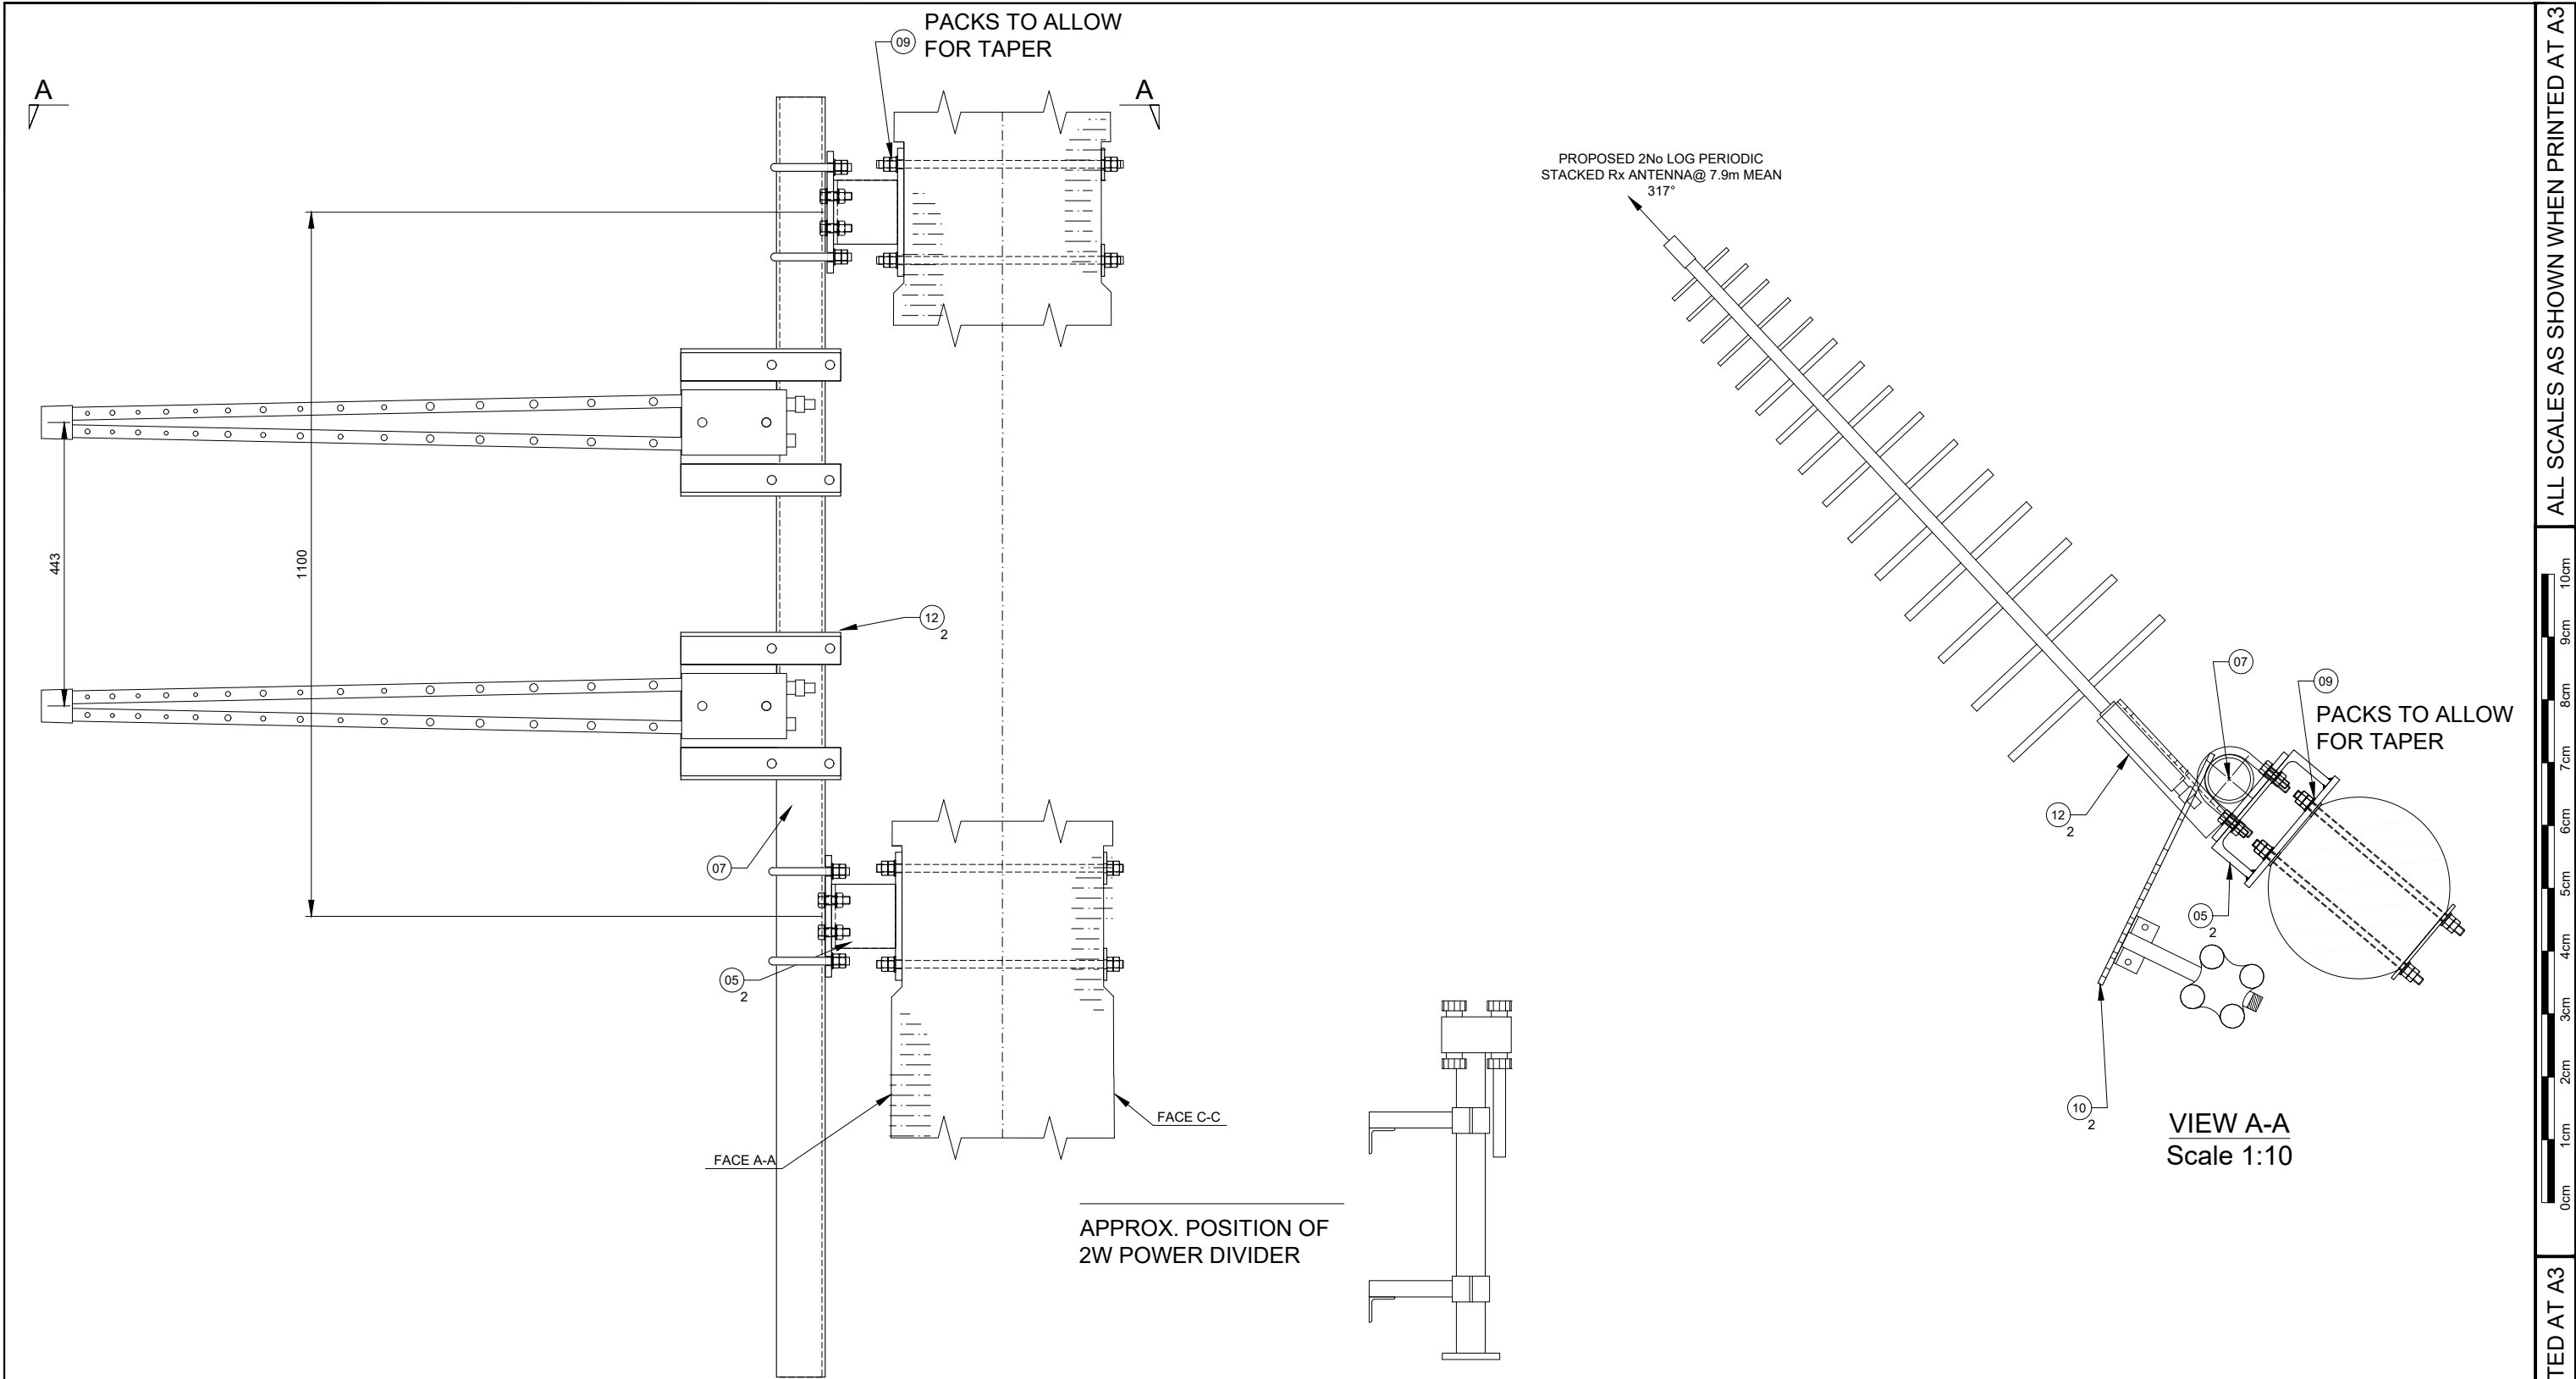

DETAIL I - Rx ANTENNA MOUNT
Scale 1:10

	
--	--	


ALL SCALES AS SHOWN WHEN PRINTED AT A3

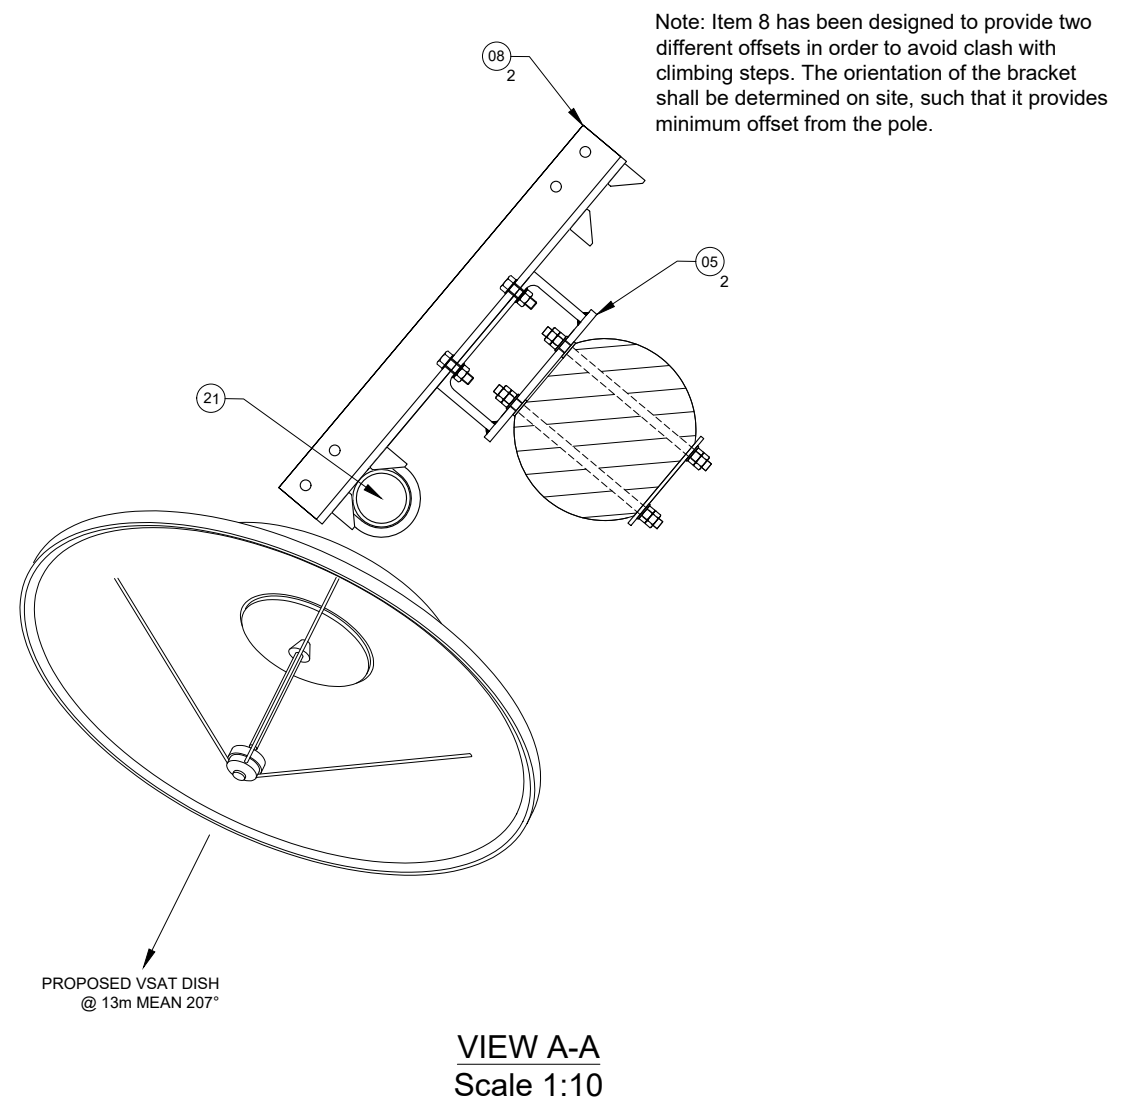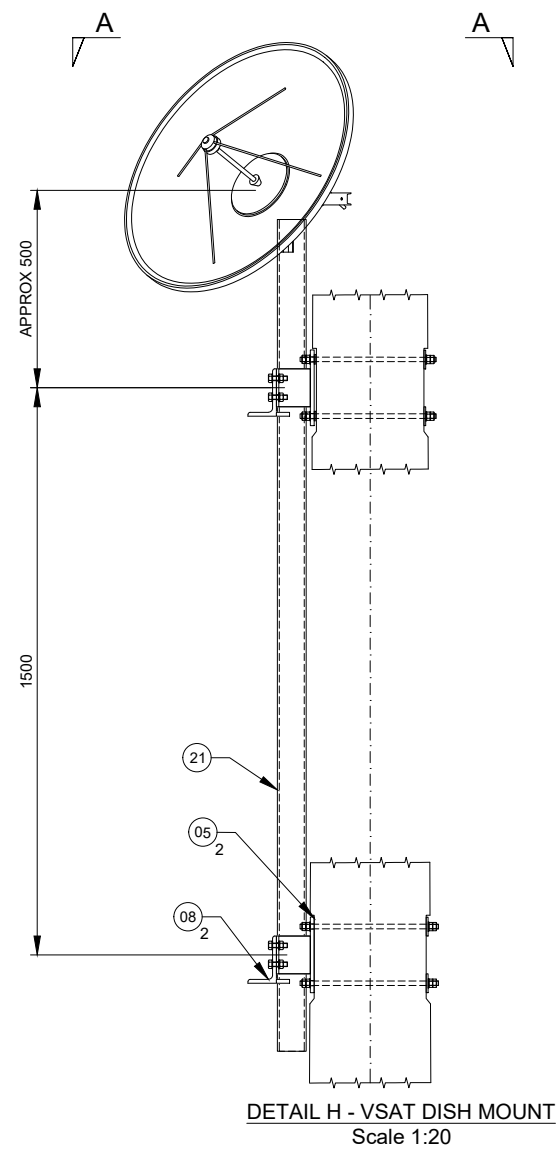

ALL SCALES AS SHOWN WHEN PRINTED AT A3




ALL SCALES AS SHOWN WHEN PRINTED AT A3

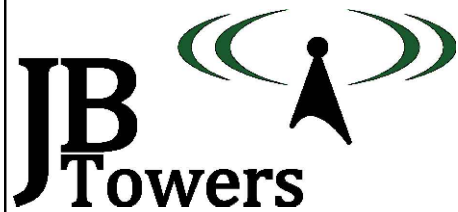


01	FIRST ISSUE			TT	20/06/19
REV	REV			BY	DATE
SCALE AS SHOWN WHEN PRINTED AT A3		DRAWN AM DATE 20/06/19	CHECKED MP DATE 20/06/19	APPROVED JBT DATE 20/06/19	
ALL DIMENSIONS IN mm UNLESS OTHERWISE STATED. THIS DRAWING TO BE READ IN CONJUNCTION WITH OTHER RELEVANT DRAWINGS.					

TITLE
VSAT DISH MOUNT
DETAIL H

SITE ADDRESS		
TRI PEN HAD ROAD DYFED CARMARTHENSHIRE SA17 5UR		
ARQIVA REF. 140665	DRG No. 205	REV 01

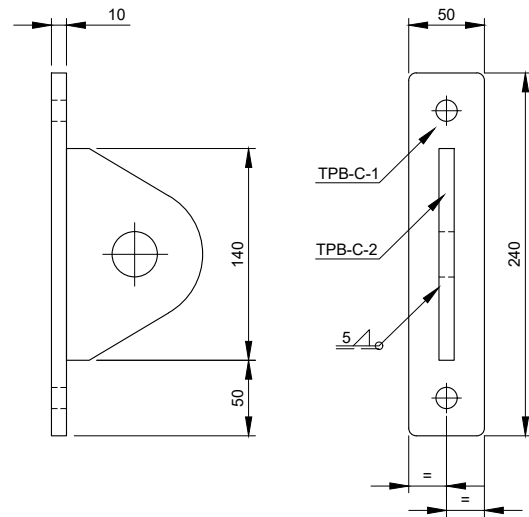

PART TPB-C
Scale 1:5

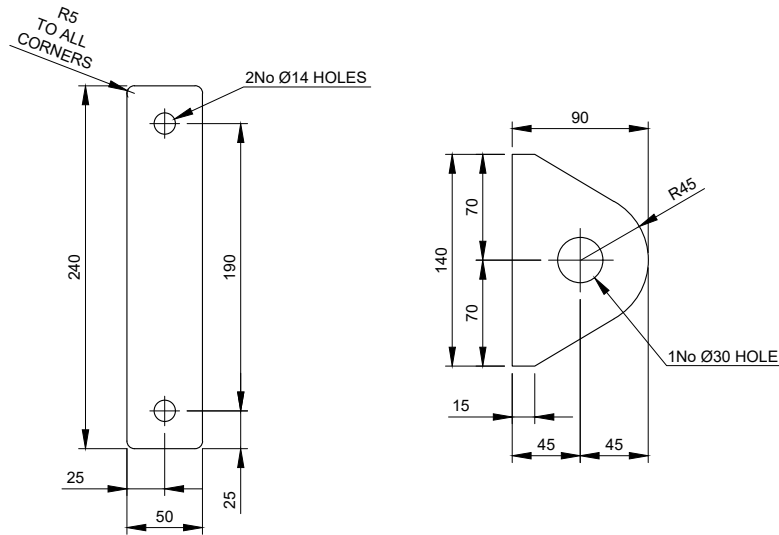


TPB-C-1 - 10mm THICK
Scale 1:5

TPB-C-2 - 10mm THICK
Scale 1:5


Parts list for TPB-C

Item	Part	Quantity	Part description	Length	Material	Weight
01	TPB-C-1	1	Plate 240x50x10mm	N/A	S275J0	0.94 kg
02	TPB-C-2	1	Plate 140x90x10mm	N/A	S275J0	0.99 kg
03	STUDS	1	M12 STUDDING	350mm	GRADE 8.8	0.31 kg
Total Weight:						2.24 kg

- All steel hot dip galvanized
- Each STUD to be supplied with 4 Full Nuts, 2 Flat Washers and 2 Spring Washers
- For fabrication notes see drawing 305

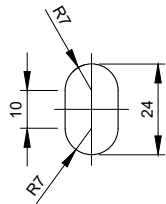

SLOTTED HOLE DETAIL
Scale 1:2

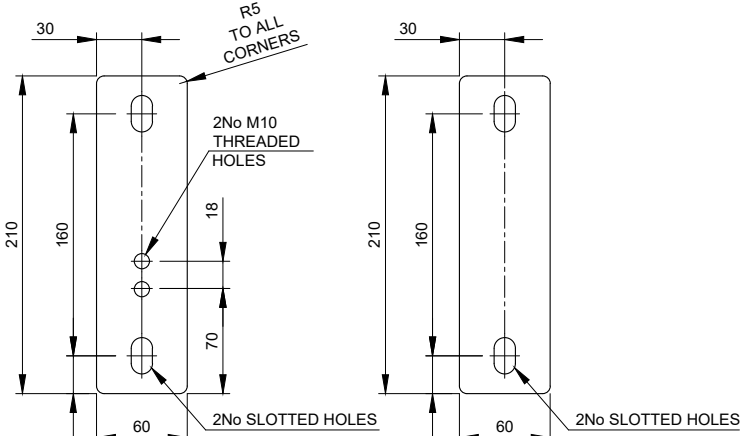


PART TPS-R-1
Scale 1:5

PART TPS-R-2
Scale 1:5

Parts list for TPS-R

Item	Part	Quantity	Part description	Length	Material	Weight
01	TPS-R-1	1	Plate 210x60x15mm	N/A	S275J0	1.48 kg
02	TPS-R-2	1	Plate 210x60x5mm	N/A	S275J0	0.49 kg
03	STUDS	2	M12 STUDDING	500mm	GRADE 8.8	0.44 kg
04	NUT-S	2	M12 SHALLOW NUT	N/A	GRADE 8.8	-
05	NUT	4	M12 NUT	N/A	GRADE 8.8	-
06	WSH	4	M12 WASHER	N/A	GRADE 8.8	-
Total Weight:						2.41 kg

- All steel hot dip galvanized
- For fabrication notes see drawing 305

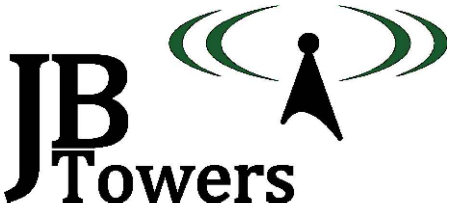

01	FIRST ISSUE	TT	20/06/19
REV	REV	BY	DATE
SCALE AS SHOWN WHEN PRINTED AT A3	DRAWN AM DATE 20/06/19	CHECKED MP DATE 20/06/19	APPROVED JBT DATE 20/06/19
ALL DIMENSIONS IN mm UNLESS OTHERWISE STATED. THIS DRAWING TO BE READ IN CONJUNCTION WITH OTHER RELEVANT DRAWINGS.			

TITLE

ATTACHMENT POINT &
TEMPORARY STEP DETAILS

PARTS: TPB-C; TPS-R

SITE ADDRESS

TRI PEN HAD ROAD
DYFED
CARMARTHENSHIRE
SA17 5UR

ARQIVA REF.
140665



DRG No.
300

REV
01


ALL SCALES AS SHOWN WHEN PRINTED AT A3




ALL SCALES AS SHOWN WHEN PRINTED AT A3

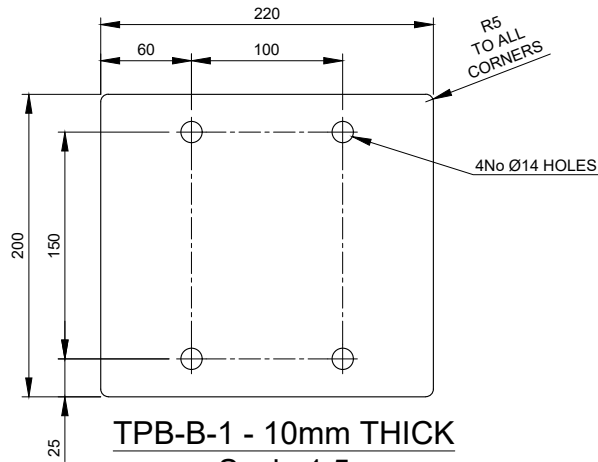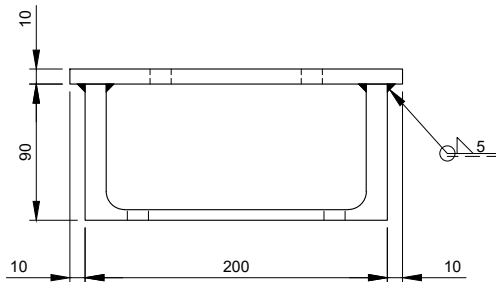


TPB-B-1 - 10mm THICK
Scale 1:5

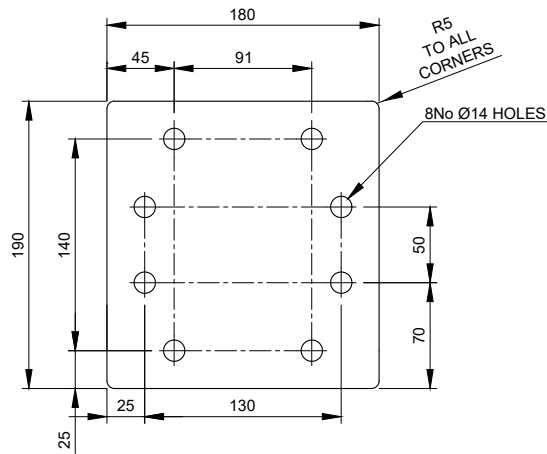


TPB-B-5 - 10mm THICK
Scale 1:5

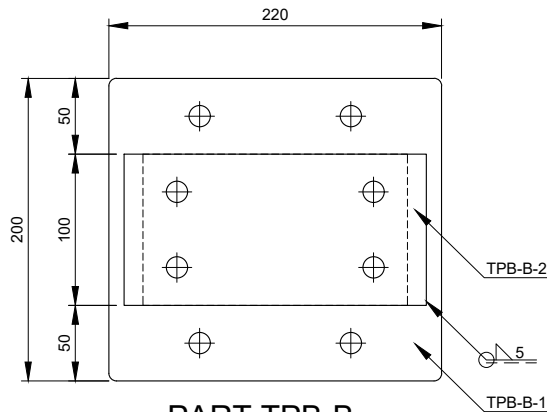


PART TPB-B
Scale 1:5

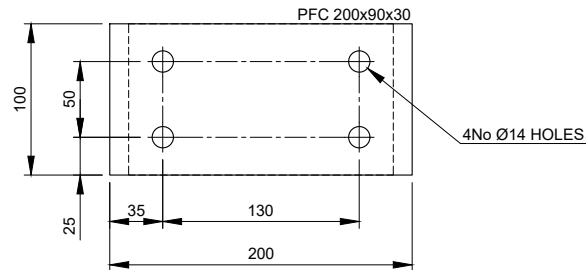

TPB-B-2 - PFC 200x90x30
Scale 1:5

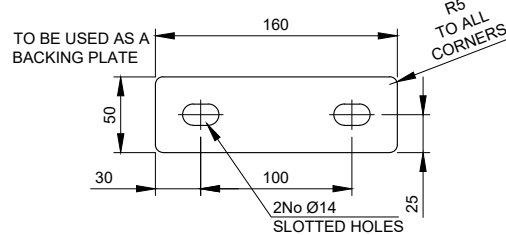

TPB-B-4 - 5mm THICK
Scale 1:5

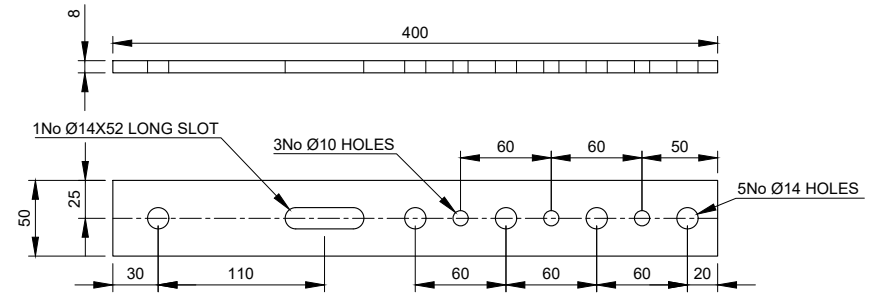


TPA-PD - 8mm THICK
Scale 1:5

Parts list for TPB-B

Item	Part	Quantity	Part description	Length	Material	Weight
01	TPB-B-1	1	Plate 220x200x10mm	N/A	S275J0	3.45 kg
02	TPB-B-2	1	PFC 200x90x30	100mm	S275J0	3.00 kg
03	TPB-B-4	2	Plate 160x50x5mm	N/A	S275J0	0.31 kg
04	TPB-B-5	1	Plate 190x180x10mm	N/A	S275J0	2.70 kg
05	STUDS	4	M12 STUDDING	400mm	GRADE 8.8	0.35 kg
06	BOLT	4	M12 45mm LONG (2D+6)	45mm	GRADE 8.8	-
07	U-BOLT	2	M12 U-BOLT FOR CHS 76.1	N/A	GRADE 8.8	-
Total Weight:						11.17 kg

- All steel hot dip galvanized
- Each STUD & U-BOLT to be supplied with 4 Full Nuts, 2 Flat Washers and 2 Spring Washers
- Each BOLT to be supplied with 1 Full Nut, 1 Form E Flat Washer and 1 Spring Washer
- For fabrication notes see drawing 305

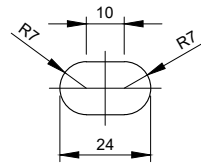


SLOTTED HOLE DETAIL
Scale 1:2

Parts list for TPA-PD

Item	Part	Quantity	Part description	Length	Material	Weight
01	TPA-PD	1	Plate 400x50x8mm	N/A	S275J0	1.26 kg
02	U-BOLT	1	M12 U-BOLT FOR CHS 76.1mm	N/A	GRADE 8.8	-
Total Weight:						1.26 kg

- All steel hot dip galvanized
- Each U-BOLT to be supplied with 4 Full Nuts, 2 Flat Washers and 2 Spring Washers
- For fabrication notes see drawing 305

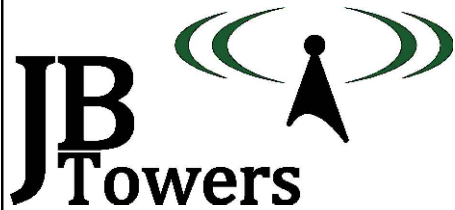

01	FIRST ISSUE	TT	20/06/19
REV	REV	BY	DATE
SCALE AS SHOWN WHEN PRINTED AT A3	DRAWN AM DATE 20/06/19	CHECKED MP DATE 20/06/19	APPROVED JBT DATE 20/06/19
ALL DIMENSIONS IN mm UNLESS OTHERWISE STATED. THIS DRAWING TO BE READ IN CONJUNCTION WITH OTHER RELEVANT DRAWINGS.			

TITLE
STEELWORK BRACKET,
POWER DIVIDER STRAP
PART: TPB-B & TPA-PD


SITE ADDRESS
TRI PEN HAD ROAD
DYFED
CARMARTHENSHIRE
SA17 5UR

ARQIVA REF.
140665
DRG No.
301
REV
01



ALL SCALES AS SHOWN WHEN PRINTED AT A3



ALL SCALES AS SHOWN WHEN PRINTED AT A3

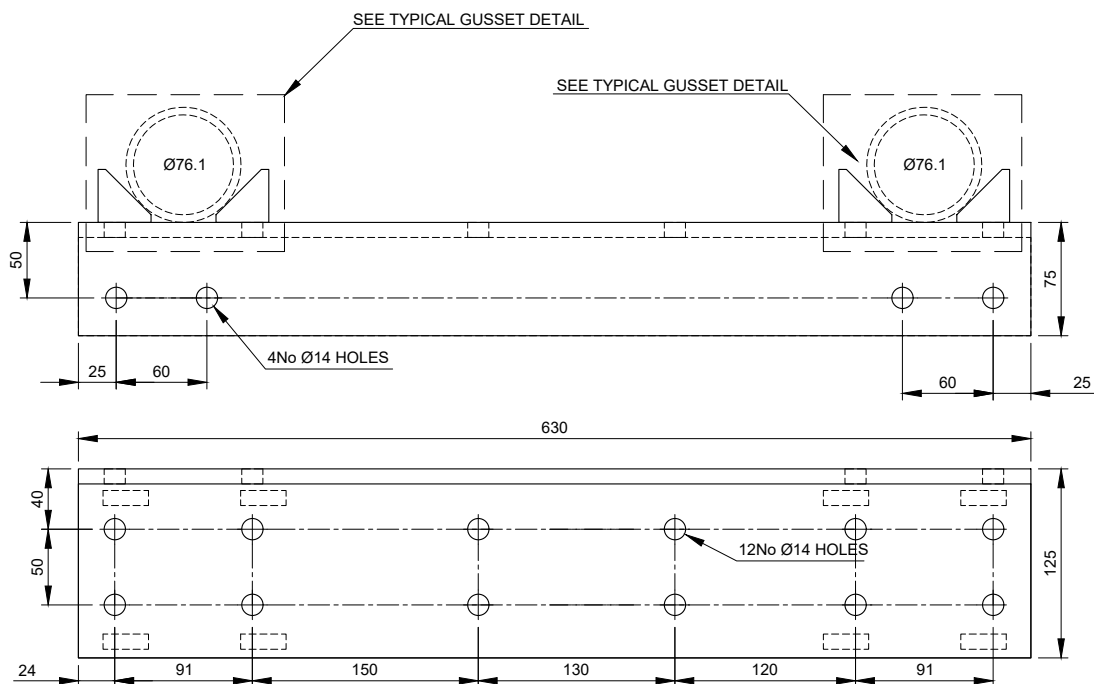

TPA-M - UA125x75x10
Scale 1:5

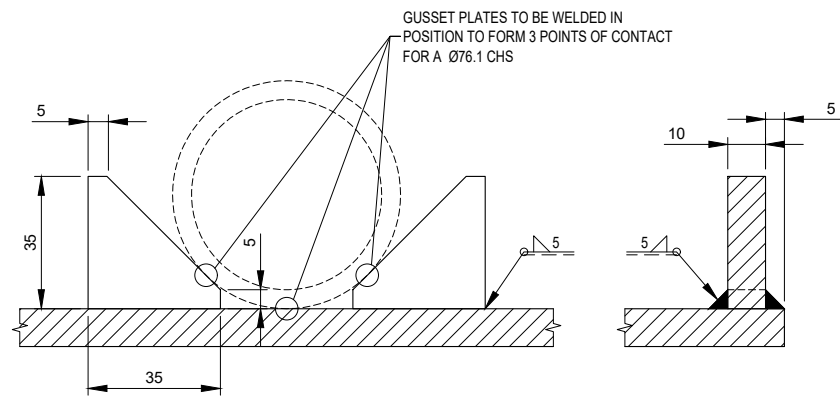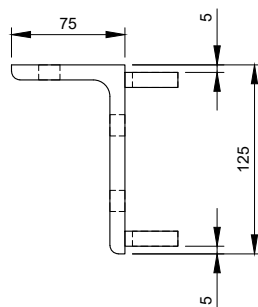


TYPICAL GUSSET PLATE DETAIL
Scale 1:2

Parts list for TPA-M

Item	Part	Quantity	Part description	Length	Material	Weight
01	TPA-M	1	UA125x75x10 C/W GUSSETS	630mm	S275J0	9.45 kg
02	U-BOLT	2	M12 U-BOLT FOR CHS 76.1mm	N/A	GRADE 8.8	-
03	BOLT	4	M12x45 (2D+6) BOLT	N/A	GRADE 8.8	-
Total Weight:						9.45 kg

- All steel hot dip galvanized
- Each STUD & U-BOLT to be supplied with 4 Full Nuts, 2 Flat Washers and 2 Spring Washers
- Each BOLT to be supplied with 1 Full Nut, 1 Form E FLat Washer and 1 Spring Washer
- For fabrication notes see drawing 305

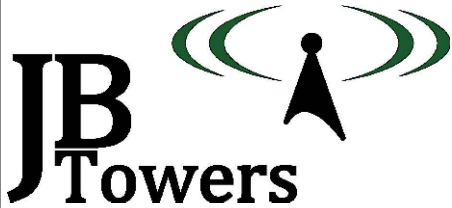

01	FIRST ISSUE	TT	20/06/19
REV	REV	BY	DATE
SCALE AS SHOWN WHEN PRINTED AT A3	DRAWN AM DATE 20/06/19	CHECKED MP DATE 20/06/19	APPROVED JBT DATE 20/06/19
ALL DIMENSIONS IN mm UNLESS OTHERWISE STATED. THIS DRAWING TO BE READ IN CONJUNCTION WITH OTHER RELEVANT DRAWINGS.			

TITLE
VSAT DISH MOUNTING
BRACKET

PARTS: TPA-M


SITE ADDRESS
TRI PEN HAD ROAD
DYFED
CARMARTHENSHIRE
SA17 5UR

ARQIVA REF.
140665
DRG No.
302
REV
01


ALL SCALES AS SHOWN WHEN PRINTED AT A3





ALL SCALES AS SHOWN WHEN PRINTED AT A3

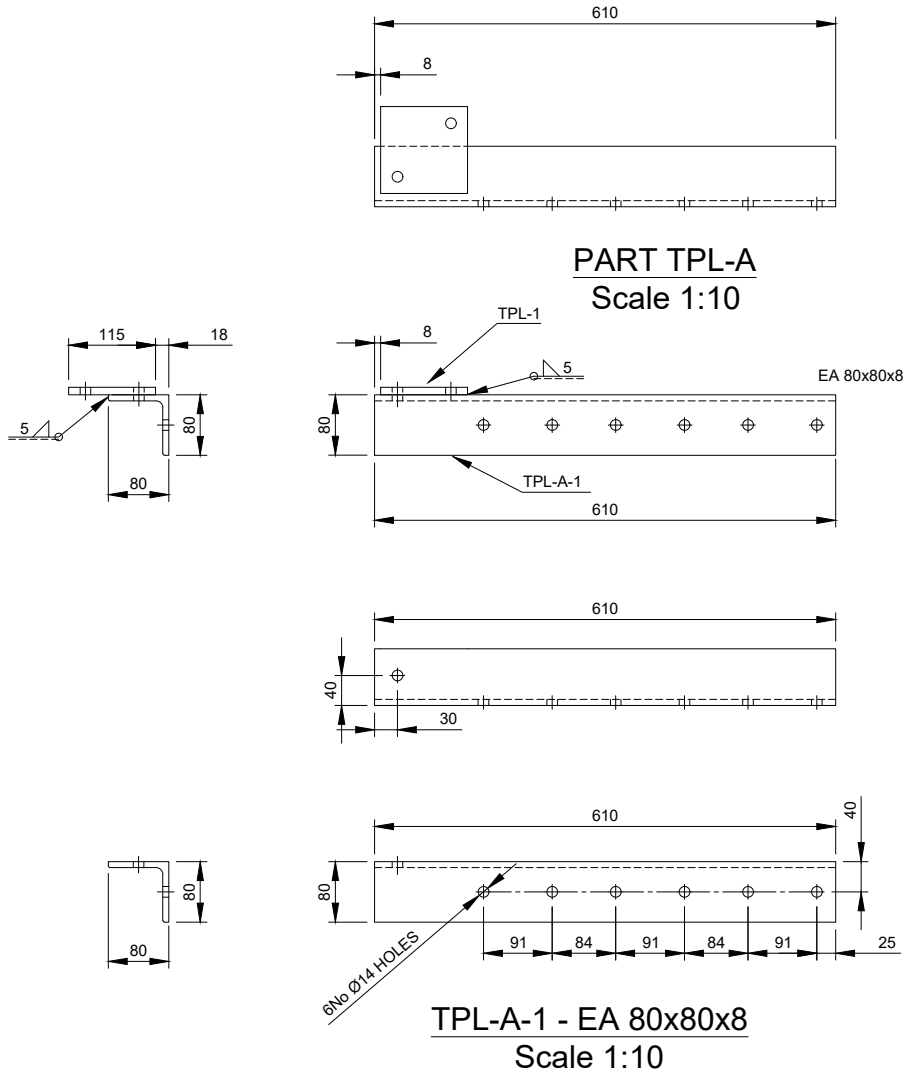

Parts list for TPL-A						
Item	Part	Quantity	Part description	Length	Material	Weight
01	TPL-A-1	1	EA 80x80x8	610mm	S275J0	5.87 kg
02	TPL-1	1	Plate 115x115x10mm	N/A	S275J0	1.04 kg
03	U-BOLT	3	M12 U-BOLT FOR CHS 76.1mm	N/A	GRADE 8.8	-
Total Weight:						6.91 kg
- All steel hot dip galvanized						
- Each U-BOLT to be supplied with 4 Full Nuts, 2 Flat Washers and 2 Spring Washers						
- For fabrication notes see drawing 305						

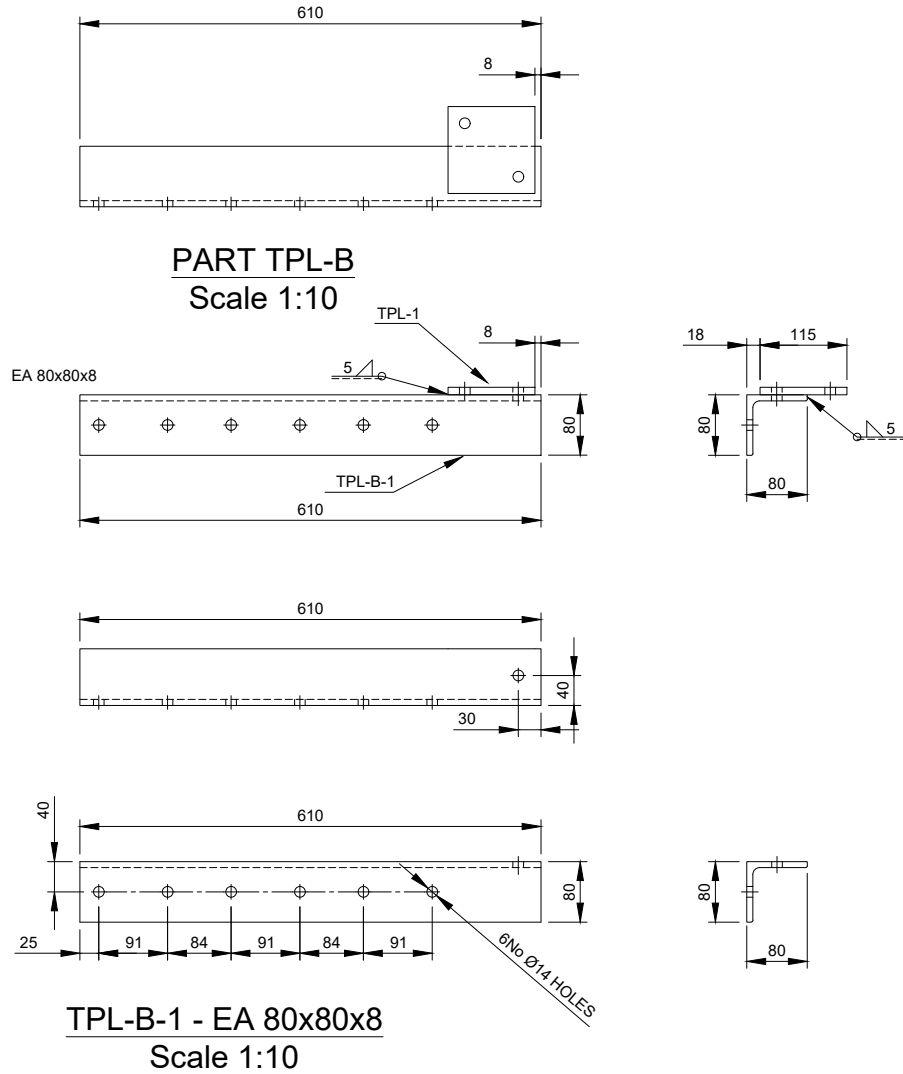

Parts list for TPL-B						
Item	Part	Quantity	Part description	Length	Material	Weight
01	TPL-B-1	1	EA 80x80x8	610mm	S275J0	5.87 kg
02	TPL-1	1	Plate 115x115x10mm	N/A	S275J0	1.04 kg
03	U-BOLT	3	M12 U-BOLT FOR CHS 76.1mm	N/A	GRADE 8.8	-
Total Weight:						6.91 kg
- All steel hot dip galvanized						
- Each U-BOLT to be supplied with 4 Full Nuts, 2 Flat Washers and 2 Spring Washers						
- For fabrication notes see drawing 305						

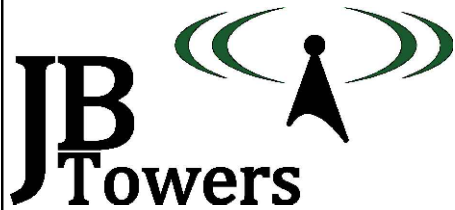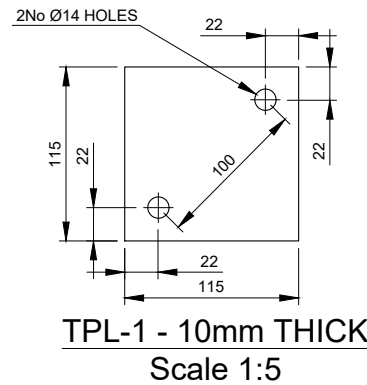

01	FIRST ISSUE	TT	20/06/19
REV	REV	BY	DATE
SCALE AS SHOWN	DRAWN	AM	CHECKED
WHEN PRINTED AT A3	DATE	20/06/19	DATE
ALL DIMENSIONS IN mm UNLESS OTHERWISE STATED.			
THIS DRAWING TO BE READ IN CONJUNCTION WITH			
OTHER RELEVANT DRAWINGS.			

TITLE

LOG MOUNTS

PARTS: TPL-A; TPL-B

SITE ADDRESS

TRI PEN HAD ROAD

DYFED

CARMARTHENSHIRE

SA17 5UR

ARQIVA REF.

140665

DRG No.

303


REV

01

ALL SCALES AS SHOWN WHEN PRINTED AT A3




ALL SCALES AS SHOWN WHEN PRINTED AT A3

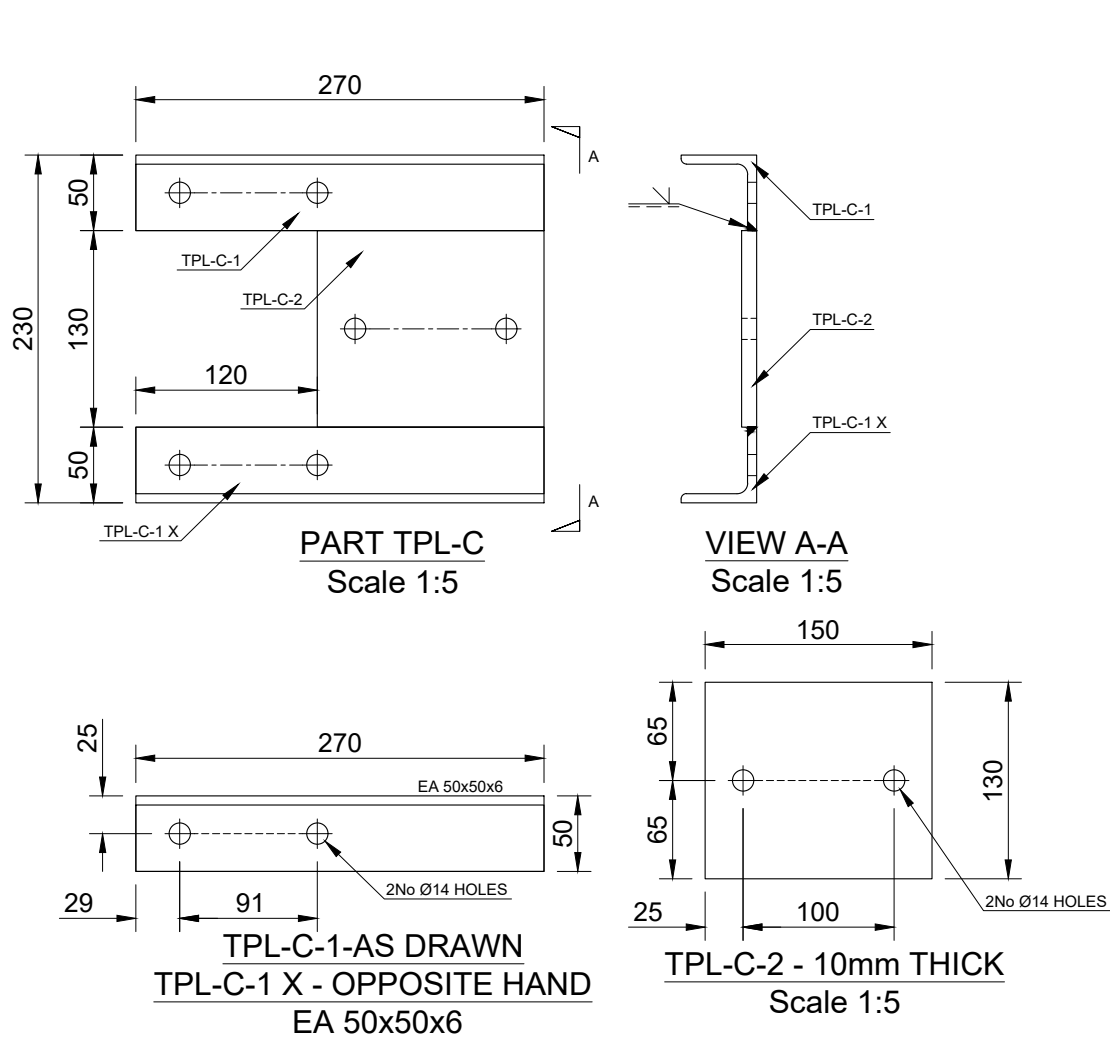

Parts list for TPL-C

Item	Part	Quantity	Part description	Length	Material	Weight
01	TPL-C-1	1	EA 50x50x6	270mm	S275J0	1.21 kg
02	TPL-C-1 X	1	EA 50x50x6	270mm	S275J0	1.21 kg
03	TPL-C-2	1	Plate 150x130x10mm	N/A	S275J0	1.53 kg
04	U-BOLT	2	M12 U-BOLT FOR CHS 76.1mm	N/A	GRADE 8.8	-
Total Weight:						3.95 kg


- All steel hot dip galvanized
- Each U-BOLT to be supplied with 4 Full Nuts, 2 Flat Washers and 2 Spring Washers
- For fabrication notes see drawing 305

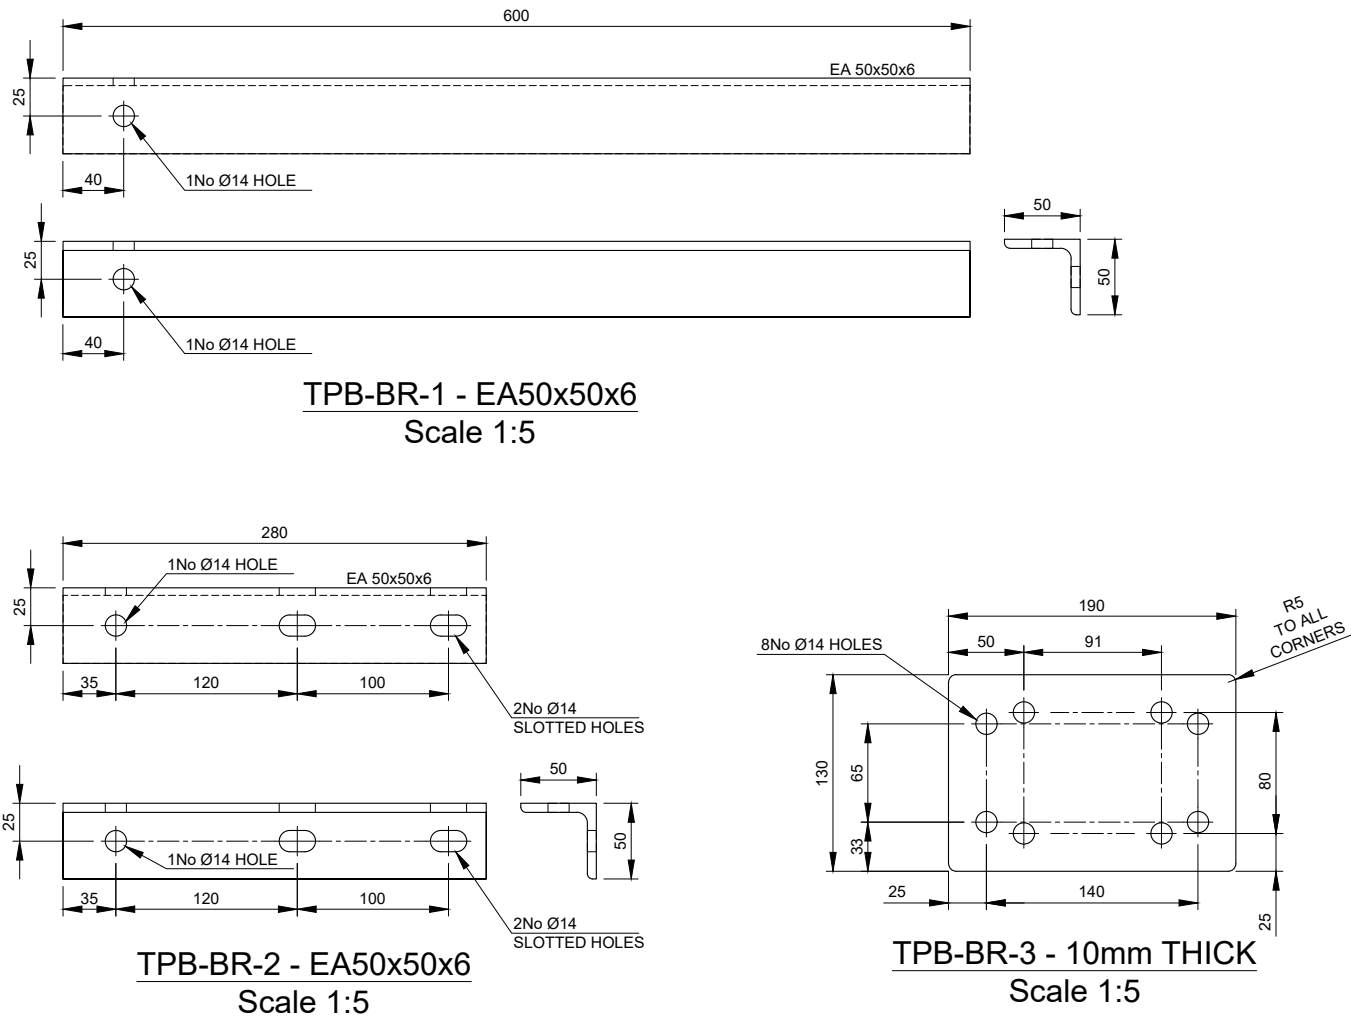

Parts list for TPB-BR

Item	Part	Quantity	Part description	Length	Material	Weight
01	TPB-BR-1	1	EA 50x50x6	280mm	S275J0	1.25 kg
02	TPB-BR-2	1	EA 50x50x6	600mm	S275J0	2.70 kg
03	TPB-BR-3	1	Plate 130x190x10mm	N/A	S275J0	1.94 kg
04	BOLT	1	M12 SET BOLT - 30mm LONG	N/A	GRADE 8.8	-
05	N-BOLT	2	M12 N-BOLT FOR EA 50x50x6	N/A	GRADE 8.8	-
06	U-BOLT	2	M12 U-BOLT FOR CHS 76.1mm	N/A	GRADE 8.8	-
Total Weight:						5.89 kg

- All steel hot dip galvanized
- Each BOLT to be supplied with 1 Full Nut, 1 Form E FLat Washer and 1 Spring Washer
- Each STUD & U-BOLT to be supplied with 4 Full Nuts, 2 Flat Washers and 2 Spring Washers
- For fabrication notes see drawing 305

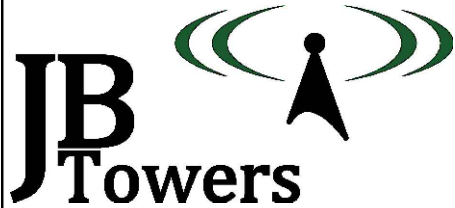

01	FIRST ISSUE	TT	20/06/19
REV	REV	BY	DATE
SCALE AS SHOWN WHEN PRINTED AT A3	DRAWN AM DATE 20/06/19	CHECKED MP DATE 20/06/19	APPROVED JBT DATE 20/06/19
ALL DIMENSIONS IN mm UNLESS OTHERWISE STATED. THIS DRAWING TO BE READ IN CONJUNCTION WITH OTHER RELEVANT DRAWINGS.			

TITLE
LOG MOUNT, BRACING ARM
PARTS: TPL-C, TPA-BR

SITE ADDRESS
TRI PEN HAD ROAD
DYFED
CARMARTHENSHIRE
SA17 5UR

ARQIVA REF.
140665
DRG No.
304
REV
01


ALL SCALES AS SHOWN WHEN PRINTED AT A3

Item	Part	Drawing	Quantity	Part description	Length	Material	Weight
01	01	200	1	3 MAN LATCHWAY SYSTEM & 4No. WIRE GUIDES FOR FACE MOUNTED MONOPOLE	17000	N/A	-
02	TPB-C	300	2	FALL ARREST ATTACHMENT POINT	N/A	S275J0	4.48 kg
03	03	200	46	PERMANENT BT STEP c/w 3No 10x75mm ZINC-PLATED COACH SCREWS	N/A	S275J0	13.80 kg
04	TPS-R	300	9	'MonoStep' ASSEMBLY	N/A	S275J0	21.69 kg
05	TPB-B	301	6	MOUNTING BRACKET	N/A	S275J0	67.02 kg
07	07	203/204	2	CHS 76.1x5mm	2000mm	S355J2H	35.08 kg
08	TPA-M	302	2	VSAT DISH MOUNTING BRACKET	630mm	S275J0	18.9 kg
09	09	203	24	M12 WASHER	N/A	GRADE 8.8	-
10	TPA-PD	301	4	POWER DIVIDER STRAP	N/A	S275J0	5.04 kg
11	11	203	2	CHS 76.1x5mm	1700mm	S355J2H	29.82 kg
12	TPL-C	304	2	LOG MOUNTING BRACKET	250mm	S275J0	7.89 kg
13	13	200	1	FEEDER COVER - 2/CG/100	3500mm	UV RESISTANT PLASTIC	-
14	14	200	17	FEEDER CLAMP - 2/FCD/028	N/A	POLYPROPYLENE	-
15	15	200	17	M10 SCREW DOWELS WTH M10 NUT	100mm	STAINLESS STEEL	-
16	16	200	1	PoleSaver	750mm	N/A	-
17	17	200	8	M12 STUD + 4No NUTS + 2No FLAT WASHERS + 1No Ø50mm WASHER (FOR FALL ARREST SYSTEM)	500mm	GRADE 8.8	3.56 kg
18	TPL-A	303	2	LOG MOUNTING BRACKET	610mm	S275J0	13.82 kg
19	TPL-B	303	2	LOG MOUNTING BRACKET	610mm	S275J0	13.82 kg
21	21	205	1	CHS 76.1x5mm	2200mm	S355J2H	19.29 kg
22	TPB-BR	304	1	BRACING ARM	N/A	S275J0	5.89 kg
Total Weight:							260.10 kg

- All steel hot dip galvanized
- All U-BOLTS to be FLA supply, each Supplied with 4 Full Nuts, 2 Flat Washers and 2 Spring Washers

NOTES:

1. WELDING TO BE IN ACCORDANCE WITH BS EN 1011-1:2009
2. LINEAR DIMS TO BE WITHIN ±1mm;
3. ANGULAR TOLERANCES TO BE WITHIN 0.5°
4. WELDING SYMBOLS ARE IN ACCORDANCE WITH BS EN 22553:1995
5. ALL PROFILE EDGES TO BE DRESSED AND SHARP CORNERS REMOVED
6. ALL WELD SIZES ARE FINAL SIZES
7. ALL WELDED JOINTS ARE TO BE PICKLE TIGHT
8. ALL STEELWORK TO BE BS EN 10025 GRADE S275 J0 UNO &
9. HOT DIPPED GALVANISED TO BS EN ISO 1461. (ALL HOLLOW SECTIONS TO BE GRADE S355 J0H)
10. ALL STEEL IS TO BE SUPPLIED IN ACCORDANCE WITH EN 1090 TO EXECUTION CLASS 2
11. ALL NON PRE-LOADED BOLTS TO BE COMPLIANT STRUCTURAL BOLTS TO BS EN ISO 15048 PARTS 1&2.
12. STEELWORK COMPONENTS SHALL BE HOT DIP GALVANISED TO ACHIEVE A "VERY HIGH" DURABILITY FOR AN ENVIRONMENT CATEGORY CODE C4 FROM TABLE 1 IN BS EN ISO 14713
13. BOLTS AND NUTS SHALL BE SUPPLIED IN ACCORDANCE WITH BS 7371, SPUN GALVANISED IN ACCORDANCE WITH ISO 10684, THE NUTS RE-TAPPED AFTER GALVANISING, AND THE THREADS TREATED WITH GREASE.
14. ALL BOLTS TO BE CUT ON SITE TO EXTEND MAX 10mm BEYOND THE NUT WHEN TIGHTENED UNO.
15. ALL SITE DRILLED HOLE/CUT ENDS TO BE TREATED WITH METAFLUX 70-40 ZINC PASTE FOLLOWED BY 1 COAT OF 7-42 ZINC ALU OR 70-16 ALUMINIUM SPRAY

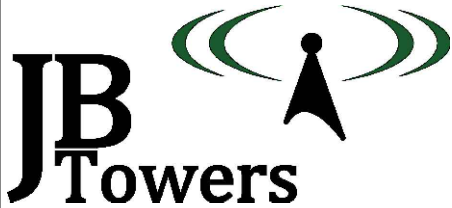

01	FIRST ISSUE			TT	20/06/19
REV	REV			BY	DATE
SCALE AS SHOWN WHEN PRINTED AT A3		DRAWN AM DATE 20/06/19	CHECKED MP DATE 20/06/19	APPROVED JBT DATE 20/06/19	
ALL DIMENSIONS IN mm UNLESS OTHERWISE STATED. THIS DRAWING TO BE READ IN CONJUNCTION WITH OTHER RELEVANT DRAWINGS.					

TITLE

PARTS LIST

SITE ADDRESS

TRI PEN HAD ROAD
DYFED
CARMARTHENSHIRE
SA17 5UR

ARQIVA REF.
140665


DRG No.
305

REV
01

ALL SCALES AS SHOWN WHEN PRINTED AT A3




ALL SCALES AS SHOWN WHEN PRINTED AT A3

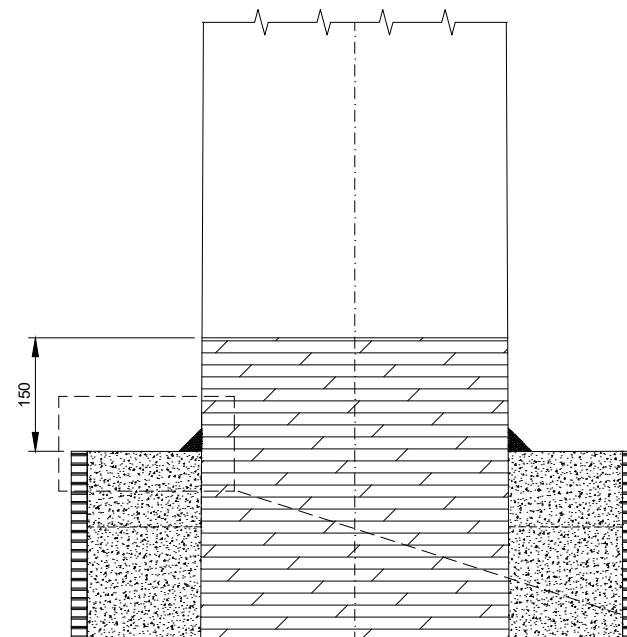

WATER PROOFING
Scale 1:10

- TIMBER POLE INSTALLATION:**
1. REFER TO DRAWING 200 FOR TIMBER POLE ORIENTATION
 2. BASE OF TIMBER POLE TO BE WRAPPED IN 'Polesaver' & INSTALLED AND LEVELLED IN OPENING. TIMBERS TO BE USED TO HOLD POLE IN POSITION
 3. ANNULUS SHALL BE FILLED WITH SITE MIXED CONCRETE UP TO 300mm BELOW GROUND LEVEL
 4. TOP 300mm SHALL BE FILLED WITH NON SHRINK GROUT. GROUT SHALL BE FORMED WITH A 1:60 FALL AT THE TOP SURFACE TO PREVENT PONDING
 5. ONCE THE GROUT/CONCRETE HAVE CURED THE TIMBER WEDGES SHALL BE REMOVED AND THE VOIDS LEFT ARE TO BE FILLED WITH NON SHRINK GROUT. FALL SHALL BE FORMED AROUND THE TIMBER POLE TO ALLOW WATER TO DRAIN AWAY

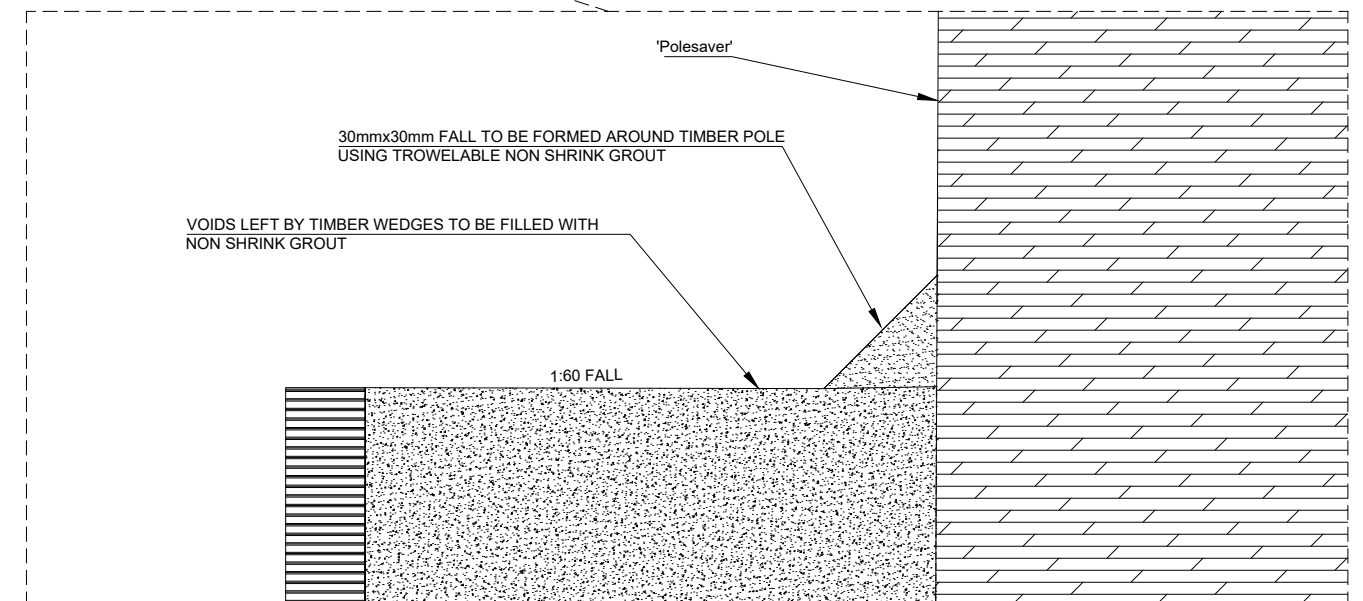

ENLARGED DETAIL
Scale 1:2

01	FIRST ISSUE		AM	20/06/19
REV	REV		BY	DAT
SCALE AS SHOWN WHEN PRINTED AT A3	DRAWN AM DATE 20/06/19	CHECKED MP DATE 20/06/19	APPROVED JB DATE 20/06/19	
ALL DIMENSIONS IN mm UNLESS OTHERWISE STATED. THIS DRAWING TO BE READ IN CONJUNCTION WITH OTHER RELEVANT DRAWINGS.				