
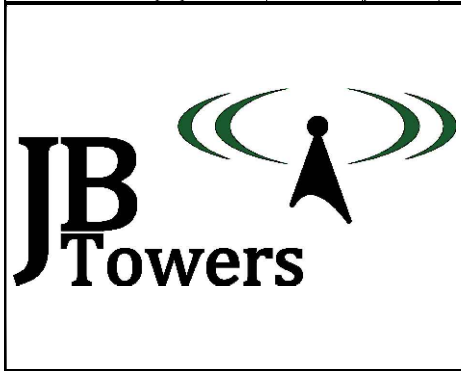
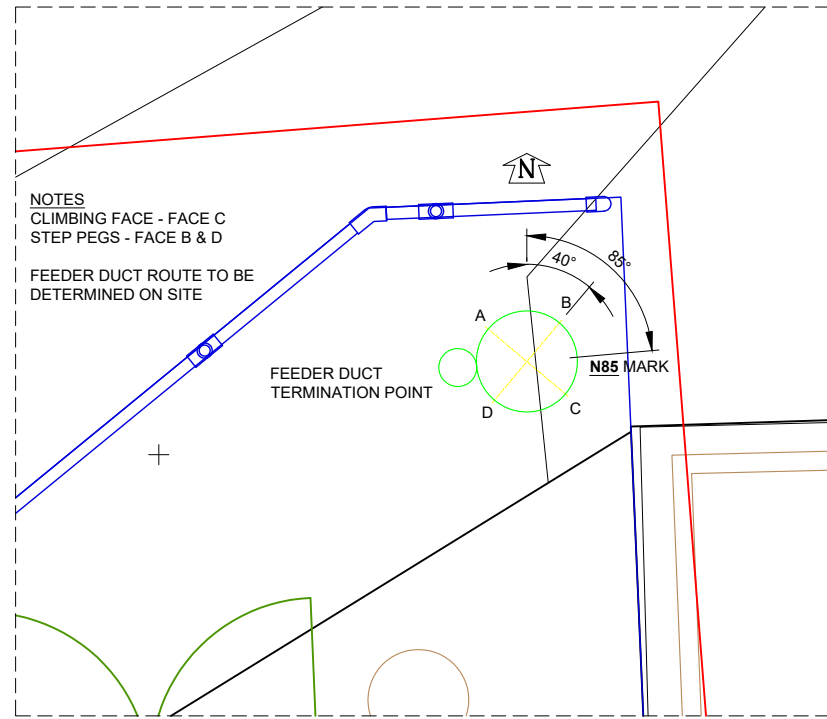


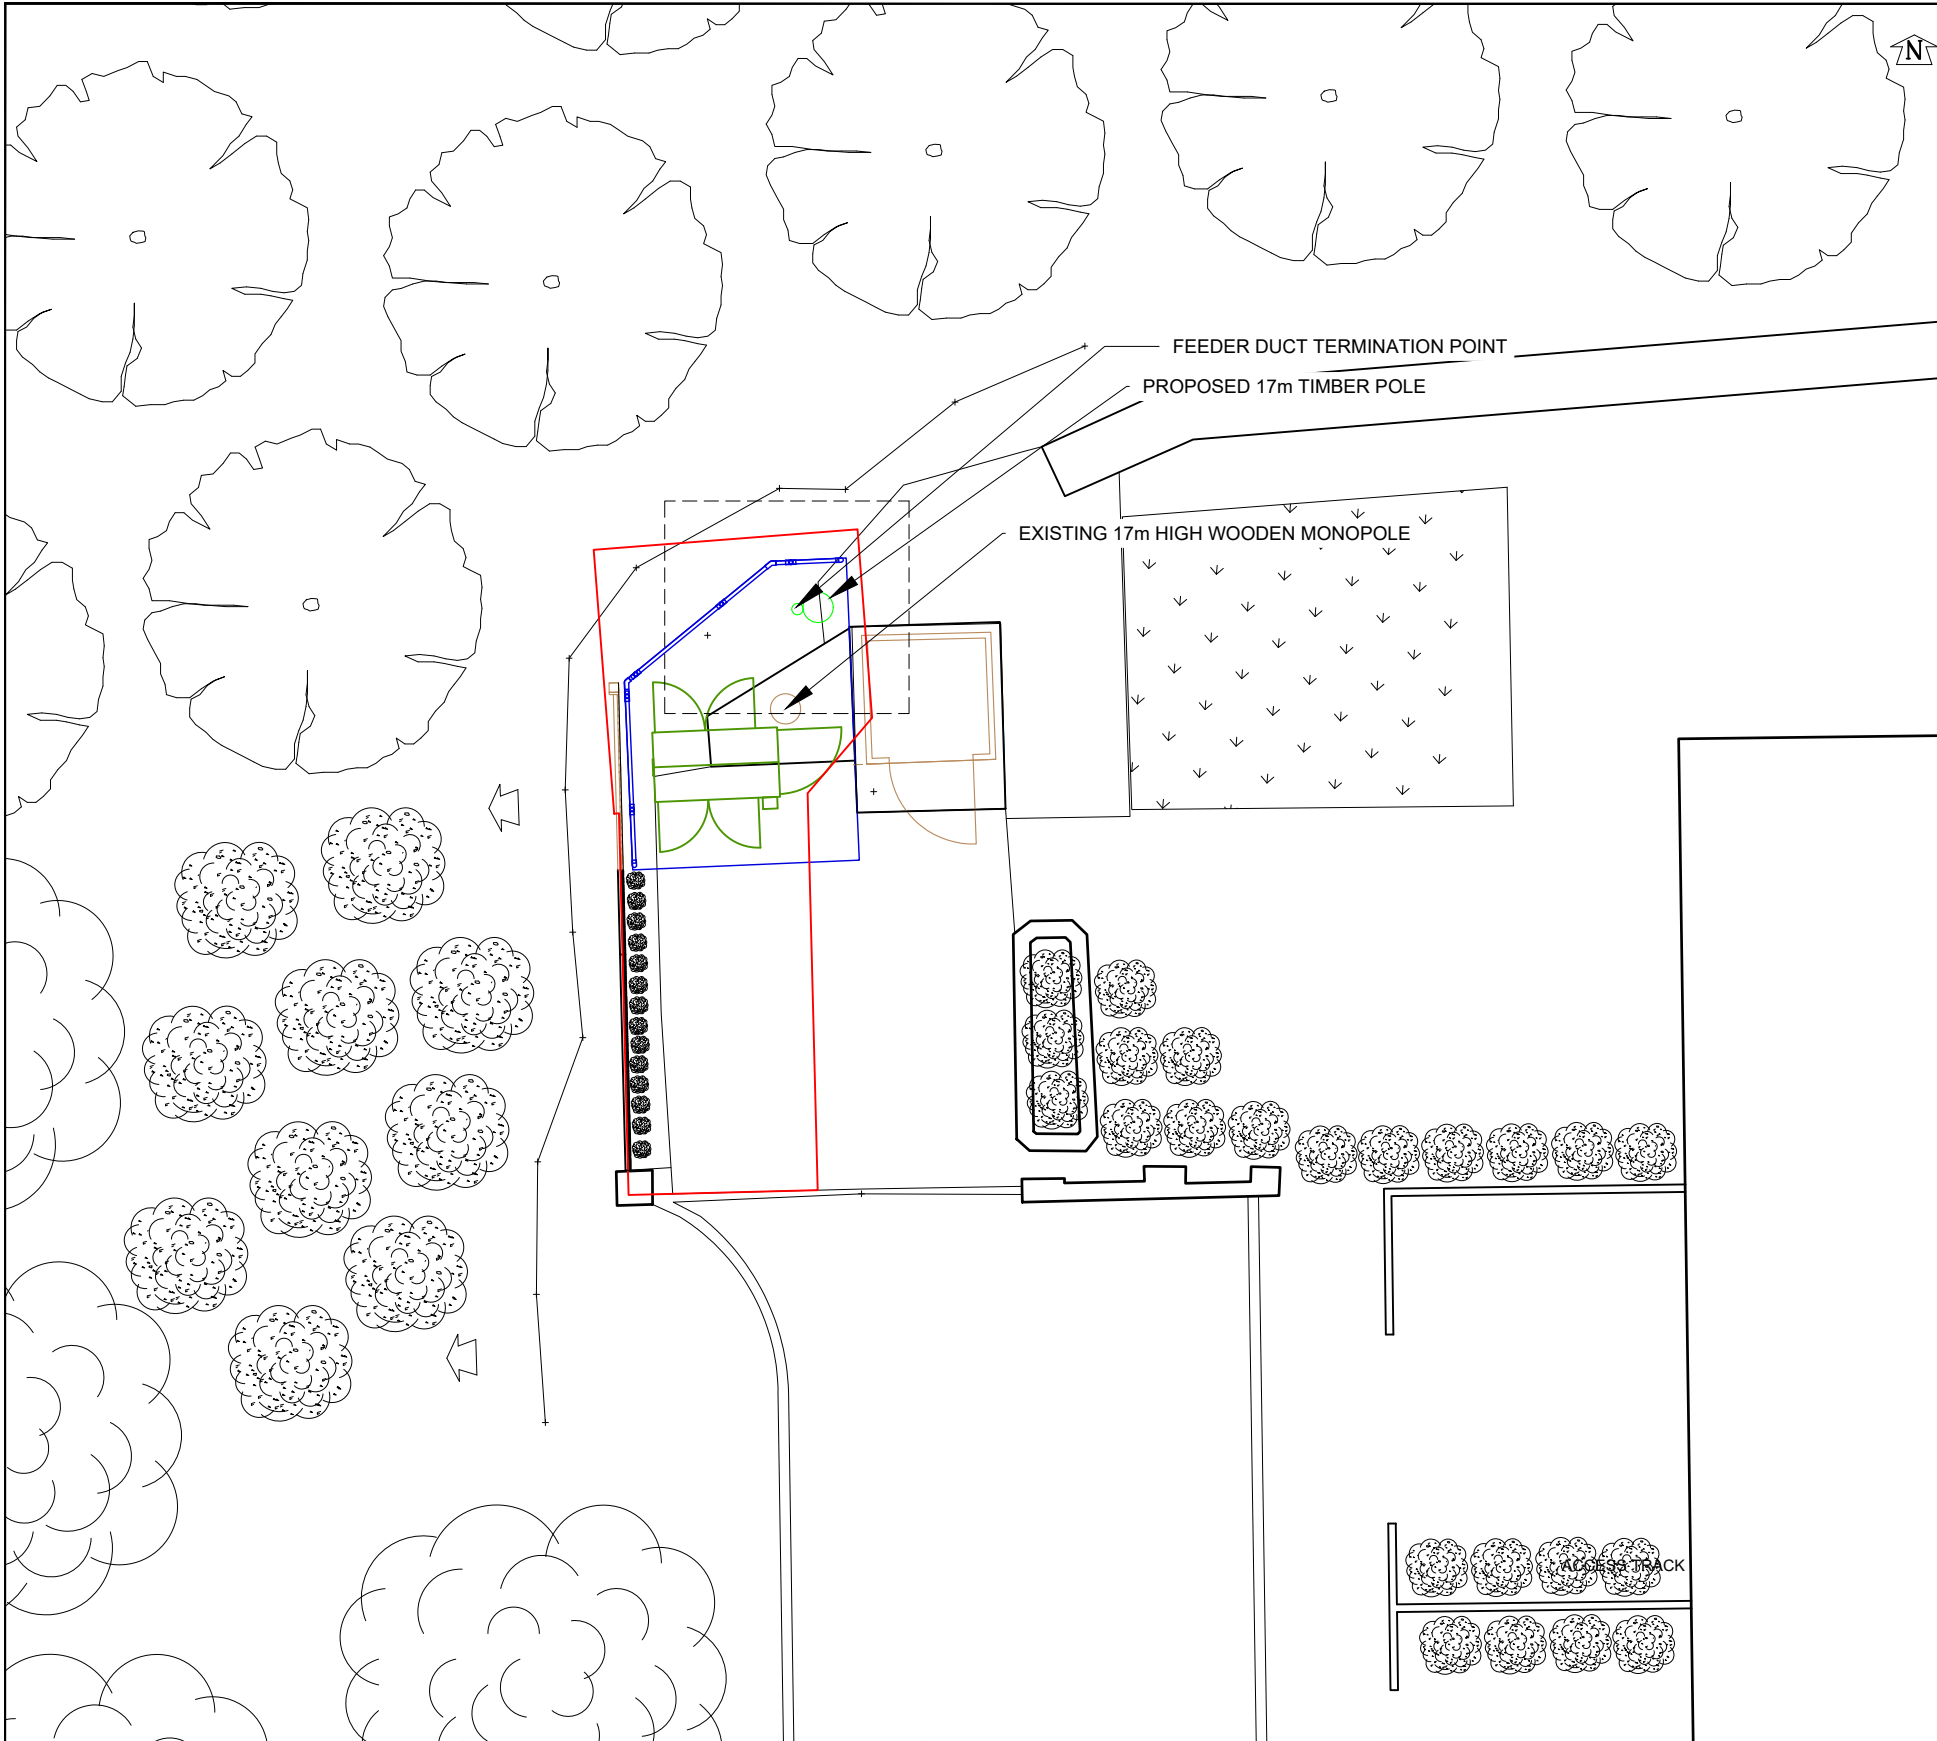


01	FIRST ISSUE	AM	10/01/20
REV	REV	BY	DATE
SCALE AS SHOWN	DRAWN	CHECKED	APPROVED
WHEN PRINTED AT A3	AM	MP	JBT
DATE	10/01/20	DATE	10/01/20
DATE	10/01/20	DATE	10/01/20
ALL DIMENSIONS IN mm UNLESS OTHERWISE STATED. THIS DRAWING TO BE READ IN CONJUNCTION WITH OTHER RELEVANT DRAWINGS.			

TITLE
HELE
SITE PLAN

SITE ADDRESS HELE THIRD AVENUE, TORQUAY, DEVON, TQ1 4JF		
ARQIVA REF. 13618	DRG No. 100	REV 01

ALL SCALES AS SHOWN WHEN PRINTED AT A3



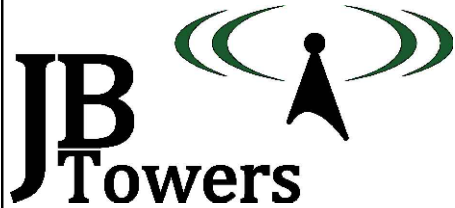

01	FIRST ISSUE			AM	10/01/20
REV	REV			BY	DATE
SCALE AS SHOWN		DRAWN	AM	CHECKED	MP
WHEN PRINTED AT A3		DATE	10/01/20	DATE	10/01/20
		APPROVED	JBT	DATE	10/01/20

ALL DIMENSIONS IN mm UNLESS OTHERWISE STATED.
THIS DRAWING TO BE READ IN CONJUNCTION WITH
OTHER RELEVANT DRAWINGS.

TITLE

HELE

GENERAL ARRANGEMENT
SHEET 1 OF 3



SITE ADDRESS

HELE
THIRD AVENUE,
TORQUAY, DEVON,
TQ1 4JF

ARQIVA REF.
13618

DRG No.
200

REV
01

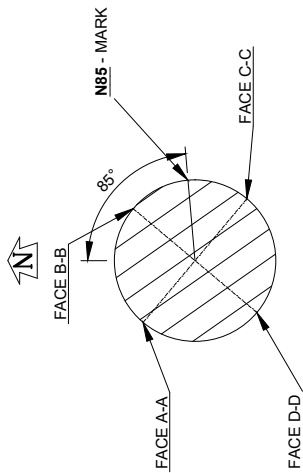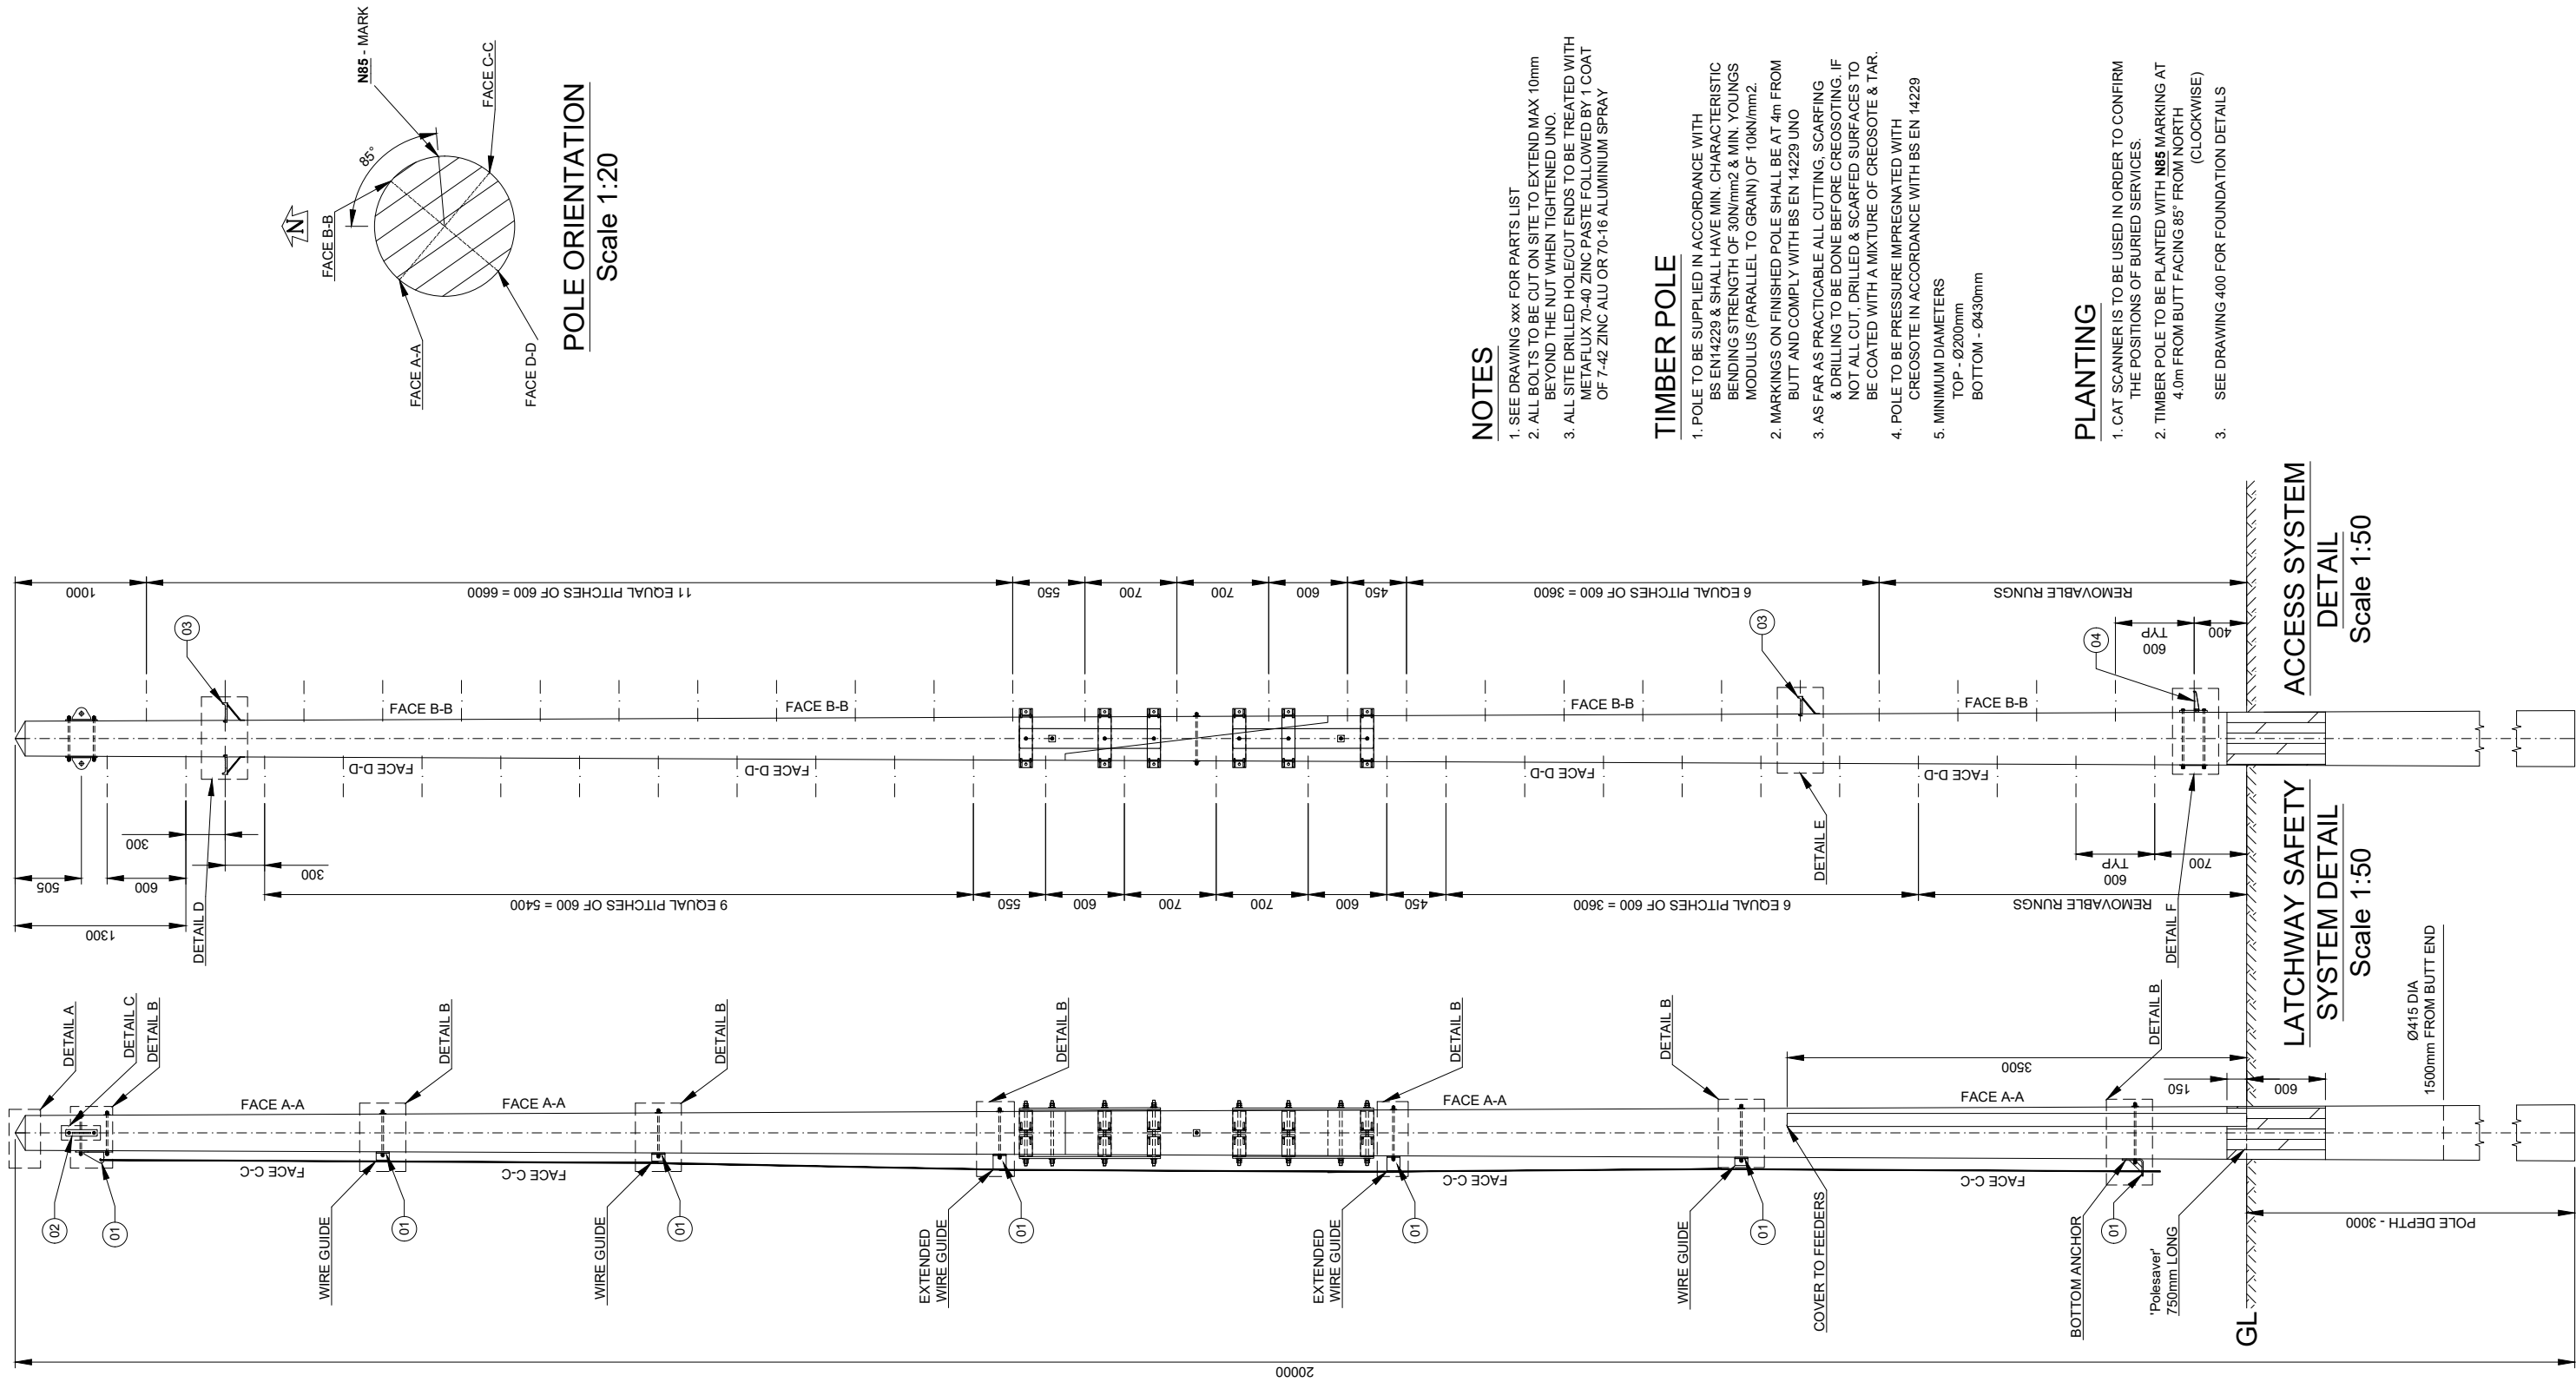

POLE ORIENTATION
Scale 1:20

NOTES

1. SEE DRAWING xxx FOR PARTS LIST
2. ALL BOLTS TO BE CUT ON SITE TO EXTEND MAX 10mm BEYOND THE NUT WHEN TIGHTENED UNO.
3. ALL SITE DRILLED HOLE/CUT ENDS TO BE TREATED WITH METAFUX 70-40 ZINC PASTE FOLLOWED BY 1 COAT OF 7-42 ZINC ALU OR 70-16 ALUMINIUM SPRAY

TIMBER POLE

1. POLE TO BE SUPPLIED IN ACCORDANCE WITH BS EN14229 & SHALL HAVE MIN. CHARACTERISTIC BENDING STRENGTH OF 30N/mm² & MIN. YOUNGS MODULUS (PARALLEL TO GRAIN) OF 10kN/mm².
2. MARKINGS ON FINISHED POLE SHALL BE AT 4m FROM BUTT AND COMPLY WITH BS EN 14229 UNO
3. AS FAR AS PRACTICABLE ALL CUTTING, SCARFING & DRILLING TO BE DONE BEFORE CREOSOTING. IF NOT ALL CUT, DRILLED & SCARFED SURFACES TO BE COATED WITH A MIXTURE OF CREOSOTE & TAR.
4. POLE TO BE PRESSURE IMPREGNATED WITH CREOSOTE IN ACCORDANCE WITH BS EN 14229
5. MINIMUM DIAMETERS
TOP - Ø200mm
BOTTOM - Ø430mm

PLANTING


1. CAT SCANNER IS TO BE USED IN ORDER TO CONFIRM THE POSITIONS OF BURIED SERVICES.
2. TIMBER POLE TO BE PLANTED WITH N85 MARKING AT 4.0m FROM BUTT FACING 85° FROM NORTH (CLOCKWISE)
3. SEE DRAWING 400 FOR FOUNDATION DETAILS

ACCESS SYSTEM
DETAIL
Scale 1:50

LATCHWAY SAFETY
SYSTEM DETAIL
Scale 1:50


ALL SCALES AS SHOWN WHEN PRINTED AT A3

ALL SCALES AS SHOWN WHEN PRINTED AT A3

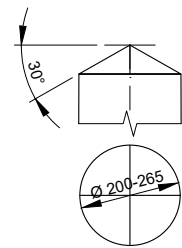


- NOTES:
1. A SINGLE COAT OF TIMBER COMPATIBLE BITUMINOUS PAINT (E.G. BIRD BRAND BLACK BITUMINOUS PAINT OR SIMILAR APPROVED PRODUCT) TO BE APPLIED TO THE UPPER SURFACES AT THE TOP OF THE POLE.
 2. PAINT TO BE APPLIED ON SITE JUST BEFORE ERECTION
- FORM: 4 WAY PYRAMID / CONE


DETAIL A - TIMBER POLE TOP
Scale 1:20

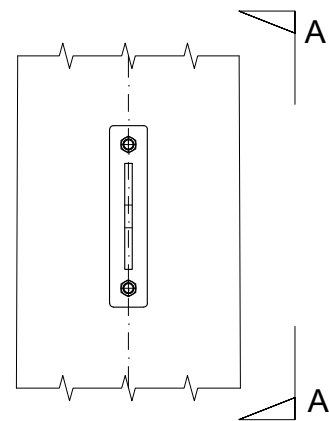


DETAIL C - FALL ARREST
ATTACHMENT POINT
Scale 1:10

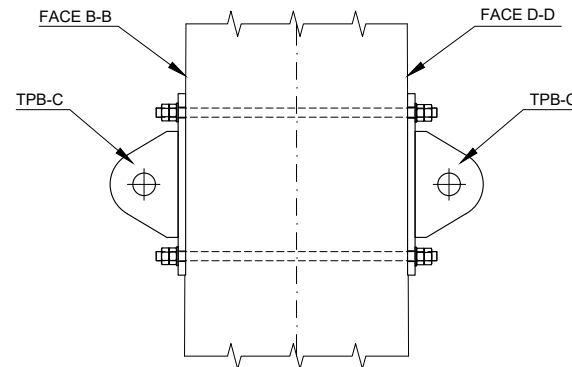


VIEW A-A
Scale 1:10

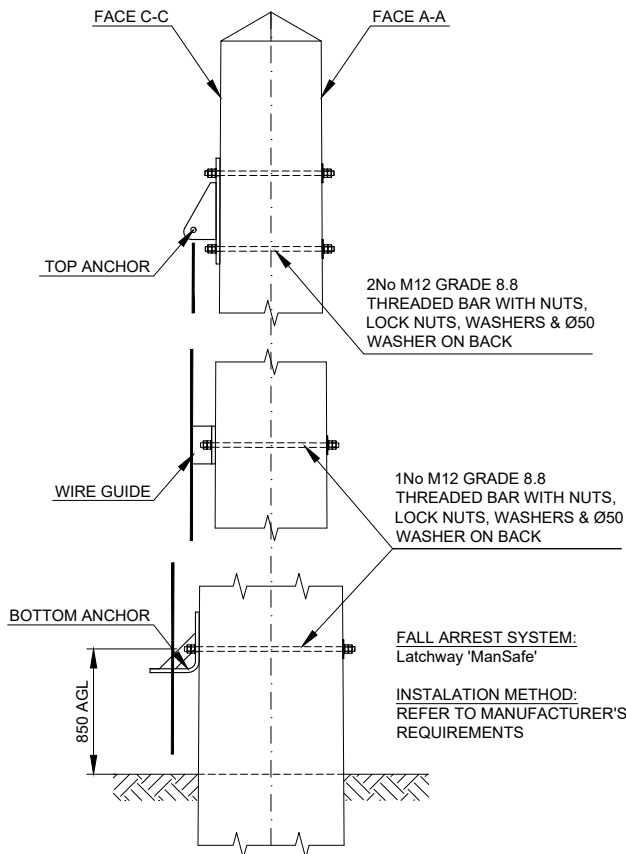

DETAIL B - FALL ARREST SYSTEM
Scale 1:20

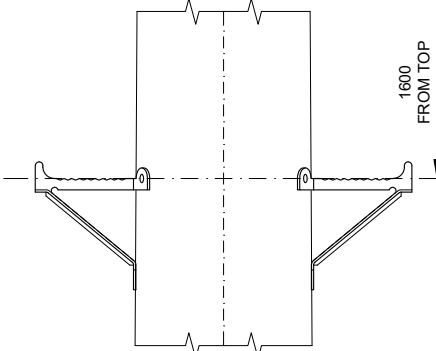


DETAIL D - ANTENNA
ACCESS CLIMBING STEP
Scale 1:10

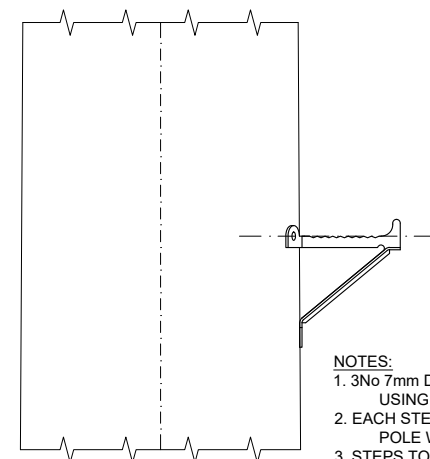


DETAIL E - PERMANENT
CLIMBING STEPS
Scale 1:10

- NOTES:
1. 3 No 7mm DIA 70mm LONG PILOT HOLES TO BE DRILLED USING THE STEP AS A TEMPLATE
 2. EACH STEP SHOULD BE FIXED TO THE TIMBER POLE WITH 3 No 10mm COACH SCREWS 75mm LONG
 3. STEPS TO BE INSTALLED ON FACES B-B & D-D ONLY

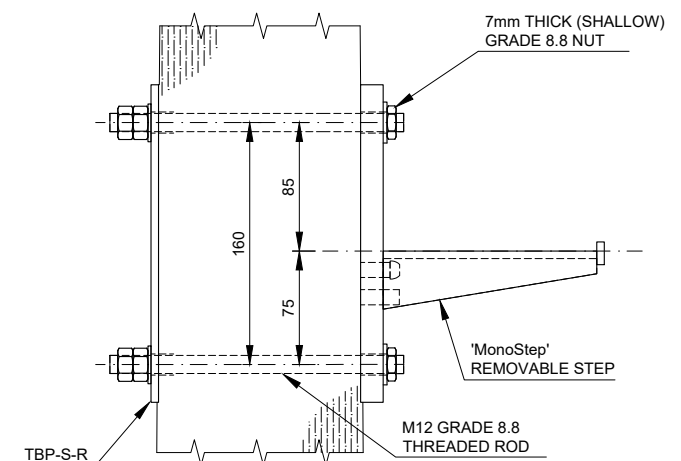

DETAIL F - REMOVABLE
CLIMBING STEPS
Scale 1:5

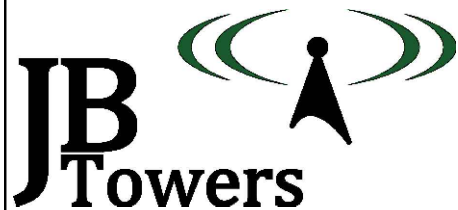

01	FIRST ISSUE	AM	10/01/20
REV	REV	BY	DATE
SCALE AS SHOWN WHEN PRINTED AT A3	DRAWN DATE 10/01/20	CHECKED DATE 10/01/20	APPROVED DATE 10/01/20
ALL DIMENSIONS IN mm UNLESS OTHERWISE STATED. THIS DRAWING TO BE READ IN CONJUNCTION WITH OTHER RELEVANT DRAWINGS.			

TITLE
HELE
GENERAL ARRANGEMENT
SHEET 3 OF 3


SITE ADDRESS
HELE
THIRD AVENUE,
TORQUAY, DEVON,
TQ1 4JF

ARQIVA REF.
13618
DRG No.
200
REV
01

ALL SCALES AS SHOWN WHEN PRINTED AT A3



ALL SCALES AS SHOWN WHEN PRINTED AT A3

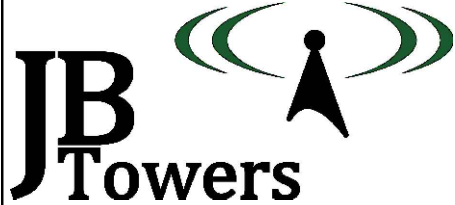

01	FIRST ISSUE			AM	10/01/20
REV	REV			BY	DATE
SCALE AS SHOWN		DRAWN	AM	CHECKED	MP
WHEN PRINTED AT A3		DATE	10/01/20	DATE	10/01/20
		APPROVED	JBT	DATE	10/01/20

ALL DIMENSIONS IN mm UNLESS OTHERWISE STATED.
THIS DRAWING TO BE READ IN CONJUNCTION WITH
OTHER RELEVANT DRAWINGS.

TITLE

HELE

TIMBER POLE HOLE SET OUT
SHEET 1 OF 2




SITE ADDRESS

HELE
THIRD AVENUE,
TORQUAY, DEVON,
TQ1 4JF


ARQIVA REF.
13618

DRG No.
201

REV
01

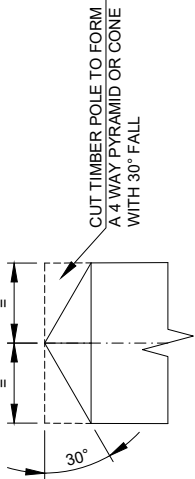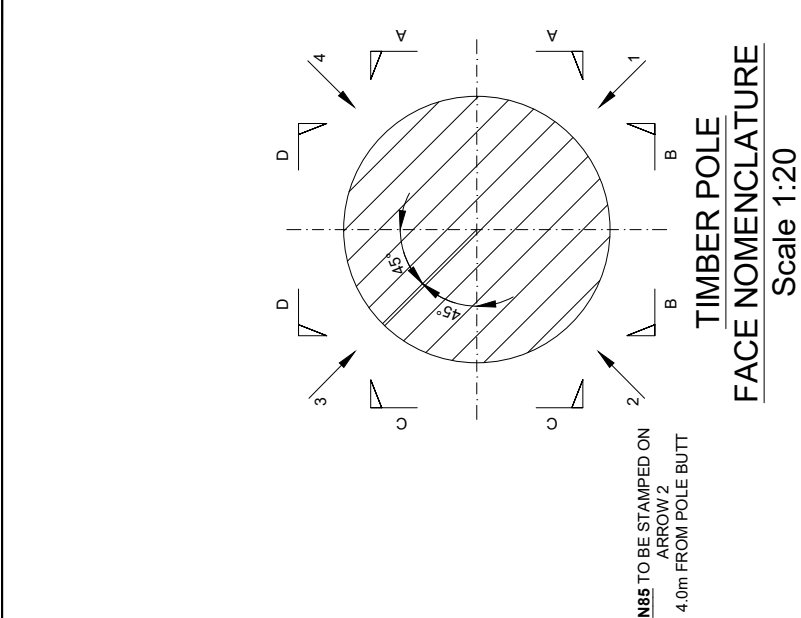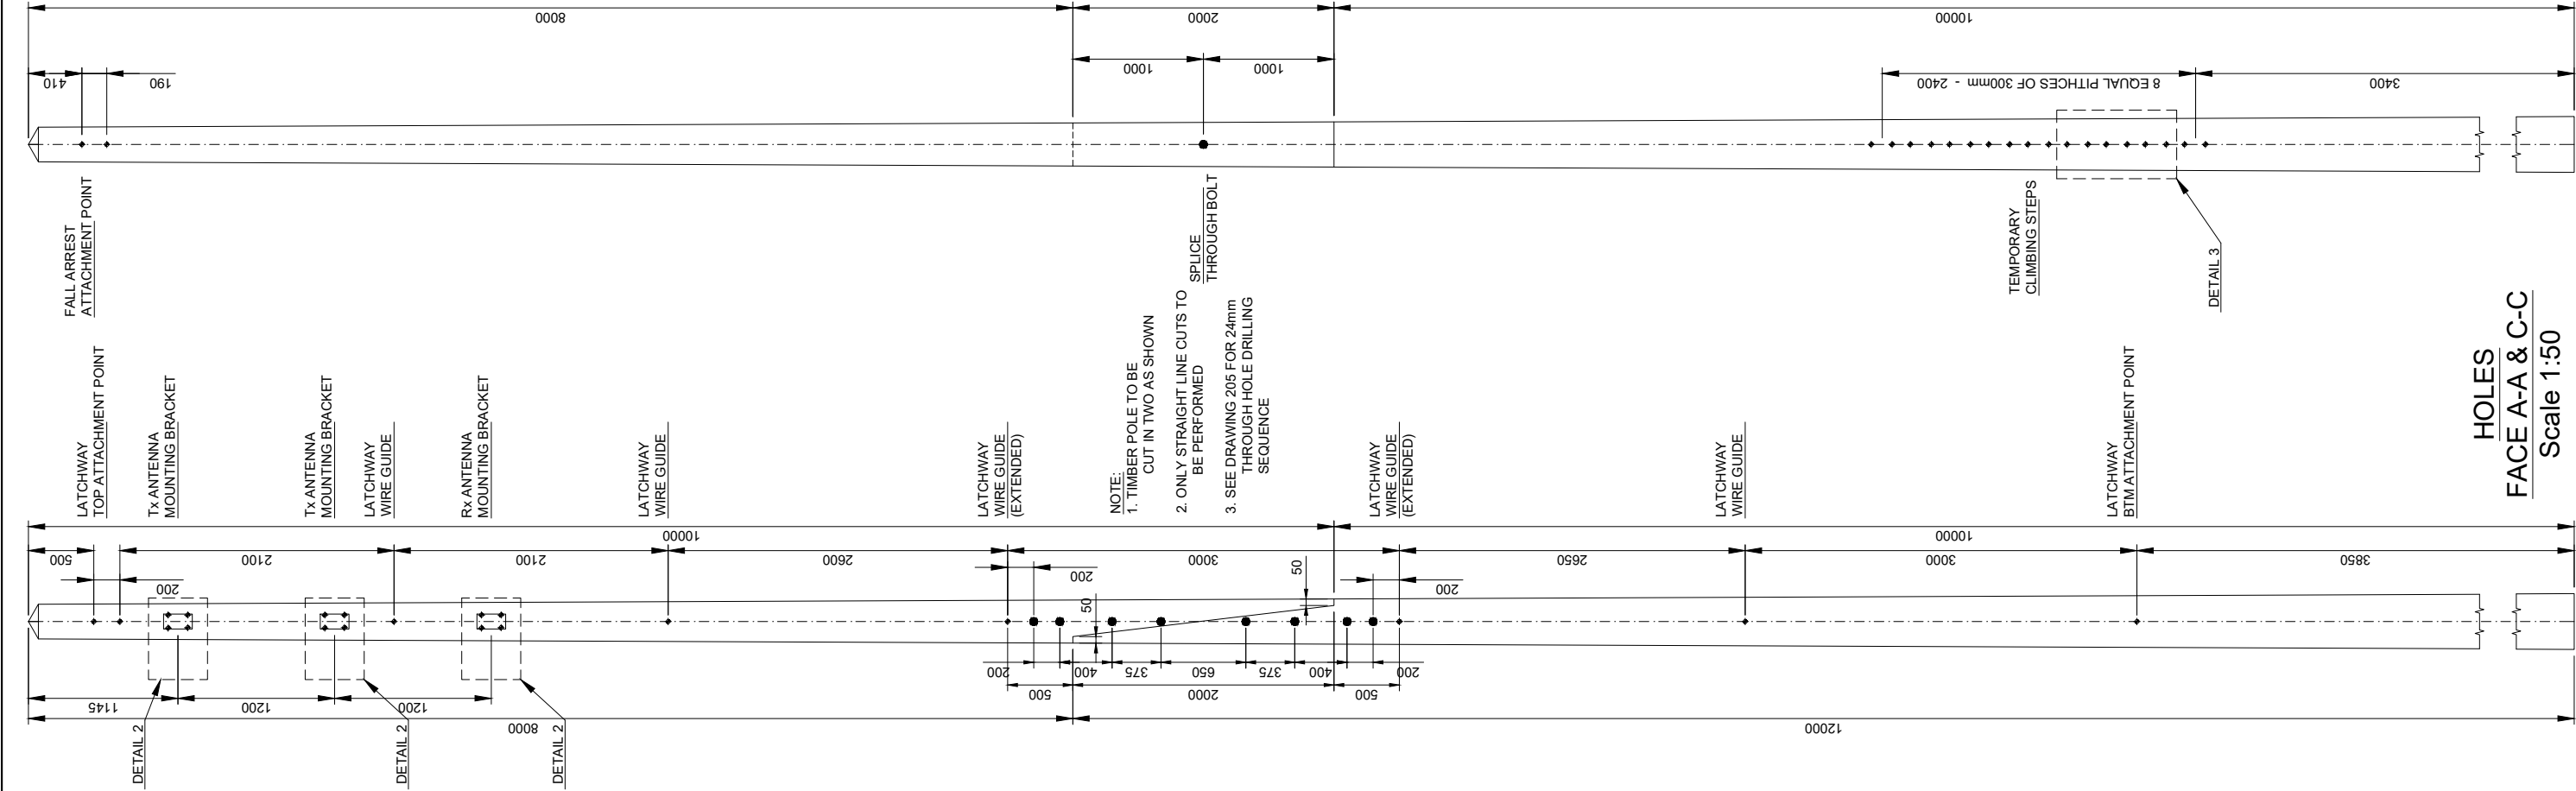


DETAIL 1
Scale 1:10

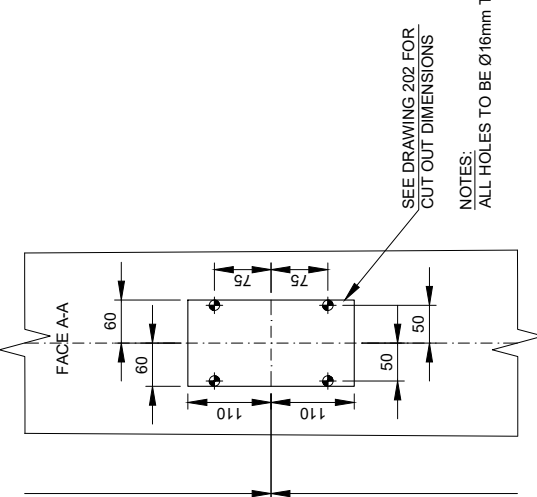

NOTES:
ALL HOLES TO BE Ø16mm THROUGH HOLES

DETAIL 2 - TYPICAL
Scale 1:10

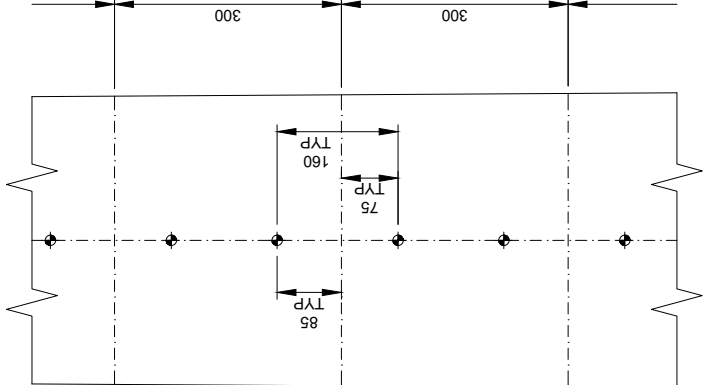

DETAIL 3 - TYPICAL
Scale 1:10




HOLES
FACE B-B & D-D
Scale 1:50

HOLES
FACE A-A & C-C
Scale 1:50



ALL SCALES AS SHOWN WHEN PRINTED AT A3

ALL SCALES AS SHOWN WHEN PRINTED AT A3

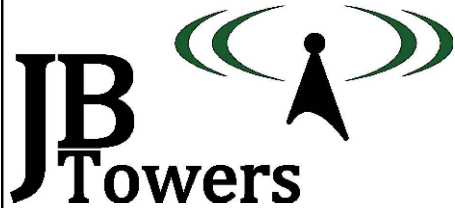

01	FIRST ISSUE			AM	10/01/20
REV	REV			BY	DATE
SCALE AS SHOWN		DRAWN	AM	CHECKED	MP
WHEN PRINTED AT A3		DATE	10/01/20	DATE	10/01/20
APPROVED		JBT			
DATE		10/01/20			

ALL DIMENSIONS IN mm UNLESS OTHERWISE STATED.
THIS DRAWING TO BE READ IN CONJUNCTION WITH
OTHER RELEVANT DRAWINGS.

TITLE


HELE

TIMBER POLE HOLE SET OUT
SHEET 2 OF 2

SITE ADDRESS


HELE
THIRD AVENUE,
TORQUAY, DEVON,
TQ1 4JF

ARQIVA REF. 13618	DRG No. 201	REV 01
----------------------	----------------	-----------

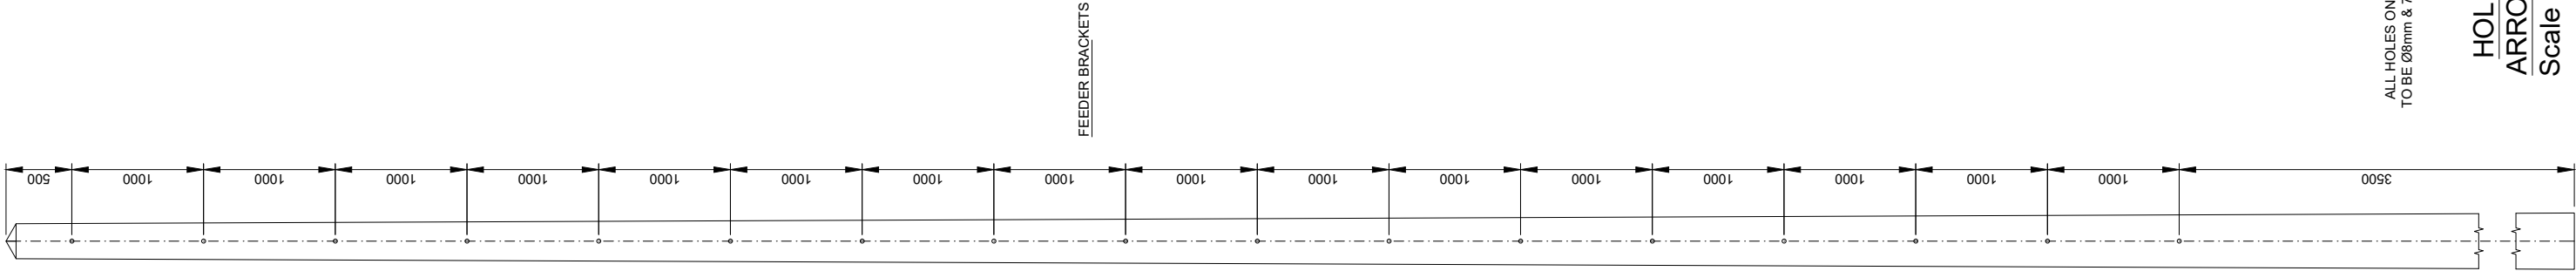


ALL HOLES ON ARROW 4
TO BE Ø8mm & 70mm LONG

HOLES
ARROW 4
Scale 1:50

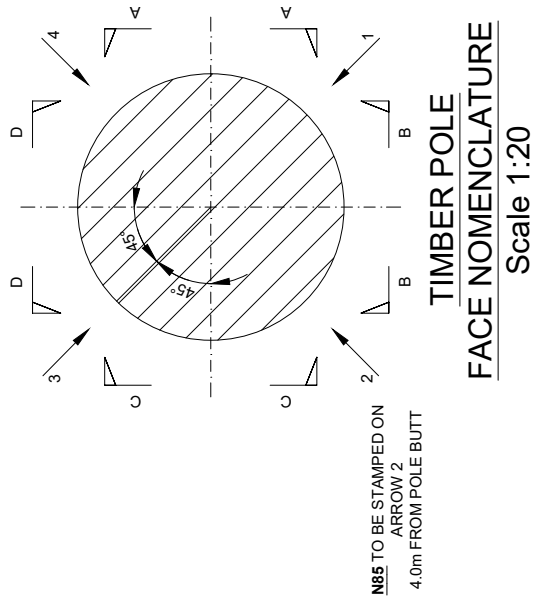

ALL SCALES AS SHOWN WHEN PRINTED AT A3

ALL SCALES AS SHOWN WHEN PRINTED AT A3

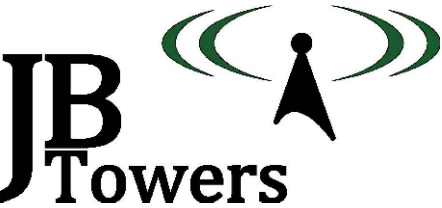


01	FIRST ISSUE							AM	10/01/20
REV	REV							BY	DATE
SCALE AS SHOWN		DRAWN	AM	CHECKED	MP	APPROVED		JBT	
WHEN PRINTED AT A3		DATE	10/01/20	DATE	10/01/20	DATE		10/01/20	
ALL DIMENSIONS IN mm UNLESS OTHERWISE STATED.									
THIS DRAWING TO BE READ IN CONJUNCTION WITH									
OTHER RELEVANT DRAWINGS.									

TITLE

HELE

TIMBER POLE CUT OUT
DETAIL




SITE ADDRESS HELE THIRD AVENUE, TORQUAY, DEVON, TQ1 4JF		
ARQIVA REF. 13618	DRG No. 202	REV 01

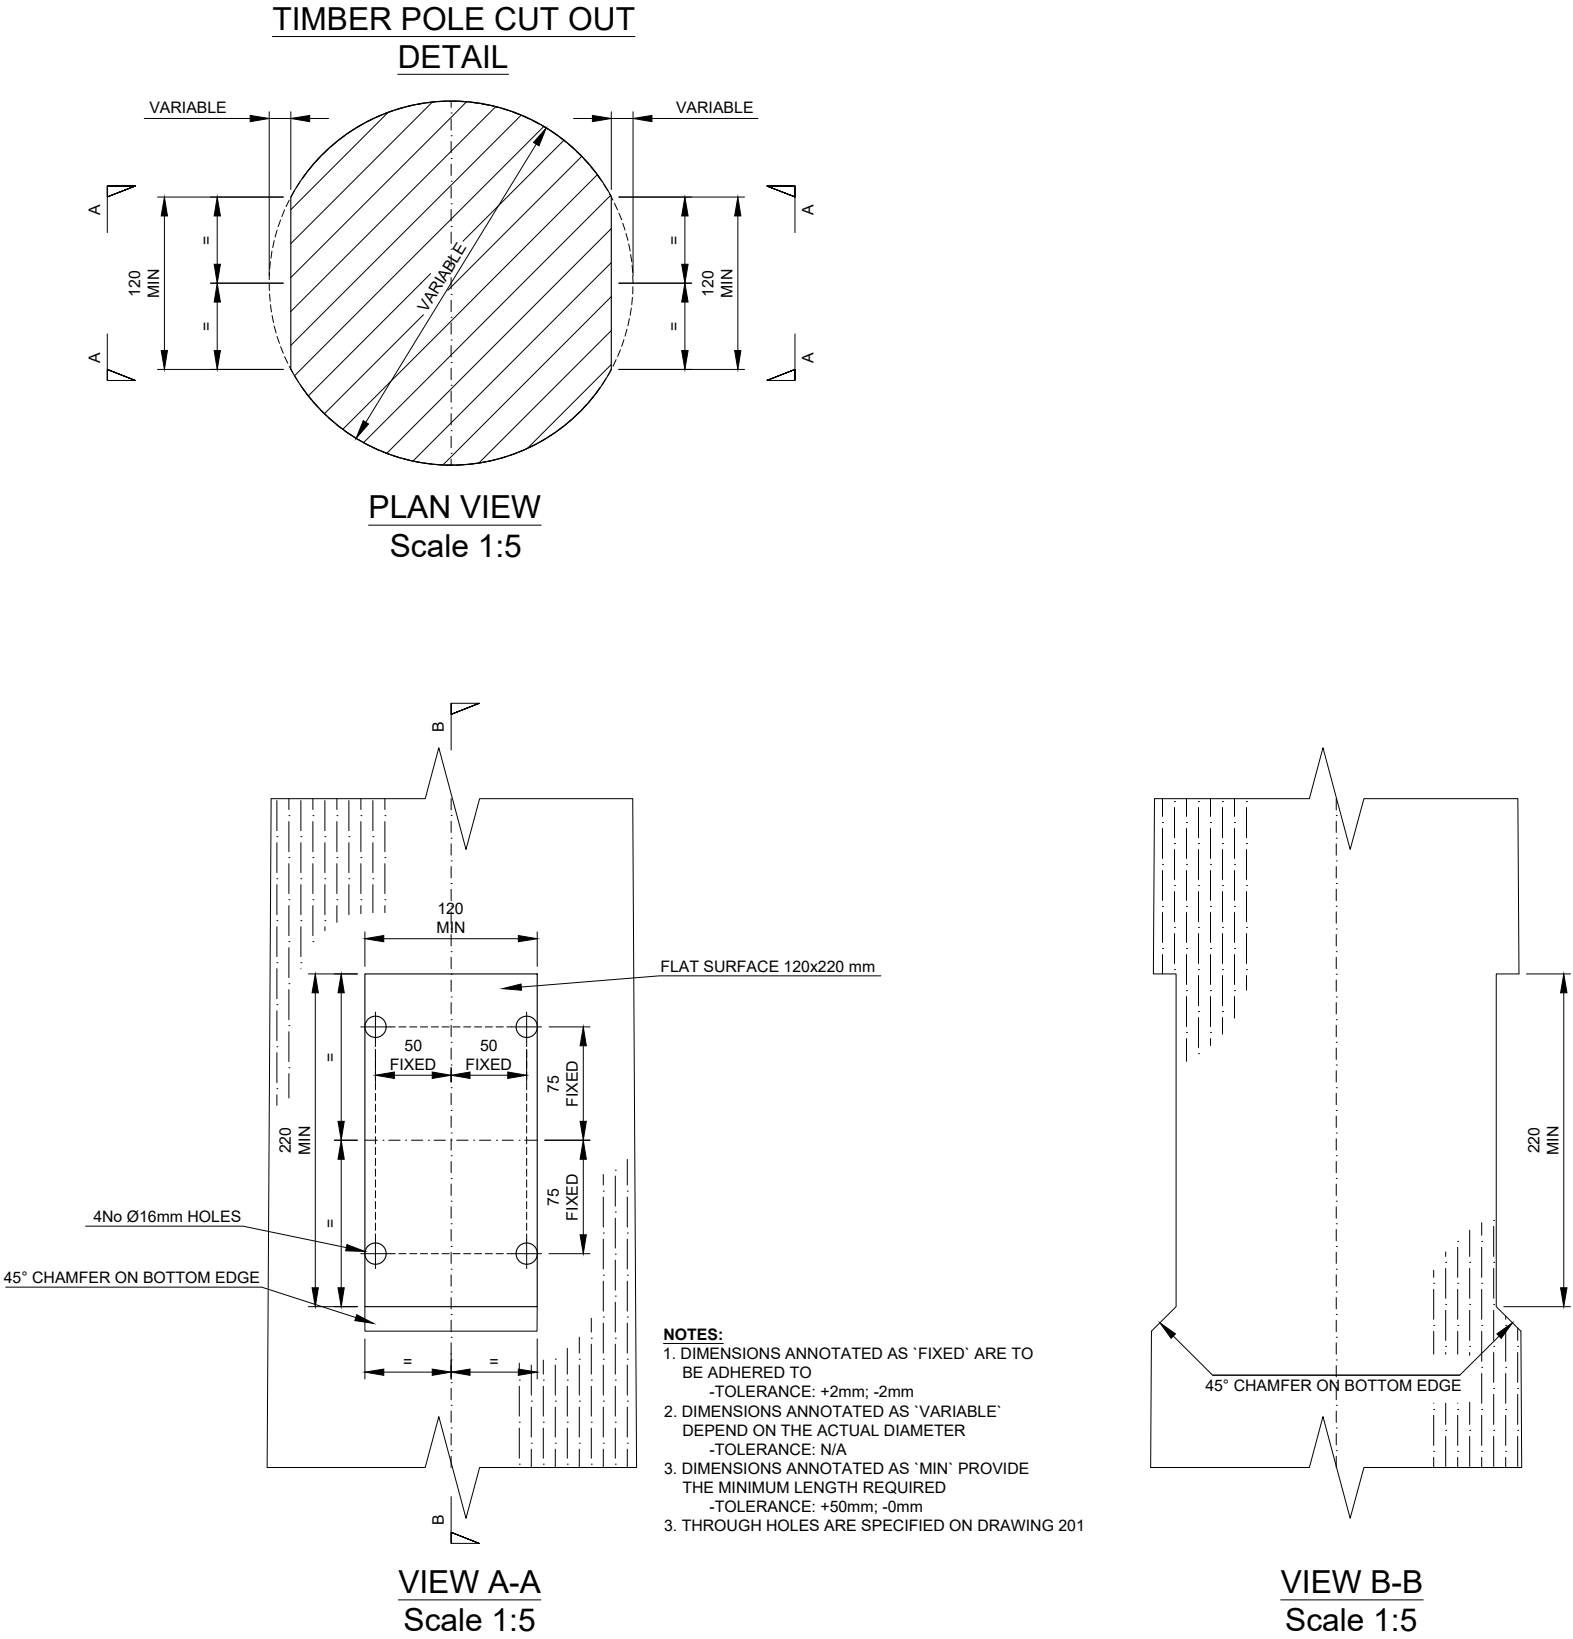

ALL SCALES AS SHOWN WHEN PRINTED AT A3



ALL SCALES AS SHOWN WHEN PRINTED AT A3

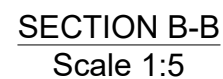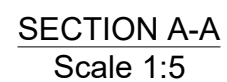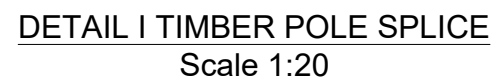

NOTE:

- ALL M16 BOLTS TO BE TIGHTENED TO 90Nm
- ALL SITE DRILLED HOLE/CUT ENDS TO BE TREATED WITH METAFLUX 70-40 ZINC PASTE FOLLOWED BY 1 COAT OF 7-42 ZINC ALU OR 70-16 ALUMINIUM SPRAY

- WORK SEQUENCE (PRIOIR TO POLE BEING SENT TO SITE):**
1. LOCATION OF COLLARS TO BE MARKED ON POLE AND POLE OD AT THESE LOCATIONS TO BE MEASURED AND USED TO INFORM THE FABRICATION OF THE STEEL COLLARS.
(COLLAR HOLES FOR THE THROUGH BOLTS ARE TO BE DRILLED LATER)
 2. HOLES IN POLE FOR ALL COLLAR THROUGH BOLTS TO BE DRILLED.
 3. SPLICE JOINT TO BE CUT IN POLE.
 4. POLE TO BE PRESSURE IMPREGNATED WITH CREOSOTE.
 5. POLE SECTIONS TO BE OFFERED TO ONE ANOTHER AND ONCE IN THE CORRECT POSITION COLLARS 2 SHALL BE INSTALLED TO HOLD THE POLE IN POSITION AND THE CLAMPING BOLTS TORQUED.
 6. THE THROUGH BOLT IN THE CENTRE OF THE SPLICE SHALL BE DRILLED AND THE THROUGH BOLT INSERTED.
 7. THE THROUGH BOLTS FOR COLLARS 1 & 3 SHALL BE INSTALLED AND THE COLLARS OFFERED UP AND THE REQD HOLE LOCATIONS IN THE COLLARS MARKED AND THEN DRILLED.
 8. THESE COLLARS SHALL BE INSTALLED OVER THE THROUGH BOLTS AND THEN THE CLAMPING BOLTS TORQUED.
 9. COLLARS 2 SHALL THEN BE REMOVED AND THE THROUGH BOLTS INSTALLED AND THE COLLARS OFFERED UP AND THE REQD HOLE LOCATIONS IN THE COLLARS MARKED AND THEN DRILLED.
 10. THESE COLLARS SHALL BE INSTALLED OVER THE THROUGH BOLTS AND THEN THE CLAMPING BOLTS TORQUED.
 11. THE VERTICAL PLATES STRAPPING THE COLLARS TOGETHER SHALL THEN BE INSTALLED.
 12. THE FIT OF ALL ELEMENTS OF THE SPLICE SHALL BE CHECKED AND ONCE SATISFACTORY FIT HAS BEEN CONFIRMED THE SPLICE JOINT CAN BE DISASSEMBLED.
 13. ANY DISTURBED SURFACES SHALL HAVE THEIR WATERPROOFING REPAIRED AS PER NOTES ON DRG 200
 14. THE CLAMPING BOLTS USED IN THE CHECK ERECTION SHALL BE DISCARDED AND NEW BOLTS SUPPLIED TO SITE.



01	FIRST ISSUE		AM	10/01/2	
REV	REV		BY	DATE	
SCALE AS SHOWN WHEN PRINTED AT A3	DRAWN AM DATE 10/01/20	CHECKED MP DATE 10/01/20	APPROVED JB DATE 10/01/20	JB	
ALL DIMENSIONS IN mm UNLESS OTHERWISE STATED. THIS DRAWING TO BE READ IN CONJUNCTION WITH OTHER RELEVANT DRAWINGS.					