
 
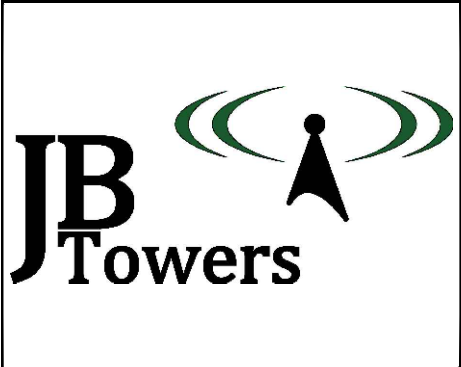


DRAWING ISSUE SHEET

[illegible]

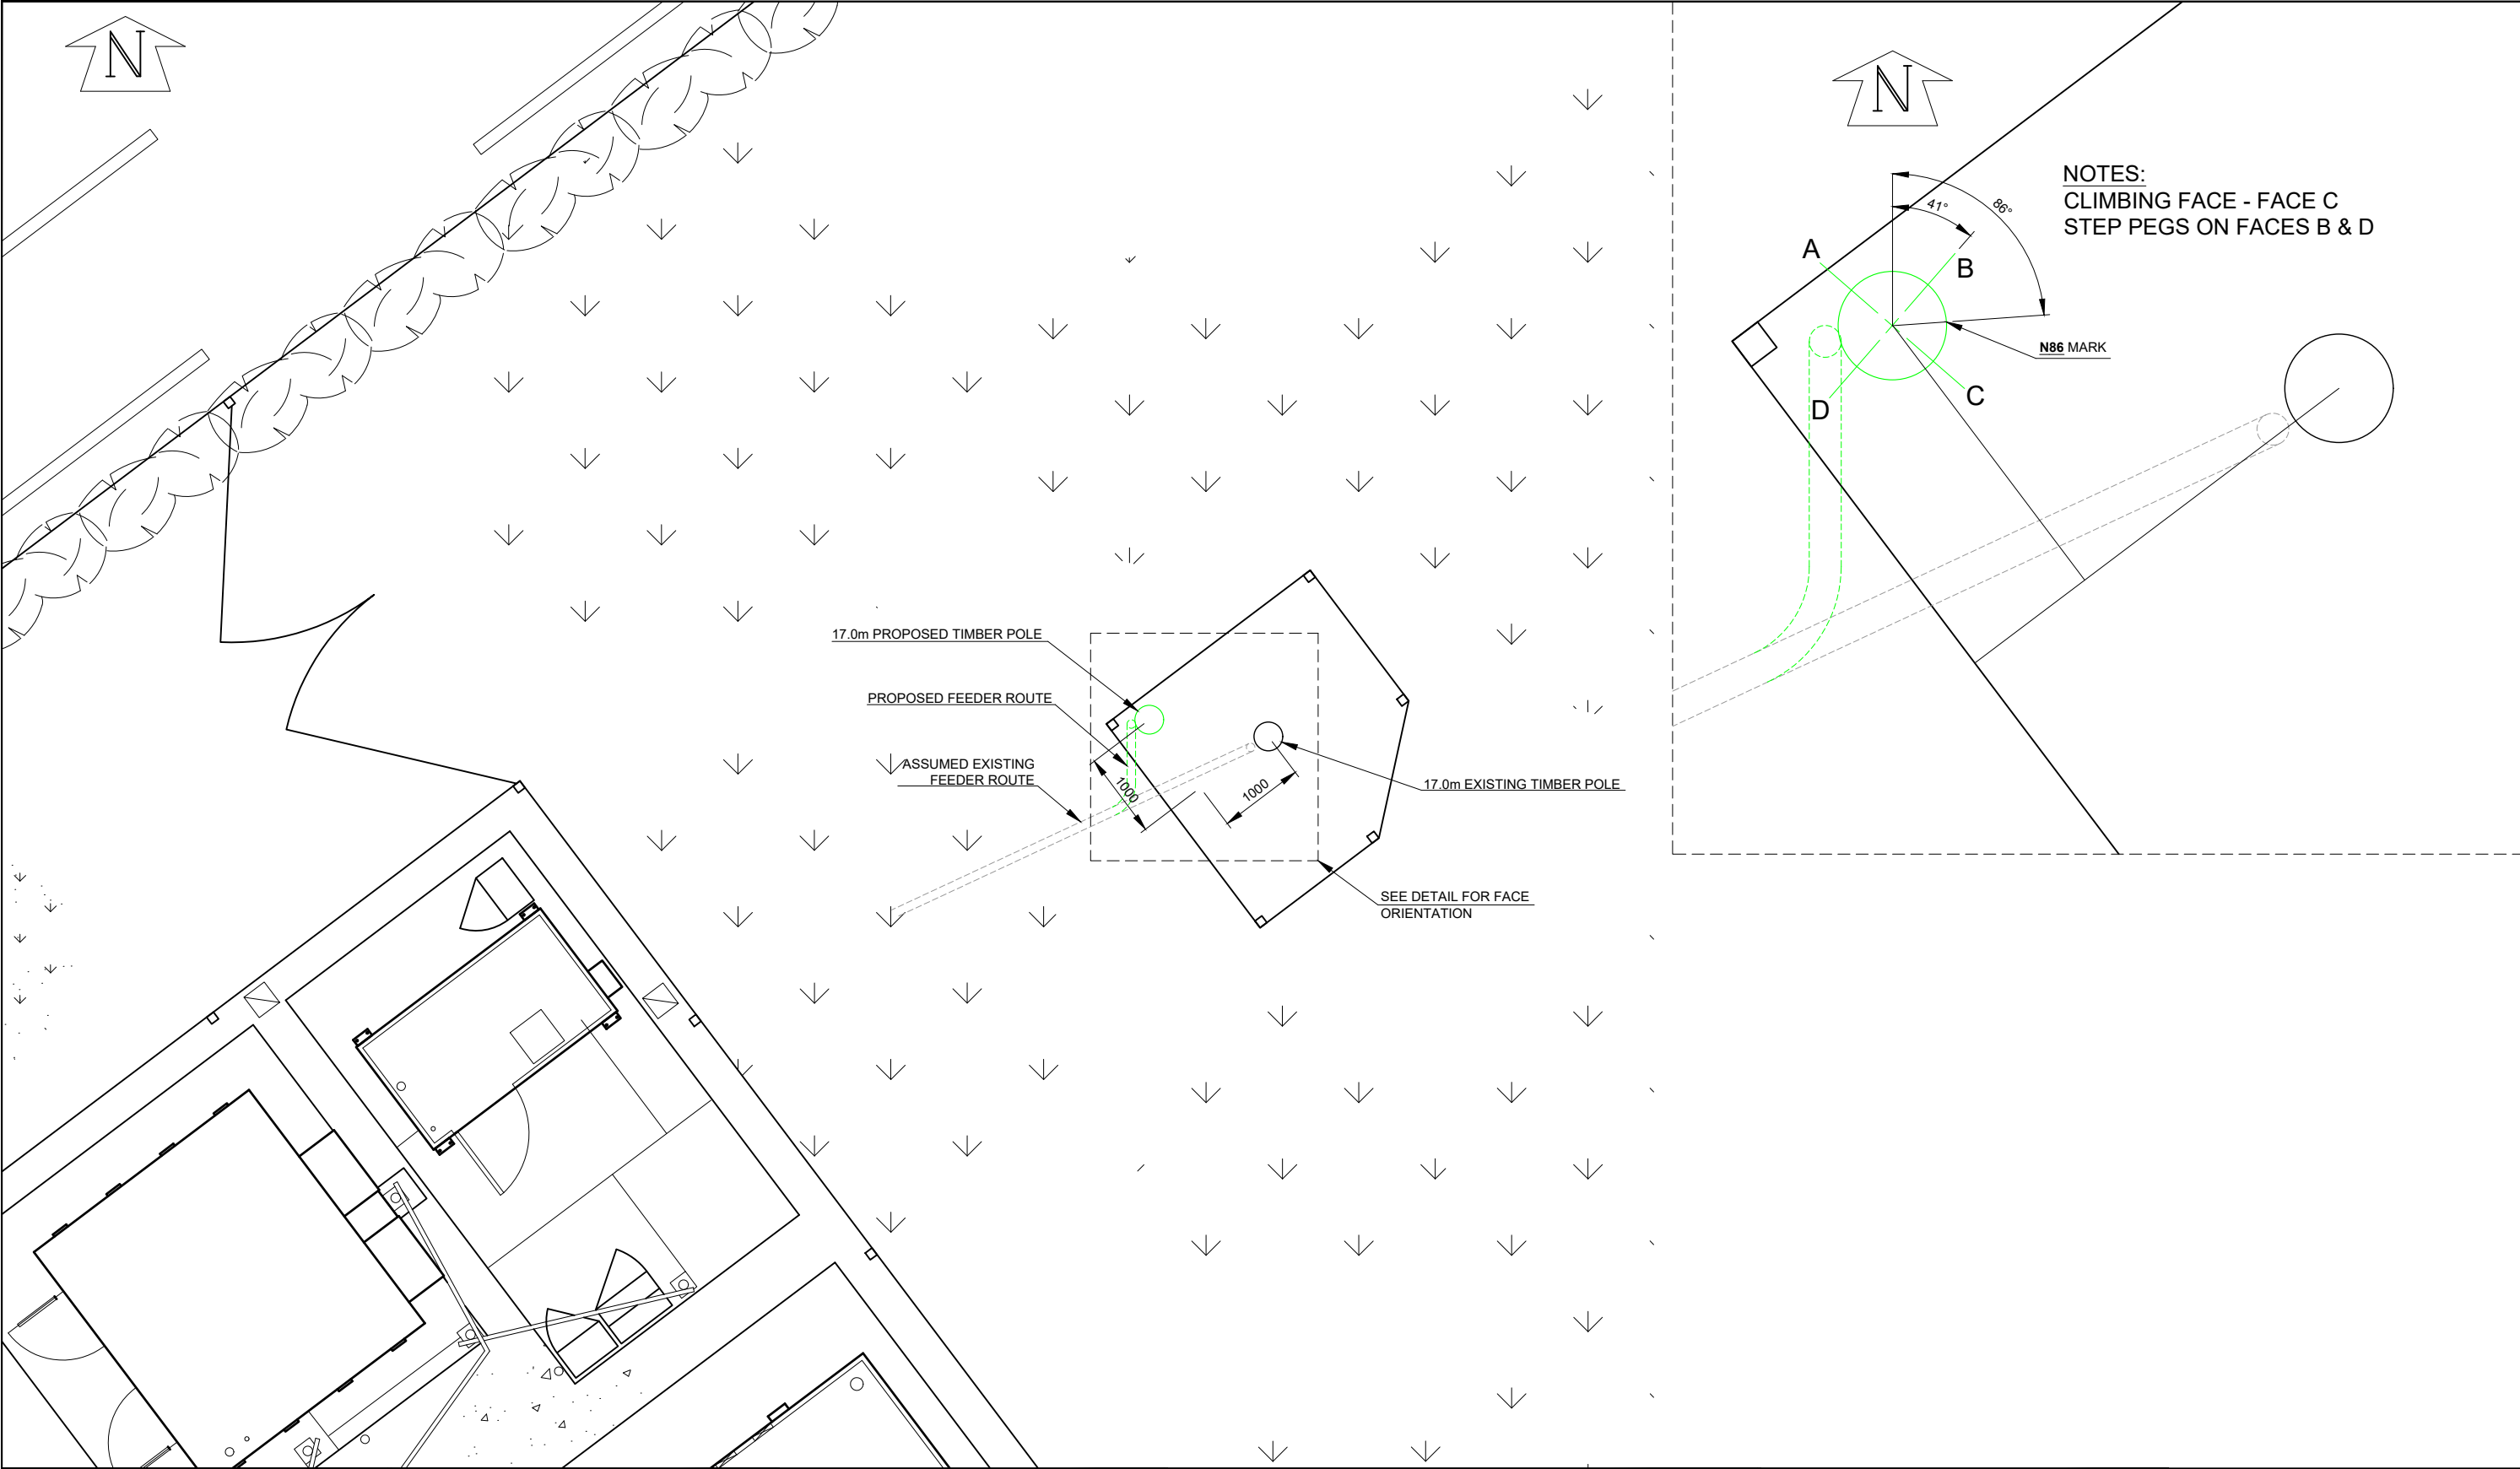


01	FIRST ISSUE	AM	25/04/19
REV	REV	BY	DATE
SCALE AS SHOWN	DRAWN	AM	CHECKED
WHEN PRINTED AT A3	DATE	25/04/19	DATE
ALL DIMENSIONS IN mm UNLESS OTHERWISE STATED.			
THIS DRAWING TO BE READ IN CONJUNCTION WITH			
OTHER RELEVANT DRAWINGS.			

TITLE	LLANDYFRIOG	SITE ADDRESS	ARQIVA SITE
SITE PLAN			CWRWS MILL
			NEWCASTLE EMLYN
			CEREDIGION
			SA44 5TR
		ARQIVA REF.	141023
		DRG No.	100
		REV	01

TITLE	LLANDYFRIOG	SITE ADDRESS	ARQIVA SITE
SITE PLAN			CWRWS MILL
			NEWCASTLE EMLYN
			CEREDIGION
			SA44 5TR
		ARQIVA REF.	141023
		DRG No.	100
		REV	01

TITLE	LLANDYFRIOG	SITE ADDRESS	ARQIVA SITE
SITE PLAN			CWRWS MILL
			NEWCASTLE EMLYN
			CEREDIGION
			SA44 5TR
		ARQIVA REF.	141023
		DRG No.	100
		REV	01

ALL SCALES AS SHOWN WHEN PRINTED AT A3

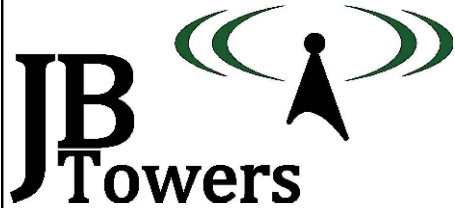

01	FIRST ISSUE			AM	25/04/19
REV	REV			BY	DATE
SCALE AS SHOWN		DRAWN	AM	CHECKED	MP
WHEN PRINTED AT A3		DATE	25/04/19	DATE	25/04/19
		DATE	25/04/19	DATE	25/04/19
ALL DIMENSIONS IN mm UNLESS OTHERWISE STATED. THIS DRAWING TO BE READ IN CONJUNCTION WITH OTHER RELEVANT DRAWINGS.					

TITLE

LLANDYFRIOG

GENERAL ARRANGEMENT

SHEET 1 OF 3

SITE ADDRESS

ARQIVA SITE

CWRWS MILL

NEWCASTLE EMLYN

CEREDIGION

SA44 5TR

ARQIVA REF.



141023

DRG No.

200

REV

01

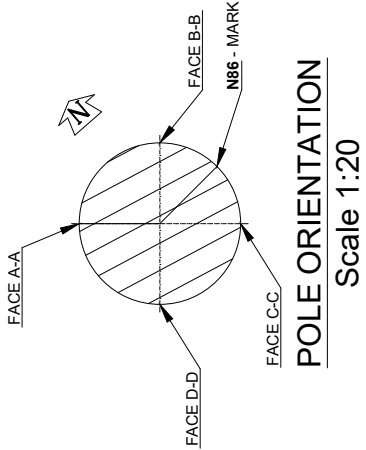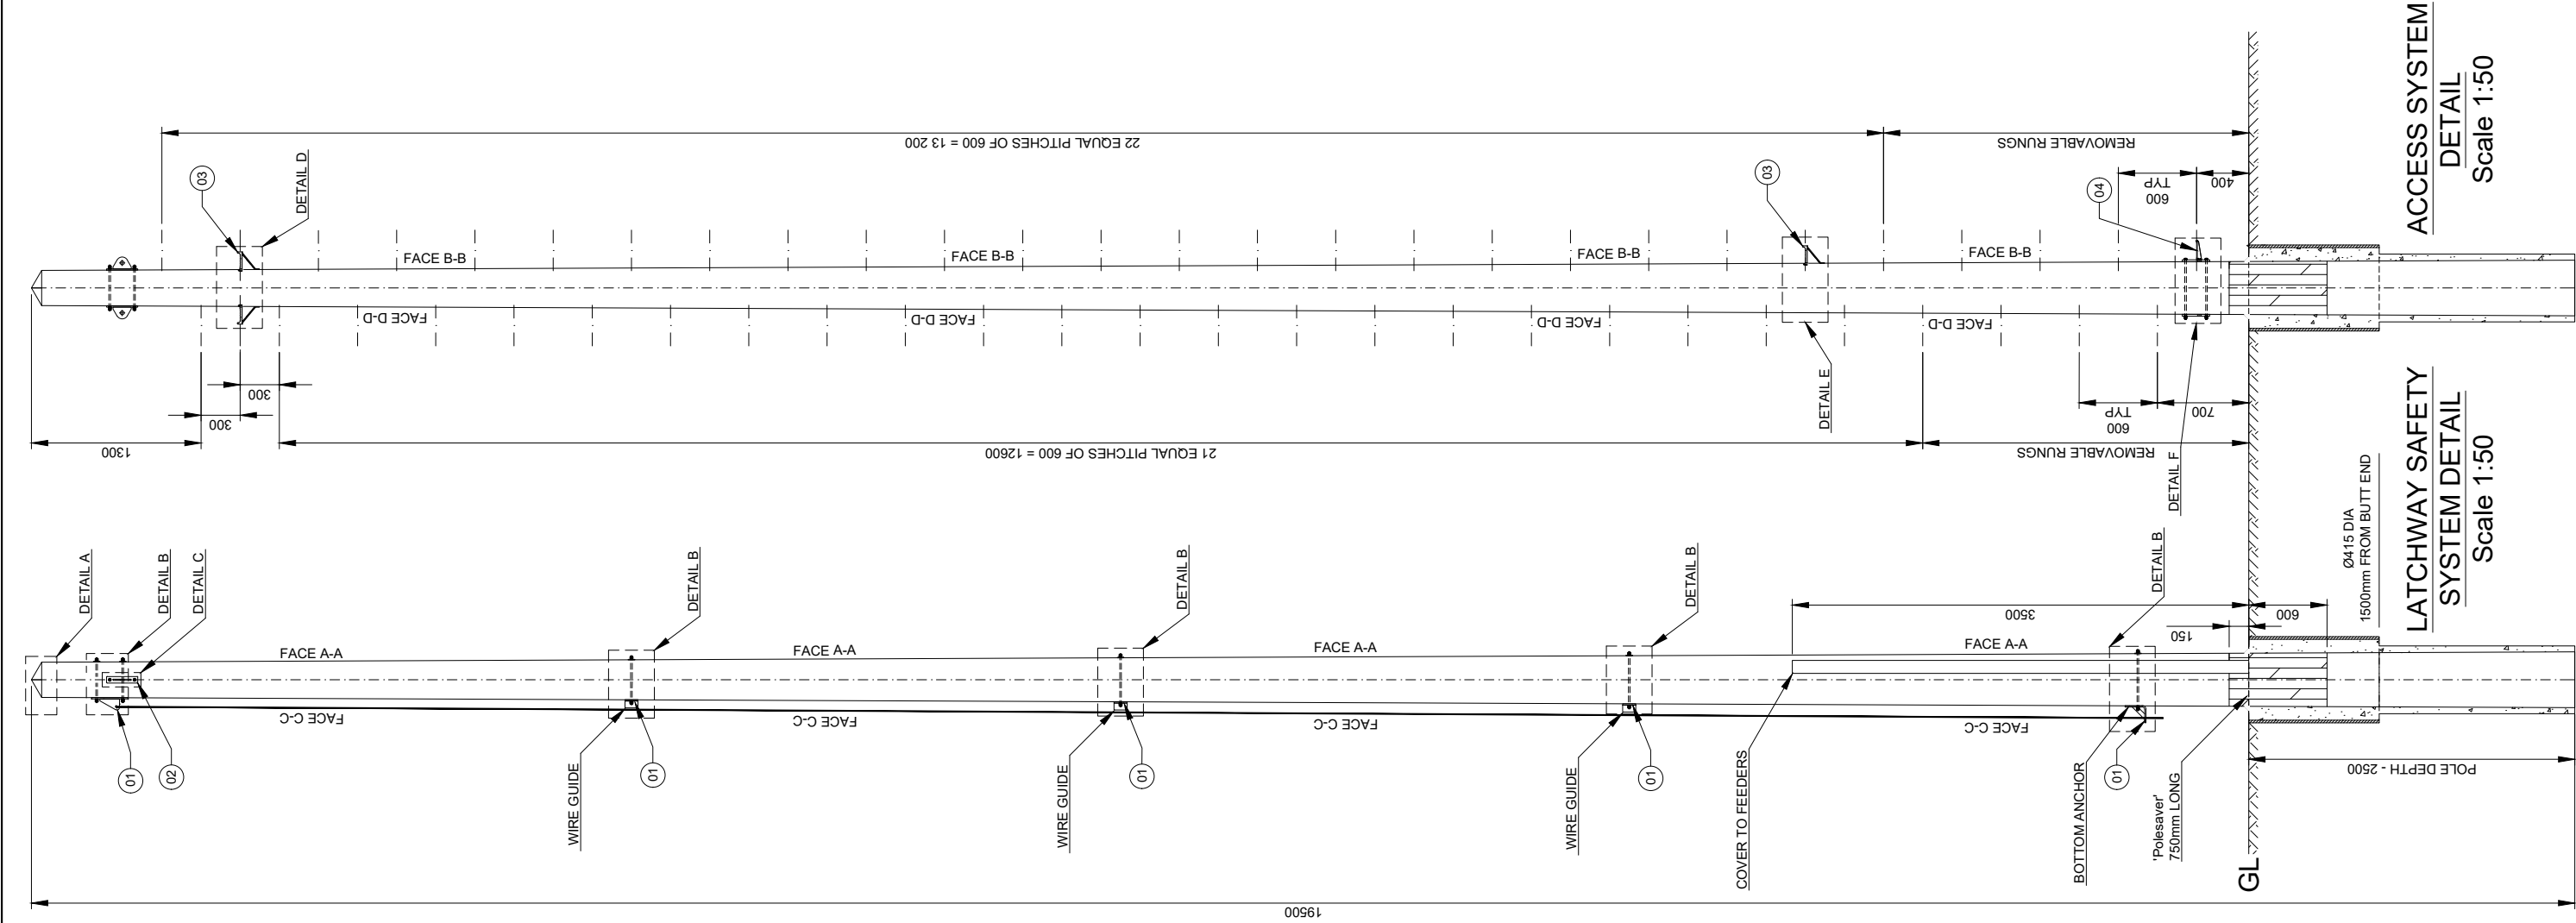

NOTES

1. SEE DRAWING 306 FOR PARTS LIST
2. ALL BOLTS TO BE CUT ON SITE TO EXTEND MAX 10mm BEYOND THE NUT WHEN TIGHTENED UNO.
3. ALL SITE DRILLED HOLE/CUT ENDS TO BE TREATED WITH METALUX 70-40 ZINC PASTE FOLLOWED BY 1 COAT OF 7-42 ZINC ALU OR 70-16 ALUMINIUM SPRAY

TIMBER POLE

1. POLE TO BE SUPPLIED IN ACCORDANCE WITH BS EN14229 & SHALL HAVE MIN. CHARACTERISTIC BENDING STRENGTH OF 30N/mm2 & MIN. YOUNGS MODULUS (PARALLEL TO GRAIN) OF 10KN/mm2.
2. MARKINGS ON FINISHED POLE SHALL BE AT 4m FROM BUTT AND COMPLY WITH BS EN 14229 UNO
3. AS FAR AS PRACTICABLE ALL CUTTING, SCARFING & DRILLING TO BE DONE BEFORE CREOSOTING. IF NOT ALL CUT, DRILLED & SCARFED SURFACES TO BE COATED WITH A MIXTURE OF CREOSOTE & TAR.
4. POLE TO BE PRESSURE IMPREGNATED WITH CREOSOTE IN ACCORDANCE WITH BS EN 14229
5. MINIMUM DIAMETERS
TOP - Ø205mm
BOTTOM - Ø430mm
6. 19.5m LONG POLE TO BE SOURCED BY TRIMMING 20m LONG POLE BY 0.5m AT THE TOP

PLANTING

1. CAT SCANNER IS TO BE USED IN ORDER TO CONFIRM THE POSITIONS OF BURIED SERVICES.
2. 'Perma-Soil Stabiliser' OR A SIMILAR APPROVED SHOULD BE USED IN ACCORDANCE WITH THE MANUFACTURER'S RECOMMENDATION.
3. ANY MATERIAL USED FOR BACK-FILLING IS TO BE OF EQUAL OF BETTER QUALITY THAN THE EXCAVATED MATERIAL.
4. ALL BACK-FILLING MATERIAL IS TO BE PLACED AND COMPACTED IN 150mm THICK LAYERS.
5. TIMBER POLE TO BE PLANTED WITH N86 MARKING AT 4.0m FROM BUTT FACING 86° FROM NORTH (CLOCKWISE)

ACCESS SYSTEM
DETAIL
Scale 1:50

LATCHWAY SAFETY
SYSTEM DETAIL
Scale 1:50



ALL SCALES AS SHOWN WHEN PRINTED AT A3

ALL SCALES AS SHOWN WHEN PRINTED AT A3

01	FIRST ISSUE			AM	25/04/19
REV	REV			BY	DATE
SCALE AS SHOWN WHEN PRINTED AT A3		DRAWN AM DATE 25/04/19	CHECKED MP DATE 25/04/19	APPROVED JBT DATE 25/04/19	
ALL DIMENSIONS IN mm UNLESS OTHERWISE STATED. THIS DRAWING TO BE READ IN CONJUNCTION WITH OTHER RELEVANT DRAWINGS.					


TITLE
LLANDYFRIOG
GENERAL ARRANGEMENT
SHEET 2 OF 3

SITE ADDRESS
ARQIVA SITE
CWRWS MILL
NEWCASTLE EMLYN
CEREDIGION
SA44 5TR

ARQIVA REF.
141023

DRG No.
200

REV
01

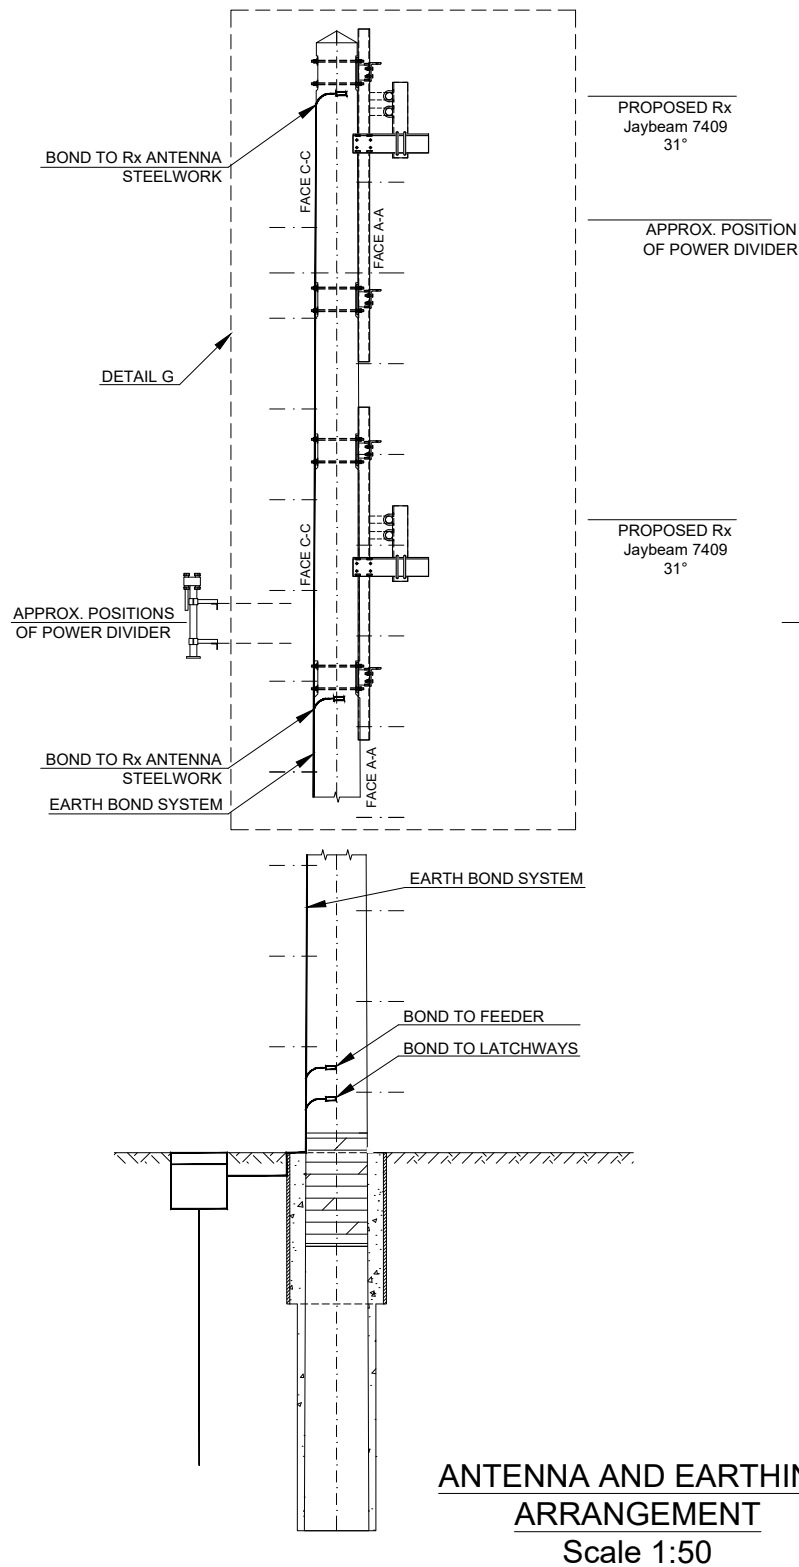

NOTES


1. AS FAR AS IS PRACTICABLE ALL CUTTING SCARFING AND DRILLING TO BE DONE BEFORE CREOSOTING. WHERE THIS IS NOT POSSIBLE ALL CUT, DRILLED, AND SCARFED SURFACES TO BE COATED WITH A MIXTURE OF CREOSOTE AND TAR


FEEDERS

1. SUPPLY OF FEEDERS BY OTHERS LCF78-50 TO Rx ANTENNA
2. FEEDERS FIXED AT 1000mm CENTRES

EARTHING


1. CONNECT EARTH BOND TO NEW EARTHING SYSTEM
2. MAXIMUM VALUE FOR GROUND RESISTANCE TO BE 10 OHMS
3. CABLE OR TAPE TO BE FIXED TO POLE AT 1000mm CENTRES
4. EARTHING SHOULD COMPLY WITH ARQIVA'S DOCUMENT BOS147

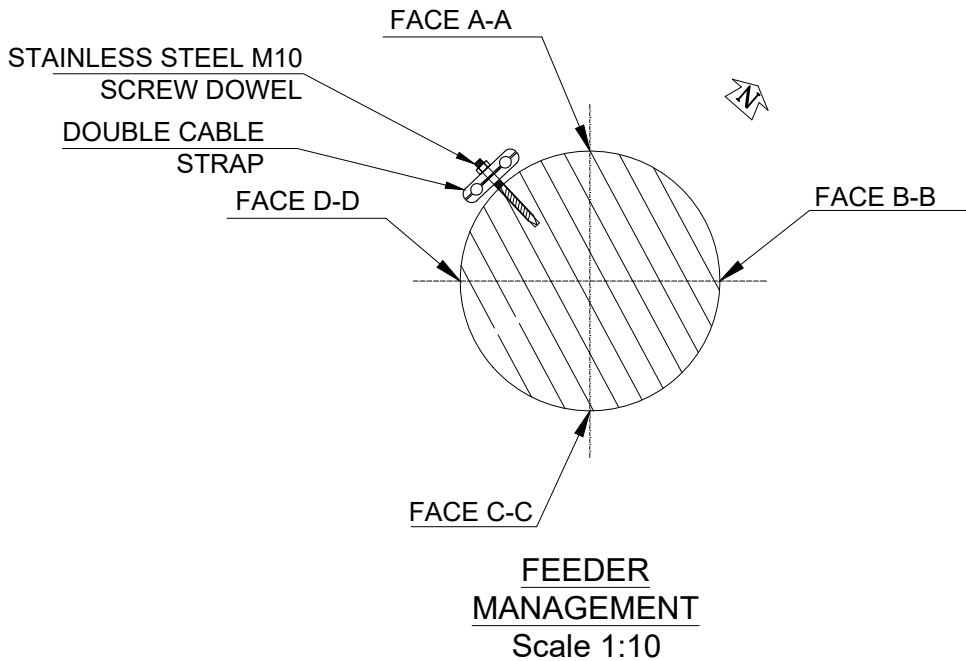

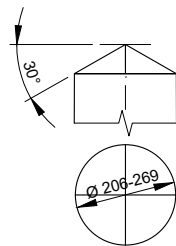


- NOTES:
1. A SINGLE COAT OF TIMBER COMPATIBLE BITUMINOUS PAINT (E.G. BIRD BRAND BLACK BITUMINOUS PAINT OR SIMILAR APPROVED PRODUCT) TO BE APPLIED TO THE UPPER SURFACES AT THE TOP OF THE POLE.
 2. PAINT TO BE APPLIED ON SITE JUST BEFORE ERECTION
- FORM: 4 WAY PYRAMID / CONE


DETAIL A - TIMBER POLE TOP
Scale 1:20

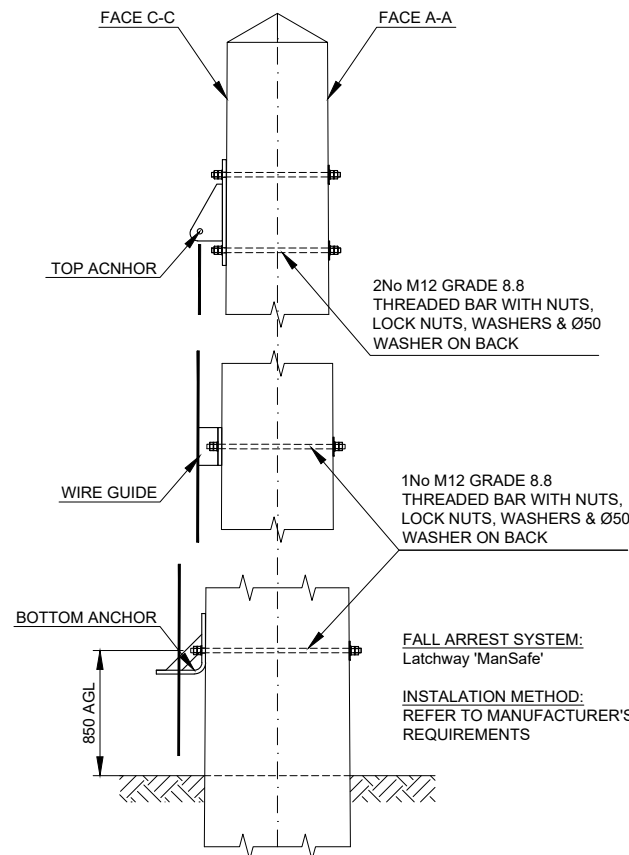


DETAIL B - FALL ARREST SYSTEM
Scale 1:20

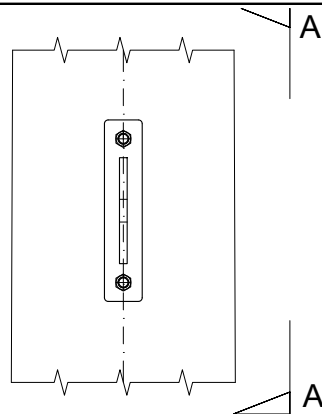

DETAIL C - FALL ARREST
ATTACHMENT POINT
Scale 1:10

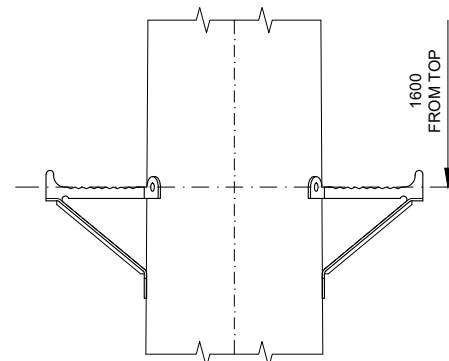


DETAIL D - ANTENNA
ACCESS CLIMBING STEP
Scale 1:10

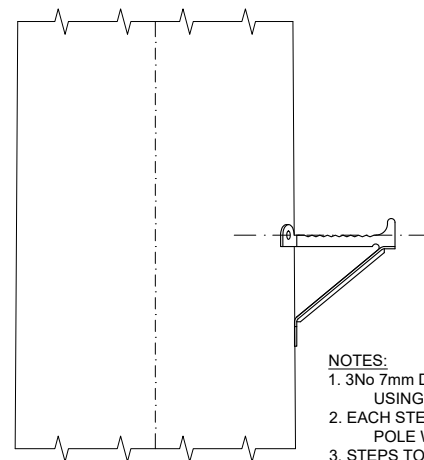


DETAIL E - PERMANENT
CLIMBING STEPS
Scale 1:10


- NOTES:
1. 3No 7mm DIA 70mm LONG PILOT HOLES TO BE DRILLED USING THE STEP AS A TEMPLATE
 2. EACH STEP SHOULD BE FIXED TO THE TIMBER POLE WITH 3No 10mm COACH SCREWS 75mm LONG
 3. STEPS TO BE INSTALLED ON FACES B-B & D-D ONLY

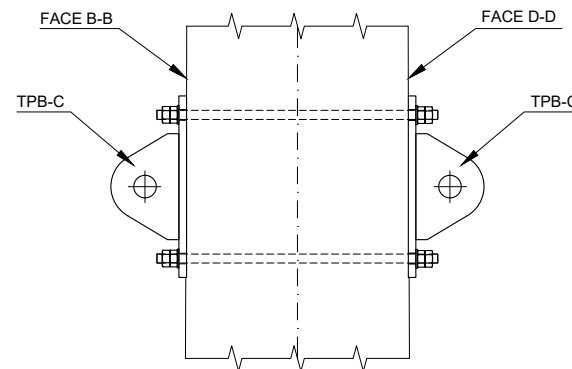

VIEW A-A
Scale 1:10

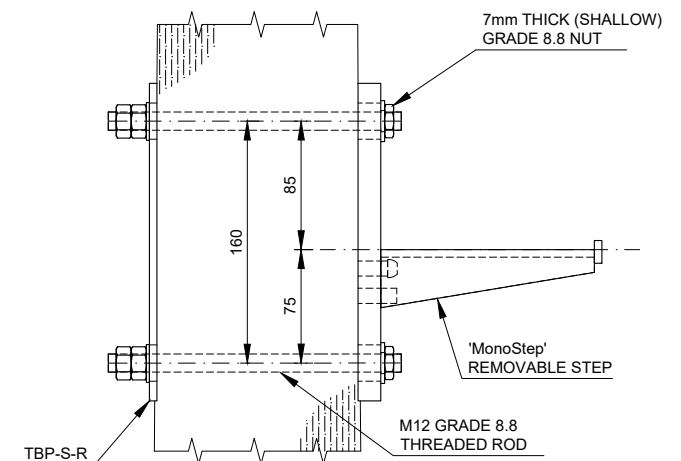

DETAIL F - REMOVABLE
CLIMBING STEPS
Scale 1:5

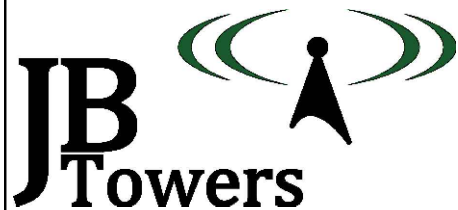


01	FIRST ISSUE	AM	25/04/19
REV	REV	BY	DATE
SCALE AS SHOWN WHEN PRINTED AT A3	DRAWN DATE 25/04/19	CHECKED DATE 25/04/19	APPROVED DATE 25/04/19
ALL DIMENSIONS IN mm UNLESS OTHERWISE STATED. THIS DRAWING TO BE READ IN CONJUNCTION WITH OTHER RELEVANT DRAWINGS.			

TITLE		SITE ADDRESS	
LLANDYFRIOG		ARQIVA SITE	
GENERAL ARRANGEMENT		CWRWS MILL	
SHEET 3 OF 3		NEWCASTLE EMLYN	
		CEREDIGION	
		SA44 5TR	
ARQIVA REF. 141023		DRG No. 200	REV 01

ALL SCALES AS SHOWN WHEN PRINTED AT A3



ALL SCALES AS SHOWN WHEN PRINTED AT A3

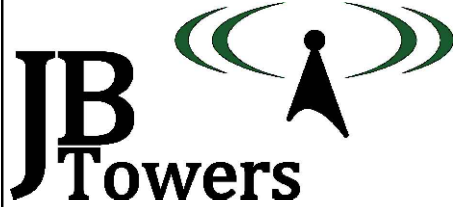

01	FIRST ISSUE			AM	25/04/19
REV	REV			BY	DATE
SCALE AS SHOWN		DRAWN	AM	CHECKED	MP
WHEN PRINTED AT A3		DATE	25/04/19	DATE	25/04/19
				APPROVED	JBT
				DATE	25/04/19
ALL DIMENSIONS IN mm UNLESS OTHERWISE STATED. THIS DRAWING TO BE READ IN CONJUNCTION WITH OTHER RELEVANT DRAWINGS.					

TITLE

LLANDYFRIOG

TIMBER POLE HOLE SET OUT

SHEET 1 OF 2

SITE ADDRESS

ARQIVA SITE

CWRWS MILL

NEWCASTLE EMLYN

CEREDIGION

SA44 5TR

ARQIVA REF.







141023

DRG No.

201

REV

01

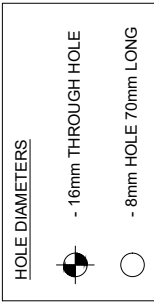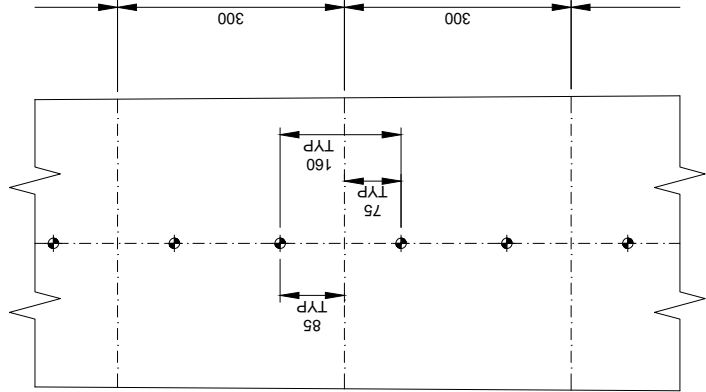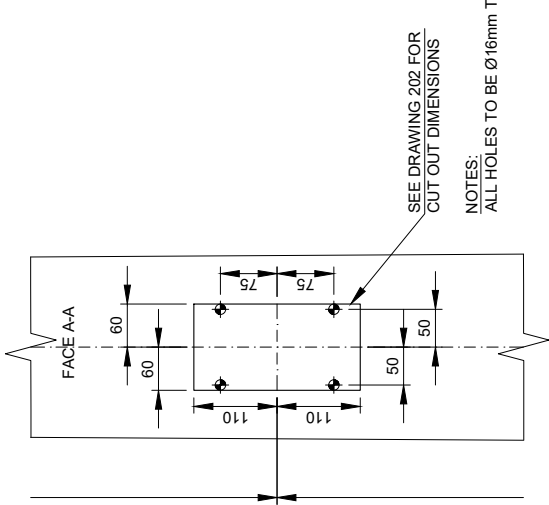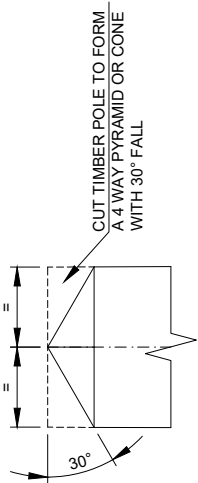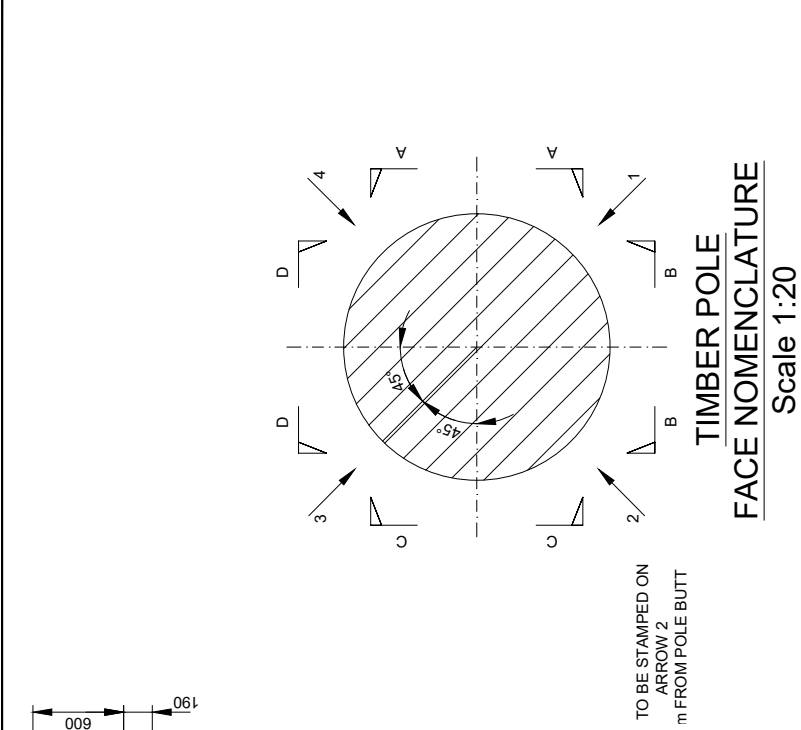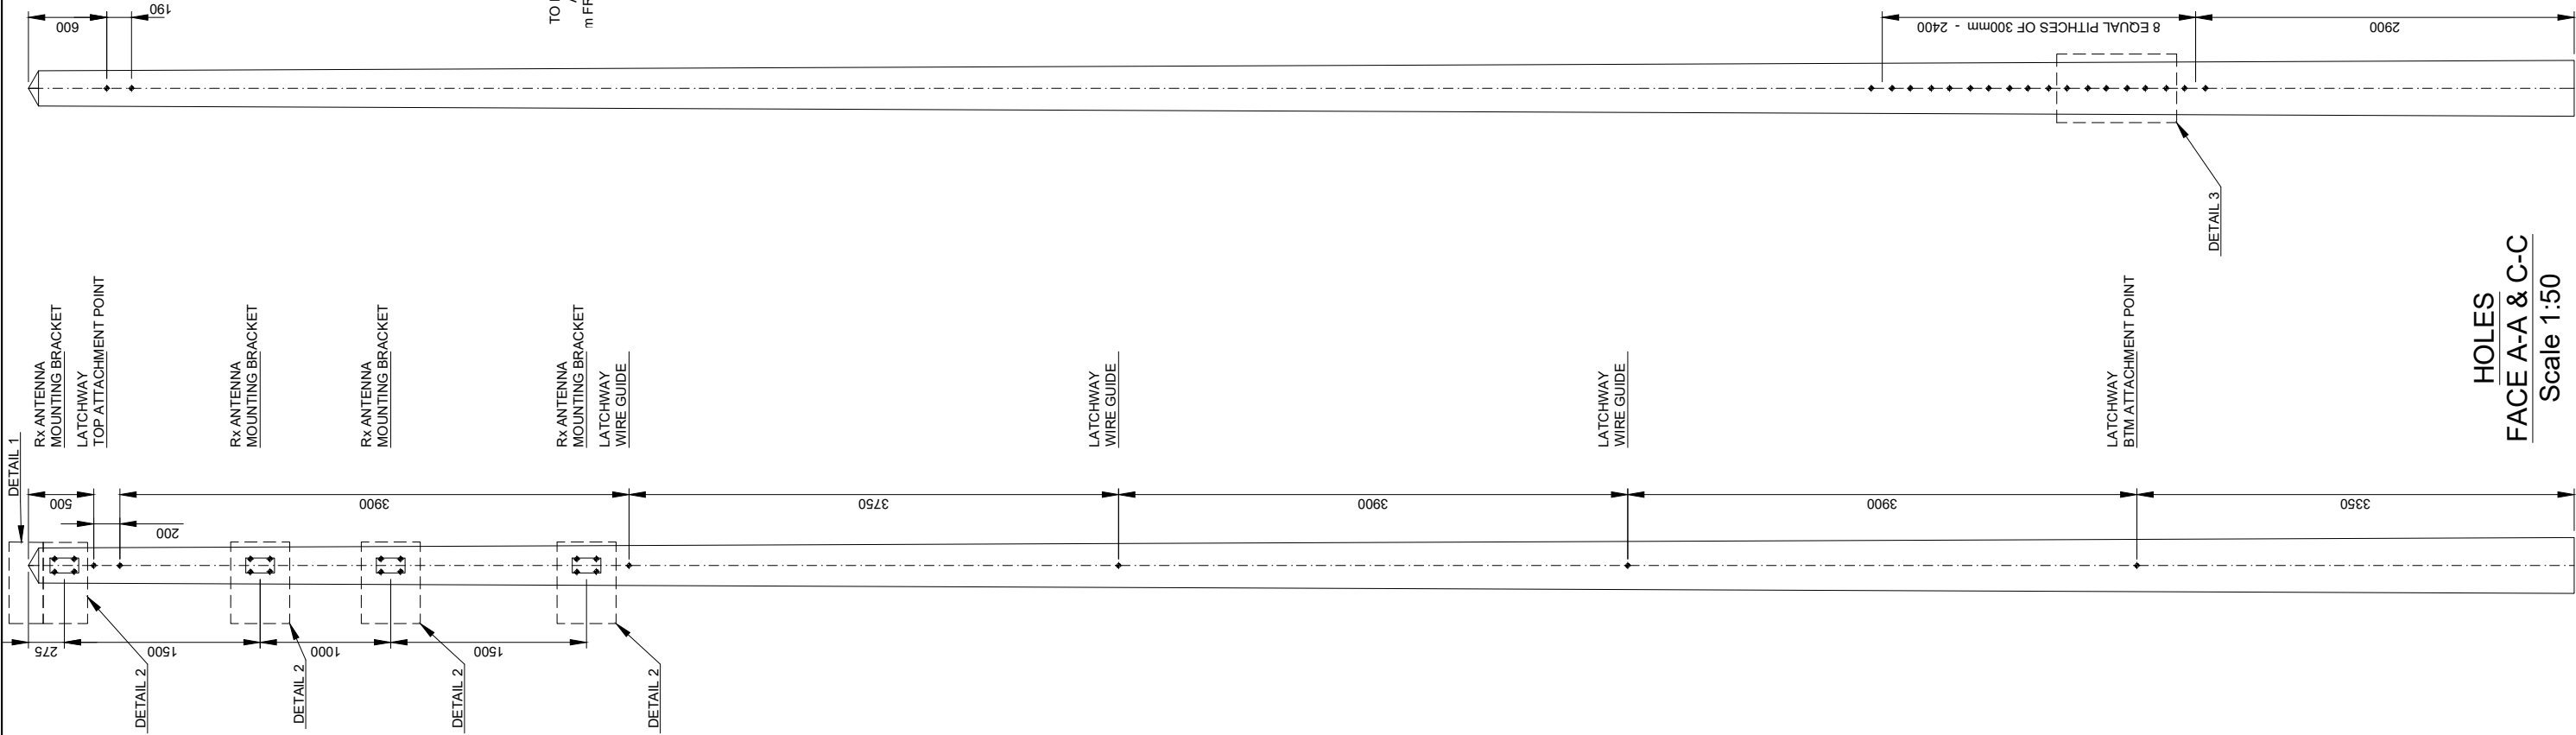


HOLES
FACE B-B & D-D

Scale 1:50



ALL SCALES AS SHOWN WHEN PRINTED AT A3

ALL SCALES AS SHOWN WHEN PRINTED AT A3

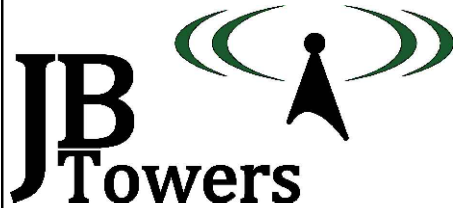

01	FIRST ISSUE			AM	25/04/19
REV	REV			BY	DATE
SCALE AS SHOWN WHEN PRINTED AT A3		DRAWN AM DATE 25/04/19	CHECKED MP DATE 25/04/19	APPROVED JBT DATE 25/04/19	
ALL DIMENSIONS IN mm UNLESS OTHERWISE STATED. THIS DRAWING TO BE READ IN CONJUNCTION WITH OTHER RELEVANT DRAWINGS.					

TITLE

LLANDYFRIOG

TIMBER POLE HOLE SET OUT

SHEET 2 OF 2

SITE ADDRESS

ARQIVA SITE

CWRWS MILL

NEWCASTLE EMLYN

CEREDIGION

SA44 5TR

ARQIVA REF.


141023

DRG No.

201

REV


01

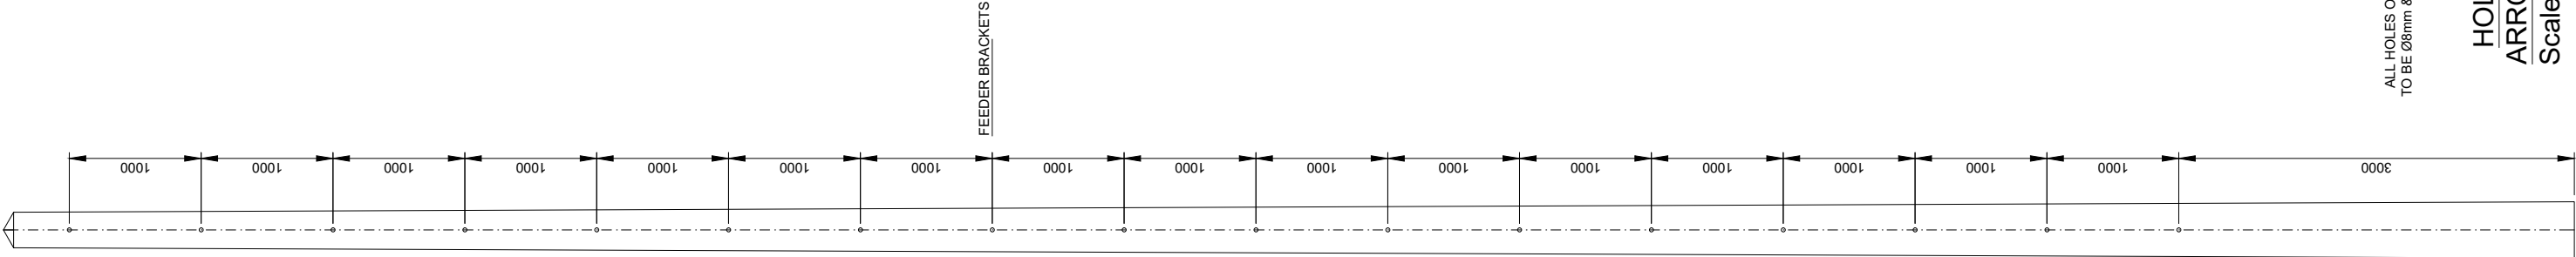

FEEDER BRACKETS

ALL HOLES ON ARROW 4
TO BE Ø8mm & 70mm LONG

HOLES
ARROW 4
Scale 1:50

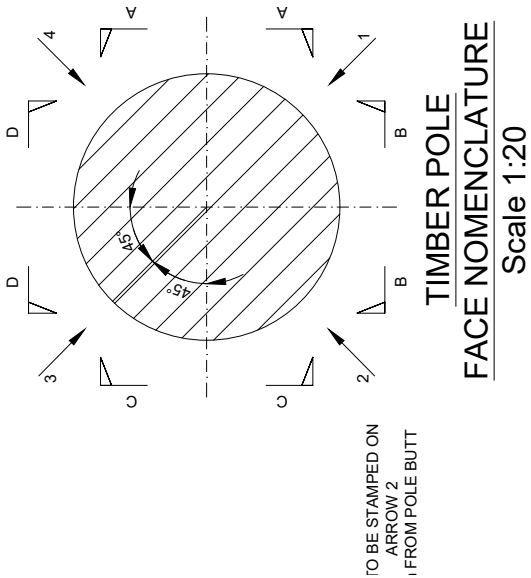

TO BE STAMPED ON
ARROW 2
FROM POLE BUTT

TIMBER POLE
FACE NOMENCLATURE
Scale 1:20





ALL SCALES AS SHOWN WHEN PRINTED AT A3

ALL SCALES AS SHOWN WHEN PRINTED AT A3

01	FIRST ISSUE			AM	25/04/19
REV	REV			BY	DATE
SCALE AS SHOWN		DRAWN	AM	CHECKED	MP
WHEN PRINTED AT A3		DATE	25/04/19	DATE	25/04/19
		APPROVED	JBT	DATE	25/04/19
ALL DIMENSIONS IN mm UNLESS OTHERWISE STATED. THIS DRAWING TO BE READ IN CONJUNCTION WITH OTHER RELEVANT DRAWINGS.					

TITLE		SITE ADDRESS	
LLANDYFRIOG		ARQIVA SITE	
TIMBER POLE CUT OUT		CWRWS MILL	
DETAIL		NEWCASTLE EMLYN	
		CEREDIGION	
		SA44 5TR	
ARQIVA REF.		DRG No.	REV
141023		202	01

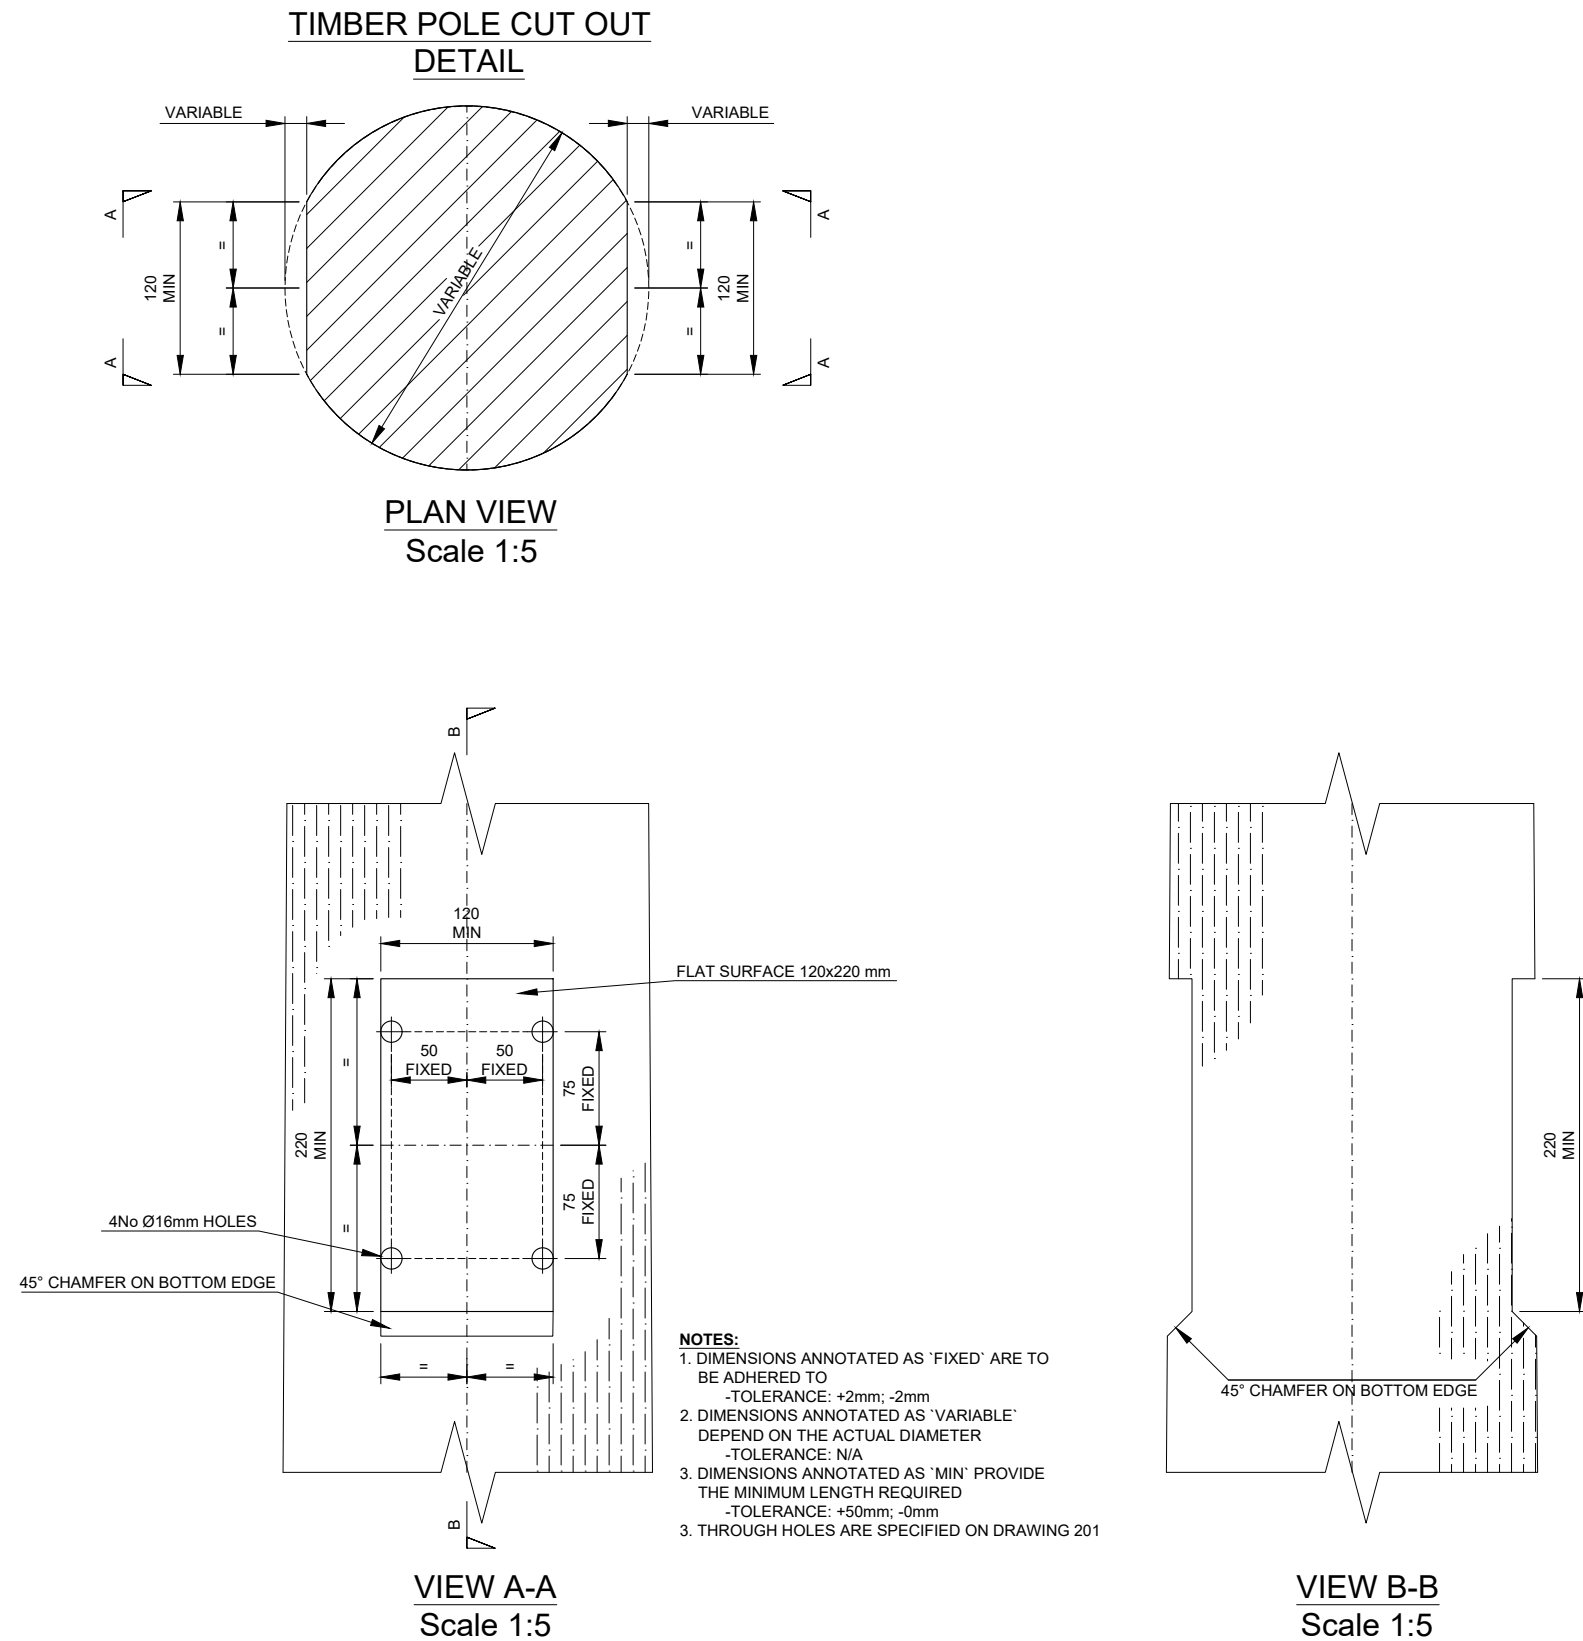

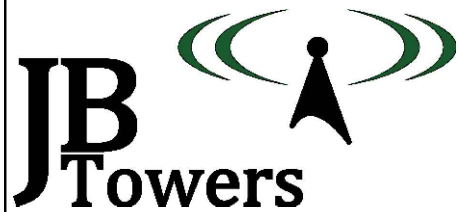


01	FIRST ISSUE			AM	25/04/19
REV	REV			BY	DATE
SCALE AS SHOWN		DRAWN	AM	CHECKED	MP
WHEN PRINTED AT A3		DATE	25/04/19	DATE	25/04/19
		DATE	25/04/19	DATE	25/04/19
ALL DIMENSIONS IN mm UNLESS OTHERWISE STATED. THIS DRAWING TO BE READ IN CONJUNCTION WITH OTHER RELEVANT DRAWINGS.					

TITLE
ANTENNA MOUNT
DETAIL G

SITE ADDRESS
ARQIVA SITE
CWRWS MILL
NEWCASTLE EMLYN
CEREDIGION
SA44 5TR


ARQIVA REF. 141023	DRG No. 203	REV 01
-----------------------	----------------	-----------

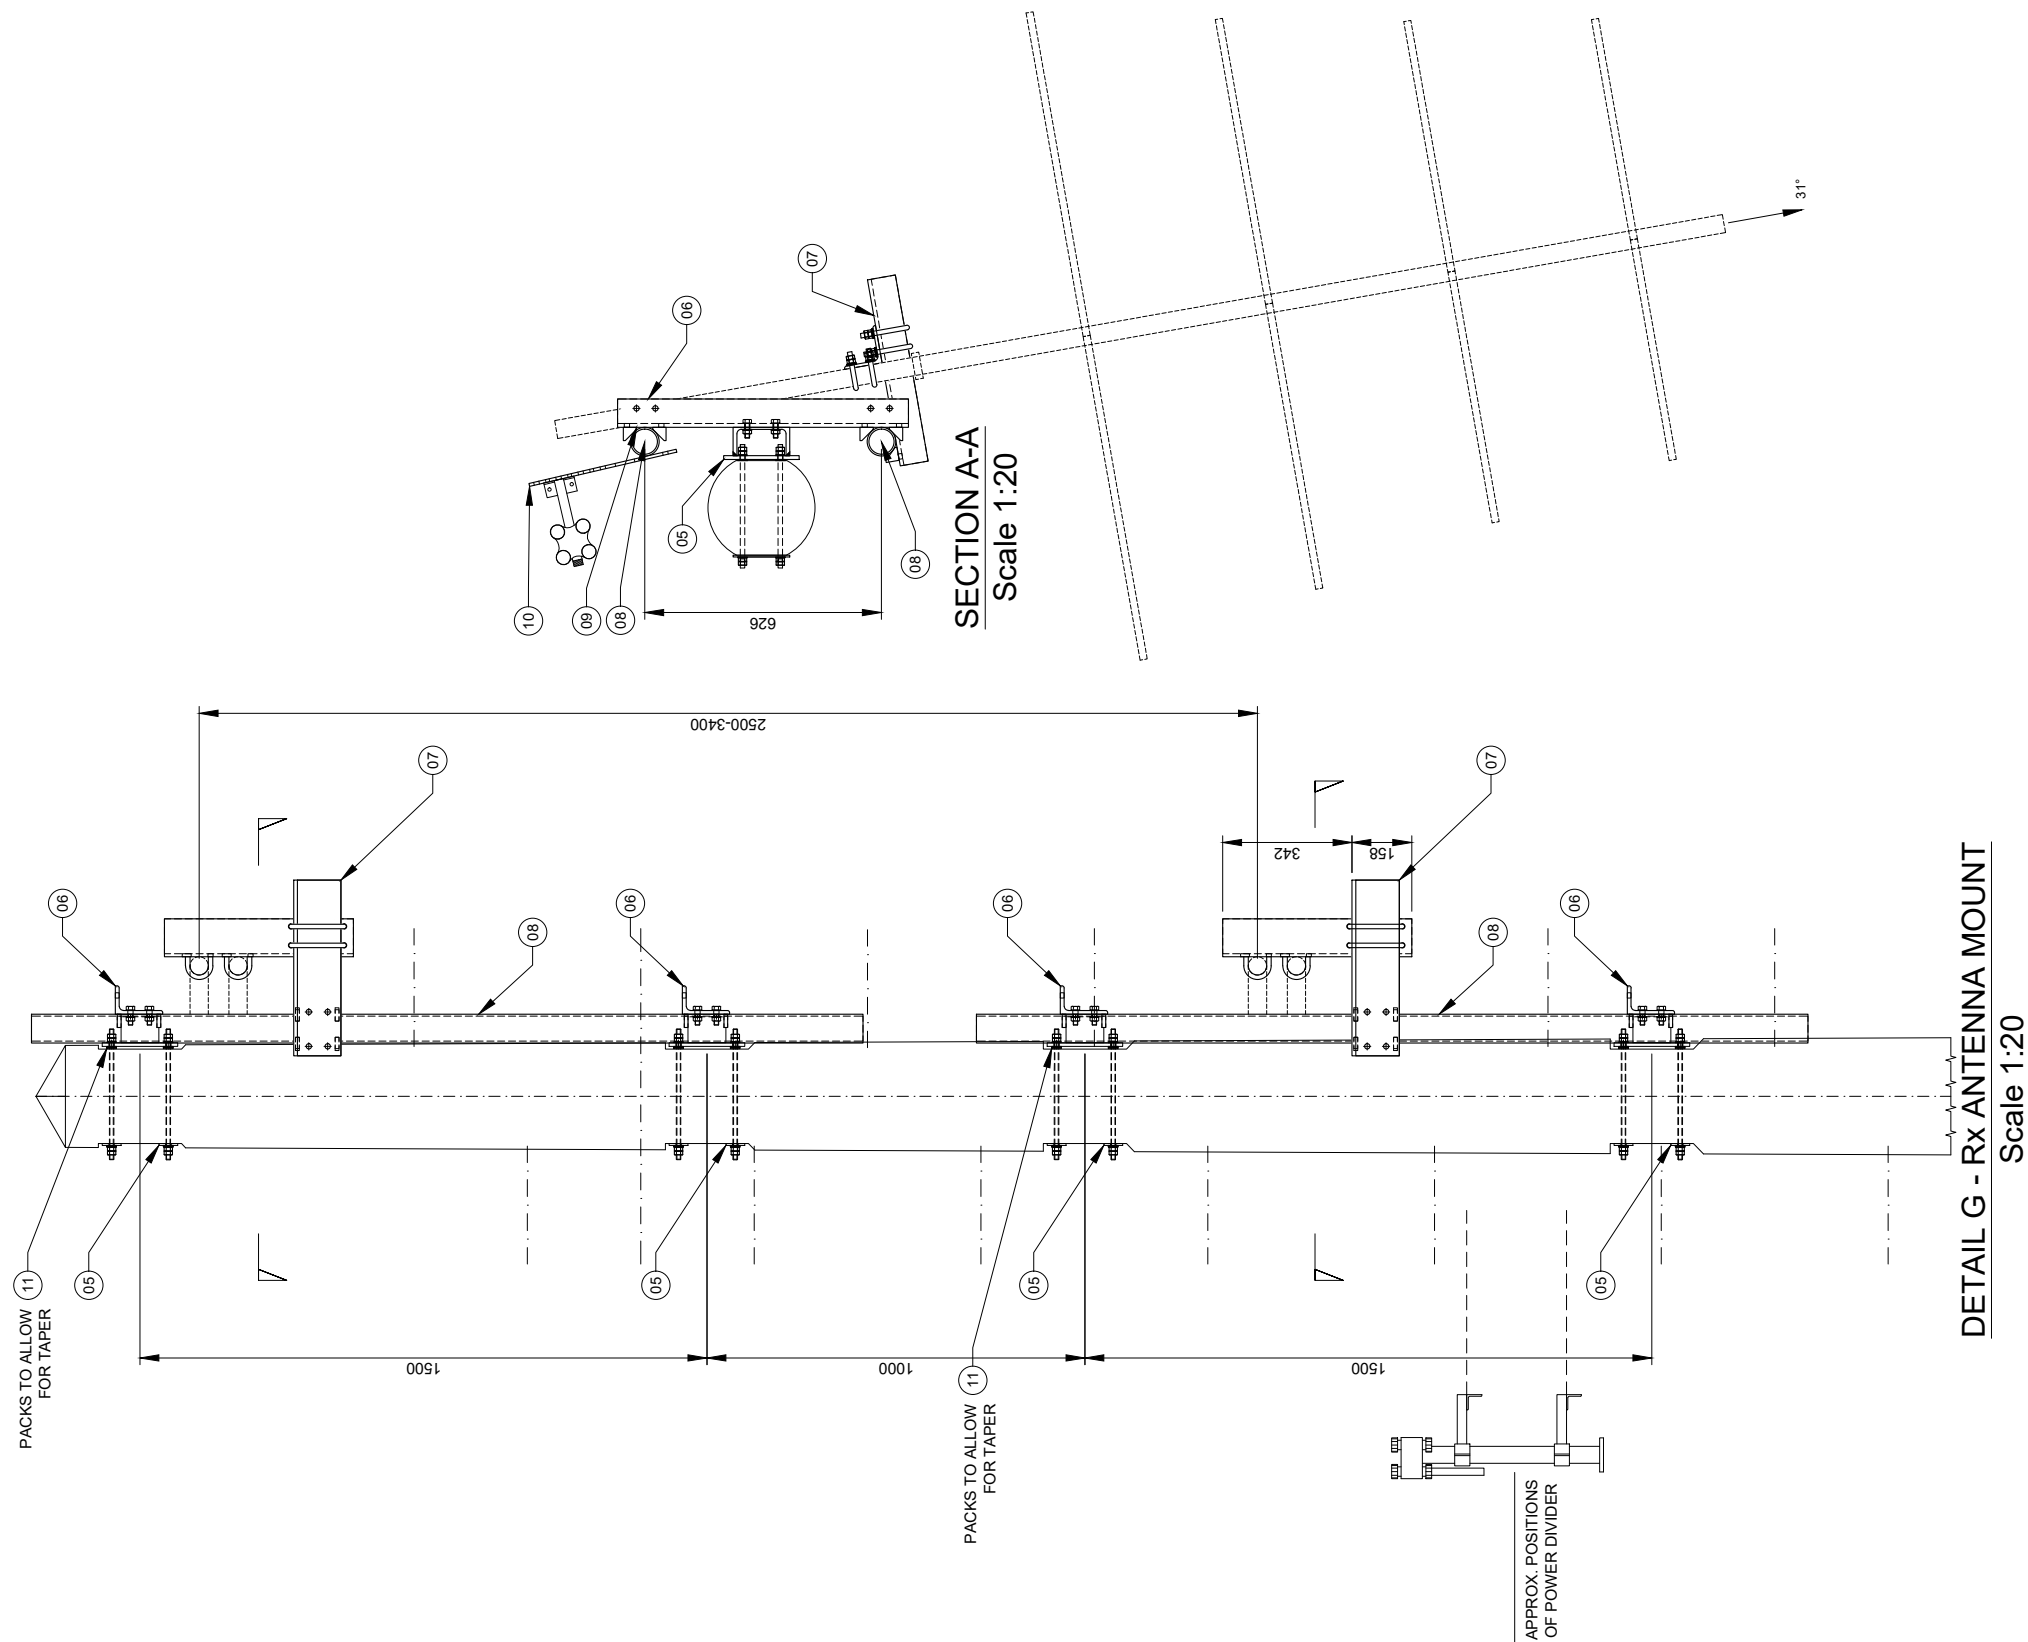

ALL SCALES AS SHOWN WHEN PRINTED AT A3




ALL SCALES AS SHOWN WHEN PRINTED AT A3

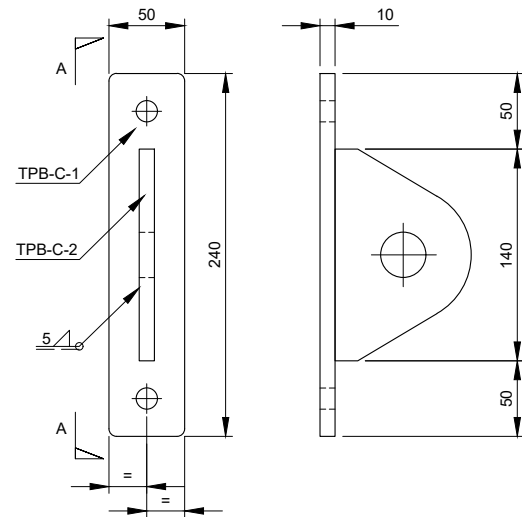


PART TPB-C
Scale 1:5


VIEW A-A
Scale 1:5

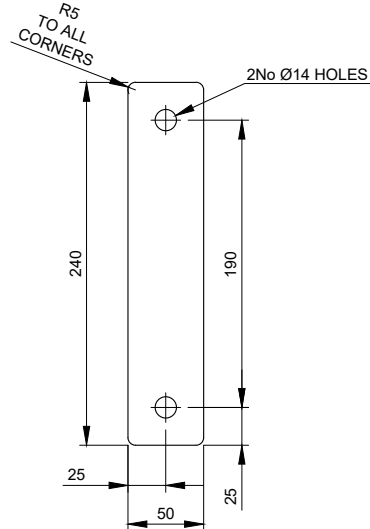

TPB-C-1 - 10mm THICK
Scale 1:5

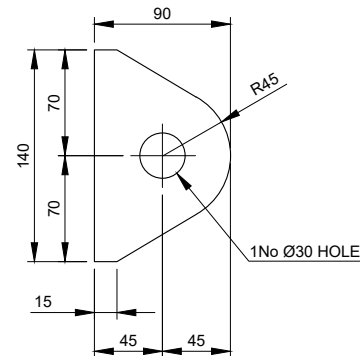


TPB-C-2 - 10mm THICK
Scale 1:5

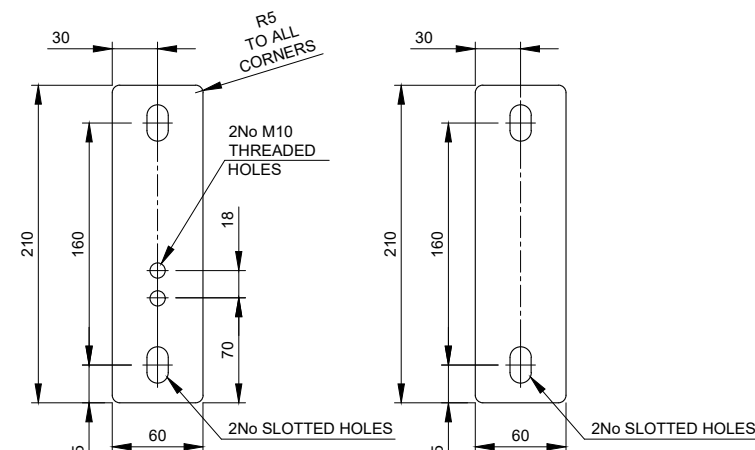

PART TPS-R-1
Scale 1:5

PART TPS-R-2
Scale 1:5

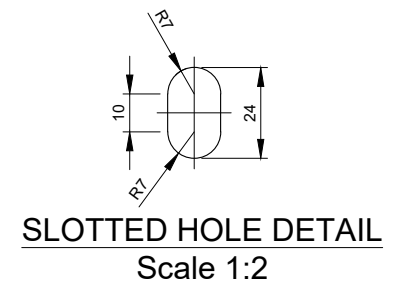

Parts list for TPS-R


Item	Part	Quantity	Part description	Length	Material	Weight
01	TPS-R-1	1	210x60x15mm	N/A	S275J0	1.48 kg
02	TPS-R-2	1	210x60x5mm	N/A	S275J0	0.49 kg
03	STUDS	2	M12 STUDDING	500mm	GRADE 8.8	0.44 kg
04	NUT-S	2	M12 SHALLOW NUT	N/A	GRADE 8.8	-
05	NUT	4	M12 NUT	N/A	GRADE 8.8	-
06	WSH	4	M12 WASHER	N/A	GRADE 8.8	-
Total Weight:						2.85 kg

- All steel hot dip galvanized
- For fabrication notes see drawing 304

Parts list for TPB-C

Item	Part	Quantity	Part description	Length	Material	Weight
01	TPB-C-1	1	240x50x10mm	N/A	S275J0	0.94 kg
02	TPB-C-2	1	140x90x10mm	N/A	S275J0	0.99 kg
03	STUDS	1	M12 STUDDING	350mm	GRADE 8.8	0.31 kg
Total Weight:						2.24 kg

- All steel hot dip galvanized
- Each STUD to be supplied with 4 Full Nuts, 2 Flat Washers and 2 Spring Washers
- For fabrication notes see drawing 304

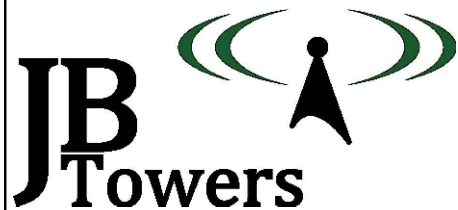







01	FIRST ISSUE	AM	25/04/19
REV	REV	BY	DATE
SCALE AS SHOWN	DRAWN	CHECKED	APPROVED
WHEN PRINTED AT A3	AM	MP	JBT
DATE	25/04/19	DATE	25/04/19
DATE	25/04/19	DATE	25/04/19
ALL DIMENSIONS IN mm UNLESS OTHERWISE STATED. THIS DRAWING TO BE READ IN CONJUNCTION WITH OTHER RELEVANT DRAWINGS.			

TITLE		SITE ADDRESS	
ATTACHMENT POINT & TEMPORARY STEP DETAILS		ARQIVA SITE CWRWS MILL NEWCASTLE EMLYN CEREDIGION SA44 5TR	
PARTS: TPB-C; TPS-R		ARQIVA REF. 141023	DRG No. 300
		REV 01	

ALL SCALES AS SHOWN WHEN PRINTED AT A3




ALL SCALES AS SHOWN WHEN PRINTED AT A3

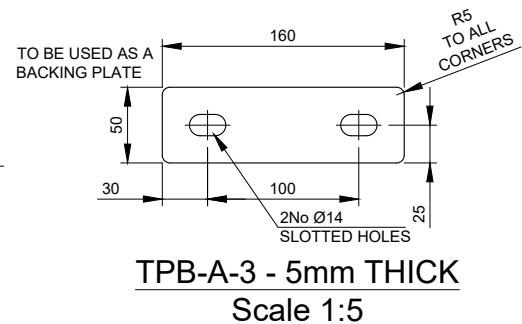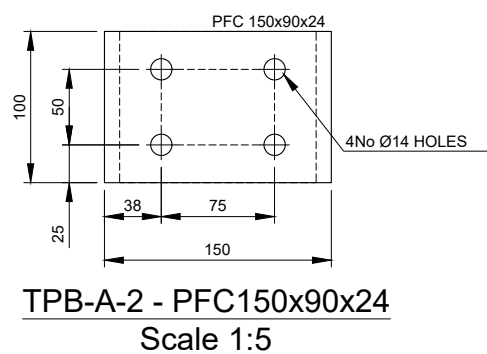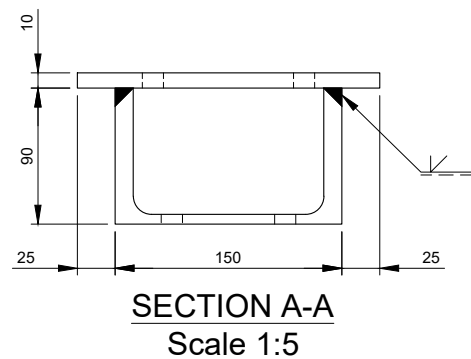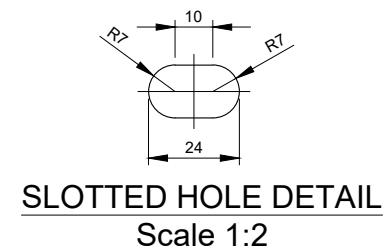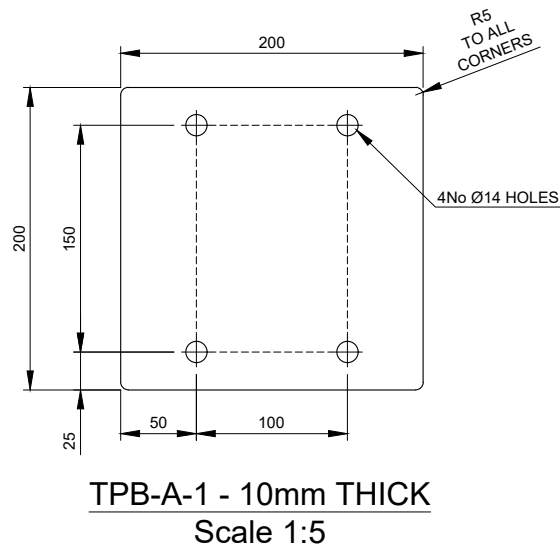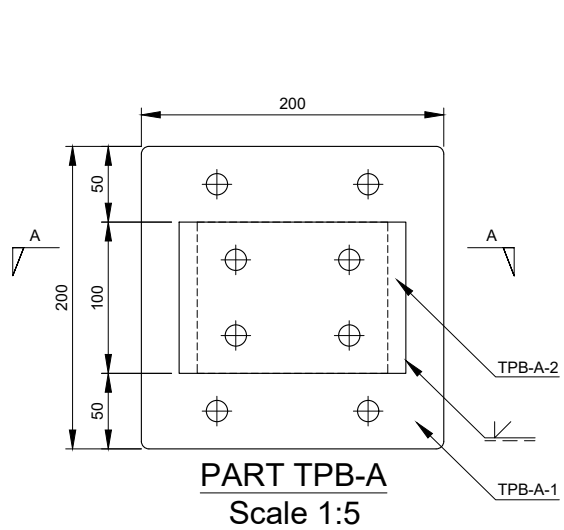

Parts list for TPB-A

Item	Part	Quantity	Part description	Length	Material	Weight
01	TPB-A-1	1	220x200x10mm	N/A	S275J0	3.45 kg
02	TPB-A-2	1	PFC 150x90x24	100mm	S275J0	2.40 kg
03	TPB-A-3	2	160x50x5mm	N/A	S275J0	0.31 kg
04	STUDS	4	M12 STUDDING	400mm	GRADE 8.8	0.34 kg
05	U-BOLT	2	M12 U-BOLT FOR CHS 60.3mm	N/A	GRADE 8.8	-
Total Weight:						7.83 kg

- All steel hot dip galvanized
- Each STUD & U-BOLT to be supplied with 4 Full Nuts, 2 Flat Washers and 2 Spring Washers
- Each BOLT to be supplied with 1 Full Nut, 1 Form E FLat Washer and 1 Spring Washer
- For fabrication notes see drawing 304

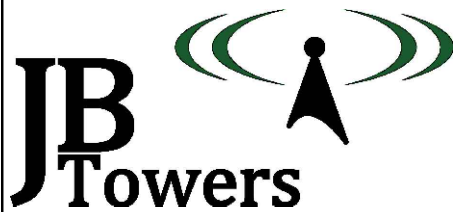

01	FIRST ISSUE			AM	25/04/19
REV	REV			BY	DATE
SCALE AS SHOWN	DRAWN	AM	CHECKED	MP	APPROVED
WHEN PRINTED AT A3	DATE	25/04/19	DATE	25/04/19	DATE
ALL DIMENSIONS IN mm UNLESS OTHERWISE STATED. THIS DRAWING TO BE READ IN CONJUNCTION WITH OTHER RELEVANT DRAWINGS.					


TITLE
STEELWORK BRACKET
PART: TPB-A

SITE ADDRESS
ARQIVA SITE
CWRWS MILL
NEWCASTLE EMLYN
CEREDIGION
SA44 5TR



ARQIVA REF.
141023
DRG No.
301
REV
01

ALL SCALES AS SHOWN WHEN PRINTED AT A3



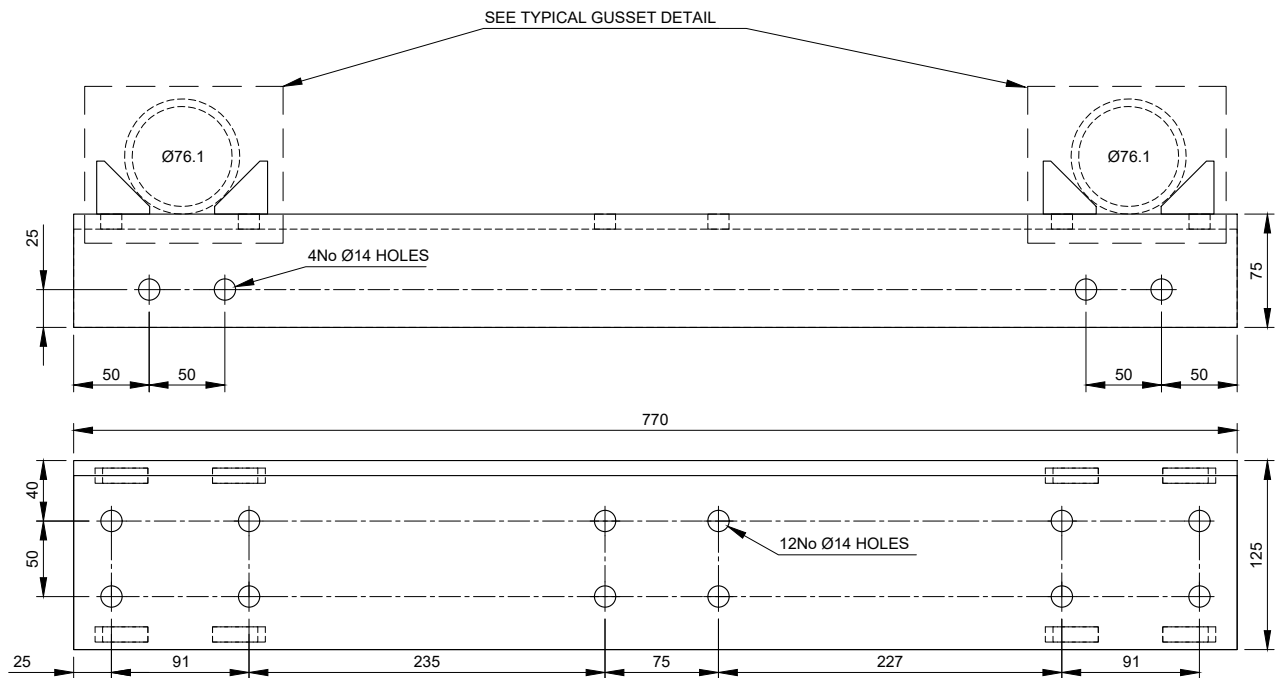


TPA-A - UA125x75x10
Scale 1:5

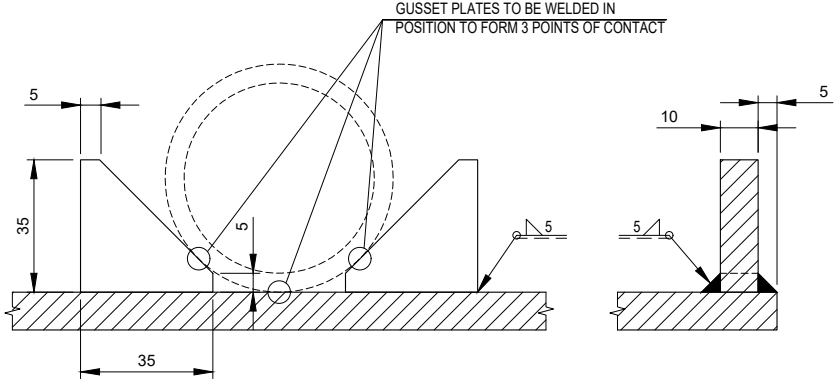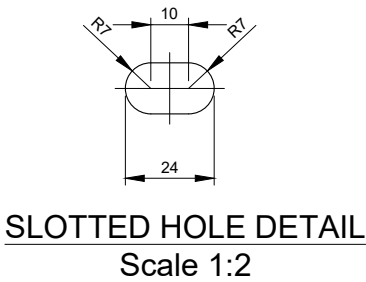

Parts list for TPA-A

Item	Part	Quantity	Part description	Length	Material	Weight
01	TPA-A	1	UA125x75x10	770mm	S275J0	11.60 kg
02	BOLT	4	M12 45mm LONG (2D+6)	45mm	GRADE 8.8	-
02	U-BOLT	4	M12 U-BOLT FOR CHS 76.1mm	N/A	GRADE 8.8	-
Total Weight:						11.60 kg

- All steel hot dip galvanized
- Each U-BOLT to be supplied with 4 Full Nuts, 2 Flat Washers and 2 Spring Washers
- Each BOLT to be supplied with 1 Full Nut, 1 Form E FLat Washer and 1 Spring Washer
- For fabrication notes see drawing 304

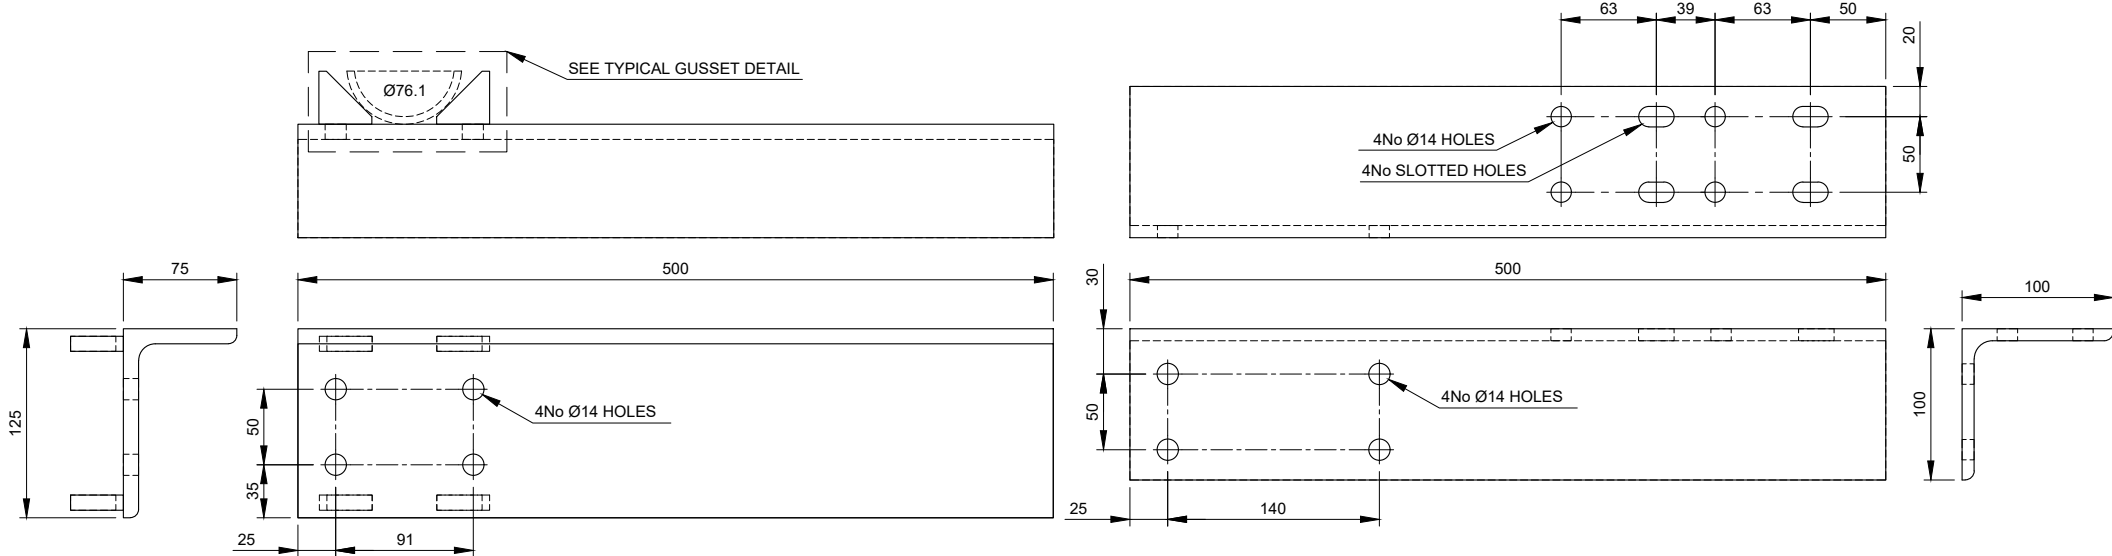


TPA-B-2 - UA125x75x10
Scale 1:5

TPA-B-1 - EA100x100x8
Scale 1:5

Parts list for TPA-B

Item	Part	Quantity	Part description	Length	Material	Weight
01	TPA-B-1	1	EA100x100x8	500mm	S275J0	6.10 kg
02	TPA-B-2	1	UA 125x75x10	500mm	S275J0	7.50 kg
03	U-BOLT	4	M12 U-BOLT FOR CHS 48.3mm	N/A	GRADE 8.8	-
04	U-BOLT	2	M12 U-BOLT FOR CHS 76.1mm	N/A	GRADE 8.8	-
05	N-BOLT	2	M12 N-BOLT FOR UA125x75 (140mm CC)	N/A	GRADE 8.8	-
Total Weight:						13.60 kg

- All steel hot dip galvanized
- Each U-BOLT & N-BOLT to be supplied with 4 Full Nuts, 2 Flat Washers and 2 Spring Washers
- For fabrication notes see drawing 304

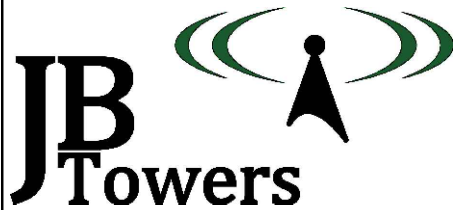

02	TPA-B-2 ADDED; U-BOLTS FOR CHS48.3 UPDATED		AM 02/05/19
01	FIRST ISSUE		AM 25/04/19
REV	REV		BY DATE
SCALE AS SHOWN WHEN PRINTED AT A3		DRAWN AM DATE 25/04/19	CHECKED MP DATE 25/04/19
		APPROVED JBT DATE 25/04/19	
ALL DIMENSIONS IN mm UNLESS OTHERWISE STATED. THIS DRAWING TO BE READ IN CONJUNCTION WITH OTHER RELEVANT DRAWINGS.			

TITLE
STEELWORK BRACKETS
PART: TPA-A; TPA-B


SITE ADDRESS
ARQIVA SITE
CWRWS MILL
NEWCASTLE EMLYN
CEREDIGION
SA44 5TR

ARQIVA REF.
141023
DRG No.
302
REV
02

ALL SCALES AS SHOWN WHEN PRINTED AT A3



ALL SCALES AS SHOWN WHEN PRINTED AT A3

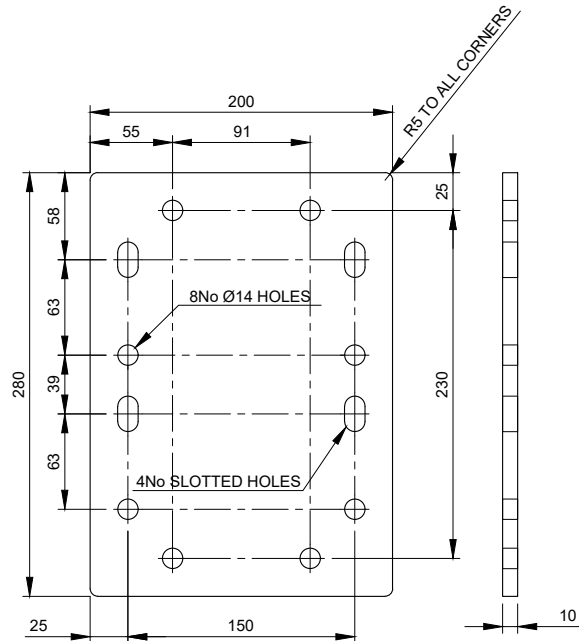


TPA-C - 10mm THICK
Scale 1:5


Parts list for TPA-C

Item	Part	Quantity	Part description	Length	Material	Weight
01	TPA-C	1	280x200x10mm	N/A	S275J0	4.40 kg
02	U-BOLT	2	M12 U-BOLT FOR CHS 76.1mm	N/A	GRADE 8.8	-
03	U-BOLT	4	M12 U-BOLT FOR CHS 48.3mm	N/A	GRADE 8.8	-
Total Weight:						4.40 kg

- All steel hot dip galvanized
- Each U-BOLT to be supplied with 4 Full Nuts, 2 Flat Washers and 2 Spring Washers
- For fabrication notes see drawing 304

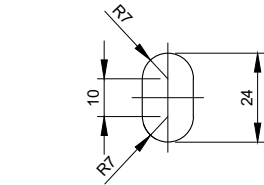

SLOTTED HOLE DETAIL
Scale 1:2

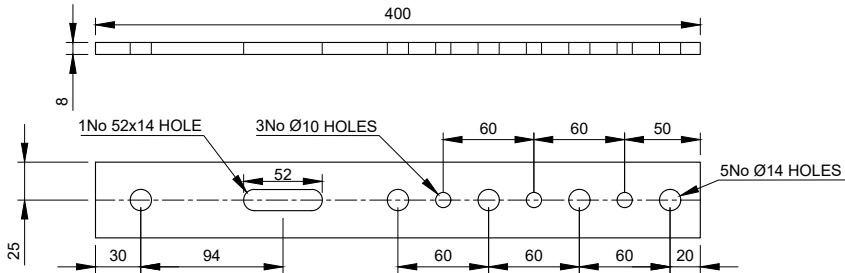


TPA-PD - 8mm THICK
Scale 1:5


Parts list for TPA-PD

Item	Part	Quantity	Part description	Length	Material	Weight
01	TPA-PD	1	400x50x8mm	N/A	S275J0	1.26 kg
02	U-BOLT	1	M12 U-BOLT FOR CHS 76.1mm	N/A	GRADE 8.8	-
Total Weight:						1.26 kg

- All steel hot dip galvanized
- Each U-BOLT to be supplied with 4 Full Nuts, 2 Flat Washers and 2 Spring Washers
- For fabrication notes see drawing 304

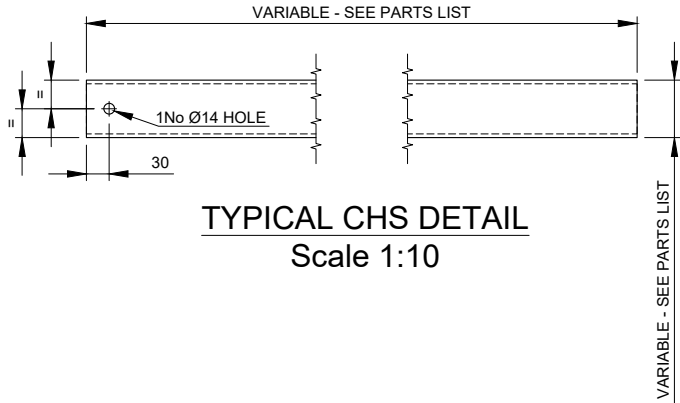

TYPICAL CHS DETAIL
Scale 1:10

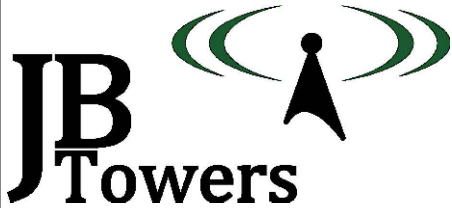

01	FIRST ISSUE			AM	25/04/19	
REV	REV			BY	DATE	
SCALE AS SHOWN WHEN PRINTED AT A3	DRAWN	AM	CHECKED	MP	APPROVED	JBT
	DATE	25/04/19	DATE	25/04/19	DATE	25/04/19
ALL DIMENSIONS IN mm UNLESS OTHERWISE STATED. THIS DRAWING TO BE READ IN CONJUNCTION WITH OTHER RELEVANT DRAWINGS.						

TITLE
CROSS OVER PLATE &
POWER DIVIDER
PARTS: TPA-C; TPA-PD

SITE ADDRESS
ARQIVA SITE
CWRWS MILL
NEWCASTLE EMLYN
CEREDIGION
SA44 5TR

ARQIVA REF.
141023
DRG No.
303
REV
01

ALL SCALES AS SHOWN WHEN PRINTED AT A3



ALL SCALES AS SHOWN WHEN PRINTED AT A3


Item	Part	Drawing	Quantity	Part description	Length	Material	Weight
01	01	200	1	3 MAN LATCHWAY SYSTEM & 3No. WIRE GUIDES FOR FACE MOUNTED MONOPOLE	17000	N/A	-
02	TPB-C	300	2	FALL ARREST ATTACHMENT POINT	N/A	S275J0	4.48 kg
03	03	200	45	PERMANENT BT STEP c/w 3No 10x75mm ZINC-PLATED COACH SCREWS	N/A	S275J0	13.50 kg
04	TPS-R	300	9	'MonoStep' ASSEMBLY	N/A	S275J0	30.60 kg
05	TPB-A	301	4	MOUNTING BRACKET	N/A	S275J0	31.32 kg
06	TPA-A	302	4	MOUNTING BRACKET A	N/A	S275J0	46.40 kg
07	TPA-B	302	2	MOUNTING BRACKET B	N/A	S275J0	27.20 kg
08	08	203	4	CHS 76.1x5mm	2200mm	S355J2H	77.20 kg
09	TPA-C	303	2	CROSS OVER PLATE	N/A	S275J0	8.80 kg
10	TPA-PD	303	2	POWER DIVIDER STRAP	N/A	S275J0	2.52 kg
11	11	203	24	M12 WASHER	N/A	GRADE 8.8	-
12	12	200	1	FEEDER COVER - 2/CG/100	3500mm	UV RESISTANT PLASTIC	-
13	13	200	17	FEEDER CLAMP - 2/FCD/028	N/A	POLYPROPYLENE	-
14	14	200	17	M10 SCREW DOWELS WTH M10 NUT	100mm	STAINLESS STEEL	-
15	15	200	1	PoleSaver	750mm	N/A	-
16	16	200	8	M12 STUD + 4No NUTS + 2No FLAT WASHERS + 1No Ø50mm WASHER (FOR FALL ARREST SYSTEM)	500mm	GRADE 8.8	3.56 kg

- All steel hot dip galvanized
- All U-BOLTS to be FLA supply, each Supplied with 4 Full Nuts, 2 Flat Washers and 2 Spring Washers

Total Weight: 171.05 kg

NOTES:

1. WELDING TO BE IN ACCORDANCE WITH BS EN 1011-1:2009
2. LINEAR DIMS TO BE WITHIN ±1mm;
3. ANGULAR TOLERANCES TO BE WITHIN 0.5°
4. WELDING SYMBOLS ARE IN ACCORDANCE WITH BS EN 22553:1995
5. ALL PROFILE EDGES TO BE DRESSED AND SHARP CORNERS REMOVED
6. ALL WELD SIZES ARE FINAL SIZES
7. ALL WELDED JOINTS ARE TO BE PICKLE TIGHT
8. ALL STEELWORK TO BE BS EN 10025 GRADE S275 J0 UNO & HOT DIPPED GALVANISED TO BS EN ISO 1461. (ALL HOLLOW SECTIONS TO BE GRADE S355 J0H)
9. ALL STEEL IS TO BE SUPPLIED IN ACCORDANCE WITH EN 1090 TO EXECUTION CLASS 2
10. ALL NON PRE-LOADED BOLTS TO BE COMPLIANT STRUCTURAL BOLTS TO BS EN ISO 15048 PARTS 1&2.
11. STEELWORK COMPONENTS SHALL BE HOT DIP GALVANISED TO ACHIEVE A "VERY HIGH" DURABILITY FOR AN ENVIRONMENT CATEGORY CODE C4 FROM TABLE 1 IN BS EN ISO 14713
12. BOLTS AND NUTS SHALL BE SUPPLIED IN ACCORDANCE WITH BS 7371, SPUN GALVANISED IN ACCORDANCE WITH ISO 10684, THE NUTS RE-TAPPED AFTER GALVANISING, AND THE THREADS TREATED WITH GREASE.
13. ALL BOLTS TO BE CUT ON SITE TO EXTEND MAX 10mm BEYOND THE NUT WHEN TIGHTENED UNO.
14. ALL SITE DRILLED HOLE/CUT ENDS TO BE TREATED WITH METAFLUX 70-40 ZINC PASTE FOLLOWED BY 1 COAT OF 7-42 ZINC ALU OR 70-16 ALUMINIUM SPRAY

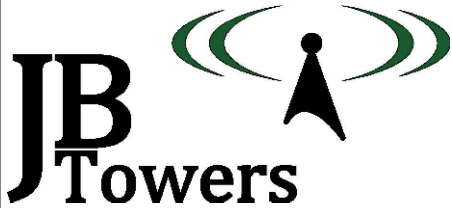

01	FIRST ISSUE	AM	25/04/19
REV	REV	BY	DATE
SCALE AS SHOWN WHEN PRINTED AT A3	DRAWN AM DATE 25/04/19	CHECKED MP DATE 25/04/19	APPROVED JBT DATE 25/04/19
ALL DIMENSIONS IN mm UNLESS OTHERWISE STATED. THIS DRAWING TO BE READ IN CONJUNCTION WITH OTHER RELEVANT DRAWINGS.			


TITLE
PARTS LIST

SITE ADDRESS ARQIVA SITE CWRWS MILL NEWCASTLE EMLYN CEREDIGION SA44 5TR		
ARQIVA REF. 141023	DRG No. 304	REV 01

ALL SCALES AS SHOWN WHEN PRINTED AT A3



ALL SCALES AS SHOWN WHEN PRINTED AT A3

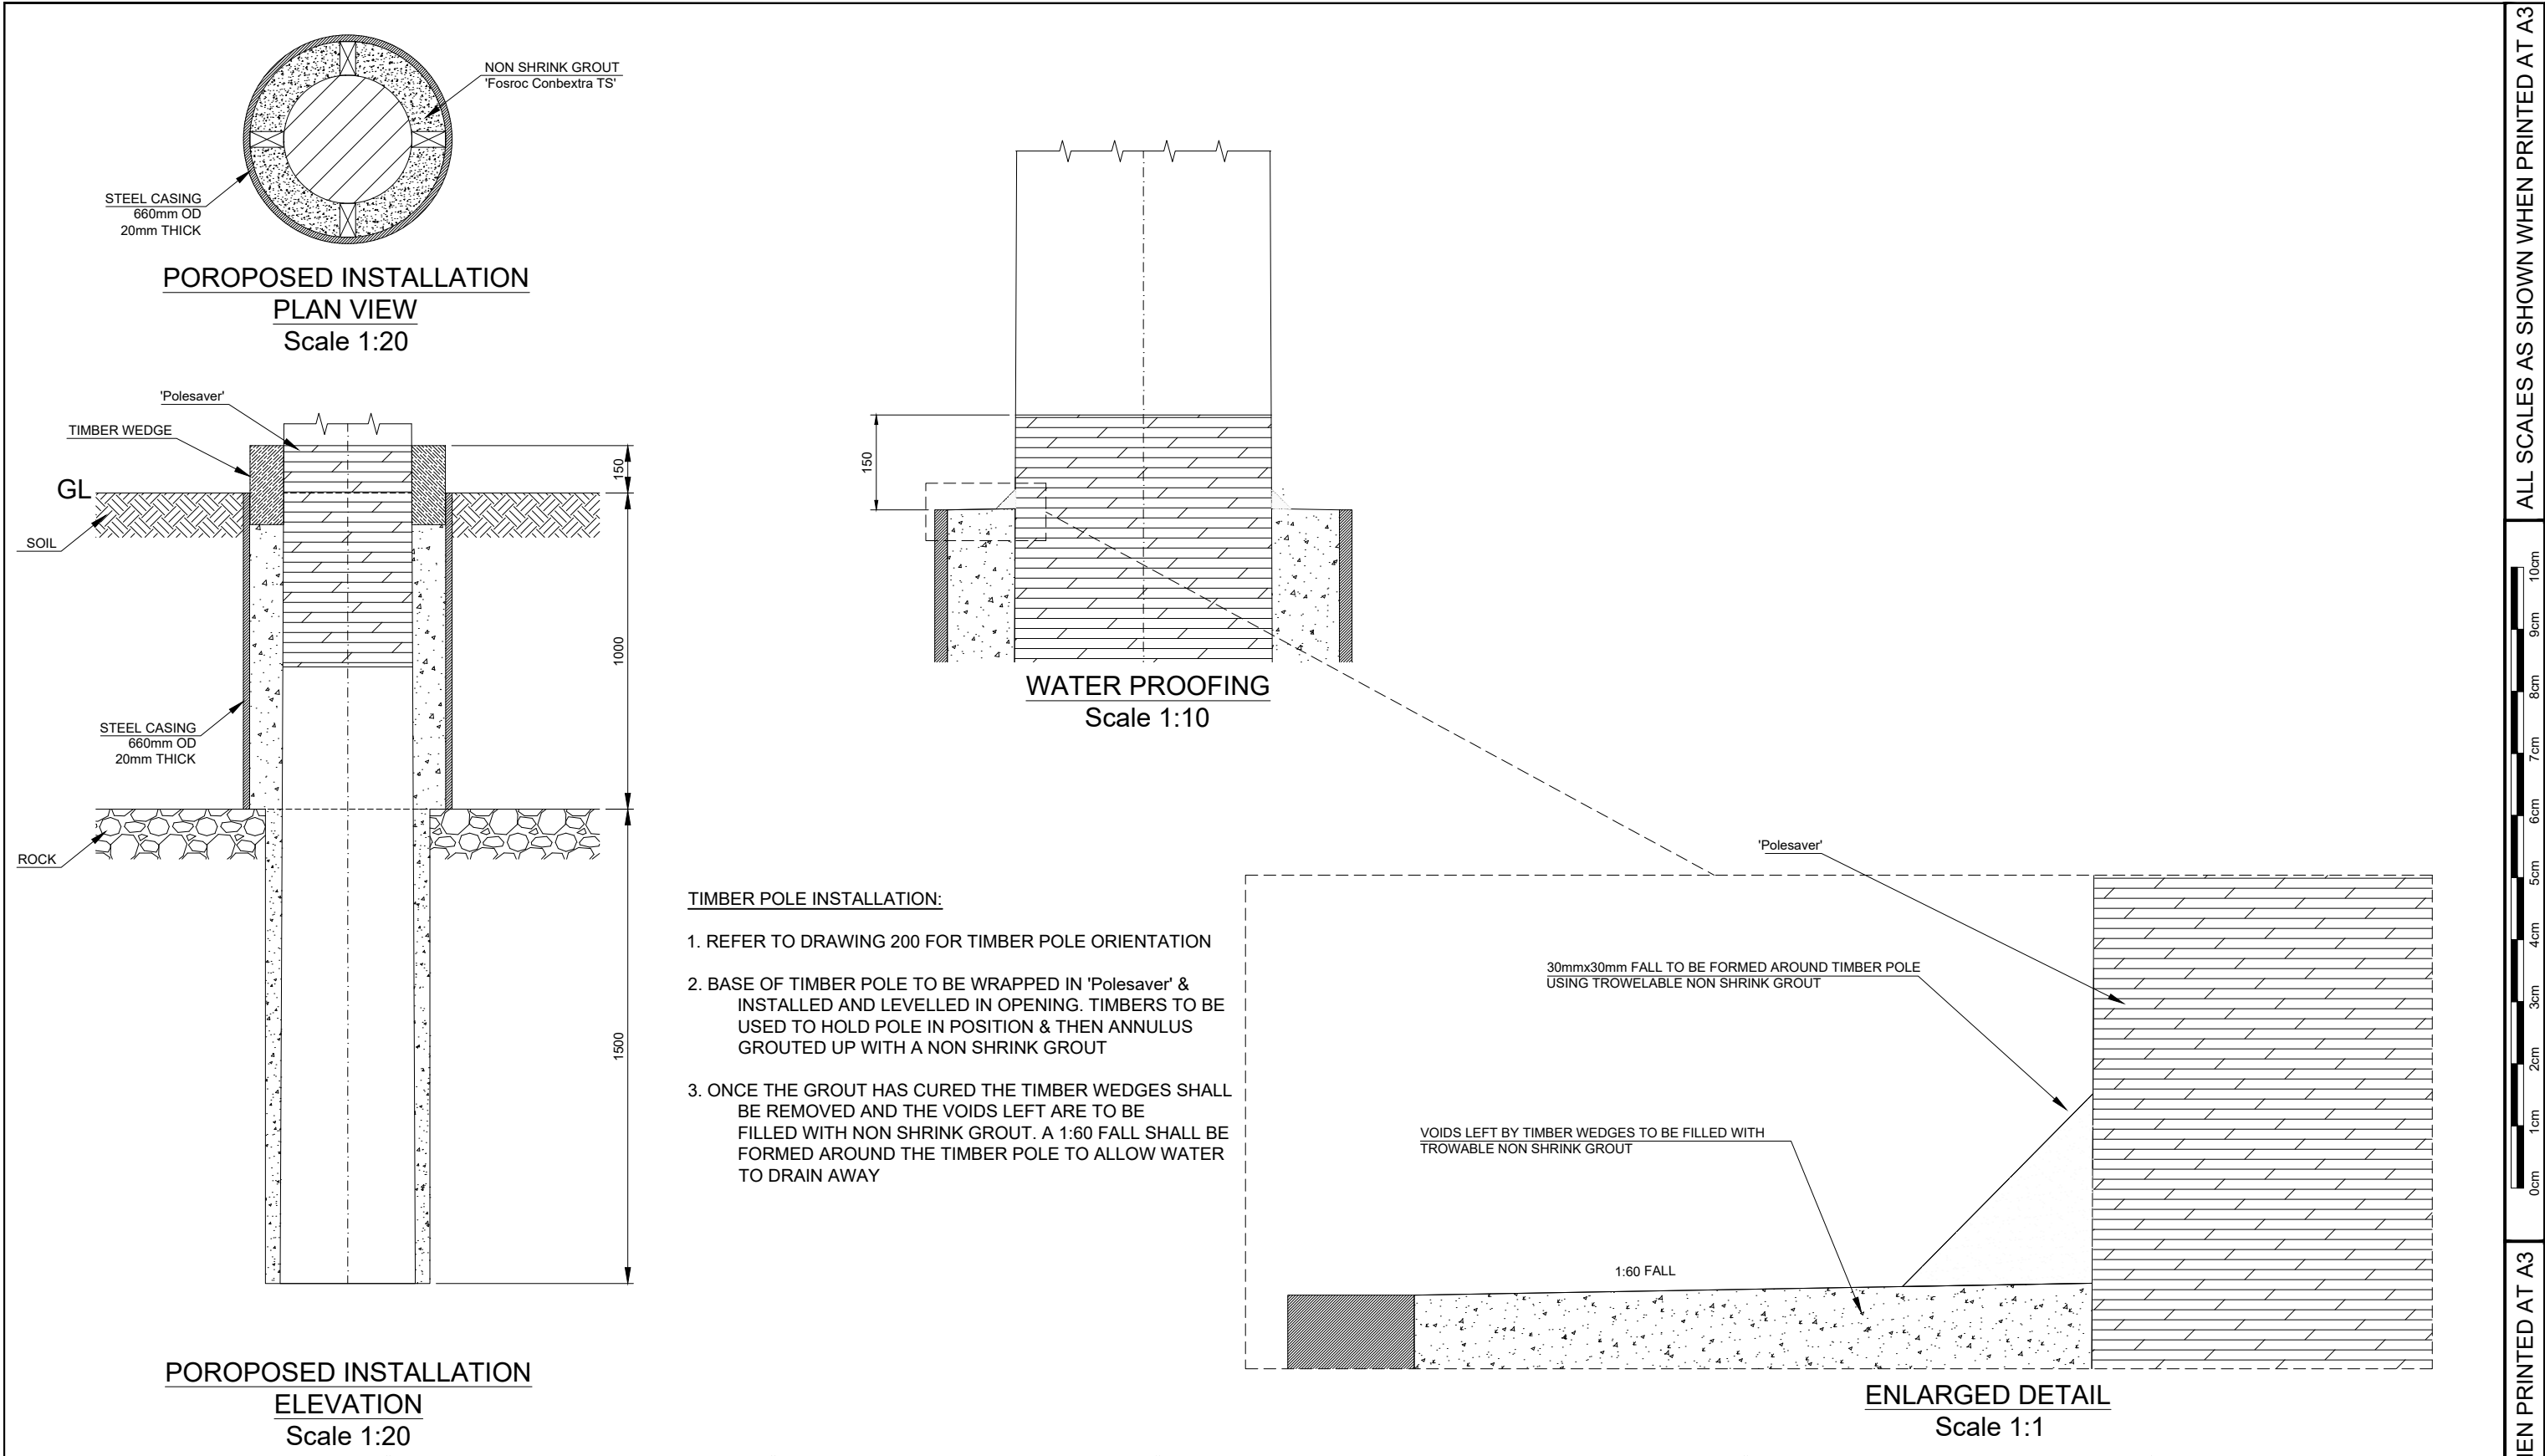

											TITLE				FOUNDATION DETAILS				SITE ADDRESS ARQIVA SITE CWRWS MILL NEWCASTLE EMLYN CEREDIGION SA44 5TR			
			01		FIRST ISSUE						AM		25/04/19									
			REV		REV						BY		DATE									
			SCALE AS SHOWN		DRAWN		AM		CHECKED		MP		APPROVED		JBT							
			WHEN PRINTED AT A3		DATE		25/04/19		DATE		25/04/19		DATE		25/04/19							
			ALL DIMENSIONS IN mm UNLESS OTHERWISE STATED. THIS DRAWING TO BE READ IN CONJUNCTION WITH OTHER RELEVANT DRAWINGS.																			
															ARQIVA REF. 141023				DRG No. 400		REV 01	

ALL SCALES AS SHOWN WITHIN DRAWING

ALL SCALES AS SHOWN WHEN PRINTED AT A3

0cm 1cm 2cm 3cm 4cm 5cm 6cm 7cm 8cm 9cm 10cm

ALL SCALES AS SHOWN WHEN PRINTED AT A3