
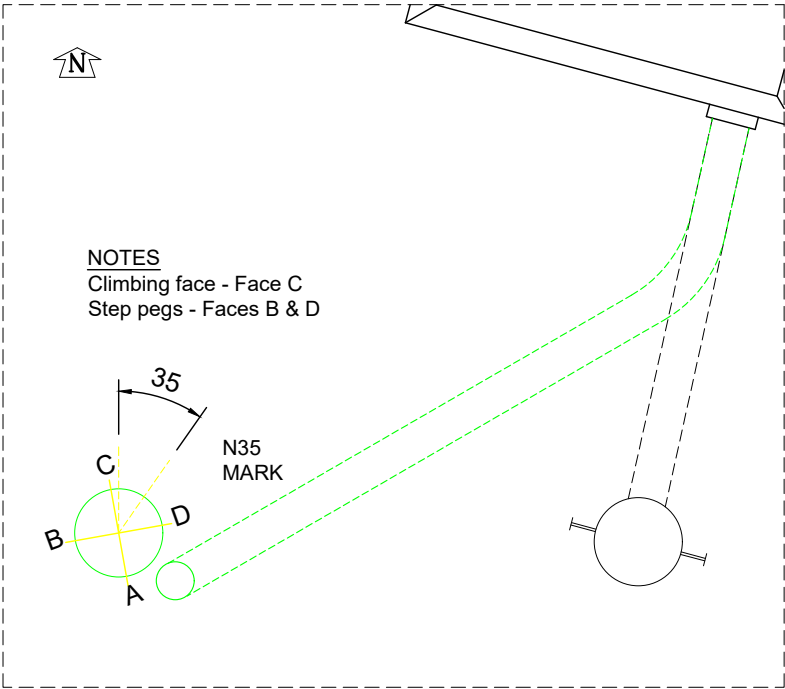


DRAWING ISSUE SHEET

[illegible]

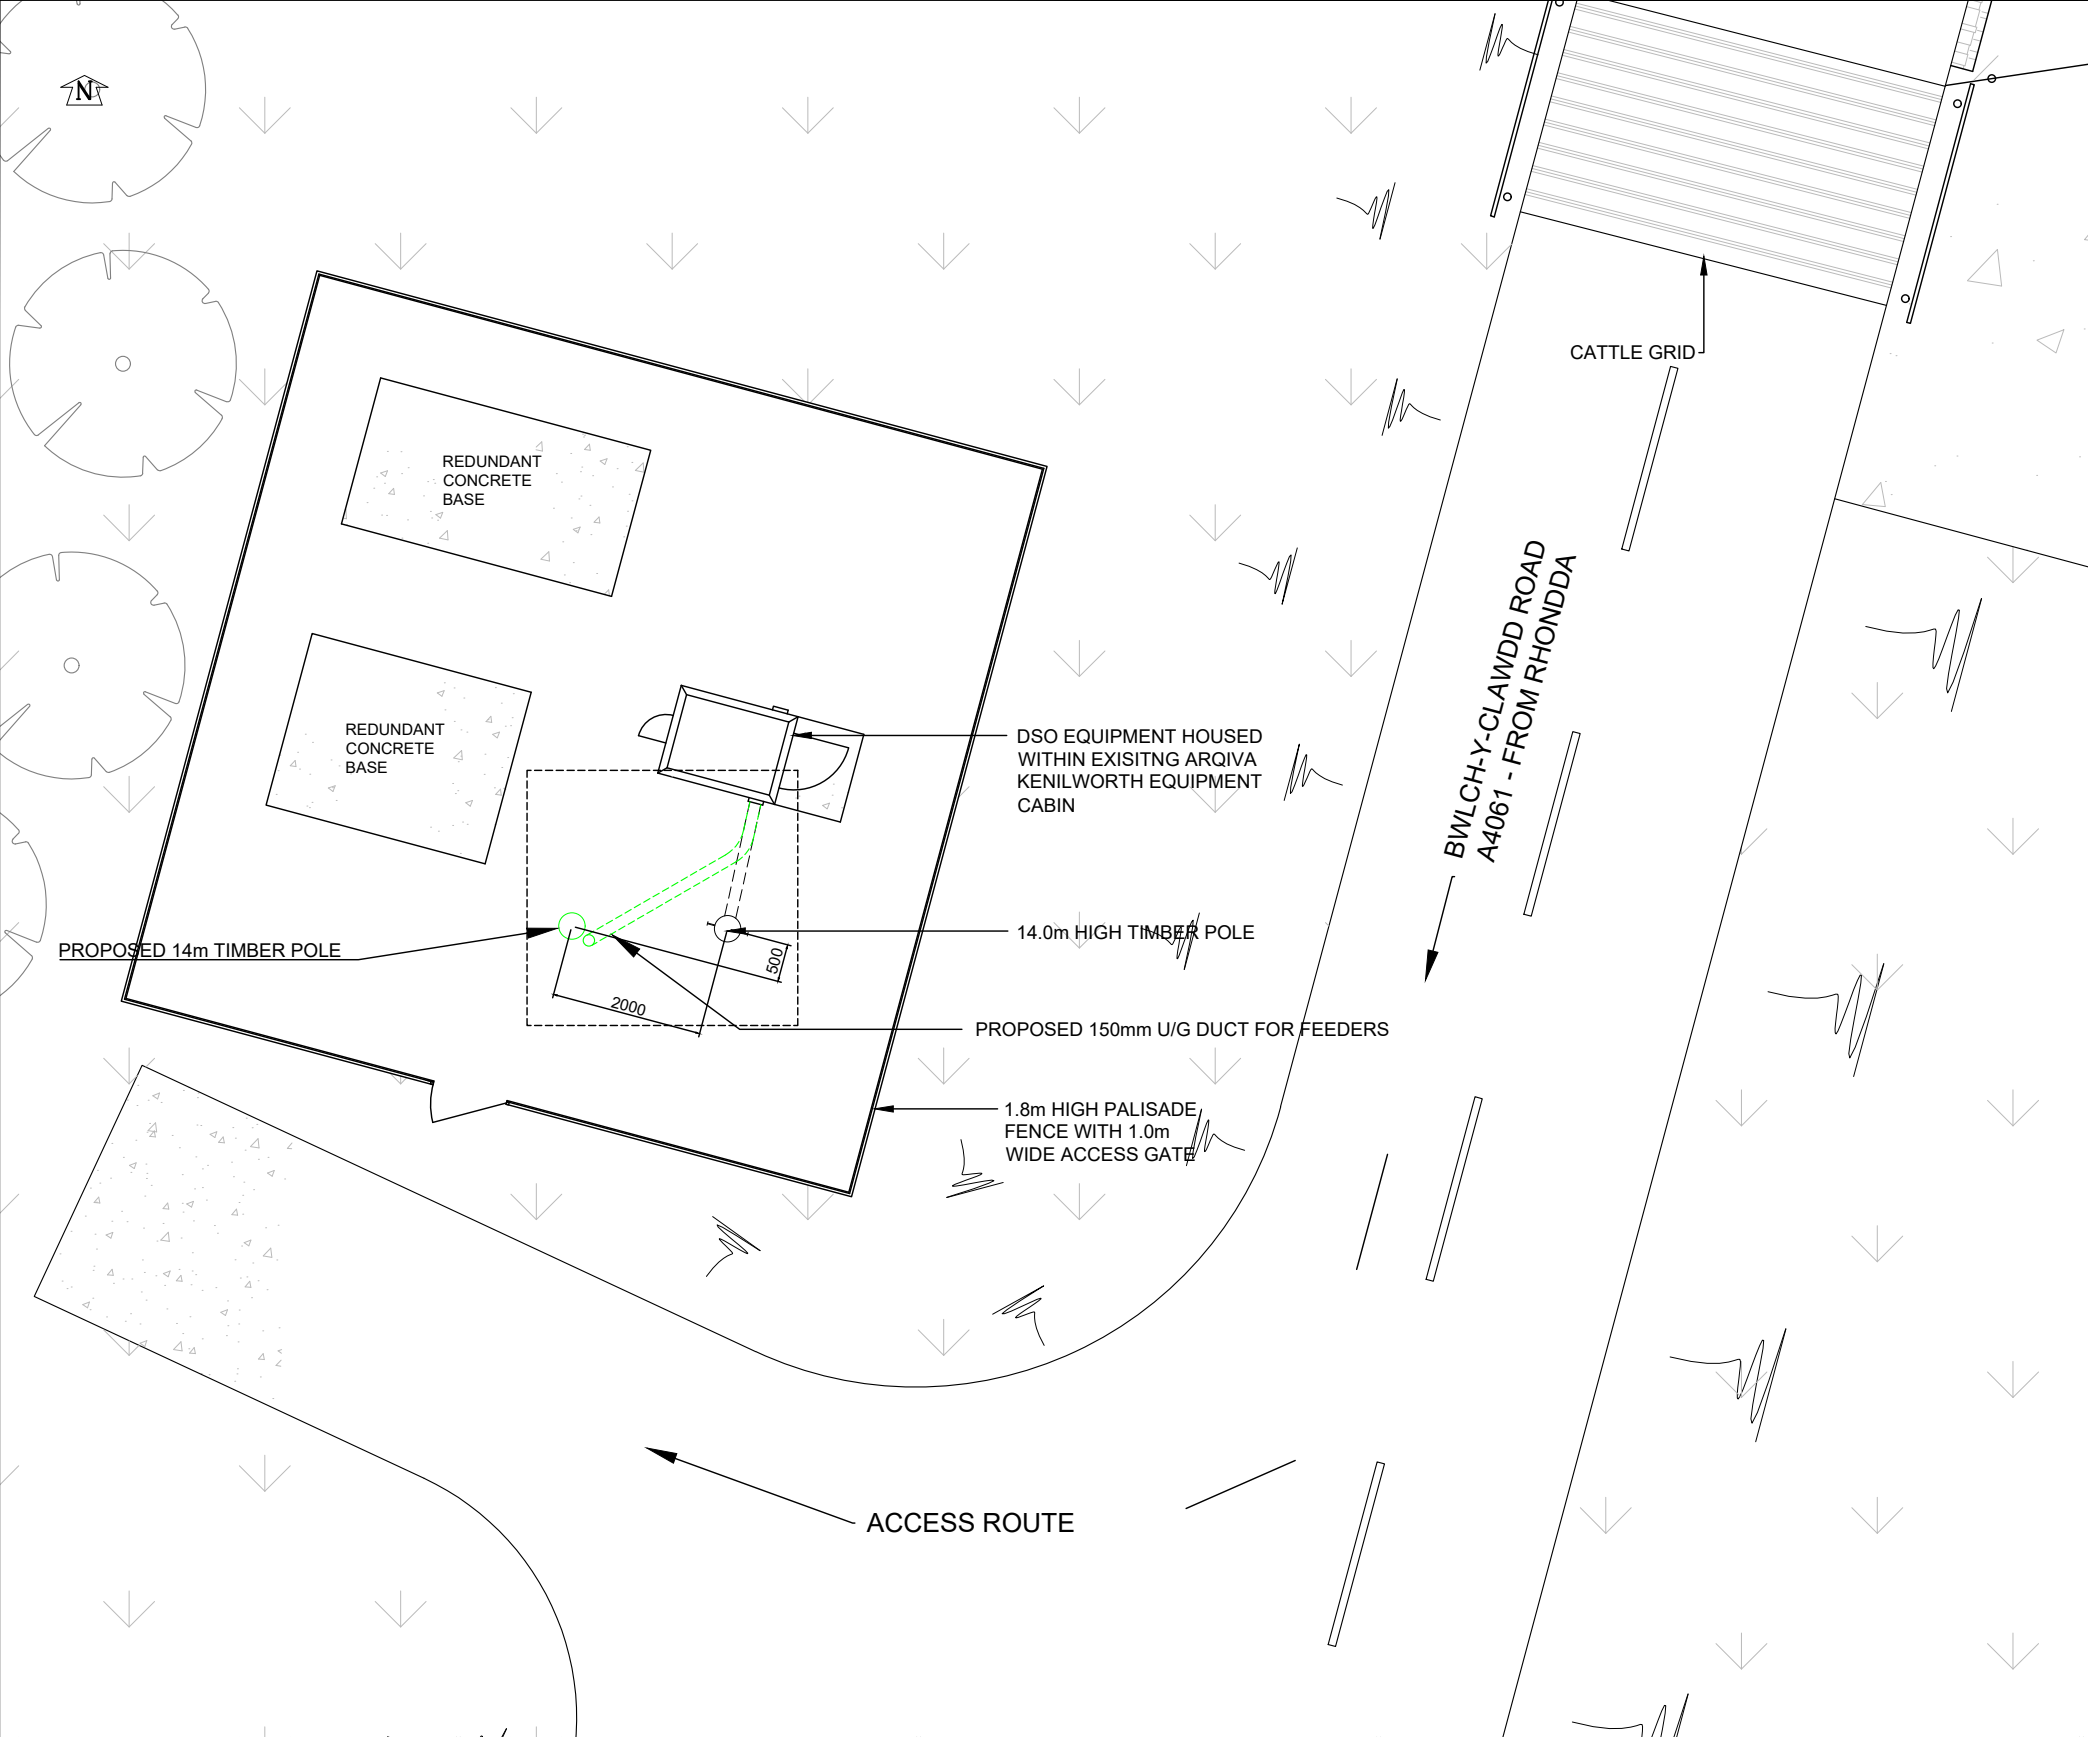


NOTES
Climbing face - Face C
Step pegs - Faces B & D

ALL SCALES AS SHOWN WHEN PRINTED AT A3



ALL SCALES AS SHOWN WHEN PRINTED AT A3

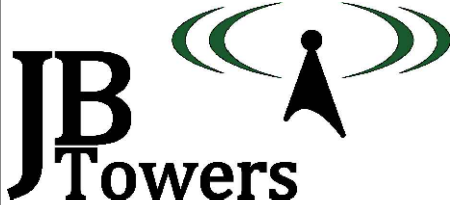

01	FIRST ISSUE				TT	15/05/19
REV	REV				BY	DATE
SCALE AS SHOWN		DRAWN	AM	CHECKED	MP	APPROVED JBT
WHEN PRINTED AT A3		DATE	15/05/19	DATE	15/05/19	DATE 15/05/19
ALL DIMENSIONS IN mm UNLESS OTHERWISE STATED. THIS DRAWING TO BE READ IN CONJUNCTION WITH OTHER RELEVANT DRAWINGS.						


TITLE
NANT-Y-MOEL
SITE PLAN

SITE ADDRESS
ADJACENT A4061
NORTH OF NANT-Y-MOEL
RHONDDA CYNON TAFF
CF32 7PB

ARQIVA REF.
141296

DRG No.
100

REV
01

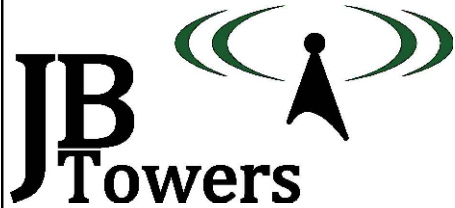

01	FIRST ISSUE			TT	15/05/19
REV	REV			BY	DATE
SCALE AS SHOWN WHEN PRINTED AT A3		DRAWN AM DATE 15/05/19	CHECKED MP DATE 15/05/19	APPROVED	JBT DATE 15/05/19
ALL DIMENSIONS IN mm UNLESS OTHERWISE STATED. THIS DRAWING TO BE READ IN CONJUNCTION WITH OTHER RELEVANT DRAWINGS.					

TITLE

NANT-Y-MOEL

GENERAL ARRANGEMENT

SHEET 1 OF 3

SITE ADDRESS

ADJACENT A4061

NORTH OF NANT-Y-MOEL

RHONDDA CYNON TAFF

CF32 7PB

ARQIVA REF.



141296

DRG No.

200

REV

01

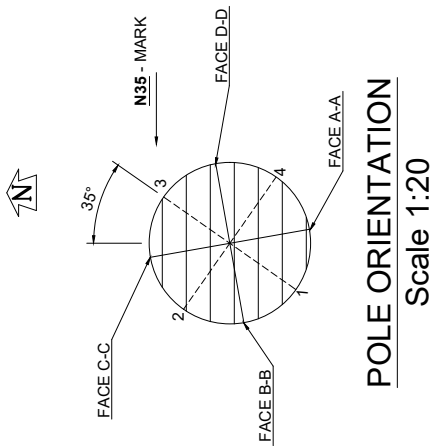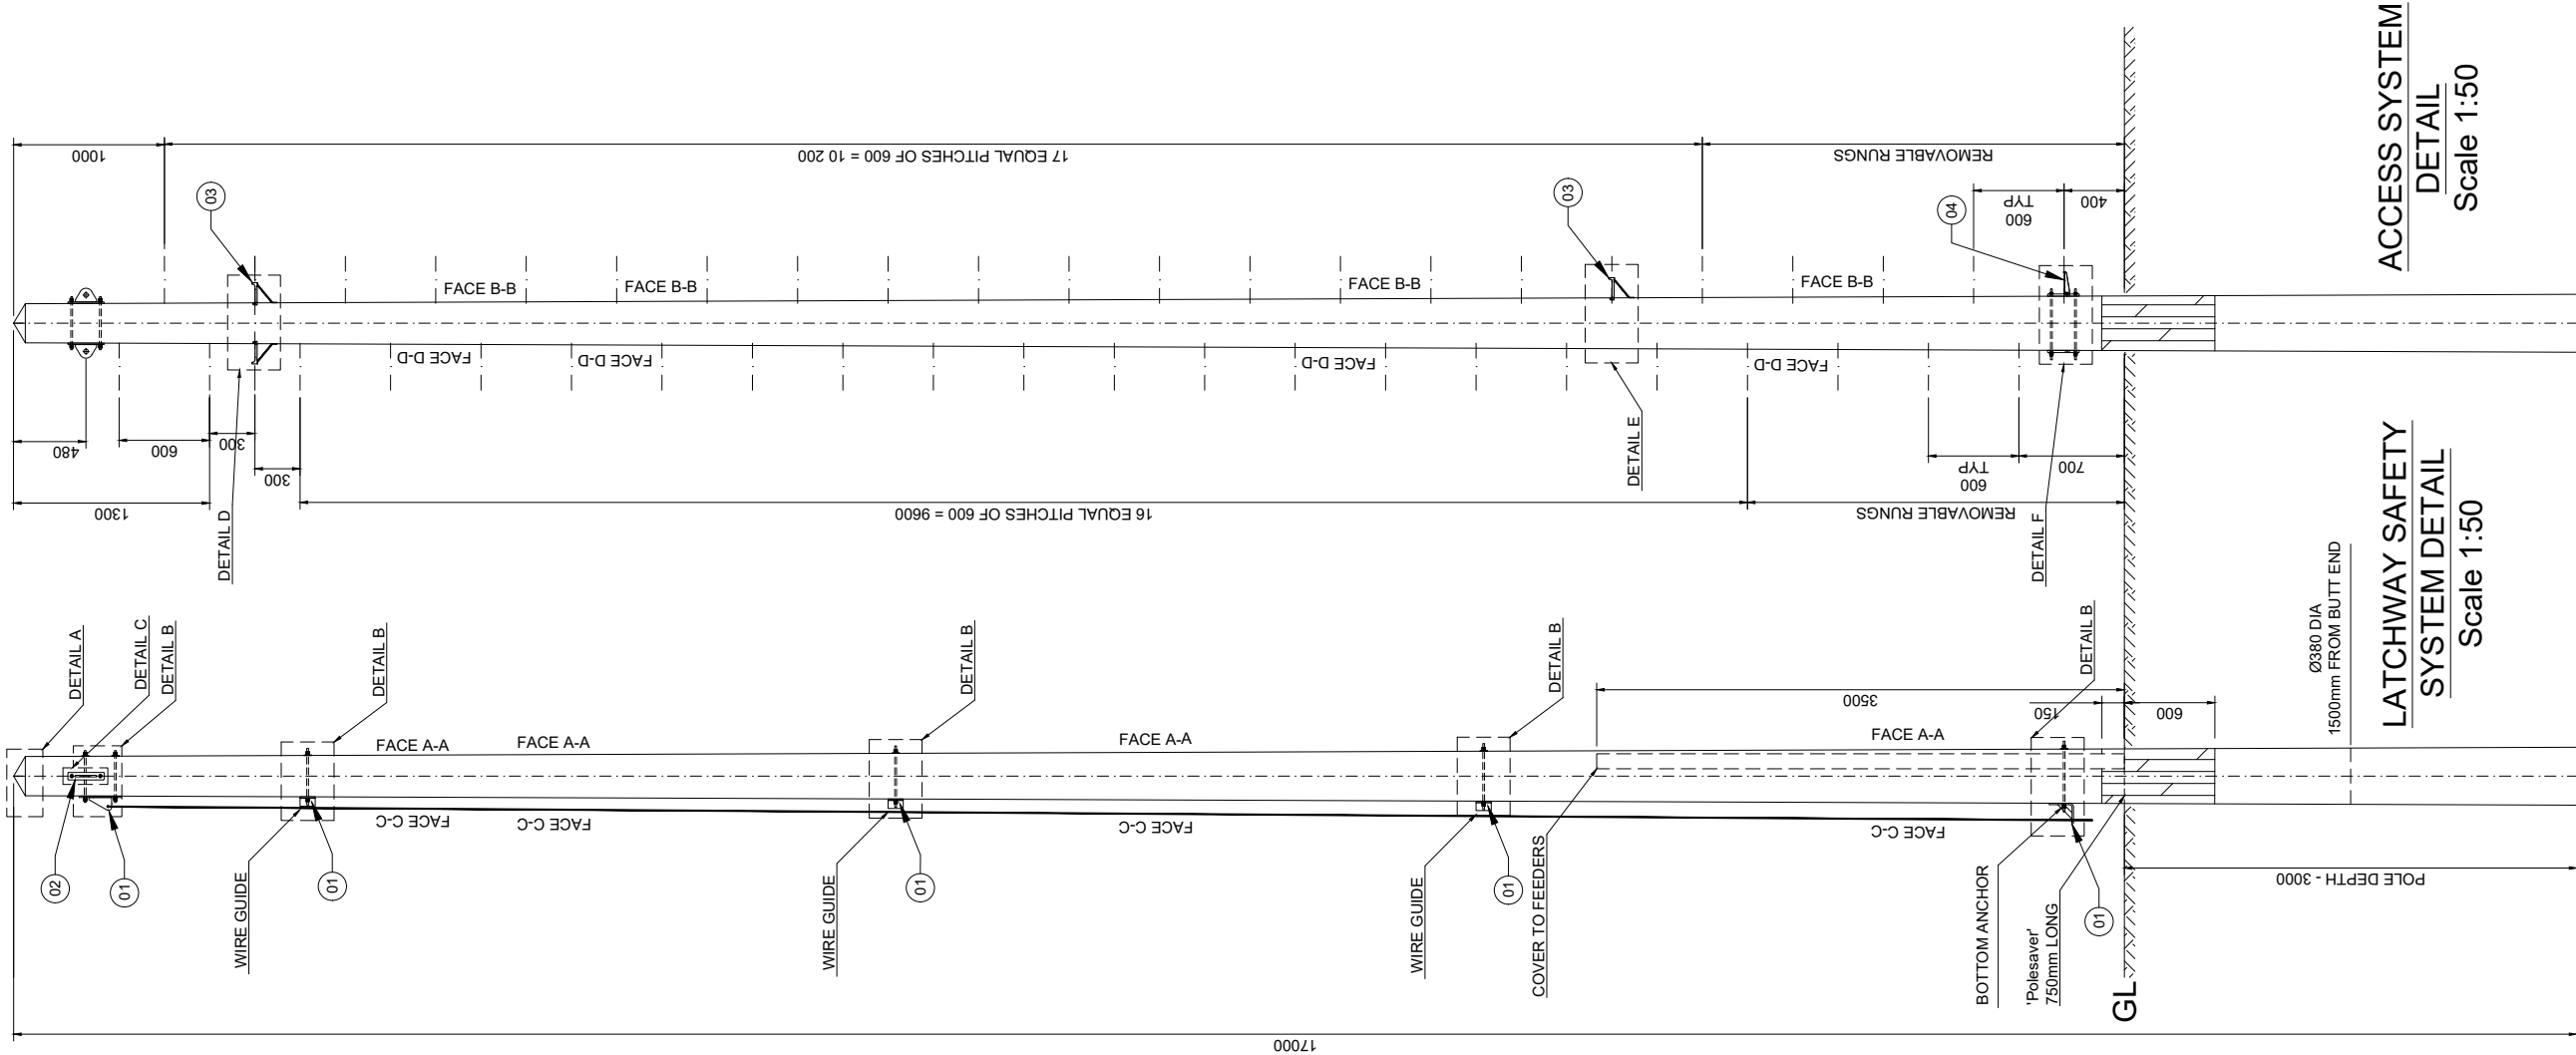

NOTES

1. SEE DRAWING 302 FOR PARTS LIST
2. ALL BOLTS TO BE CUT ON SITE TO EXTEND MAX 10mm BEYOND THE NUT WHEN TIGHTENED UNO.
3. ALL SITE DRILLED HOLE/CUT ENDS TO BE TREATED WITH METAFUX 70-40 ZINC PASTE FOLLOWED BY 1 COAT OF 7-42 ZINC ALU OR 70-16 ALUMINIUM SPRAY

TIMBER POLE




1. POLE TO BE SUPPLIED IN ACCORDANCE WITH BS EN14229 & SHALL HAVE MIN. CHARACTERISTIC BENDING STRENGTH OF 30N/mm2 & MIN. YOUNGS MODULUS (PARALLEL TO GRAIN) OF 10KN/mm2.
2. MARKINGS ON FINISHED POLE SHALL BE AT 4m FROM BUTT AND COMPLY WITH BS EN 14229 UNO
3. AS FAR AS PRACTICABLE ALL CUTTING, SCARFING & DRILLING TO BE DONE BEFORE CREOSOTING. IF NOT ALL CUT, DRILLED & SCARFED SURFACES TO BE COATED WITH A MIXTURE OF CREOSOTE & TAR.
4. POLE TO BE PRESSURE IMPREGNATED WITH CREOSOTE IN ACCORDANCE WITH BS EN 14229
5. MINIMUM DIAMETERS
TOP - Ø2000mm
BOTTOM - Ø395mm
6. 17m LONG POLE TO BE SOURCED BY TRIMMING 18m LONG POLE BY 1m AT THE BOTTOM

PLANTING

1. CAT SCANNER IS TO BE USED IN ORDER TO CONFIRM THE POSITIONS OF BURIED SERVICES.
2. 'Perma-Soil Stabiliser' OR A SIMILAR APPROVED SHOULD BE USED IN ACCORDANCE WITH THE MANUFACTURER'S RECOMMENDATION.
3. ANY MATERIAL USED FOR BACK-FILLING IS TO BE OF EQUAL OF BETTER QUALITY THAN THE EXCAVATED MATERIAL.
4. ALL BACK-FILLING MATERIAL IS TO BE PLACED AND COMPACTED IN 150mm THICK LAYERS.
5. TIMBER POLE TO BE PLANTED WITH N35 MARKING AT 4m FROM BUTT FACING 35° FROM NORTH (CLOCKWISE)

ACCESS SYSTEM
DETAIL
Scale 1:50

LATCHWAY SAFETY
SYSTEM DETAIL
Scale 1:50

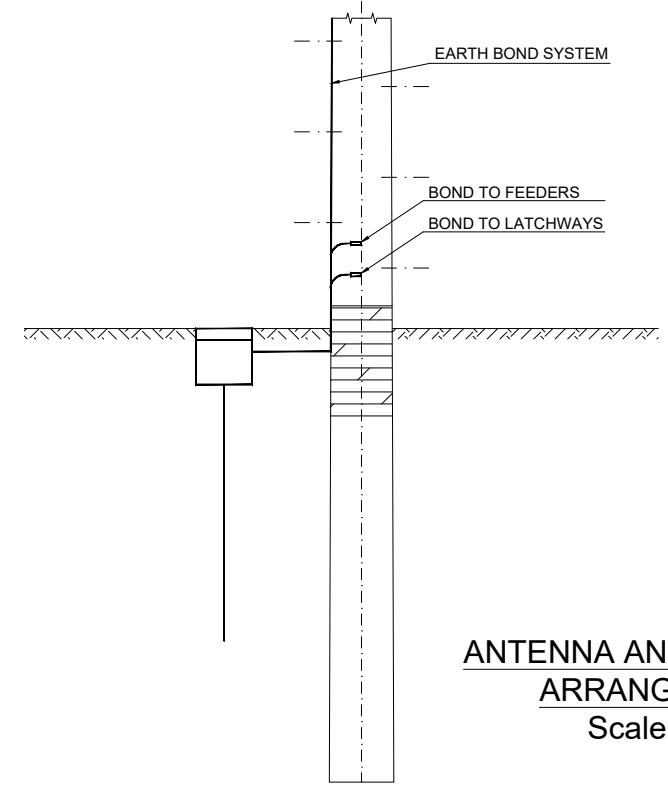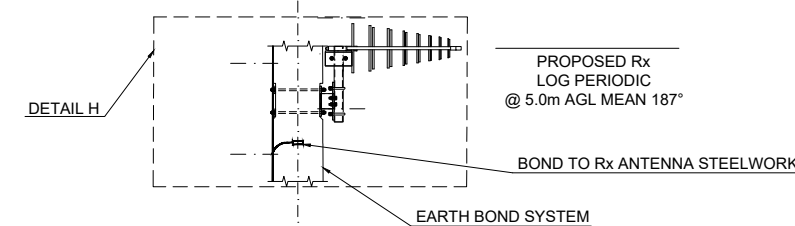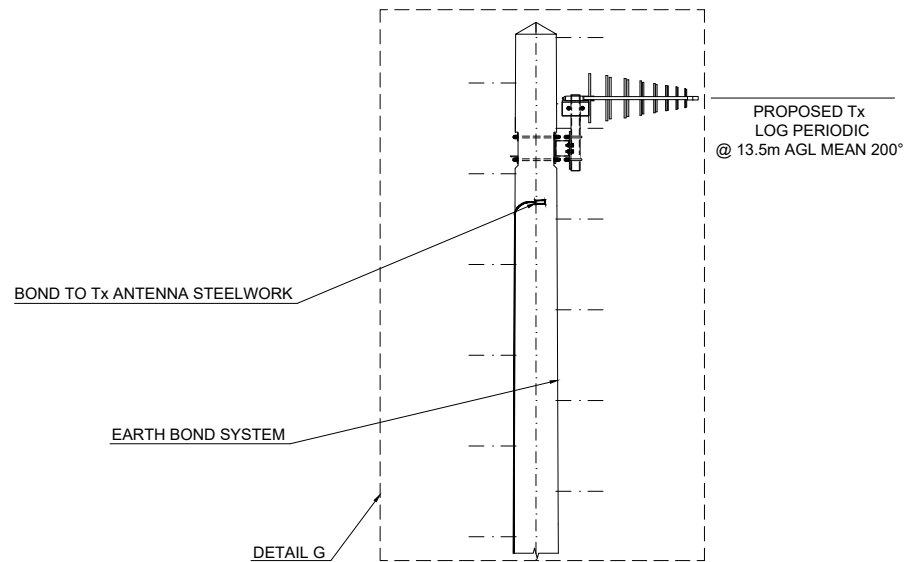

ANTENNA AND EARTHING
ARRANGEMENT
Scale 1:50

NOTES



1. AS FAR AS IS PRACTICABLE ALL CUTTING SCARFING AND DRILLING TO BE DONE BEFORE CREOSOTING. WHERE THIS IS NOT POSSIBLE ALL CUT, DRILLED, AND SCARFED SURFACES TO BE COATED WITH A MIXTURE OF CREOSOTE AND TAR

FEEDERS

1. SUPPLY OF FEEDERS BY OTHERS
LCF78-50 TO Tx ANTENNA &
LCF12-50 TO Rx ANTENNA
2. FEEDERS FIXED AT 1000mm CENTRES

EARTHING

1. CONNECT EARTH BOND TO NEW EARTHING SYSTEM
2. MAXIMUM VALUE FOR GROUND RESISTANCE TO BE 10 OHMS
3. CABLE OR TAPE TO BE FIXED TO POLE AT 1000mm CENTRES
4. EARTHING SHOULD COMPLY WITH ARQIVA'S DOCUMENT BOS147

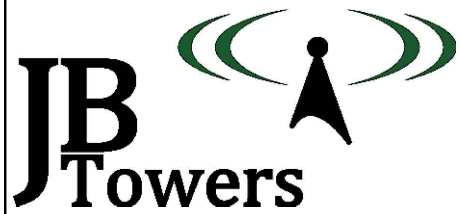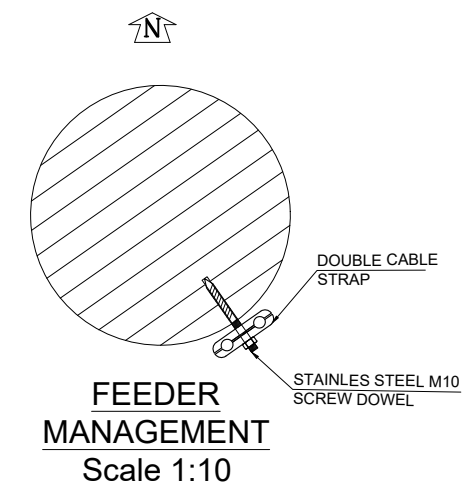


01	FIRST ISSUE				TT	15/05/19
REV	REV				BY	DATE
SCALE AS SHOWN WHEN PRINTED AT A3		DRAWN AM DATE 15/05/19	CHECKED MP DATE 15/05/19	APPROVED JBT DATE 15/05/19		
ALL DIMENSIONS IN mm UNLESS OTHERWISE STATED. THIS DRAWING TO BE READ IN CONJUNCTION WITH OTHER RELEVANT DRAWINGS.						

TITLE		SITE ADDRESS		
NANT-Y-MOEL		ADJACENT A4061 NORTH OF NANT-Y-MOEL RHONDDA CYNON TAFF CF32 7PB		
GENERAL ARRANGEMENT SHEET 2 OF 3		ARQIVA REF. 141296	DRG No. 200	REV 01


ALL SCALES AS SHOWN WHEN PRINTED AT A3



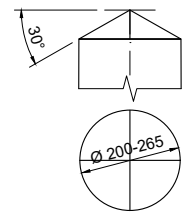


- NOTES:
1. A SINGLE COAT OF TIMBER COMPATIBLE BITUMINOUS PAINT (E.G. BIRD BRAND BLACK BITUMINOUS PAINT OR SIMILAR APPROVED PRODUCT) TO BE APPLIED TO THE UPPER SURFACES AT THE TOP OF THE POLE.
 2. PAINT TO BE APPLIED ON SITE JUST BEFORE ERECTION
- FORM: 4 WAY PYRAMID / CONE


DETAIL A - TIMBER POLE TOP
Scale 1:20

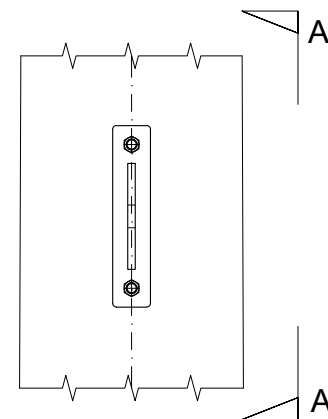


DETAIL C - FALL ARREST
ATTACHMENT POINT
Scale 1:10

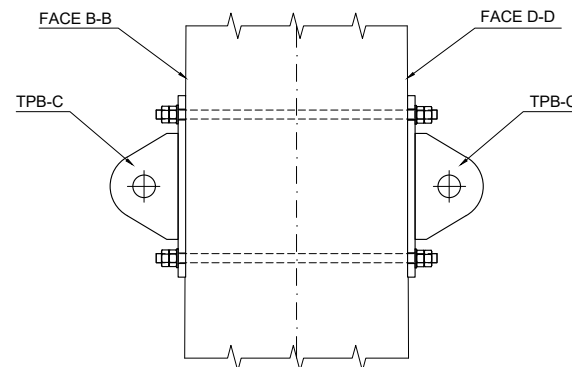


VIEW A-A
Scale 1:10

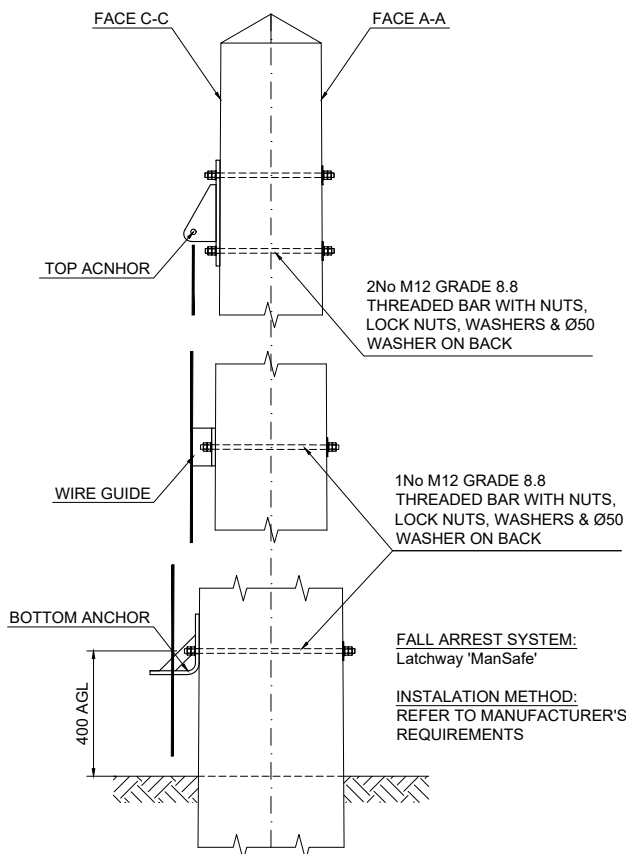

DETAIL B - FALL ARREST SYSTEM
Scale 1:20

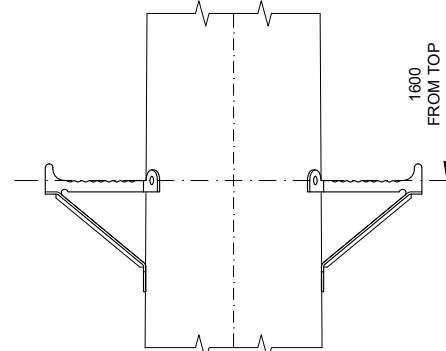


DETAIL D - ANTENNA
ACCESS CLIMBING STEP
Scale 1:10

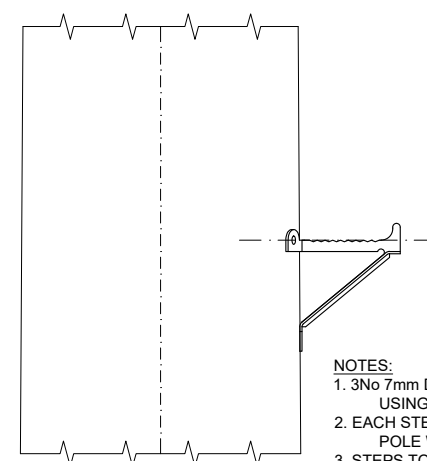


DETAIL E - PERMANENT
CLIMBING STEPS
Scale 1:10

- NOTES:
1. 3No 7mm DIA 70mm LONG PILOT HOLES TO BE DRILLED USING THE STEP AS A TEMPLATE
 2. EACH STEP SHOULD BE FIXED TO THE TIMBER POLE WITH 3No 10mm COACH SCREWS 75mm LONG
 3. STEPS TO BE INSTALLED ON FACES B-B & D-D ONLY

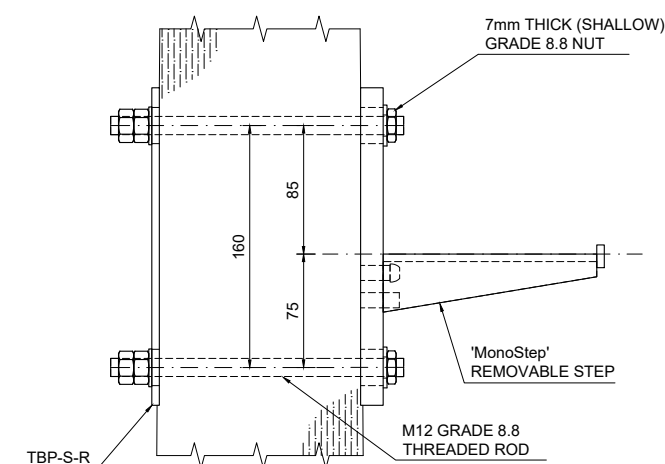

DETAIL F - REMOVABLE
CLIMBING STEPS
Scale 1:5

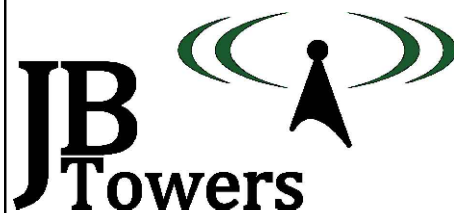


01	FIRST ISSUE	TT	15/05/19
REV	REV	BY	DATE
SCALE AS SHOWN WHEN PRINTED AT A3	DRAWN AM DATE 15/05/19	CHECKED MP DATE 15/05/19	APPROVED JBT DATE 15/05/19
ALL DIMENSIONS IN mm UNLESS OTHERWISE STATED. THIS DRAWING TO BE READ IN CONJUNCTION WITH OTHER RELEVANT DRAWINGS.			


TITLE
NANT-Y-MOEL
GENERAL ARRANGEMENT
SHEET 3 OF 3

SITE ADDRESS
ADJACENT A4061
NORTH OF NANT-Y-MOEL
RHONDDA CYNON TAFF
CF32 7PB

ARQIVA REF.
141296
DRG No.
200
REV
01

ALL SCALES AS SHOWN WHEN PRINTED AT A3

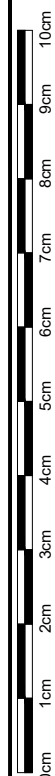

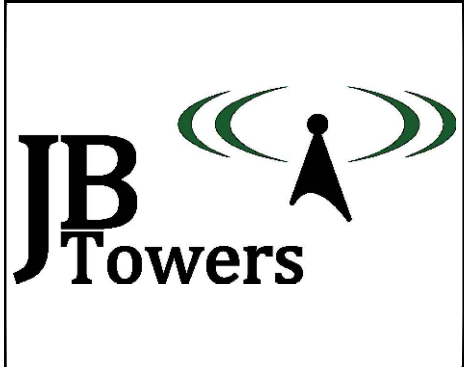

01	FIRST ISSUE						TT	15/05/19	
REV	REV						BY	DATE	
SCALE AS SHOWN WHEN PRINTED AT A3		DRAWN	AM	CHECKED	MP	APPROVED		JBT	
		DATE 15/05/19		DATE 15/05/19		DATE 15/05/19			
ALL DIMENSIONS IN mm UNLESS OTHERWISE STATED. THIS DRAWING TO BE READ IN CONJUNCTION WITH OTHER RELEVANT DRAWINGS.									

TITLE

NANT-Y-MOEL






TIMBER POLE HOLE SET OUT

SHEET 1 OF 2



SITE ADDRESS


ADJACENT A4061
NORTH OF NANT-Y-MOEL
RHONDDA CYNON TAFF
CF32 7PB

ARQIVA REF. 141296	DRG No. 201	REV 01
-----------------------	----------------	-----------

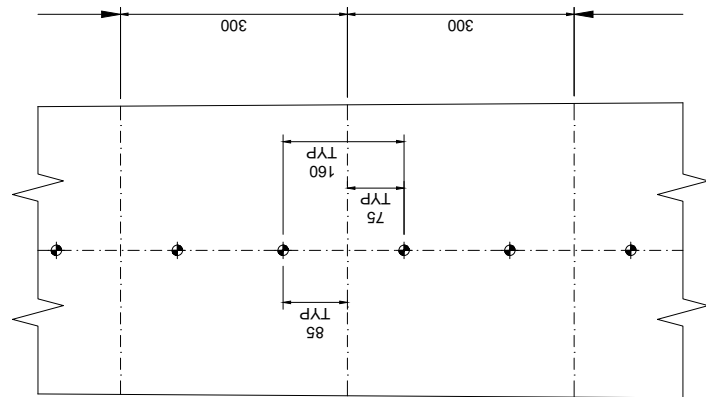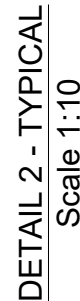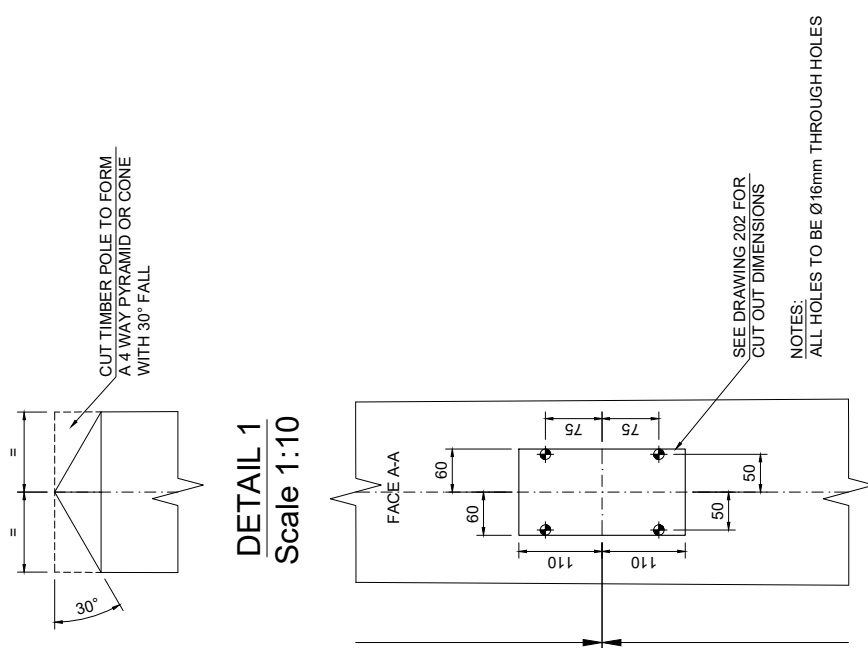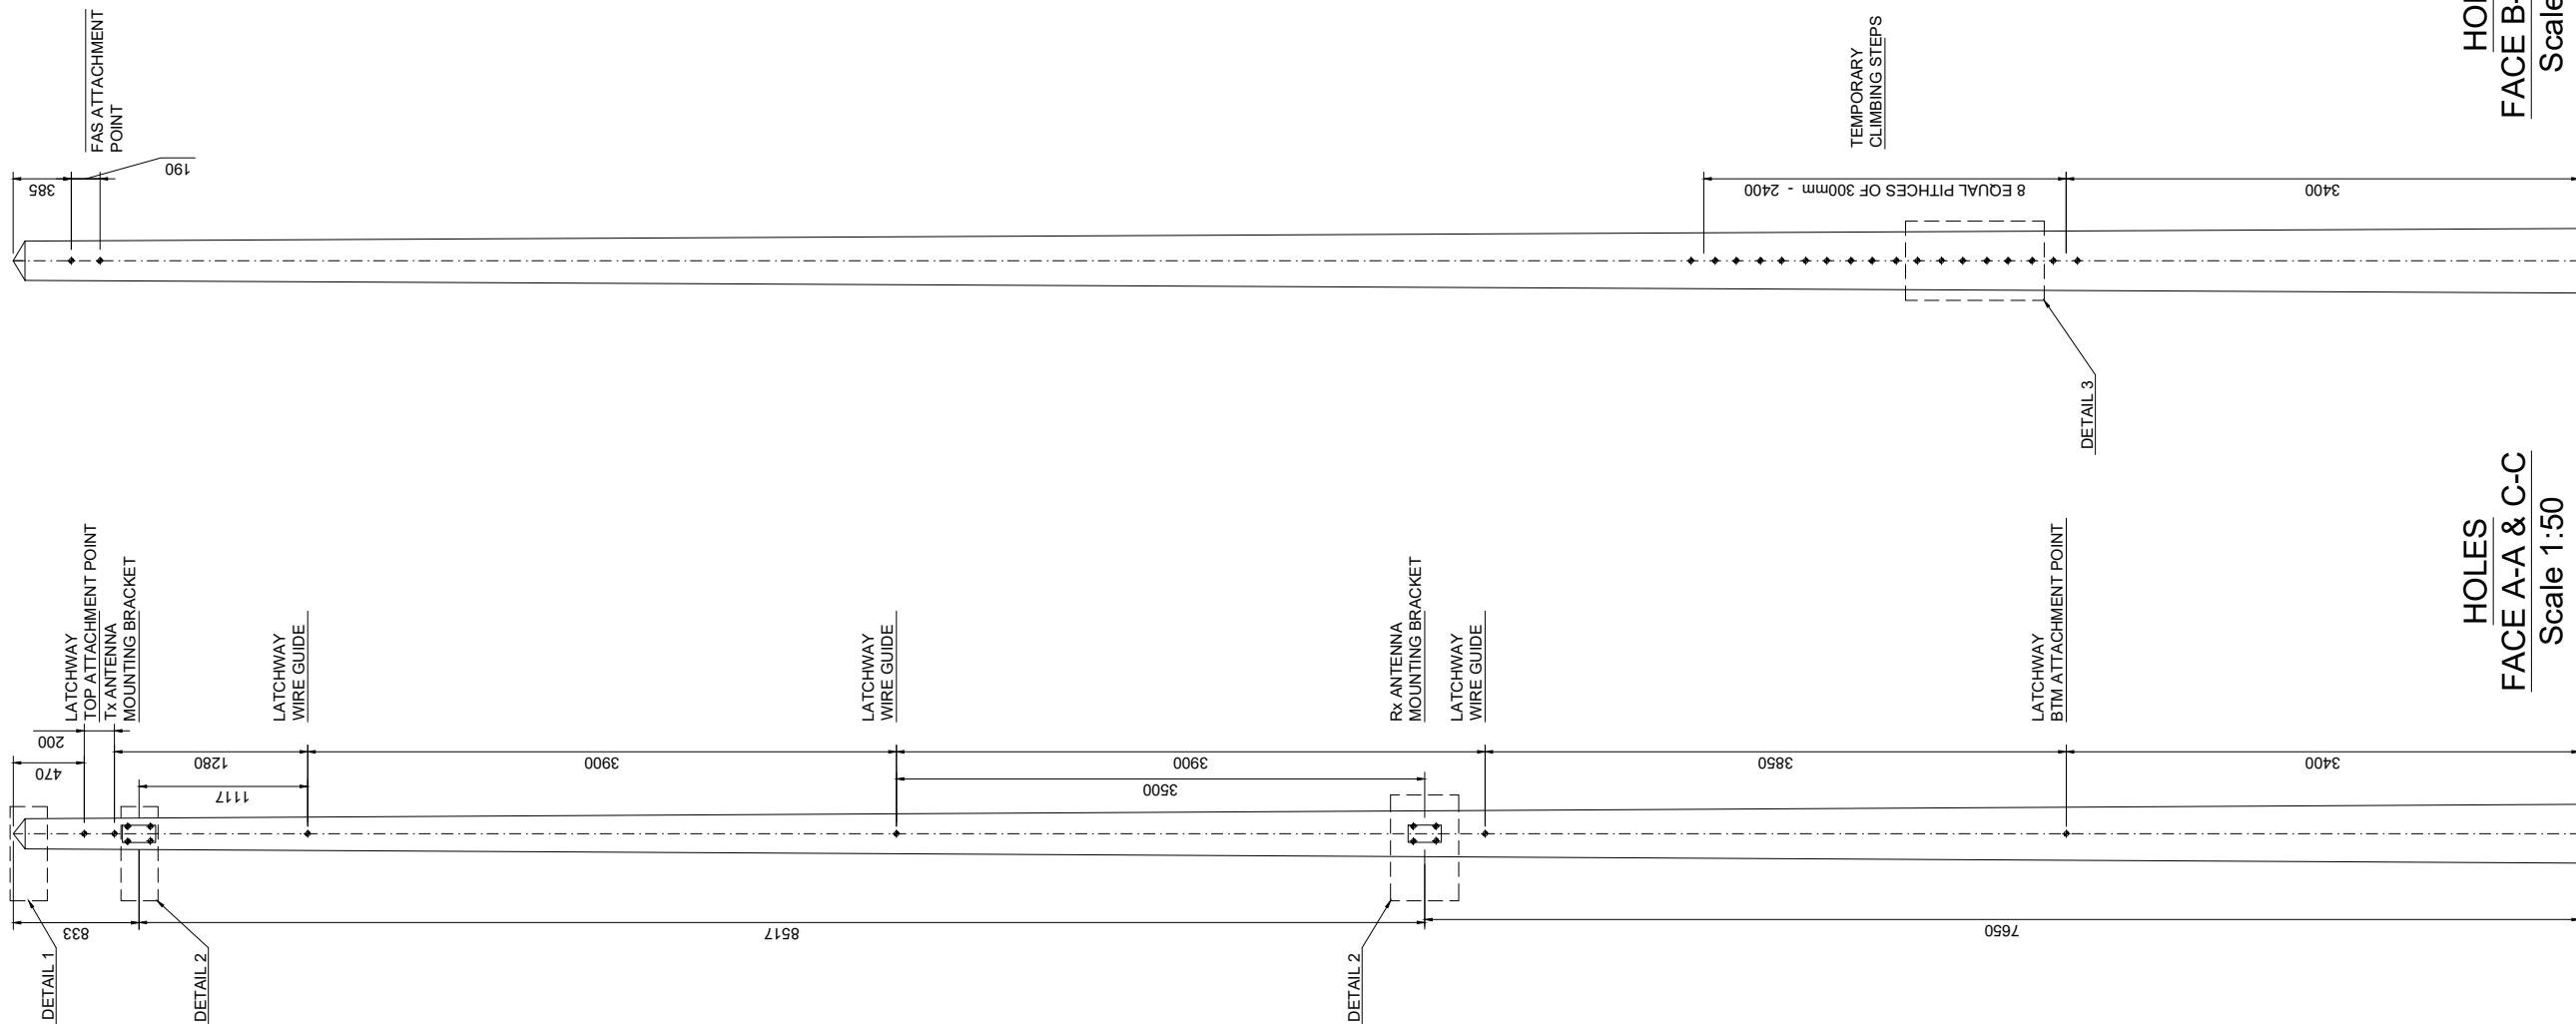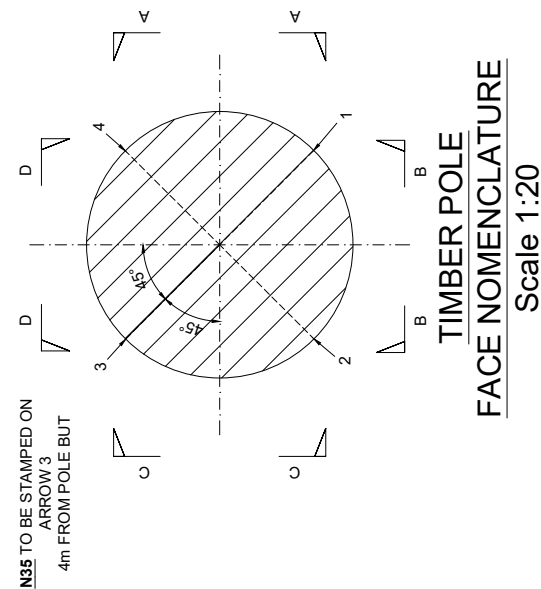

DETAIL 3 - TYPICAL
Scale 1:10

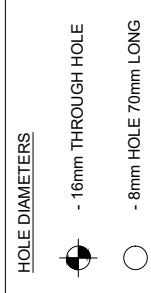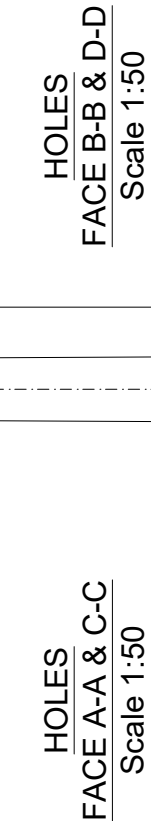

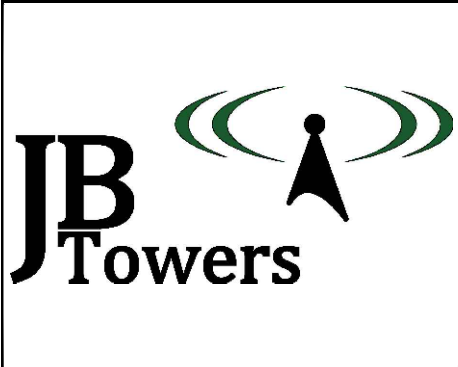

01	FIRST ISSUE			TT	15/05/19
REV	REV			BY	DATE
SCALE AS SHOWN WHEN PRINTED AT A3	DRAWN	AM	CHECKED	MP	APPROVED JBT
	DATE 15/05/19		DATE 15/05/19		DATE 15/05/19
ALL DIMENSIONS IN mm UNLESS OTHERWISE STATED. THIS DRAWING TO BE READ IN CONJUNCTION WITH OTHER RELEVANT DRAWINGS.					

TITLE

NANT-Y-MOEL


TIMBER POLE HOLE SET OUT

SHEET 2 OF 2

SITE ADDRESS

ADJACENT A4061
NORTH OF NANT-Y-MOEL
RHONDDA CYNON TAFF
CF32 7PB

ARQIVA REF. 141296	DRG No. 201	REV 01
-----------------------	----------------	-----------

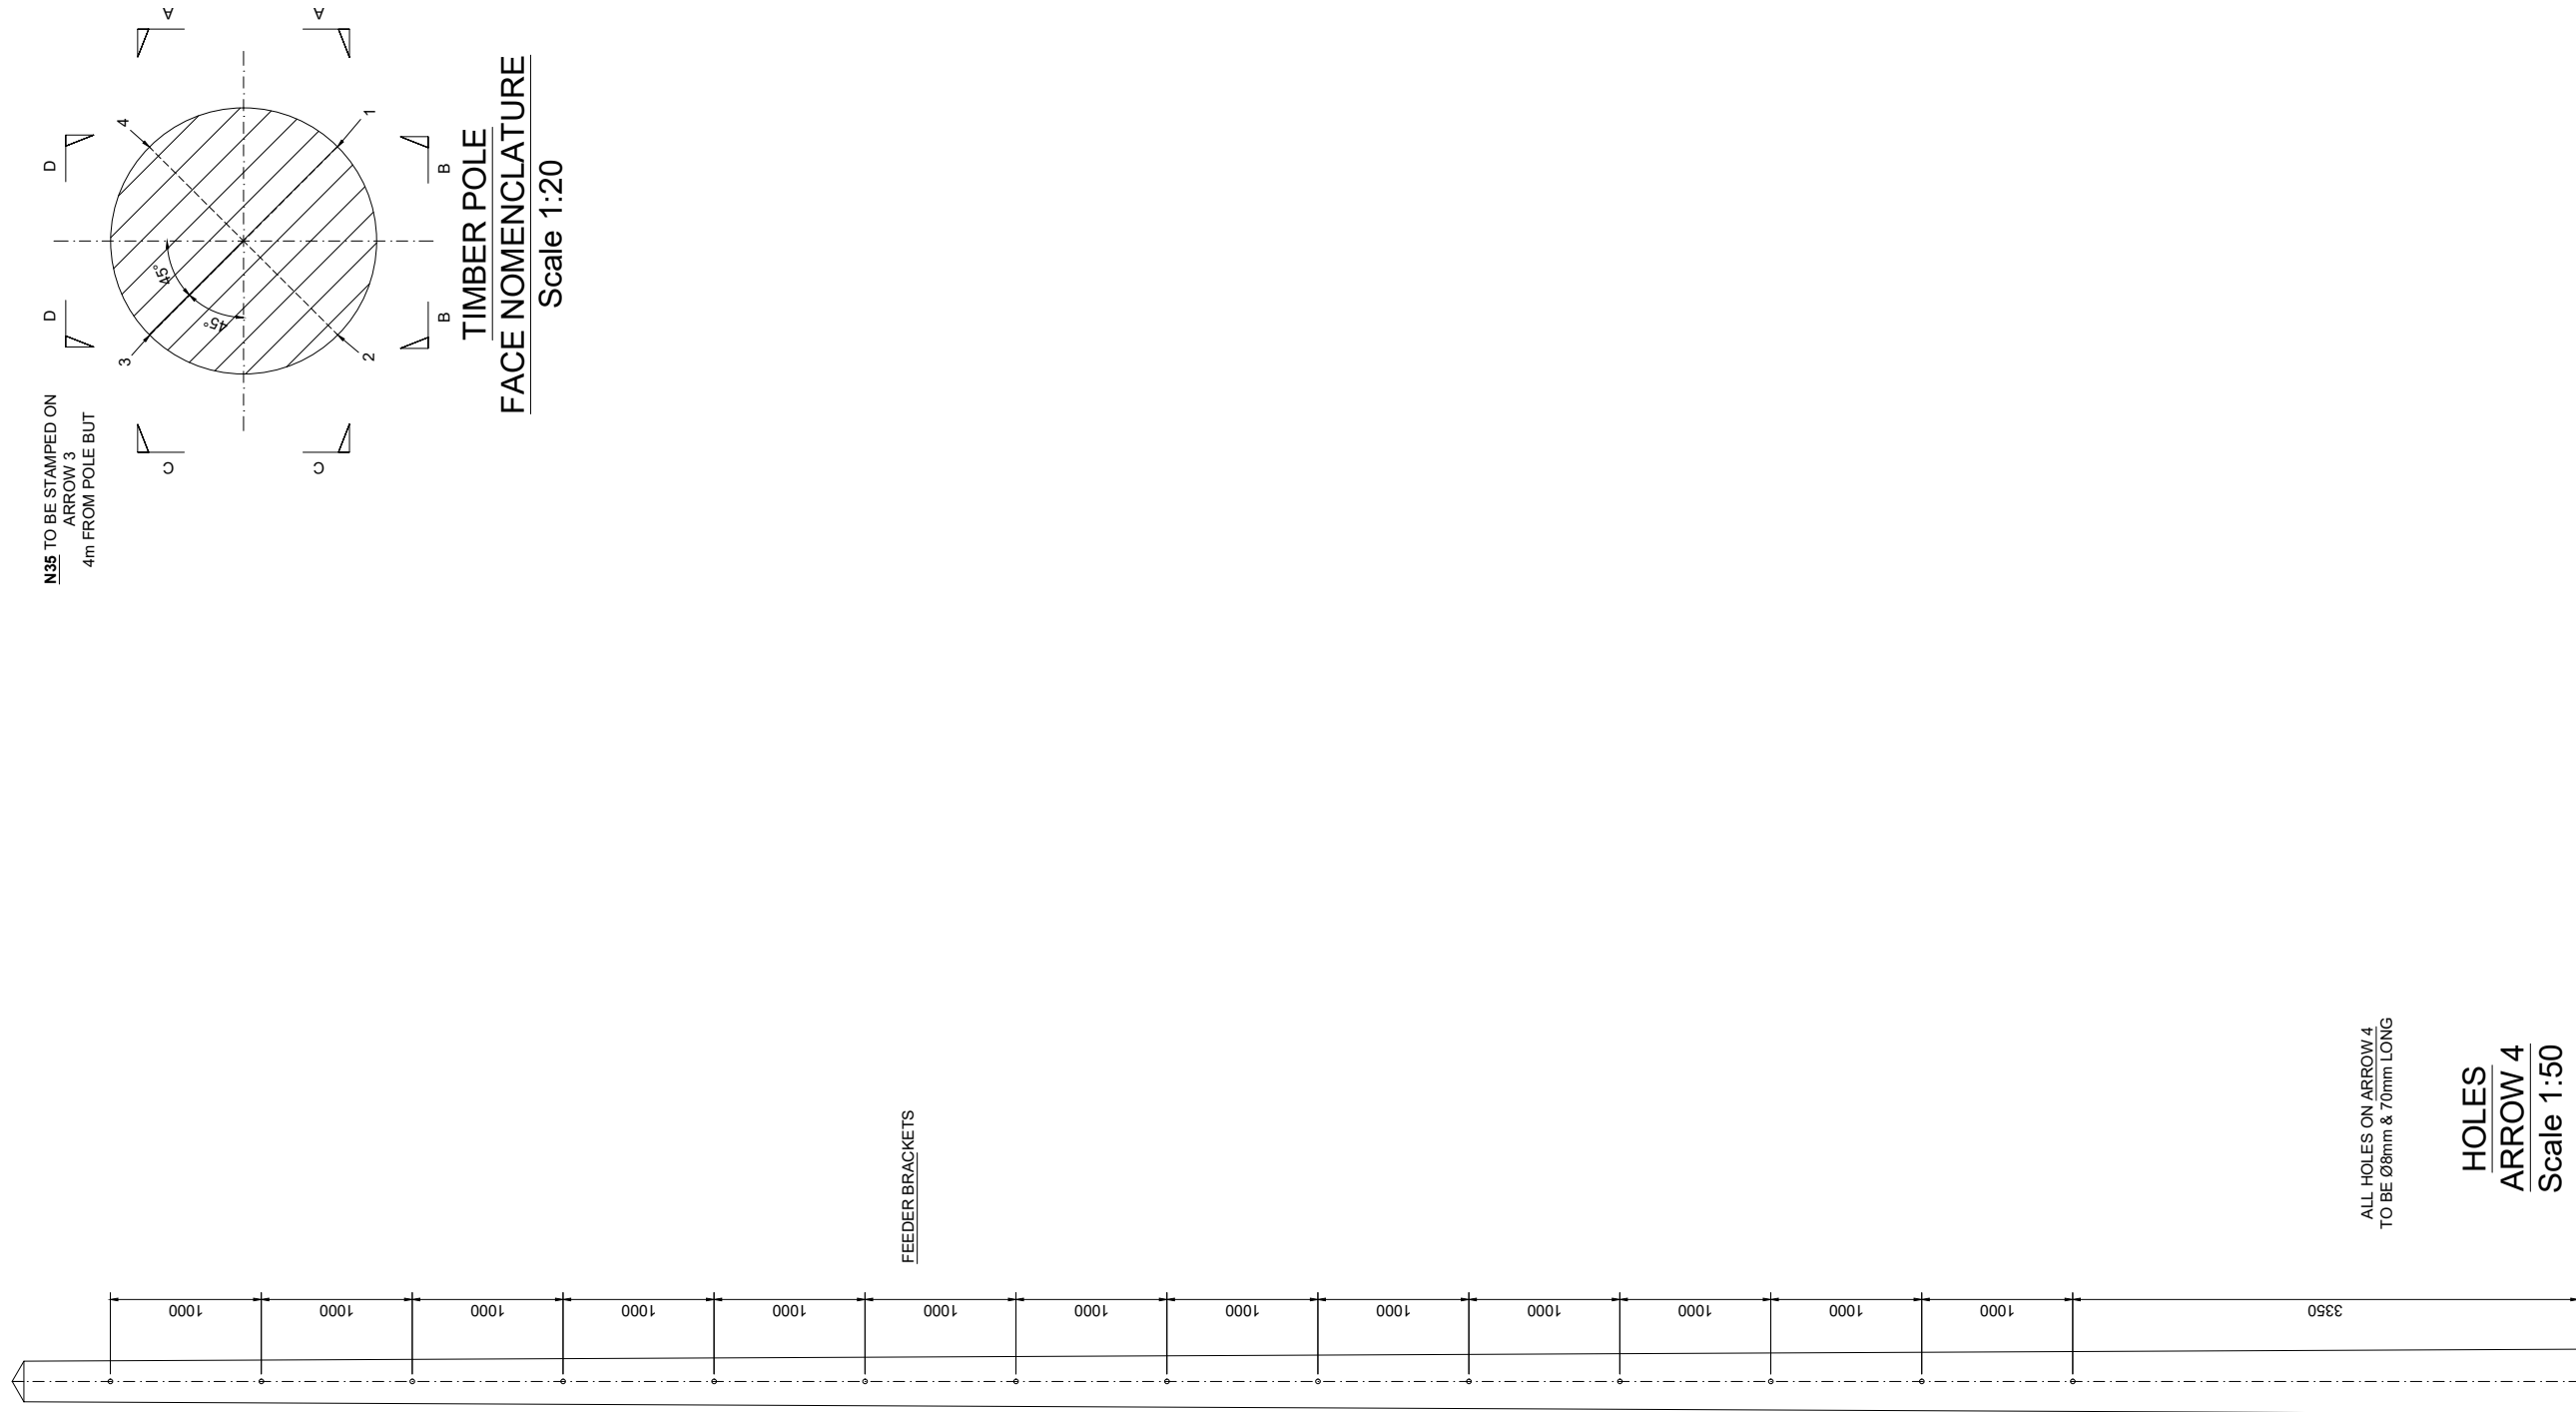REV
01


HOLES
ARROW 4
Scale 1:50


ALL SCALES AS SHOWN WHEN PRINTED AT A3

01	FIRST ISSUE						TT	15/05/19	
REV	REV						BY	DATE	
SCALE AS SHOWN WHEN PRINTED AT A3		DRAWN AM		CHECKED MP		APPROVED JBT			
		DATE 15/05/19		DATE 15/05/19		DATE 15/05/19			
ALL DIMENSIONS IN mm UNLESS OTHERWISE STATED. THIS DRAWING TO BE READ IN CONJUNCTION WITH OTHER RELEVANT DRAWINGS.									


TITLE
NANT-Y-MOEL
TIMBER POLE CUT OUT
DETAIL

SITE ADDRESS
ADJACENT A4061
NORTH OF NANT-Y-MOEL
RHONDDA CYNON TAFF
CF32 7PB

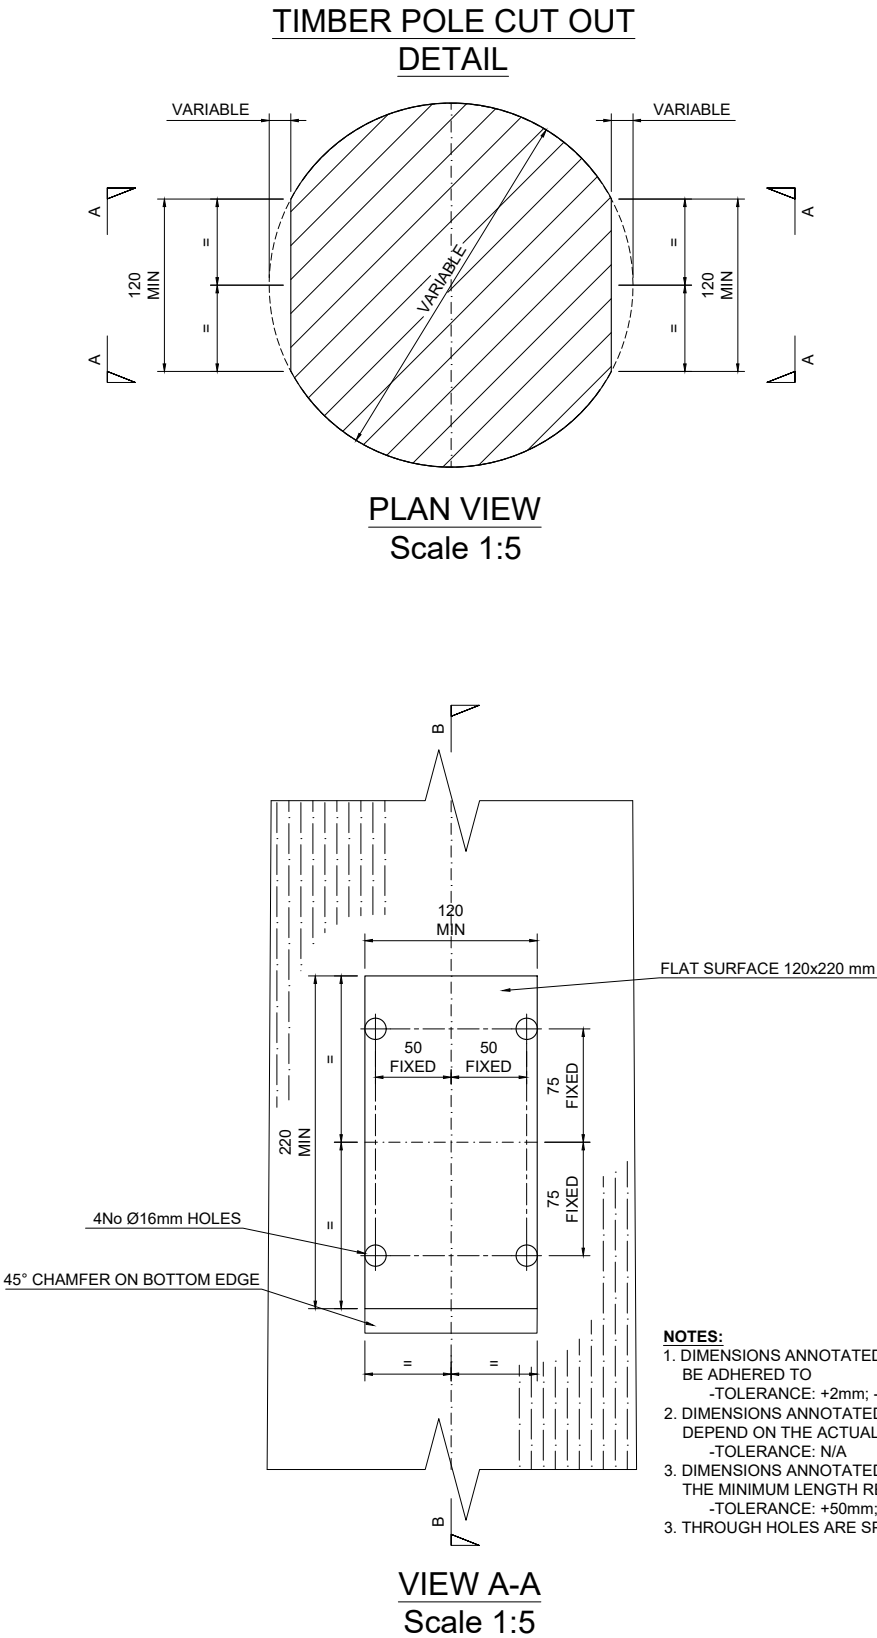

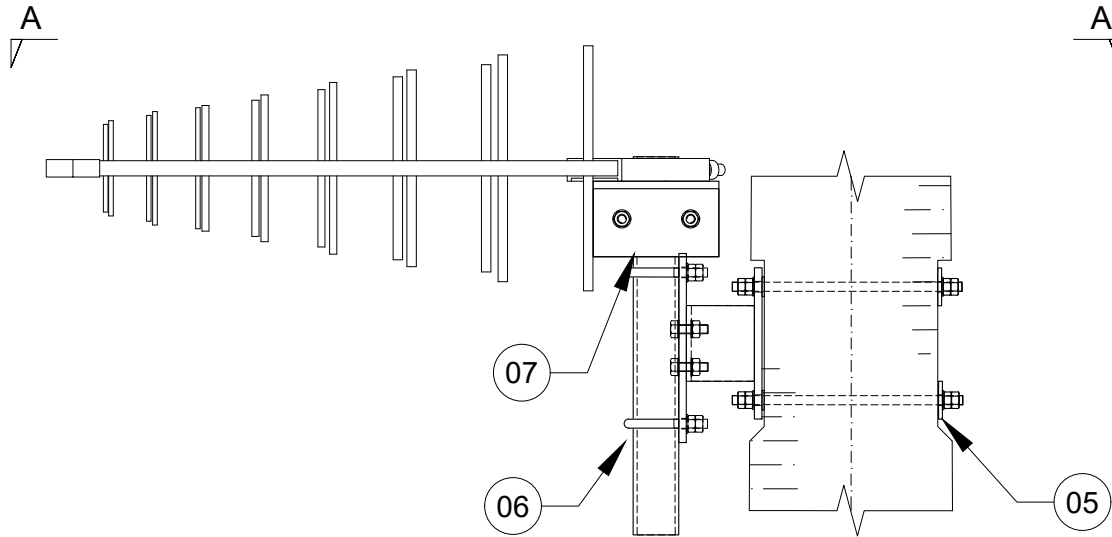

DETAIL G -Tx ANTENNA MOUNT
Scale 1:10

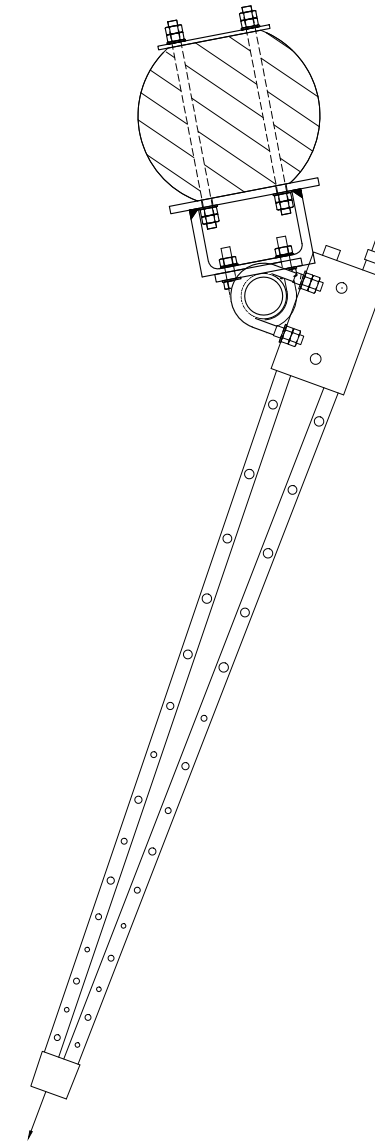


PROPOSED LOG PERIODIC Tx ANTENNA @ 13.5m MEAN 200°

VIEW ON A-A
Scale 1:10

ALL SCALES AS SHOWN WHEN PRINTED AT A3



ALL SCALES AS SHOWN WHEN PRINTED AT A3

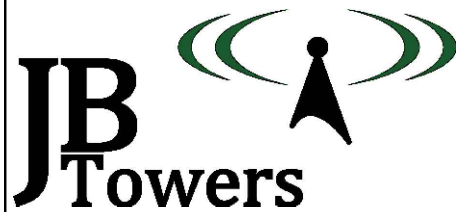

01	FIRST ISSUE			TT	15/05/19
REV	REV			BY	DATE
SCALE AS SHOWN WHEN PRINTED AT A3		DRAWN AM DATE 15/05/19	CHECKED MP DATE 15/05/19	APPROVED JBT DATE 15/05/19	
ALL DIMENSIONS IN mm UNLESS OTHERWISE STATED. THIS DRAWING TO BE READ IN CONJUNCTION WITH OTHER RELEVANT DRAWINGS.					

TITLE
ANTENNA MOUNT
DETAIL G


SITE ADDRESS
ADJACENT A4061
NORTH OF NANT-Y-MOEL
RHONDDA CYNON TAFF
CF32 7PB

ARQIVA REF.
141296

DRG No.
203


REV
01

C

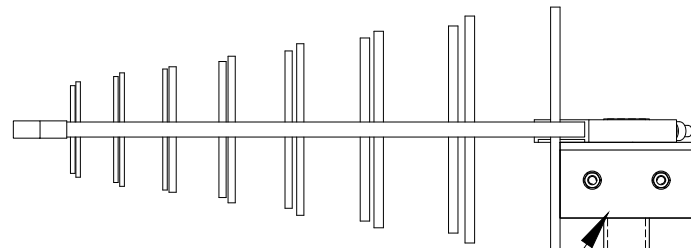

07


06

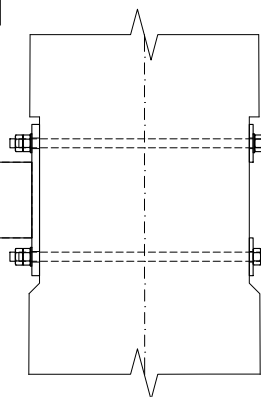

05

DETAIL H - Rx ANTENNA MOUNT
Scale 1:10

C

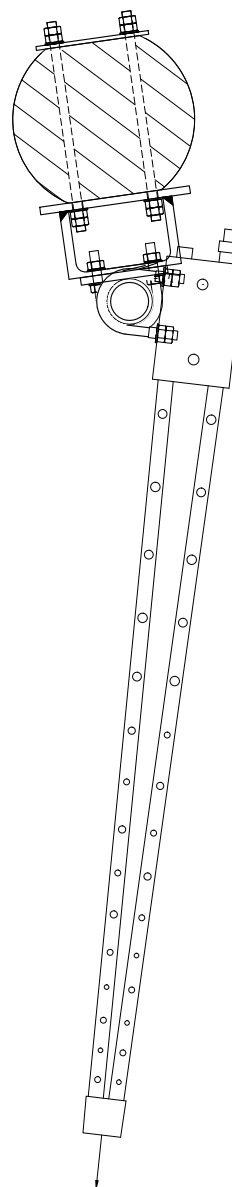


PROPOSED LOG PERIODIC Rx ANTENNA @ 5m MEAN 187°

VIEW ON C-C
Scale 1:10

ALL SCALES AS SHOWN WHEN PRINTED AT A3



ALL SCALES AS SHOWN WHEN PRINTED AT A3

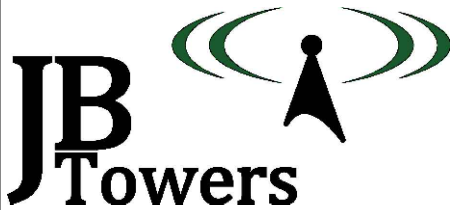


01	FIRST ISSUE				TT	15/05/19
REV	REV				BY	DATE
SCALE AS SHOWN WHEN PRINTED AT A3		DRAWN	AM	CHECKED	MP	APPROVED JBT
		DATE	15/05/19	DATE	15/05/19	DATE 15/05/19
ALL DIMENSIONS IN mm UNLESS OTHERWISE STATED. THIS DRAWING TO BE READ IN CONJUNCTION WITH OTHER RELEVANT DRAWINGS.						

TITLE
ANTENNA MOUNT
DETAIL H


SITE ADDRESS
ADJACENT A4061
NORTH OF NANT-Y-MOEL
RHONDDA CYNON TAFF
CF32 7PB

ARQIVA REF. 141296	DRG No. 204	REV 01
-----------------------	----------------	-----------

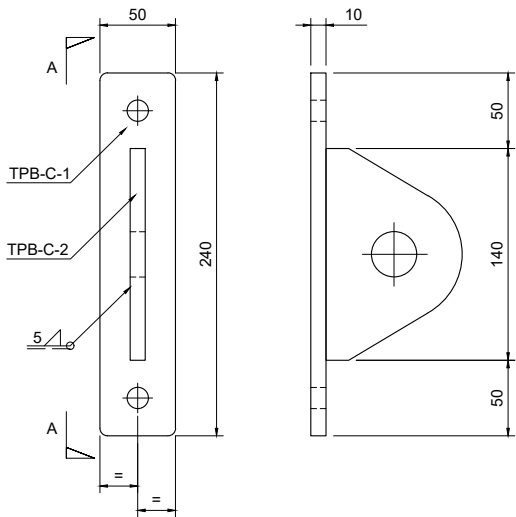

PART TPB-C
Scale 1:5

VIEW A-A
Scale 1:5

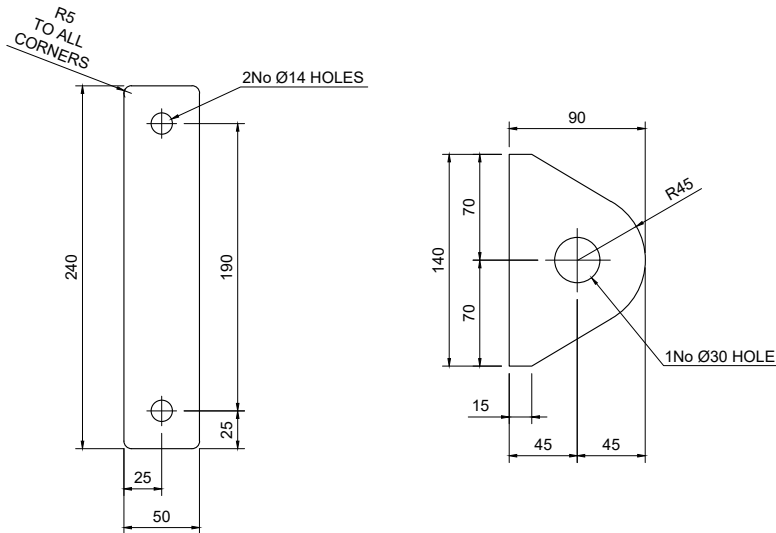


TPB-C-1 - 10mm THICK
Scale 1:5

TPB-C-2 - 10mm THICK
Scale 1:5

Parts list for TPB-C


Item	Part	Quantity	Part description	Length	Material	Weight
01	TPB-C-1	1	240x50x10mm	N/A	S275J0	0.94 kg
02	TPB-C-2	1	140x90x10mm	N/A	S275J0	0.99 kg
03	STUDS	1	M12 STUDDING	350mm	GRADE 8.8	0.31 kg
Total Weight:						2.24 kg

- All steel hot dip galvanized
- Each STUD to be supplied with 4 Full Nuts, 2 Flat Washers and 2 Spring Washers
- For fabrication notes see drawing 302

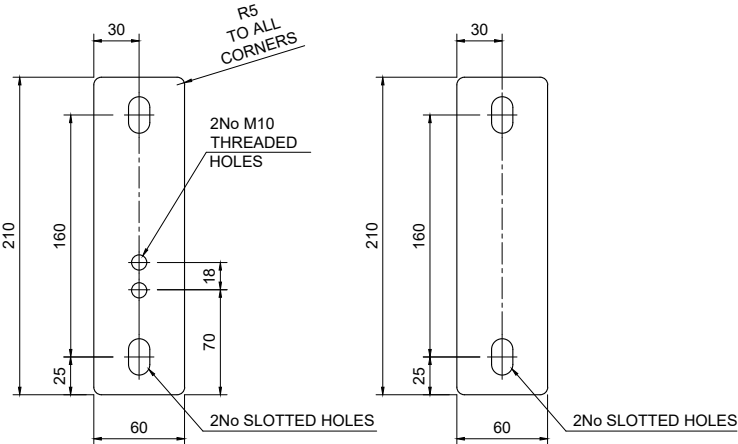

PART TPS-R-1
Scale 1:5

PART TPS-R-2
Scale 1:5

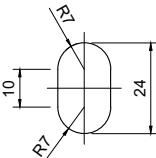


SLOTTED HOLE DETAIL
Scale 1:2

Parts list for TPS-R

Item	Part	Quantity	Part description	Length	Material	Weight
01	TPS-R-1	1	210x60x15mm	N/A	S275J0	1.48 kg
02	TPS-R-2	1	210x60x5mm	N/A	S275J0	0.49 kg
03	STUDS	2	M12 STUDDING	500mm	GRADE 8.8	0.44 kg
04	NUT-S	2	M12 SHALLOW NUT	N/A	GRADE 8.8	-
05	NUT	4	M12 NUT	N/A	GRADE 8.8	-
06	WSH	4	M12 WASHER	N/A	GRADE 8.8	-
Total Weight:						2.41 kg

- All steel hot dip galvanized
- For fabrication notes see drawing 302

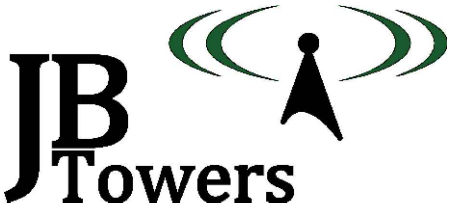

01	FIRST ISSUE	TT	15/05/19
REV	REV	BY	DATE
SCALE AS SHOWN WHEN PRINTED AT A3	DRAWN DATE 15/05/19	AM DATE 15/05/19	CHECKED DATE 15/05/19
APPROVED DATE 15/05/19			
ALL DIMENSIONS IN mm UNLESS OTHERWISE STATED. THIS DRAWING TO BE READ IN CONJUNCTION WITH OTHER RELEVANT DRAWINGS.			

TITLE
ATTACHMENT POINT &
TEMPORARY STEP DETAILS
PARTS: TPB-C; TPS-R










SITE ADDRESS
ADJACENT A4061
NORTH OF NANT-Y-MOEL
RHONDDA CYNON TAFF
CF32 7PB

ARQIVA REF.
141296
DRG No.
300
REV
01

ALL SCALES AS SHOWN WHEN PRINTED AT A3



ALL SCALES AS SHOWN WHEN PRINTED AT A3

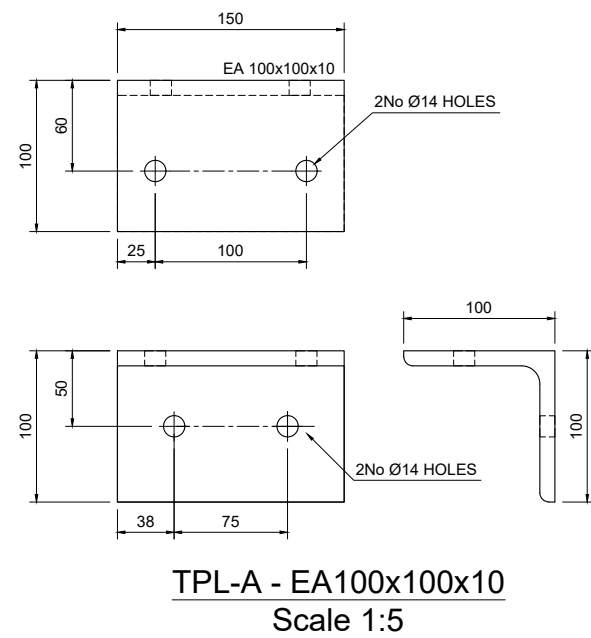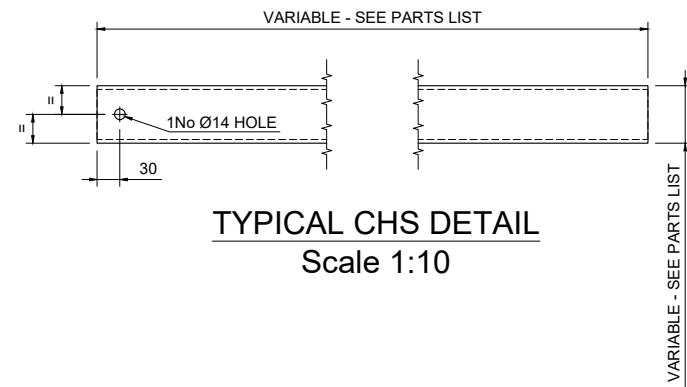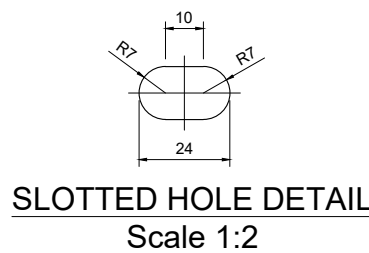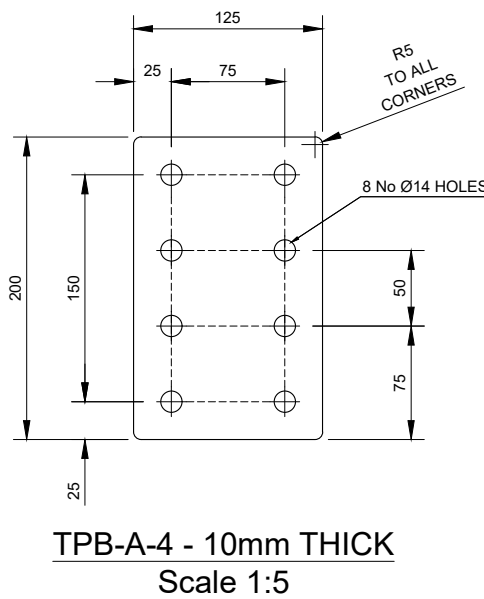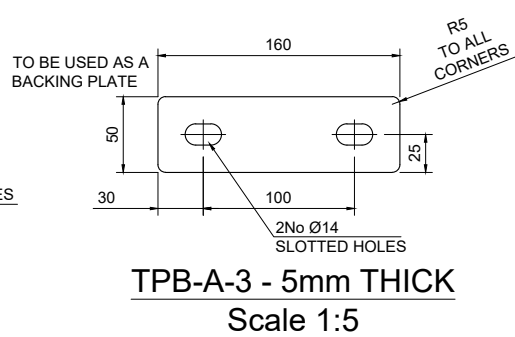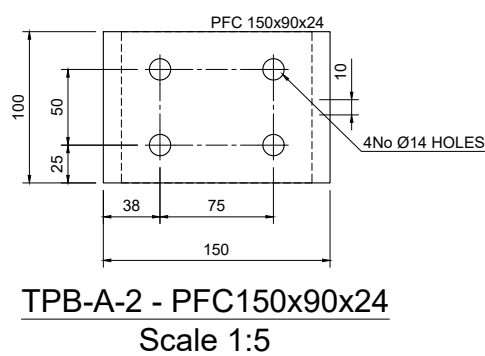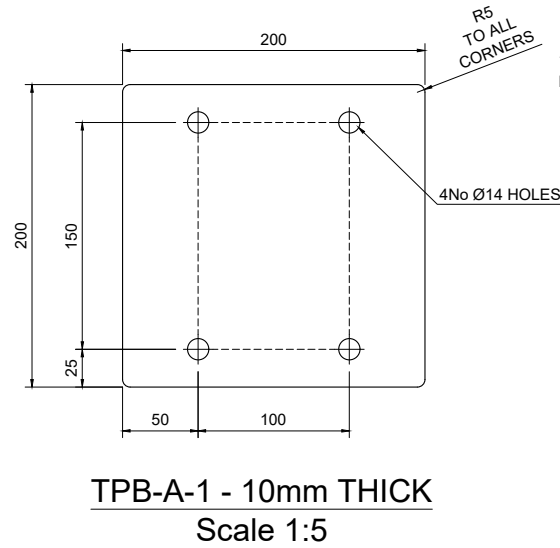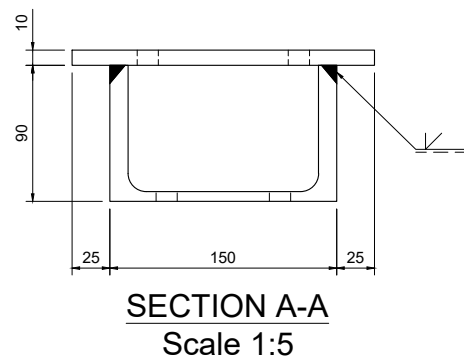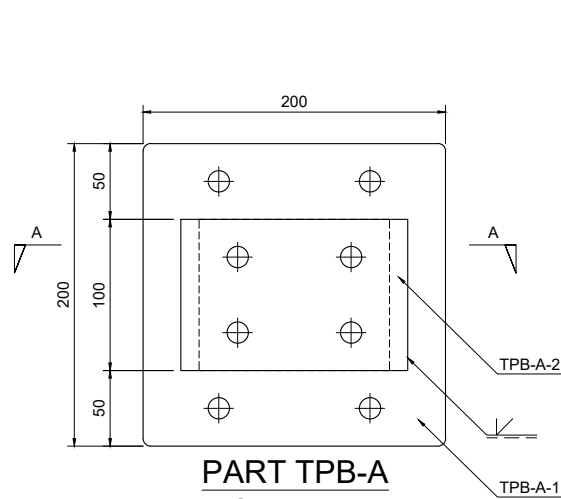

Parts list for TPB-A


Item	Part	Quantity	Part description	Length	Material	Weight
01	TPB-A-1	1	200x200x10mm	N/A	S275J0	3.14 kg
02	TPB-A-2	1	PFC 150x90x24	100mm	S275J0	2.4 kg
03	TPB-A-3	2	160x50x5mm	N/A	S275J0	0.31 kg
04	TPB-A-4	1	200x125x10mm	N/A	S275J0	1.96 kg
05	BOLT	4	M12 45mm LONG (2D+6)	45mm	GRADE 8.8	-
06	STUDS	4	M12 STUDDING	400mm	GRADE 8.8	0.36 kg
07	U-BOLT	2	M12 U-BOLT FOR CHS 60.3mm	N/A	GRADE 8.8	-
Total Weight:						8.17 kg

- All steel hot dip galvanized
- Each BOLT to be supplied with 1 Full Nut, 1 Form E FLat Washer and 1 Spring Washer
- Each STUD & U-BOLT to be supplied with 4 Full Nuts, 2 Flat Washers and 2 Spring Washers
- For fabrication notes see drawing 302

Parts list for TPL-A

Item	Part	Quantity	Part description	Length	Material	Weight
01	TPL-A	1	EA100x100x10	150mm	S275J0	2.25 kg
02	BOLT	2	M12 55mm LONG SET BOLT	55mm	GRADE 8.8	-
03	U-BOLT	1	M12 U-BOLT FOR CHS 60.3mm	N/A	GRADE 8.8	-
Total Weight:						2.25 kg

- All steel hot dip galvanized
- Each STUD & U-BOLT to be supplied with 4 Full Nuts, 2 Flat Washers and 2 Spring Washers
- Each BOLT to be supplied with 1 Full Nut, 1 Form E FLat Washer and 1 Spring Washer
- For fabrication notes see drawing 302

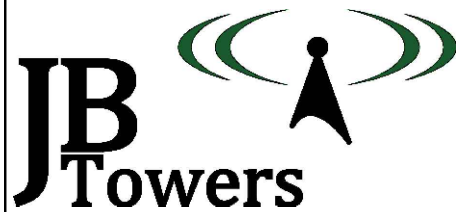

01	FIRST ISSUE	TT	15/05/19
REV	REV	BY	DATE
SCALE AS SHOWN WHEN PRINTED AT A3	DRAWN AM	CHECKED MP	APPROVED JBT
DATE 15/05/19	DATE 15/05/19	DATE 15/05/19	
ALL DIMENSIONS IN mm UNLESS OTHERWISE STATED. THIS DRAWING TO BE READ IN CONJUNCTION WITH OTHER RELEVANT DRAWINGS.			

TITLE
STEELWORK BRACKET & TYPICAL CHS DETAIL
PART: TPB-A

SITE ADDRESS
ADJACENT A4061 NORTH OF NANT-Y-MOEL RHONDDA CYNON TAFF CF32 7PB

ARQIVA REF. 141296
DRG No. 301
REV 01

ALL SCALES AS SHOWN WHEN PRINTED AT A3




ALL SCALES AS SHOWN WHEN PRINTED AT A3

Item	Part	Drawing	Quantity	Part description	Length	Material	Weight
01	01	200	1	3 MAN LATCHWAY SYSTEM & 3No. WIRE GUIDES FOR FACE MOUNTED MONOPOLE	14000	N/A	-
02	TPB-C	300	2	FALL ARREST ATTACHMENT POINT	N/A	S275J0	4.48 kg
03	03	200	36	PERMANENT BT STEP c/w 3No 10x75mm ZINC-PLATED COACH SCREWS	N/A	S275J0	24.4 kg
04	TPS-R	300	9	'MonoStep' ASSEMBLY	N/A	S275J0	21.69 kg
05	TPB-A	301	2	MOUNTING BRACKET	N/A	S275J0	16.34 kg
06	06	203	2	CHS 60.3x5mm	500mm	S355J2H	6.82 kg
07	TPL-A	301	2	MOUNTING BRACKET	N/A	S275J0	4.50 kg
08	08	200	1	FEEDER COVER - 2/CG/100	3500mm	UV RESISTANT PLASTIC	-
09	09	200	14	FEEDER CLAMP - 2/FCD/028	N/A	POLYPROPYLENE	-
10	10	200	14	M10 SCREW DOWELS WTH M10 NUT	100mm	STAINLESS STEEL	-
11	11	200	1	PoleSaver	750mm	N/A	-
12	12	200	8	M12 STUD + 4No NUTS + 2No FLAT WASHERS + 1No Ø50mm WASHER (FOR FALL ARREST SYSTEM)	500mm	GRADE 8.8	3.56 kg
Total Weight:							81.79 kg

- All steel hot dip galvanized
- All U-BOLTS to be FLA supply, each Supplied with 4 Full Nuts, 2 Flat Washers and 2 Spring Washers

NOTES:

1. WELDING TO BE IN ACCORDANCE WITH BS EN 1011-1:2009
2. LINEAR DIMS TO BE WITHIN ±1mm;
3. ANGULAR TOLERANCES TO BE WITHIN 0.5°
4. WELDING SYMBOLS ARE IN ACCORDANCE WITH BS EN 22553:1995
5. ALL PROFILE EDGES TO BE DRESSED AND SHARP CORNERS REMOVED
6. ALL WELD SIZES ARE FINAL SIZES
7. ALL WELDED JOINTS ARE TO BE PICKLE TIGHT
8. ALL STEELWORK TO BE BS EN 10025 GRADE S275 J0 UNO
9. HOT DIPPED GALVANISED TO BS EN ISO 1461. (ALL HOLLOW SECTIONS TO BE GRADE S355 J0H)
10. ALL STEEL IS TO BE SUPPLIED IN ACCORDANCE WITH EN 1090 TO EXECUTION CLASS 2
11. ALL NON PRE-LOADED BOLTS TO BE COMPLIANT STRUCTURAL BOLTS TO BS EN ISO 15048 PARTS 1&2.
12. STEELWORK COMPONENTS SHALL BE HOT DIP GALVANISED TO ACHIEVE A "VERY HIGH" DURABILITY FOR AN ENVIRONMENT CATEGORY CODE C4 FROM TABLE 1 IN BS EN ISO 14713
13. BOLTS AND NUTS SHALL BE SUPPLIED IN ACCORDANCE WITH BS 7371, SPUN GALVANISED IN ACCORDANCE WITH ISO 10684, THE NUTS RE-TAPPED AFTER GALVANISING, AND THE THREADS TREATED WITH GREASE.
14. ALL BOLTS TO BE CUT ON SITE TO EXTEND MAX 10mm BEYOND THE NUT WHEN TIGHTENED UNO.
15. ALL SITE DRILLED HOLE/CUT ENDS TO BE TREATED WITH METAFLUX 70-40 ZINC PASTE FOLLOWED BY 1 COAT OF 7-42 ZINC ALU OR 70-16 ALUMINIUM SPRAY

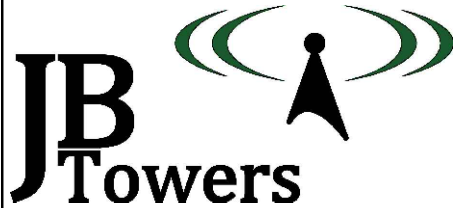

01	FIRST ISSUE			TT	15/05/19
REV	REV			BY	DATE
SCALE AS SHOWN WHEN PRINTED AT A3		DRAWN	AM	CHECKED	MP
		DATE	15/05/19	DATE	15/05/19
		DATE	15/05/19	DATE	15/05/19
ALL DIMENSIONS IN mm UNLESS OTHERWISE STATED. THIS DRAWING TO BE READ IN CONJUNCTION WITH OTHER RELEVANT DRAWINGS.					

TITLE
PARTS LIST

SITE ADDRESS		
ADJACENT A4061 NORTH OF NANT-Y-MOEL RHONDDA CYNON TAFF CF32 7PB		
ARQIVA REF. 141296	DRG No. 302	REV 01

ALL SCALES AS SHOWN WHEN PRINTED AT A3



ALL SCALES AS SHOWN WHEN PRINTED AT A3