
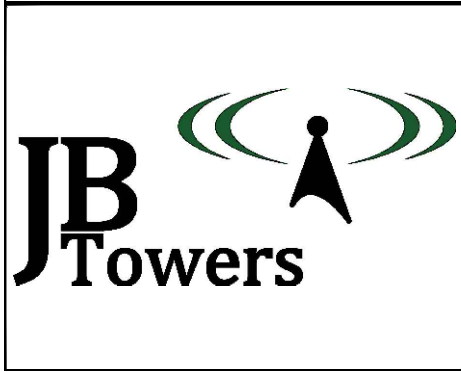
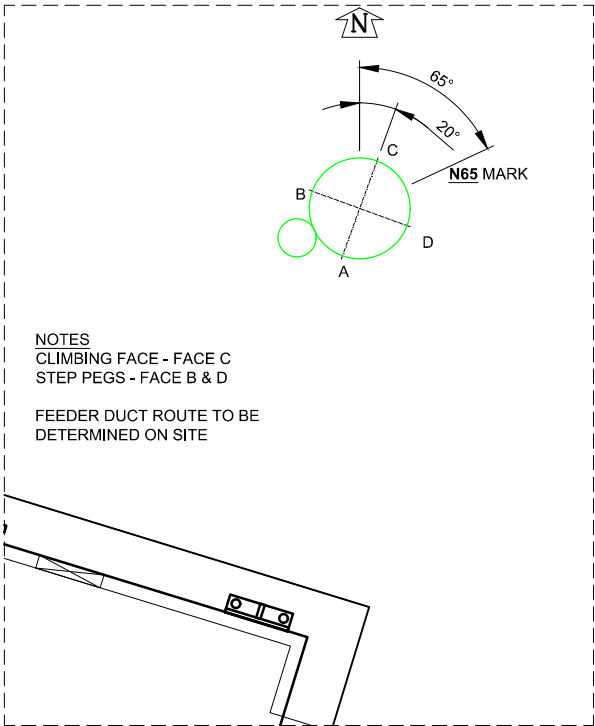


DRAWING ISSUE SHEET

[illegible]

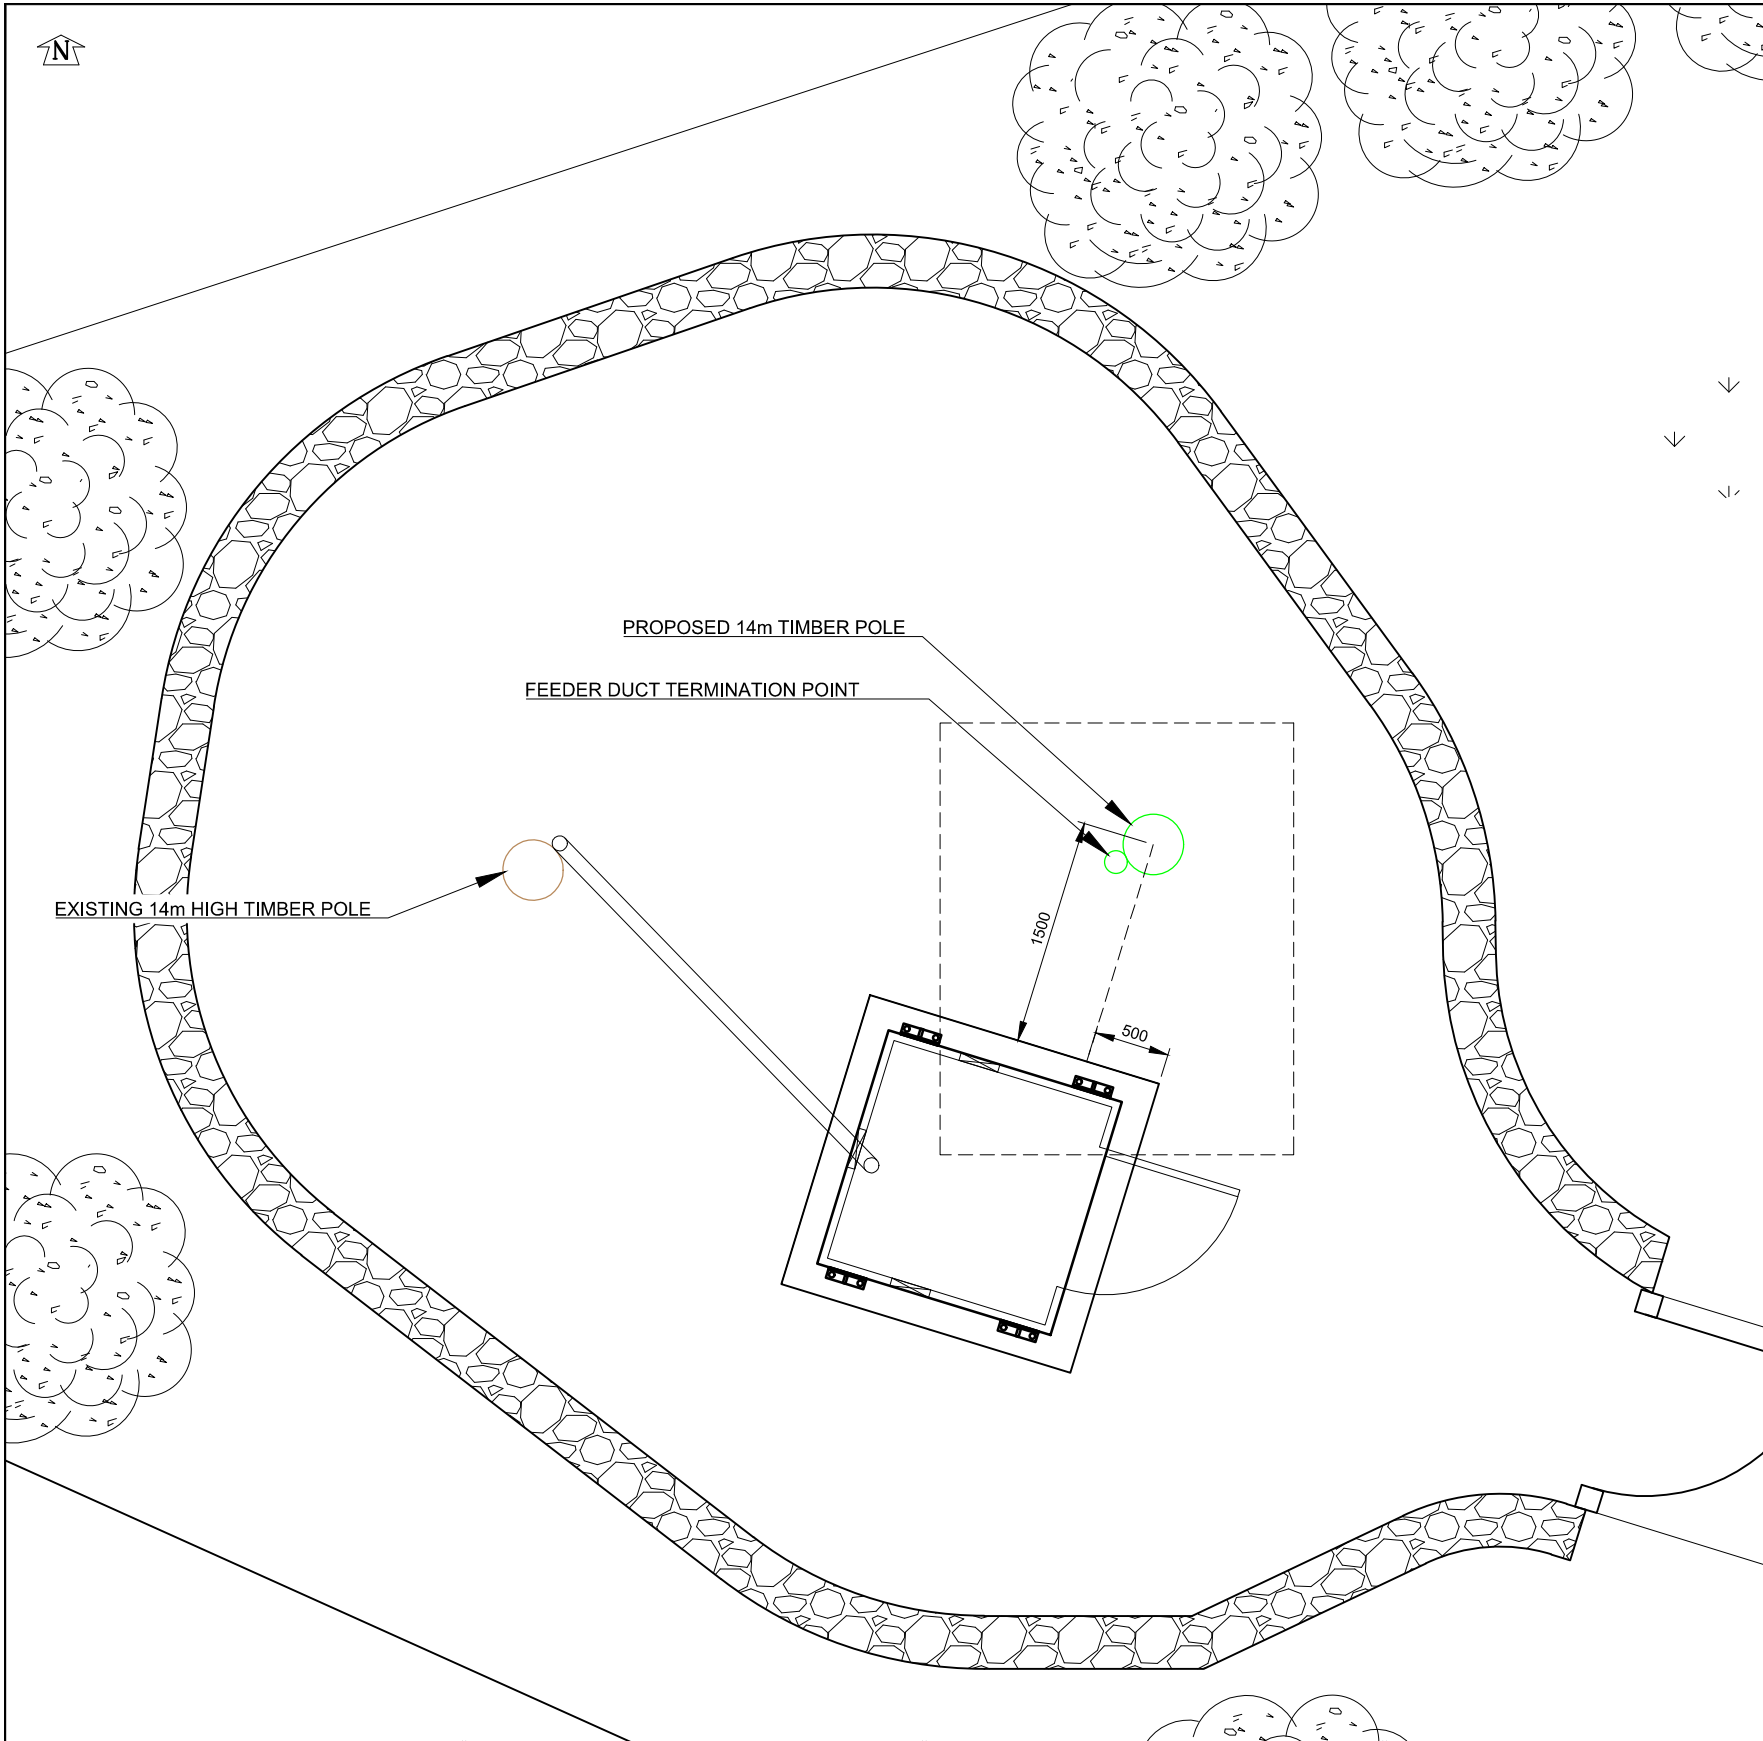


02	REVISED POSITION OF PROPOSED TIMBER POLE			AM	16/11/20
01	FIRST ISSUE			AM	22/09/20
REV	REV			BY	DATE
SCALE AS SHOWN		DRAWN	AM	CHECKED	MP
WHEN PRINTED AT A3		DATE	22/09/20	DATE	22/09/20
		DATE	22/09/20	DATE	22/09/20
ALL DIMENSIONS IN mm UNLESS OTHERWISE STATED. THIS DRAWING TO BE READ IN CONJUNCTION WITH OTHER RELEVANT DRAWINGS.					

TITLE
NEWPORT BAY
SITE PLAN

SITE ADDRESS NEWPORT BAY MILL STREET BETWS-Y-COED ABERCONWY AND COLWYN LL24 0BB		
ARQIVA REF. 141277	DRG No. 100	REV 02

ALL SCALES AS SHOWN WHEN PRINTED AT A3



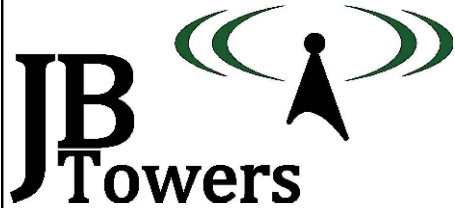

01	FIRST ISSUE			AM	22/09/20
REV	REV			BY	DATE
SCALE AS SHOWN		DRAWN	AM	CHECKED	MP
WHEN PRINTED AT A3		DATE	22/09/20	DATE	22/09/20
		APPROVED	JBT	DATE	22/09/20
ALL DIMENSIONS IN mm UNLESS OTHERWISE STATED. THIS DRAWING TO BE READ IN CONJUNCTION WITH OTHER RELEVANT DRAWINGS.					



TITLE
NEWPORT BAY
GENERAL ARRANGEMENT
SHEET 1 OF 3

SITE ADDRESS
NEWPORT BAY
MILL STREET
BETWS-Y-COED
ABERCONWY AND
COLWYN
LL24 0BB

ARQIVA REF.
141277

DRG No.
200

REV
01

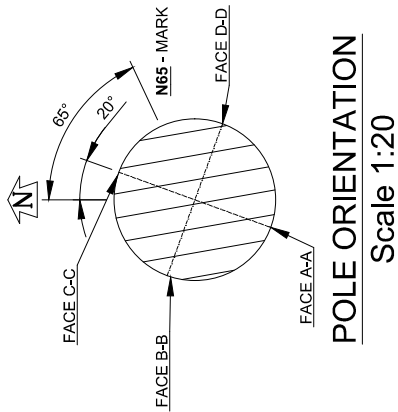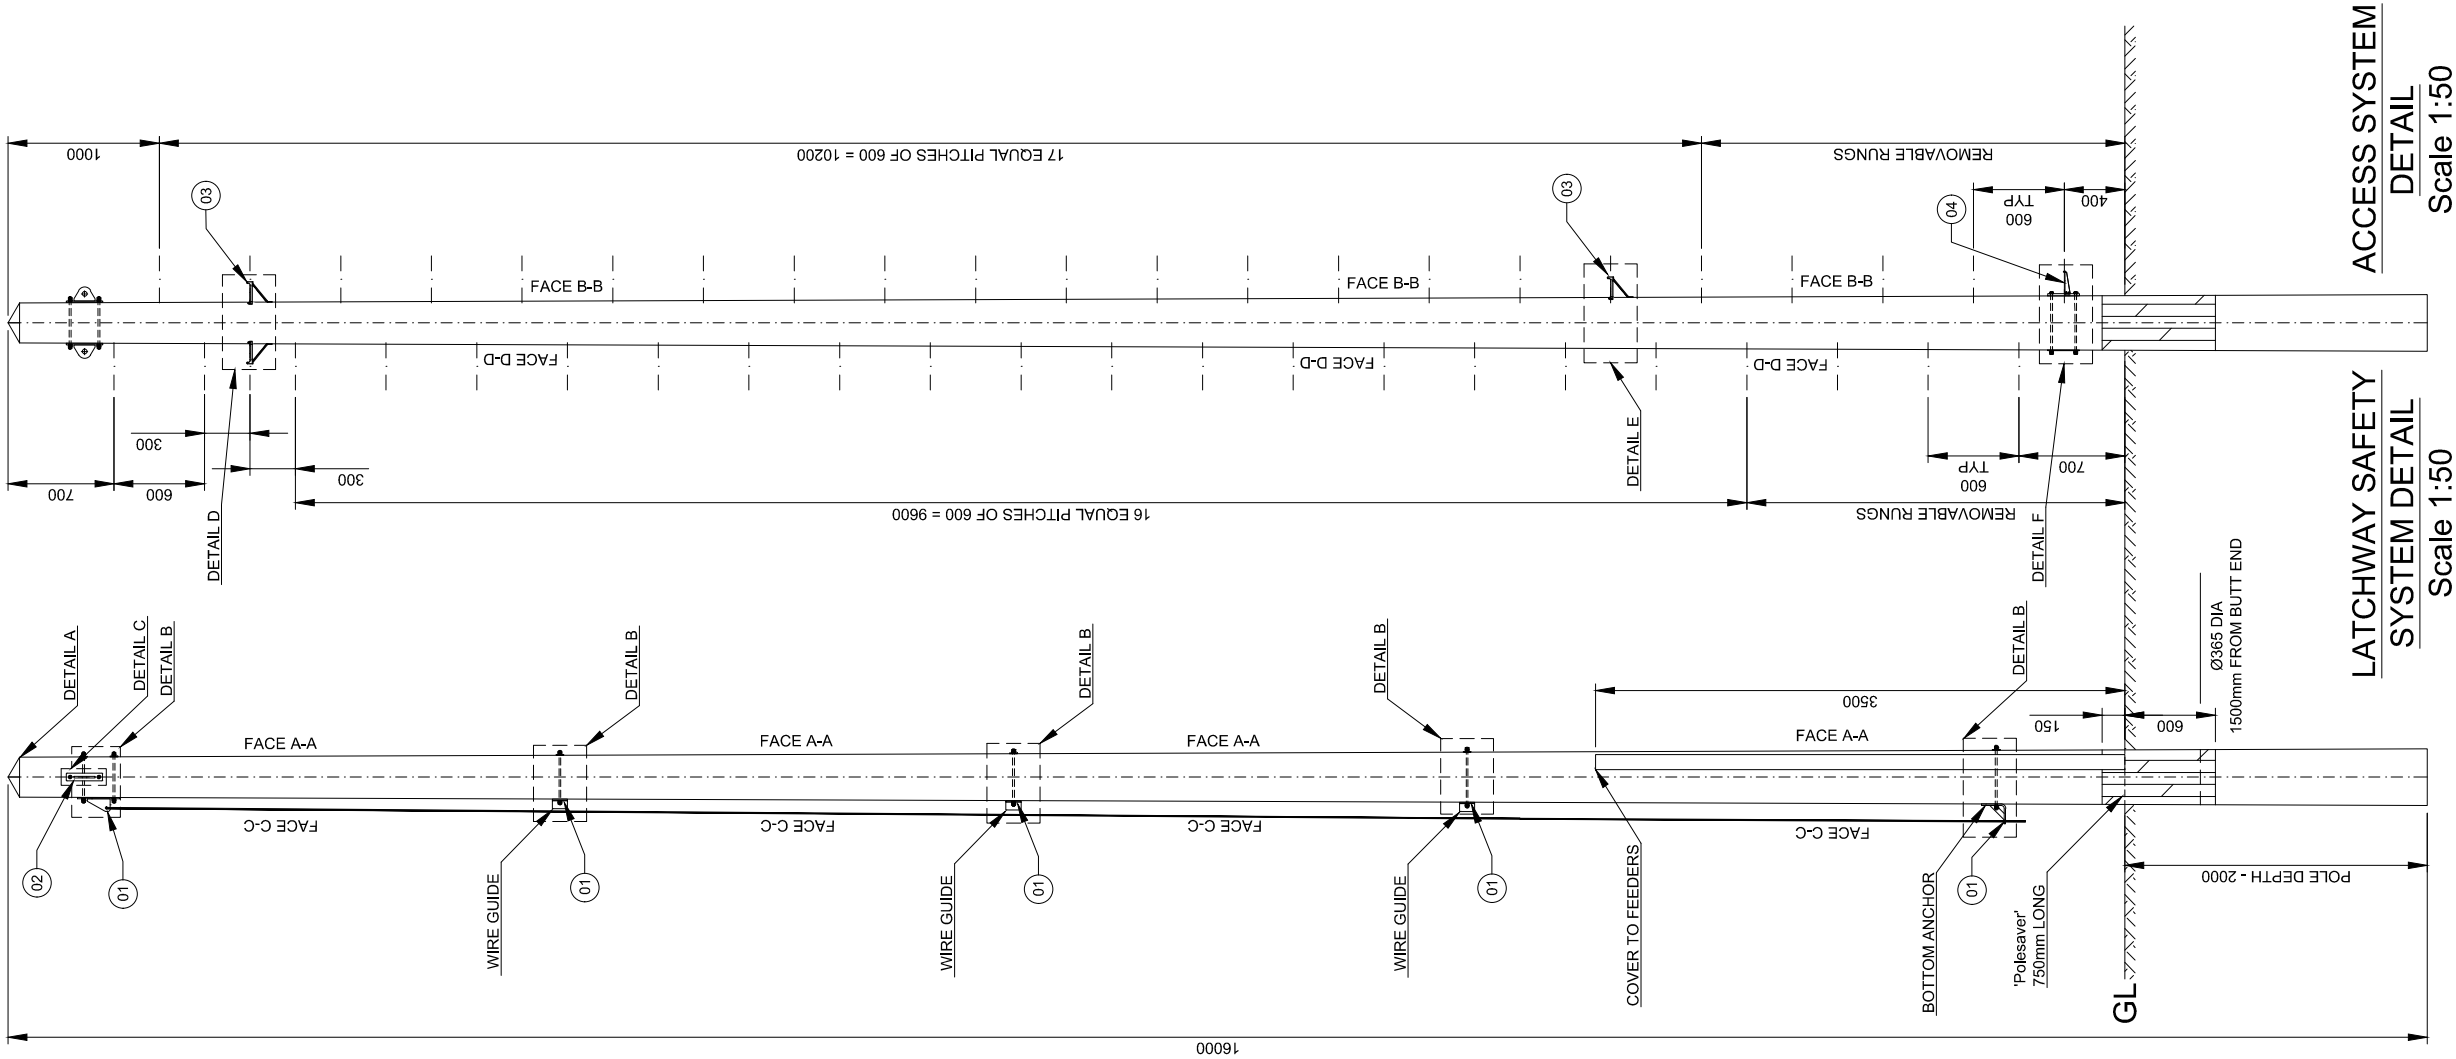

NOTES

1. SEE DRAWING 305 FOR PARTS LIST
2. ALL BOLTS TO BE CUT ON SITE TO EXTEND MAX 10mm BEYOND THE NUT WHEN TIGHTENED UNO.
3. ALL SITE DRILLED HOLE/CUT ENDS TO BE TREATED WITH METALUX 70-40 ZINC PASTE FOLLOWED BY 1 COAT OF 7-42 ZINC ALU OR 70-16 ALUMINIUM SPRAY

TIMBER POLE

1. POLE TO BE SUPPLIED IN ACCORDANCE WITH BS EN14229 & SHALL HAVE MIN. CHARACTERISTIC BENDING STRENGTH OF 30N/mm2 & MIN. YOUNGS MODULUS (PARALLEL TO GRAIN) OF 10kN/mm2.
2. MARKINGS ON FINISHED POLE SHALL BE AT 3.5m FROM BUTT AND COMPLY WITH BS EN 14229 UNO
3. AS FAR AS PRACTICABLE ALL CUTTING, SCARFING & DRILLING TO BE DONE BEFORE CREOSOTING. IF NOT ALL CUT, DRILLED & SCARFED SURFACES TO BE COATED WITH A MIXTURE OF CREOSOTE & TAR.
4. POLE TO BE PRESSURE IMPREGNATED WITH CREOSOTE IN ACCORDANCE WITH BS EN 14229
5. MINIMUM DIAMETERS
TOP - Ø200mm
BOTTOM - Ø375mm

PLANTING

1. CAT SCANNER IS TO BE USED IN ORDER TO CONFIRM THE POSITIONS OF BURIED SERVICES.
2. TIMBER POLE TO BE PLANTED WITH N65 MARKING AT 3.0m FROM BUT FACING 65° FROM NORTH (CLOCKWISE)
3. SEE DRAWING 400 FOR FOUNDATION DETAILS


LATCHWAY SAFETY
SYSTEM DETAIL
Scale 1:50

ACCESS SYSTEM
DETAIL
Scale 1:50



ALL SCALES AS SHOWN WHEN PRINTED AT A3

ALL SCALES AS SHOWN WHEN PRINTED AT A3

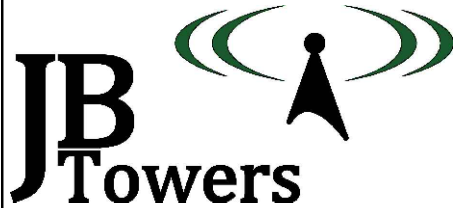

01	FIRST ISSUE			AM	22/09/20
REV	REV			BY	DATE
SCALE AS SHOWN		DRAWN	AM	CHECKED	MP
WHEN PRINTED AT A3		DATE	22/09/20	DATE	22/09/20
				APPROVED	JBT
				DATE	22/09/20
ALL DIMENSIONS IN mm UNLESS OTHERWISE STATED. THIS DRAWING TO BE READ IN CONJUNCTION WITH OTHER RELEVANT DRAWINGS.					




TITLE
NEWPORT BAY
GENERAL ARRANGEMENT
SHEET 2 OF 3

SITE ADDRESS
NEWPORT BAY
MILL STREET
BETWS-Y-COED
ABERCONWY AND
COLWYN
LL24 0BB

ARQIVA REF.
141277

DRG No.
200

REV
01

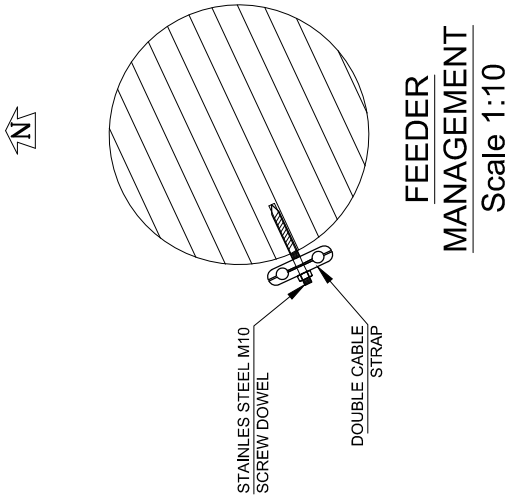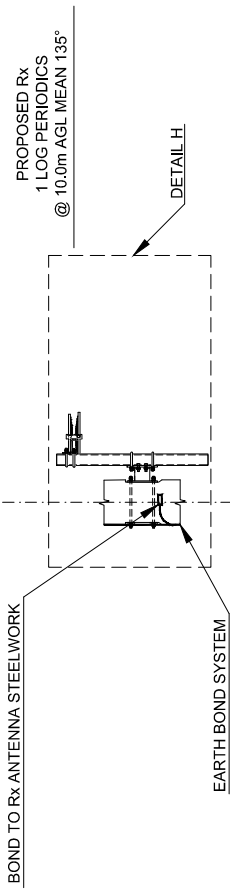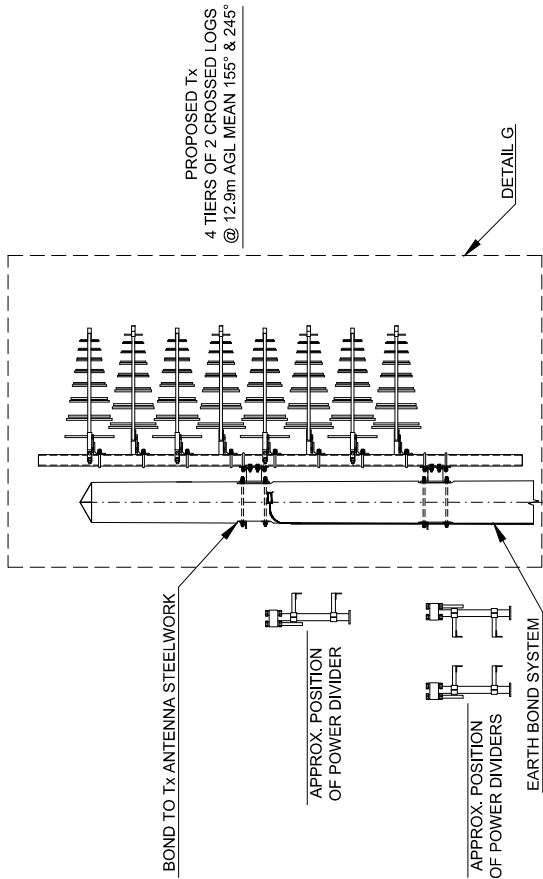


NOTES

1. AS FAR AS IS PRACTICABLE ALL CUTTING SCARFING AND DRILLING TO BE DONE BEFORE CREOSOTING. WHERE THIS IS NOT POSSIBLE ALL CUT, DRILLED, AND SCARFED SURFACES TO BE COATED WITH A MIXTURE OF CREOSOTE AND TAR

FEEDERS


1. SUPPLY OF FEEDERS BY OTHERS LCF7/8-50 TO Tx ANTENNA & LCF12-50 TO Rx ANTENNA
2. FEEDERS FIXED AT 1000mm CENTRES
1. CONNECT EARTH BOND TO NEW EARTHING SYSTEM
2. MAXIMUM VALUE FOR GROUND RESISTANCE TO BE 10 OHMS
3. CABLE OR TAPE TO BE FIXED TO POLE AT 1000mm CENTRES
4. EARTHING SHOULD COMPLY WITH ARQIVA'S DOCUMENT BOS147

ANTENNA AND EARTHING ARRANGEMENT Scale 1:50

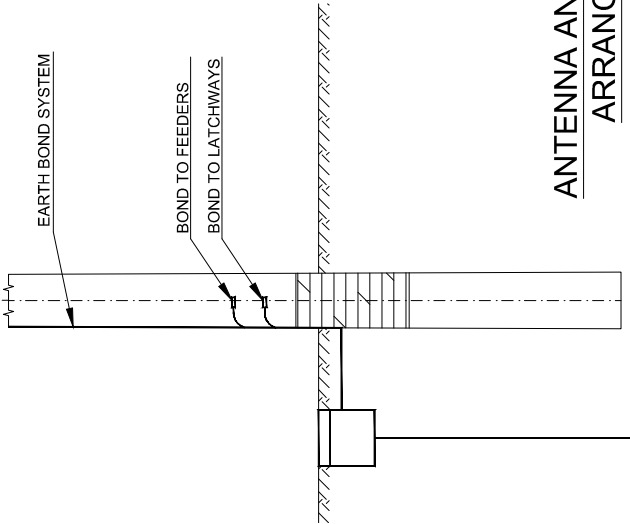


ALL SCALES AS SHOWN WHEN PRINTED AT A3

ALL SCALES AS SHOWN WHEN PRINTED AT A3

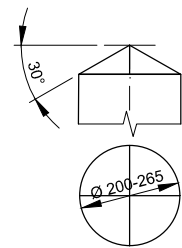


- NOTES:
1. A SINGLE COAT OF TIMBER COMPATIBLE BITUMINOUS PAINT (E.G. BIRD BRAND BLACK BITUMINOUS PAINT OR SIMILAR APPROVED PRODUCT) TO BE APPLIED TO THE UPPER SURFACES AT THE TOP OF THE POLE.
 2. PAINT TO BE APPLIED ON SITE JUST BEFORE ERECTION
- FORM: 4 WAY PYRAMID / CONE


DETAIL A - TIMBER POLE TOP
Scale 1:20

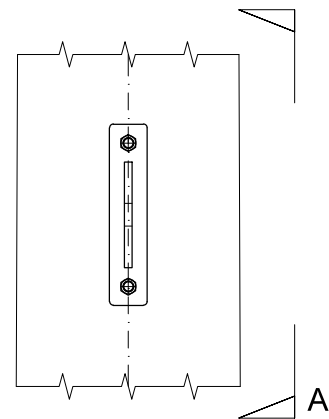


DETAIL C - FALL ARREST
ATTACHMENT POINT
Scale 1:10

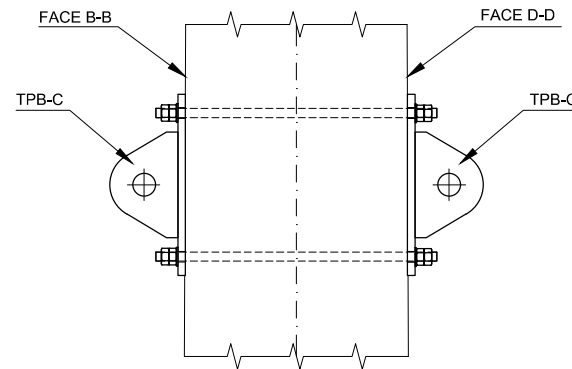


VIEW A-A
Scale 1:10

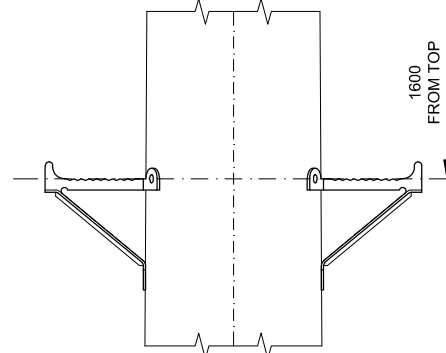


DETAIL D - ANTENNA
ACCESS CLIMBING STEP
Scale 1:10

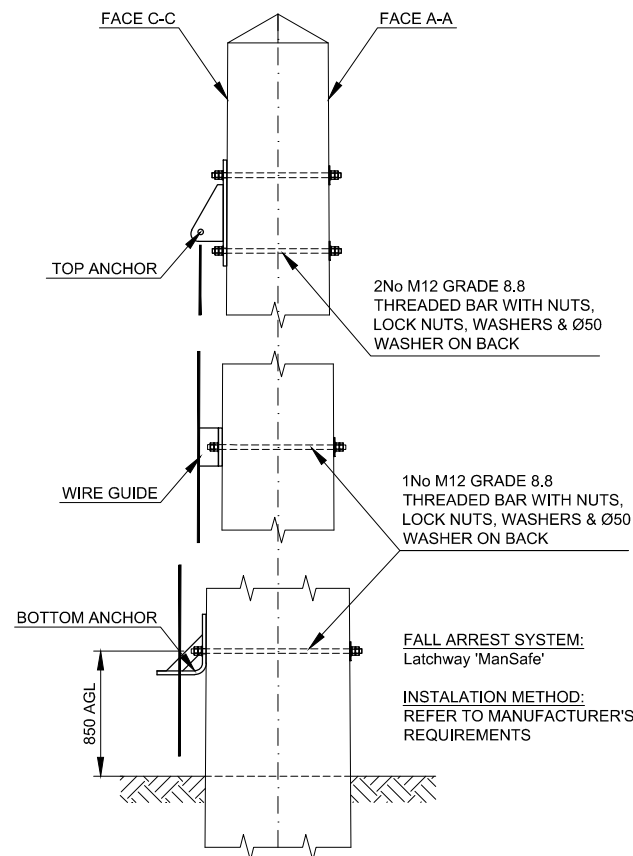


DETAIL B - FALL ARREST SYSTEM
Scale 1:20

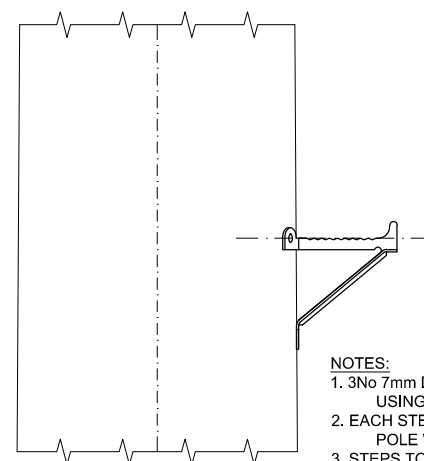

- NOTES:
1. 3No 7mm DIA 70mm LONG PILOT HOLES TO BE DRILLED USING THE STEP AS A TEMPLATE
 2. EACH STEP SHOULD BE FIXED TO THE TIMBER POLE WITH 3No 10mm COACH SCREWS 75mm LONG
 3. STEPS TO BE INSTALLED ON FACES B-B & D-D ONLY

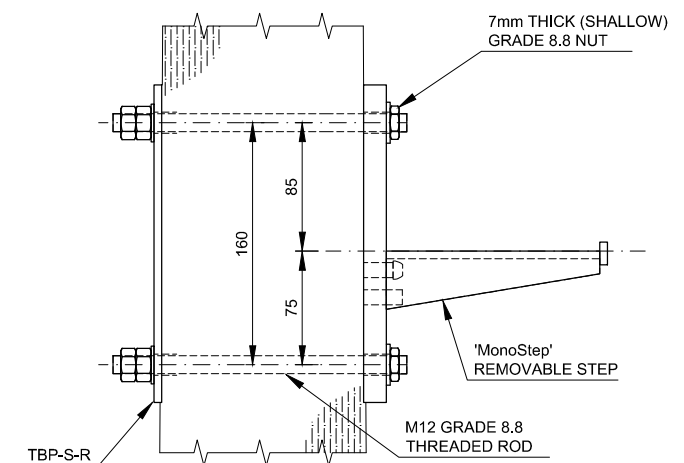

DETAIL F - REMOVABLE
CLIMBING STEPS
Scale 1:5

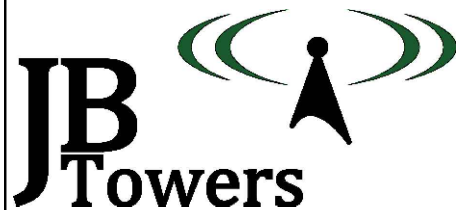

01	FIRST ISSUE	AM	22/09/20
REV	REV	BY	DATE
SCALE AS SHOWN	DRAWN	CHECKED	APPROVED
WHEN PRINTED AT A3	AM	MP	JBT
DATE	22/09/20	DATE	22/09/20
DATE	22/09/20	DATE	22/09/20
ALL DIMENSIONS IN mm UNLESS OTHERWISE STATED. THIS DRAWING TO BE READ IN CONJUNCTION WITH OTHER RELEVANT DRAWINGS.			

TITLE
NEWPORT BAY
GENERAL ARRANGEMENT
SHEET 3 OF 3

SITE ADDRESS
NEWPORT BAY
MILL STREET
BETWS-Y-COED
ABERCONWY AND
COLWYN
LL24 0BB

ARQIVA REF.
141277


DRG No.
200

REV
01

ALL SCALES AS SHOWN WHEN PRINTED AT A3



ALL SCALES AS SHOWN WHEN PRINTED AT A3


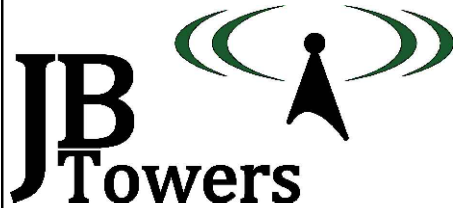


01	FIRST ISSUE			AM	22/09/20
REV	REV			BY	DATE
SCALE AS SHOWN		DRAWN	AM	CHECKED	MP
WHEN PRINTED AT A3		DATE	22/09/20	DATE	22/09/20
		APPROVED	JBT	DATE	22/09/20
ALL DIMENSIONS IN mm UNLESS OTHERWISE STATED. THIS DRAWING TO BE READ IN CONJUNCTION WITH OTHER RELEVANT DRAWINGS.					


TITLE
NEWPORT BAY
TIMBER POLE HOLE SET OUT
SHEET 1 OF 2

SITE ADDRESS
NEWPORT BAY
MILL STREET
BETWS-Y-COED
ABERCONWY AND
COLWYN
LL24 0BB


ARQIVA REF. 141277	DRG No. 201	REV 01
-----------------------	----------------	-----------

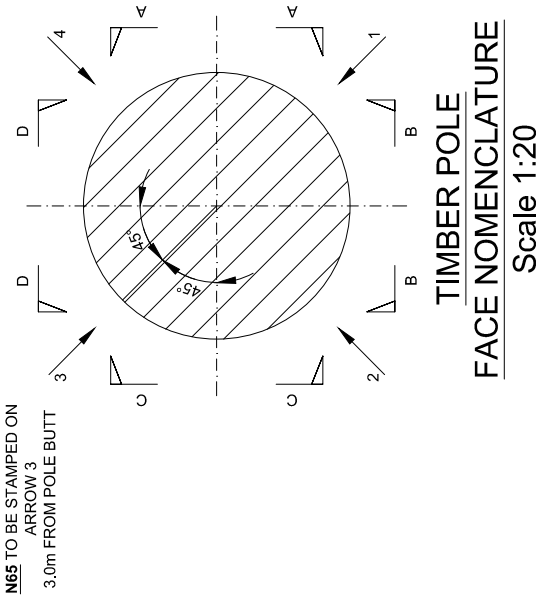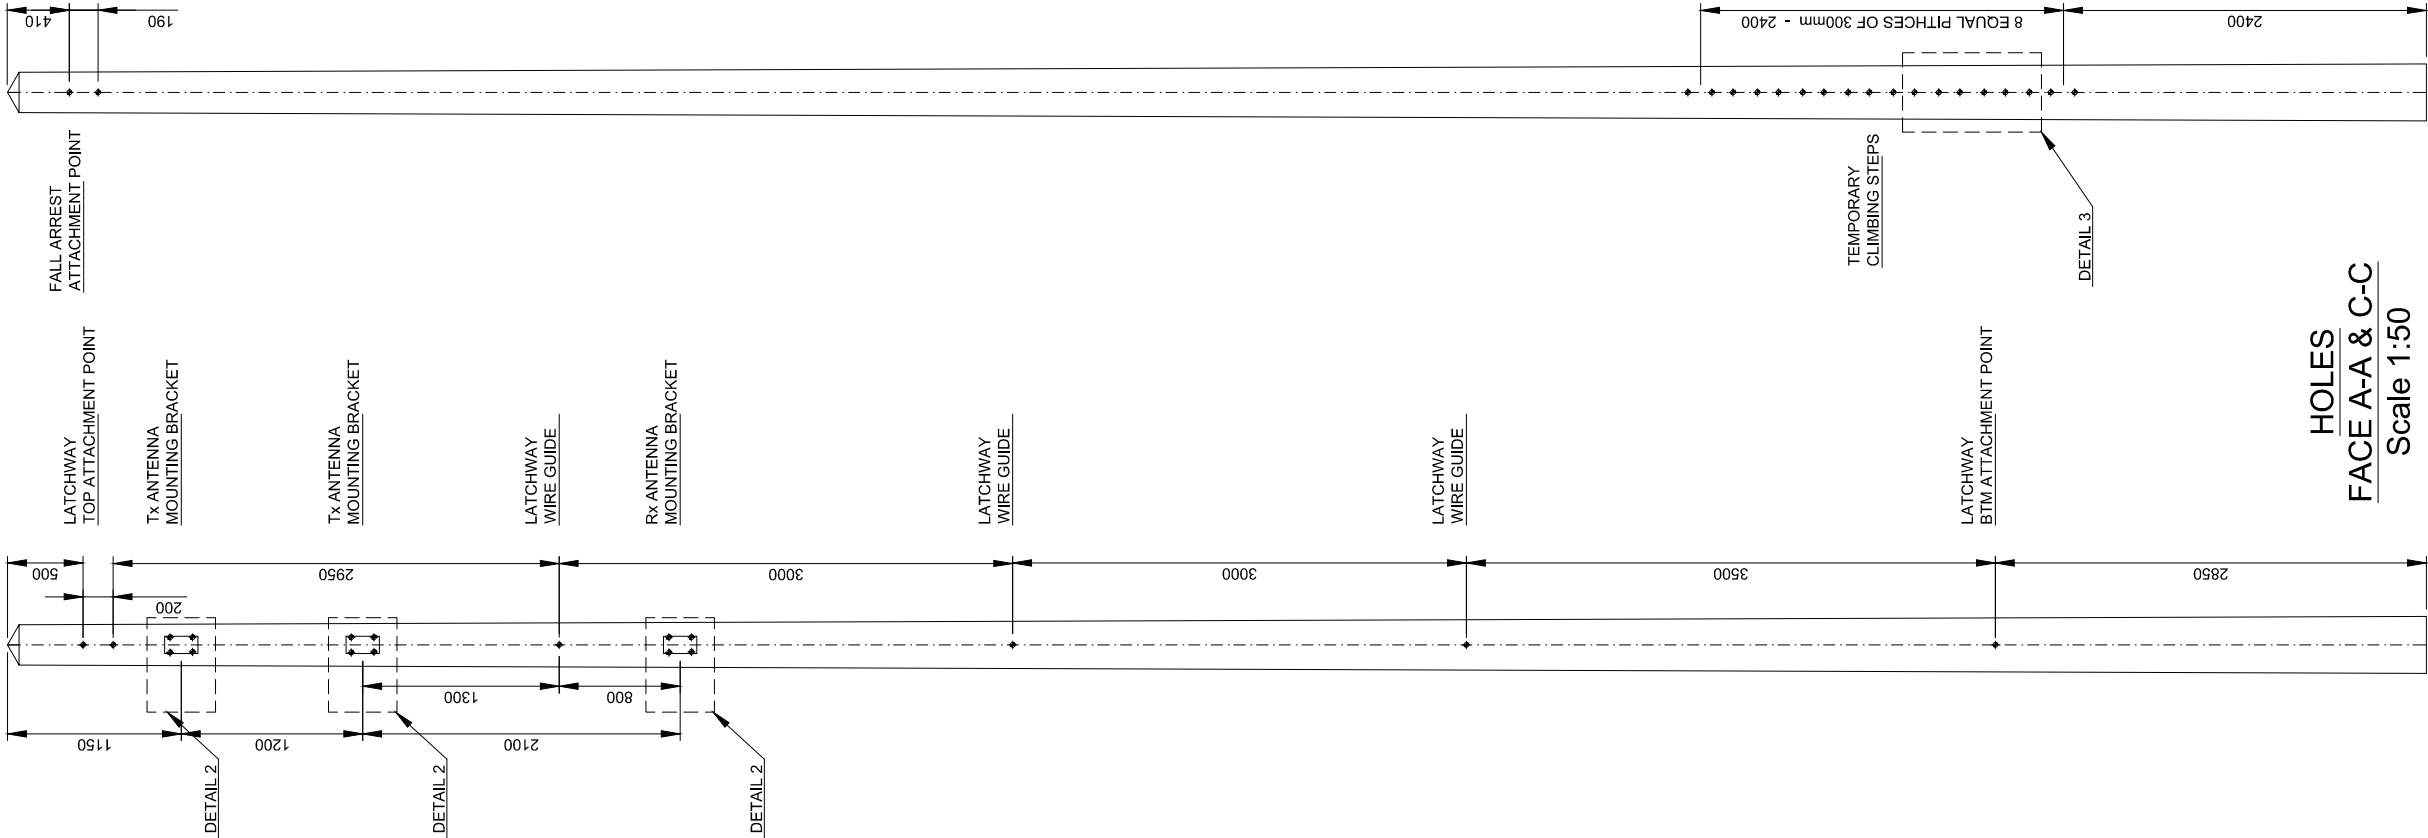

TIMBER POLE
FACE NOMENCLATURE
Scale 1:20

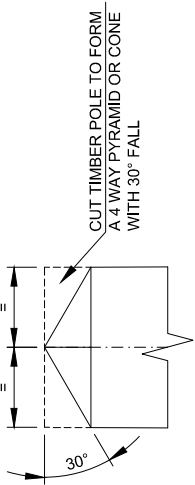


DETAIL 1
Scale 1:10

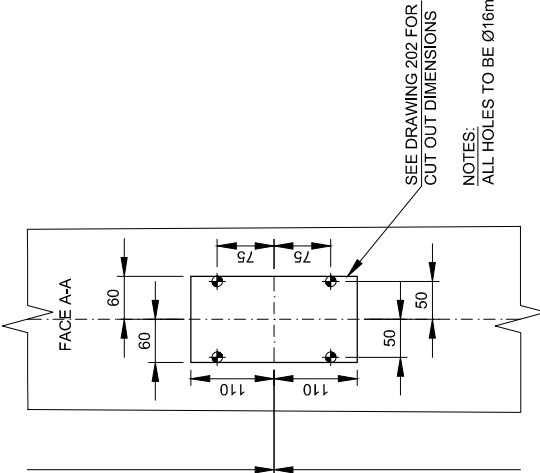

NOTES:
ALL HOLES TO BE Ø16mm THROUGH HOLES

DETAIL 2 - TYPICAL
Scale 1:10

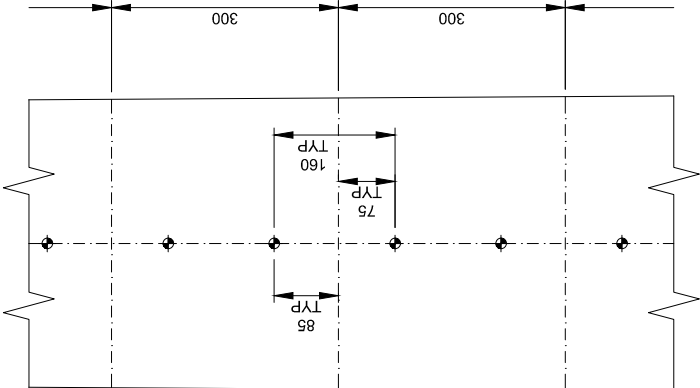


DETAIL 3 - TYPICAL
Scale 1:10

HOLES
FACE B-B & D-D
Scale 1:50

HOLES
FACE A-A & C-C
Scale 1:50



ALL SCALES AS SHOWN WHEN PRINTED AT A3

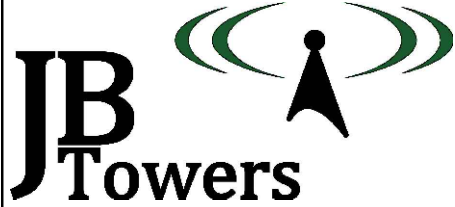

01	FIRST ISSUE			AM	22/09/20
REV	REV			BY	DATE
SCALE AS SHOWN		DRAWN	AM	CHECKED	MP
WHEN PRINTED AT A3		DATE	22/09/20	DATE	22/09/20
		DATE	22/09/20	DATE	22/09/20
ALL DIMENSIONS IN mm UNLESS OTHERWISE STATED. THIS DRAWING TO BE READ IN CONJUNCTION WITH OTHER RELEVANT DRAWINGS.					

TITLE

NEWPORT BAY

TIMBER POLE HOLE SET OUT

SHEET 2 OF 2

SITE ADDRESS

NEWPORT BAY

MILL STREET

BETWS-Y-COED

ABERCONWY AND

COLWYN

LL24 0BB

ARQIVA REF.


141277

DRG No.

201



REV

01

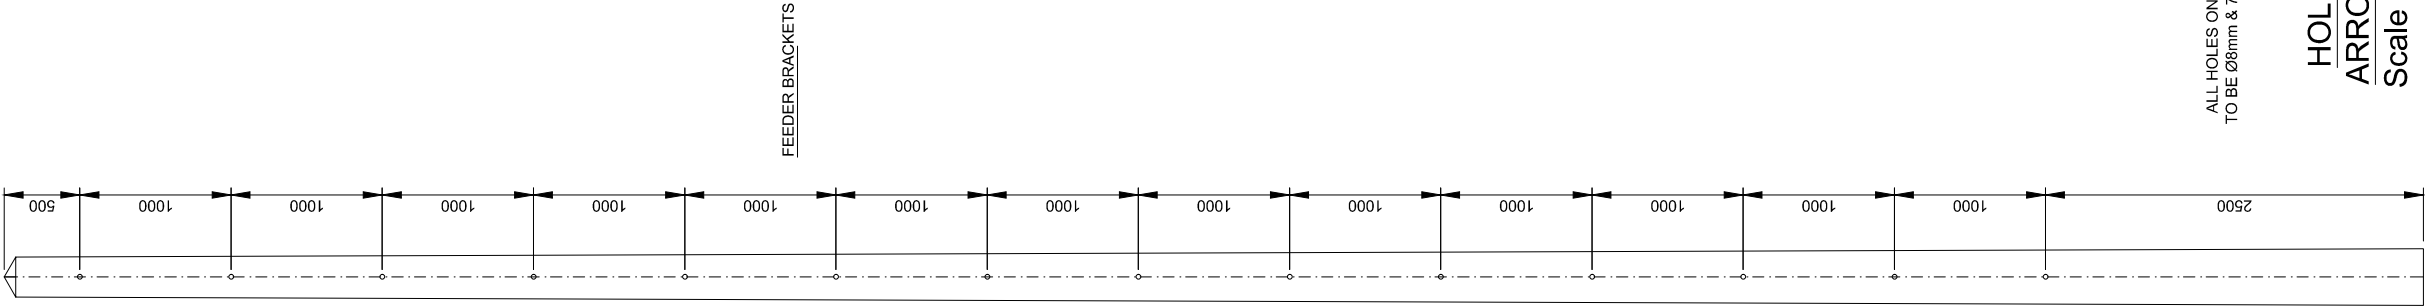

ALL HOLES ON ARROW 1
TO BE Ø8mm & 70mm LONG

HOLES
ARROW 1
Scale 1:50

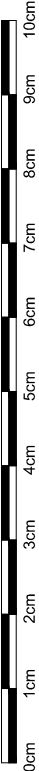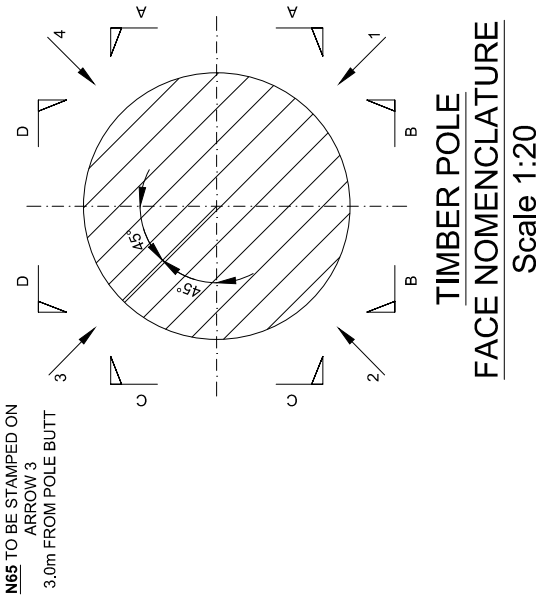


ALL SCALES AS SHOWN WHEN PRINTED AT A3


01	FIRST ISSUE			AM	22/09/20
REV	REV			BY	DATE
SCALE AS SHOWN		DRAWN	AM	CHECKED	MP
WHEN PRINTED AT A3		DATE	22/09/20	DATE	22/09/20
		APPROVED	JBT	DATE	22/09/20
ALL DIMENSIONS IN mm UNLESS OTHERWISE STATED. THIS DRAWING TO BE READ IN CONJUNCTION WITH OTHER RELEVANT DRAWINGS.					

TITLE
NEWPORT BAY
TIMBER POLE CUT OUT
DETAIL

SITE ADDRESS
NEWPORT BAY
MILL STREET
BETWS-Y-COED
ABERCONWY AND
COLWYN
LL24 0BB

ARQIVA REF. 141277	DRG No. 202	REV 01
-----------------------	----------------	-----------

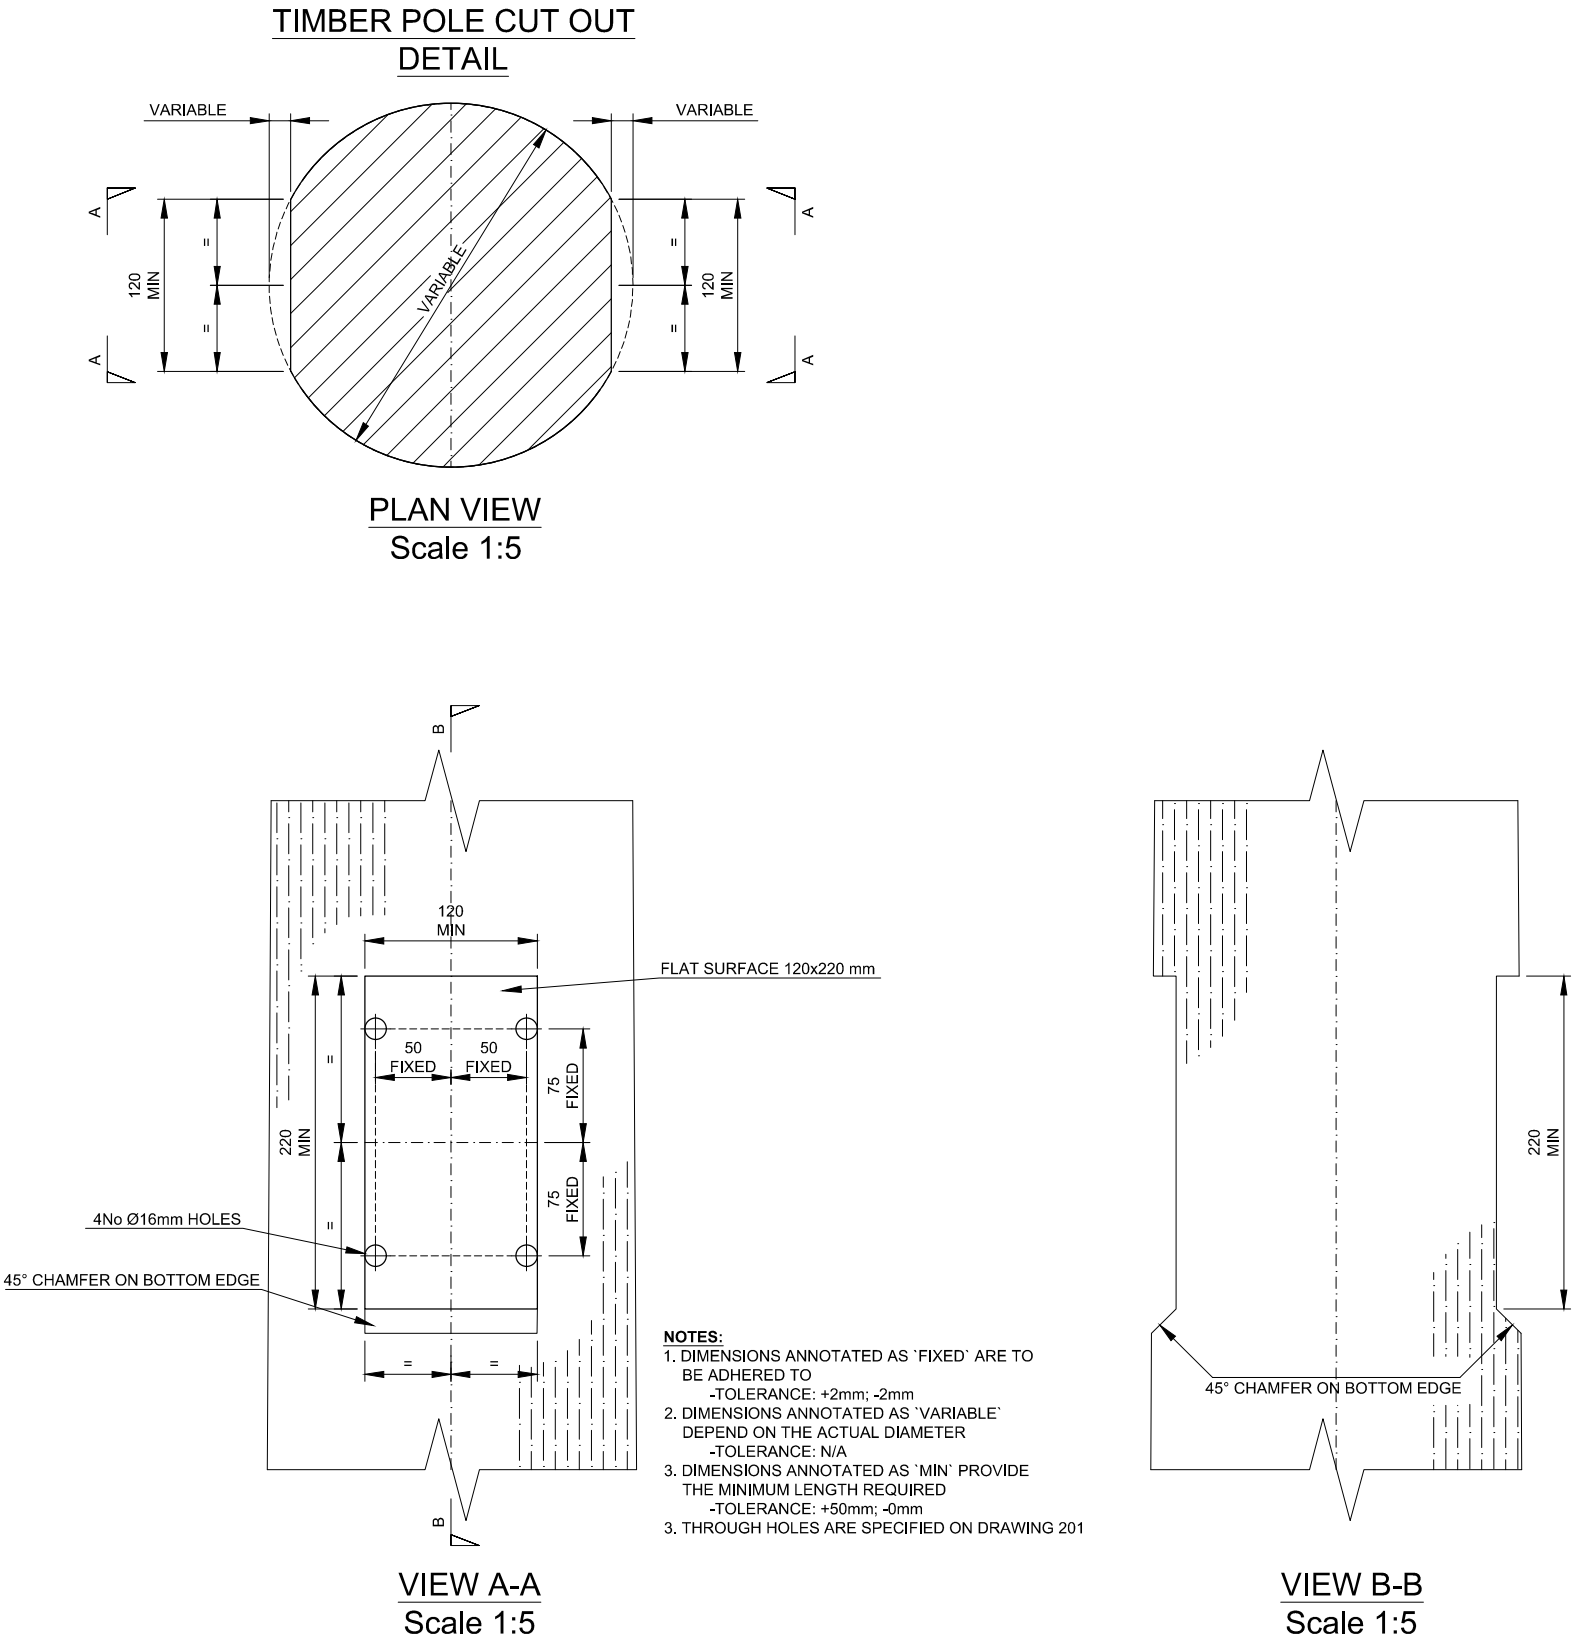


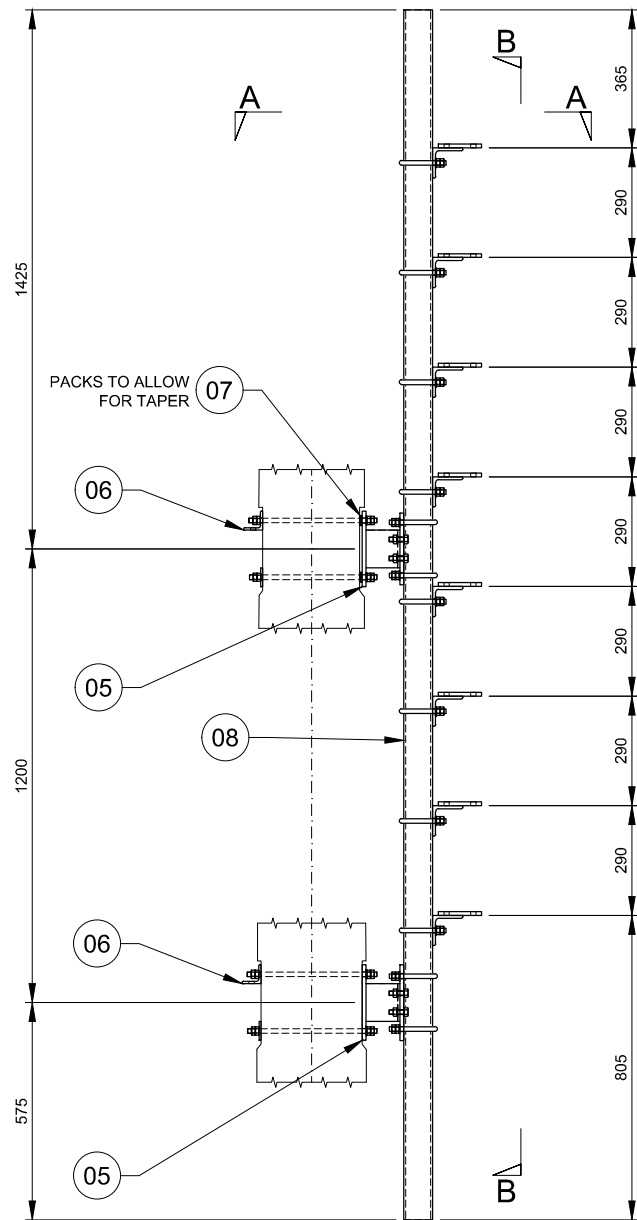


DETAIL G - Tx ANTENNA MOUNT
Scale 1:20

POSITION OF POWER
DIVIDER
TO BE DETERMINED
ON SITE

POSITION OF POWER
DIVIDERS
TO BE DETERMINED
ON SITE

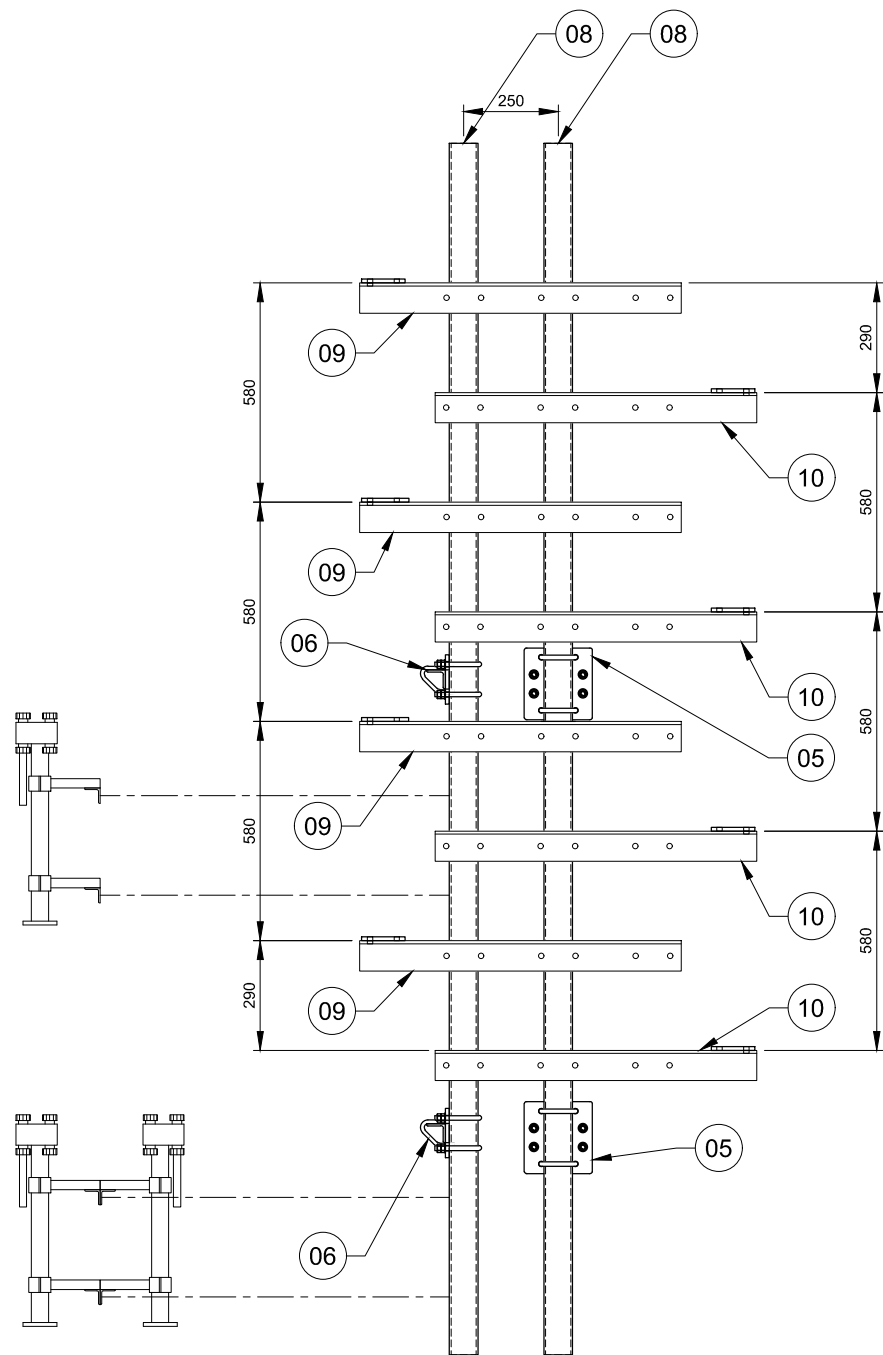


SECTION B-B
Scale 1:20

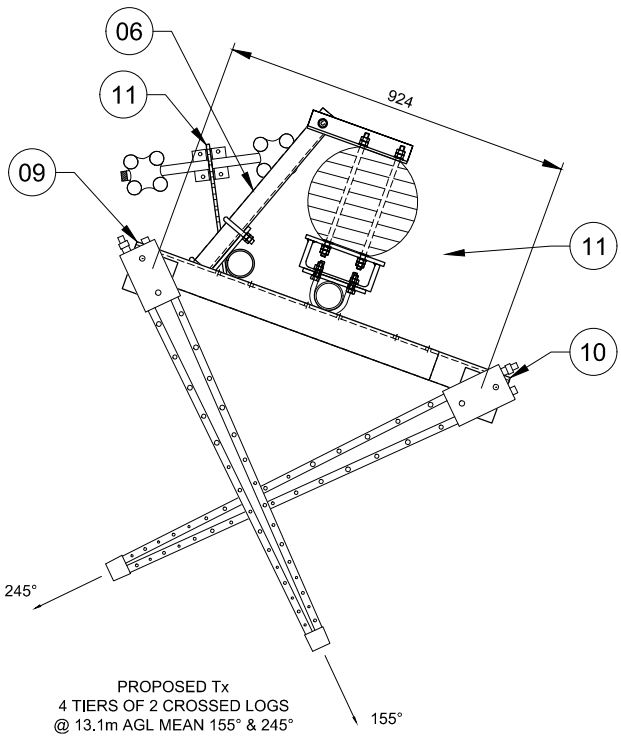

SECTION A-A
Scale 1:20

PROPOSED Tx
4 TIERS OF 2 CROSSED LOGS
@ 13.1m AGL MEAN 155° & 245°

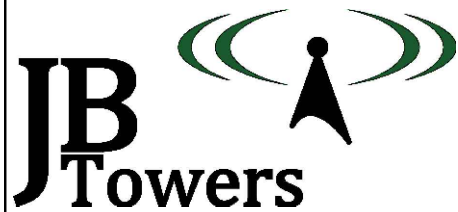

arqiva

02	MINOR UPDATE	AM	16/11/20
01	FIRST ISSUE	AM	22/09/20
REV	REV	BY	DATE
SCALE AS SHOWN WHEN PRINTED AT A3	DRAWN DATE 22/09/20	CHECKED DATE 22/09/20	APPROVED DATE 22/09/20
ALL DIMENSIONS IN mm UNLESS OTHERWISE STATED. THIS DRAWING TO BE READ IN CONJUNCTION WITH OTHER RELEVANT DRAWINGS.			

TITLE
NEWPORT BAY
Tx ANTENNA MOUNT
DETAIL G

SITE ADDRESS
NEWPORT BAY
MILL STREET
BETWS-Y-COED
ABERCONWY AND
COLWYN
LL24 0BB

ARQIVA REF.
141277


DRG No.
203

REV
02

ALL SCALES AS SHOWN WHEN PRINTED AT A3



ALL SCALES AS SHOWN WHEN PRINTED AT A3

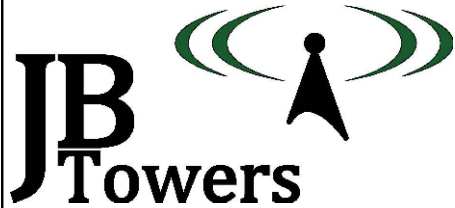

01	FIRST ISSUE			AM	22/09/20
REV	REV			BY	DATE
SCALE AS SHOWN		DRAWN	AM	CHECKED	MP
WHEN PRINTED AT A3		DATE	22/09/20	DATE	22/09/20
APPROVED JBT					
ALL DIMENSIONS IN mm UNLESS OTHERWISE STATED.					
THIS DRAWING TO BE READ IN CONJUNCTION WITH					
OTHER RELEVANT DRAWINGS.					


TITLE
NEWPORT BAY
Rx ANTENNA MOUNT
DETAIL H

SITE ADDRESS
NEWPORT BAY
MILL STREET
BETWS-Y-COED
ABERCONWY AND
COLWYN
LL24 0BB


ARQIVA REF.
141277

DRG No.
204

REV
01

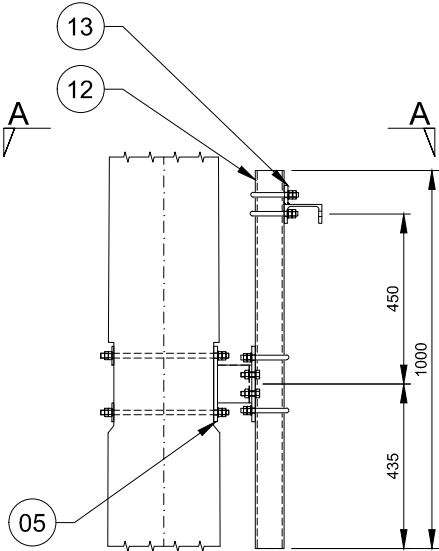

DETAIL H - Rx ANTENNA MOUNT
Scale 1:20

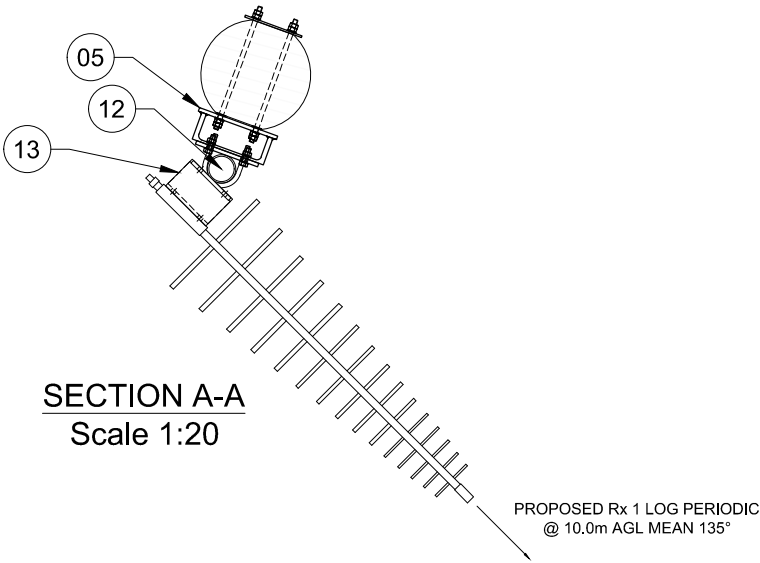


SECTION A-A
Scale 1:20




ALL SCALES AS SHOWN WHEN PRINTED AT A3

ALL SCALES AS SHOWN WHEN PRINTED AT A3

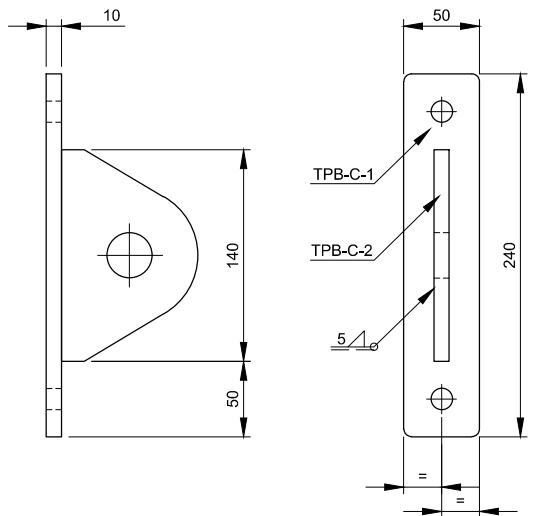

PART TPB-C
Scale 1:5

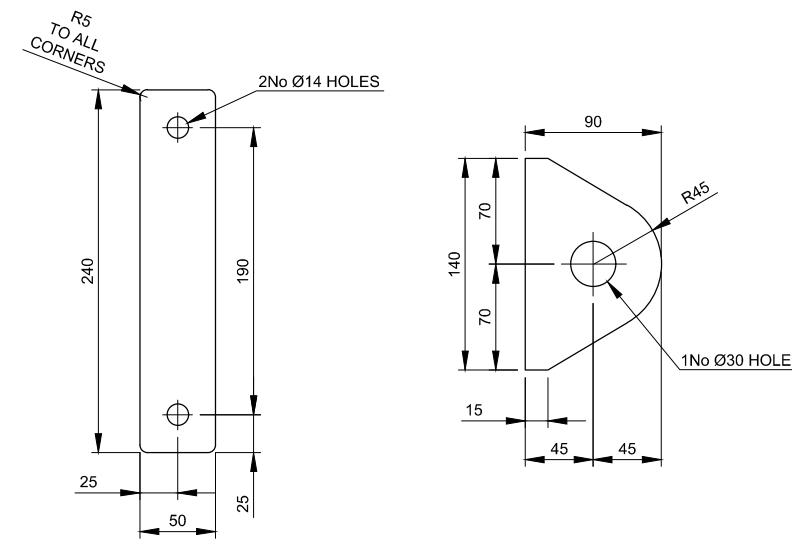


TPB-C-1 - 10mm THICK
Scale 1:5

TPB-C-2 - 10mm THICK
Scale 1:5


Parts list for TPB-C

Item	Part	Quantity	Part description	Length	Material	Weight
01	TPB-C-1	1	Plate 240x50x10mm	N/A	S275J0	0.94 kg
02	TPB-C-2	1	Plate 140x90x10mm	N/A	S275J0	0.99 kg
03	STUDS	1	M12 STUDDING	350mm	GRADE 8.8	0.31 kg
Total Weight:						2.24 kg

- All steel hot dip galvanized
- Each STUD to be supplied with 4 Full Nuts, 2 Flat Washers and 2 Spring Washers
- For fabrication notes see drawing 305

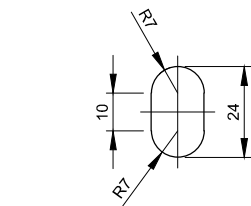

SLOTTED HOLE DETAIL
Scale 1:2

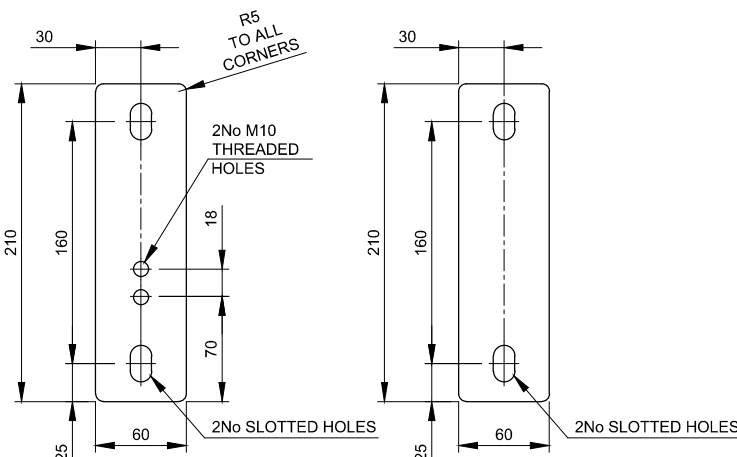


PART TPS-R-1
Scale 1:5

PART TPS-R-2
Scale 1:5

Parts list for TPS-R

Item	Part	Quantity	Part description	Length	Material	Weight
01	TPS-R-1	1	Plate 210x60x15mm	N/A	S275J0	1.48 kg
02	TPS-R-2	1	Plate 210x60x5mm	N/A	S275J0	0.49 kg
03	STUDS	2	M12 STUDDING	500mm	GRADE 8.8	0.44 kg
04	NUT-S	2	M12 SHALLOW NUT	N/A	GRADE 8.8	-
05	NUT	4	M12 NUT	N/A	GRADE 8.8	-
06	WSH	4	M12 WASHER	N/A	GRADE 8.8	-
Total Weight:						2.41 kg

- All steel hot dip galvanized
- For fabrication notes see drawing 305

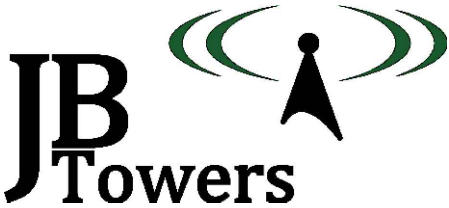

01	FIRST ISSUE	AM	22/09/20
REV	REV	BY	DATE
SCALE AS SHOWN WHEN PRINTED AT A3	DRAWN DATE 22/09/20	CHECKED DATE 22/09/20	APPROVED DATE 22/09/20
ALL DIMENSIONS IN mm UNLESS OTHERWISE STATED. THIS DRAWING TO BE READ IN CONJUNCTION WITH OTHER RELEVANT DRAWINGS.			

TITLE
NEWPORT BAY
ATTACHMENT POINT &
TEMPORARY STEP DETAILS
PARTS: TPB-C; TPS-R








SITE ADDRESS
NEWPORT BAY
MILL STREET
BETWS-Y-COED
ABERCONWY AND
COLWYN
LL24 0BB

ARQIVA REF.
141277
DRG No.
300
REV
01

ALL SCALES AS SHOWN WHEN PRINTED AT A3



ALL SCALES AS SHOWN WHEN PRINTED AT A3

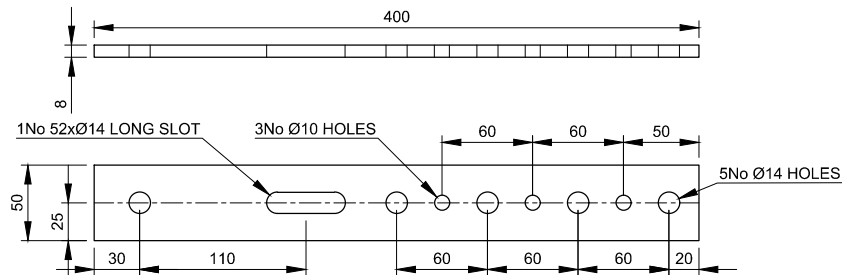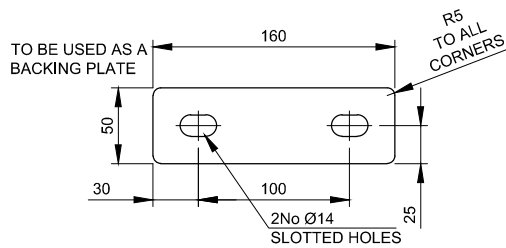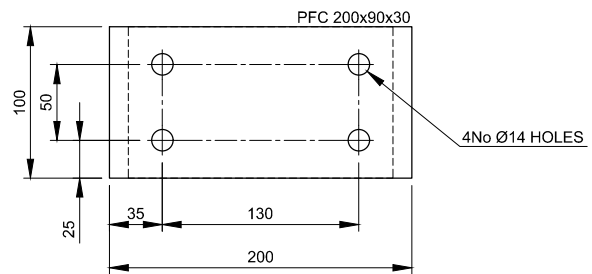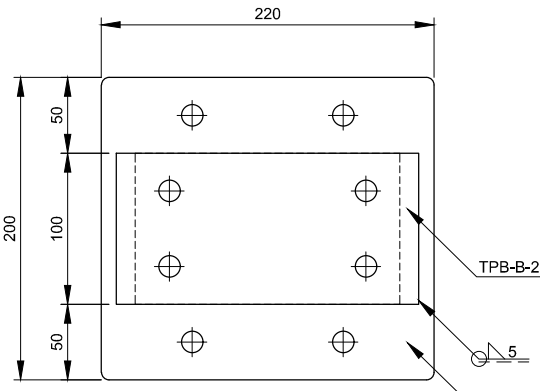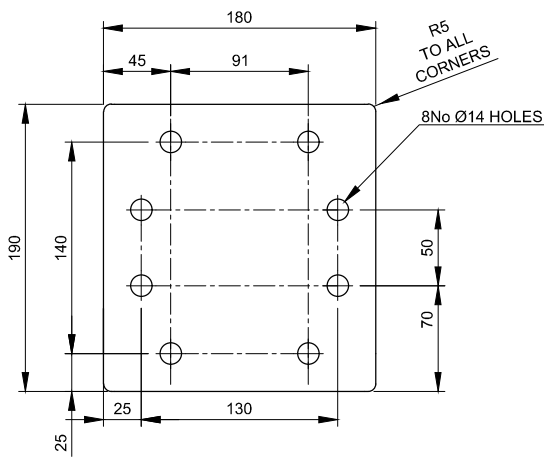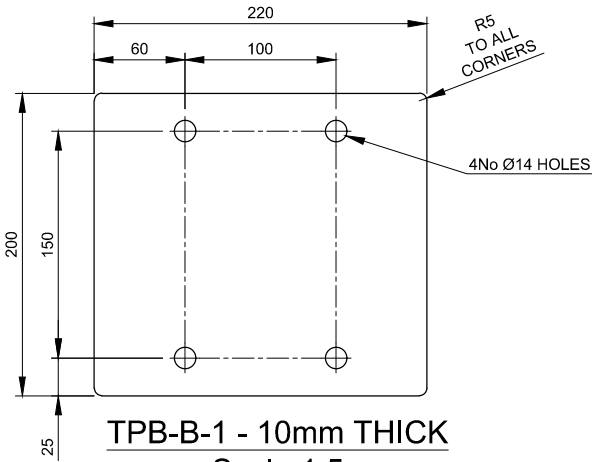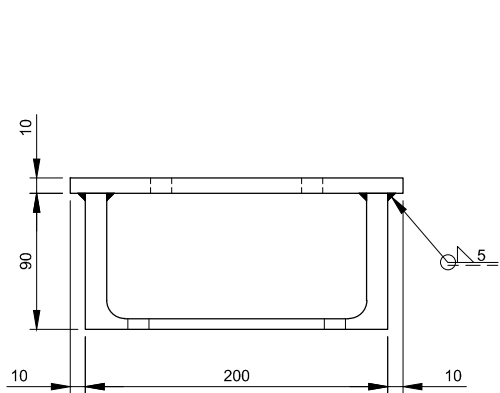


Parts list for TPB-B

Item	Part	Quantity	Part description	Length	Material	Weight
01	TPB-B-1	1	Plate 220x200x10mm	N/A	S275J0	3.45 kg
02	TPB-B-2	1	PFC 200x90x30	100mm	S275J0	3.00 kg
03	TPB-B-4	2	Plate 160x50x5mm	N/A	S275J0	0.31 kg
04	TPB-B-5	1	Plate 190x180x10mm	N/A	S275J0	2.70 kg
05	STUDS	4	M12 STUDDING	450mm	GRADE 8.8	0.39 kg
06	BOLT	4	M12 45mm LONG (2D+6)	45mm	GRADE 8.8	-
07	U-BOLT	2	M12 U-BOLT FOR CHS 76.1	N/A	GRADE 8.8	-

- All steel hot dip galvanized
- Each STUD & U-BOLT to be supplied with 4 Full Nuts, 2 Flat Washers and 2 Spring Washers
- Each BOLT to be supplied with 1 Full Nut, 1 Form E FLat Washer and 1 Spring Washer
- For fabrication notes see drawing 305

Total Weight: 11.33 kg

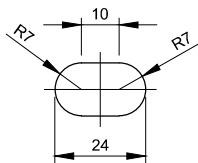


SLOTTED HOLE DETAIL
Scale 1:2

Parts list for TPA-PD

Item	Part	Quantity	Part description	Length	Material	Weight
01	TPA-PD	1	400x50x8mm	N/A	S275J0	1.26 kg
02	U-BOLT	1	M12 U-BOLT FOR CHS 76.1mm	N/A	GRADE 8.8	-

Total Weight: 1.26 kg

- All steel hot dip galvanized
- Each U-BOLT to be supplied with 4 Full Nuts, 2 Flat Washers and 2 Spring Washers
- For fabrication notes see drawing 305

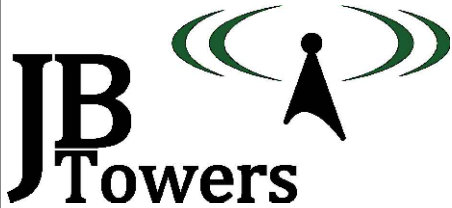

01	FIRST ISSUE	AM	22/09/20
REV	REV	BY	DATE
SCALE AS SHOWN WHEN PRINTED AT A3	DRAWN DATE 22/09/20	CHECKED DATE 22/09/20	APPROVED DATE 22/09/20
ALL DIMENSIONS IN mm UNLESS OTHERWISE STATED. THIS DRAWING TO BE READ IN CONJUNCTION WITH OTHER RELEVANT DRAWINGS.			

TITLE
NEWPORT BAY
STEELWORK BRACKET,
POWER DIVIDER STRAP
PARTS: TPB-B, TPA-PD


SITE ADDRESS
NEWPORT BAY
MILL STREET
BETWS-Y-COED
ABERCONWY AND
COLWYN
LL24 0BB

ARQIVA REF. 141277	DRG No. 301	REV 01
-----------------------	----------------	-----------

ALL SCALES AS SHOWN WHEN PRINTED AT A3




ALL SCALES AS SHOWN WHEN PRINTED AT A3

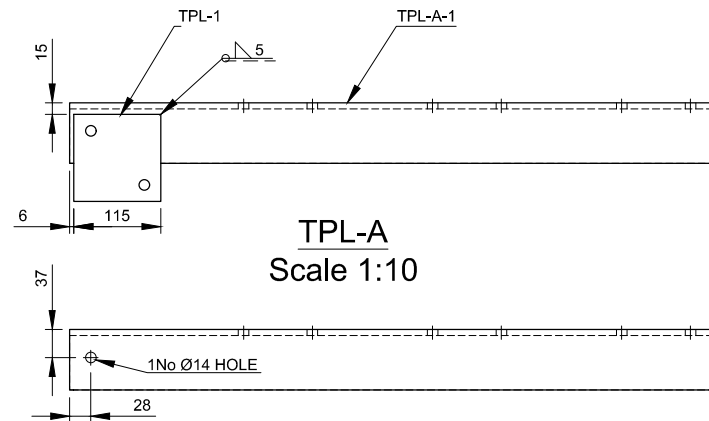

TPL-A
Scale 1:10


TPL-A-1 - EA 80x80x8
Scale 1:10

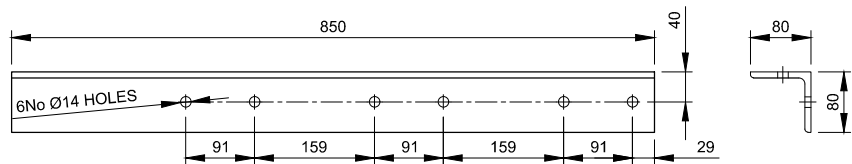

Parts list for TPL-A


Item	Part	Quantity	Part description	Length	Material	Weight
01	TPL-A-1	1	EA 80x80x8	850mm	S275J0	8.30 kg
02	TPL-1	1	Plate 115x115x10	N/A	S275J0	1.00 kg
03	U-BOLT	2	M12 U-BOLT FOR CHS 76.1mm	N/A	GRADE 8.8	-
Total Weight:						9.30 kg

- All steel hot dip galvanized
- Each U-BOLT to be supplied with 4 Full Nuts, 2 Flat Washers and 2 Spring Washers
- For fabrication notes see drawing 305

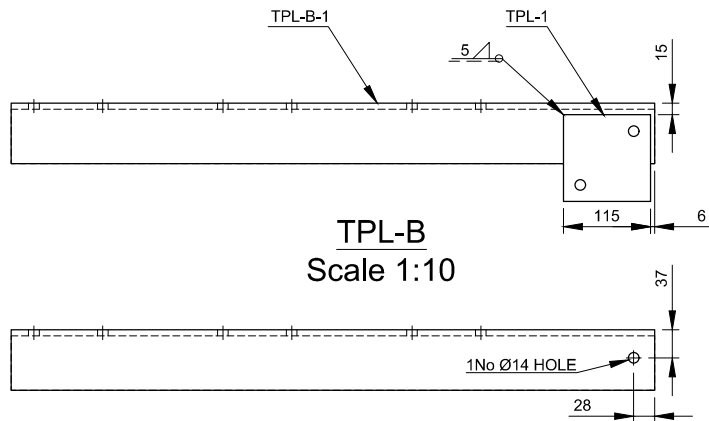

TPL-B
Scale 1:10


TPL-B-1 - EA 80x80x8
Scale 1:10

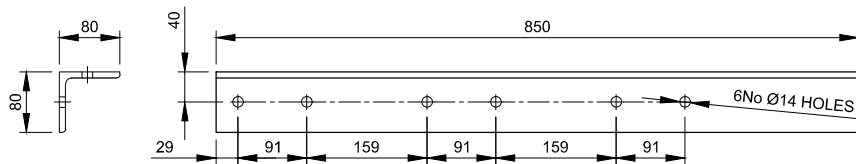


Parts list for TPL-A

Item	Part	Quantity	Part description	Length	Material	Weight
01	TPL-A-1	1	EA 80x80x8	850mm	S275J0	8.30 kg
02	TPL-1	1	Plate 115x115x10	N/A	S275J0	1.00 kg
03	U-BOLT	2	M12 U-BOLT FOR CHS 76.1mm	N/A	GRADE 8.8	-
Total Weight:						9.30 kg

- All steel hot dip galvanized
- Each U-BOLT to be supplied with 4 Full Nuts, 2 Flat Washers and 2 Spring Washers
- For fabrication notes see drawing 305

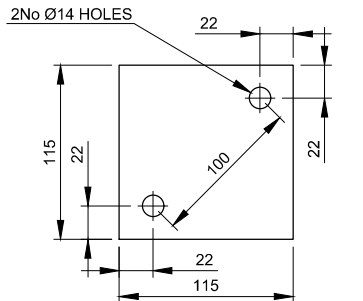

TPL-1 - 10mm THICK
Scale 1:5

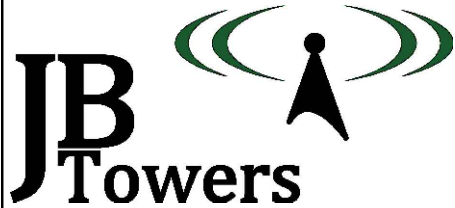

01	FIRST ISSUE					AM	22/09/20
REV	REV					BY	DATE
SCALE AS SHOWN		DRAWN	AM	CHECKED	MP	APPROVED	JBT
WHEN PRINTED AT A3		DATE	22/09/20	DATE	22/09/20	DATE	22/09/20
ALL DIMENSIONS IN mm UNLESS OTHERWISE STATED. THIS DRAWING TO BE READ IN CONJUNCTION WITH OTHER RELEVANT DRAWINGS.							

TITLE
NEWPORT BAY
LOG MOUNTS
PARTS: TPL-A; TPL-B

SITE ADDRESS
NEWPORT BAY
MILL STREET
BETWS-Y-COED
ABERCONWY AND
COLWYN
LL24 0BB

ARQIVA REF.
141277


DRG No.
302

REV
01


ALL SCALES AS SHOWN WHEN PRINTED AT A3



ALL SCALES AS SHOWN WHEN PRINTED AT A3

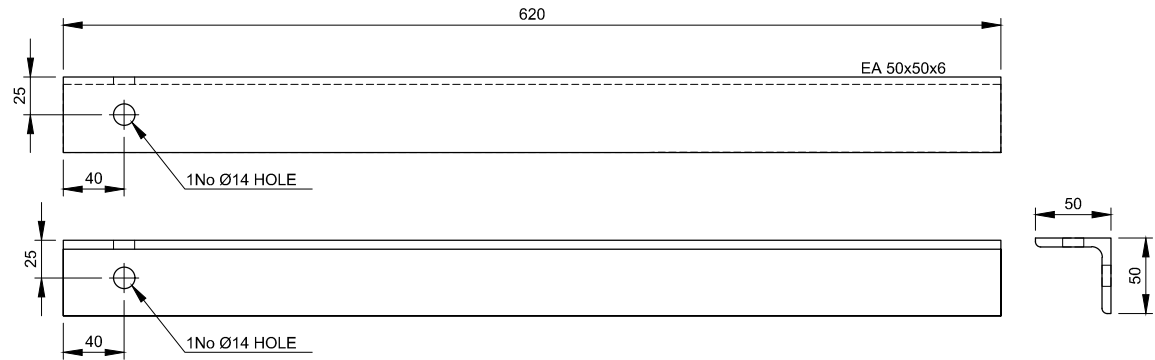


TPB-BR-1 - EA50x50x6
Scale 1:5

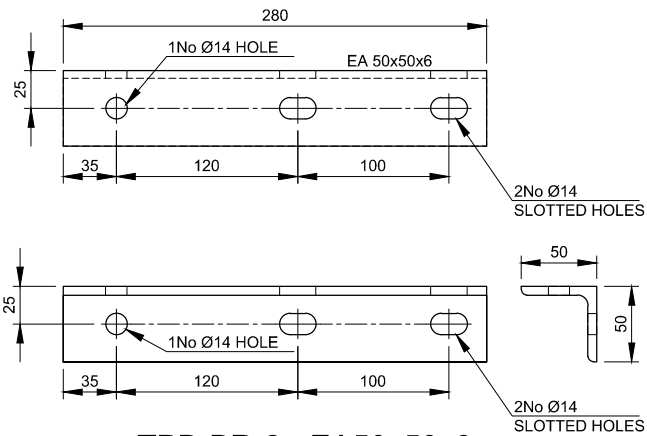


TPB-BR-2 - EA50x50x6
Scale 1:5

TPB-BR-3 - 10mm THICK
Scale 1:5

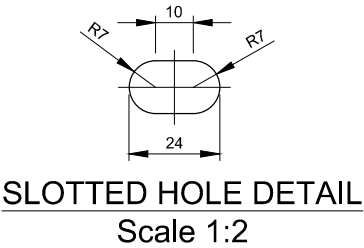

SLOTTED HOLE DETAIL
Scale 1:2

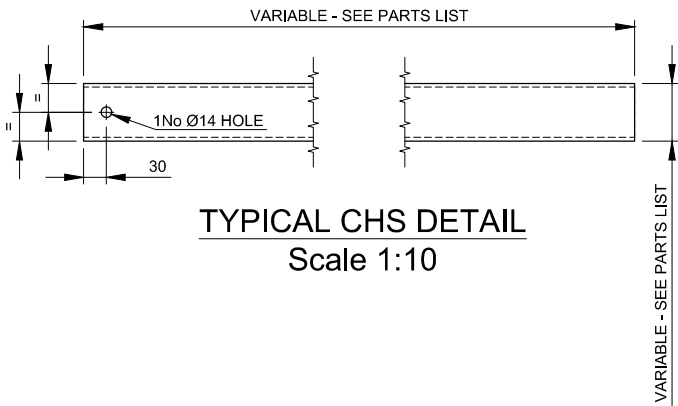


TYPICAL CHS DETAIL
Scale 1:10

Parts list for TPB-BR

Item	Part	Quantity	Part description	Length	Material	Weight
01	TPB-BR-1	1	EA 50x50x6	280mm	S275J0	2.75 kg
02	TPB-BR-2	1	EA 50x50x6	620mm	S275J0	2.50 kg
03	TPB-BR-3	1	Plate 130x190x10mm	N/A	S275J0	1.95 kg
04	BOLT	1	M12 SET BOLT - 30mm LONG	N/A	GRADE 8.8	-
05	N-BOLT	2	M12 N-BOLT FOR EA 50x50x6	N/A	GRADE 8.8	-
06	U-BOLT	2	M12 U-BOLT FOR CHS 76.1mm	N/A	GRADE 8.8	-
Total Weight:						7.20 kg

- All steel hot dip galvanized
- Each BOLT to be supplied with 1 Full Nut, 1 Form E FLat Washer and 1 Spring Washer
- Each STUD & U-BOLT to be supplied with 4 Full Nuts, 2 Flat Washers and 2 Spring Washers
- For fabrication notes see drawing 305

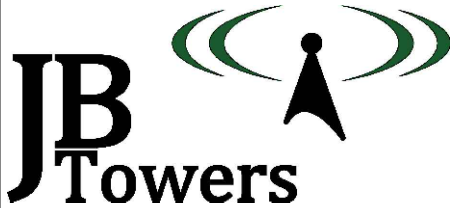



01	FIRST ISSUE			AM	22/09/20
REV	REV			BY	DATE
SCALE AS SHOWN WHEN PRINTED AT A3		DRAWN AM DATE 22/09/20	CHECKED MP DATE 22/09/20	APPROVED JBT DATE 22/09/20	
ALL DIMENSIONS IN mm UNLESS OTHERWISE STATED. THIS DRAWING TO BE READ IN CONJUNCTION WITH OTHER RELEVANT DRAWINGS.					

TITLE
NEWPORT BAY
BRACING ARM & TYPICAL
CHS DETAIL
PART: TPB-BR

SITE ADDRESS
NEWPORT BAY
MILL STREET
BETWS-Y-COED
ABERCONWY AND
COLWYN
LL24 0BB

ARQIVA REF. 141277	DRG No. 303	REV 01
-----------------------	----------------	-----------

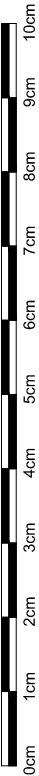


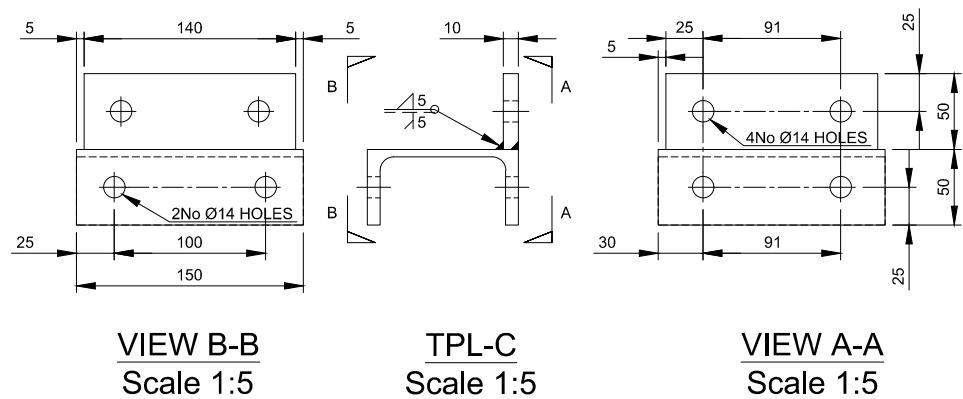

Parts list for TPL-C

Item	Part	Quantity	Part description	Length	Material	Weight
01	TPL-C-1	1	PFC100x50x10	150mm	S275J0	1.50 kg
02	TPL-2	1	PLATE 140x50x10	-	S275J0	0.55 kg
03	U-BOLT	2	M12 U-BOLT FOR CHS 76.1mm	N/A	GRADE 8.8	-
Total Weight:						2.05 kg

- All steel hot dip galvanized
- Each U-BOLT to be supplied with 4 Full Nuts, 2 Flat Washers and 2 Spring Washers
- For fabrication notes see drawing 305

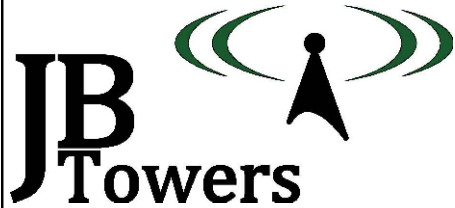

01	FIRST ISSUE			AM	22/09/20
REV	REV			BY	DATE
SCALE AS SHOWN		DRAWN	AM	CHECKED	MP
WHEN PRINTED AT A3		DATE	22/09/20	DATE	22/09/20
APPROVED		JBT			
ALL DIMENSIONS IN mm UNLESS OTHERWISE STATED.		THIS DRAWING TO BE READ IN CONJUNCTION WITH OTHER RELEVANT DRAWINGS.			

TITLE
NEWPORT BAY
LOG MOUNT
PART: TPL-C

SITE ADDRESS
NEWPORT BAY
MILL STREET
BETWS-Y-COED
ABERCONWY AND
COLWYN
LL24 0BB

ARQIVA REF. 141277	DRG No. 303	REV 01
-----------------------	----------------	-----------

ALL SCALES AS SHOWN WHEN PRINTED AT A3




ALL SCALES AS SHOWN WHEN PRINTED AT A3

Item	Part	Drawing	Quantity	Part description	Length	Material	Weight
01	01	200	1	3 MAN LATCHWAY SYSTEM & 3No. WIRE GUIDES FOR FACE MOUNTED MONOPOLE	14000	N/A	-
02	TPB-C	300	2	FALL ARREST ATTACHMENT POINT	N/A	S275J0	4.50 kg
03	03	200	36	PERMANENT BT STEP c/w 3No 10x75mm ZINC-PLATED COACH SCREWS	N/A	S275J0	11.30 kg
04	TPS-R	300	9	'MonoStep' ASSEMBLY	N/A	S275J0	21.70 kg
05	TPB-B	301	3	MOUNTING BRACKET	N/A	S275J0	34.00 kg
06	TPB-BR	303	2	BRACING ARM	N/A	S275J0	14.40 kg
07	07	203	12	M12 WASHER	N/A	GRADE 8.8	-
08	08	203	2	CHS 76.1x5mm	3200mm	S355J2H	56.10 kg
09	TPL-A	302	4	LOG MOUNTING BRACKET	860mm	S275J0	37.20 kg
10	TPL-B	302	4	LOG MOUNTING BRACKET	860mm	S275J0	37.20 kg
11	TPA-PD	301	6	POWER DIVIDER STRAP	N/A	S275J0	7.60 kg
12	12	204	1	CHS 76.1x5mm	1000mm	S355J2H	9.00 kg
13	TPL-C	303	1	LOG MOUNTING BRACKET	N/A	S275J0	2.05 kg
14	14	200	1	PoleSaver	750mm	N/A	-
15	15	200	6	M12 STUD + 4No NUTS + 2No FLAT WASHERS + 1No Ø50mm WASHER (FOR FALL ARREST SYSTEM)	500mm	GRADE 8.8	2.70 kg
16	16	200	1	FEEDER COVER - 2/CG/100	3500mm	UV RESISTANT PLASTIC	-
17	17	200	14	FEEDER CLAMP - 2/FCD/028	N/A	POLYPROPYLENE	-
18	18	200	14	M10 SCREW DOWELS WTH M10 NUT	100mm	STAINLESS STEEL	-
Total Weight:							237.75 kg

- All steel hot dip galvanized
- All U-BOLTS to be FLA supply, each Supplied with 4 Full Nuts, 2 Flat Washers and 2 Spring Washers

NOTES:

1. WELDING TO BE IN ACCORDANCE WITH BS EN 1011-1:2009
2. LINEAR DIMS TO BE WITHIN ±1mm;
3. ANGULAR TOLERANCES TO BE WITHIN 0.5°
4. WELDING SYMBOLS ARE IN ACCORDANCE WITH BS EN 22553:1995
5. ALL PROFILE EDGES TO BE DRESSED AND SHARP CORNERS REMOVED
6. ALL WELD SIZES ARE FINAL SIZES
7. ALL WELDED JOINTS ARE TO BE PICKLE TIGHT
8. ALL STEELWORK TO BE BS EN 10025 GRADE S275 J0 UNO, HOT DIPPED GALVANISED TO BS EN ISO 1461. (ALL HOLLOW SECTIONS TO BE GRADE S355 J0H)
9. ALL STEEL IS TO BE SUPPLIED IN ACCORDANCE WITH EN 1090 TO EXECUTION CLASS 2
10. ALL NON PRE-LOADED BOLTS TO BE COMPLIANT STRUCTURAL BOLTS TO BS EN ISO 15048 PARTS 1&2.
11. STEELWORK COMPONENTS SHALL BE HOT DIP GALVANISED TO ACHIEVE A "VERY HIGH" DURABILITY FOR AN ENVIRONMENT CATEGORY CODE C4 FROM TABLE 1 IN BS EN ISO 14713
12. BOLTS AND NUTS SHALL BE SUPPLIED IN ACCORDANCE WITH BS 7371, SPUN GALVANISED IN ACCORDANCE WITH ISO 10684, THE NUTS RE-TAPPED AFTER GALVANISING, AND THE THREADS TREATED WITH GREASE.
13. ALL BOLTS TO BE CUT ON SITE TO EXTEND MAX 10mm BEYOND THE NUT WHEN TIGHTENED UNO.
14. ALL SITE DRILLED HOLE/CUT ENDS TO BE TREATED WITH METAFLUX 70-40 ZINC PASTE FOLLOWED BY 1 COAT OF 7-42 ZINC ALU OR 70-16 ALUMINIUM SPRAY

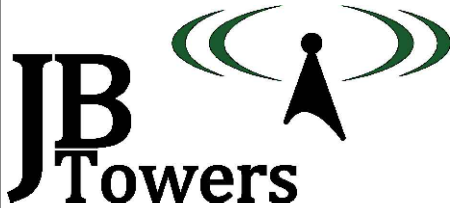

01	FIRST ISSUE			AM	22/09/20
REV	REV			BY	DATE
SCALE AS SHOWN		DRAWN	AM	CHECKED	MP
WHEN PRINTED AT A3		DATE	22/09/20	DATE	22/09/20
APPROVED		JBT			
ALL DIMENSIONS IN mm UNLESS OTHERWISE STATED.		THIS DRAWING TO BE READ IN CONJUNCTION WITH OTHER RELEVANT DRAWINGS.			

TITLE

NEWPORT BAY

PARTS LIST

SITE ADDRESS

NEWPORT BAY

MILL STREET

BETWS-Y-COED

ABERCONWY AND

COLWYN

LL24 0BB

ARQIVA REF.

141277

DRG No.

305


REV

01


ALL SCALES AS SHOWN WHEN PRINTED AT A3



ALL SCALES AS SHOWN WHEN PRINTED AT A3

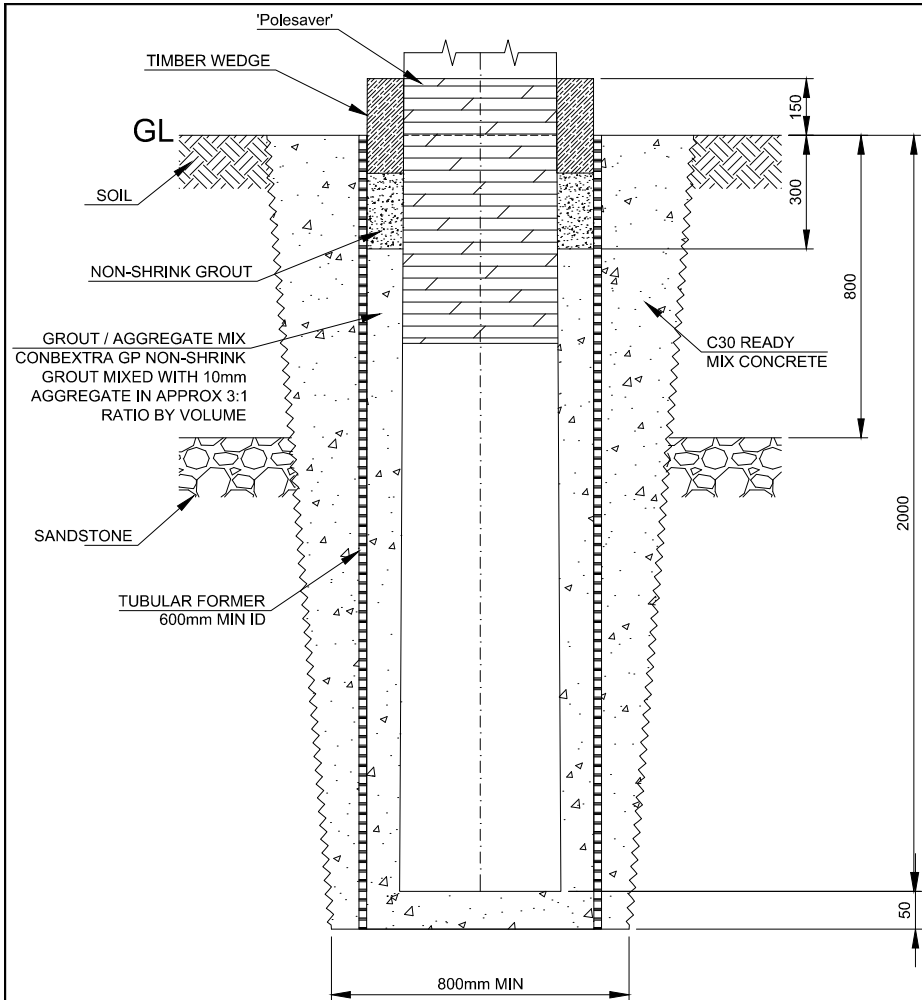


POROPOSED INSTALLATION
ELEVATION
Scale 1:20

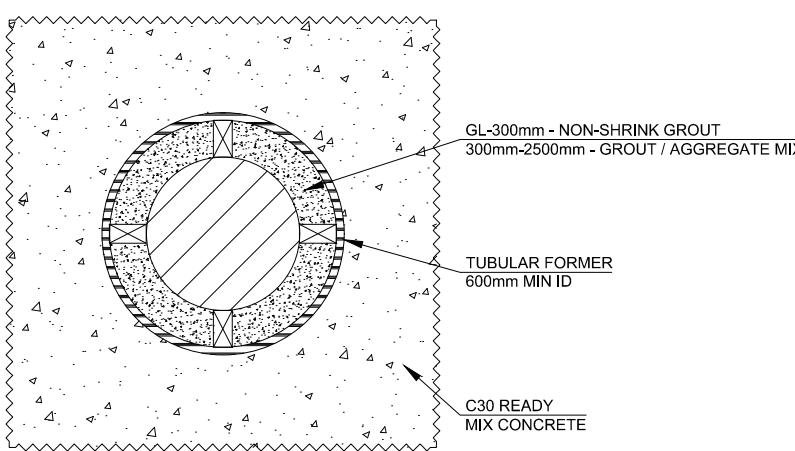


POROPOSED INSTALLATION
PLAN VIEW
Scale 1:20


- TIMBER POLE INSTALLATION:**
1. REFER TO DRAWING 200 FOR TIMBER POLE ORIENTATION
 2. EXCAVATE A HOLE MIN. 800mm SQUARE TO A DEPTH OF 2050mm
 3. INSERT FORMER WITH APPROPRIATE SUPPORT TO ENSURE IT HOLDS ITS SHAPE
 4. POUR CONCRETE AROUND OUTSIDE OF BASE OF FORMER UPTO ~0.5m FROM BASE OF HOLE & PLACE 50mm OF GROUT / AGGREGATE MIX INSIDE BASE OF FORMER. CONCRETE MIX TO ACHIEVE MIN STRENGTH OF 15 N/mm2 AFTER 2 DAYS & MIN 30 N/mm2 AFTER 28 DAYS
 5. REMAINDER OF CONCRETE TO BE POURED THE FOLLOWING DAY
 6. POLE TO BE WRAPPED IN 'POLESAVER' AND INSTALLED AND LEVELLED IN OPENING. TIMBERS TO BE USED TO HOLD POLE IN POSITION. POLE TO BE INSTALLED MIN OF 2 DAYS AFTER INITIAL CONCRETE POUR
 7. ANNULUS SHALL BE FILLED WITH GROUT / AGGREGATE MIX TO 300mm BELOW GL
 8. TOP 300mm SHALL BE FILLED WITH NON-SHRINK GROUT. A 1:60 FALL SHALL BE FORMED AROUND TIMBER POLE TO ALLOW WATER TO DRAIN AWAY FROM POLE
 9. ONCE GROUT HAS CURED REMOVE TIMBER WEDGES AND FILL REMAINING VOIDS WITH NON-SHRINK GROUT

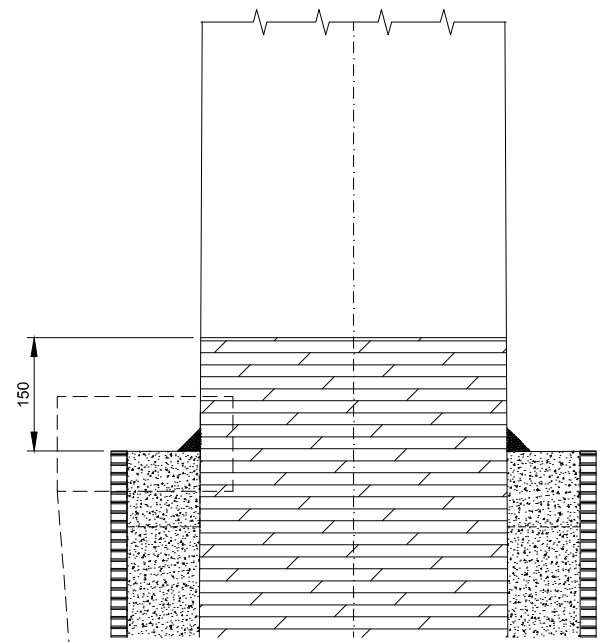

WATER PROOFING
Scale 1:10

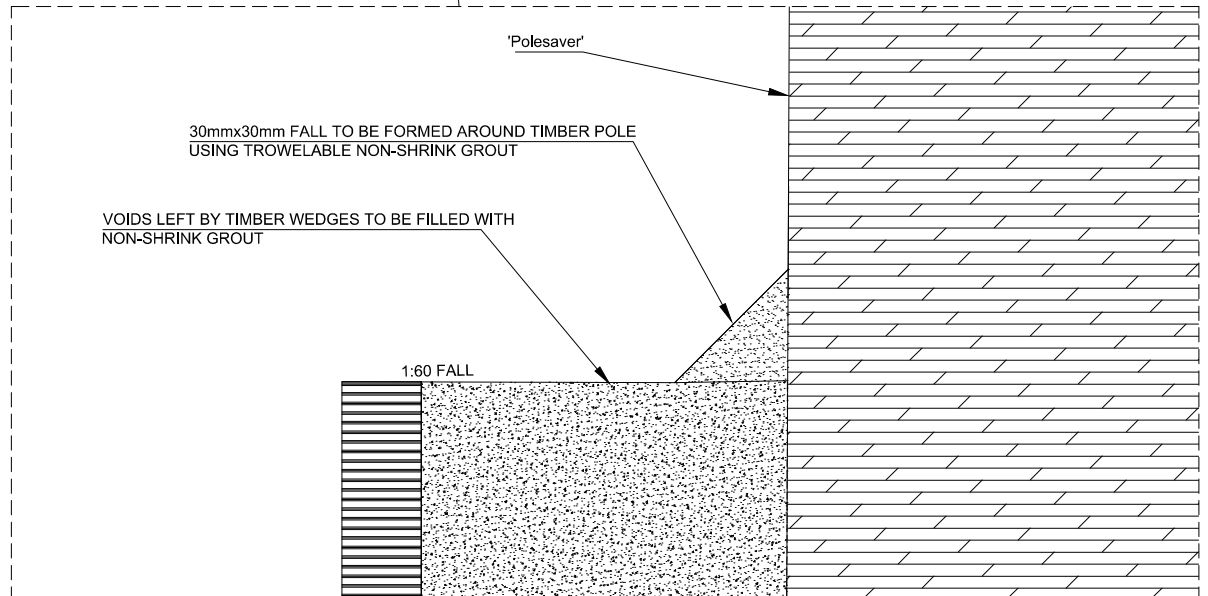

ENLARGED DETAIL
Scale 1:2

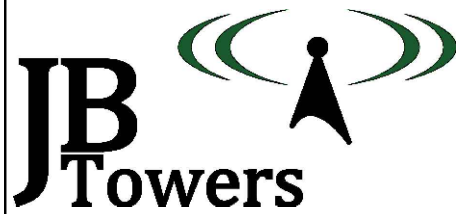

01	FIRST ISSUE			AM	22/09/20
REV	REV			BY	DATE
SCALE AS SHOWN		DRAWN	AM	CHECKED	MP
WHEN PRINTED AT A3		DATE	22/09/20	DATE	22/09/20
		DATE	22/09/20	DATE	22/09/20
ALL DIMENSIONS IN mm UNLESS OTHERWISE STATED. THIS DRAWING TO BE READ IN CONJUNCTION WITH OTHER RELEVANT DRAWINGS.					

TITLE
NEWPORT BAY
TIMBER POLE FOUNDATION
DETAILS

SITE ADDRESS
NEWPORT BAY
MILL STREET
BETWS-Y-COED
ABERCONWY AND
COLWYN
LL24 0BB

ARQIVA REF. 141277	DRG No. 400	REV 01
-----------------------	----------------	-----------

