

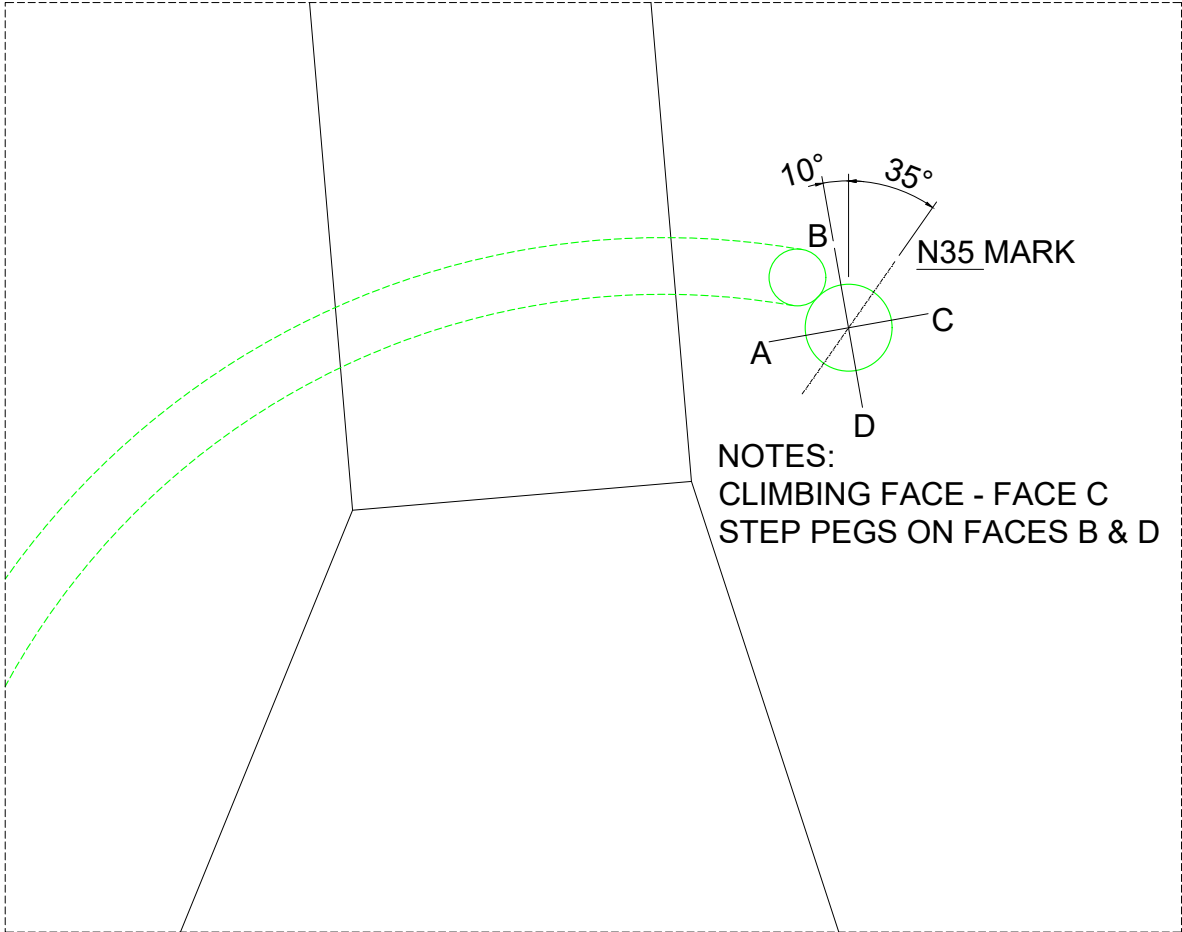


DRAWING ISSUE SHEET

[illegible]

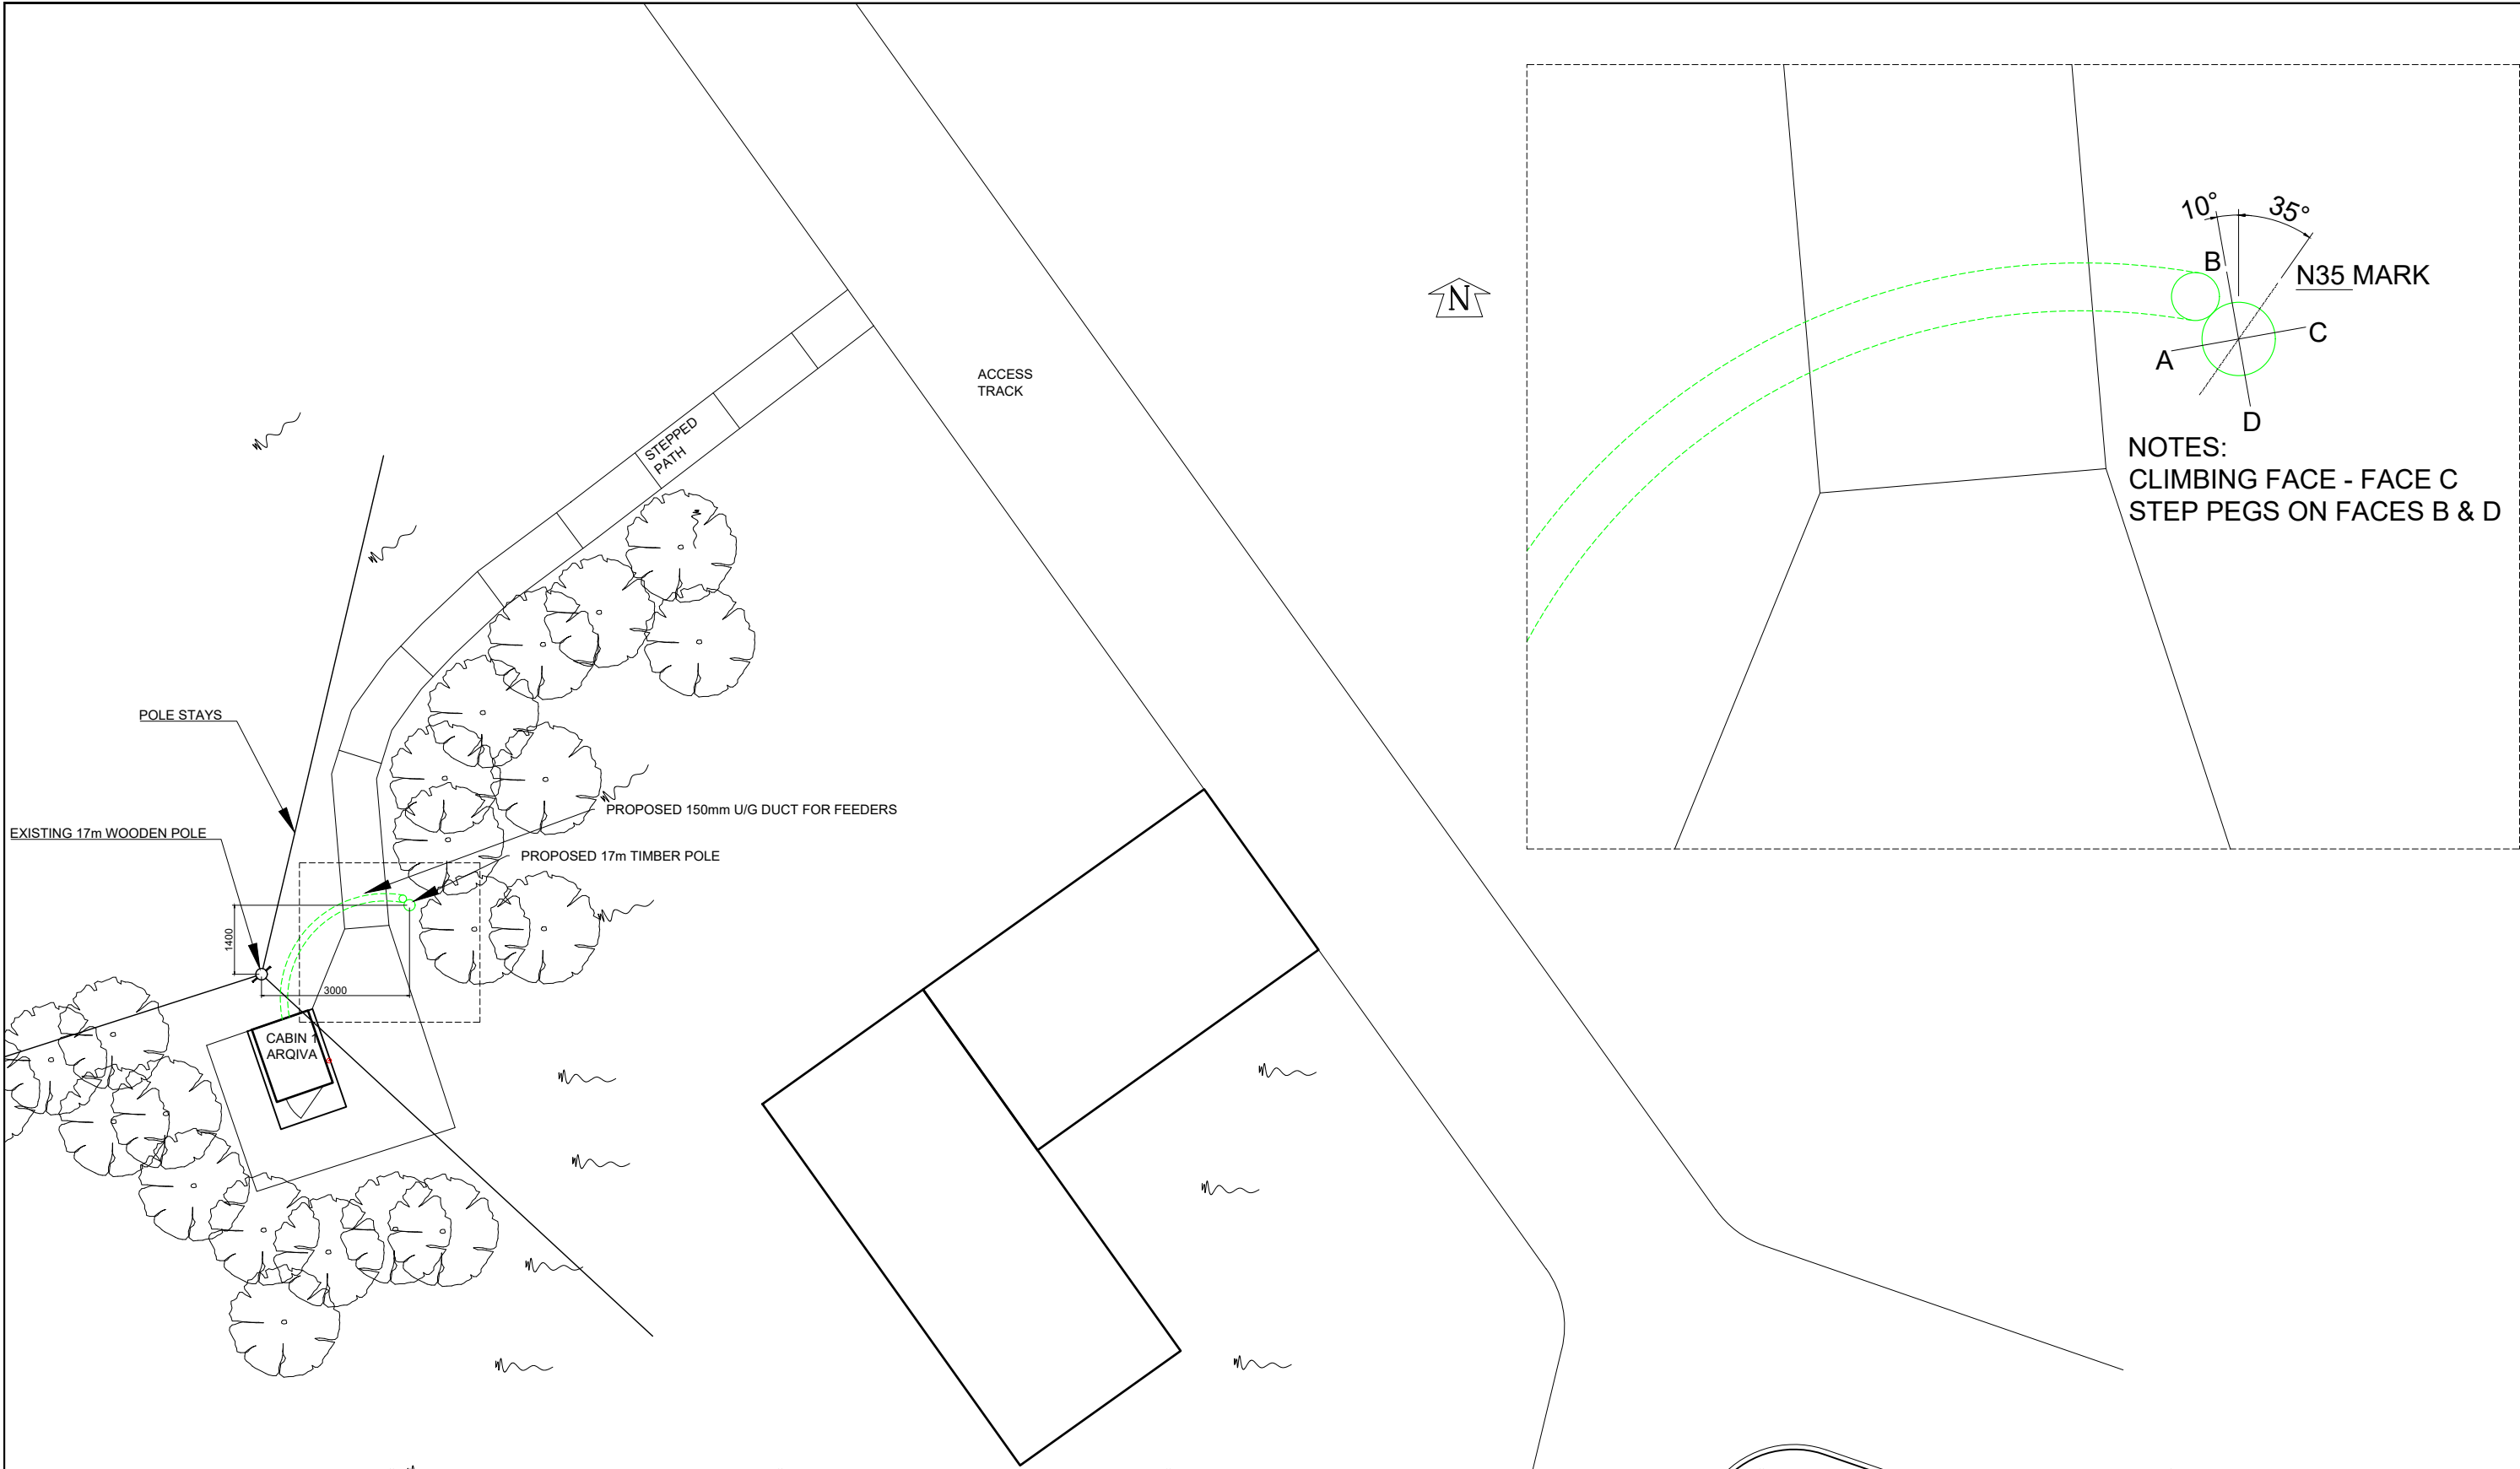

NOTES:
CLIMBING FACE - FACE C
STEP PEGS ON FACES B & D

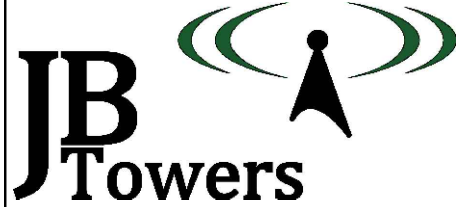


01	FIRST ISSUE				TT	24/06/19
REV	REV				BY	DATE
SCALE AS SHOWN		DRAWN	AM	CHECKED	MP	APPROVED JBT
WHEN PRINTED AT A3		DATE	24/06/19	DATE	24/06/19	DATE 24/06/19
ALL DIMENSIONS IN mm UNLESS OTHERWISE STATED. THIS DRAWING TO BE READ IN CONJUNCTION WITH OTHER RELEVANT DRAWINGS.						

TITLE
POOLEWE
SITE PLAN

SITE ADDRESS
INVEREWE GARDENS
POOLEWE
HIGHLAND
IV22 2LG

ARQIVA REF. 141370	DRG No. 100	REV 01
-----------------------	----------------	-----------

ALL SCALES AS SHOWN WHEN PRINTED AT A3

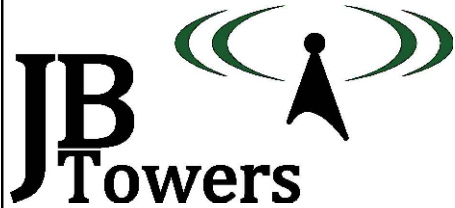

03	WIRE GUIDES POSITIONS UPDATED			AM	17/07/19
02	SPLICE DETAIL & INSTALLATION NOTES UPDATED			AM	15/07/19
01	FIRST ISSUE			TT	24/06/19
REV	REV			BY	DATE
SCALE AS SHOWN WHEN PRINTED AT A3		DRAWN	AM	CHECKED	MP
		DATE	24/06/19	DATE	24/06/19
APPROVED		JBT			
DATE		24/06/19			
ALL DIMENSIONS IN mm UNLESS OTHERWISE STATED. THIS DRAWING TO BE READ IN CONJUNCTION WITH OTHER RELEVANT DRAWINGS.					

TITLE

POOLEWE

GENERAL ARRANGEMENT

SHEET 1 OF 3

SITE ADDRESS

INVEREWE GARDENS

POOLEWE

HIGHLAND

IV22 2LG

ARQIVA REF.



141370

DRG No.

200

REV

03

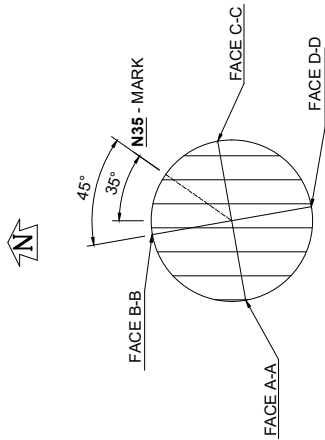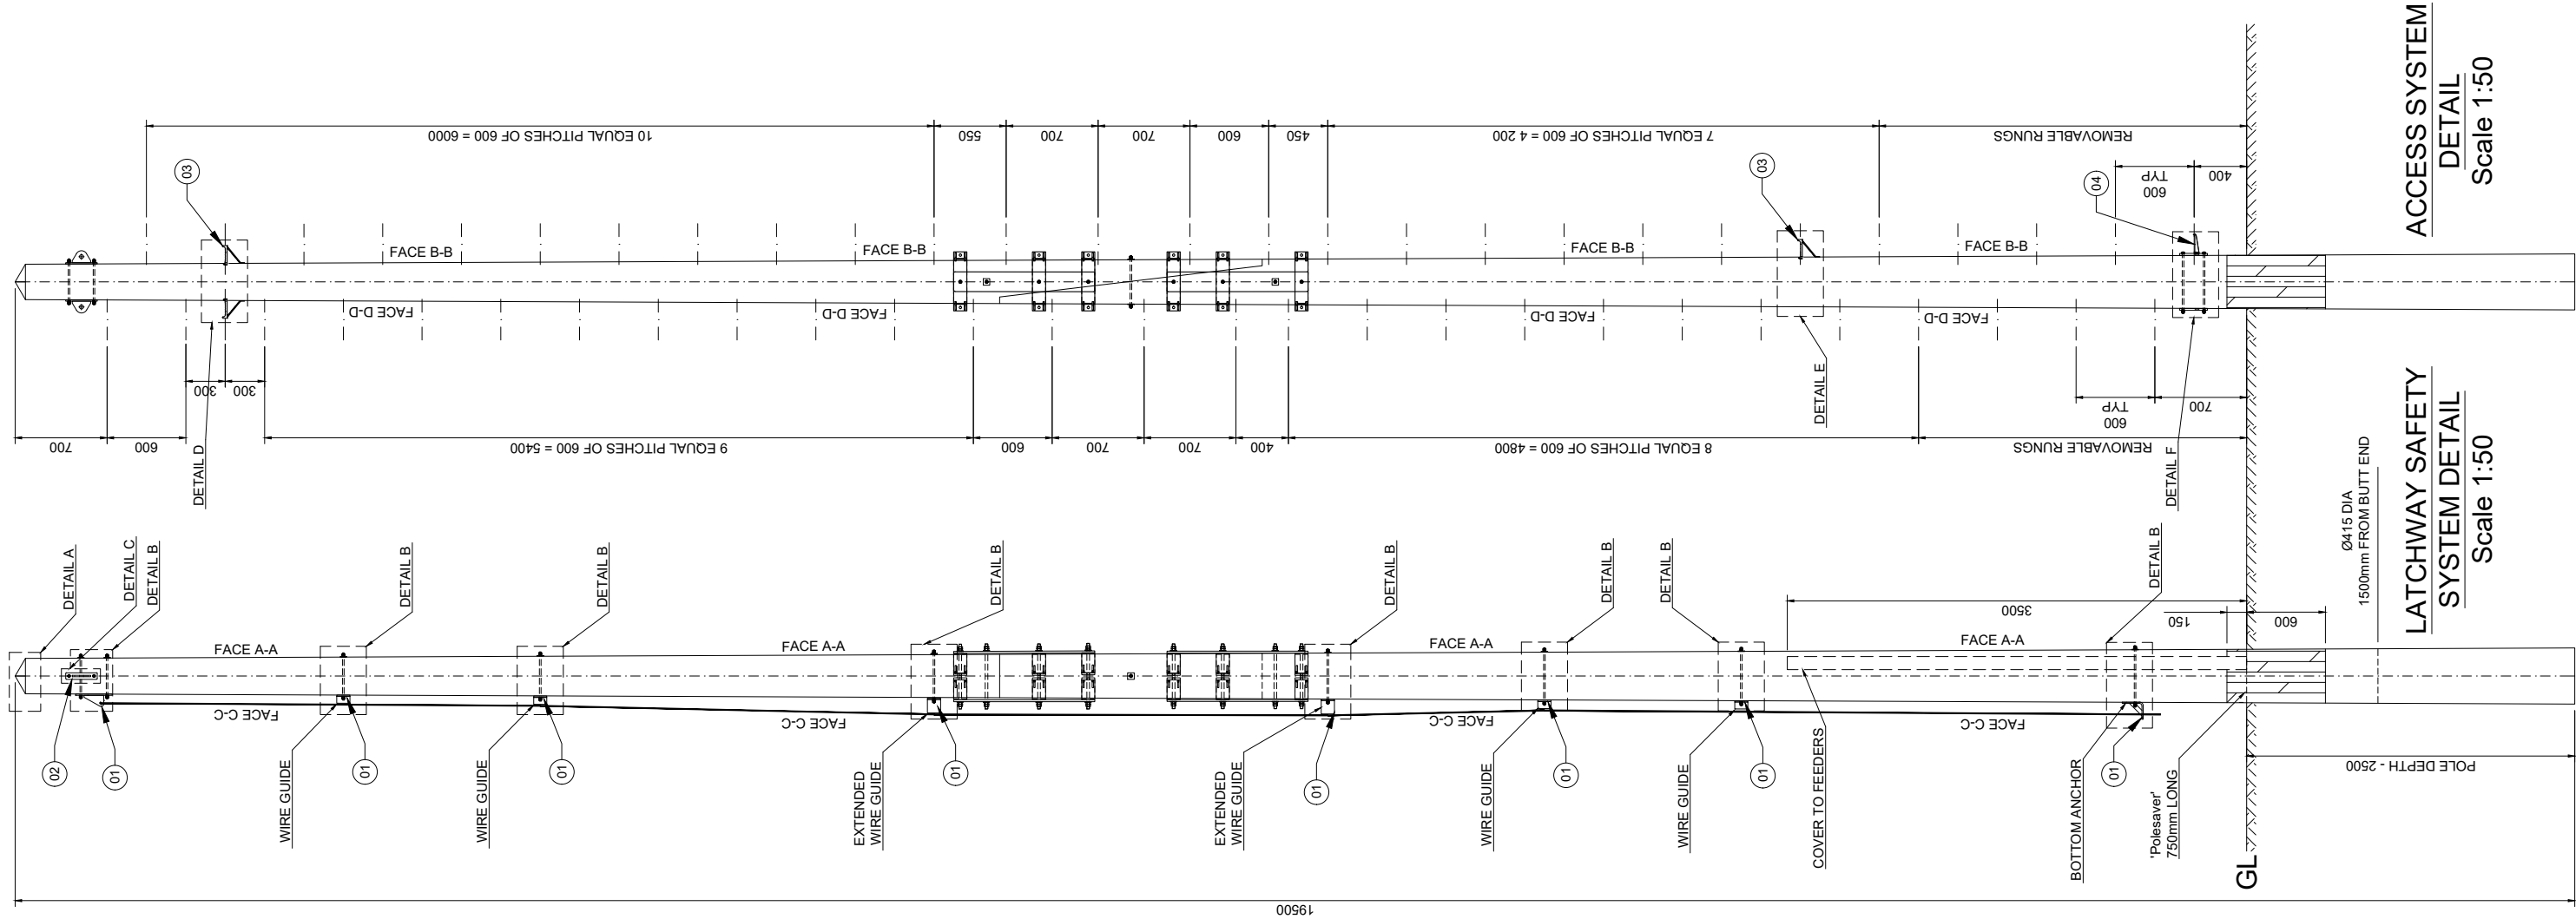

POLE ORIENTATION

Scale 1:20

NOTES

1. SEE DRAWING 305 FOR PARTS LIST
2. ALL BOLTS TO BE CUT ON SITE TO EXTEND MAX 10mm BEYOND THE NUT WHEN TIGHTENED UNO.
3. ALL SITE DRILLED HOLE/CUT ENDS TO BE TREATED WITH METALFLUX 70-40 ZINC PASTE FOLLOWED BY 1 COAT OF 7-42 ZINC ALU OR 70-16 ALUMINIUM SPRAY

TIMBER POLE

1. POLE TO BE SUPPLIED IN ACCORDANCE WITH BS EN14229 & SHALL HAVE MIN. CHARACTERISTIC BENDING STRENGTH OF 30N/mm² & MIN. YOUNGS MODULUS (PARALLEL TO GRAIN) OF 10kN/mm².
2. MARKINGS ON FINISHED POLE SHALL BE AT 4m FROM BUTT AND COMPLY WITH BS EN 14229 UNO
3. AS FAR AS PRACTICABLE ALL CUTTING, SCARFING & DRILLING TO BE DONE BEFORE CREOSOTING. IF NOT ALL CUT, DRILLED & SCARFED SURFACES TO BE COATED WITH A MIXTURE OF CREOSOTE & TAR.
4. POLE TO BE PRESSURE IMPREGNATED WITH CREOSOTE IN ACCORDANCE WITH BS EN 14229
5. MINIMUM DIAMETERS
TOP - Ø205mm
BOTTOM - Ø430mm
6. 19.5m LONG POLE TO BE SOURCED BY TRIMMING 20m LONG POLE BY 0.5m AT THE TOP

SPLICE CONNECTION

1. THE CONTACT SURFACES AND ALL THROUGH HOLES OF THE TIMBER POLE SPLICE ARE TO BE TREATED LIBERALLY WITH SINGLE COAT OF TIMBER COMPATIBLE BITUMINOUS PAINT (E.G. BIRD BRAND BLACK BITUMINOUS PAINT OR SIMILAR APPROVED PRODUCT).
2. PAINT TO BE APPLIED JUST BEFORE SPLICING THE TWO PARTS
3. ANY DISTURBED SURFACES SHALL HAVE THEIR WATERPROOFING REPAIRED WITH SINGLE COAT OF TIMBER COMPATIBLE BITUMINOUS PAINT (E.G. BIRD BRAND BLACK BITUMINOUS PAINT OR SIMILAR APPROVED PRODUCT).

PLANTING

1. CAT SCANNER IS TO BE USED IN ORDER TO CONFIRM THE POSITIONS OF BURIED SERVICES.
2. TIMBER POLE TO BE PLANTED WITH N35 MARKING AT 3.5m FROM BUT FACING 35° FROM NORTH (CLOCKWISE)
3. SEE DRAWING 400 FOR FOUNDATION DETAILS

LATCHWAY SAFETY SYSTEM DETAIL

Scale 1:50


ACCESS SYSTEM DETAIL

Scale 1:50

ALL SCALES AS SHOWN WHEN PRINTED AT A3



ALL SCALES AS SHOWN WHEN PRINTED AT A3

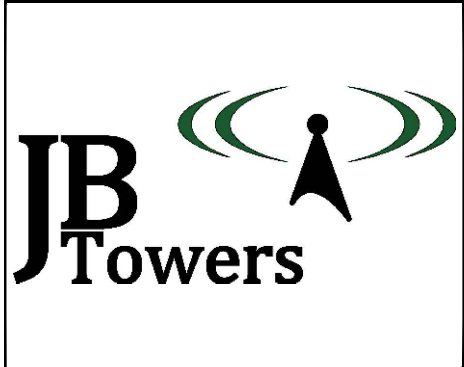

02	SPLICE DETAIL UPDATED		AM	15/07/19	
01	FIRST ISSUE		TT	24/06/19	
REV	REV		BY	DATE	
SCALE AS SHOWN WHEN PRINTED AT A3	DRAWN AM DATE 24/06/19	CHECKED MP DATE 24/06/19	APPROVED JBT DATE 24/06/19		

TITLE


POOLEWE

GENERAL ARRANGEMENT
SHEET 2 OF 3

SITE ADDRESS

INVEREWE GARDENS
POOLEWE
HIGHLAND
IV22 2LG

ARQIVA REF. 141370	DRG No. 200
-----------------------	----------------

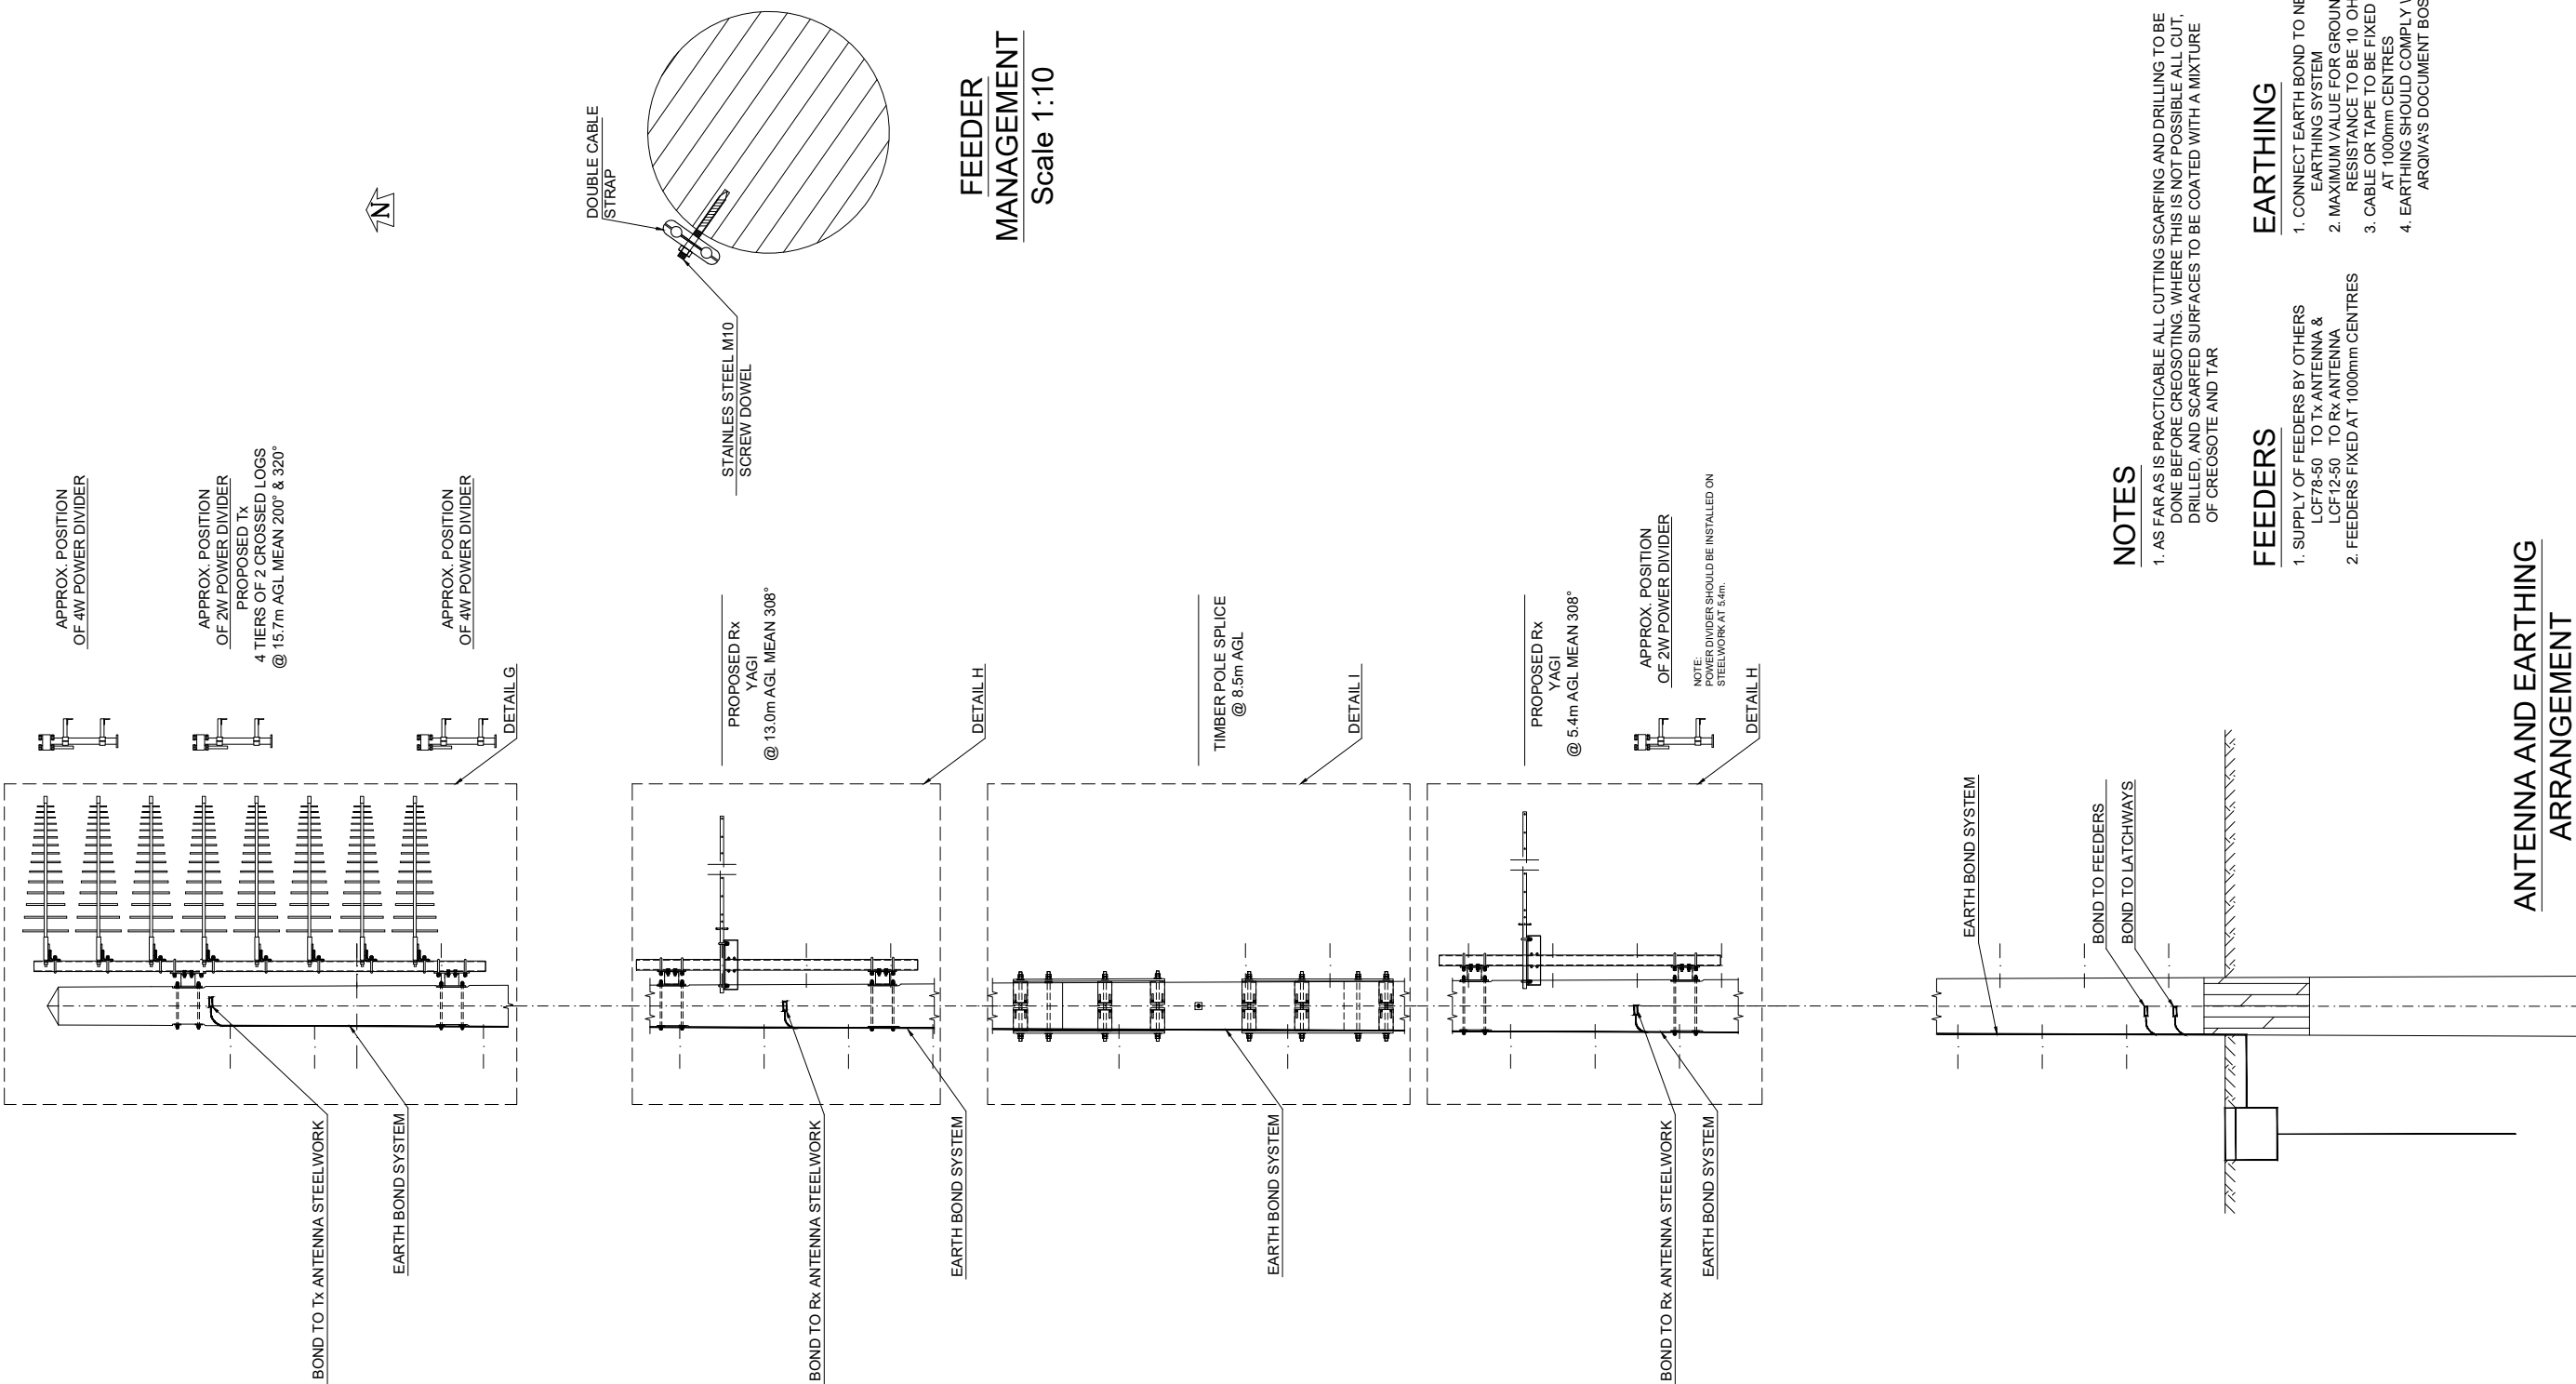


VENNA AND EART ARRANGEMENT

Scale 1:50




ALL SCALES AS SHOWN WHEN PRINTED AT A3

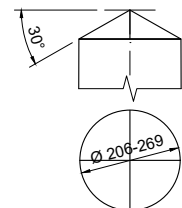


- NOTES:
1. A SINGLE COAT OF TIMBER COMPATIBLE BITUMINOUS PAINT (E.G. BIRD BRAND BLACK BITUMINOUS PAINT OR SIMILAR APPROVED PRODUCT) TO BE APPLIED TO THE UPPER SURFACES AT THE TOP OF THE POLE.
 2. PAINT TO BE APPLIED ON SITE JUST BEFORE ERECTION
- FORM: 4 WAY PYRAMID / CONE


DETAIL A - TIMBER POLE TOP
Scale 1:20

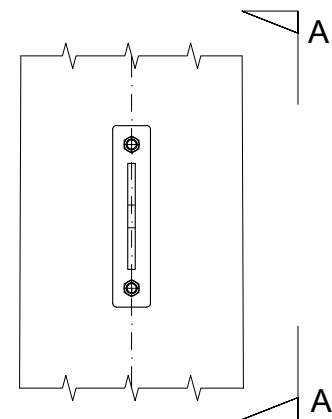


DETAIL C - FALL ARREST
ATTACHMENT POINT
Scale 1:10

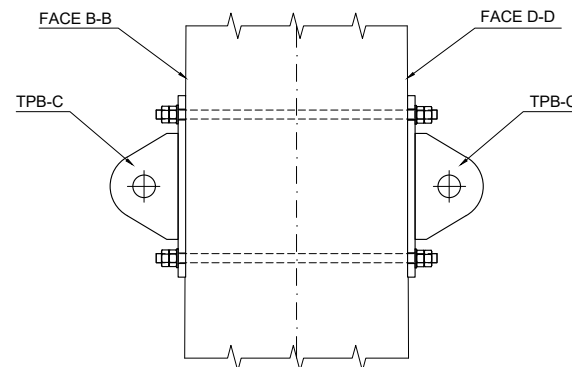


VIEW A-A
Scale 1:10

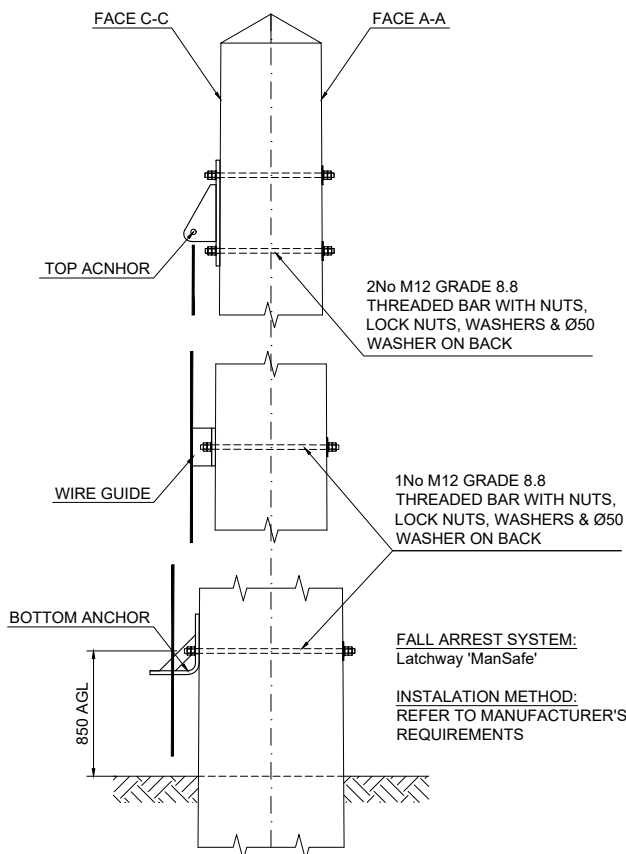

DETAIL B - FALL ARREST SYSTEM
Scale 1:20

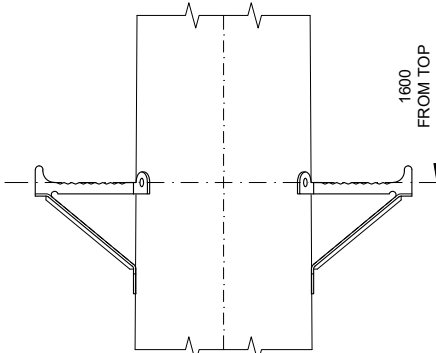


DETAIL D - ANTENNA
ACCESS CLIMBING STEP
Scale 1:10

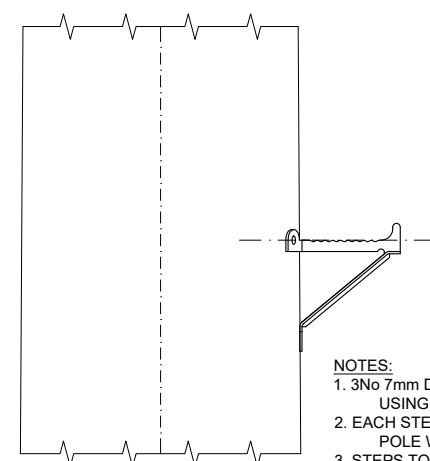


DETAIL E - PERMANENT
CLIMBING STEPS
Scale 1:10

- NOTES:
1. 3 No 7mm DIA 70mm LONG PILOT HOLES TO BE DRILLED USING THE STEP AS A TEMPLATE
 2. EACH STEP SHOULD BE FIXED TO THE TIMBER POLE WITH 3 No 10mm COACH SCREWS 75mm LONG
 3. STEPS TO BE INSTALLED ON FACES B-B & D-D ONLY

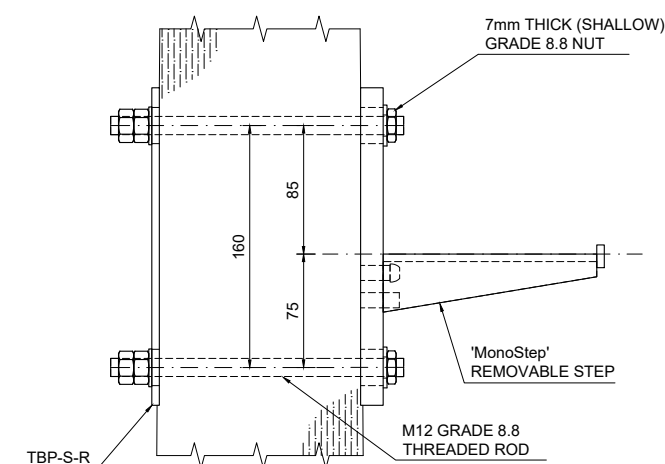

DETAIL F - REMOVABLE
CLIMBING STEPS
Scale 1:5

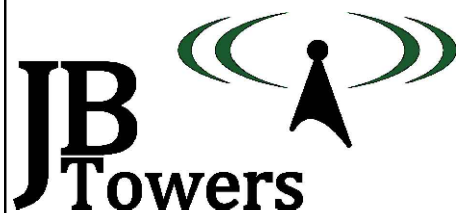

01	FIRST ISSUE	TT	24/06/19
REV	REV	BY	DATE
SCALE AS SHOWN WHEN PRINTED AT A3	DRAWN DATE	AM 24/06/19	CHECKED DATE
	MP 24/06/19	APPROVED DATE	JBT 24/06/19
ALL DIMENSIONS IN mm UNLESS OTHERWISE STATED. THIS DRAWING TO BE READ IN CONJUNCTION WITH OTHER RELEVANT DRAWINGS.			

TITLE
POOLEWE
GENERAL ARRANGEMENT
SHEET 3 OF 3


SITE ADDRESS
INVERWE GARDENS
POOLEWE
HIGHLAND
IV22 2LG

ARQIVA REF.
141370


DRG No.
200

REV
01

ALL SCALES AS SHOWN WHEN PRINTED AT A3

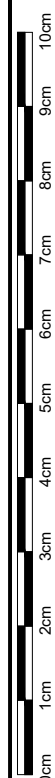

ALL SCALES AS SHOWN WHEN PRINTED AT A3

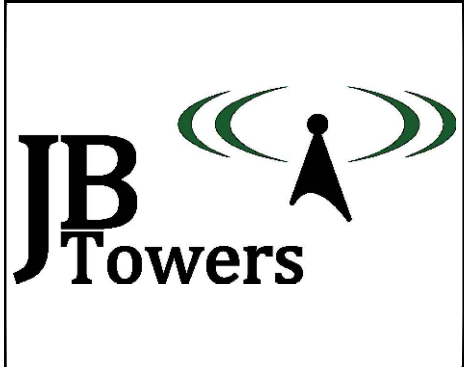

03	WIRE GUIDES POSITIONS UPDATED			AM	17/07/19
02	INTERFACE PLATE THROUGH HOLES ADDED			AM	15/07/19
01	FIRST ISSUE			TT	24/06/19
REV	REV			BY	DATE
SCALE AS SHOWN WHEN PRINTED AT A3		DRAWN	AM	CHECKED	MP
		DATE	24/06/19	DATE	24/06/19
		APPROVED	JBT	DATE	24/06/19
ALL DIMENSIONS IN mm UNLESS OTHERWISE STATED. THIS DRAWING TO BE READ IN CONJUNCTION WITH OTHER RELEVANT DRAWINGS.					

TITLE

POOLEWE


TIMBER POLE HOLE SET OUT

SHEET 1 OF 2


SITE ADDRESS

INVEREWE GARDENS
POOLEWE
HIGHLAND
IV22 2LG

ARQIVA REF. 141370	DRG No. 201
-----------------------	----------------

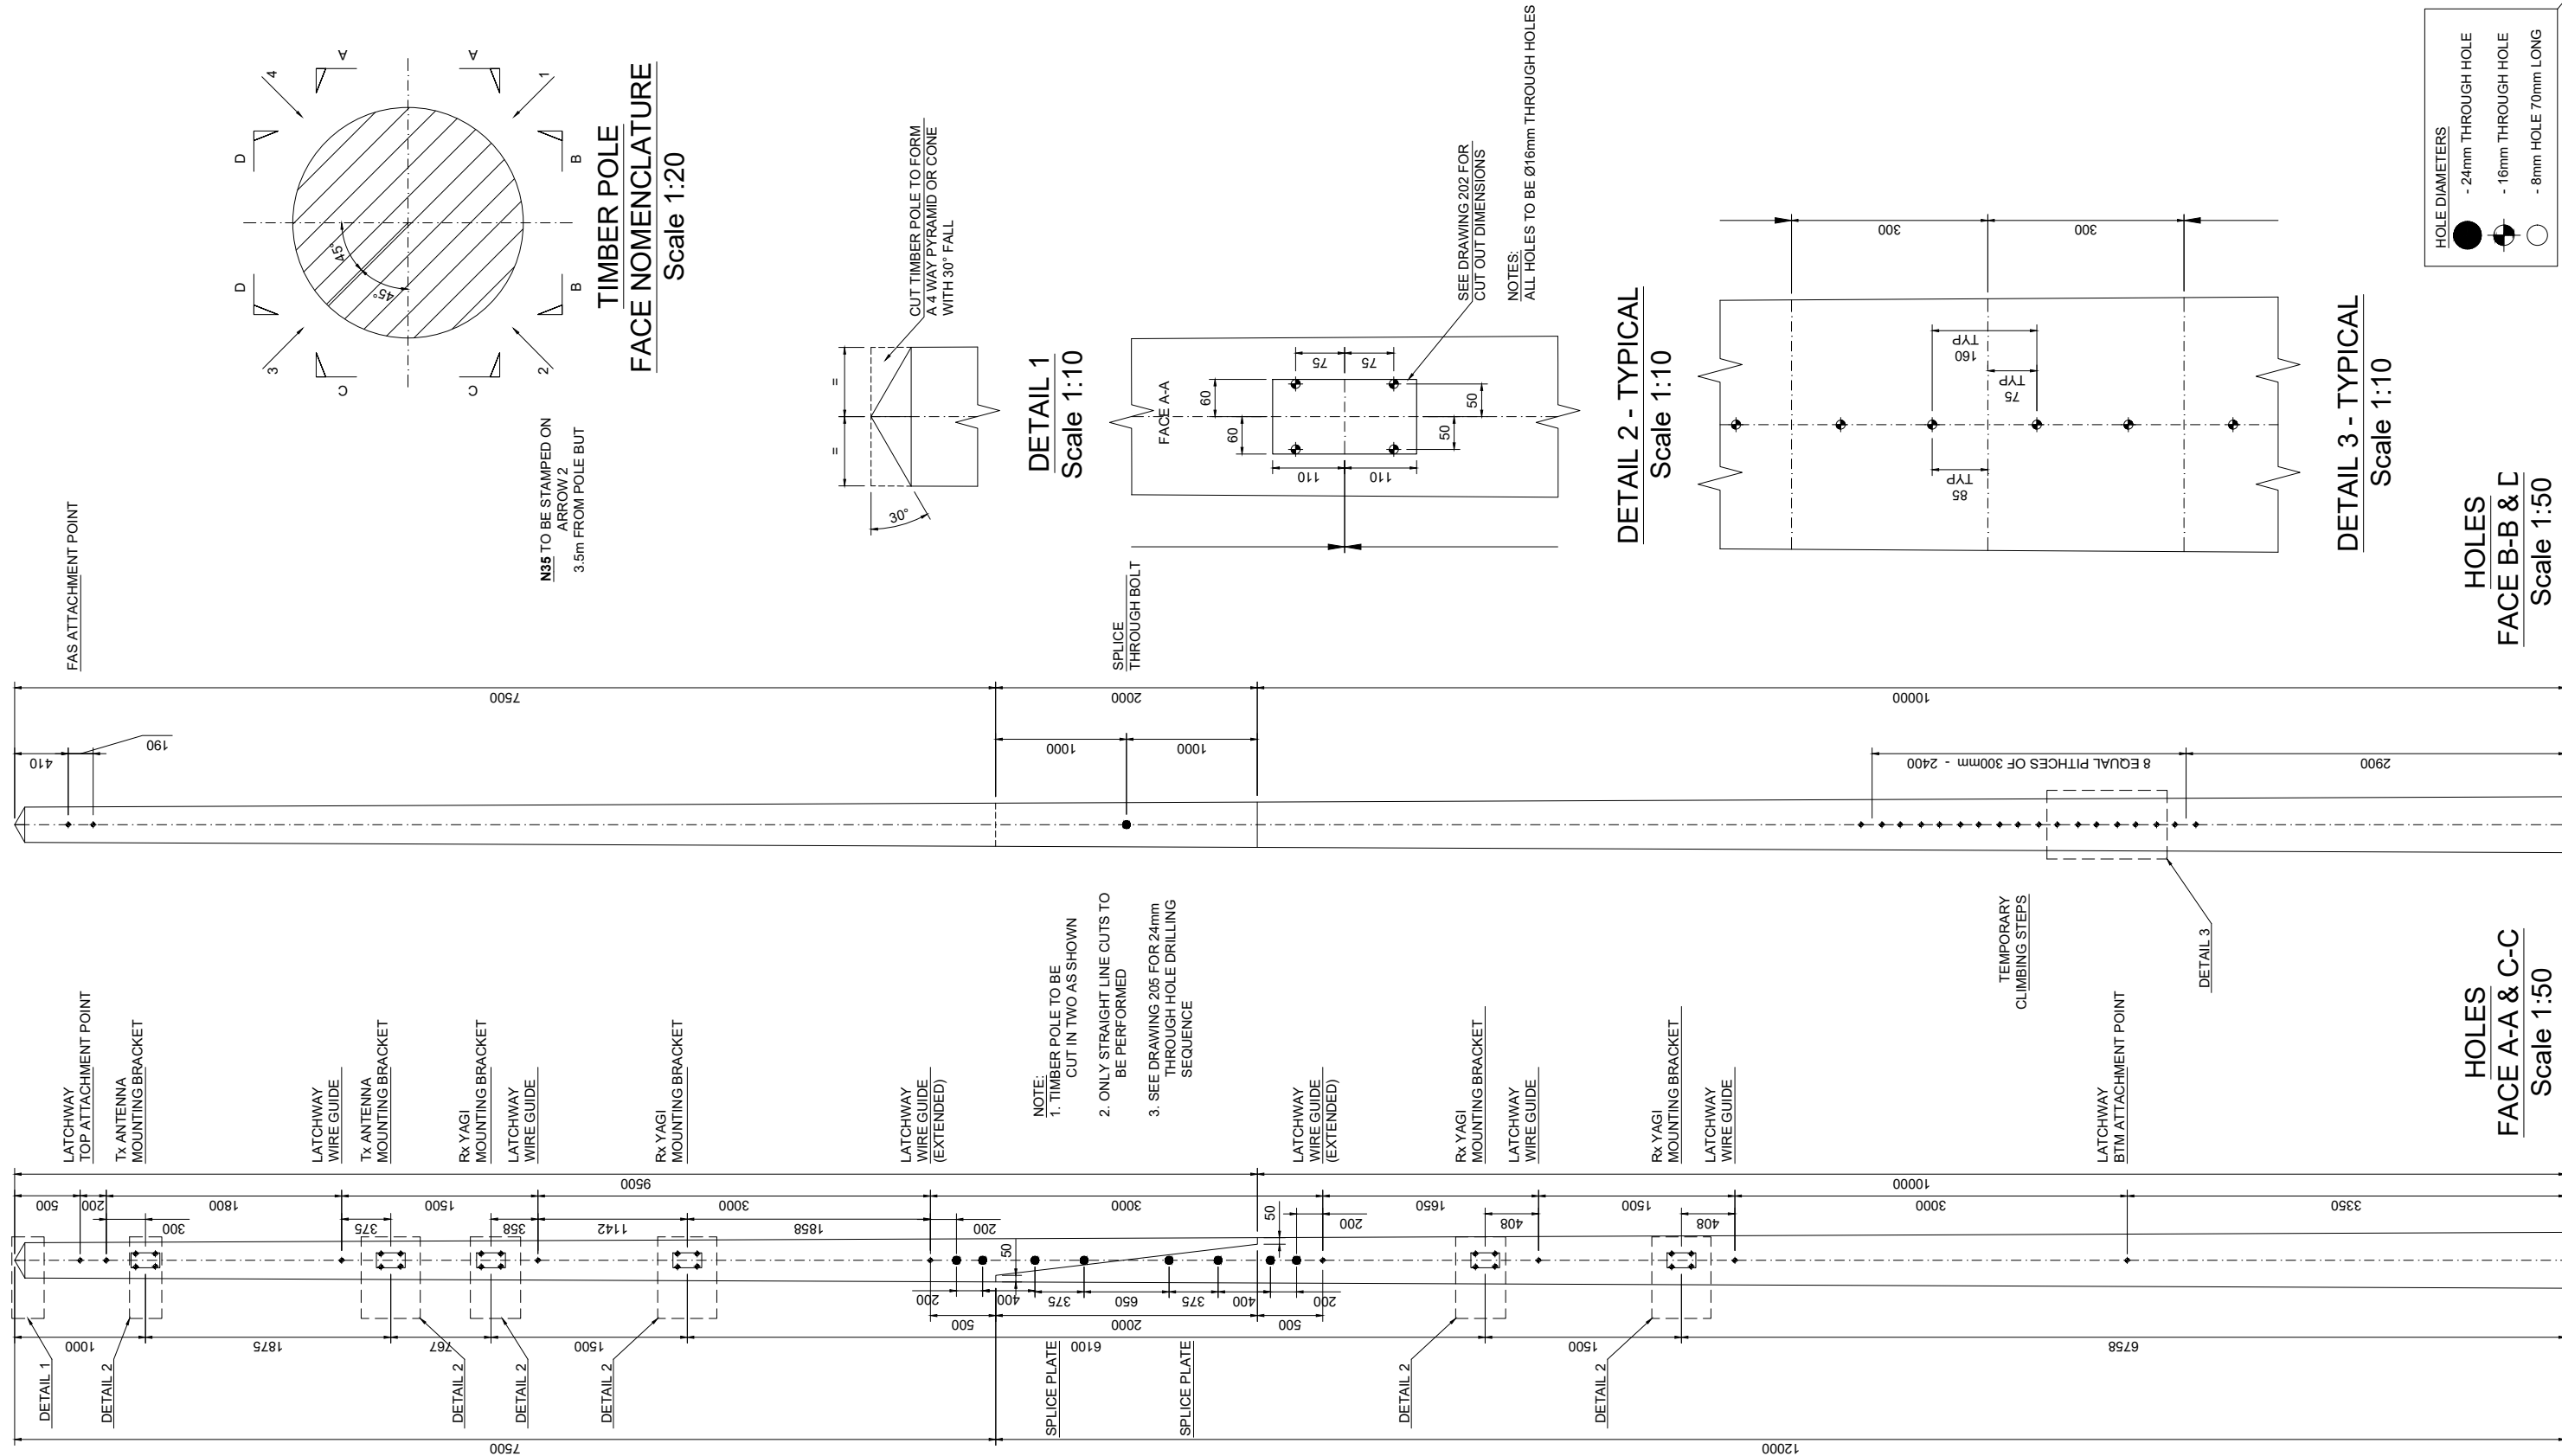REV
03

ALL SCALES AS SHOWN WHEN PRINTED AT A3

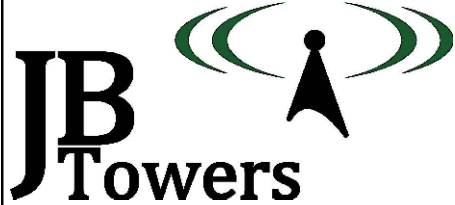

01	FIRST ISSUE			TT	24/06/19
REV	REV			BY	DATE
SCALE AS SHOWN		DRAWN	AM	CHECKED	MP
WHEN PRINTED AT A3		DATE	24/06/19	DATE	24/06/19
		APPROVED	JBT	DATE	24/06/19
ALL DIMENSIONS IN mm UNLESS OTHERWISE STATED. THIS DRAWING TO BE READ IN CONJUNCTION WITH OTHER RELEVANT DRAWINGS.					

TITLE

POOLEWE
TIMBER POLE HOLE SET OUT
SHEET 2 OF 2


SITE ADDRESS

INVEREWE GARDENS
POOLEWE
HIGHLAND
IV22 2LG

ARQIVA REF.
141370

DRG No.
201


REV
01

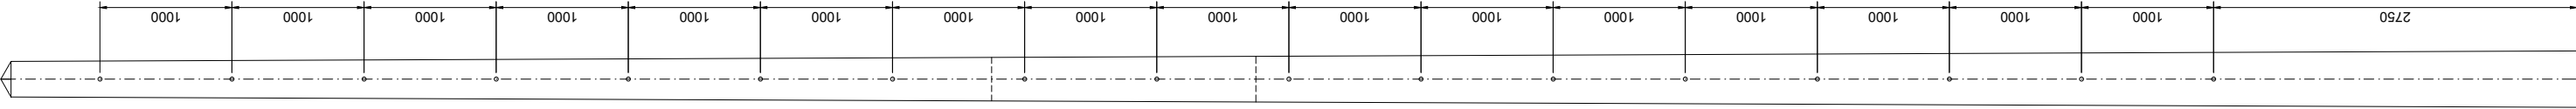

FEEDER BRACKETS

ALL HOLES ON ARROW 1
TO BE Ø8mm & 70mm LONG

HOLES
ARROW 1
Scale 1:50

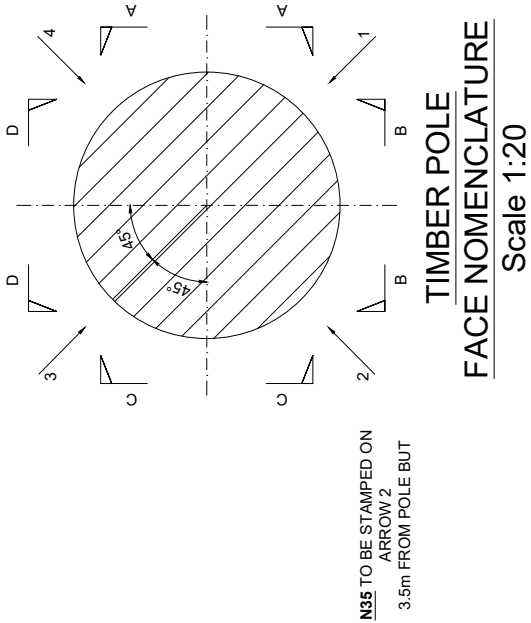

N35 TO BE STAMPED ON
ARROW 2
3.5m FROM POLE BUT

TIMBER POLE
FACE NOMENCLATURE
Scale 1:20



ALL SCALES AS SHOWN WHEN PRINTED AT A3

ALL SCALES AS SHOWN WHEN PRINTED AT A3

01	FIRST ISSUE			TT	24/06/19
REV	REV			BY	DATE
SCALE AS SHOWN		DRAWN	AM	CHECKED	MP
WHEN PRINTED AT A3		DATE	24/06/19	DATE	24/06/19
		APPROVED	JBT	DATE	24/06/19
ALL DIMENSIONS IN mm UNLESS OTHERWISE STATED. THIS DRAWING TO BE READ IN CONJUNCTION WITH OTHER RELEVANT DRAWINGS.					


TITLE
POOLEWE
TIMBER POLE CUT OUT
DETAIL



SITE ADDRESS
INVEREWE GARDENS
POOLEWE
HIGHLAND
IV22 2LG

ARQIVA REF.
141370



DRG No.
202

REV
01

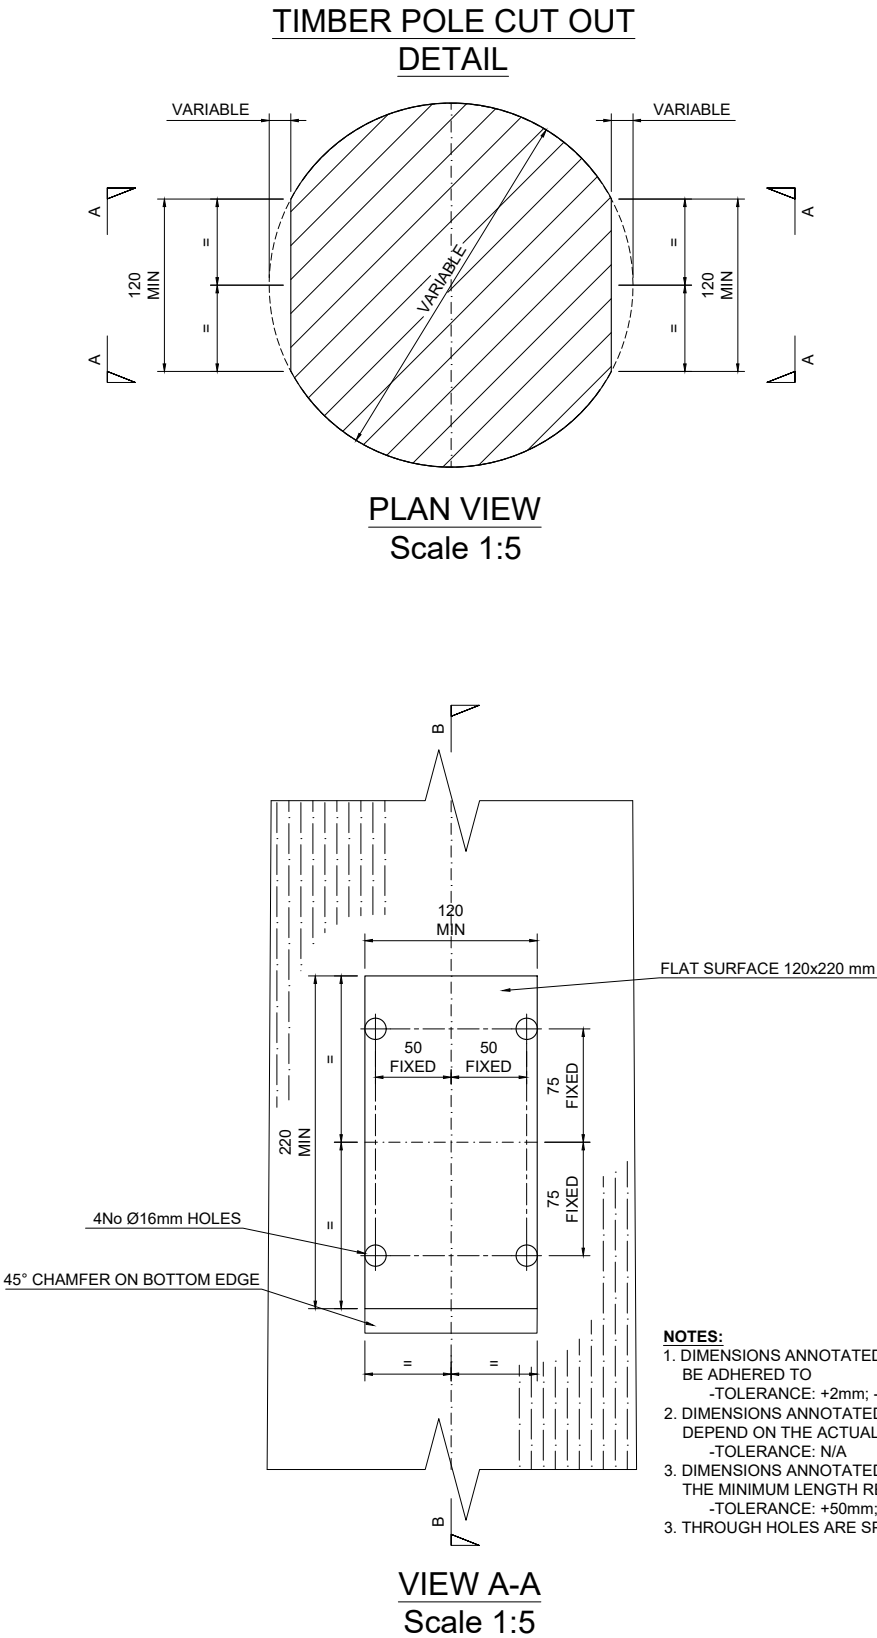

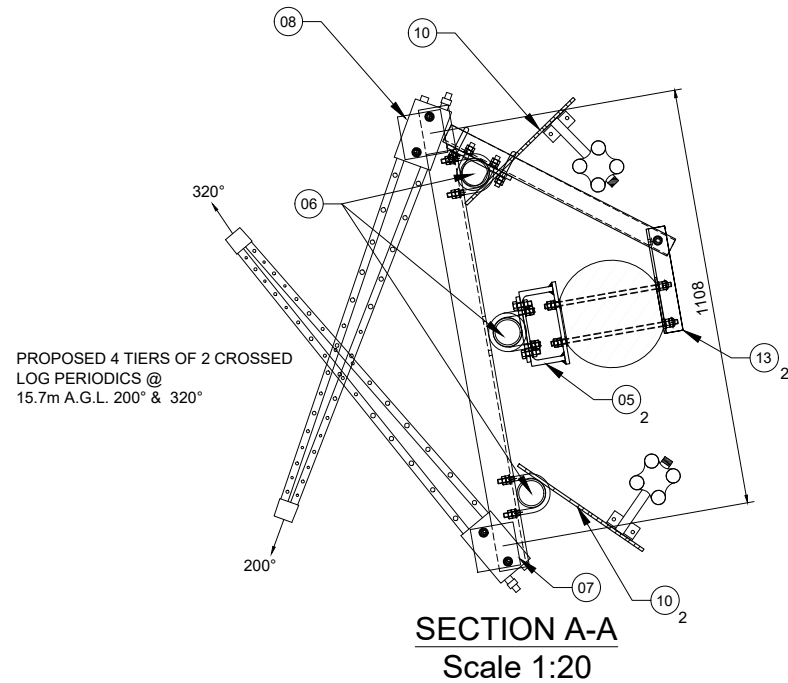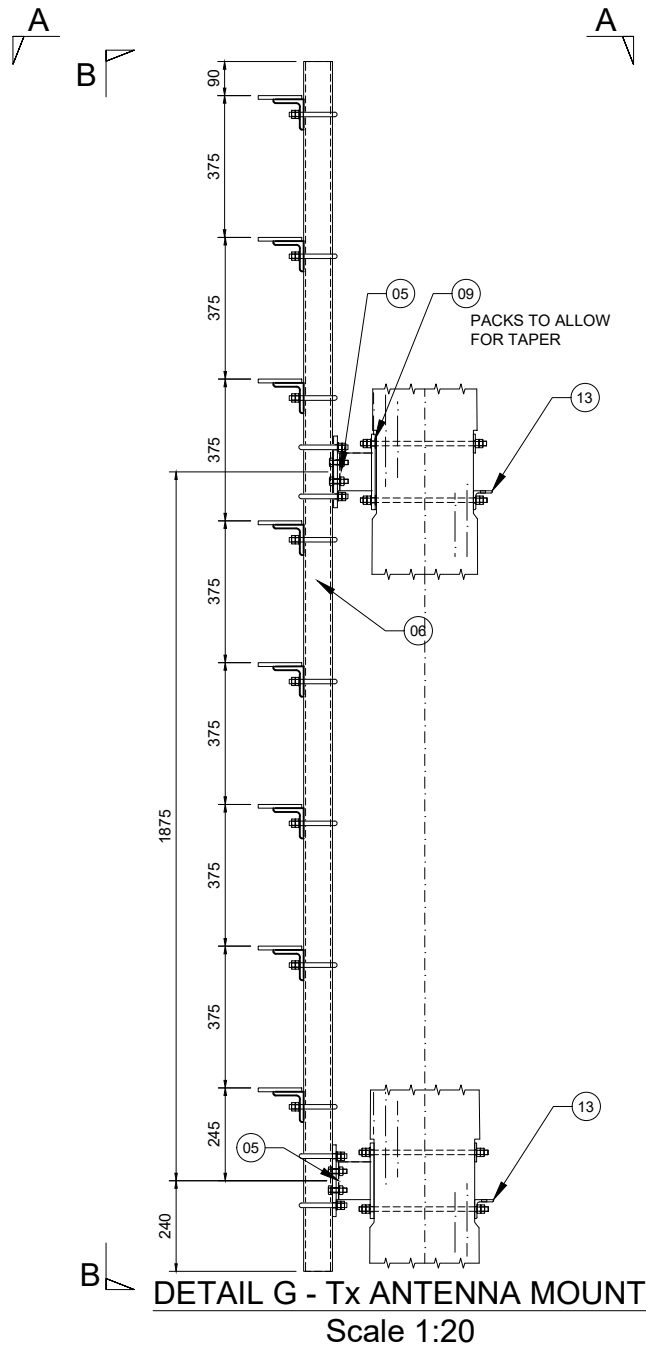

NOTE:
ALL M12 U-BOLTS TO BE
TIGHTENED TO 50Nm

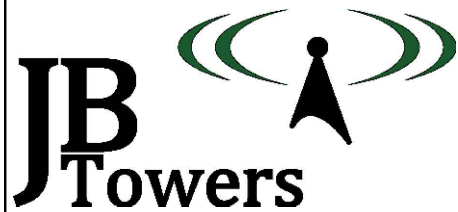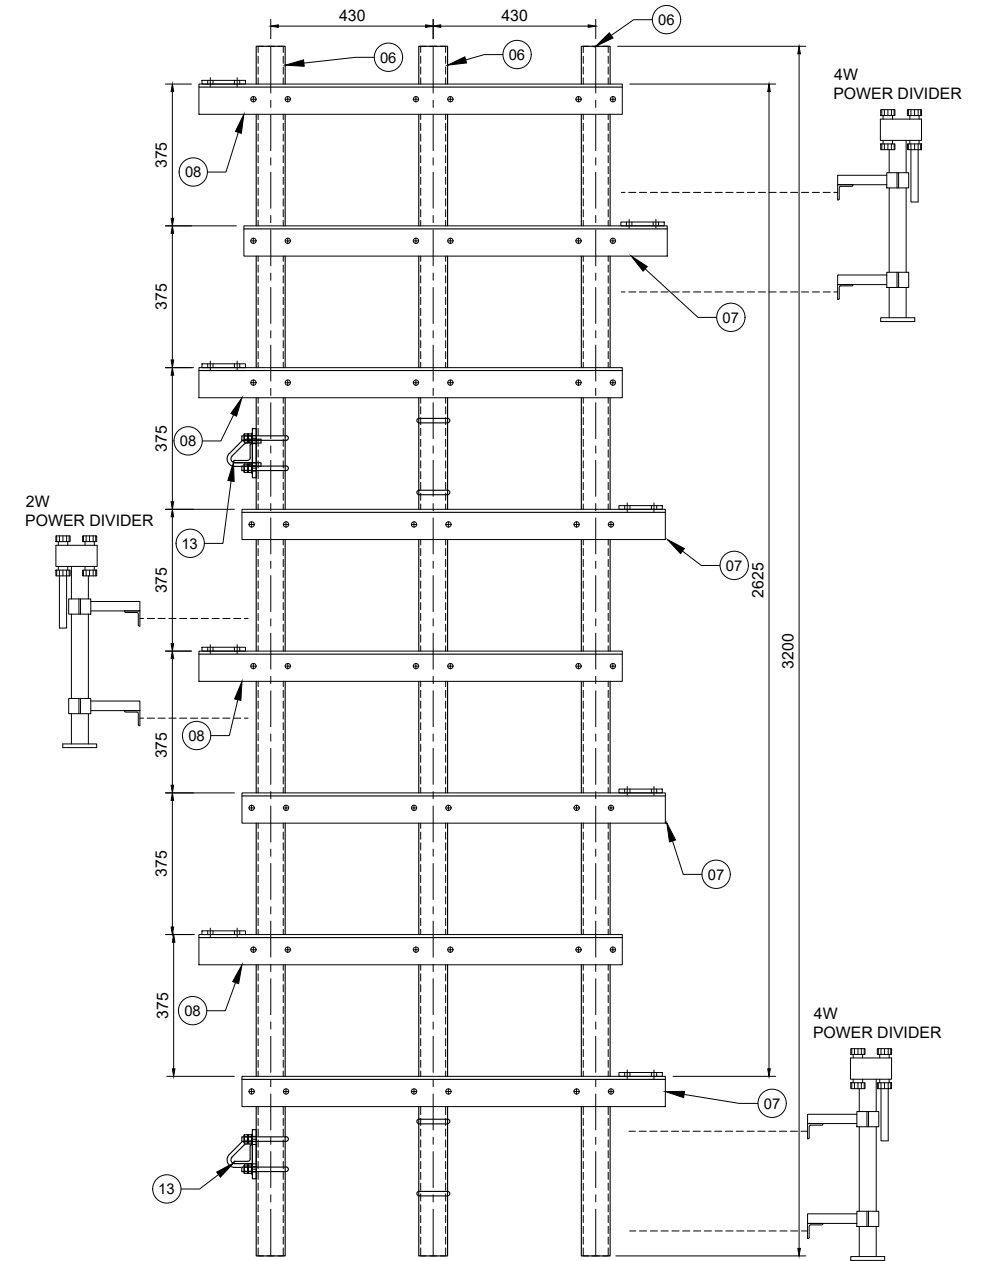


01	FIRST ISSUE	TT	24/06/19
REV	REV	BY	DATE
SCALE AS SHOWN WHEN PRINTED AT A3	DRAWN DATE 24/06/19	CHECKED DATE 24/06/19	APPROVED DATE 24/06/19
ALL DIMENSIONS IN mm UNLESS OTHERWISE STATED. THIS DRAWING TO BE READ IN CONJUNCTION WITH OTHER RELEVANT DRAWINGS.			


TITLE	SITE ADDRESS		
ANTENNA MOUNT	INVEREWE GARDENS		
DETAIL G	POOLEWE		
	HIGHLAND		
	IV22 2LG		
	ARQIVA REF. 141370	DRG No. 203	REV 01

ALL SCALES AS SHOWN WHEN PRINTED AT A3




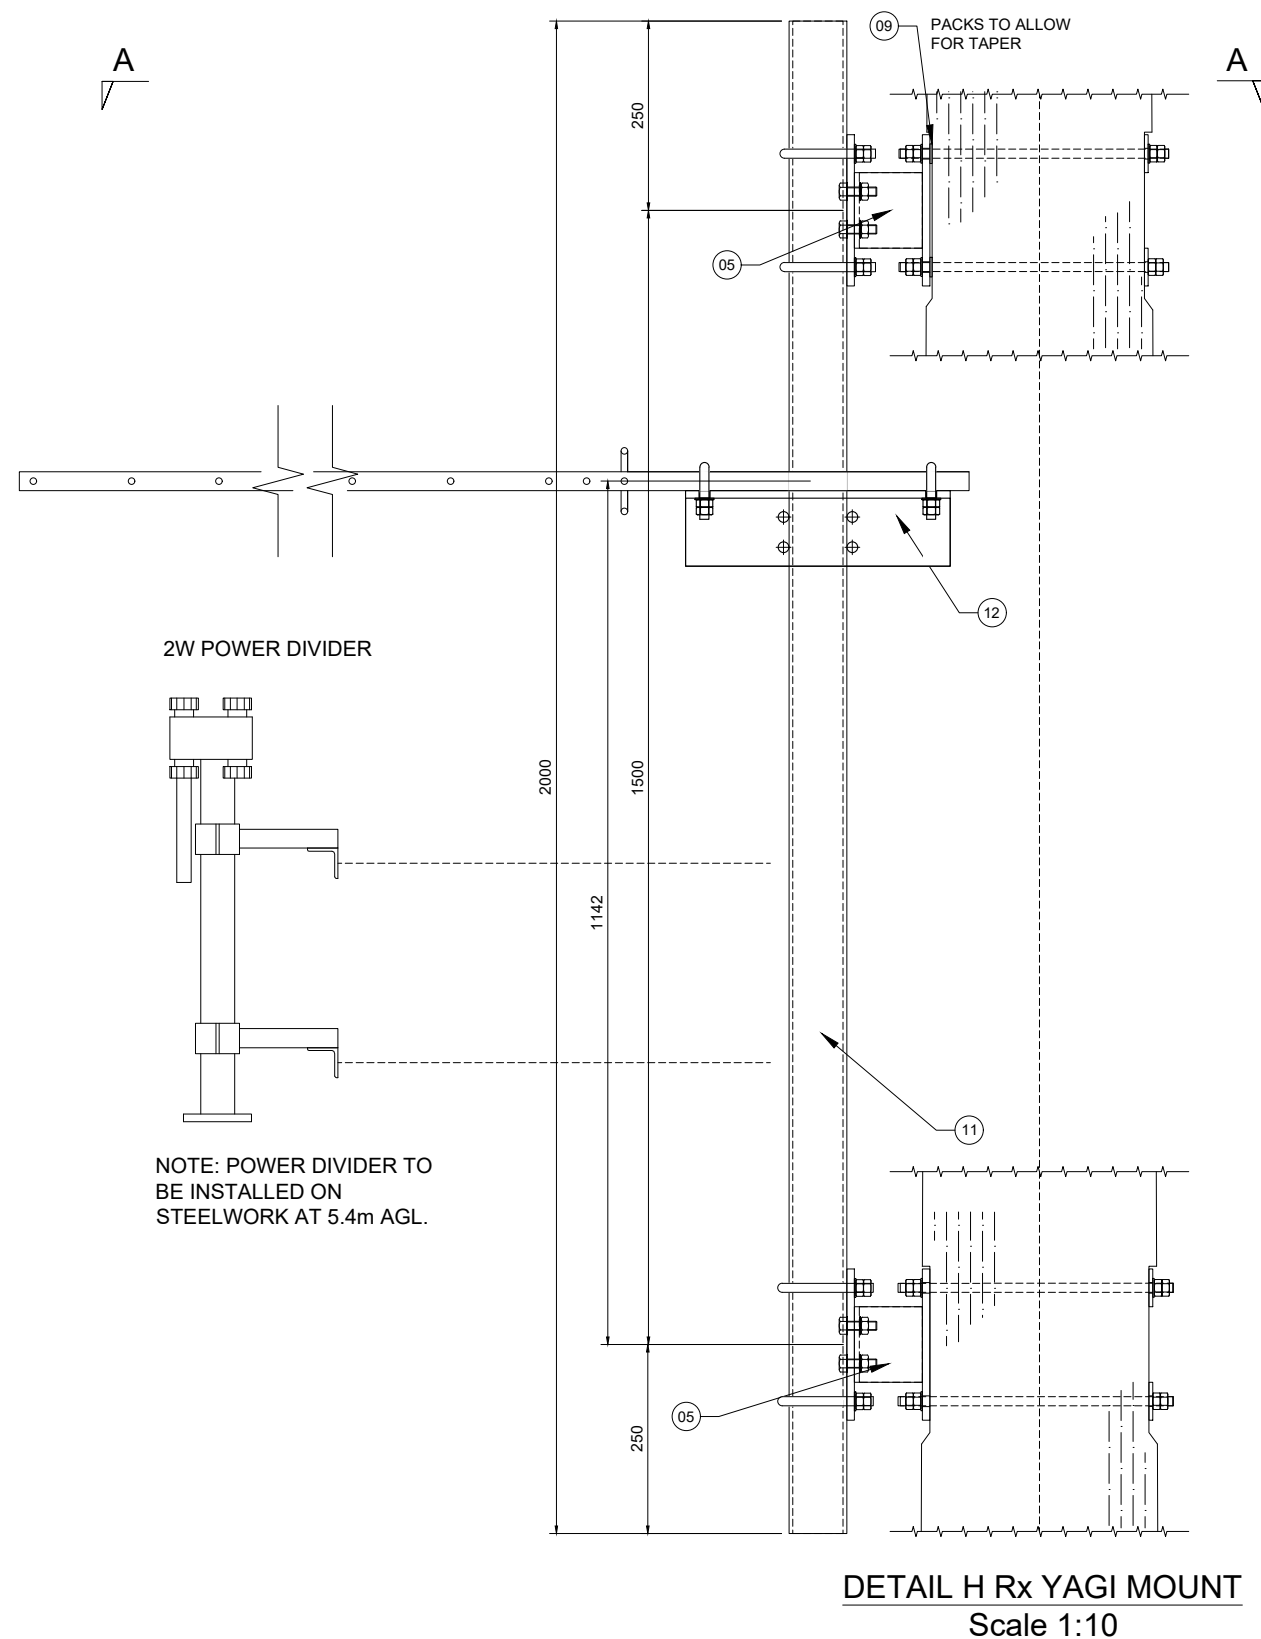

PROPOSED 1No. YAGI ANTENNA
@ 5.4m & 13.0m A.G.L. 308°

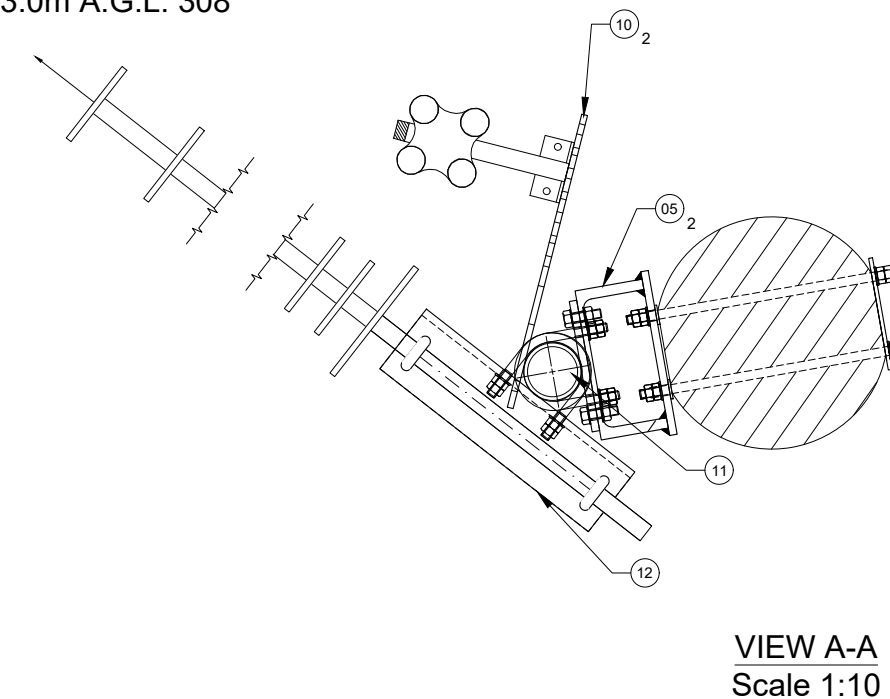

NOTE:
ALL M12 U-BOLTS TO BE
TIGHTENED TO 50Nm

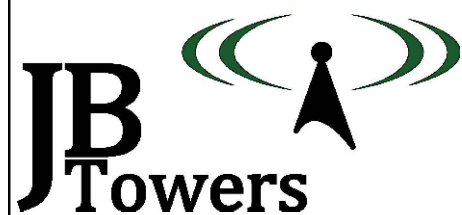

01	FIRST ISSUE	TT	24/06/19
REV	REV	BY	DATE
SCALE AS SHOWN WHEN PRINTED AT A3	DRAWN AM DATE 24/06/19	CHECKED MP DATE 24/06/19	APPROVED JBT DATE 24/06/19
ALL DIMENSIONS IN mm UNLESS OTHERWISE STATED. THIS DRAWING TO BE READ IN CONJUNCTION WITH OTHER RELEVANT DRAWINGS.			

TITLE
ANTENNA MOUNT
DETAIL H

SITE ADDRESS
INVEREWE GARDENS
POOLEWE
HIGHLAND
IV22 2LG

ARQIVA REF.
141370


DRG No.
204

REV
01


ALL SCALES AS SHOWN WHEN PRINTED AT A3



ALL SCALES AS SHOWN WHEN PRINTED AT A3

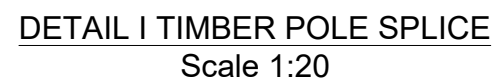


- ALL M16 BOLTS TO BE TIGHTENED TO 90Nm
- ALL M20 THROUGH BOLTS, COMBINING THE COLLARS & INTERFACE PLATES TO BE FINGER TIGHT
- ALL SITE DRILLED HOLE/CUT ENDS TO BE TREATED WITH METAFLUX 70-40 ZINC PASTE FOLLOWED BY 1 COAT OF 7-42 ZINC ALU OR 70-16 ALUMINIUM SPRAY

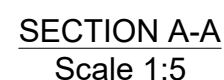


- WORK SEQUENCE (PRIOR TO POLE BEING SENT TO SITE):
1. LOCATION OF COLLARS TO BE MARKED ON POLE AND POLE OD AT THESE LOCATIONS TO BE MEASURED AND USED TO INFORM THE FABRICATION OF THE STEEL COLLARS.
(COLLAR HOLES FOR THE THROUGH BOLTS ARE TO BE DRILLED LATER)
 2. HOLES IN POLE FOR ALL COLLAR THROUGH BOLTS TO BE DRILLED.
 3. SPLICE JOINT TO BE CUT IN POLE.
 4. POLE TO BE PRESSURE IMPREGNATED WITH CREOSOTE.
 5. POLE SECTIONS TO BE OFFERED TO ONE ANOTHER AND ONCE IN THE CORRECT POSITION COLLARS 2 SHALL BE INSTALLED TO HOLD THE POLE IN POSITION AND THE CLAMPING BOLTS TORQUED.
 6. THE THROUGH BOLT IN THE CENTRE OF THE SPLICE SHALL BE DRILLED AND THE THROUGH BOLT INSERTED.
 7. THE THROUGH BOLTS FOR COLLARS 1 & 3 SHALL BE INSTALLED AND THE COLLARS OFFERED UP AND THE REQD HOLE LOCATIONS IN THE COLLARS MARKED AND THEN DRILLED.
 8. THESE COLLARS SHALL BE INSTALLED OVER THE THROUGH BOLTS AND THEN THE CLAMPING BOLTS TORQUED.
 9. COLLARS 2 SHALL THEN BE REMOVED AND THE THROUGH BOLTS INSTALLED AND THE COLLARS OFFERED UP AND THE REQD HOLE LOCATIONS IN THE COLLARS MARKED AND THEN DRILLED.
 10. THESE COLLARS SHALL BE INSTALLED OVER THE THROUGH BOLTS AND THEN THE CLAMPING BOLTS TORQUED.
 11. THE VERTICAL PLATES STRAPPING THE COLLARS TOGETHER SHALL THEN BE INSTALLED.
 12. THE FIT OF ALL ELEMENTS OF THE SPLICE SHALL BE CHECKED AND ONCE SATISFACTORY FIT HAS BEEN CONFIRMED THE SPLICE JOINT CAN BE DISASSEMBLED.
 13. ANY DISTURBED SURFACES SHALL HAVE THEIR WATERPROOFING REPAIRED AS PER NOTES ON DRG 200
 14. THE CLAMPING BOLTS USED IN THE CHECK ERECTION SHALL BE DISCARDED AND NEW BOLTS SUPPLIED TO SITE.



02	DETAIL UPDATED			AM	16/07/19
01	FIRST ISSUE			AM	24/06/19
REV	REV			BY	DAT
SCALE AS SHOWN WHEN PRINTED AT A3		DRAWN AM DATE 24/06/19	CHECKED MP DATE 24/06/19	APPROVED JB DATE 24/06/19	
ALL DIMENSIONS IN mm UNLESS OTHERWISE STATED. THIS DRAWING TO BE READ IN CONJUNCTION WITH OTHER RELEVANT DRAWINGS.					

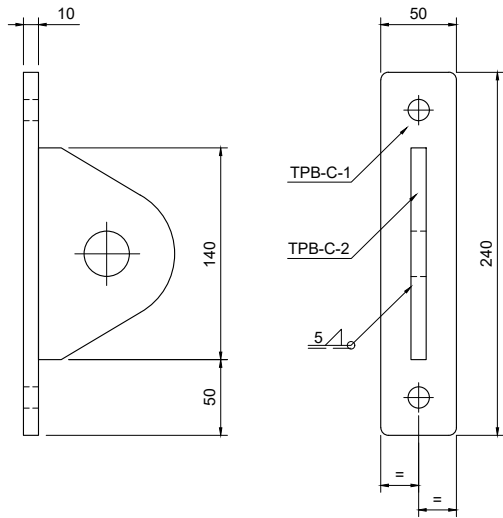

PART TPB-C
Scale 1:5

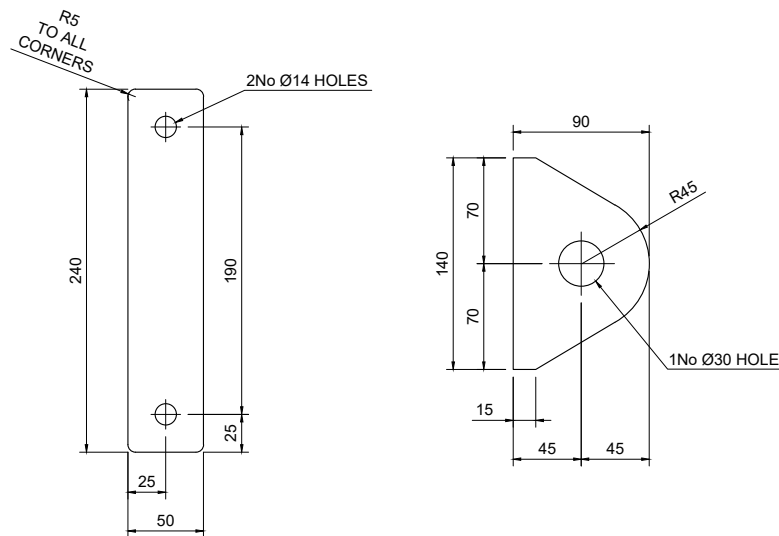


TPB-C-1 - 10mm THICK
Scale 1:5

TPB-C-2 - 10mm THICK
Scale 1:5

Parts list for TPB-C


Item	Part	Quantity	Part description	Length	Material	Weight
01	TPB-C-1	1	Plate 240x50x10mm	N/A	S275J0	0.94 kg
02	TPB-C-2	1	Plate 140x90x10mm	N/A	S275J0	0.99 kg
03	STUDS	1	M12 STUDDING	350mm	GRADE 8.8	0.31 kg
Total Weight:						2.24 kg

- All steel hot dip galvanized
- Each STUD to be supplied with 4 Full Nuts, 2 Flat Washers and 2 Spring Washers
- For fabrication notes see drawing 305

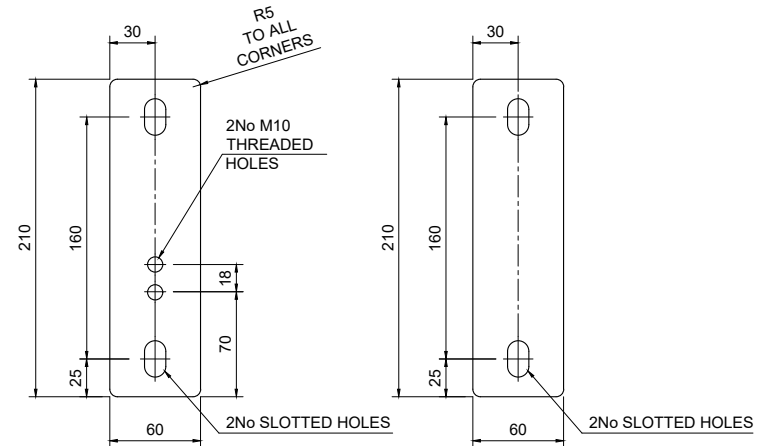

PART TPS-R-1
Scale 1:5

PART TPS-R-2
Scale 1:5

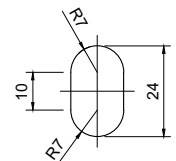


SLOTTED HOLE DETAIL
Scale 1:2

Parts list for TPS-R

Item	Part	Quantity	Part description	Length	Material	Weight
01	TPS-R-1	1	210x60x15mm	N/A	S275J0	1.48 kg
02	TPS-R-2	1	210x60x5mm	N/A	S275J0	0.49 kg
03	STUDS	2	M12 STUDDING	500mm	GRADE 8.8	0.44 kg
04	NUT-S	2	M12 SHALLOW NUT	N/A	GRADE 8.8	-
05	NUT	4	M12 NUT	N/A	GRADE 8.8	-
06	WSH	4	M12 WASHER	N/A	GRADE 8.8	-
Total Weight:						2.85 kg

- All steel hot dip galvanized
- For fabrication notes see drawing 305

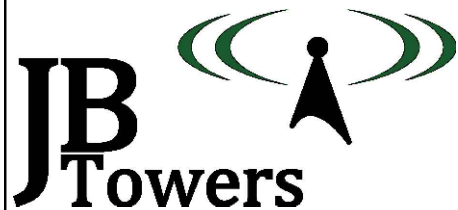



01	FIRST ISSUE	TT	24/06/19
REV	REV	BY	DATE
SCALE AS SHOWN WHEN PRINTED AT A3	DRAWN DATE 24/06/19	CHECKED DATE 24/06/19	APPROVED DATE 24/06/19
ALL DIMENSIONS IN mm UNLESS OTHERWISE STATED. THIS DRAWING TO BE READ IN CONJUNCTION WITH OTHER RELEVANT DRAWINGS.			

TITLE ATTACHMENT POINT & TEMPORARY STEP DETAILS PARTS: TPB-C; TPS-R		SITE ADDRESS INVEREWE GARDENS POOLEWE HIGHLAND IV22 2LG	
ARQIVA REF. 141370		DRG No. 300	REV 01


ALL SCALES AS SHOWN WHEN PRINTED AT A3




ALL SCALES AS SHOWN WHEN PRINTED AT A3

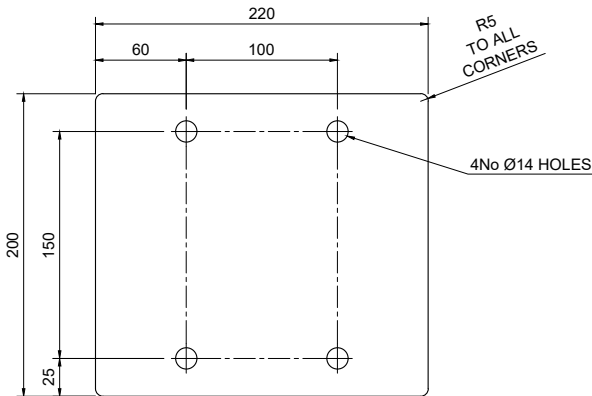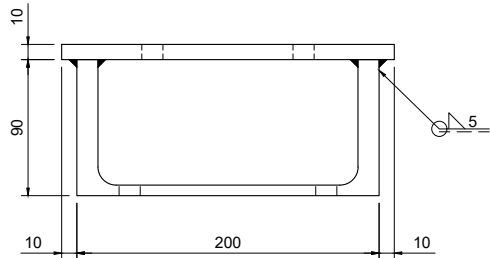


TPB-B-1 - 10mm THICK
Scale 1:5

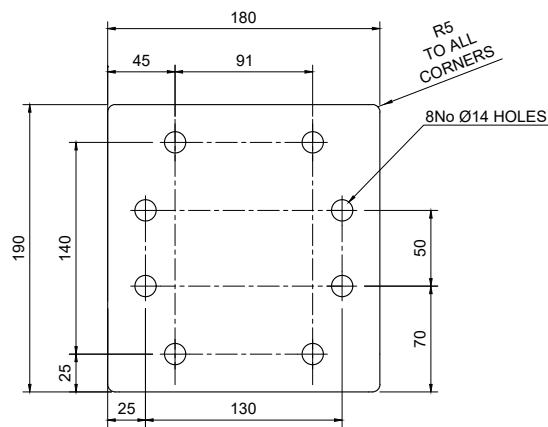


TPB-B-5 - 10mm THICK
Scale 1:5

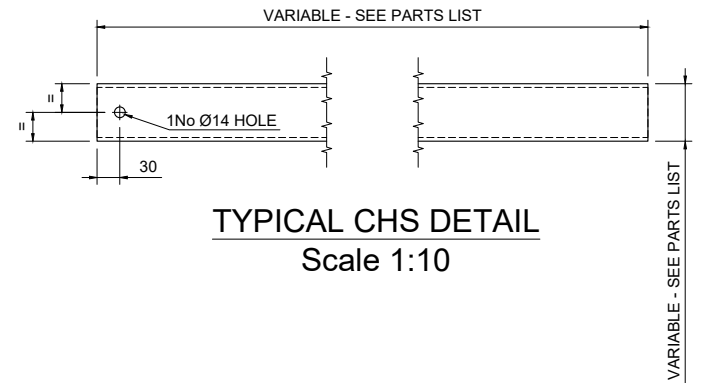


TYPICAL CHS DETAIL
Scale 1:10

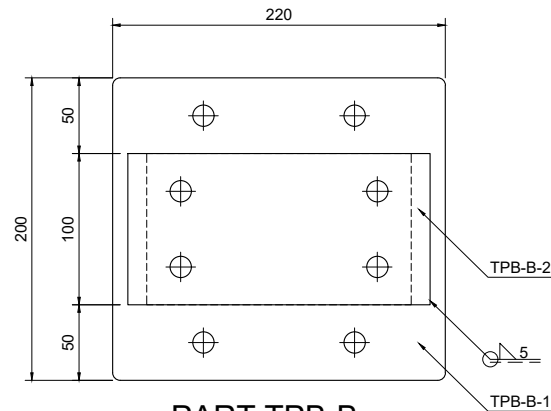

PART TPB-B
Scale 1:5

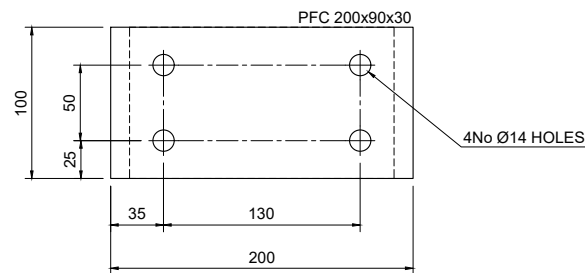

TPB-B-2 - PFC 200x90x30
Scale 1:5

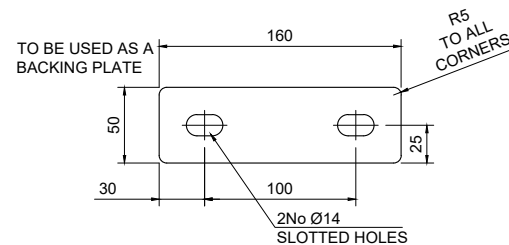


TPB-B-4 - 5mm THICK
Scale 1:5


Parts list for TPB-B

Item	Part	Quantity	Part description	Length	Material	Weight
01	TPB-B-1	1	Plate 220x200x10mm	N/A	S275J0	3.45 kg
02	TPB-B-2	1	PFC 200x90x30	100mm	S275J0	3.00 kg
03	TPB-B-4	2	Plate 160x50x5mm	N/A	S275J0	0.31 kg
04	TPB-B-5	1	Plate 190x180x10mm	N/A	S275J0	2.70 kg
05	STUDS	4	M12 STUDDING	450mm	GRADE 8.8	0.39 kg
06	BOLT	4	M12 45mm LONG (2D+6)	45mm	GRADE 8.8	-
07	U-BOLT	2	M12 U-BOLT FOR CHS 76.1	N/A	GRADE 8.8	-
Total Weight:						11.02 kg

- All steel hot dip galvanized
- Each STUD & U-BOLT to be supplied with 4 Full Nuts, 2 Flat Washers and 2 Spring Washers
- Each BOLT to be supplied with 1 Full Nut, 1 Form E FLat Washer and 1 Spring Washer
- For fabrication notes see drawing 305

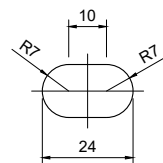

SLOTTED HOLE DETAIL
Scale 1:2

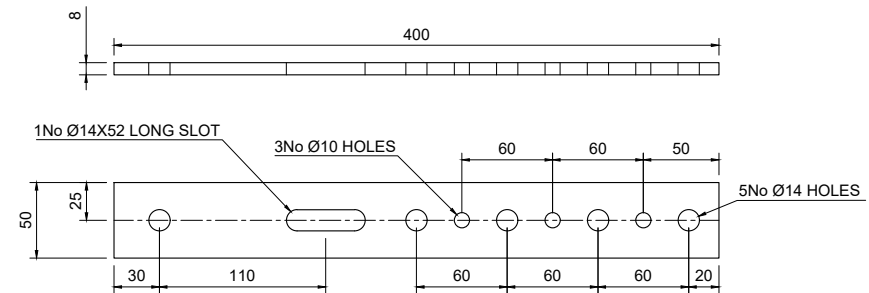


TPA-PD - 8mm THICK
Scale 1:5

Parts list for TPA-PD

Item	Part	Quantity	Part description	Length	Material	Weight
01	TPA-PD	1	Plate 400x50x8mm	N/A	S275J0	1.26 kg
02	U-BOLT	1	M12 U-BOLT FOR CHS 76.1mm	N/A	GRADE 8.8	-
Total Weight:						1.26 kg

- All steel hot dip galvanized
- Each U-BOLT to be supplied with 4 Full Nuts, 2 Flat Washers and 2 Spring Washers
- For fabrication notes see drawing 305

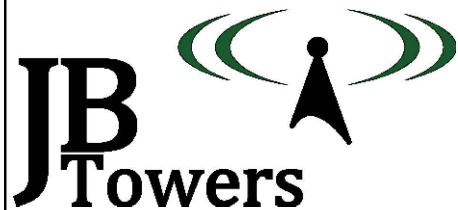

01	FIRST ISSUE	TT	24/06/19
REV	REV	BY	DATE
SCALE AS SHOWN WHEN PRINTED AT A3	DRAWN DATE	AM 24/06/19	CHECKED DATE
MP		APPROVED	JBT
DATE		DATE	DATE
ALL DIMENSIONS IN mm UNLESS OTHERWISE STATED. THIS DRAWING TO BE READ IN CONJUNCTION WITH OTHER RELEVANT DRAWINGS.			

TITLE
STEELWORK BRACKET;
POWER DIVIDER STRAP;
TYPICAL CHS DETAIL
PARTS: TPB-B; TPA-PD

SITE ADDRESS
INVEREWE GARDENS
POOLEWE
HIGHLAND
IV22 2LG

ARQIVA REF. 141370	DRG No. 301	REV 01
-----------------------	----------------	-----------

ALL SCALES AS SHOWN WHEN PRINTED AT A3



ALL SCALES AS SHOWN WHEN PRINTED AT A3

TPA-BR-1 - EA50x50x6
Scale 1:5

TPA-BR-2 - EA50x50x6
Scale 1:5

TPB-BR-3 - 10mm THICK
Scale 1:5

TPY-A - EA100x100x10
Scale 1:5

Parts list for TPY-A


Item	Part	Quantity	Part description	Length	Material	Weight
01	TPY-A	1	EA100x100x10	350mm	S275J0	5.25 kg
02	U-BOLT	2	M12 U-BOLT FOR CHS 25mm	N/A	GRADE 8.8	-
03	U-BOLT	2	M12 U-BOLT FOR CHS 76.1mm	N/A	GRADE 8.8	-
- All steel hot dip galvanized					Total Weight:	5.25 kg

- All steel hot dip galvanized
- Each STUD & U-BOLT to be supplied with 4 Full Nuts, 2 Flat Washers and 2 Spring Washers
- Each BOLT to be supplied with 1 Full Nut, 1 Form E FLat Washer and 1 Spring Washer
- For fabrication notes see drawing 305

Parts list for TPA-BR


Item	Part	Quantity	Part description	Length	Material	Weight
01	TPB-BR-1	1	EA 50x50x6	280mm	S275J0	1.25 kg
02	TPB-BR-2	1	EA 50x50x6	690mm	S275J0	3.09 kg
03	TPB-BR-3	1	130x190x10mm	N/A	S275J0	1.94 kg
04	BOLT	1	M12 SET BOLT - 30mm LONG	N/A	GRADE 8.8	-
05	N-BOLT	2	M12 N-BOLT FOR EA 50x50x6	N/A	GRADE 8.8	-
06	U-BOLT	2	M12 U-BOLT FOR CHS 76.1mm	N/A	GRADE 8.8	-
- All steel hot dip galvanized					Total Weight:	6.28 kg

- All steel hot dip galvanized
- Each BOLT to be supplied with 1 Full Nut, 1 Form E FLat Washer and 1 Spring Washer
- Each STUD & U-BOLT to be supplied with 4 Full Nuts, 2 Flat Washers and 2 Spring Washers
- For fabrication notes see drawing 305

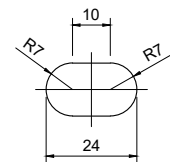

SLOTTED HOLE DETAIL
Scale 1:2

TYPICAL GUSSET PLATE DETAIL
Scale 1:2

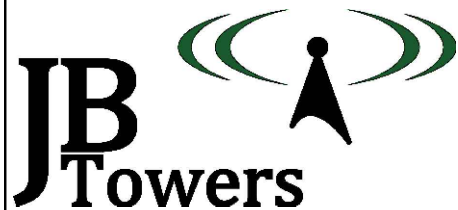

01	FIRST ISSUE		TT	24/06/19	
REV	REV		BY	DAT	
SCALE AS SHOWN WHEN PRINTED AT A3	DRAWN AM DATE 24/06/19	CHECKED MP DATE 24/06/19	APPROVED JB DATE 24/06/19		
ALL DIMENSIONS IN mm UNLESS OTHERWISE STATED. THIS DRAWING TO BE READ IN CONJUNCTION WITH OTHER RELEVANT DRAWINGS.					

19

E

T


9

TITLE	SITE ADDRESS		
BRACING KIT; YAGI MOUNT	INVEREWE GARDENS		
PARTS: TPA-BR;	POOLEWE		
TPY-A	HIGHLAND		
	IV22 2LG		
	ARQIVA REF. 141370	DRG No. 302	REV 01


ALL SCALES AS SHOWN WHEN PRINTED AT A3




ALL SCALES AS SHOWN WHEN PRINTED A1 A3

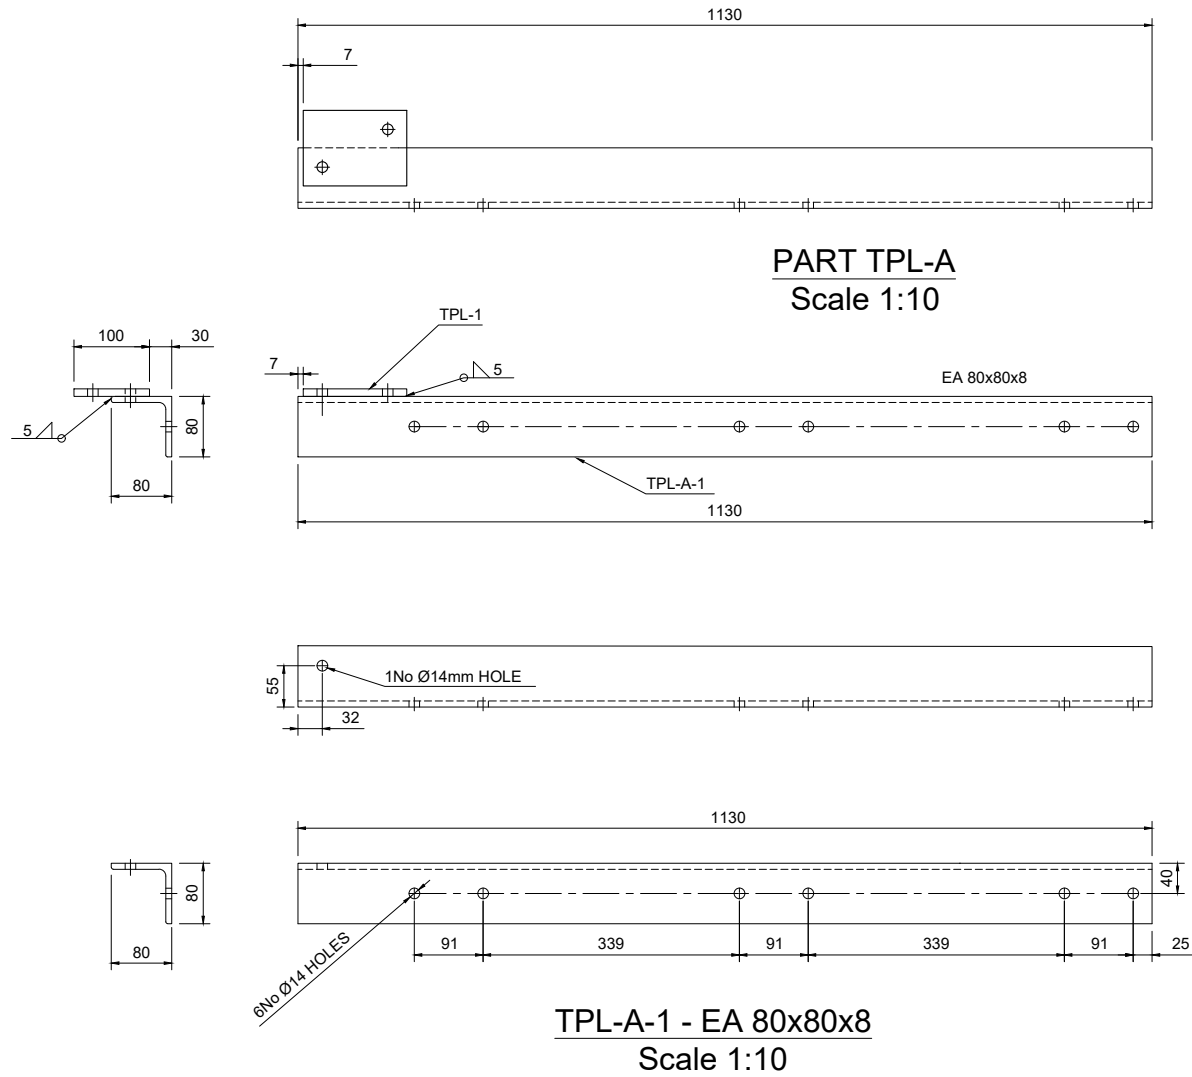


Parts list for TPL-A						
Item	Part	Quantity	Part description	Length	Material	Weight
01	TPL-A-1	1	EA 80x80x8	1130mm	S275J0	10.88 kg
02	TPL-1	1	Plate 137x100x10mm	N/A	S275J0	1.08 kg
03	U-BOLT	3	M12 U-BOLT FOR CHS 76.1mm	N/A	GRADE 8.8	-
Total Weight:						11.96 kg
- All steel hot dip galvanized - Each U-BOLT to be supplied with 4 Full Nuts, 2 Flat Washers and 2 Spring Washers - For fabrication notes see drawing 305						

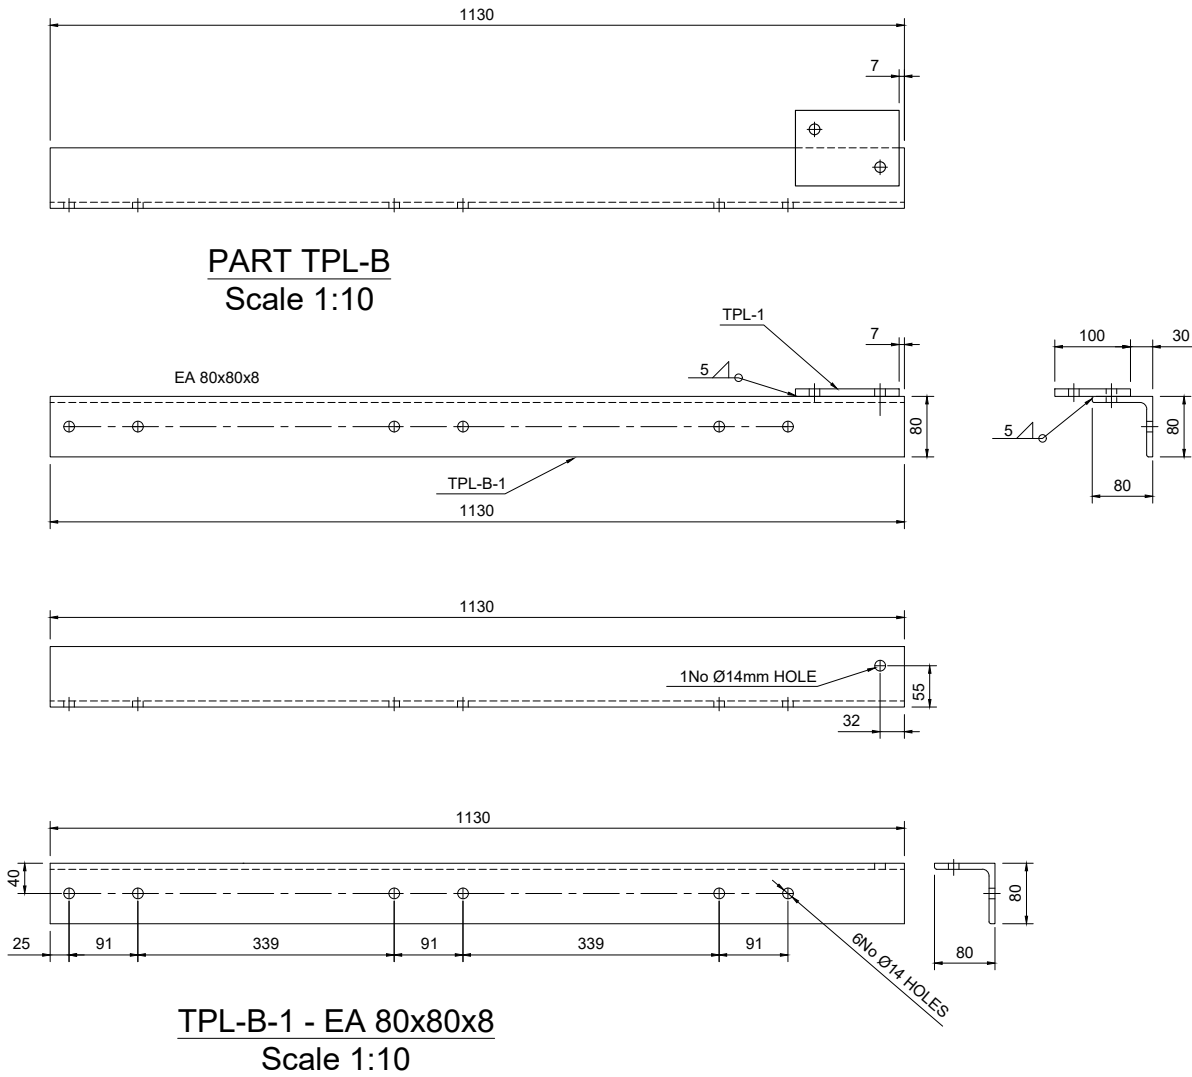

Parts list for TPL-B						
Item	Part	Quantity	Part description	Length	Material	Weight
01	TPL-B-1	1	EA 80x80x8	1130mm	S275J0	10.88 kg
02	TPL-1	1	Plate 137x100x10mm	N/A	S275J0	1.08 kg
03	U-BOLT	3	M12 U-BOLT FOR CHS 76.1mm	N/A	GRADE 8.8	-
Total Weight:						11.96 kg
- All steel hot dip galvanized - Each U-BOLT to be supplied with 4 Full Nuts, 2 Flat Washers and 2 Spring Washers - For fabrication notes see drawing 305						

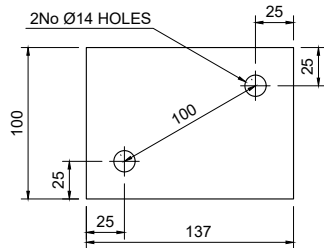

TPL-1 - 10mm THICK
Scale 1:5

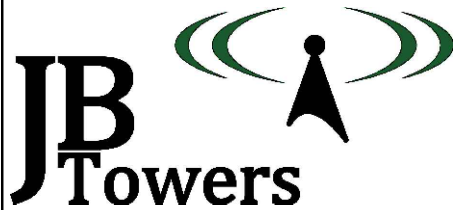

01	FIRST ISSUE	TT	24/06/19
REV	REV	BY	DATE
SCALE AS SHOWN WHEN PRINTED AT A3	DRAWN DATE 24/06/19	CHECKED DATE 24/06/19	APPROVED DATE 24/06/19
ALL DIMENSIONS IN mm UNLESS OTHERWISE STATED. THIS DRAWING TO BE READ IN CONJUNCTION WITH OTHER RELEVANT DRAWINGS.			

TITLE
LOG MOUNTING BRACKETS
PARTS: TPL-A; TPL-B


SITE ADDRESS
INVEREWE GARDENS
POOLEWE
HIGHLAND
IV22 2LG

ARQIVA REF.
141370
DRG No.
303
REV
01



ALL SCALES AS SHOWN WHEN PRINTED AT A3




ALL SCALES AS SHOWN WHEN PRINTED AT A3

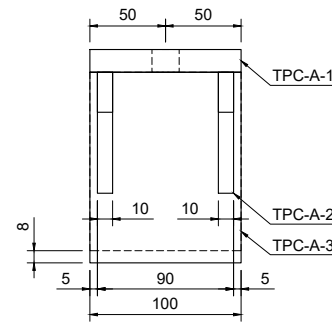


TPC-A
Scale 1:5

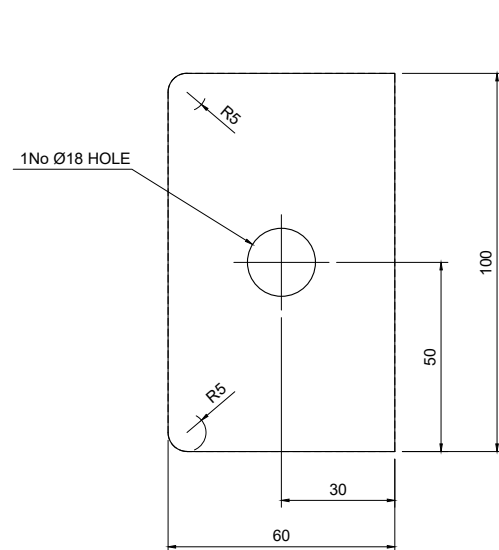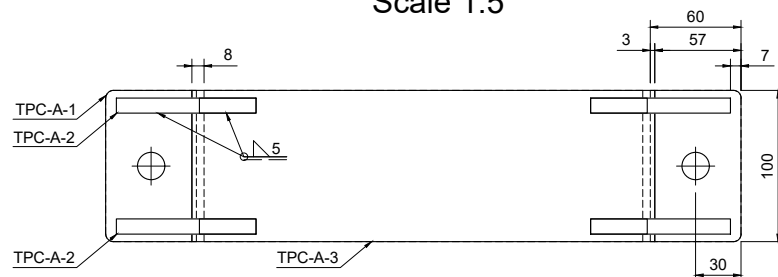

TPC-A-1 - 15mm THICK
Scale 1:2

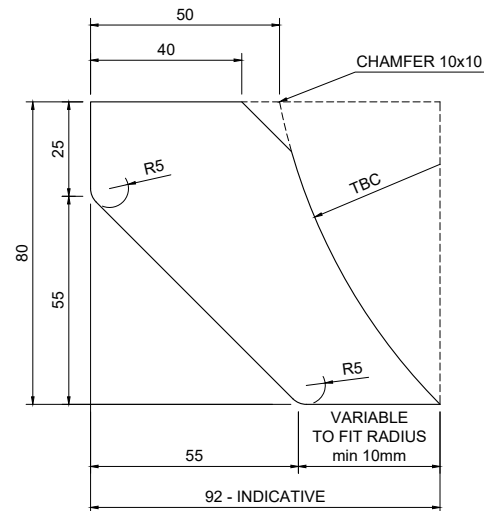


TPC-A-2 - 10mm THICK
Scale 1:2

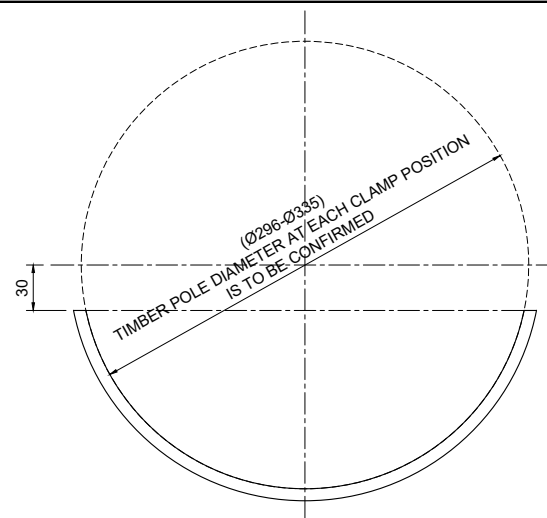

TPC-A-3 - 100x8mm PLATE
Scale 1:5

Item	Part	Quantity	Part description	Length	Material	Weight
01	TPC-A-1	4	PLATE 100x60x15mm	TBC	S275J0	0.71 kg
02	TPC-A-2	8	PLATE 80x50x10mm	N/A	S275J0	0.30 kg
03	TPC-A-3	2	PLATE 100mm WIDE & 8mm THICK	N/A	S275J0	3.00 kg
04	NUT	2	M16 - HALF NUT	N/A	GRADE 8.8	-
05	BOLT	2	M16 100mm LONG SET BOLT	N/A	GRADE 8.8	-


Total Weight:

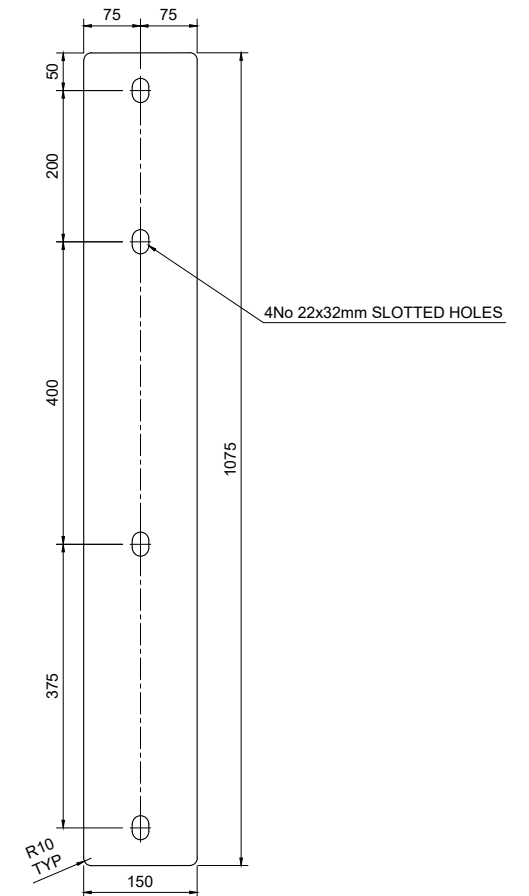

TPC-B - 15mm THICK
Scale 1:10

Item	Part	Quantity	Part description	Length	Material	Weight
01	TPC-B	2	PLATE 1075x150x15mm	N/A	S275J0	19.00 kg
02	STUD	4	M20 STUD	500mm	GRADE 8.8	1.25 kg
03	SQ-WSH	6	M20 50x50x3mm SQUARE WASHER	N/A	GRADE 8.8	-

Total Weight:	
---------------	--

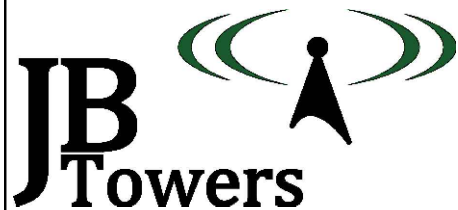

02	TPC-B ADDED			AM	15/07/19
01	FIRST ISSUE			AM	24/06/19
REV	REV			BY	DAT
SCALE AS SHOWN WHEN PRINTED AT A3		DRAWN AM DATE 24/06/19	CHECKED MP DATE 24/06/19	APPROVED JB DATE 24/06/19	
ALL DIMENSIONS IN mm UNLESS OTHERWISE STATED. THIS DRAWING TO BE READ IN CONJUNCTION WITH OTHER RELEVANT DRAWINGS.					

SPLICE COLLAR; INTERFACE
PLATES

PARTS: TPC-A; TPC-B

INVERWE GARDENS
POOLEWE
HIGHLAND
IV22 2LG

ARQIVA REF.
141370

DRG No.
304

ALL SCALES AS SHOWN WHEN PRINTED AT A3



ALL SCALES AS SHOWN WHEN PRINTED AT A3


NOTE:
2No. EXTENDED WIRE GUIDES - PART NO. 35397-00
4No. REGULAR WIRE GUIDES - PART NO. 30050-00

Item	Part	Drawing	Quantity	Part description	Length	Material	Weight
01	01	200	1	3 MAN LATCHWAY SYSTEM & *6No. WIRE GUIDES FOR FACE MOUNTED MONOPOLE (see notes)	17000	N/A	-
02	TPB-C	300	2	FALL ARREST ATTACHMENT POINT	N/A	S275J0	4.48 kg
03	03	200	46	PERMANENT BT STEP c/w 3No 10x75mm ZINC-PLATED COACH SCREWS	N/A	S275J0	13.80 kg
04	TPS-R	300	9	'MonoStep' ASSEMBLY	N/A	S275J0	25.65 kg
05	TPB-B	301	6	MOUNTING BRACKET	N/A	S275J0	66.12 kg
06	06	203	3	CHS 76.1x5mm	3200mm	S355J2H	84.19 kg
07	TPL-A	303	4	LOG MOUNTING BRACKET	1130mm	S275J0	47.84 kg
08	TPL-B	303	4	LOG MOUNTING BRACKET	1130mm	S275J0	47.84 kg
09	09	203	36	M12 WASHER	N/A	GRADE 8.8	-
10	TPA-PD	301	8	POWER DIVIDER STRAP	N/A	S275J0	10.08 kg
11	11	204	2	CHS 76.1x5mm	2000mm	S355J2H	35.08 kg
12	TPY-A	302	2	YAGI MOUNTING BRACKET	350mm	S275J0	10.50 kg
13	TPA-BR	302	2	BRACING KIT	N/A	S275J0	12.56 kg
14	14	200	1	FEEDER COVER - 2/CG/100	3500mm	UV RESISTANT PLASTIC	-
15	15	200	17	FEEDER CLAMP - 2/FCD/028	N/A	POLYPROPYLENE	-
16	16	200	17	M10 SCREW DOWELS WTH M10 NUT	100mm	STAINLESS STEEL	-
17	17	200	1	PoleSaver	750mm	N/A	-
18	18	200	9	M12 STUD + 4No NUTS + 2No FLAT WASHERS + 1No Ø50mm WASHER (FOR FALL ARREST SYSTEM)	500mm	GRADE 8.8	4.00 kg
19	TPC-A	304	6	TIMBER POLE SPLICE COLLAR	N/A	S275J0	67.44 kg
20	TPC-B	304	2	TIMBER POLE SPLICE INTERFACE PLATE	N/A	S275J0	86.00 kg
21	21	205	1	M20 STUD C/W 4No NUTS & 2No SQ WSH	450mm	GRADE 8.8	1.11 kg
Total Weight:							516.70 kg

- All steel hot dip galvanized
- All U-BOLTS to be FLA supply, each Supplied with 4 Full Nuts, 2 Flat Washers and 2 Spring Washers

NOTES:

1. WELDING TO BE IN ACCORDANCE WITH BS EN 1011-1:2009
2. LINEAR DIMS TO BE WITHIN ±1mm;
3. ANGULAR TOLERANCES TO BE WITHIN 0.5°
4. WELDING SYMBOLS ARE IN ACCORDANCE WITH BS EN 22553:1995
5. ALL PROFILE EDGES TO BE DRESSED AND SHARP CORNERS REMOVED
6. ALL WELD SIZES ARE FINAL SIZES
7. ALL WELDED JOINTS ARE TO BE PICKLE TIGHT
8. ALL STEELWORK TO BE BS EN 10025 GRADE S275 J0 UNO
9. HOT DIPPED GALVANISED TO BS EN ISO 1461. (ALL HOLLOW SECTIONS TO BE GRADE S355 J0H)
10. ALL STEEL IS TO BE SUPPLIED IN ACCORDANCE WITH EN 1090 TO EXECUTION CLASS 2
11. ALL NON PRE-LOADED BOLTS TO BE COMPLIANT STRUCTURAL BOLTS TO BS EN ISO 15048 PARTS 1&2.
12. STEELWORK COMPONENTS SHALL BE HOT DIP GALVANISED TO ACHIEVE A "VERY HIGH" DURABILITY FOR AN ENVIRONMENT CATEGORY CODE C4 FROM TABLE 1 IN BS EN ISO 14713
13. BOLTS AND NUTS SHALL BE SUPPLIED IN ACCORDANCE WITH BS 7371, SPUN GALVANISED IN ACCORDANCE WITH ISO 10684, THE NUTS RE-TAPPED AFTER GALVANISING, AND THE THREADS TREATED WITH GREASE.
14. ALL BOLTS TO BE CUT ON SITE TO EXTEND MAX 10mm BEYOND THE NUT WHEN TIGHTENED UNO.
15. ALL SITE DRILLED HOLE/CUT ENDS TO BE TREATED WITH METAFLUX 70-40 ZINC PASTE FOLLOWED BY 1 COAT OF 7-42 ZINC ALU OR 70-16 ALUMINIUM SPRAY

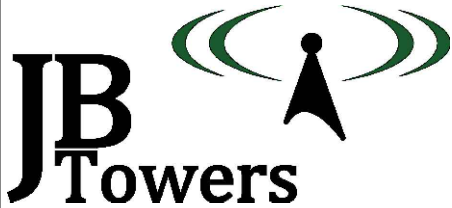

03	WIRE GUIDES INFORMATION ADDED	AM	17/07/19
02	PARTS LIST UPDATED	AM	15/07/19
01	FIRST ISSUE	TT	24/06/19
REV	REV	BY	DATE
SCALE AS SHOWN WHEN PRINTED AT A3	DRAWN AM DATE 24/06/19	CHECKED MP DATE 24/06/19	APPROVED JBT DATE 24/06/19
ALL DIMENSIONS IN mm UNLESS OTHERWISE STATED. THIS DRAWING TO BE READ IN CONJUNCTION WITH OTHER RELEVANT DRAWINGS.			


TITLE
PARTS LIST

SITE ADDRESS		
INVEREWE GARDENS POOLEWE HIGHLAND IV22 2LG		
ARQIVA REF. 141370	DRG No. 305	REV 03

ALL SCALES AS SHOWN WHEN PRINTED AT A3




ALL SCALES AS SHOWN WHEN PRINTED AT A3

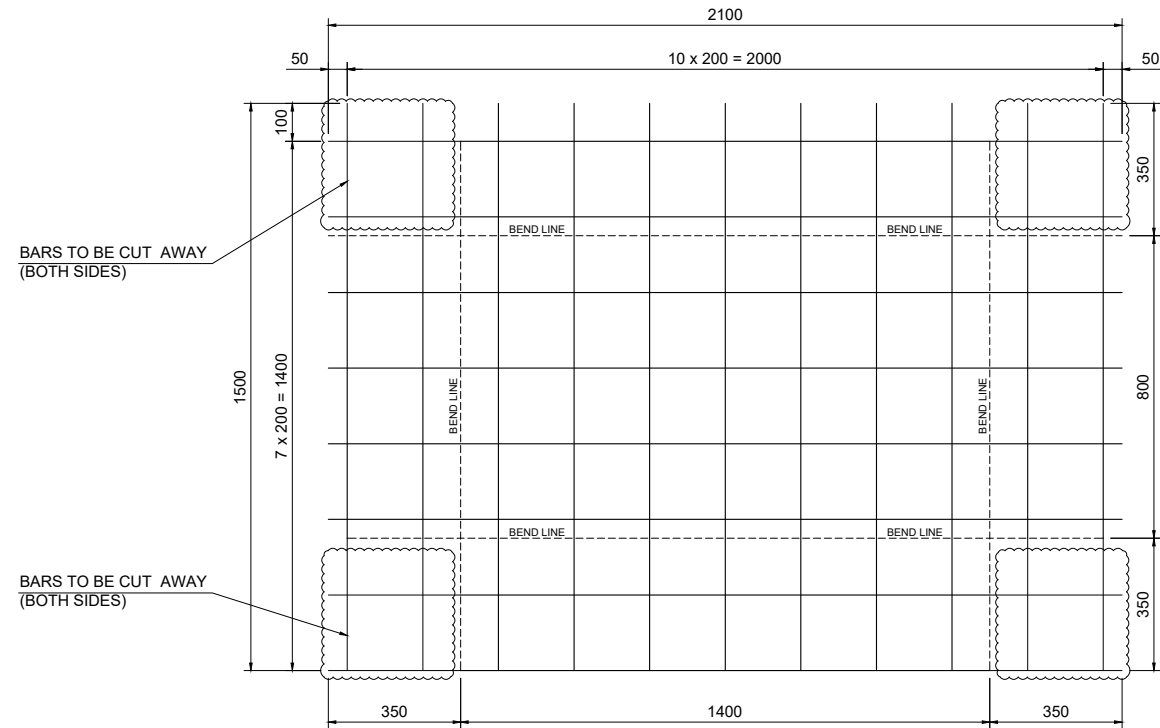

01- A252 MESH
1500x2100mm
Scale 1:20

BAR BENDING SCHEDULE IN ACCORDANCE WITH BS 8666											
BAR MARK	TYPE AND SIZE	NO. OF MBRs	NO. OF BARS IN EACH	TOTAL NO.	LENGTH OF EACH BAR	SHAPE CODE	A mm	B mm	C mm	D mm	E mm
01	A252	01	04	04	-	99					
02	T8	01	16	16	-	01	850				

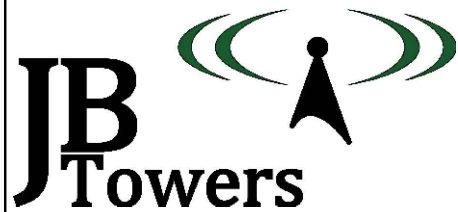

01	FIRST ISSUE	AM	16/07/19
REV	REV	BY	DATE
SCALE AS SHOWN WHEN PRINTED AT A3	DRAWN AM	CHECKED MP	APPROVED JBT
DATE 16/07/19	DATE 16/07/19	DATE 16/07/19	DATE 16/07/19
ALL DIMENSIONS IN mm UNLESS OTHERWISE STATED. THIS DRAWING TO BE READ IN CONJUNCTION WITH OTHER RELEVANT DRAWINGS.			

TITLE		SITE ADDRESS	
BAR BENDING SCHEDULE		INVEREWE GARDENS POOLEWE HIGHLAND IV22 2LG	
ARQIVA REF. 141370		DRG No. 401	REV 01

