

ALL SCALES AS SHOWN WHEN PRINTED AT A3



ALL SCALES AS SHOWN WHEN PRINTED AT A3

ACCESS SYSTEM DETAIL Scale 1:50

LATCHWAY SAFETY SYSTEM DETAIL Scale 1:50

- PLANTING**
1. CAT SCANNER IS TO BE USED IN ORDER TO CONFIRM THE POSITIONS OF BURIED SERVICES.
 2. Perma-Soil Stabiliser OR A SIMILAR APPROVED SHOULD BE USED IN ACCORDANCE WITH THE MANUFACTURERS RECOMMENDATION.
 3. ANY MATERIAL USED FOR BACK-FILLING IS TO BE OF EQUAL OR BETTER QUALITY THAN THE EXCAVATED MATERIAL.
 4. ALL BACK-FILLING MATERIAL IS TO BE PLACED AND COMPACTED IN 150mm THICK LAYERS.
 5. TIMBER POLE TO BE PLANTED WITH N8S MARKING AT 4m FROM BUT FACING 78° FROM NORTH (CLOCKWISE)

- NOTES**
1. SEE DRAWING 304 FOR PARTS LIST
 2. ALL BOLTS TO BE CUT ON SITE TO EXTEND MAX 10mm BEYOND THE NUT WHEN TIGHTENED UNO.
 3. ALL SITE DRILLED HOLE/CUT ENDS TO BE TREATED WITH METAFIX 70-40 ZINC PASTE FOLLOWED BY 1 COAT OF 7-42 ZINC ALU OR 70-16 ALUMINIUM SPRAY
 1. POLE TO BE SUPPLIED IN ACCORDANCE WITH BS EN 14229 & SHALL HAVE FAN CHARACTERISTIC BEIDING STRENGTH OF 30kN/m² & MIN. YOUNGS MODULUS (PARALLEL TO GRAIN) OF 10kN/mm².
 2. MARKINGS ON FINISHED POLE SHALL BE AT 4m FROM BUT AND COMPLY WITH BS EN 14229 UNO
 3. AS FAR AS PRACTICABLE ALL CUTTING, SCARPING & DRILLING TO BE DONE BEFORE CREOSOTING. IF BE COATED WITH A MIXTURE OF CREOSOTE & TAR.
 4. POLE TO BE PRESSURE IMPREGNATED WITH CREOSOTE IN ACCORDANCE WITH BS EN 14229
 5. MINIMUM DIAMETERS
BOTTOM - Ø425mm
TOP - Ø206mm
 6. 19.5m LONG POLE TO BE SOURCED BY TRIMMING 20m LONG POLE BY 0.5m AT THE TOP

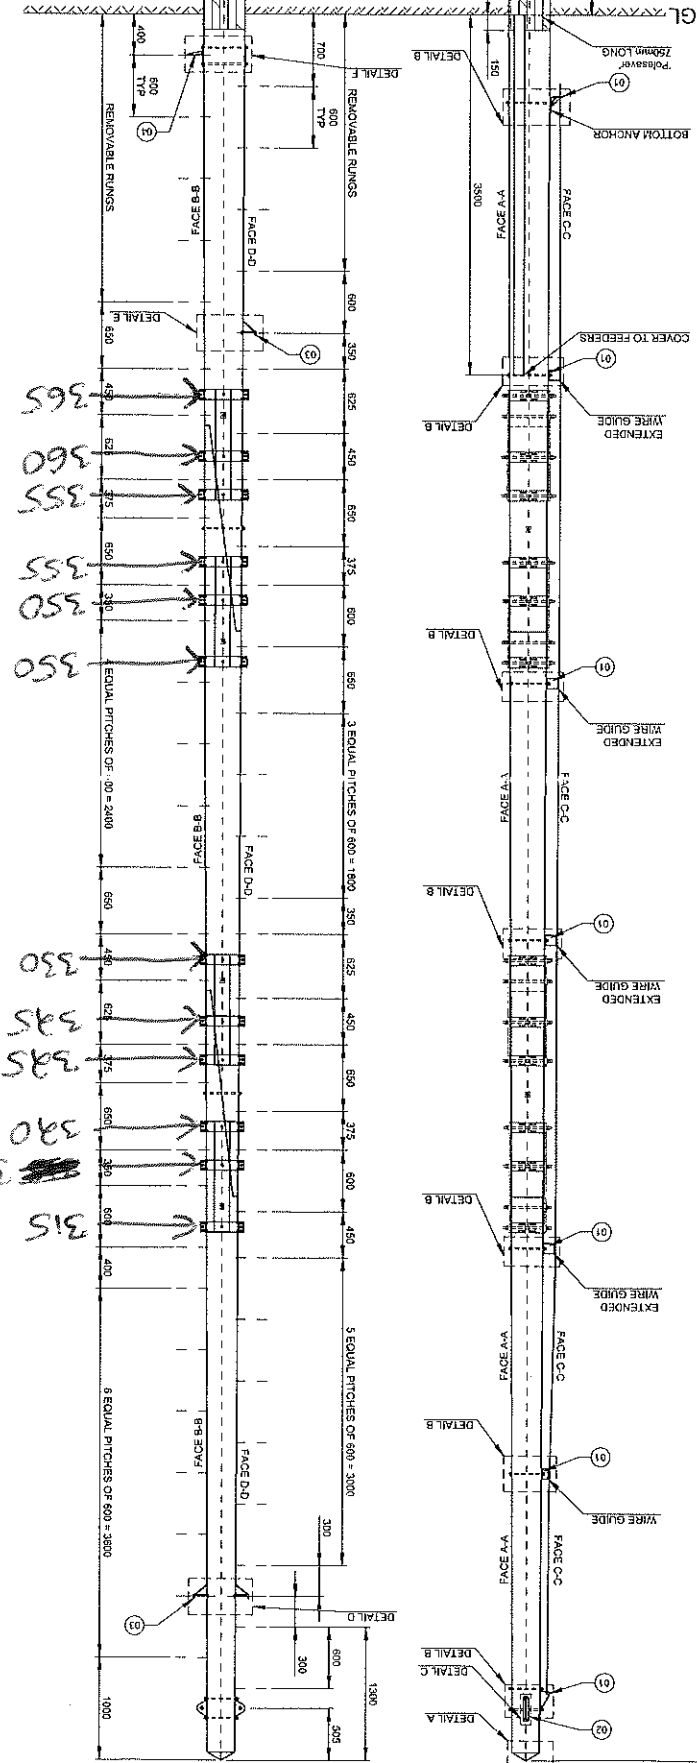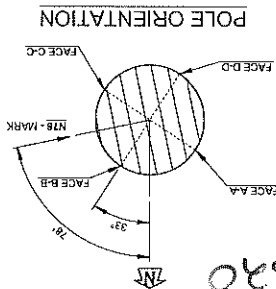

REV	02
ORG	200
ARCIVA REF	141568
SITE ADDRESS	
VALENTINE FARM	
SHOGMOOR LANE	
SKIRMETT	
HENLEY-ON-THAMES	
RG9 6TD	

TITLE	
SKIRMETT	
GENERAL ARRANGEMENT	
SHEET 1 OF 3	

SCALE	AS SHOWN	DRAWN	AM	CHECKED	MP	APPROVED	JBT
DATE	19/11/18	DATE	19/11/18	DATE	19/11/18	DATE	19/11/18
ALL DIMENSIONS IN mm UNLESS OTHERWISE STATED.							
THIS DRAWING TO BE READ IN CONJUNCTION WITH OTHER RELEVANT DRAWINGS.							

