
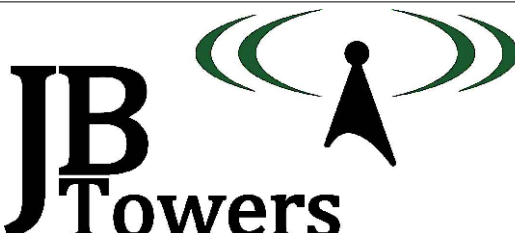
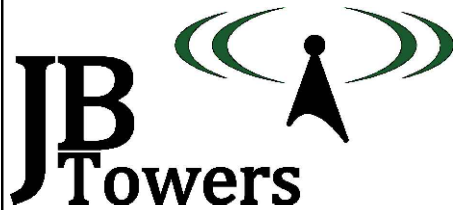
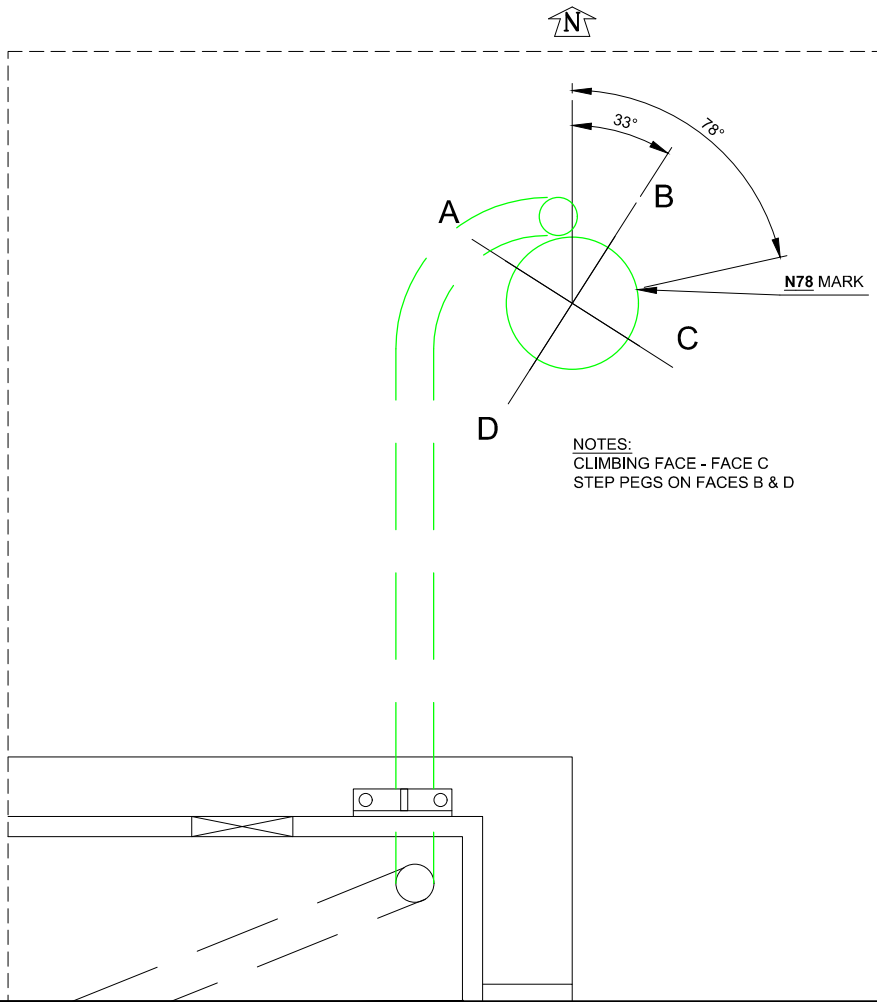


DRAWING ISSUE SHEET

SITE NAME		SKIRMETT																		
SITE REFERENCE		141568-01-JBT																		
CONSULTANT		JB TOWERS																		
CONSULTANT TEL		01684 628040																		
				DATE ISSUED	19/11/18	24/04/19	08/05/19	13/01/21												
DRAWING NUMBER	ARCHIVE DOCUMENT PRODUCED			FILE FORMAT	Rev No.	Rev No.	Rev No.	Rev No.												
141568-01-JBT-100	SITE PLAN			PDF	01	01	02	02												
141568-01-JBT-200	GENERAL ARRANGEMENT SHEET 1 OF 3			PDF	01	01	01	02												
141568-01-JBT-200	GENERAL ARRANGEMENT SHEET 2 OF 3			PDF	01	02	02	03												
141568-01-JBT-200	GENERAL ARRANGEMENT SHEET 3 OF 3			PDF	01	01	01	01												
141568-01-JBT-201	TIMBER POLE HOLE SET OUT SHEET 1 OF 2			PDF	01	01	01	02												
141568-01-JBT-201	TIMBER POLE HOLE SET OUT SHEET 2 OF 2			PDF	01	01	01	01												
141568-01-JBT-202	TIMBER POLE CUT OUT DETAIL			PDF	01	01	01	01												
141568-01-JBT-203	ANTENNA MOUNT DETAIL G			PDF	01	02	03	03												
141568-01-JBT-204	ANTENNA MOUNT DETAIL H			PDF	01	01	01	02												
141568-01-JBT-205	TIMBER POLE SPLICE DETAIL I			PDF	-	-	-	01												
141568-01-JBT-300	ATTACHMENT POINT & TEMPORARY STEP DETAILS			PDF	01	01	01	01												
141568-01-JBT-301	ANTENNA MOUNTING BRACKET & TYP CHS DETAIL			PDF	01	02	02	02												
141568-01-JBT-302	ANTENNA MOUNTING BRACKETS			PDF	01	01	01	01												
141568-01-JBT-303	LOG AND VSAT DISH MOUNTING BRACKETS			PDF	01	01	02	03												
141568-01-JBT-304	PARTS LIST			PDF	01	01	02	03												
141568-01-JBT-305	SPLICE COLLAR; INTERFACE PLATE			PDF	-	-	-	01												
141568-01-JBT-400	TIMBER POLE FOUNDATION DETAILS			PDF	-	-	-	01												
141568-01-JBT-401	PERMANENT STEPS ENLARGED DETAIL			PDF	-	-	-	01												
CHECKED					MP	MP	MP	MP												
APPROVED					JBT	JBT	JBT	JBT												
NAME	COMPANY ISSUE TO				QUANTITY	QUANTITY	QUANTITY	QUANTITY												
Jonathan Harrison	AXD				1	1	1	1												
STATUS																				
PR = PRELIMINARY PL = PLANNING T = TENDER C = CONSTRUCTION AB = AS-BUILT					C	C	C	C												
ACCEPTABLE FORMS OF ISSUE																				
H = HARD COPY E = E-MAIL FT = FILE TRANSFER PROTOCOL					E	E	E	E												

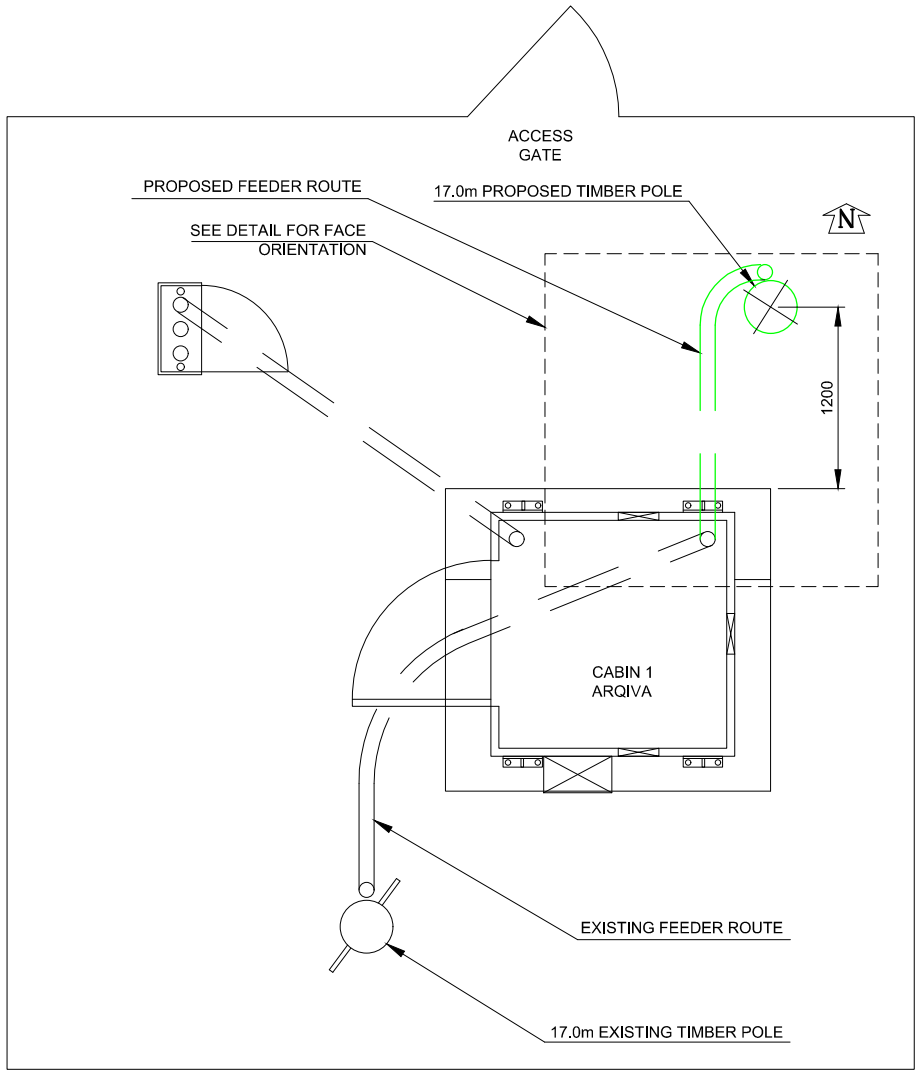

02	PROPOSED POLE POSITION UPDATED			AM	08/05/19
01	FIRST ISSUE			AM	19/11/18
REV	REV			BY	DATE
SCALE AS SHOWN		DRAWN	AM	CHECKED	MP
WHEN PRINTED AT A3		DATE	19/11/18	DATE	19/11/18
APPROVED JBT					
ALL DIMENSIONS IN mm UNLESS OTHERWISE STATED. THIS DRAWING TO BE READ IN CONJUNCTION WITH OTHER RELEVANT DRAWINGS.					

TITLE
SKIRMETT
SITE PLAN

SITE ADDRESS
VALENTINE FARM
SHOGMOOR LANE
SKIRMETT
HENLEY-ON-THAMES
RG9 6TD

ARQIVA REF.
141568


DRG No.
100

REV
02

ALL SCALES AS SHOWN WHEN PRINTED AT A3



ALL SCALES AS SHOWN WHEN PRINTED AT A3

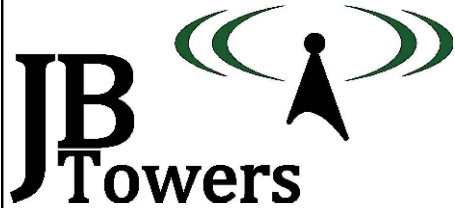

02	SPICES ADDED			MI	13/01/21
01	FIRST ISSUE			AM	19/11/18
REV	REV			BY	DATE
SCALE AS SHOWN		DRAWN	AM	CHECKED	MP
WHEN PRINTED AT A3		DATE	19/11/18	DATE	19/11/18
		APPROVED	JBT	DATE	19/11/18
ALL DIMENSIONS IN mm UNLESS OTHERWISE STATED. THIS DRAWING TO BE READ IN CONJUNCTION WITH OTHER RELEVANT DRAWINGS.					

TITLE

SKIRMETT

GENERAL ARRANGEMENT

SHEET 1 OF 3

SITE ADDRESS

VALENTINE FARM

SHOGMOOR LANE

SKIRMETT

HENLEY-ON-THAMES

RG9 6TD

ARQIVA REF.


141568

DRG No.

200


REV

02

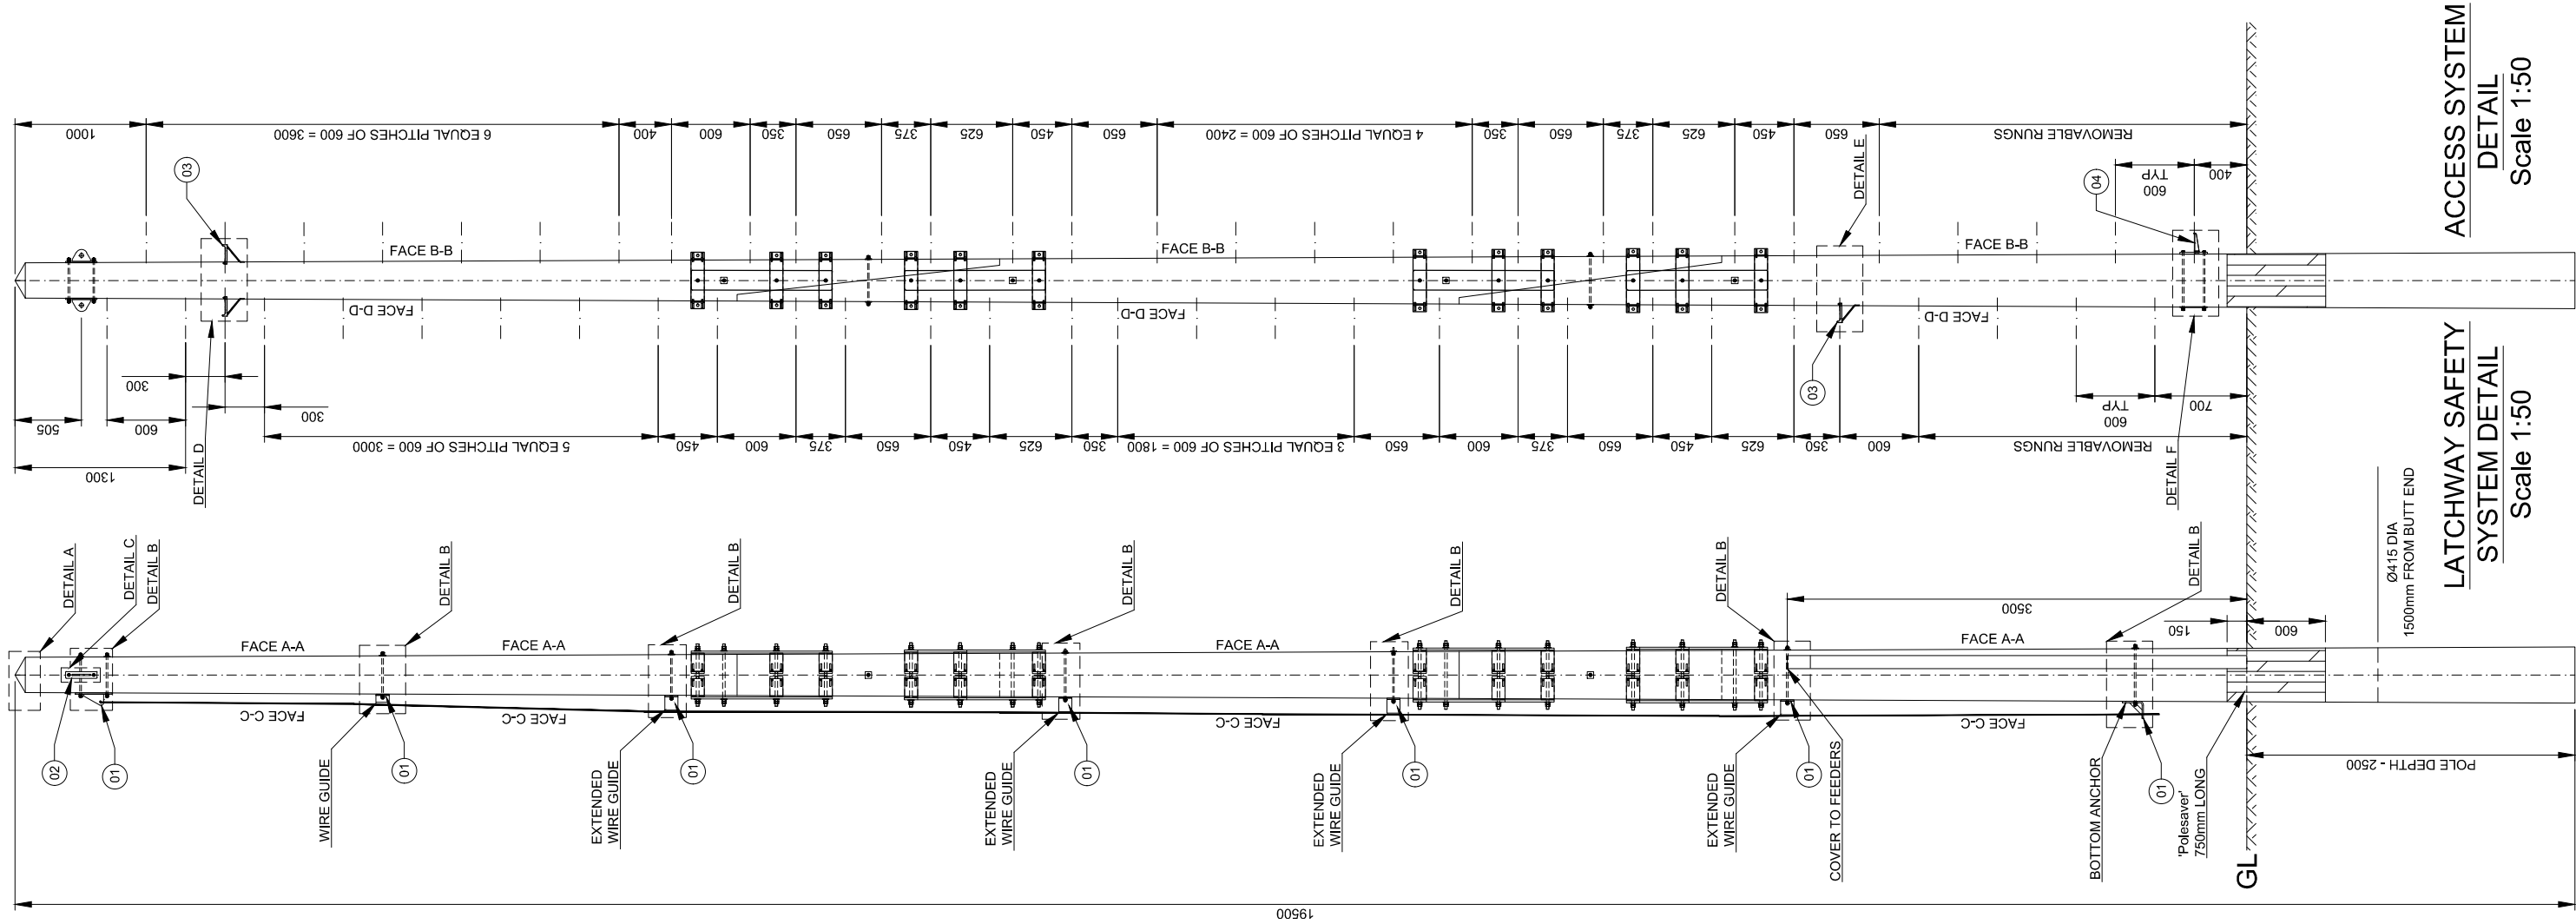

LATCHWAY SAFETY
SYSTEM DETAIL
Scale 1:50

ACCESS SYSTEM
DETAIL
Scale 1:50

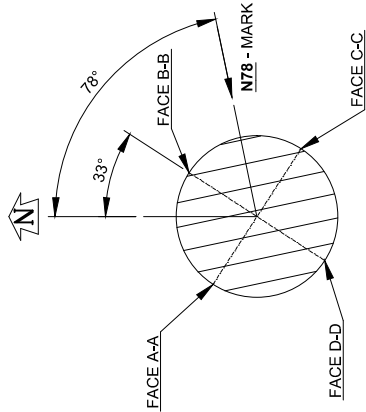

POLE ORIENTATION

NOTES


- SEE DRAWING 304 FOR PARTS LIST
- ALL BOLTS TO BE CUT ON SITE TO EXTEND MAX 10mm BEYOND THE NUT WHEN TIGHTENED UNO.
- ALL SITE DRILLED HOLE/CUT ENDS TO BE TREATED WITH METAFUX 70-40 ZINC PASTE FOLLOWED BY 1 COAT OF 7-42 ZINC ALU OR 70-16 ALUMINIUM SPRAY

TIMBER POLE

- POLE TO BE SUPPLIED IN ACCORDANCE WITH BS EN14229 & SHALL HAVE MIN. CHARACTERISTIC BENDING STRENGTH OF 30N/mm² & MIN. YOUNGS MODULUS (PARALLEL TO GRAIN) OF 10kN/mm².
- MARKINGS ON FINISHED POLE SHALL BE AT 4m FROM BUT AND COMPLY WITH BS EN 14229 UNO
- AS FAR AS PRACTICABLE ALL CUTTING, SCARFING & DRILLING TO BE DONE BEFORE CREOSOTING. IF NOT ALL CUT, DRILLED & SCARFED SURFACES TO BE COATED WITH A MIXTURE OF CREOSOTE & TAR.
- POLE TO BE PRESSURE IMPREGNATED WITH CREOSOTE IN ACCORDANCE WITH BS EN 14229
- MINIMUM DIAMETERS
TOP - Ø206mm
BOTTOM - Ø425mm
- 19.5m LONG POLE TO BE SOURCED BY TRIMMING 20m LONG POLE BY 0.5m AT THE TOP

PLANTING

- CAT SCANNER IS TO BE USED IN ORDER TO CONFIRM THE POSITIONS OF BURIED SERVICES.
- 'Perma-Soil Stabiliser' OR A SIMILAR APPROVED SHOULD BE USED IN ACCORDANCE WITH THE MANUFACTURER'S RECOMMENDATION.
- ANY MATERIAL USED FOR BACK-FILLING IS TO BE OF EQUAL OR BETTER QUALITY THAN THE EXCAVATED MATERIAL.
- ALL BACK-FILLING MATERIAL IS TO BE PLACED AND COMPACTED IN 150mm THICK LAYERS.
- TIMBER POLE TO BE PLANTED WITH N78 MARKING AT 4m FROM BUT FACING 78° FROM NORTH (CLOCKWISE)

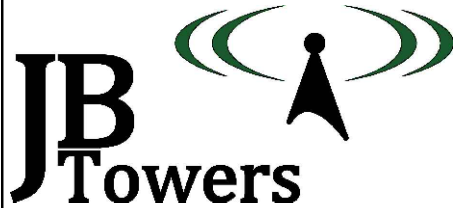

03	DETAIL H UPDATED			MI	13/01/21
02	POWER DIVIDER POSITION UPDATED			TT	24/04/19
01	FIRST ISSUE			AM	19/11/18
REV	REV			BY	DATE
SCALE AS SHOWN		DRAWN	AM	CHECKED	MP
WHEN PRINTED AT A3		DATE	19/11/18	DATE	19/11/18
ALL DIMENSIONS IN mm UNLESS OTHERWISE STATED. THIS DRAWING TO BE READ IN CONJUNCTION WITH OTHER RELEVANT DRAWINGS.					

TITLE

SKIRMETT

GENERAL ARRANGEMENT

SHEET 2 OF 3

SITE ADDRESS

VALENTINE FARM

SHOGMOOR LANE

SKIRMETT

HENLEY-ON-THAMES

RG9 6TD

ARQIVA REF.





141568

DRG No.

200

REV

03

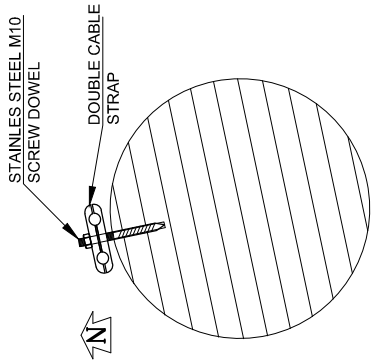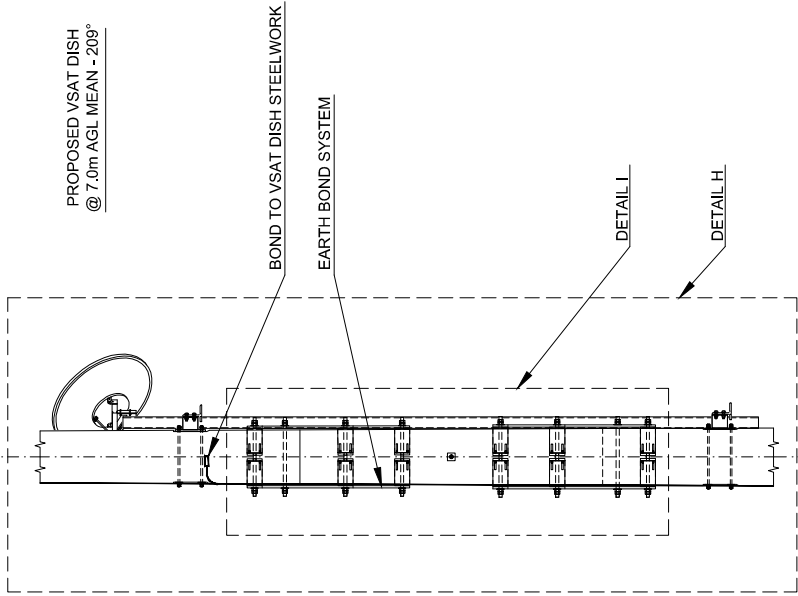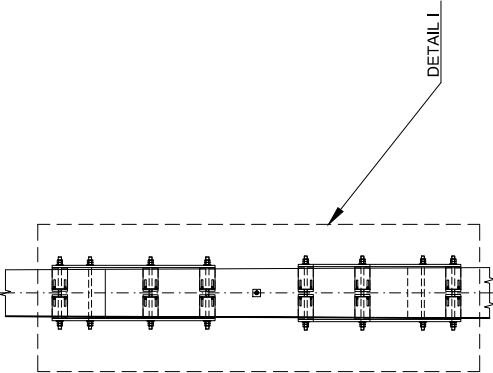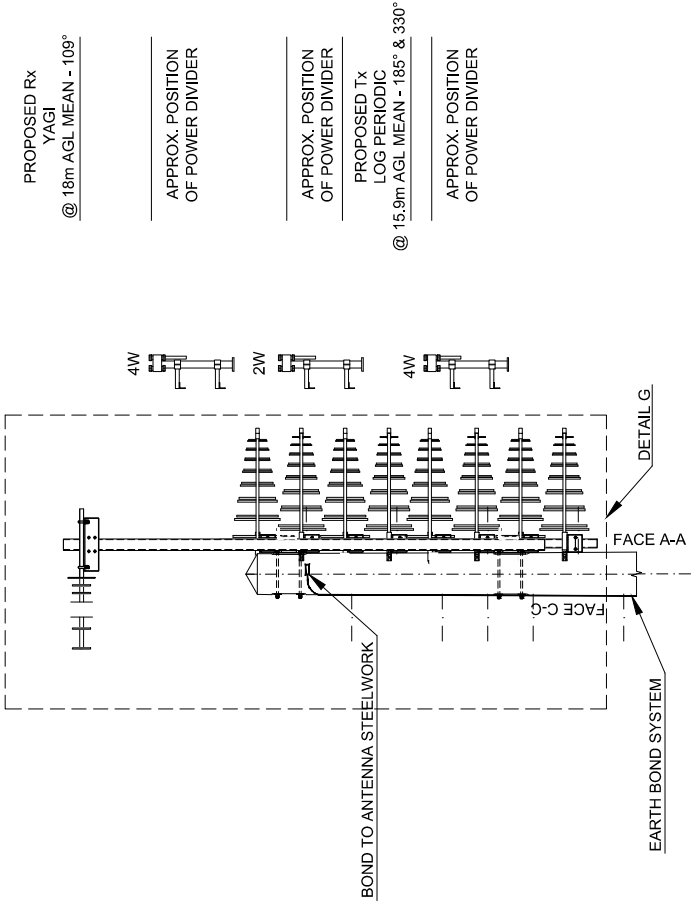

NOTES


1. AS FAR AS IS PRACTICABLE ALL CUTTING SCARFING AND DRILLING TO BE DONE BEFORE CREOSOTING. WHERE THIS IS NOT POSSIBLE ALL CUT, DRILLED, AND SCARFED SURFACES TO BE COATED WITH A MIXTURE OF CREOSOTE AND TAR

FEEDERS

1. SUPPLY OF FEEDERS BY OTHERS LCF78-50 TO TX ANTENNA & LCF12-50 TO RX ANTENNA
2. FEEDERS FIXED AT 1000mm CENTRES


EARTHING

1. CONNECT EARTH BOND TO NEW EARTHING SYSTEM
2. MAXIMUM VALUE FOR GROUND RESISTANCE TO BE 10 OHMS
3. CABLE OR TAPE TO BE FIXED TO POLE AT 1000mm CENTRES
4. EARTHING SHOULD COMPLY WITH ARQIVA'S DOCUMENT BOS147

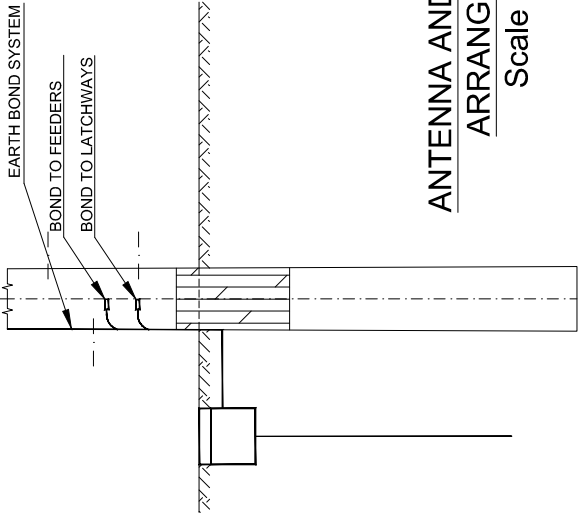


ALL SCALES AS SHOWN WHEN PRINTED AT A3

ALL SCALES AS SHOWN WHEN PRINTED AT A3

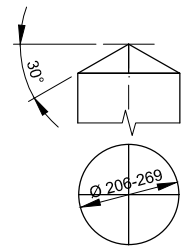


- NOTES:
1. A SINGLE COAT OF TIMBER COMPATIBLE BITUMINOUS PAINT (E.G. BIRD BRAND BLACK BITUMINOUS PAINT OR SIMILAR APPROVED PRODUCT) TO BE APPLIED TO THE UPPER SURFACES AT THE TOP OF THE POLE.
 2. PAINT TO BE APPLIED ON SITE JUST BEFORE ERECTION
- FORM: 4 WAY PYRAMID / CONE


DETAIL A - TIMBER POLE TOP
Scale 1:20

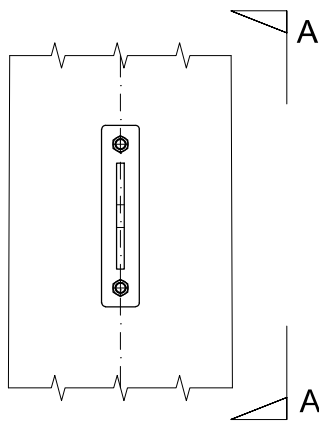


DETAIL C - FALL ARREST
ATTACHMENT POINT
Scale 1:10

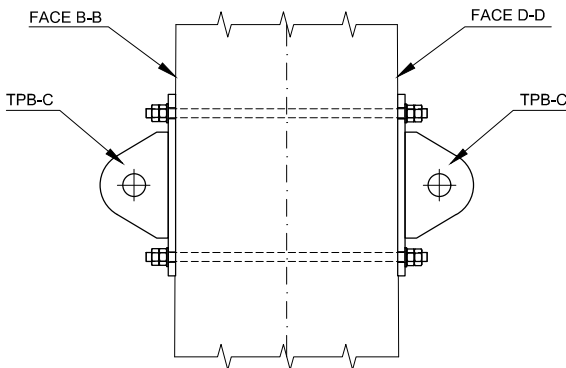

VIEW A-A
Scale 1:10

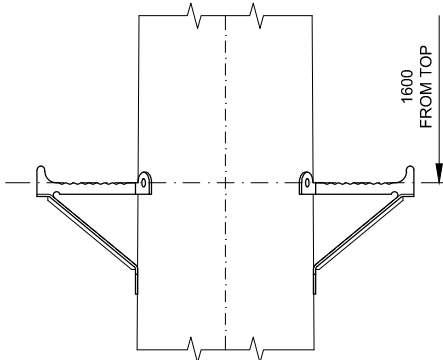


DETAIL D - ANTENNA
ACCESS CLIMBING STEP
Scale 1:10

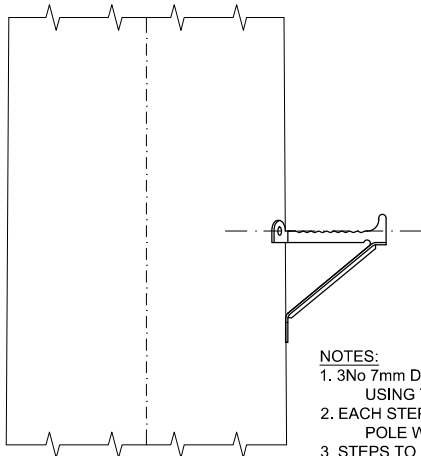


- NOTES:
1. 3No 7mm DIA 70mm LONG PILOT HOLES TO BE DRILLED USING THE STEP AS A TEMPLATE
 2. EACH STEP SHOULD BE FIXED TO THE TIMBER POLE WITH 3No 10mm COACH SCREWS 75mm LONG
 3. STEPS TO BE INSTALLED ON FACES B-B & D-D ONLY


DETAIL E - PERMANENT
CLIMBING STEPS
Scale 1:10

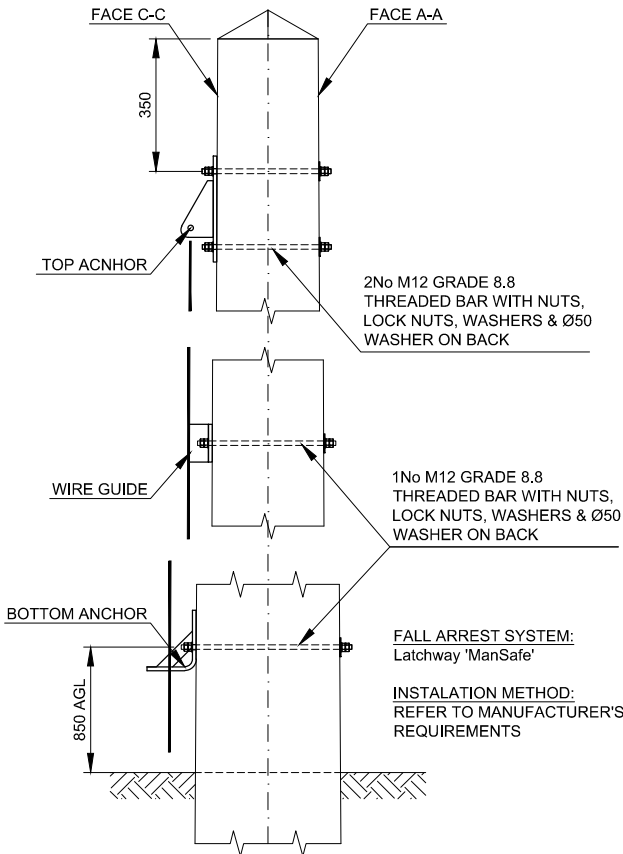

DETAIL B - FALL ARREST SYSTEM
Scale 1:20

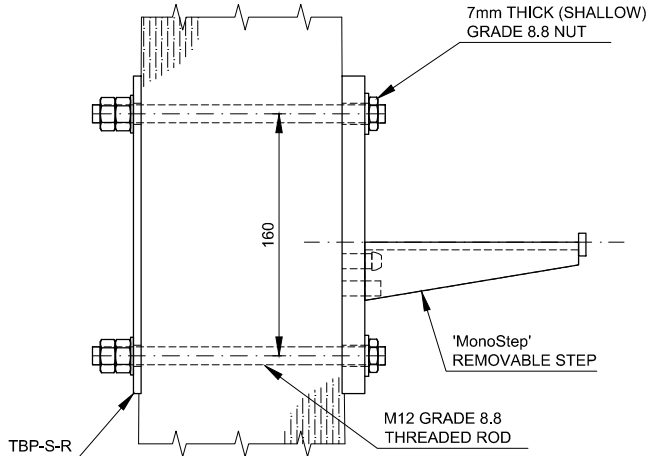

DETAIL F - REMOVABLE
CLIMBING STEPS
Scale 1:5

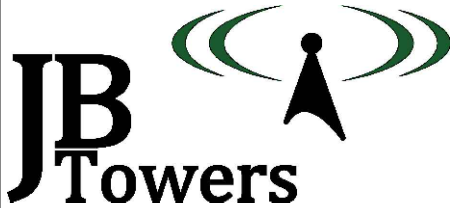

01	FIRST ISSUE			AM 19/11/18
REV	REV			BY DATE
SCALE AS SHOWN WHEN PRINTED AT A3	DRAWN	AM	CHECKED	MP
	DATE	19/11/18	DATE	19/11/18
			DATE	19/11/18

ALL DIMENSIONS IN mm UNLESS OTHERWISE STATED.
THIS DRAWING TO BE READ IN CONJUNCTION WITH
OTHER RELEVANT DRAWINGS.

TITLE
SKIRMETT
GENERAL ARRANGEMENT
SHEET 3 OF 3

SITE ADDRESS
VALENTINE FARM
SHOGMOOR LANE
SKIRMETT
HENLEY-ON-THAMES
RG9 6TD

ARQIVA REF.
141568


DRG No.
200

REV
01

ALL SCALES AS SHOWN WHEN PRINTED AT A3



ALL SCALES AS SHOWN WHEN PRINTED AT A3

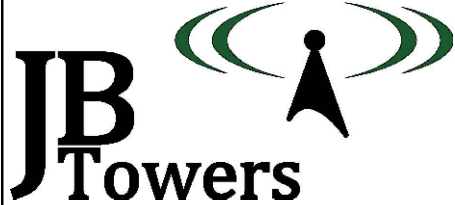

02	UPDATED HOLES FOR SPLICE			MI	13/01/21
01	FIRST ISSUE			AM	19/11/18
REV	REV			BY	DATE
SCALE AS SHOWN		DRAWN	AM	CHECKED	MP
WHEN PRINTED AT A3		DATE	19/11/18	DATE	19/11/18
		APPROVED	JBT	DATE	19/11/18
ALL DIMENSIONS IN mm UNLESS OTHERWISE STATED. THIS DRAWING TO BE READ IN CONJUNCTION WITH OTHER RELEVANT DRAWINGS.					



TITLE
SKIRMETT
TIMBER POLE HOLE SET OUT
SHEET 1 OF 2

SITE ADDRESS
VALENTINE FARM
SHOGMOOR LANE
SKIRMETT
HENLEY-ON-THAMES
RG9 6TD


ARQIVA REF.
141568

DRG No.
201


REV
02

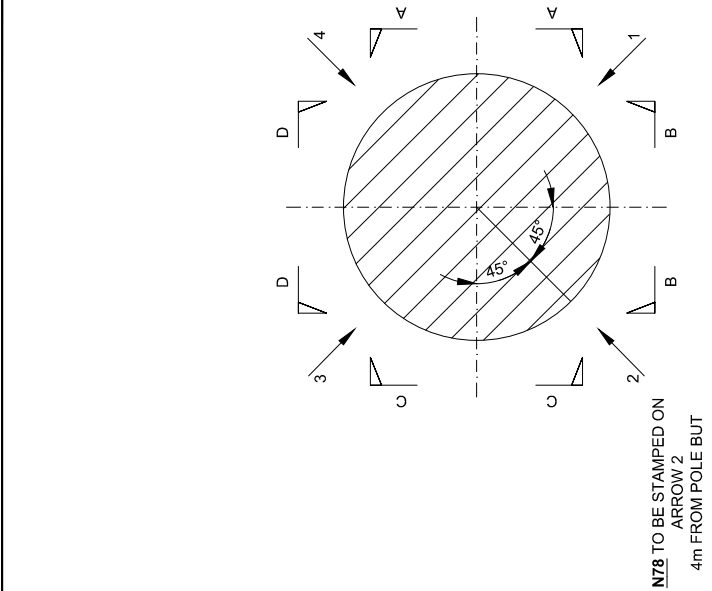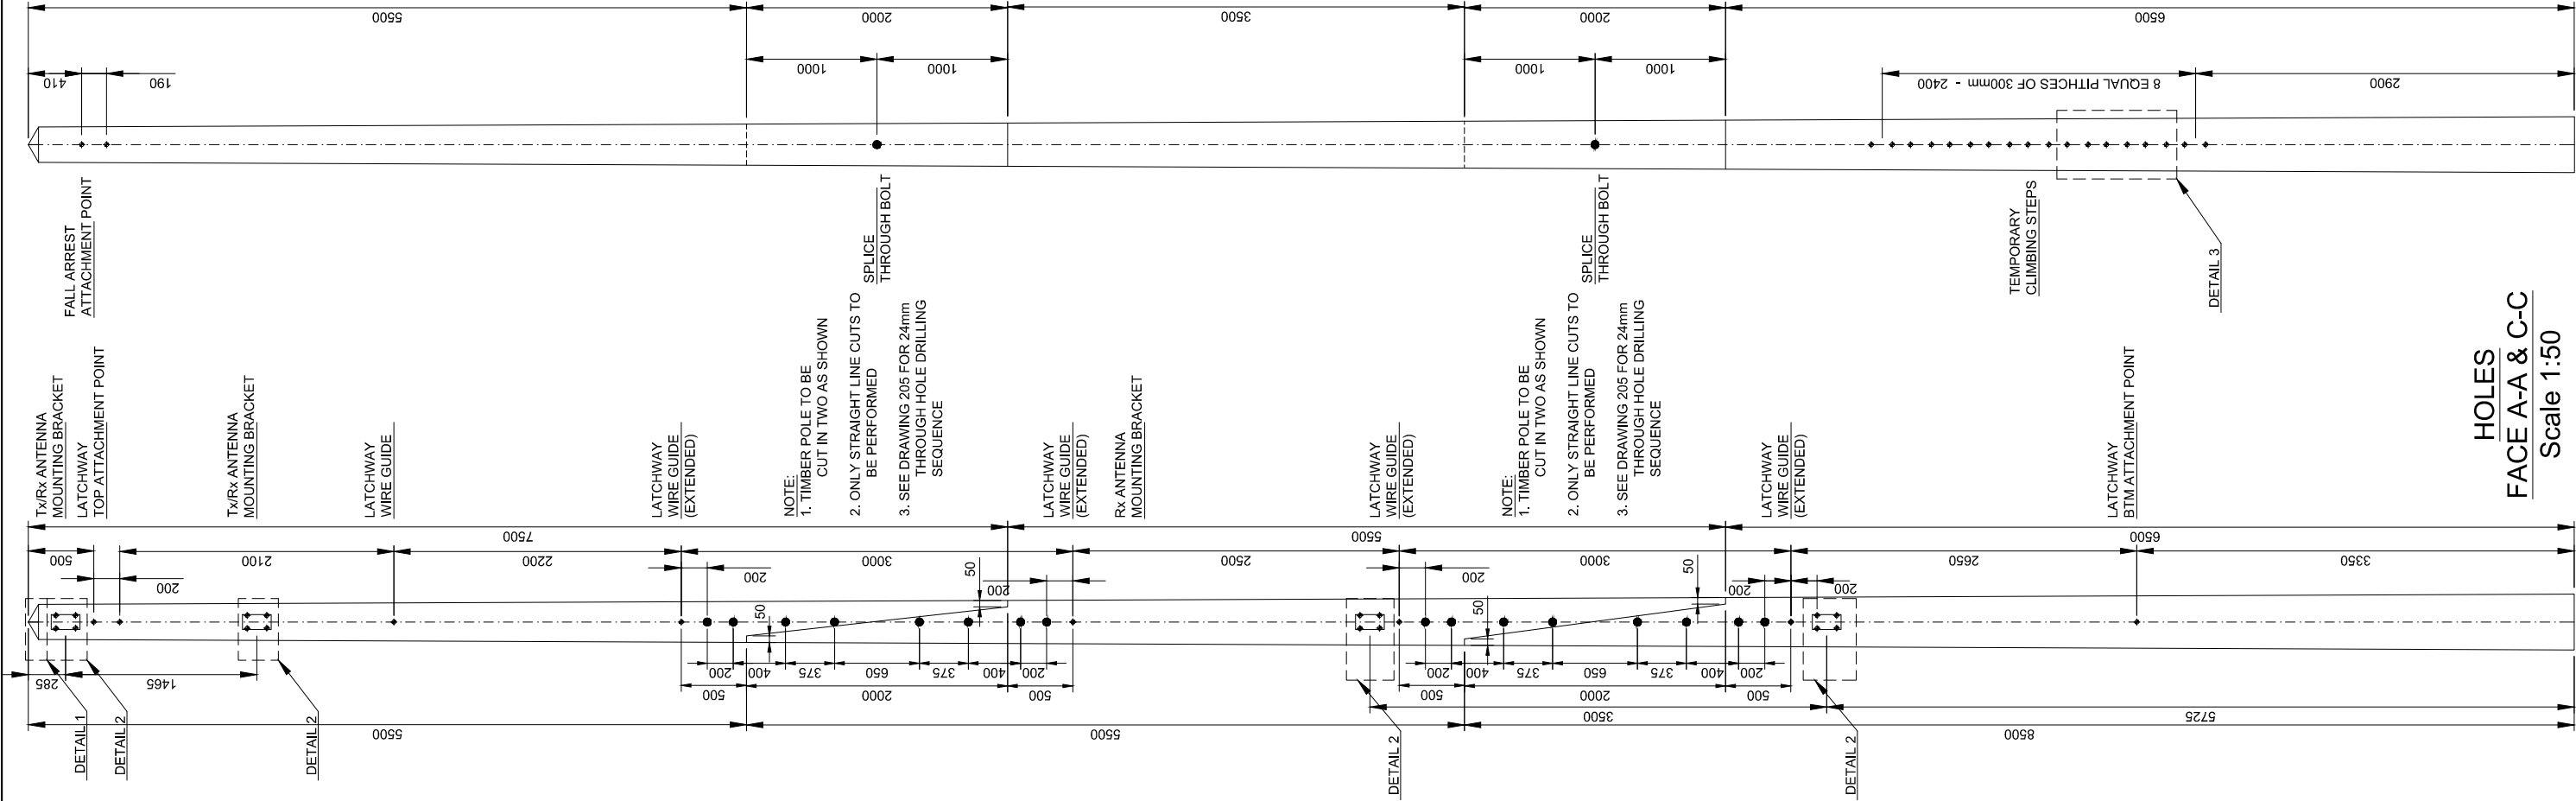


TIMBER POLE
FACE NOMENCLATURE
Scale 1:20

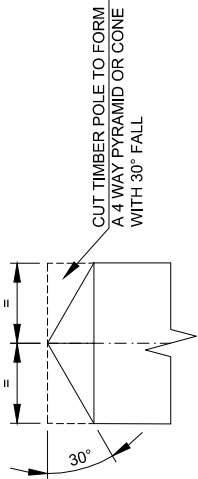

DETAIL 1
Scale 1:10

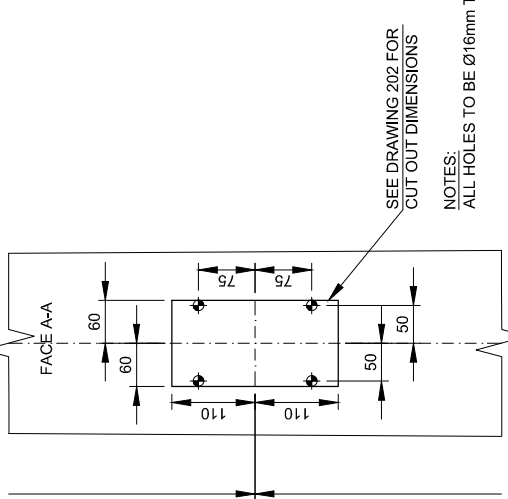



DETAIL 2 - TYPICAL
Scale 1:10

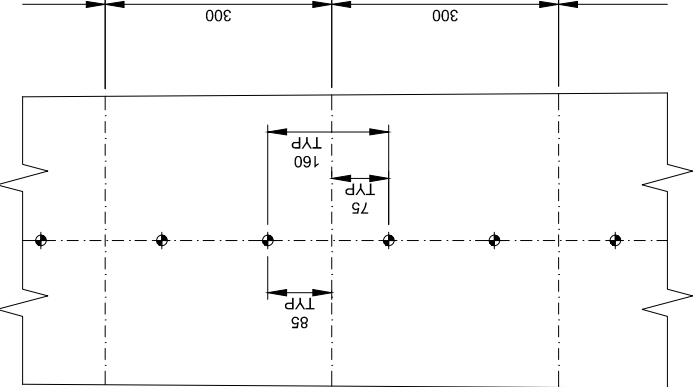

DETAIL 3 - TYPICAL
Scale 1:10


HOLES
FACE B-B & D-
Scale 1:50

HOLES
FACE A-A & C-C
Scale 1:50

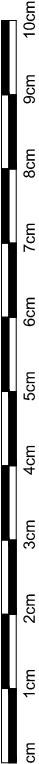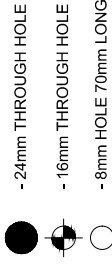

ALL SCALES AS SHOWN WHEN PRINTED AT A3

ALL SCALES AS SHOWN WHEN PRINTED AT A3

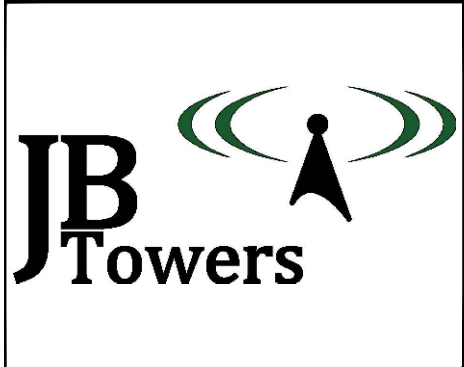


01	FIRST ISSUE							AM	19/11/18
REV	REV							BY	DATE
SCALE AS SHOWN WHEN PRINTED AT A3		DRAWN	AM	CHECKED	MP	APPROVED JBT			
		DATE	19/11/18	DATE	19/11/18	DATE 19/11/18			
ALL DIMENSIONS IN mm UNLESS OTHERWISE STATED. THIS DRAWING TO BE READ IN CONJUNCTION WITH OTHER RELEVANT DRAWINGS.									

TITLE

SKIRMETT


TIMBER POLE HOLE SET OUT
SHEET 2 OF 2

SITE ADDRESS		
VALENTINE FARM SHOGMOOR LANE SKIRMETT HENLEY-ON-THAMES RG9 6TD		
ARQIVA REF. 141568	DRG No. 201	REV 01

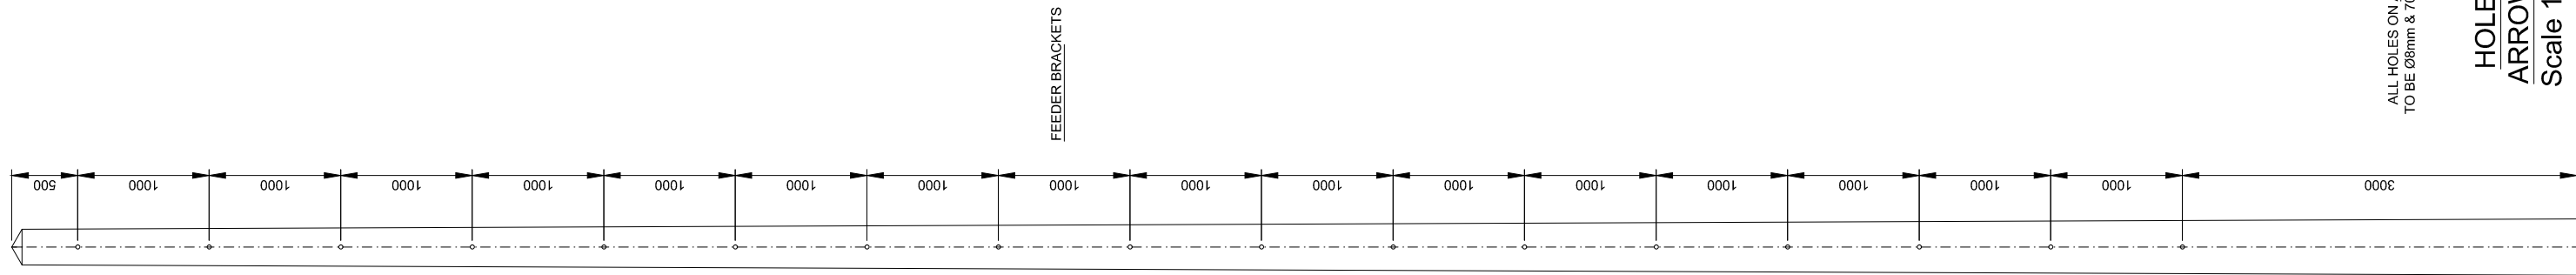


ALL HOLES ON ARROW 1
TO BE Ø8mm & 70mm LONG

HOLES
ARROW 1
Scale 1:50

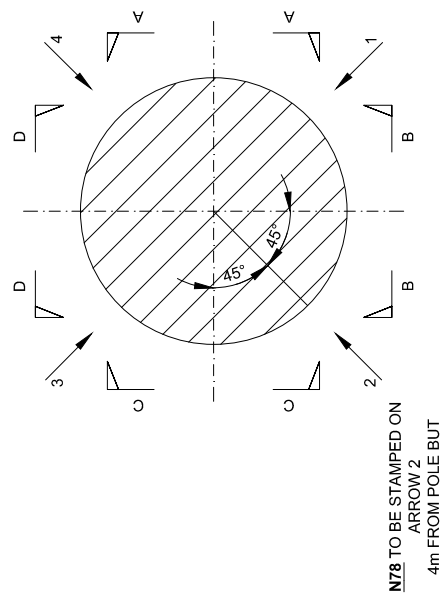

TIMBER POLE
FACE NOMENCLATURE
Scale 1:20

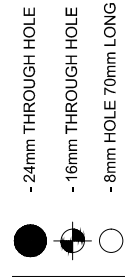

ALL SCALES AS SHOWN WHEN PRINTED AT A3

ALL SCALES AS SHOWN WHEN PRINTED AT A3


01	FIRST ISSUE					AM	19/11/18
REV	REV					BY	DATE
SCALE AS SHOWN		DRAWN	AM	CHECKED	MP	APPROVED	JBT
WHEN PRINTED AT A3		DATE	19/11/18	DATE	19/11/18	DATE	19/11/18
ALL DIMENSIONS IN mm UNLESS OTHERWISE STATED. THIS DRAWING TO BE READ IN CONJUNCTION WITH OTHER RELEVANT DRAWINGS.							

TITLE

SKIRMETT


TIMBER POLE CUT OUT
DETAIL

SITE ADDRESS		
VALENTINE FARM SHOGMOOR LANE SKIRMETT HENLEY-ON-THAMES RG9 6TD		
ARQIVA REF. 141568	DRG No. 202	REV 01

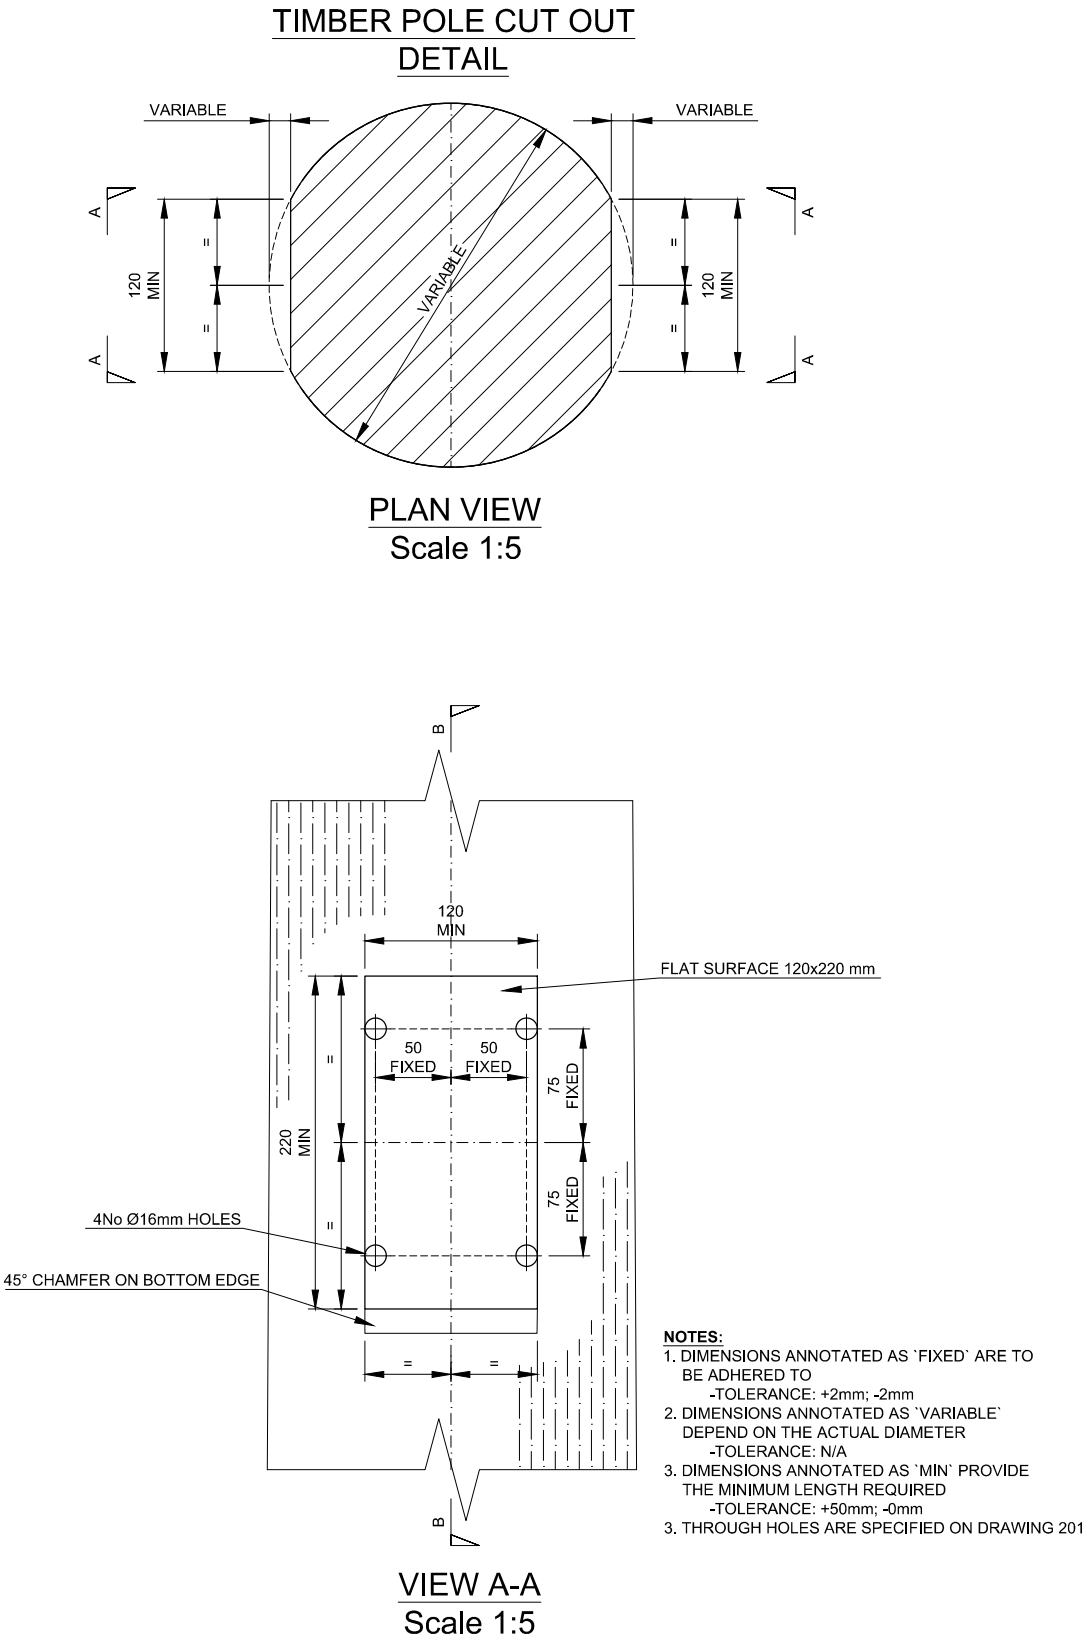


ALL SCALES AS SHOWN WHEN PRINTED AT A3

ALL SCALES AS SHOWN WHEN PRINTED AT A3

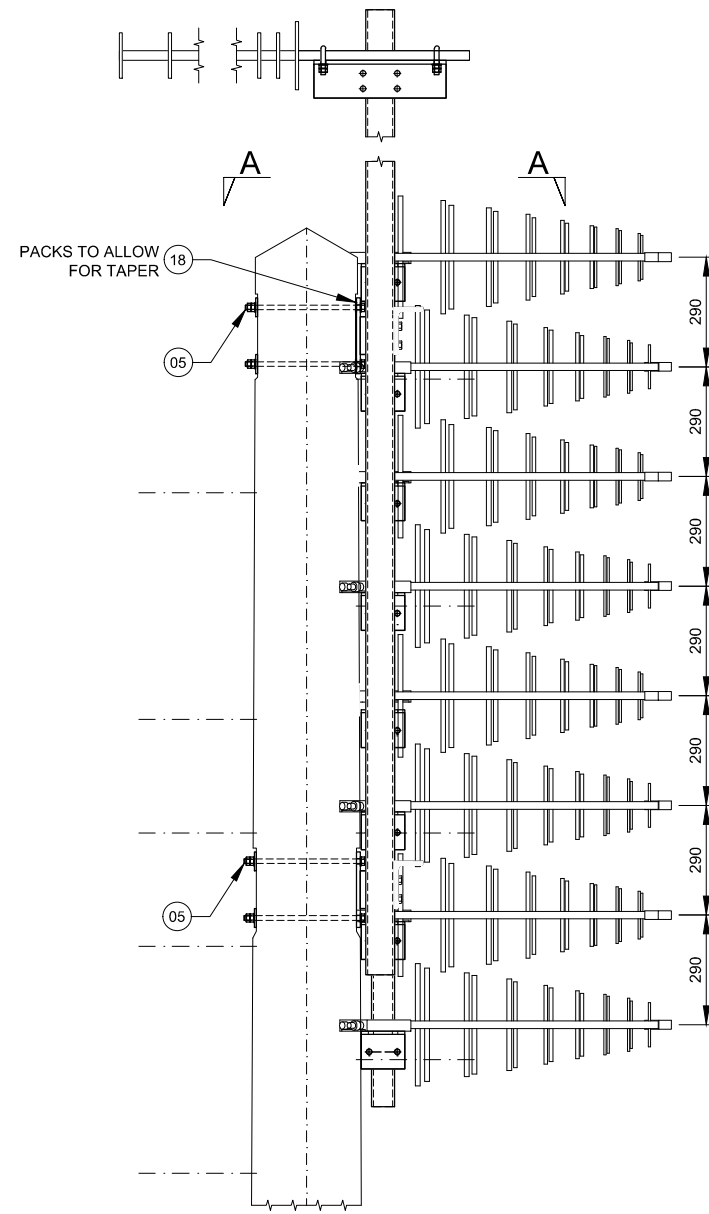


DETAIL G - Rx & Tx ANTENNA MOUNTS
Scale 1:20


**2W - TWO WAY POWER DIVIDER
4W - FOUR WAY POWER DIVIDER**

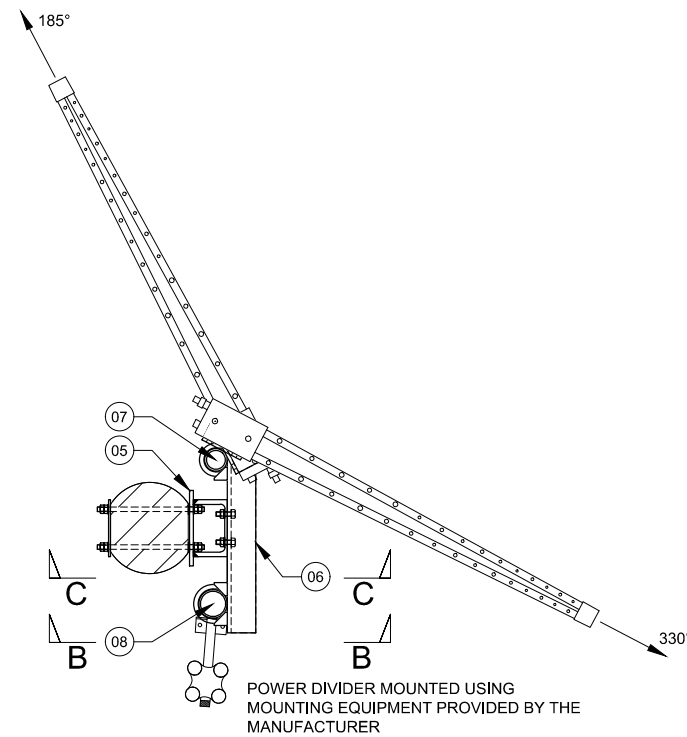

SECTION A-A
Scale 1:20

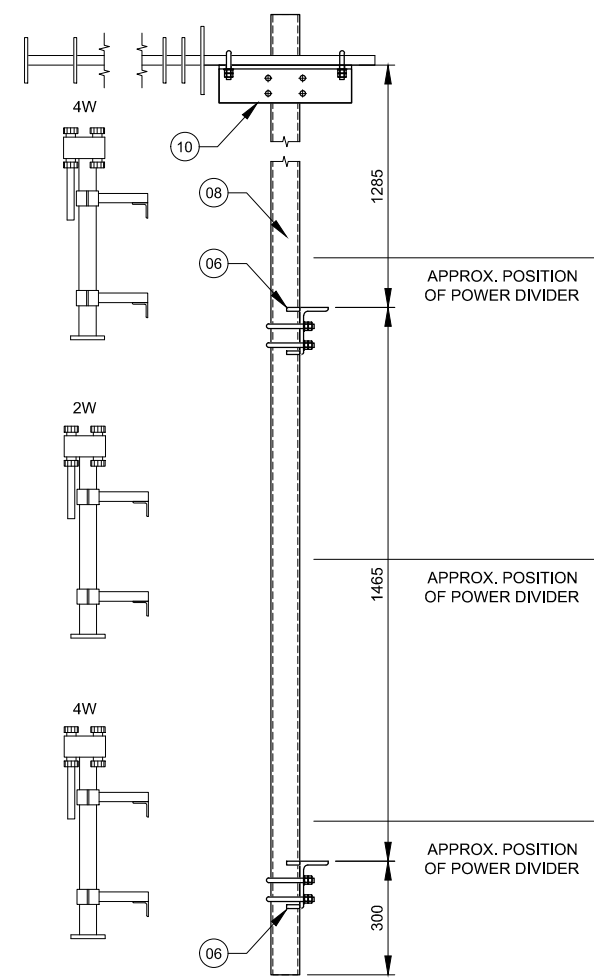

VIEW B-B
Scale 1:20

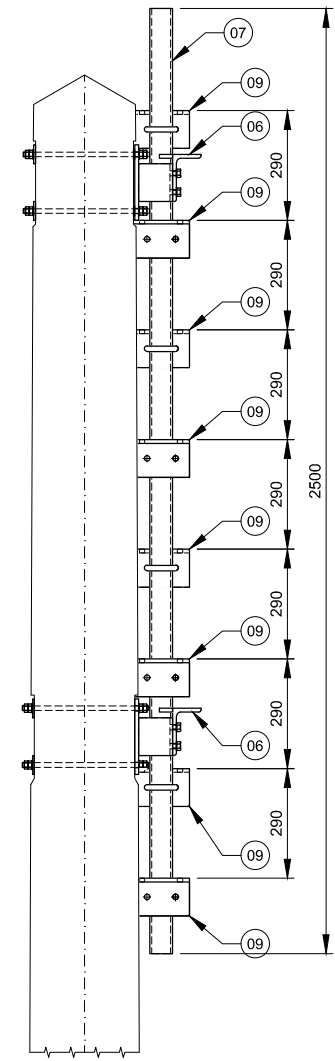


SECTION C-C
Scale 1:20

ALL SCALES AS SHOWN WHEN PRINTED AT A3



ALL SCALES AS SHOWN WHEN PRINTED AT A3

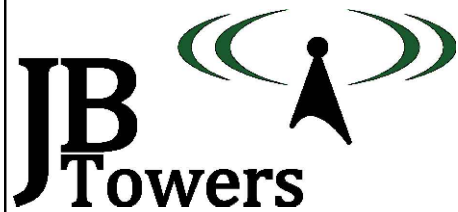

03	POWER DIVIDER MOUNTING UPDATED	AM	08/05/19
02	POWER DIVIDER POSITION UPDATED	TT	24/04/19
01	FIRST ISSUE	AM	19/11/18
REV	REV	BY	DATE
SCALE AS SHOWN WHEN PRINTED AT A3	DRAWN DATE	AM 19/11/18	CHECKED DATE
		MP 19/11/18	APPROVED DATE
		JBT 19/11/18	
ALL DIMENSIONS IN mm UNLESS OTHERWISE STATED. THIS DRAWING TO BE READ IN CONJUNCTION WITH OTHER RELEVANT DRAWINGS.			



TITLE
ANTENNA MOUNT
DETAIL G

SITE ADDRESS
**VALENTINE FARM
SHOGMOOR LANE
SKIRMETT
HENLEY-ON-THAMES
RG9 6TD**

ARQIVA REF.
141568


DRG No.
203

REV
03

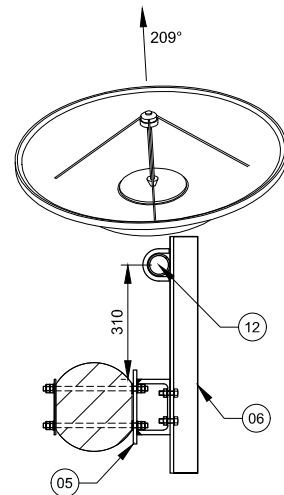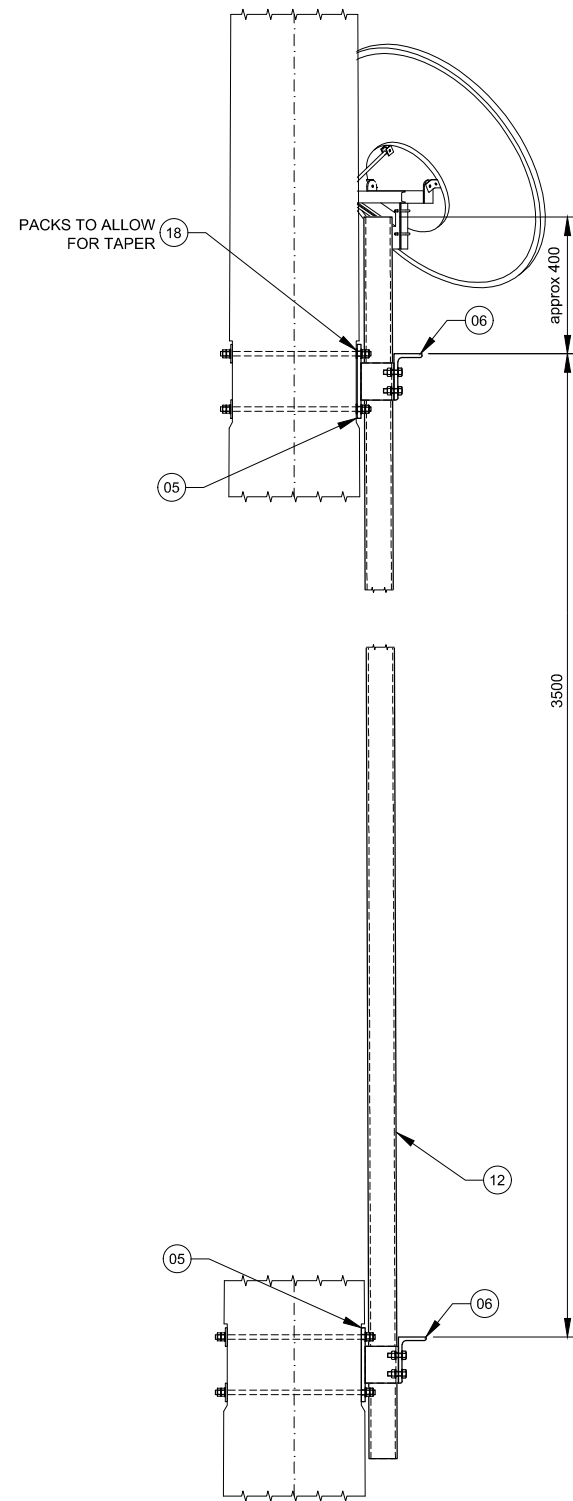

SECTION D-D
Scale 1:20


DETAIL H - VSAT DISH MOUNT
Scale 1:20

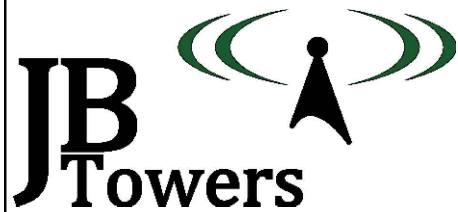

02	UPDATED DETAIL			MI	13/01/21
01	FIRST ISSUE			AM	19/11/18
REV	REV			BY	DATE
SCALE AS SHOWN		DRAWN	AM	CHECKED	MP
WHEN PRINTED AT A3		DATE	19/11/18	DATE	19/11/18
		DATE	19/11/18	DATE	19/11/18
ALL DIMENSIONS IN mm UNLESS OTHERWISE STATED. THIS DRAWING TO BE READ IN CONJUNCTION WITH OTHER RELEVANT DRAWINGS.					



TITLE		SITE ADDRESS	
ANTENNA MOUNT		VALENTINE FARM	
DETAIL H		SHOGMOOR LANE	
		SKIRMETT	
		HENLEY-ON-THAMES	
		RG9 6TD	
ARQIVA REF.		DRG No.	REV
141568		204	02

ALL SCALES AS SHOWN WHEN PRINTED AT A3

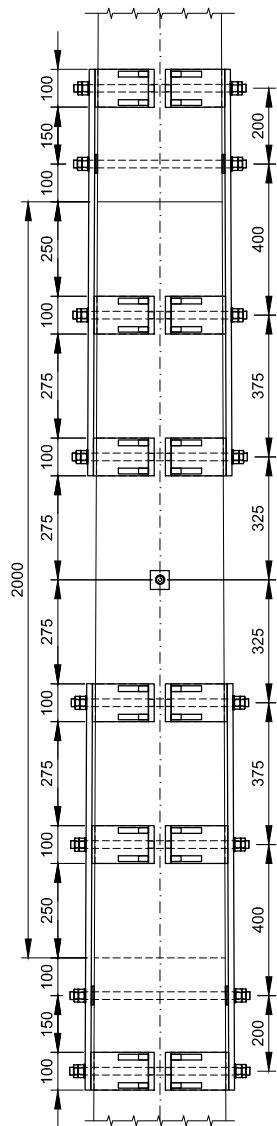


DETAIL I TIMBER POLE SPLICE
Scale 1:20

NOTE:
- ALL M16 BOLTS TO BE TIGHTENED TO 90Nm
- ALL SITE DRILLED HOLE/CUT ENDS TO BE TREATED WITH
METAFLUX 70-40 ZINC PASTE FOLLOWED BY 1 COAT OF
7-42 ZINC ALU OR 70-16 ALUMINIUM SPRAY

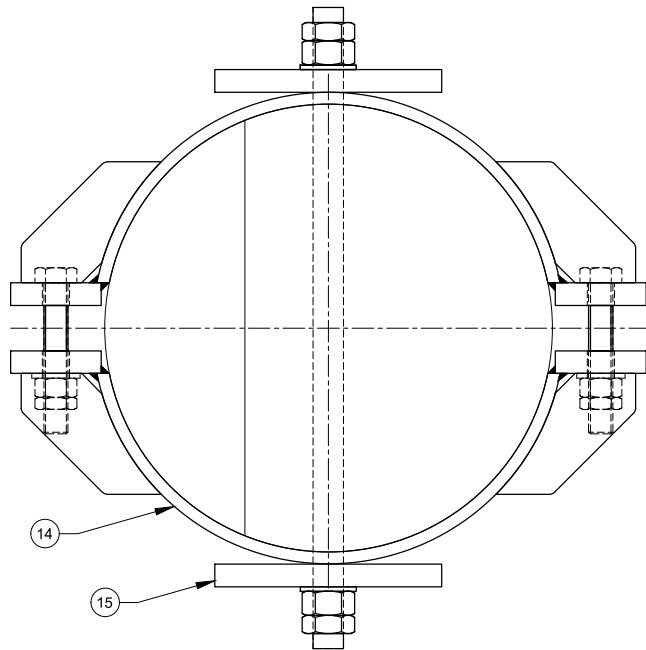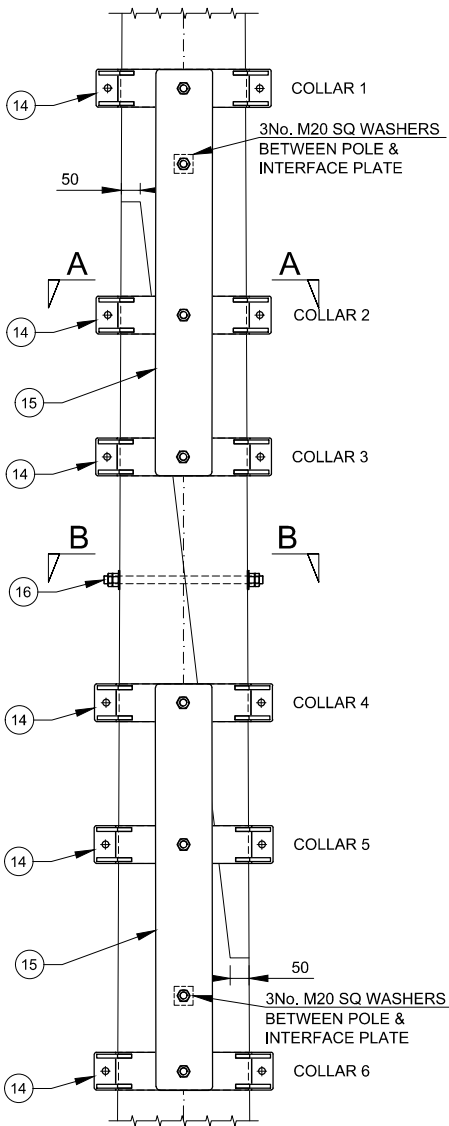


SECTION A-A
Scale 1:5

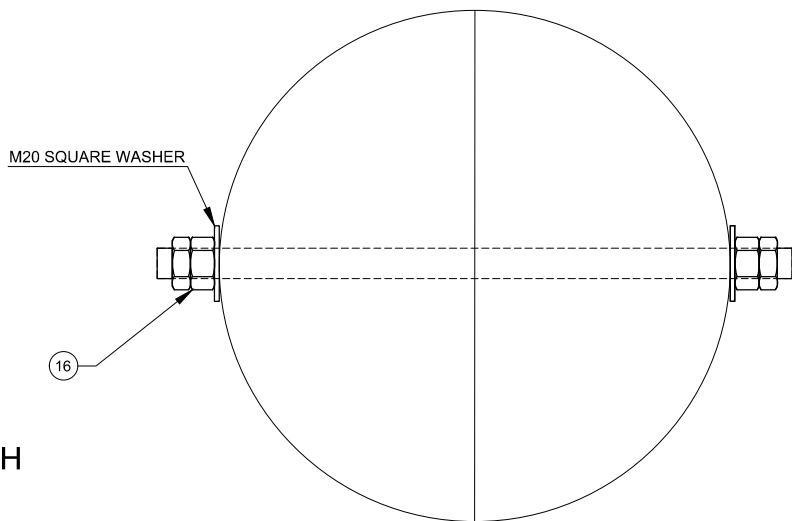

SECTION B-B
Scale 1:5

- WORK SEQUENCE (PRIOR TO POLE BEING SENT TO SITE):**
1. LOCATION OF COLLARS TO BE MARKED ON POLE AND POLE OD AT THESE LOCATIONS TO BE MEASURED AND USED TO INFORM THE FABRICATION OF THE STEEL COLLARS.
(COLLAR HOLES FOR THE THROUGH BOLTS ARE TO BE DRILLED LATER)
 2. HOLES IN POLE FOR ALL COLLAR THROUGH BOLTS TO BE DRILLED.
 3. SPLICE JOINT TO BE CUT IN POLE.
 4. POLE TO BE PRESSURE IMPREGNATED WITH CREOSOTE.
 5. POLE SECTIONS TO BE OFFERED TO ONE ANOTHER AND ONCE IN THE CORRECT POSITION COLLARS 2 & 5 SHALL BE INSTALLED TO HOLD THE POLE IN POSITION AND THE CLAMPING BOLTS TORQUED.
 6. THE THROUGH BOLT IN THE CENTRE OF THE SPLICE SHALL BE DRILLED AND THE THROUGH BOLT INSERTED.
 7. THE THROUGH BOLTS FOR COLLARS 1 & 3 AND 4 & 6 SHALL BE INSTALLED AND THE COLLARS OFFERED UP AND THE REQD HOLE LOCATIONS IN THE COLLARS MARKED AND THEN DRILLED.
 8. THESE COLLARS SHALL BE INSTALLED OVER THE THROUGH BOLTS AND THEN THE CLAMPING BOLTS TORQUED.
 9. COLLARS 2 & 5 SHALL THEN BE REMOVED AND THE THROUGH BOLTS INSTALLED AND THE COLLARS OFFERED UP AND THE REQD HOLE LOCATIONS IN THE COLLARS MARKED AND THEN DRILLED.
 10. THESE COLLARS SHALL BE INSTALLED OVER THE THROUGH BOLTS AND THEN THE CLAMPING BOLTS TORQUED.
 11. THE VERTICAL PLATES STRAPPING THE COLLARS TOGETHER SHALL THEN BE INSTALLED.
 12. THE FIT OF ALL ELEMENTS OF THE SPLICE SHALL BE CHECKED AND ONCE SATISFACTORY FIT HAS BEEN CONFIRMED THE SPLICE JOINT CAN BE DISASSEMBLED.
 13. ANY DISTURBED SURFACES SHALL HAVE THEIR WATERPROOFING REPAIRED AS PER NOTES ON DRG 200
 14. THE CLAMPING BOLTS USED IN THE CHECK ERECTION SHALL BE DISCARDED AND NEW BOLTS SUPPLIED TO SITE.

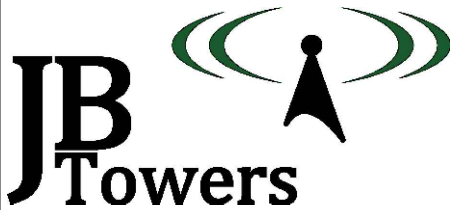


01	FIRST ISSUE	MI	13/01/21
REV	REV	BY	DATE
SCALE AS SHOWN WHEN PRINTED AT A3	DRAWN DATE 13/01/21	CHECKED DATE 13/01/21	APPROVED DATE 13/01/21
ALL DIMENSIONS IN mm UNLESS OTHERWISE STATED. THIS DRAWING TO BE READ IN CONJUNCTION WITH OTHER RELEVANT DRAWINGS.			

TITLE
SKIRMETT
TIMBER POLE SPLICE
DETAIL I

SITE ADDRESS
VALENTINE FARM
SHOGMOOR LANE
SKIRMETT
HENLEY-ON-THAMES
RG9 6TD


ARQIVA REF.
141568
DRG No.
205
REV
01

ALL SCALES AS SHOWN WHEN PRINTED AT A3

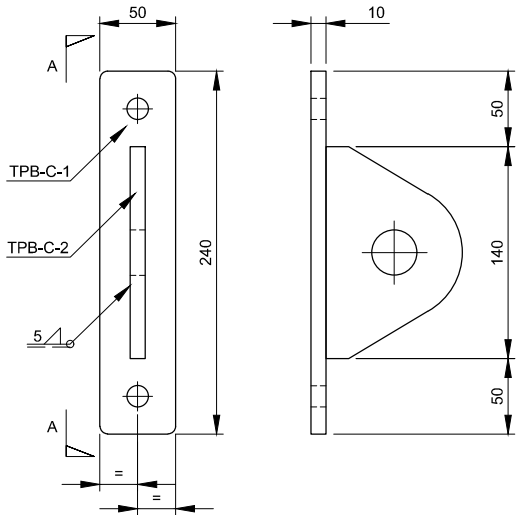

PART TPB-C
Scale 1:5

VIEW A-A
Scale 1:5

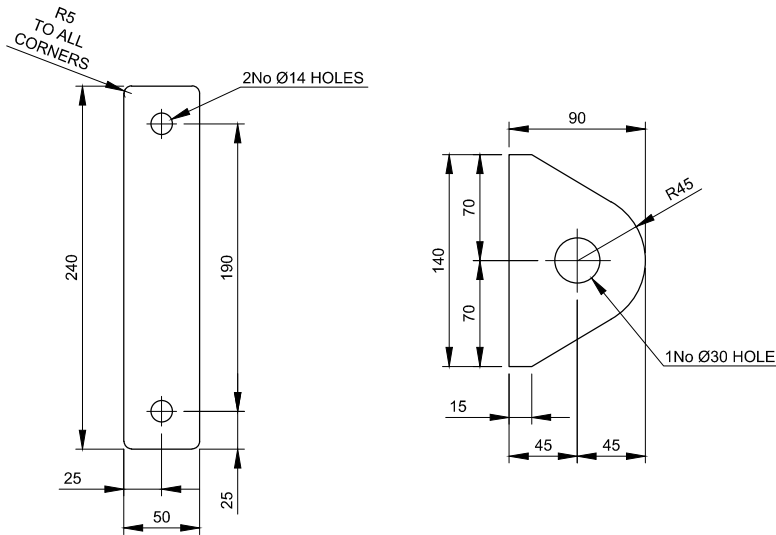

TPB-C-1 - 10mm THICK
Scale 1:5

TPB-C-2 - 10mm THICK
Scale 1:5


Parts list for TPB-C

Item	Part	Quantity	Part description	Length	Material	Weight
01	TPB-C-1	1	240x50x10mm	N/A	S275J0	0.94 kg
02	TPB-C-2	1	140x90x10mm	N/A	S275J0	0.99 kg
03	STUDS	1	M12 STUDDING	350mm	GRADE 8.8	0.31 kg

- All steel hot dip galvanized
- Each STUD to be supplied with 4 Full Nuts, 2 Flat Washers and 2 Spring Washers
- For fabrication notes see drawing 304


Total Weight:

2.24 kg

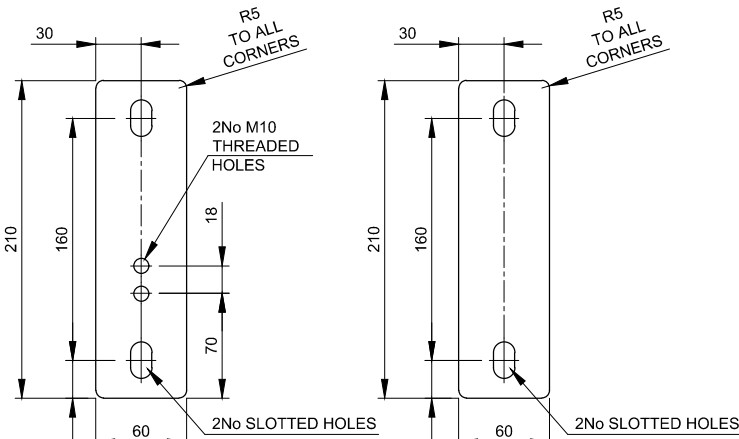

PART TPS-R-1
Scale 1:5

PART TPS-R-2
Scale 1:5

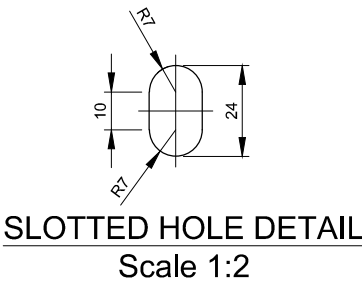

SLOTTED HOLE DETAIL
Scale 1:2


Parts list for TPS-R

Item	Part	Quantity	Part description	Length	Material	Weight
01	TPS-R-1	1	210x60x15mm	N/A	S275J0	1.48 kg
02	TPS-R-2	1	210x60x5mm	N/A	S275J0	0.49 kg
03	STUDS	2	M12 STUDDING	500mm	GRADE 8.8	0.44 kg
04	NUT-S	2	M12 SHALLOW NUT	N/A	GRADE 8.8	-
05	NUT	4	M12 NUT	N/A	GRADE 8.8	-
06	WSH	4	M12 WASHER	N/A	GRADE 8.8	-

- All steel hot dip galvanized
- For fabrication notes see drawing 304

Total Weight:

2.85 kg

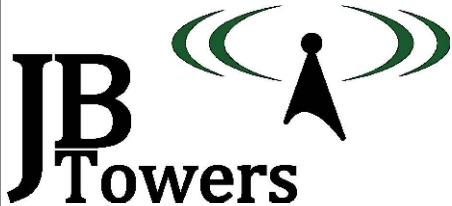

01	FIRST ISSUE	AM	19/11/18
REV	REV	BY	DATE
SCALE AS SHOWN	DRAWN	CHECKED	APPROVED
WHEN PRINTED AT A3	AM	MP	JBT
DATE	19/11/18	DATE	19/11/18
DATE	19/11/18	DATE	19/11/18
ALL DIMENSIONS IN mm UNLESS OTHERWISE STATED. THIS DRAWING TO BE READ IN CONJUNCTION WITH OTHER RELEVANT DRAWINGS.			

TITLE
ATTACHMENT POINT &
TEMPORARY STEP DETAILS
PARTS: TPB-C; TPS-R

SITE ADDRESS
VALENTINE FARM
SHOGMOOR LANE
SKIRMETT
HENLEY-ON-THAMES
RG9 6TD

ARQIVA REF.
141568


DRG No.
300

REV
01

ALL SCALES AS SHOWN WHEN PRINTED AT A3



ALL SCALES AS SHOWN WHEN PRINTED AT A3

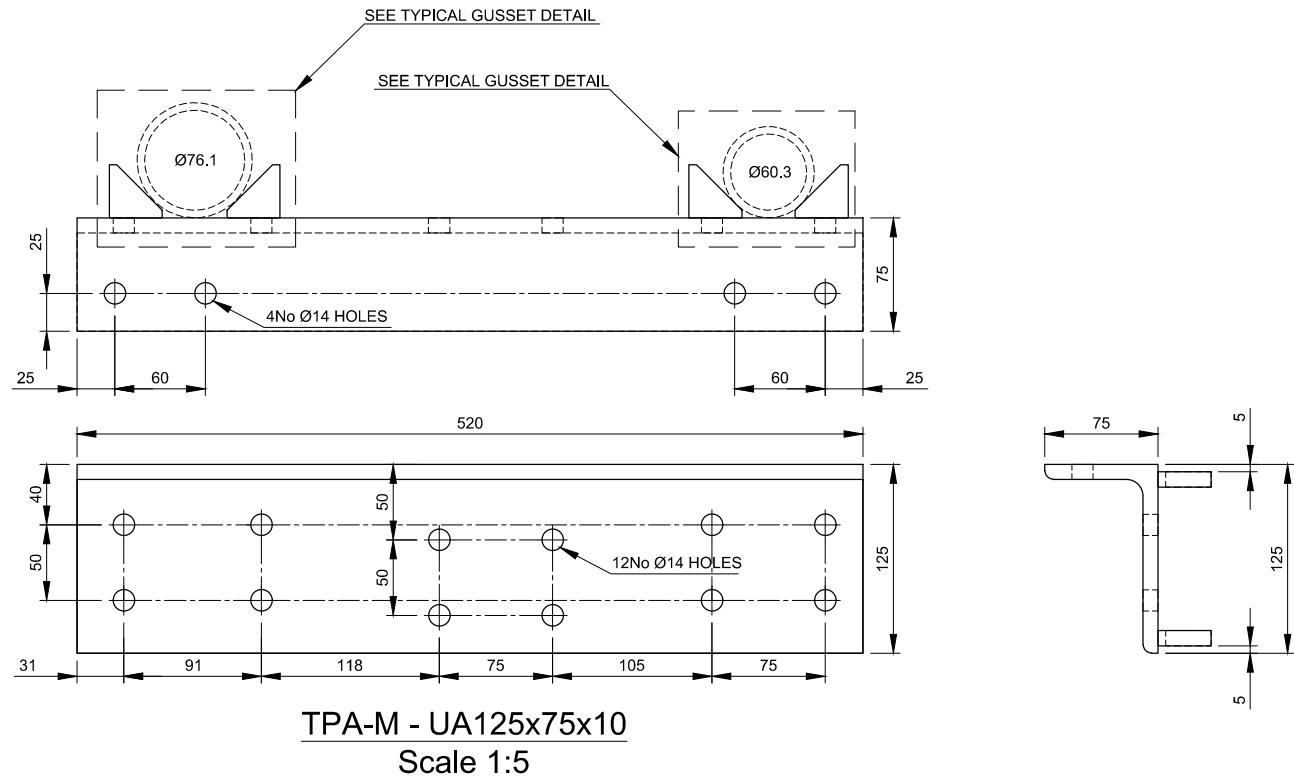


TPA-M - UA125x75x10
Scale 1:5


Parts list for TPA-M

Item	Part	Quantity	Part description	Length	Material	Weight
01	TPA-M	1	UA125x75x10 C/W GUSSETS	520mm	S275J0	7.80 kg
02	U-BOLT	2	M12 U-BOLT FOR CHS 60.3mm	N/A	GRADE 8.8	-
03	U-BOLT	2	M12 U-BOLT FOR CHS 76.1mm	N/A	GRADE 8.8	-
03	BOLT	4	M12x45 (2D+6) BOLT	N/A	GRADE 8.8	-
Total Weight:						7.80 kg

- All steel hot dip galvanized
- Each STUD & U-BOLT to be supplied with 4 Full Nuts, 2 Flat Washers and 2 Spring Washers
- Each BOLT to be supplied with 1 Full Nut, 1 Form E FLat Washer and 1 Spring Washer
- For fabrication notes see drawing 304

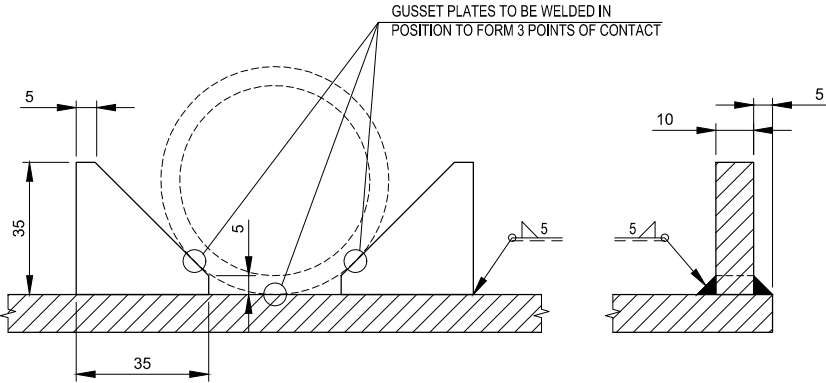

TYPICAL GUSSET PLATE DETAIL
Scale 1:2

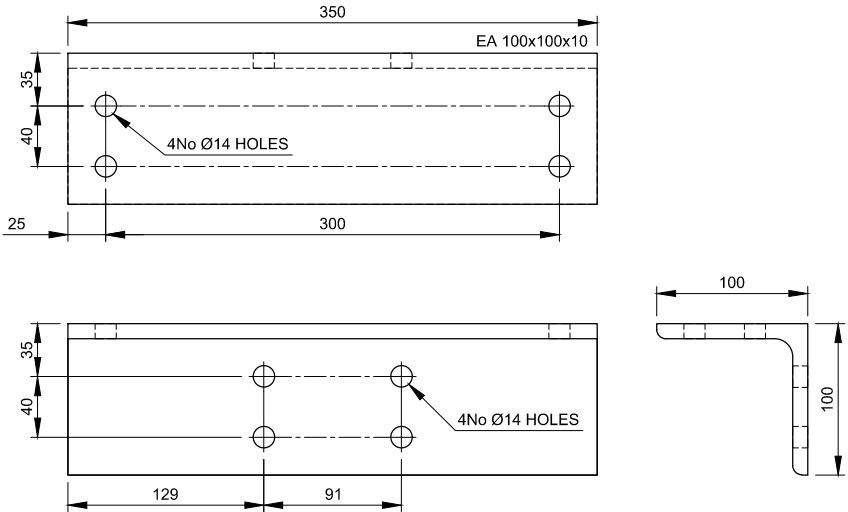


TPY-A - EA100x100x10
Scale 1:5

Parts list for TPY-A

Item	Part	Quantity	Part description	Length	Material	Weight
01	TPY-A	1	EA100x100x10	350mm	S275J0	5.25 kg
02	U-BOLT	2	M12 U-BOLT FOR CHS 25mm	N/A	GRADE 8.8	-
03	U-BOLT	2	M12 U-BOLT FOR CHS 76.1mm	N/A	GRADE 8.8	-
Total Weight:						5.25 kg

- All steel hot dip galvanized
- Each STUD & U-BOLT to be supplied with 4 Full Nuts, 2 Flat Washers and 2 Spring Washers
- Each BOLT to be supplied with 1 Full Nut, 1 Form E FLat Washer and 1 Spring Washer
- For fabrication notes see drawing 304

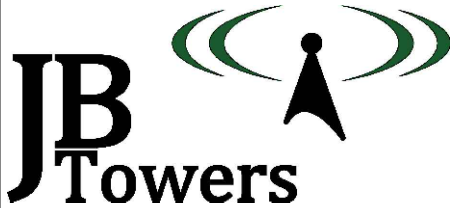

01	FIRST ISSUE					AM	19/11/18
REV	REV					BY	DATE
SCALE AS SHOWN		DRAWN	AM	CHECKED	MP	APPROVED	JBT
WHEN PRINTED AT A3		DATE	19/11/18	DATE	19/11/18	DATE	19/11/18
ALL DIMENSIONS IN mm UNLESS OTHERWISE STATED. THIS DRAWING TO BE READ IN CONJUNCTION WITH OTHER RELEVANT DRAWINGS.							

TITLE
ANTENNA MOUNTING
BRACKETS

PARTS: TPA-M; TPY-A

SITE ADDRESS
VALENTINE FARM
SHOGMOOR LANE
SKIRMETT
HENLEY-ON-THAMES
RG9 6TD

ARQIVA REF.
141568


DRG No.
302

REV
01

ALL SCALES AS SHOWN WHEN PRINTED AT A3



ALL SCALES AS SHOWN WHEN PRINTED AT A3

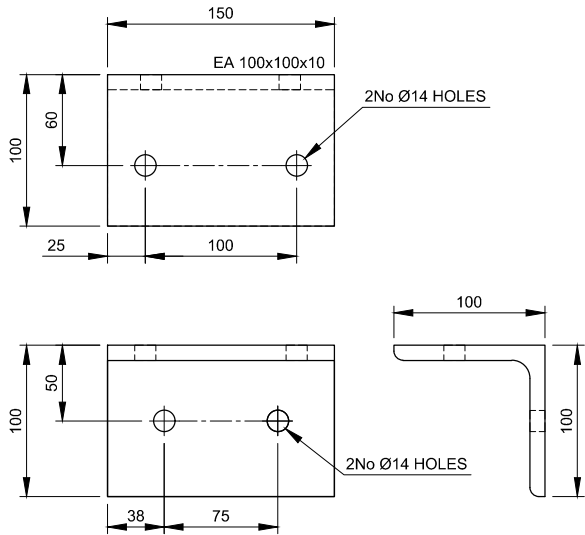


TPL-A - EA100x100x10
Scale 1:5

Parts list for TPL-A

Item	Part	Quantity	Part description	Length	Material	Weight
01	TPL-A	1	EA100x100x10	150mm	S275J0	2.25 kg
02	BOLT	2	M12 55mm LONG SET BOLT	55mm	GRADE 8.8	-
03	U-BOLT	1	M12 U-BOLT FOR CHS 60.3mm	N/A	GRADE 8.8	-
Total Weight:						2.25 kg

- All steel hot dip galvanized
- Each STUD & U-BOLT to be supplied with 4 Full Nuts, 2 Flat Washers and 2 Spring Washers
- Each BOLT to be supplied with 1 Full Nut, 1 Form E FLat Washer and 1 Spring Washer
- For fabrication notes see drawing 304

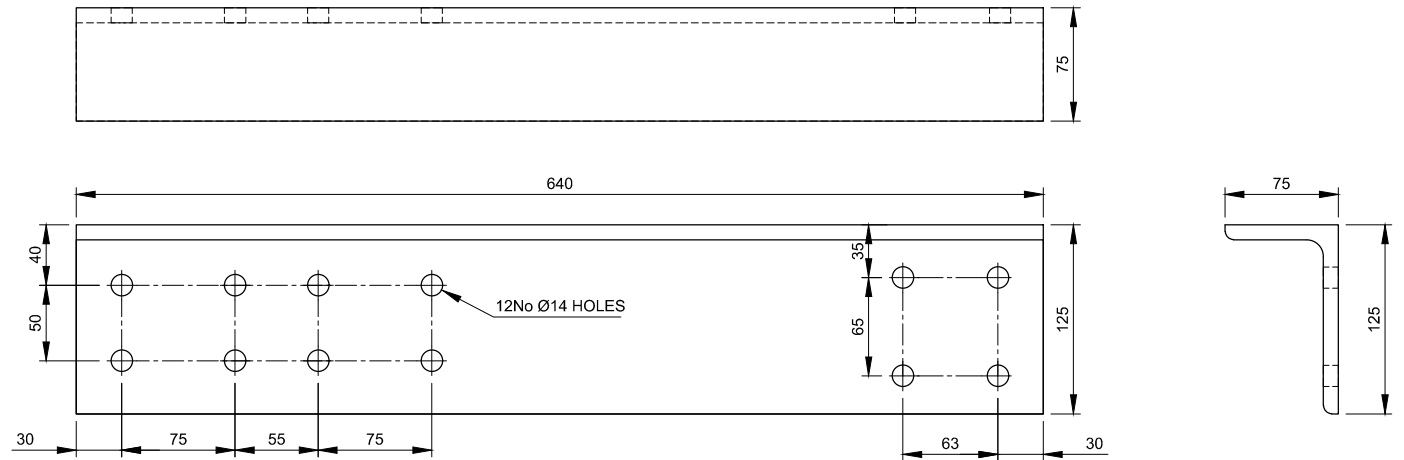


TPA-V - UA125x75x10
Scale 1:5

Parts list for 1No. TPA-V (2No. required per site)

Item	Part	Quantity	Part description	Length	Material	Weight
01	TPA-V	1	UA125x75x10	640mm	S275J0	9.60 kg
02	U-BOLT	2	M12 U-BOLT FOR CHS 48.3mm	N/A	GRADE 8.8	-
03	BOLT	4	M12x45 (2D+6) BOLT	N/A	GRADE 8.8	-
Total Weight:						9.60 kg

- Each STUD & U-BOLT to be supplied with 4 Full Nuts, 2 Flat Washers and 2 Spring Washers
- Each BOLT to be supplied with 1 Full Nut, 1 Form E FLat Washer and 1 Spring Washer
- For fabrication notes see drawing 304

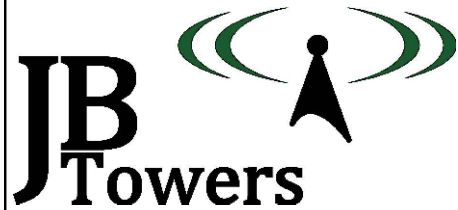

03	VSAT DISH MOUNTING BRACKET ADDED	MI	13/01/21
02	POWER DIVIDER BRACKET REMOVED	AM	08/05/19
01	FIRST ISSUE	AM	19/11/18
REV	REV	BY	DATE

SCALE AS SHOWN	DRAWN	AM	CHECKED	MP	APPROVED	JBT
WHEN PRINTED AT A3	DATE	19/11/18	DATE	19/11/18	DATE	19/11/18

ALL DIMENSIONS IN mm UNLESS OTHERWISE STATED.
THIS DRAWING TO BE READ IN CONJUNCTION WITH
OTHER RELEVANT DRAWINGS.

TITLE		SITE ADDRESS		
LOG MOUNTING BRACKET AND VSAT DISH MOUNTING BRACKET		VALENTINE FARM SHOGMOOR LANE SKIRMETT HENLEY-ON-THAMES RG9 6TD		
PART: TPL-A; TPA-V		ARQIVA REF. 141568	DRG No. 303	REV 03

ALL SCALES AS SHOWN WHEN PRINTED AT A3



ALL SCALES AS SHOWN WHEN PRINTED AT A3

NOTE:
4No. EXTENDED WIRE GUIDES - PART NO. 35397-00
1No. REGULAR WIRE GUIDES - PART NO. 30050-00


Item	Part	Drawing	Quantity	Part description	Length	Material	Weight
01	01	200	1	3 MAN LATCHWAY SYSTEM & 5No. WIRE GUIDES FOR FACE MOUNTED MONOPOLE	17000	N/A	-
02	TPB-C	300	2	FALL ARREST ATTACHMENT POINT	N/A	S275J0	4.50 kg
03	03	200	50	PERMANENT BT STEP c/w 3No 10x75mm ZINC-PLATED COACH SCREWS	N/A	S275J0	15.00 kg
04	TPS-R	300	9	'MonoStep' ASSEMBLY	N/A	S275J0	25.65 kg
05	TPB-A	301	4	MOUNTING BRACKET	N/A	S275J0	30.10 kg
06	TPA-M	302	2	ANTENNA MOUNTING BRACKET	N/A	S275J0	15.60 kg
07	07	203	1	CHS 60.3x5mm	2500mm	S355J2H	17.05 kg
08	08	203	1	CHS 76.1x5mm	3200mm	S355J2H	28.00 kg
09	TPL-A	303	8	LOG MOUNTING BRACKET	N/A	S275J0	18.00 kg
10	TPY-A	302	1	YAGI MOUNTING BRACKET	350mm	S275J0	5.25 kg
11	TPA-V	303	2	VSAT DISH MOUNTING BRACKET	640mm	S275J0	19.20 kg
12	12	204	1	CHS 76.1x5mm	4200mm	S355J2H	36.85 kg
13	13	200	1	FEEDER COVER - 2/CG/100	3500mm	UV RESISTANT PLASTIC	-
14	14	200	17	FEEDER CLAMP - 2/FCD/028	N/A	POLYPROPYLENE	-
15	15	200	17	M10 SCREW DOWELS WTH M10 NUT	100mm	STAINLESS STEEL	-
16	16	200	1	PoleSaver	750mm	N/A	-
17	17	200	8	M12 STUD + 4No NUTS + 2No FLAT WASHERS + 1No Ø50mm WASHER (FOR FALL ARREST SYSTEM)	500mm	GRADE 8.8	3.60 kg
18	18	-	24	M12 WASHER	N/A	GRADE 8.8	-
19	TPC-A	305	12	TIMBER POLE SPLICE COLLAR	N/A	S275J0	135.00kg
20	TPC-B	305	4	TIMER POLE SPLICE INTERFACE PLATE	N/A	S275J0	172.00 kg
Total Weight:							525.80 kg

- All steel hot dip galvanized

- All U-BOLTS to be FLA supply, each Supplied with 4 Full Nuts, 2 Flat Washers and 2 Spring Washers

NOTES:

1. WELDING TO BE IN ACCORDANCE WITH BS EN 1011-1:2009
2. LINEAR DIMS TO BE WITHIN ±1mm;
3. ANGULAR TOLERANCES TO BE WITHIN 0.5°
4. WELDING SYMBOLS ARE IN ACCORDANCE WITH BS EN 22553:1995
5. ALL PROFILE EDGES TO BE DRESSED AND SHARP CORNERS REMOVED
6. ALL WELD SIZES ARE FINAL SIZES
7. ALL WELDED JOINTS ARE TO BE PICKLE TIGHT
8. ALL STEELWORK TO BE BS EN 10025 GRADE S275 J0 UNO & HOT DIPPED GALVANISED TO BS EN ISO 1461. (ALL HOLLOW SECTIONS TO BE GRADE S355 J0H)
9. ALL STEEL IS TO BE SUPPLIED IN ACCORDANCE WITH EN 1090 TO EXECUTION CLASS 2
10. ALL NON PRE-LOADED BOLTS TO BE COMPLIANT STRUCTURAL BOLTS TO BS EN ISO 15048 PARTS 1&2.
11. STEELWORK COMPONENTS SHALL BE HOT DIP GALVANISED TO ACHIEVE A "VERY HIGH" DURABILITY FOR AN ENVIRONMENT CATEGORY CODE C4 FROM TABLE 1 IN BS EN ISO 14713
12. BOLTS AND NUTS SHALL BE SUPPLIED IN ACCORDANCE WITH BS 7371, SPUN GALVANISED IN ACCORDANCE WITH ISO 10684, THE NUTS RE-TAPPED AFTER GALVANISING, AND THE THREADS TREATED WITH GREASE.
13. ALL BOLTS TO BE CUT ON SITE TO EXTEND MAX 10mm BEYOND THE NUT WHEN TIGHTENED UNO.
14. ALL SITE DRILLED HOLE/CUT ENDS TO BE TREATED WITH METAFLUX 70-40 ZINC PASTE FOLLOWED BY 1 COAT OF 7-42 ZINC ALU OR 70-16 ALUMINIUM SPRAY

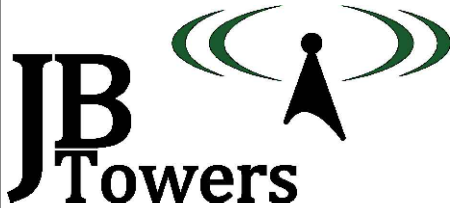


03	UPDATED PARTS LIST			MI	13/01/21
02	POWER DIVIDER BRACKET REMOVED			AM	08/05/19
01	FIRST ISSUE			AM	19/11/18
REV	REV			BY	DATE
SCALE AS SHOWN WHEN PRINTED AT A3		DRAWN	AM	CHECKED	MP
		DATE	19/11/18	DATE	19/11/18
ALL DIMENSIONS IN mm UNLESS OTHERWISE STATED. THIS DRAWING TO BE READ IN CONJUNCTION WITH OTHER RELEVANT DRAWINGS.					

TITLE		SITE ADDRESS		
PARTS LIST		VALENTINE FARM SHOGMOOR LANE SKIRMETT HENLEY-ON-THAMES RG9 6TD		
ARQIVA REF. 141568		DRG No. 304	REV 03	


ALL SCALES AS SHOWN WHEN PRINTED AT A3




ALL SCALES AS SHOWN WHEN PRINTED AT A3

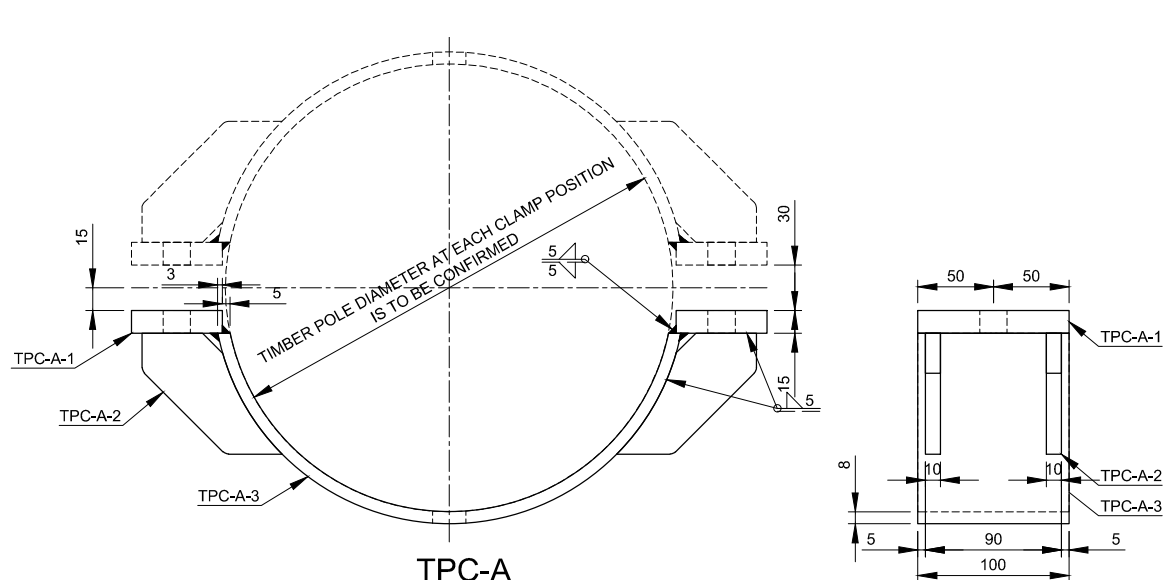

TPC-A
Scale 1:5

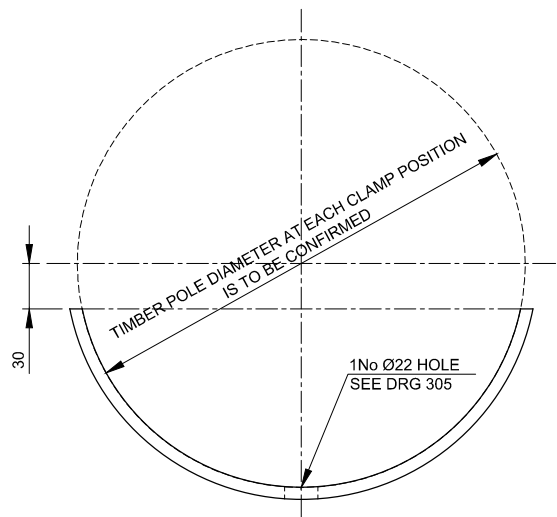


TPC-A-3 - 100x8mm PLATE
Scale 1:5

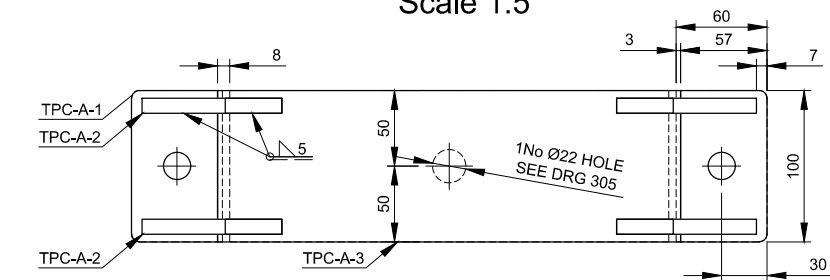


Parts list for TPC-A - 1No COLLAR (6No COLLARS REQUIRED)

Item	Part	Quantity	Part description	Length	Material	Weight
01	TPC-A-1	4	PLATE 100x60x15mm	N/A	S275J0	0.71 kg
02	TPC-A-2	8	PLATE 80x50x10mm	TBC	S275J0	0.30 kg
03	TPC-A-3	2	PLATE 100mm WIDE & 8mm THICK	TBC	S275J0	3.00 kg
04	NUT	2	M16 - HALF NUT	N/A	GRADE 8.8	-
05	BOLT	2	M16 100mm LONG SET BOLT	N/A	GRADE 8.8	-
Total Weight:						11.24 kg

- All steel hot dip galvanized
- Each BOLT to be supplied with 1 Full Nut, 1 Form E Flat Washer and 1 Spring Washer
- See DRG 500 & 501 for fabrication details of TPC-A-2 & TPC-A-3
- For fabrication notes see drawing 304

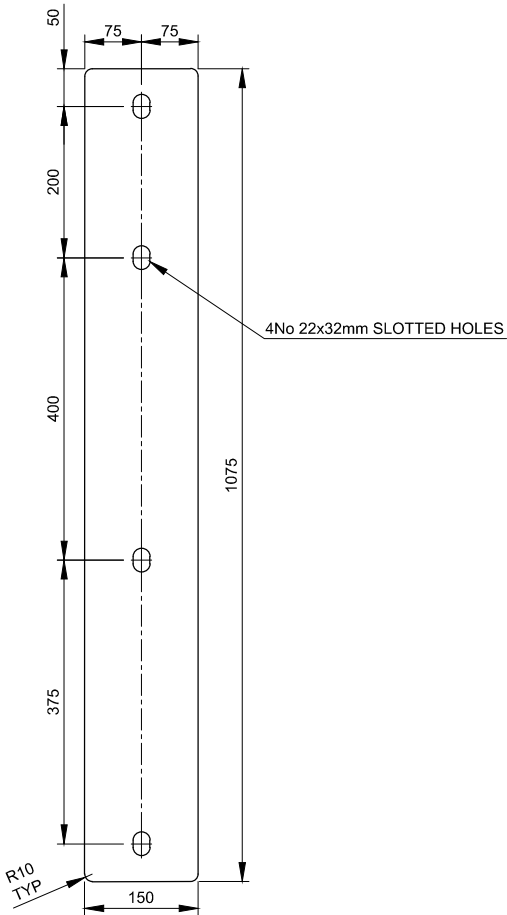

TPC-B - 15mm THICK
Scale 1:10

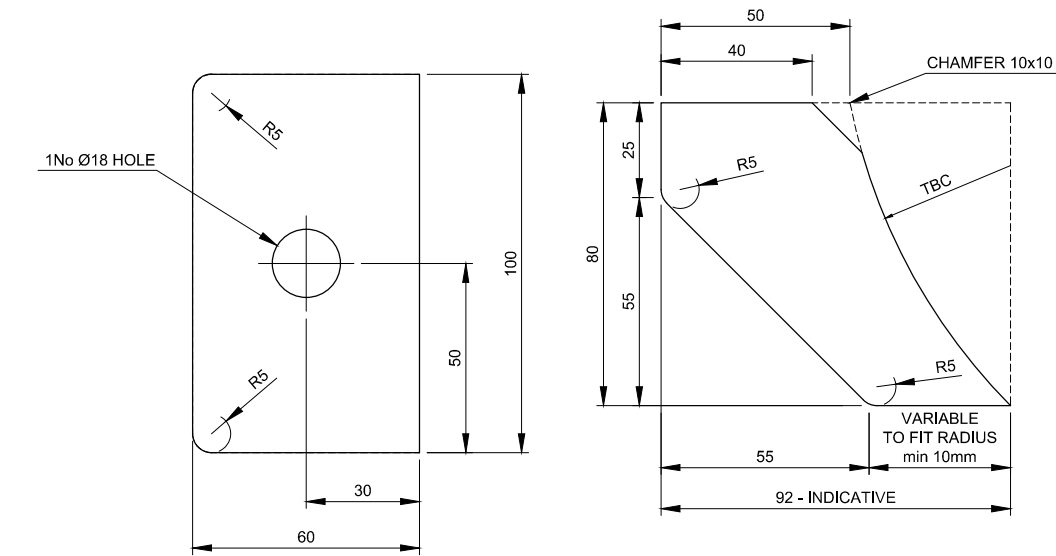


TPC-A-1 - 15mm THICK
Scale 1:2

TPC-A-2 - 10mm THICK
Scale 1:2

Parts list for TPC-B - 1No SET OF 2No INTERFACE PLATES (2No SETS REQUIRED)

Item	Part	Quantity	Part description	Length	Material	Weight
01	TPC-B	2	PLATE 1075x150x15mm	N/A	S275J0	19.00 kg
02	STUD	4	M20 STUD	500mm	GRADE 8.8	1.25 kg
03	SQ-WSH	6	M20 50x50x3mm SQUARE WASHER	N/A	GRADE 8.8	-
Total Weight:						43.00 kg

- All steel hot dip galvanized
- Each STUD to be supplied with 2 Full Nuts, 2 Half Nuts, 2 Flat Washers and 2 Spring Washers
- For fabrication notes see drawing 304

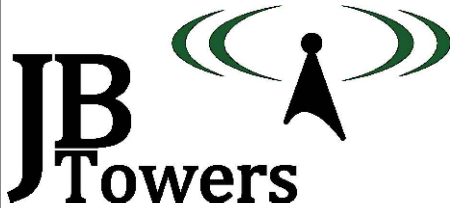

01	FIRST ISSUE	MI	13/01/21
REV	REV	BY	DATE
SCALE AS SHOWN WHEN PRINTED AT A3	DRAWN DATE 13/01/21	CHECKED DATE 13/01/21	APPROVED DATE 13/01/21
ALL DIMENSIONS IN mm UNLESS OTHERWISE STATED. THIS DRAWING TO BE READ IN CONJUNCTION WITH OTHER RELEVANT DRAWINGS.			


TITLE
SKIRMETT
SPLICE COLLAR; INTERFACE
PLATE
PARTS: TPC-A; TPC-B

SITE ADDRESS
VALENTINE FARM
SHOGMOOR LANE
SKIRMETT
HENLEY-ON-THAMES
RG9 6TD
ARQIVA REF.
141568
DRG No.
305
REV
01


ALL SCALES AS SHOWN WHEN PRINTED AT A3



ALL SCALES AS SHOWN WHEN PRINTED AT A3

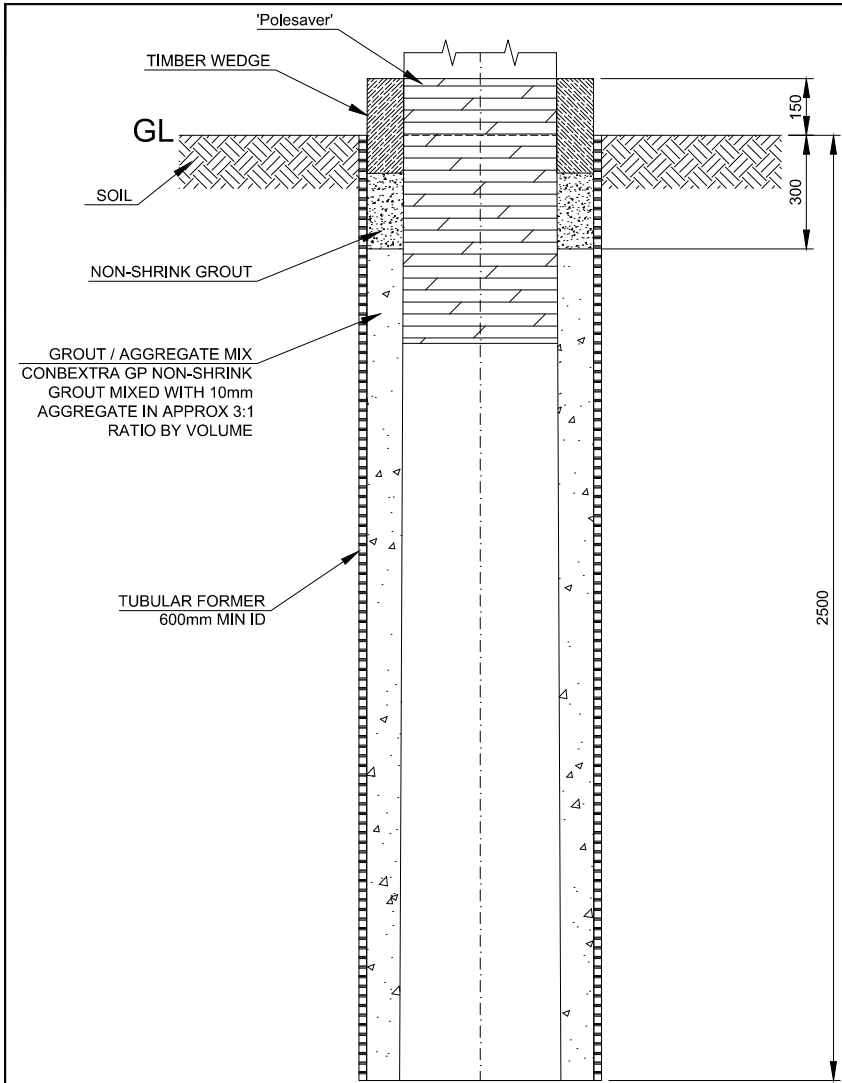


POROPOSED INSTALLATION
ELEVATION
Scale 1:20

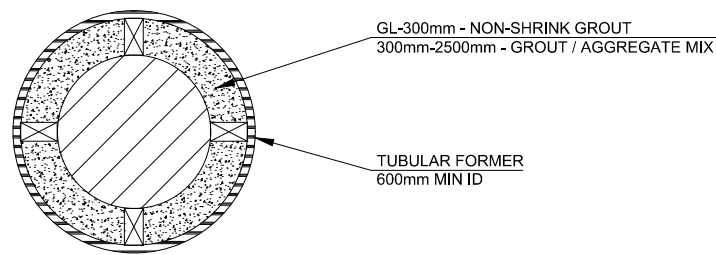


POROPOSED INSTALLATION
PLAN VIEW
Scale 1:20

TIMBER POLE INSTALLATION:


1. REFER TO DRAWING 200 FOR TIMBER POLE ORIENTATION
2. HOLE TO BE AUGURED TO REQUIRED DEPTH
3. IF REQUIRED A TUBULAR FORMER IS TO BE INSERTED AND THE ANNULUS BETWEEN THE FORMER AND THE SOIL GROUTED UP
4. POLE TO BE WRAPPED IN 'POLESAVER' AND INSTALLED AND LEVELLED IN OPENING. TIMBERS TO BE USED TO HOLD POLE IN POSITION
5. ANNULUS SHALL BE FILLED WITH GROUT / AGGREGATE MIX TO 300mm BELOW GL
6. TOP 300mm SHALL BE FILLED WITH NON-SHRINK GROUT. A 1:60 FALL SHALL BE FORMED AROUND TIMBER POLE TO ALLOW WATER TO DRAIN AWAY FROM POLE
7. ONCE GROUT HAS CURED REMOVE TIMBER WEDGES AND FILL REMAINING VOIDS WITH NON-SHRINK GROUT

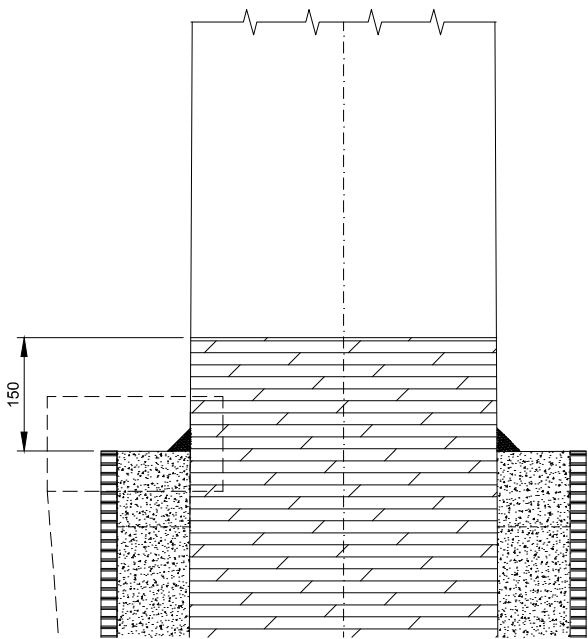

WATER PROOFING
Scale 1:10

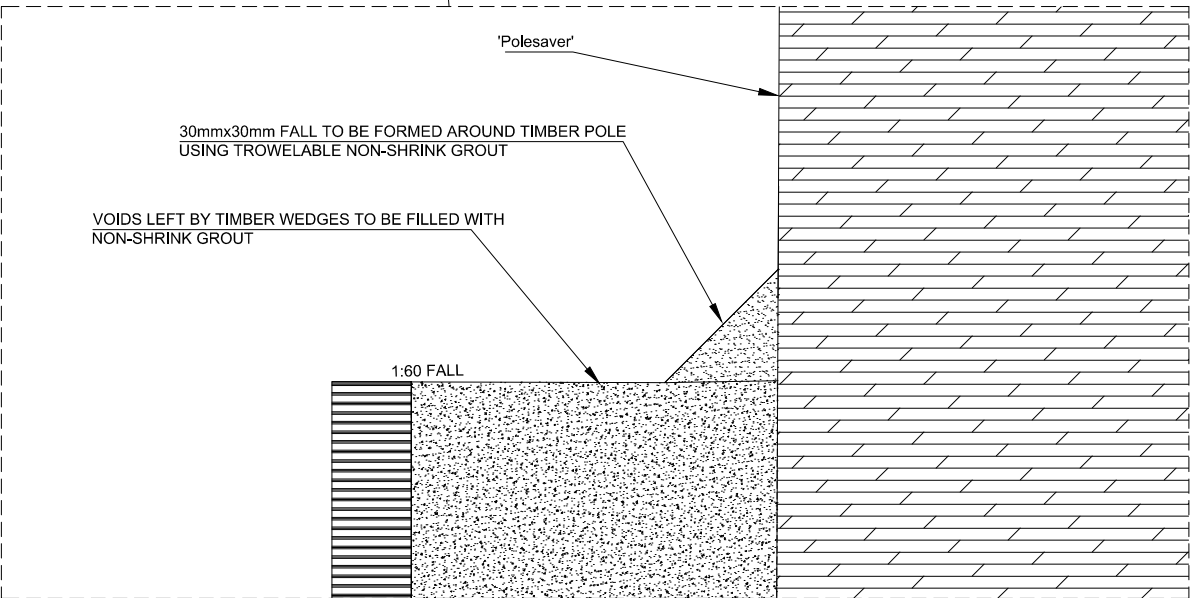

ENLARGED DETAIL
Scale 1:2

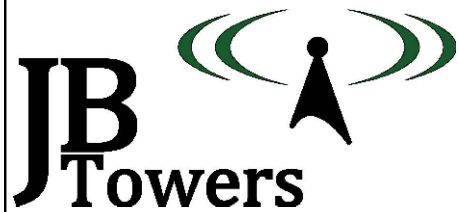

01	FIRST ISSUE	MI	12/01/21
REV	REV	BY	DATE
SCALE AS SHOWN WHEN PRINTED AT A3	DRAWN DATE 12/01/21	CHECKED DATE 12/01/21	APPROVED DATE 12/01/21
ALL DIMENSIONS IN mm UNLESS OTHERWISE STATED. THIS DRAWING TO BE READ IN CONJUNCTION WITH OTHER RELEVANT DRAWINGS.			

TITLE
SKIRMETT
TIMBER POLE FOUNDATION
DETAILS


SITE ADDRESS
VALENTINE FARM
SHOGMOOR LANE
SKIRMETT
HENLEY-ON-THAMES
RG9 6TD

ARQIVA REF.
141568
DRG No.
400
REV
01

ALL SCALES AS SHOWN WHEN PRINTED AT A3





ALL SCALES AS SHOWN WHEN PRINTED AT A3

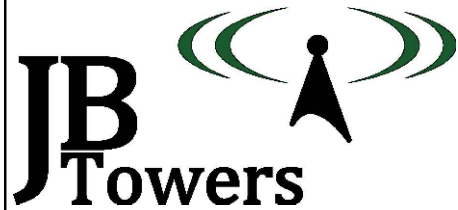

01	FIRST ISSUE			MI	13/01/21
REV	REV			BY	DATE
SCALE AS SHOWN WHEN PRINTED AT A3		DRAWN MI DATE 13/01/21	CHECKED MP DATE 13/01/21	APPROVED JBT DATE 13/01/21	
ALL DIMENSIONS IN mm UNLESS OTHERWISE STATED. THIS DRAWING TO BE READ IN CONJUNCTION WITH OTHER RELEVANT DRAWINGS.					

TITLE
SKIRMETT
PERMANENT STEPS
ENLARGED DETAIL

SITE ADDRESS		
VALENTINE FARM		
SHOGMOOR LANE		
SKIRMETT		
HENLEY-ON-THAMES		
RG9 6TD		
ARQIVA REF.	DRG No.	REV
141568	401	01

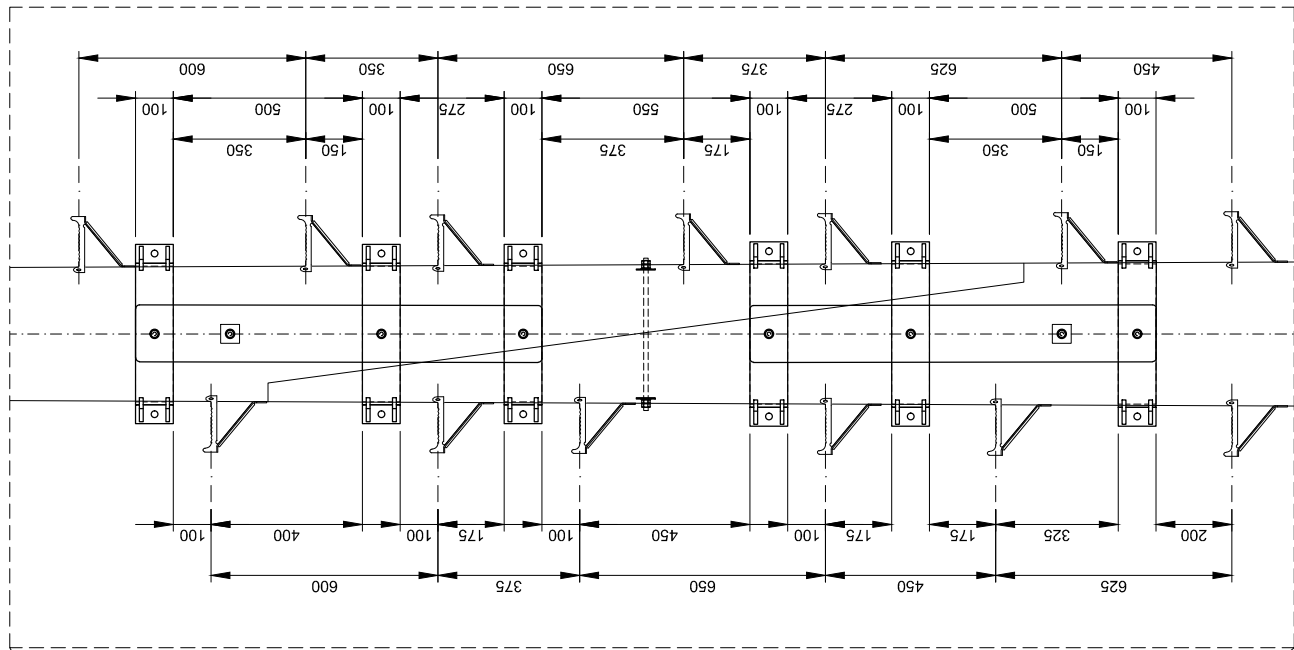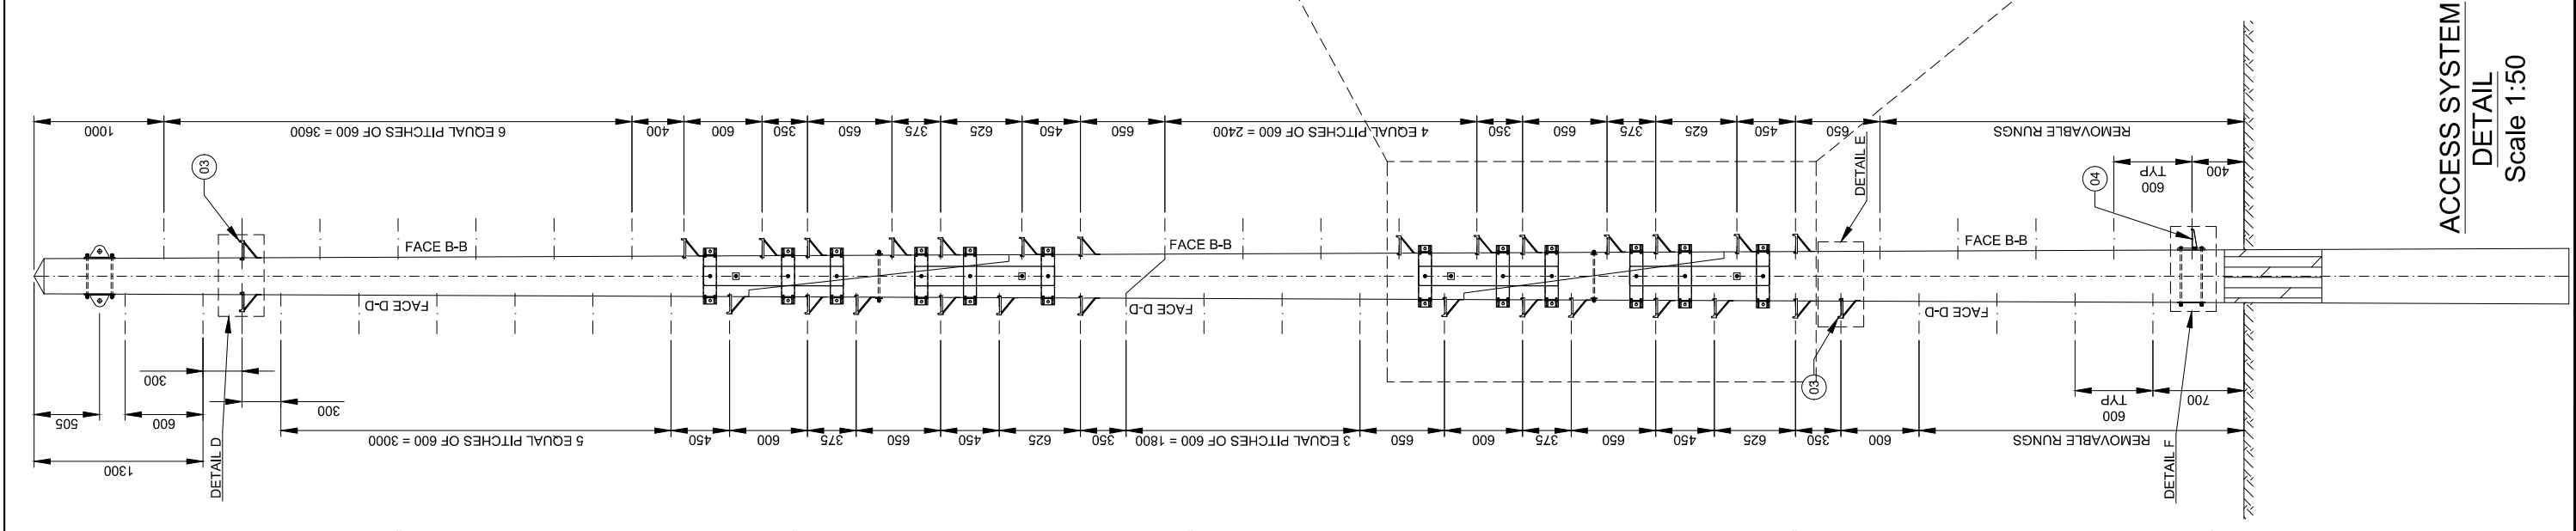

ALL SCALES AS SHOWN WHEN PRINTED AT A3



ALL SCALES AS SHOWN WHEN PRINTED AT A3