
 
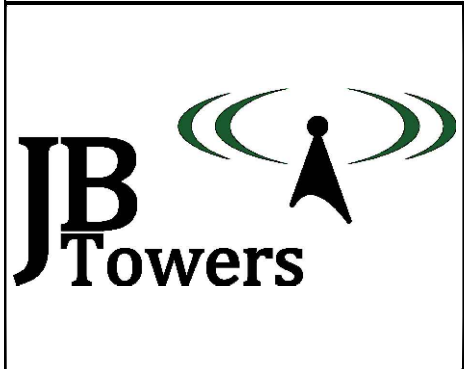


DRAWING ISSUE SHEET

[illegible]

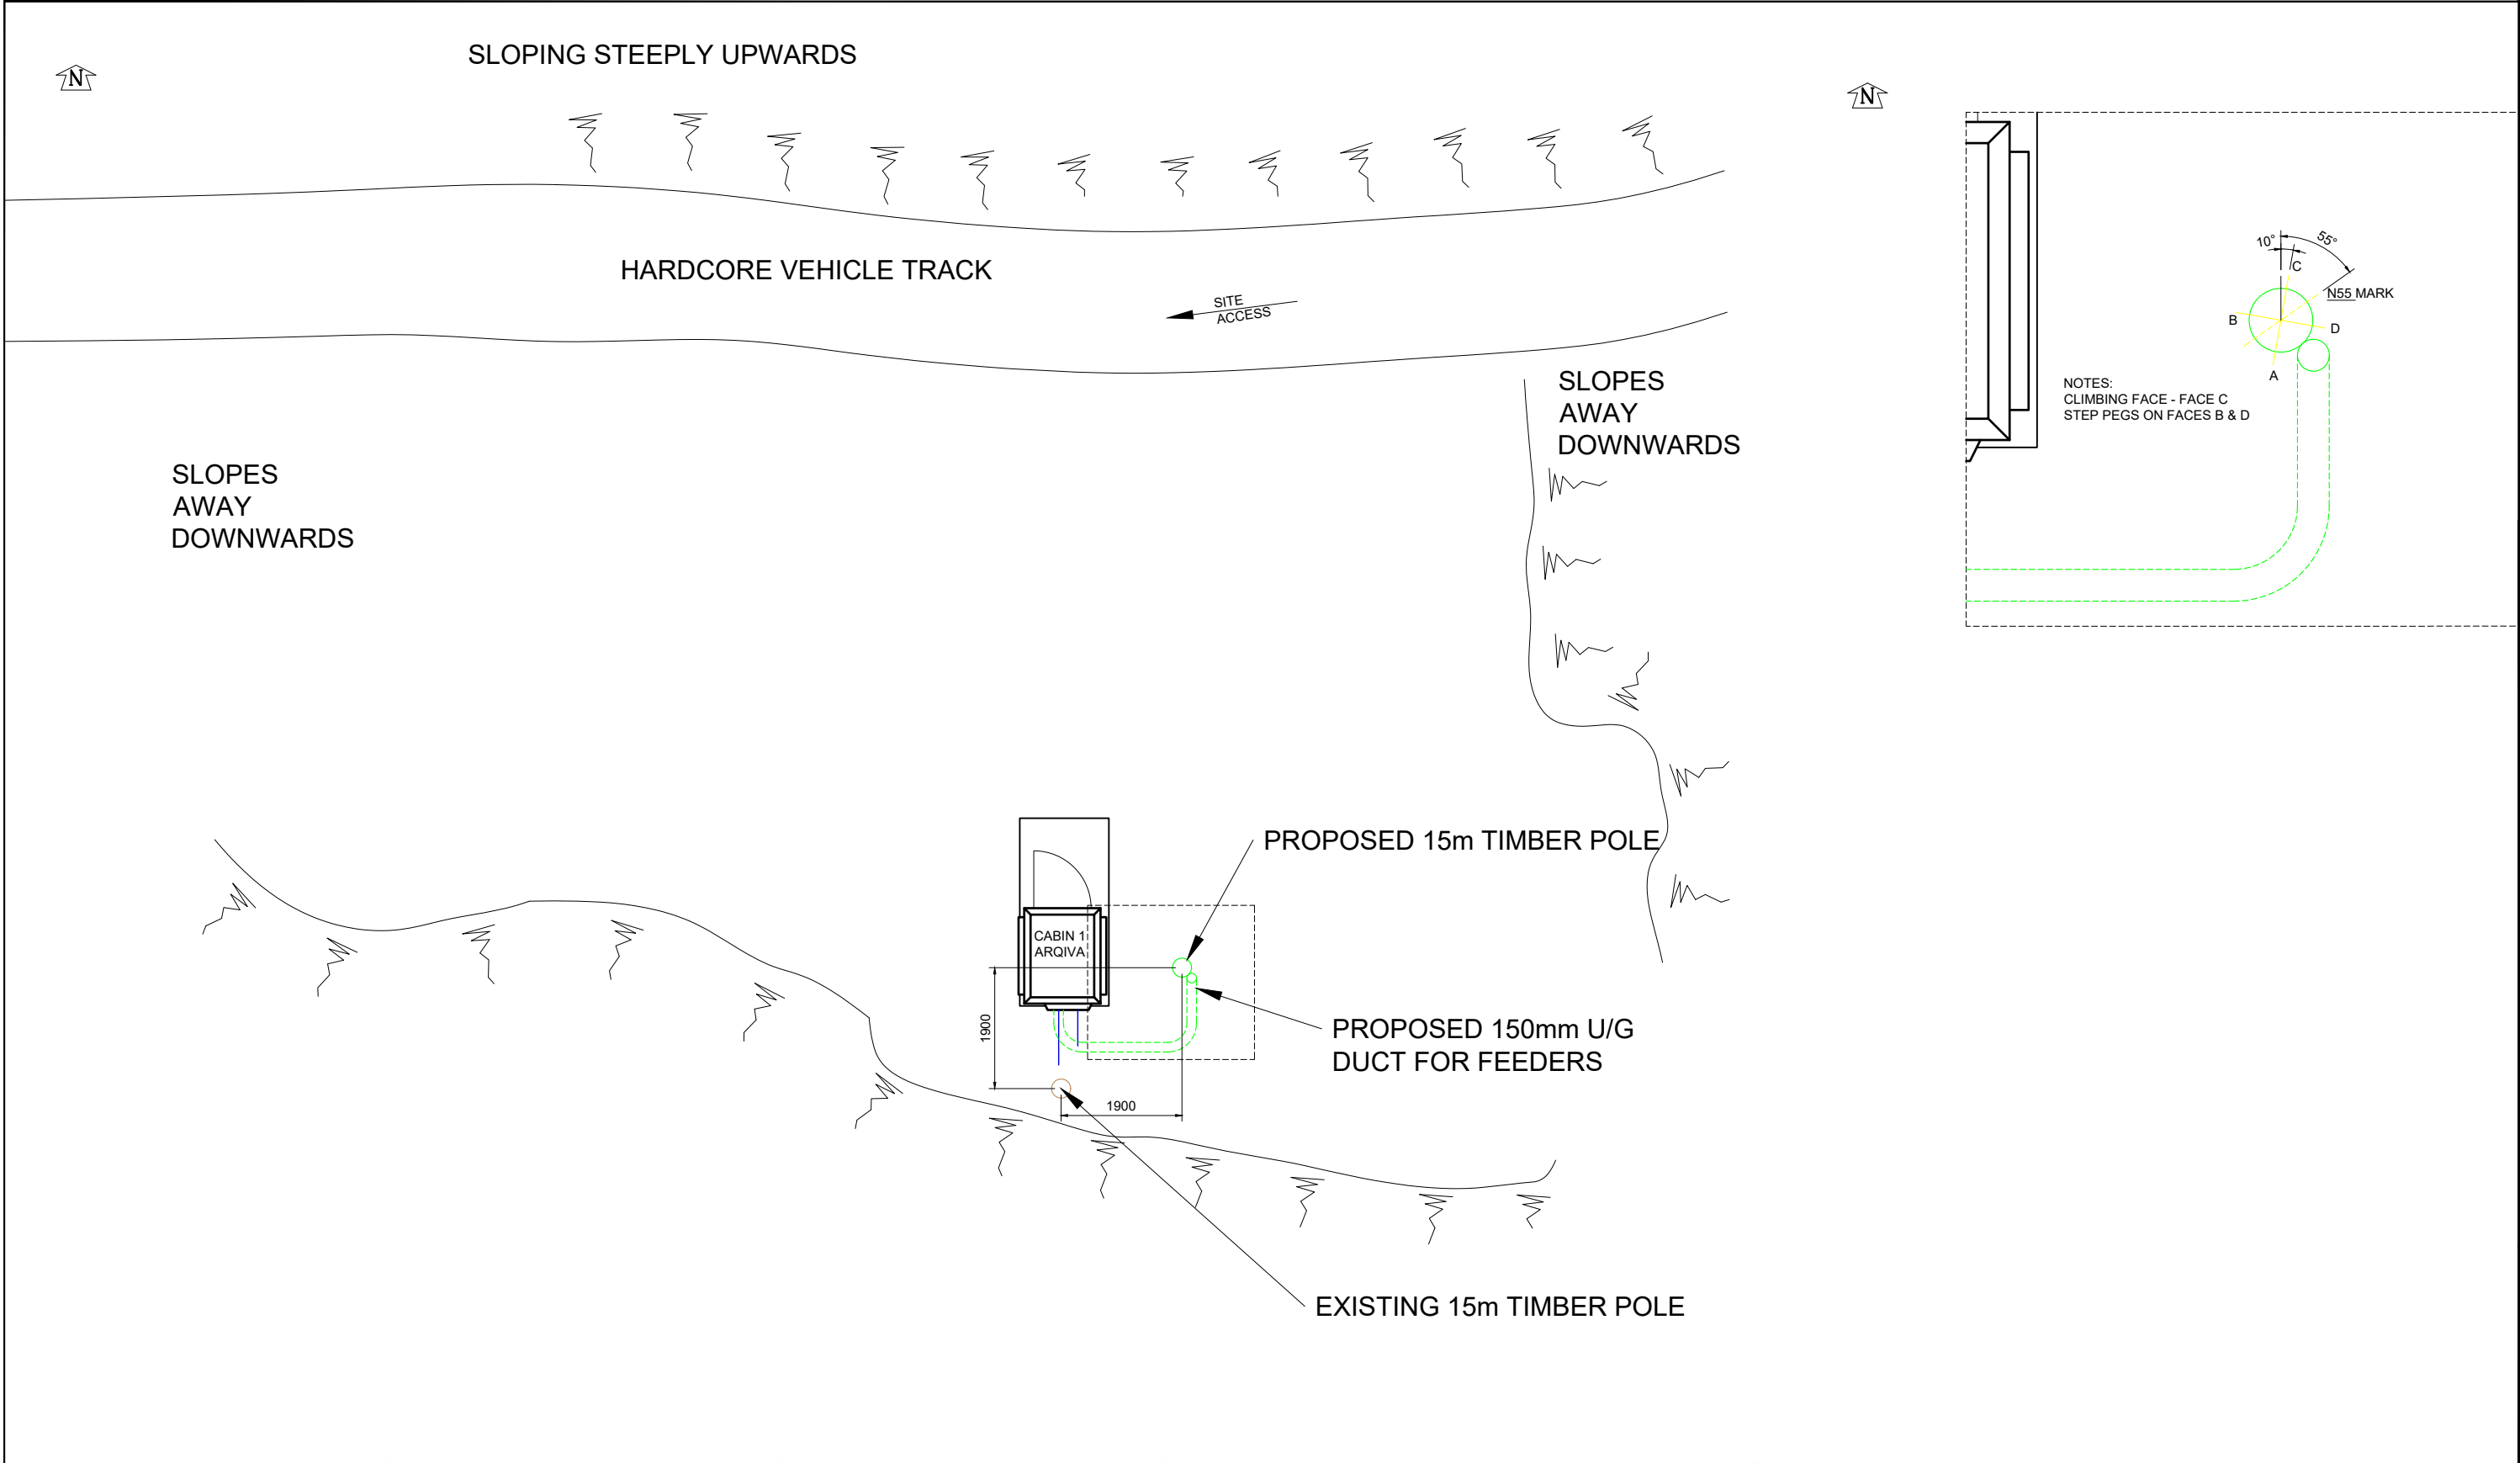


02	PROPOSED TIMBER POLE POSITION UPDATED	AM	27/06/19
01	FIRST ISSUE	TT	24/06/19
REV	REV	BY	DATE
SCALE AS SHOWN WHEN PRINTED AT A3	DRAWN DATE 24/06/19	CHECKED DATE 24/06/19	APPROVED DATE 24/06/19
ALL DIMENSIONS IN mm UNLESS OTHERWISE STATED. THIS DRAWING TO BE READ IN CONJUNCTION WITH OTHER RELEVANT DRAWINGS.			

TITLE
STRONTIAN
SITE PLAN

SITE ADDRESS		
STRONTIAN ACHARACLE HIGHLAND PH36 4JB		
ARQIVA REF. 141617	DRG No. 100	REV 02

ALL SCALES AS SHOWN WHEN PRINTED AT A3

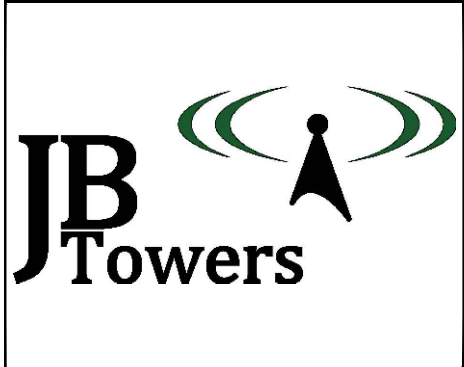


01	FIRST ISSUE			TT	24/06/19
REV	REV			BY	DATE
SCALE AS SHOWN WHEN PRINTED AT A3	DRAWN AM	CHECKED MP	APPROVED JBT		
	DATE 24/06/19	DATE 24/06/19	DATE 24/06/19		
ALL DIMENSIONS IN mm UNLESS OTHERWISE STATED. THIS DRAWING TO BE READ IN CONJUNCTION WITH OTHER RELEVANT DRAWINGS.					

TITLE

STRONTIAN

GENERAL ARRANGEMENT
SHEET 1 OF 3

SITE ADDRESS		
STRONTIAN ACHARACLE HIGHLAND PH36 4JB		
ARQIVA REF. 141917	DRG No. 200	REV 01

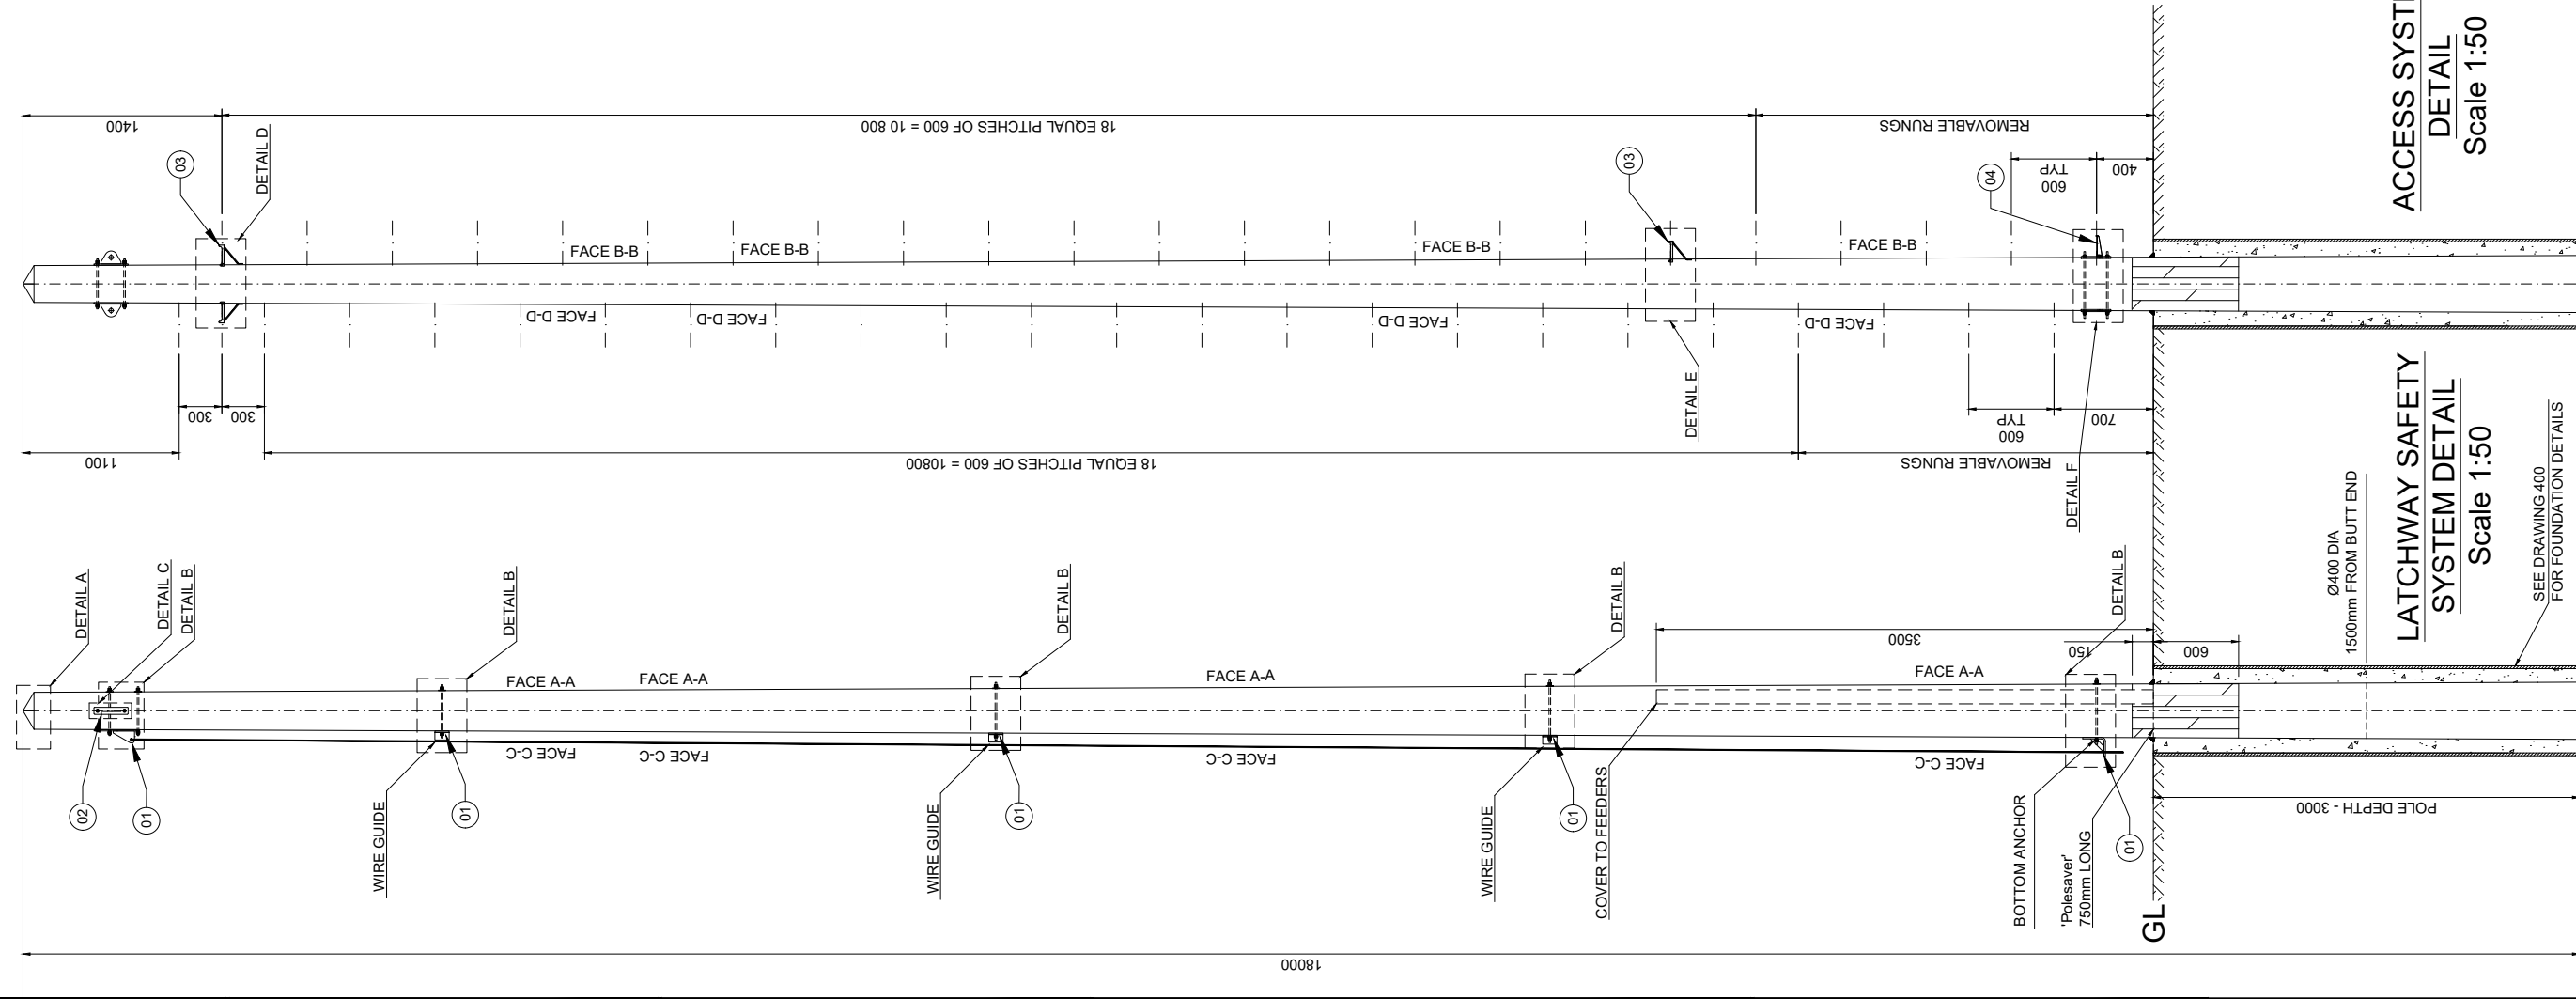REV
01

POLE ORIENTATION

Scale 1:20

NOTES

1. SEE DRAWING 302 FOR PARTS LIST
2. ALL BOLTS TO BE CUT ON SITE TO EXTEND MAX 10mm BEYOND THE NUT WHEN TIGHTENED UNO.
3. ALL SITE DRILLED HOLE/CUT ENDS TO BE TREATED WITH METAFILUX 70-40 ZINC PASTE FOLLOWED BY 1 COAT OF 7-42 ZINC ALU OR 70-16 ALUMINIUM SPRAY

TIMBER POLE

1. POLE TO BE SUPPLIED IN ACCORDANCE WITH BS EN14229 & SHALL HAVE MIN. CHARACTERISTIC BENDING STRENGTH OF 30kN/m² & MIN. YOUNG'S MODULUS (PARALLEL TO GRAIN) OF 10kN/mm².
2. MARKINGS ON FINISHED POLE SHALL BE AT 4m FROM BUTT AND COMPLY WITH BS EN 14229 UNO
3. AS FAR AS PRACTICABLE ALL CUTTING, SCARFING & DRILLING TO BE DONE BEFORE CREOSOTING. IF NOT ALL CUT, DRILLED & SCARFED SURFACES TO BE COATED WITH A MIXTURE OF CREOSOTE & TAR.
4. POLE TO BE PRESSURE IMPREGNATED WITH CREOSOTE IN ACCORDANCE WITH BS EN 14229
5. MINIMUM DIAMETERS
TOP - Ø210mm
BOTTOM - Ø410mm
6. 18m LONG POLE TO BE SOURCED BY TRIMMING 19m LONG POLE BY 1m AT THE TOP


PLANTING

1. CAT SCANNER IS TO BE USED IN ORDER TO CONFIRM THE POSITIONS OF BURIED SERVICES.
2. SEE DRAWING 400 FOR FOUNDATION DETAILS.
3. TIMBER POLE TO BE PLANTED WITH **N55** MARKING AT 4m FROM BUT FACING 55° FROM NORTH (CLOCKWISE)

ALL SCALES AS SHOWN WHEN PRINTED AT A3



ALL SCALES AS SHOWN WHEN PRINTED AT A3

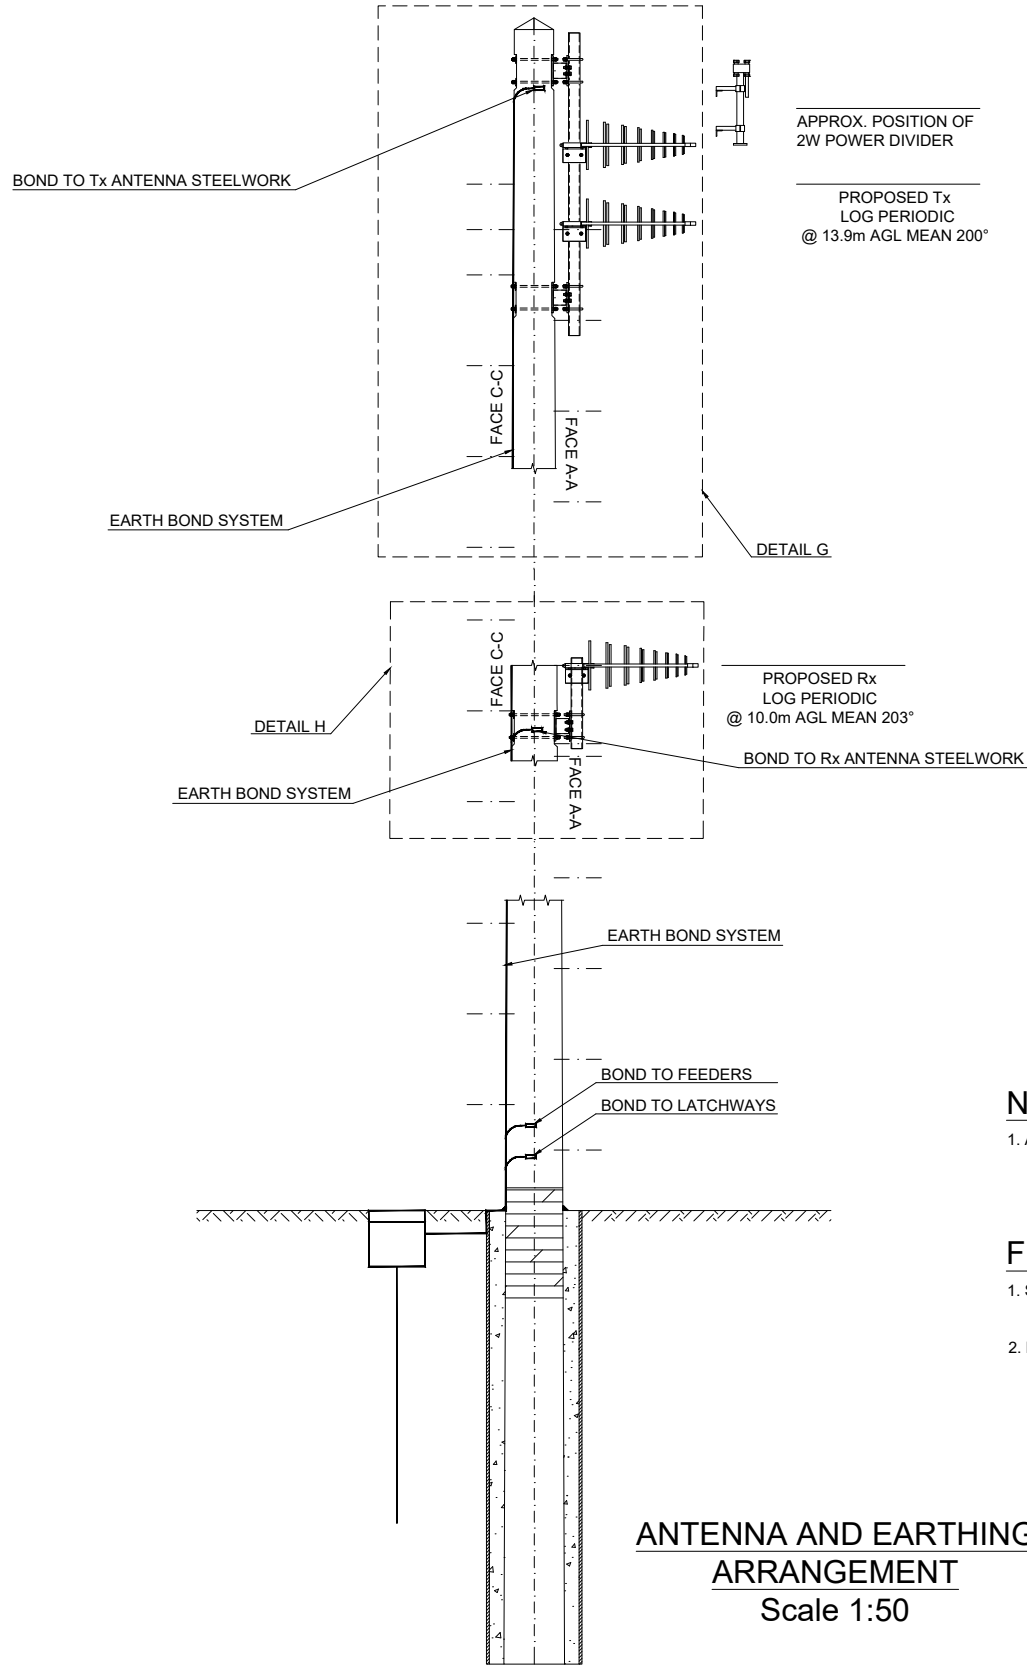

ANTENNA AND EARTHING
ARRANGEMENT
Scale 1:50

NOTES


1. AS FAR AS IS PRACTICABLE ALL CUTTING SCARFING AND DRILLING TO BE DONE BEFORE CREOSOTING. WHERE THIS IS NOT POSSIBLE ALL CUT, DRILLED, AND SCARFED SURFACES TO BE COATED WITH A MIXTURE OF CREOSOTE AND TAR

FEEDERS


1. SUPPLY OF FEEDERS BY OTHERS
LCF78-50 TO Tx ANTENNA &
LCF12-50 TO Rx ANTENNA
2. FEEDERS FIXED AT 1000mm CENTRES

EARTHING

1. CONNECT EARTH BOND TO NEW EARTHING SYSTEM
2. MAXIMUM VALUE FOR GROUND RESISTANCE TO BE 10 OHMS
3. CABLE OR TAPE TO BE FIXED TO POLE AT 1000mm CENTRES
4. EARTHING SHOULD COMPLY WITH ARQIVA'S DOCUMENT BOS147

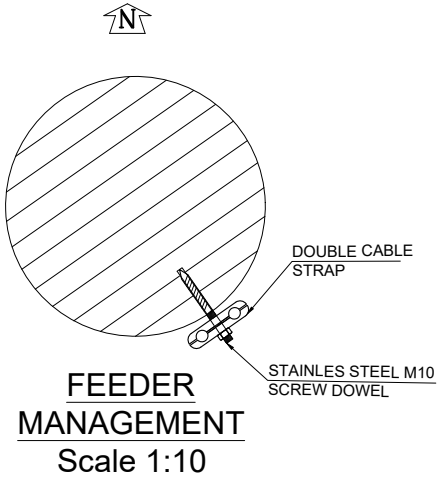

FEEDER
MANAGEMENT
Scale 1:10

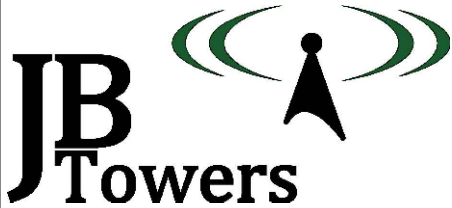

02	FACE LABELS ADDED			AM	27/06/19
01	FIRST ISSUE			TT	24/06/19
REV	REV			BY	DATE
SCALE AS SHOWN		DRAWN	AM	CHECKED	MP
WHEN PRINTED AT A3		DATE	24/06/19	DATE	24/06/19
APPROVED		JBT			
ALL DIMENSIONS IN mm UNLESS OTHERWISE STATED. THIS DRAWING TO BE READ IN CONJUNCTION WITH OTHER RELEVANT DRAWINGS.					

TITLE


STRONTIAN

GENERAL ARRANGEMENT
SHEET 2 OF 3

SITE ADDRESS STRONTIAN ACHARACLE HIGHLAND PH36 4JB		
ARQIVA REF. 141617	DRG No. 200	REV 02


ALL SCALES AS SHOWN WHEN PRINTED AT A3



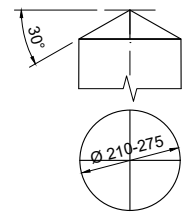


NOTES:
 1. A SINGLE COAT OF TIMBER COMPATIBLE BITUMINOUS PAINT (E.G. BIRD BRAND BLACK BITUMINOUS PAINT OR SIMILAR APPROVED PRODUCT) TO BE APPLIED TO THE UPPER SURFACES AT THE TOP OF THE POLE.
 2. PAINT TO BE APPLIED ON SITE JUST BEFORE ERECTION
 FORM: 4 WAY PYRAMID / CONE


DETAIL A - TIMBER POLE TOP
 Scale 1:20

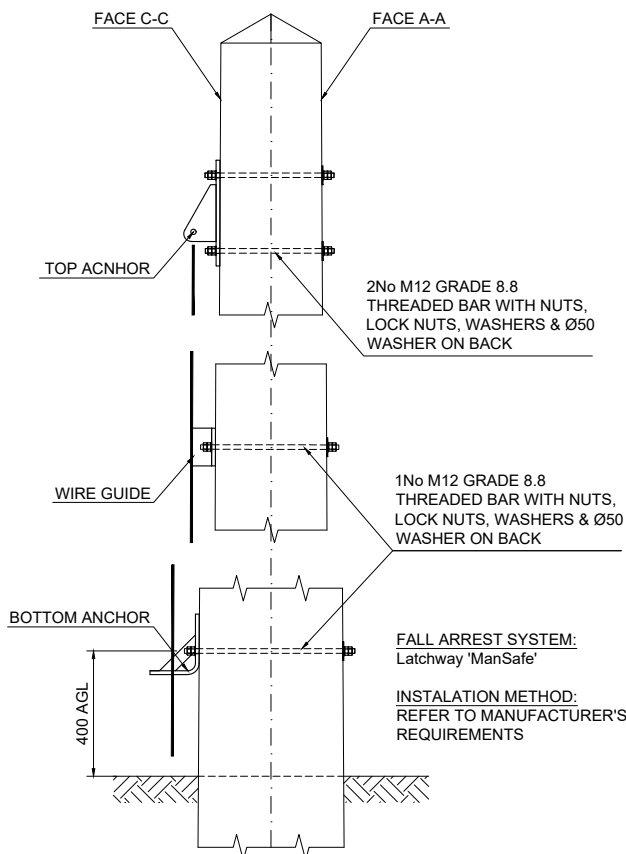


DETAIL B - FALL ARREST SYSTEM
 Scale 1:20

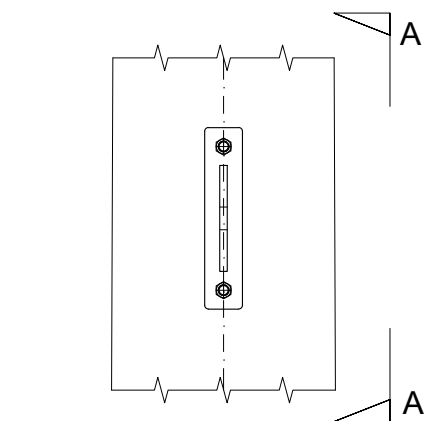


DETAIL C - FALL ARREST ATTACHMENT POINT
 Scale 1:10

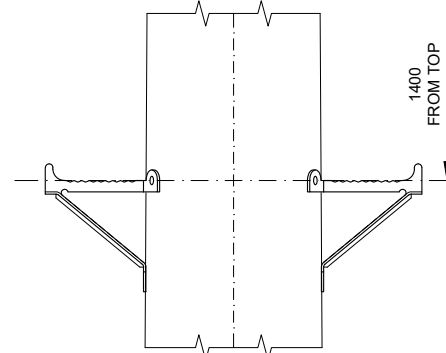


DETAIL D - ANTENNA ACCESS CLIMBING STEP
 Scale 1:10

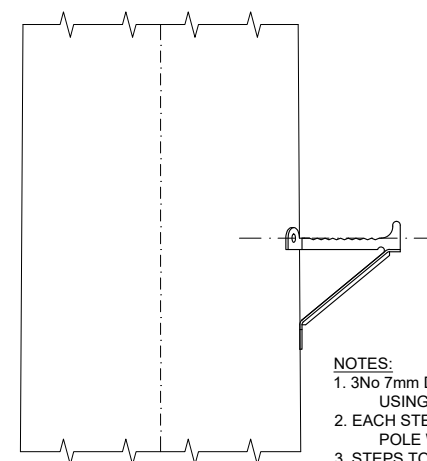

DETAIL E - PERMANENT CLIMBING STEPS
 Scale 1:10

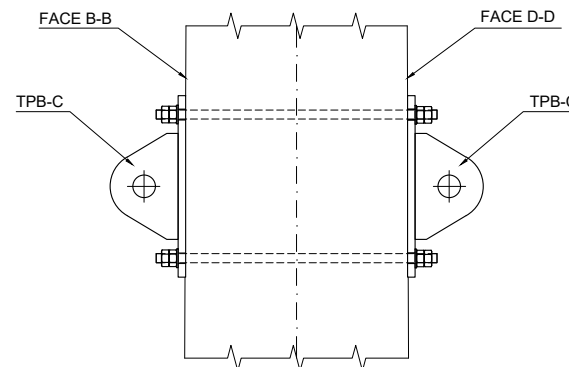


VIEW A-A
 Scale 1:10

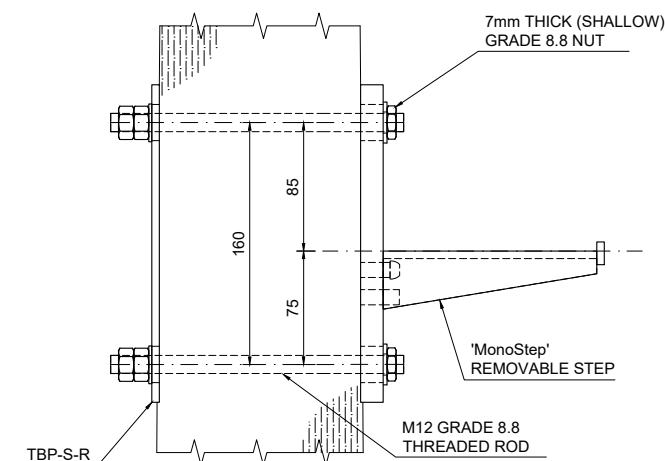


DETAIL F - REMOVABLE CLIMBING STEPS
 Scale 1:5

ALL SCALES AS SHOWN WHEN PRINTED AT A3

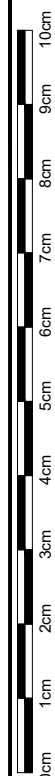

ALL SCALES AS SHOWN WHEN PRINTED AT A3

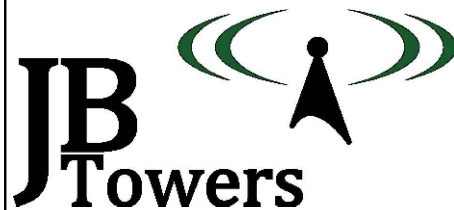

01	FIRST ISSUE	TT	24/06/19
REV	REV	BY	DATE
SCALE AS SHOWN WHEN PRINTED AT A3	DRAWN AM	CHECKED MP	APPROVED JBT
	DATE 24/06/19	DATE 24/06/19	DATE 24/06/19
ALL DIMENSIONS IN mm UNLESS OTHERWISE STATED. THIS DRAWING TO BE READ IN CONJUNCTION WITH OTHER RELEVANT DRAWINGS.			


TITLE
 STRONTIAN
 GENERAL ARRANGEMENT
 SHEET 3 OF 3

SITE ADDRESS
 STRONTIAN
 ACHARACLE
 HIGHLAND
 PH36 4JB

ARQIVA REF.
 141617

DRG No.
 200

REV
 01

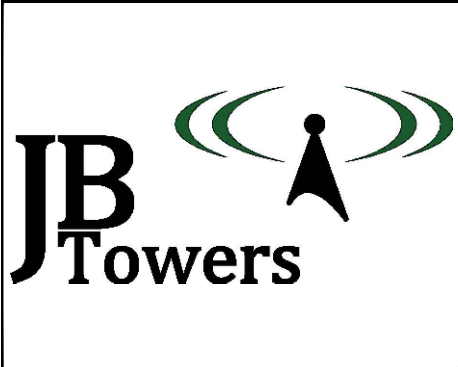

01	FIRST ISSUE			TT	24/06/19
REV	REV			BY	DATE
SCALE AS SHOWN WHEN PRINTED AT A3	DRAWN	AM	CHECKED	MP	APPROVED JBT
	DATE	24/06/19	DATE	24/06/19	DATE 24/06/19
ALL DIMENSIONS IN mm UNLESS OTHERWISE STATED. THIS DRAWING TO BE READ IN CONJUNCTION WITH OTHER RELEVANT DRAWINGS.					

TITLE

STRONTIAN


TIMBER POLE HOLE SET OUT

SHEET 1 OF 2

SITE ADDRESS

STRONTIAN
ACHARACLE
HIGHLAND
PH36 4JB


ARQIVA REF. 141617	DRG No. 201	REV 01
-----------------------	----------------	-----------

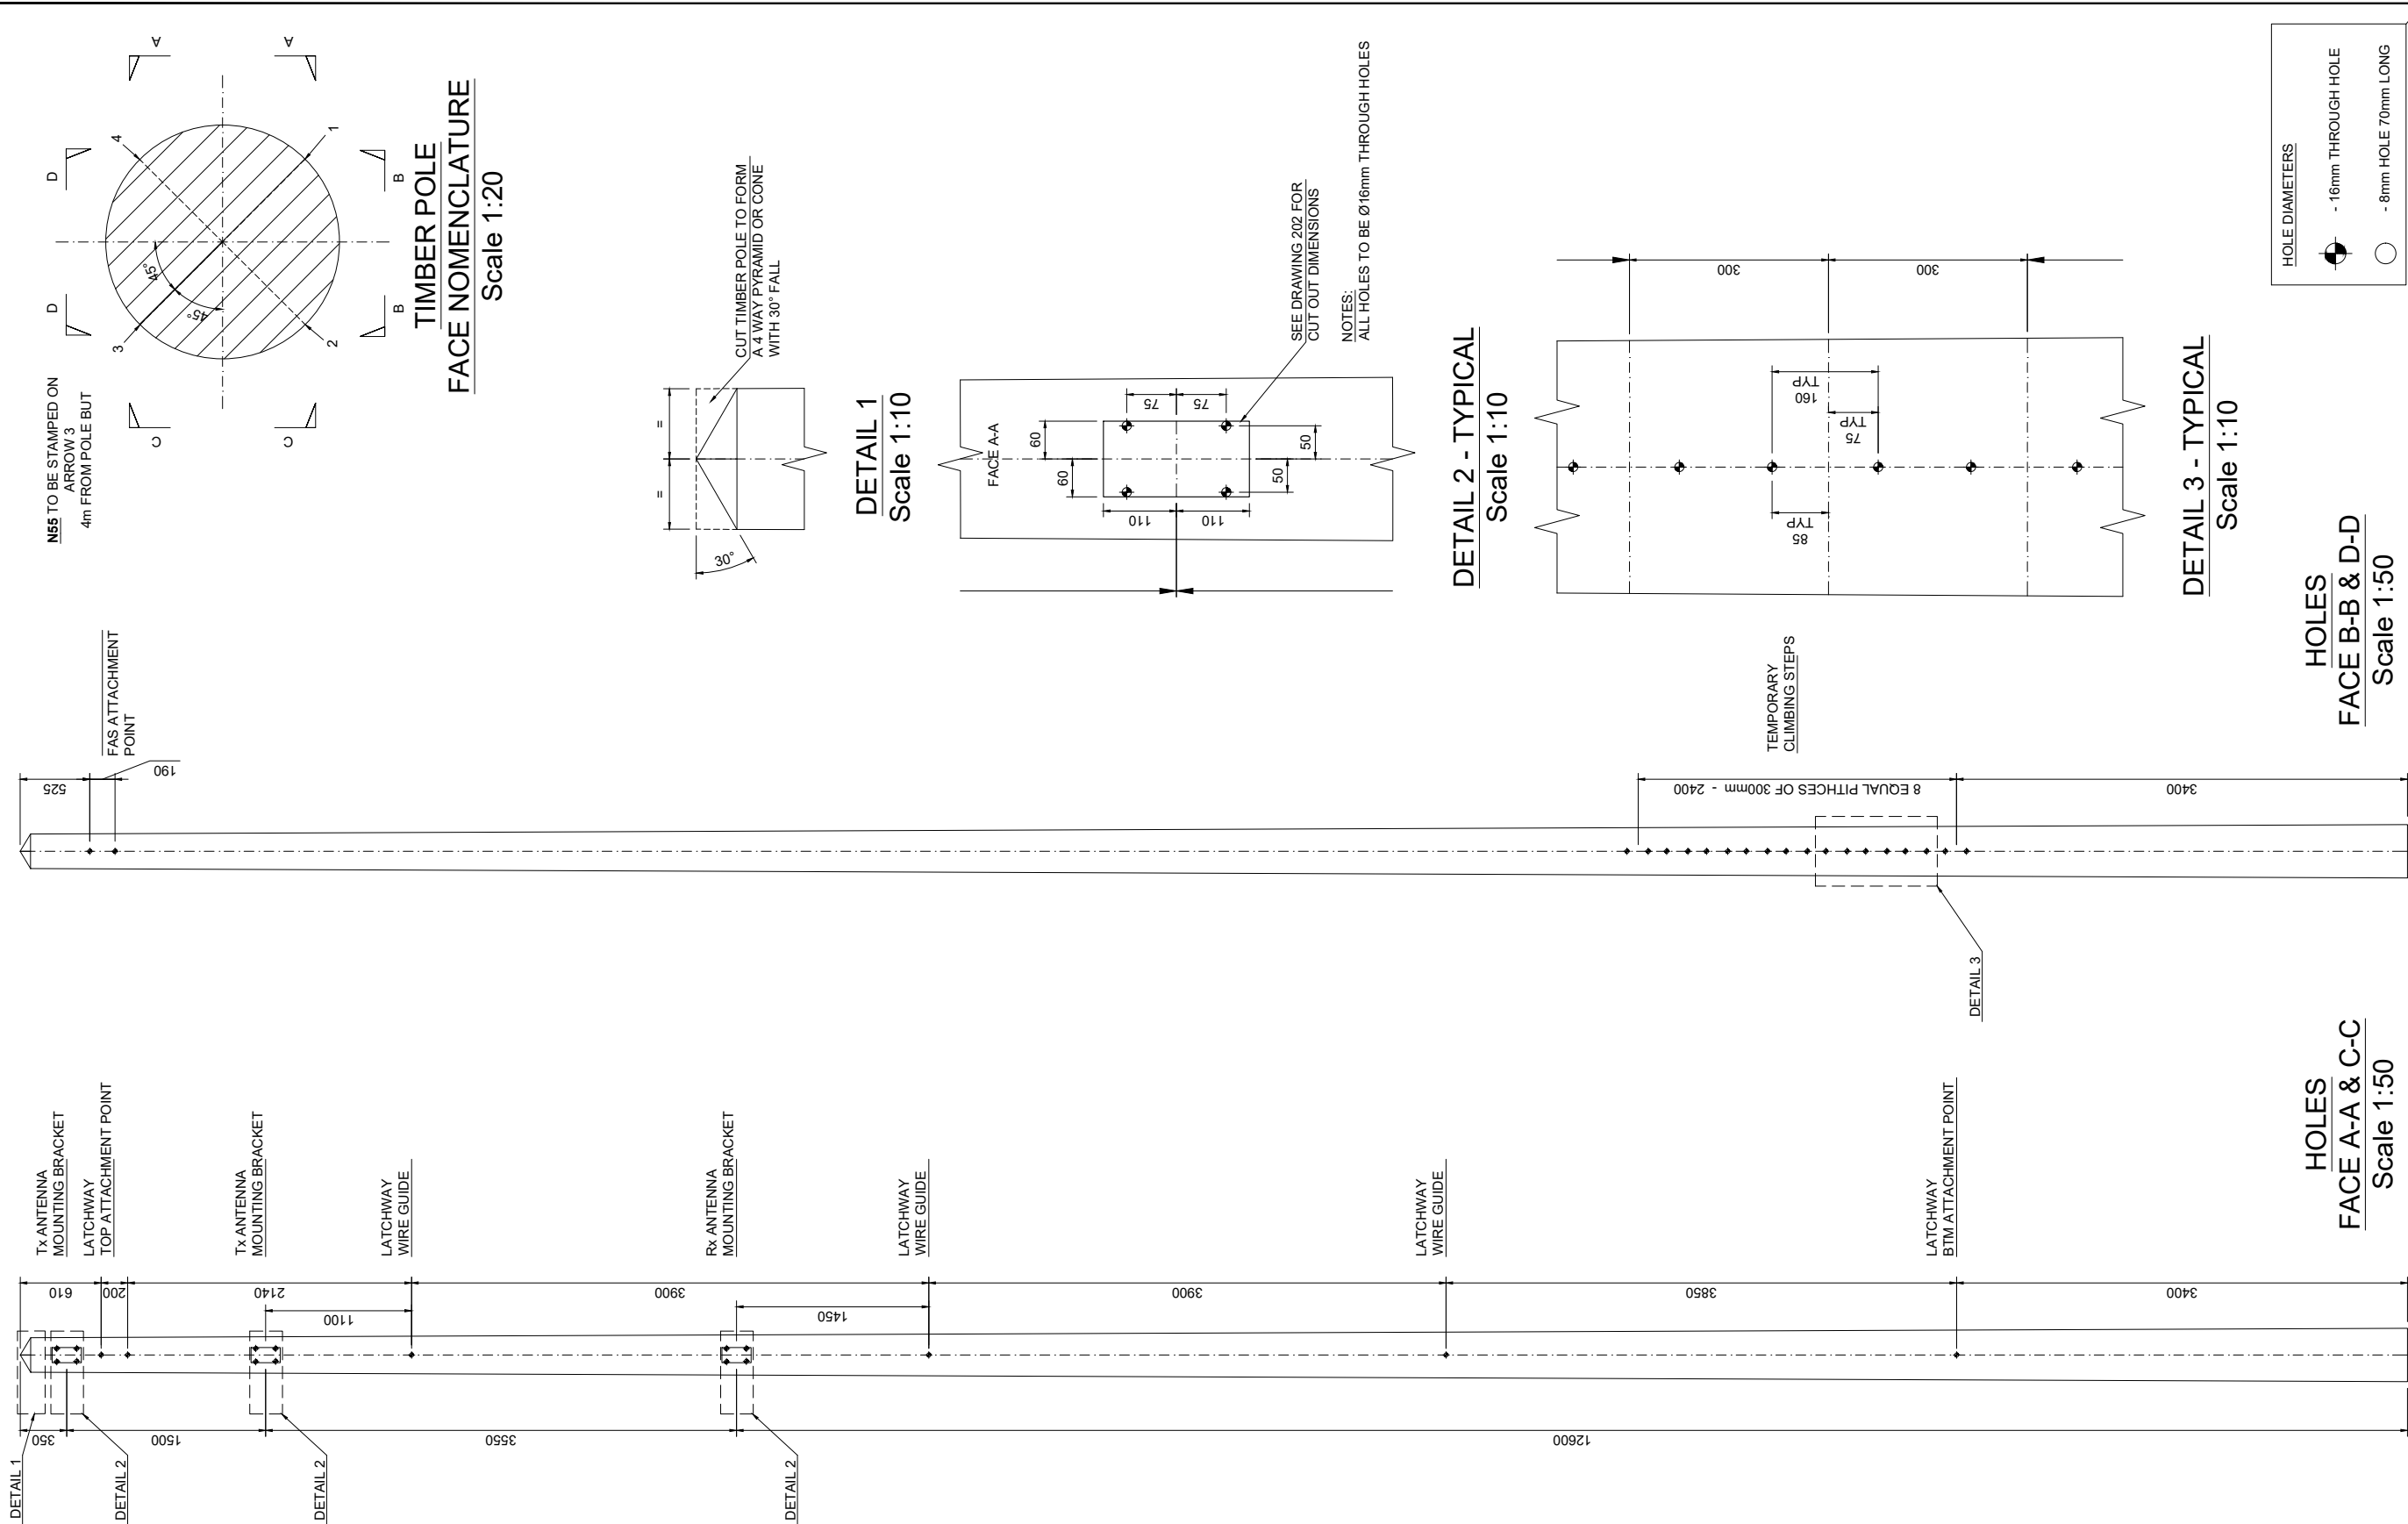REV
01

ALL SCALES AS SHOWN WHEN PRINTED AT A3	0mm	1cm	2cm	3cm	4cm	5cm	6cm	7cm	8cm	9cm	10cm
ALL SCALES AS SHOWN WHEN PRINTED AT A3	0mm	1cm	2cm	3cm	4cm	5cm	6cm	7cm	8cm	9cm	10cm

ALL SCALES AS SHOWN WHEN PRINTED AT A3

ALL SCALES AS SHOWN WHEN PRINTED AT A3

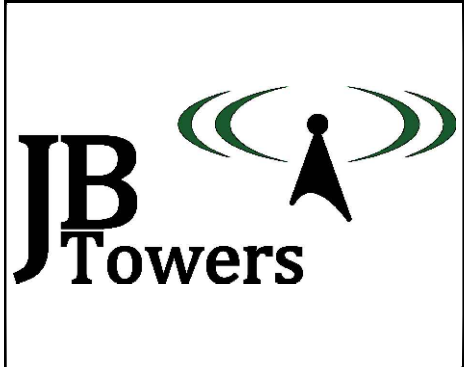


01	FIRST ISSUE			TT	24/06/19
REV	REV			BY	DATE
SCALE AS SHOWN WHEN PRINTED AT A3	DRAWN AM	CHECKED MP	APPROVED JBT		
	DATE 24/06/19	DATE 24/06/19	DATE 24/06/19		
ALL DIMENSIONS IN mm UNLESS OTHERWISE STATED. THIS DRAWING TO BE READ IN CONJUNCTION WITH OTHER RELEVANT DRAWINGS.					

STRONTIAN

TIMBER POLE HOLE SET OUT
SHEET 2 OF 2

STRONTIAN
ACHARACLE
HIGHLAND
PH36 4JB

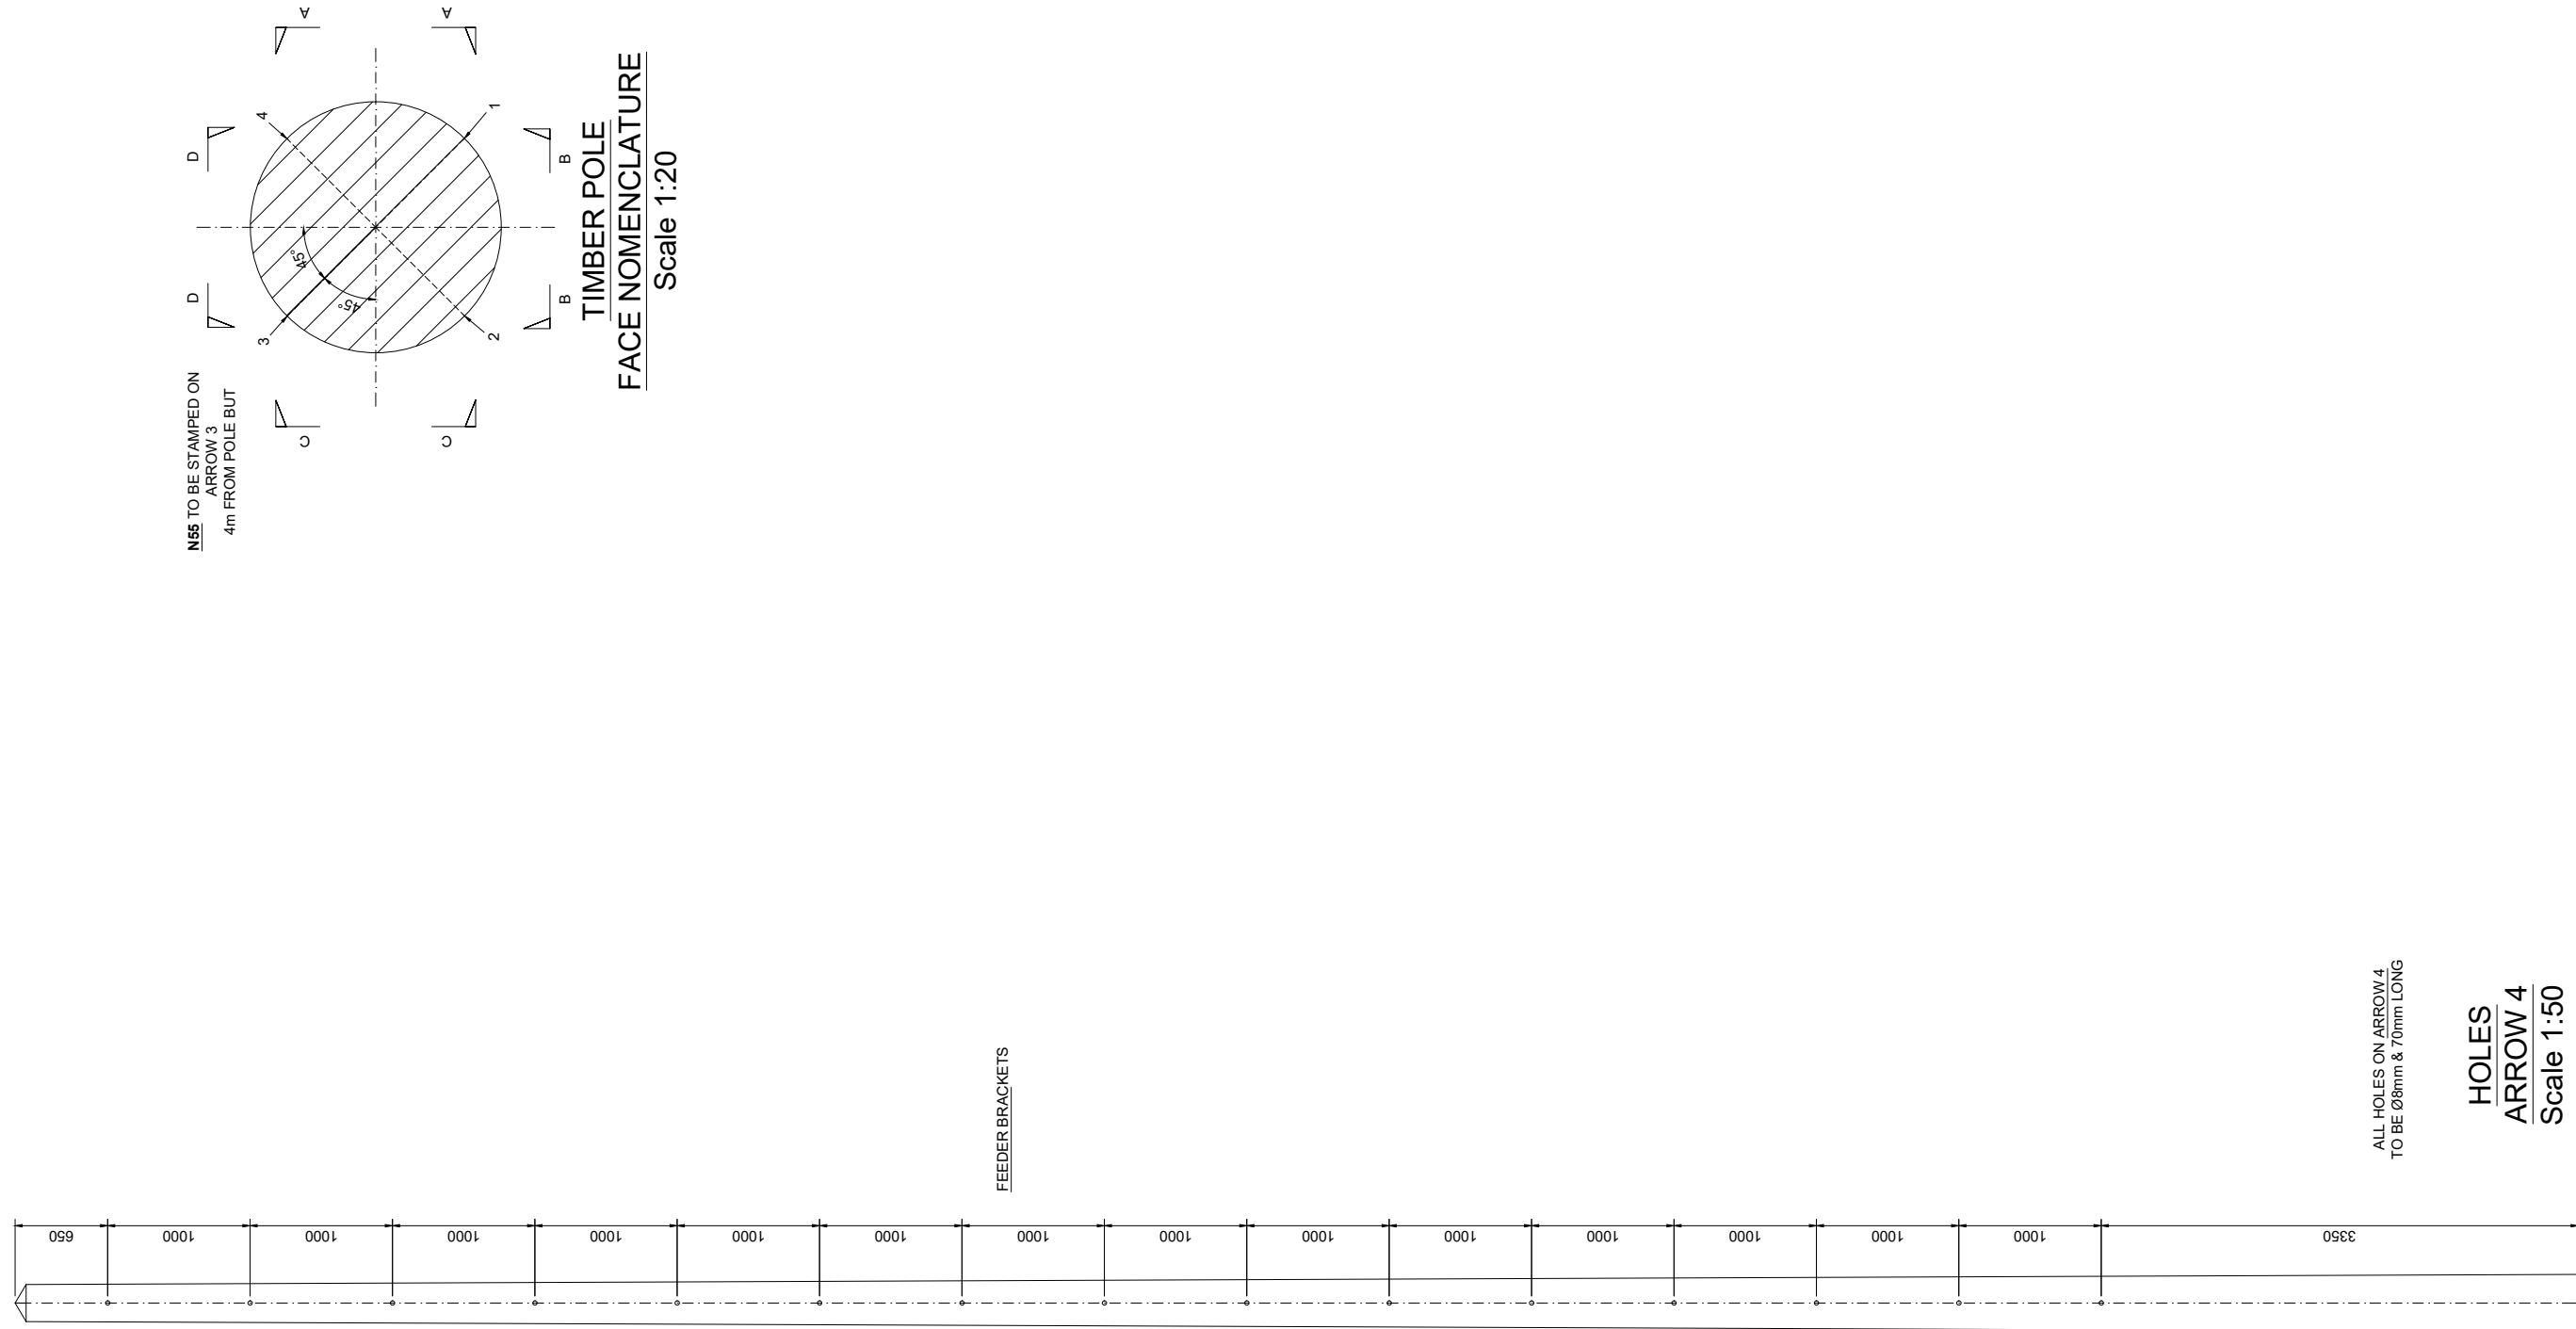REV
01

FEEDER BRACKETS

ALL HOLES ON ARROW 4
TO BE Ø8mm & 70mm LONG


HOLES
ARROW 4
Scale 1:50

HOLE DIAMETERS

	- 16mm THROUGH HOLE
	- 8mm HOLE 70mm LONG



ALL SCALES AS SHOWN WHEN PRINTED AT A3

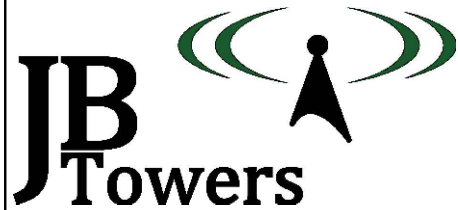


01	FIRST ISSUE			TT	24/06/19
REV	REV			BY	DATE
SCALE AS SHOWN WHEN PRINTED AT A3		DRAWN AM	CHECKED MP	APPROVED JBT	
		DATE 24/06/19	DATE 24/06/19	DATE 24/06/19	
ALL DIMENSIONS IN mm UNLESS OTHERWISE STATED. THIS DRAWING TO BE READ IN CONJUNCTION WITH OTHER RELEVANT DRAWINGS.					

TITLE

STRONTIAN

TIMBER POLE CUT OUT
DETAIL


SITE ADDRESS		
STRONTIAN ACHARACLE HIGHLAND PH36 4JB		
ARQIVA REF. 141617	DRG No. 202	REV 01

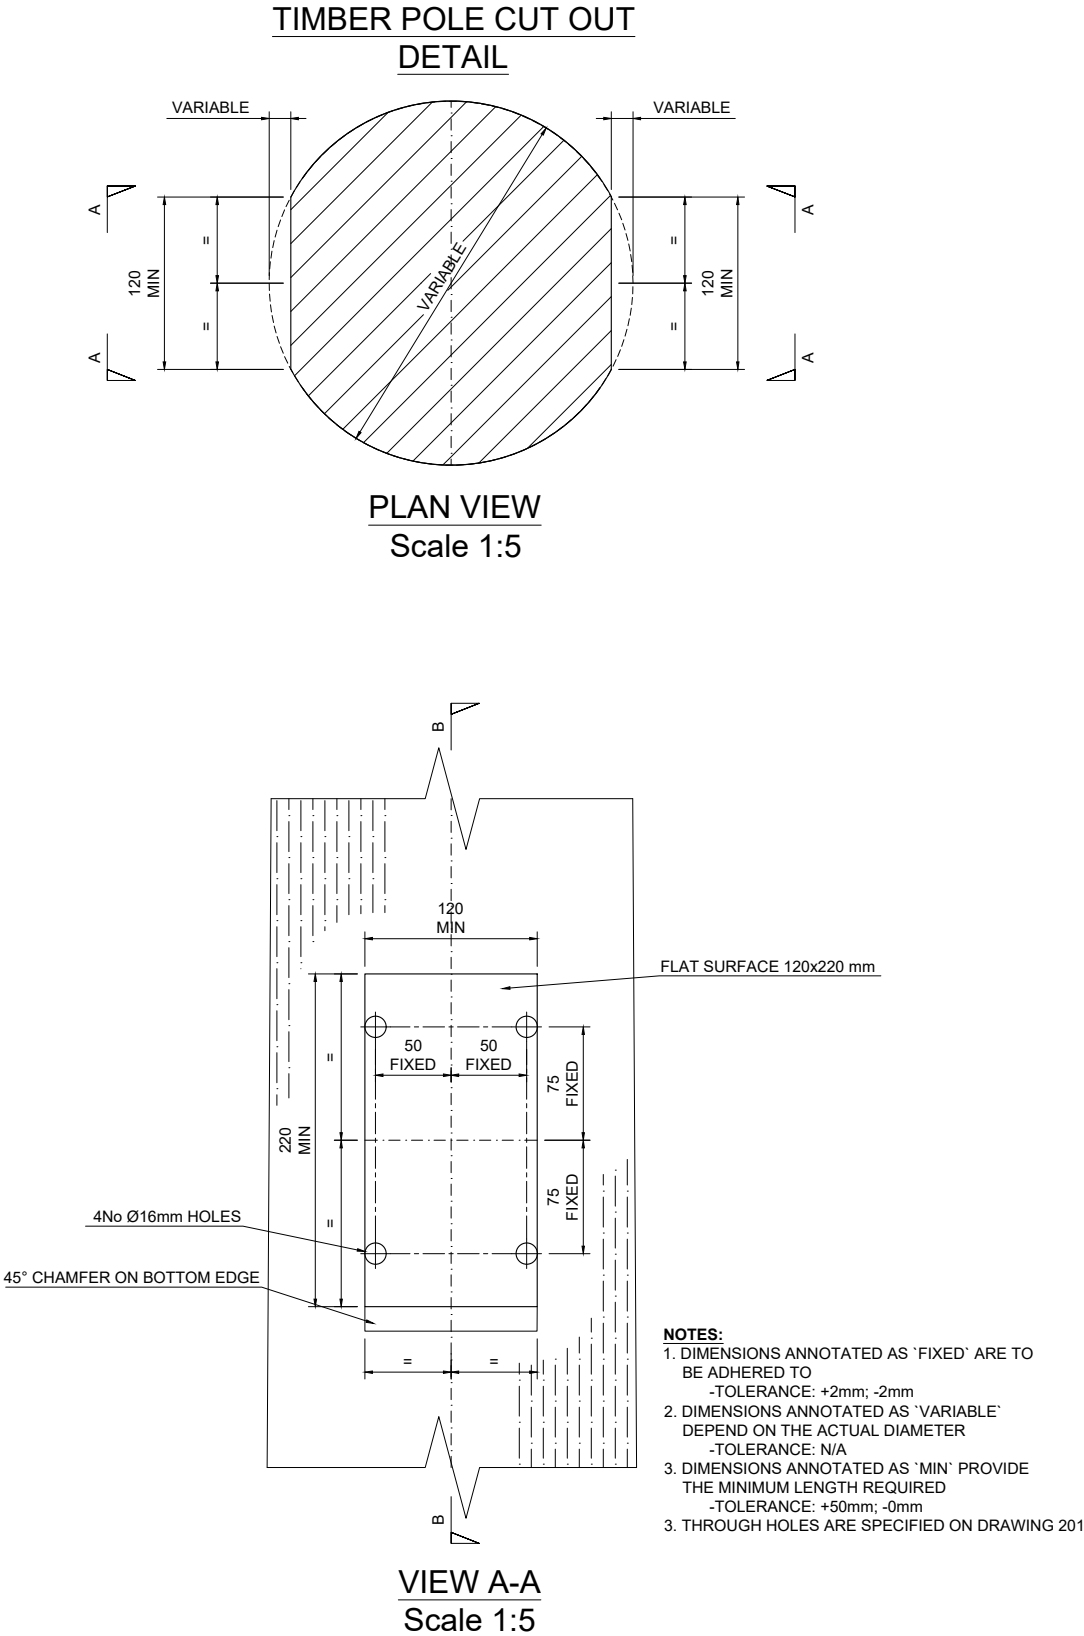


ALL SCALES AS SHOWN WHEN PRINTED AT A3

ALL SCALES AS SHOWN WHEN PRINTED AT A3


2W POWER DIVIDER

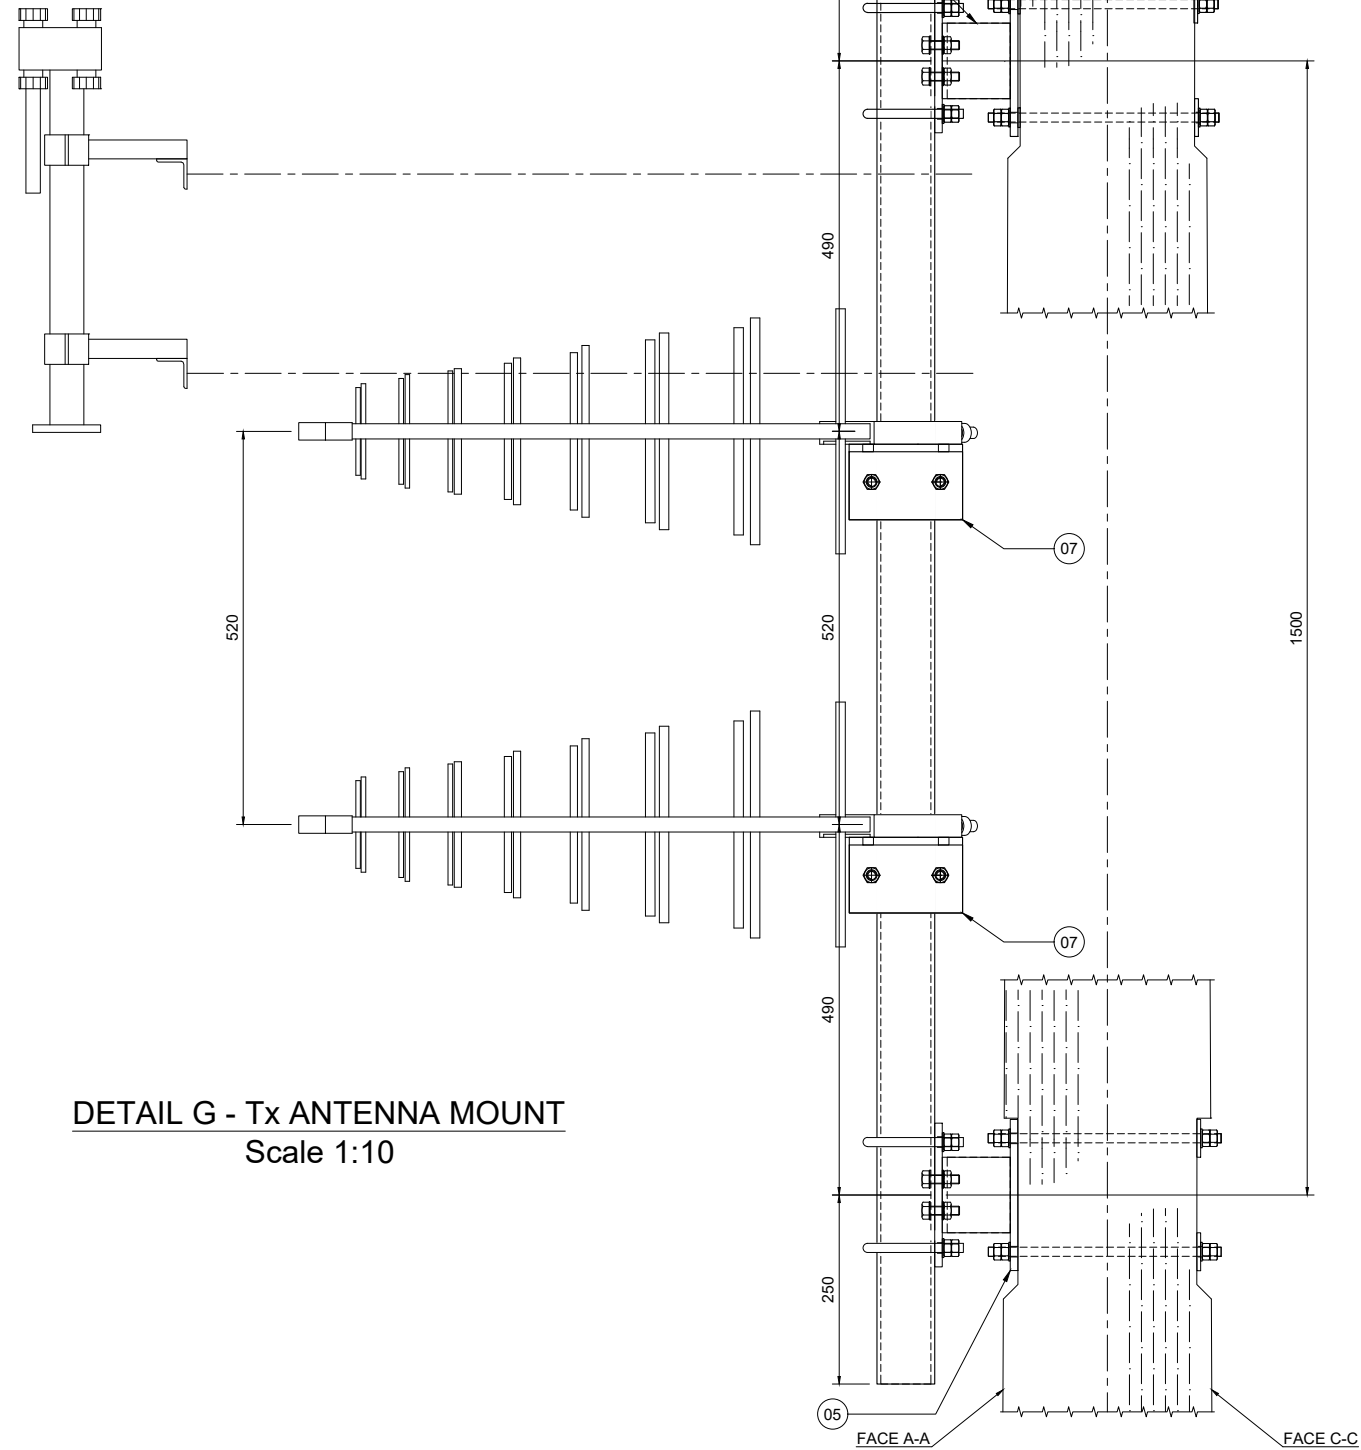

DETAIL G - Tx ANTENNA MOUNT
Scale 1:10

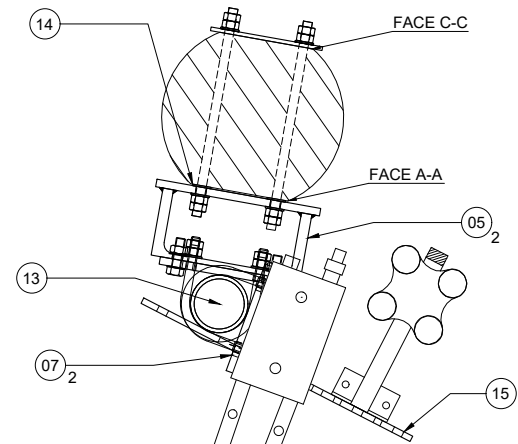

Proposed 2 Tiers of 1 Log
Periodic Antennas @ 13.9m
a.g.l 200°

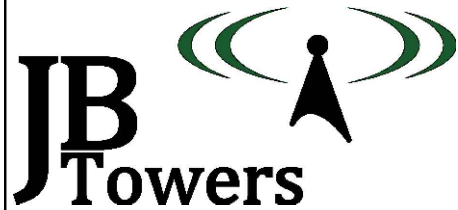


03	POWER DIVIDER POSITION UPDATED	AM	03/07/19
02	FACE LABELS ADDED	AM	27/06/19
01	FIRST ISSUE	TT	24/06/19
REV	REV	BY	DATE
SCALE AS SHOWN WHEN PRINTED AT A3	DRAWN AM DATE 24/06/19	CHECKED MP DATE 24/06/19	APPROVED JBT DATE 24/06/19
ALL DIMENSIONS IN mm UNLESS OTHERWISE STATED. THIS DRAWING TO BE READ IN CONJUNCTION WITH OTHER RELEVANT DRAWINGS.			


TITLE		SITE ADDRESS	
ANTENNA MOUNT		STRONTIAN	
DETAIL G		ACHARACLE	
		HIGHLAND	
		PH36 4JB	
ARQIVA REF. 141617		DRG No. 203	REV 03

ALL SCALES AS SHOWN WHEN PRINTED AT A3



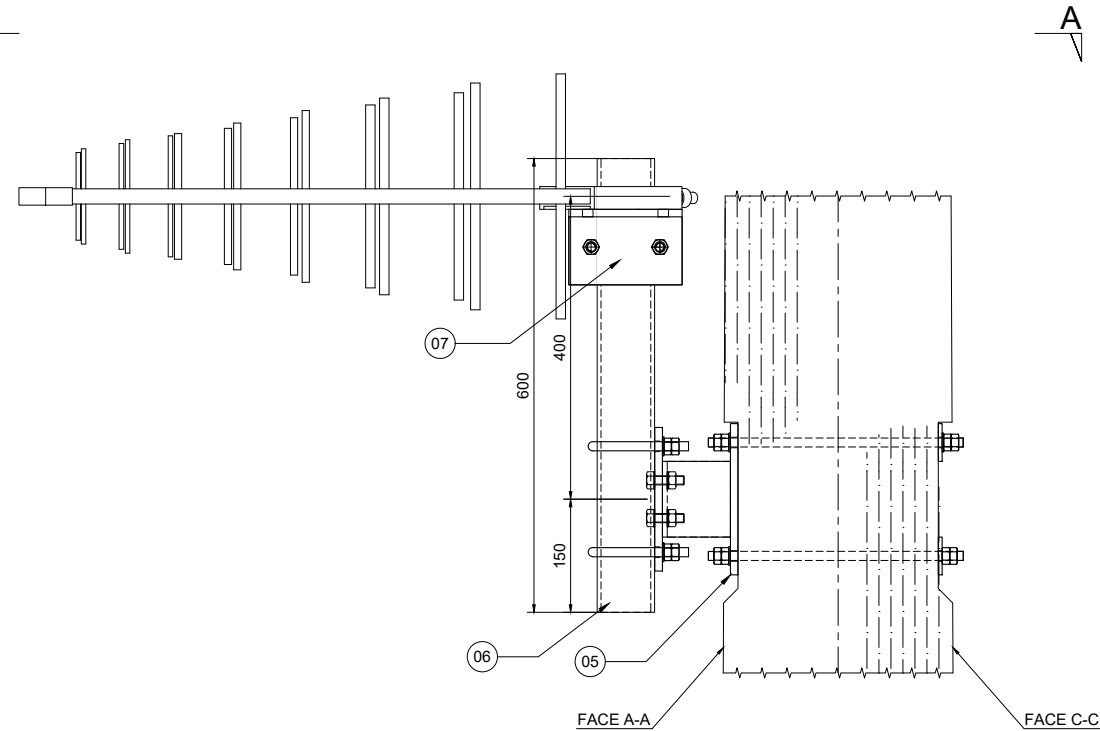

DETAIL H - Rx ANTENNA MOUNT
Scale 1:10

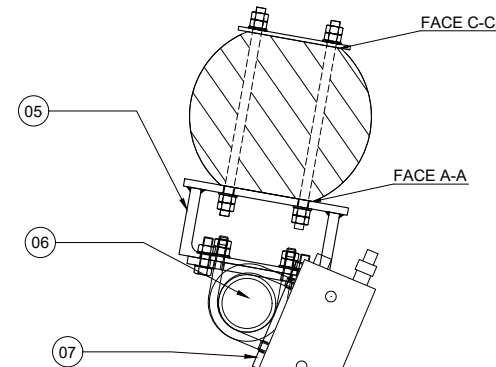


VIEW ON A-A
Scale 1:10

Proposed 1No. Log Periodic
Antenna @ 10.0m a.g.l 203°

ALL SCALES AS SHOWN WHEN PRINTED AT A3



ALL SCALES AS SHOWN WHEN PRINTED AT A3

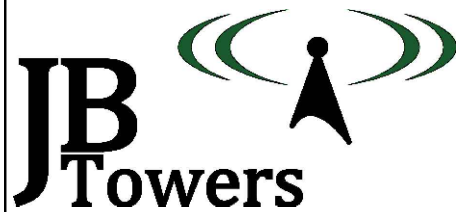

02	FACE LABELS ADDED	AM	27/06/19
01	FIRST ISSUE	TT	24/06/19
REV	REV	BY	DATE
SCALE AS SHOWN WHEN PRINTED AT A3	DRAWN DATE 24/06/19	CHECKED DATE 24/06/19	APPROVED DATE 24/06/19
ALL DIMENSIONS IN mm UNLESS OTHERWISE STATED. THIS DRAWING TO BE READ IN CONJUNCTION WITH OTHER RELEVANT DRAWINGS.			


TITLE
ANTENNA MOUNT
DETAIL H

SITE ADDRESS
STRONTIAN
ACHARACLE
HIGHLAND
PH36 4JB

ARQIVA REF.
141617


DRG No.
204

REV
02

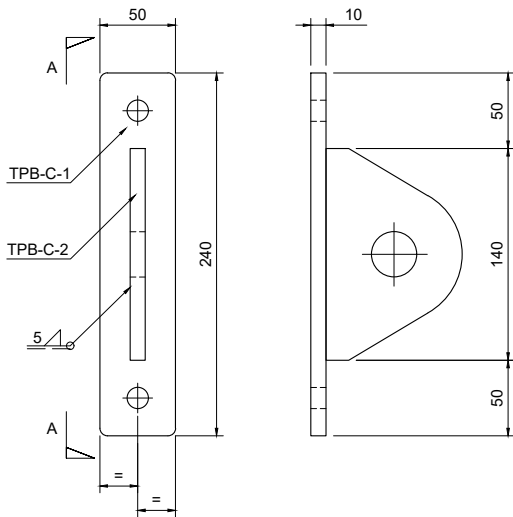

PART TPB-C
Scale 1:5

VIEW A-A
Scale 1:5

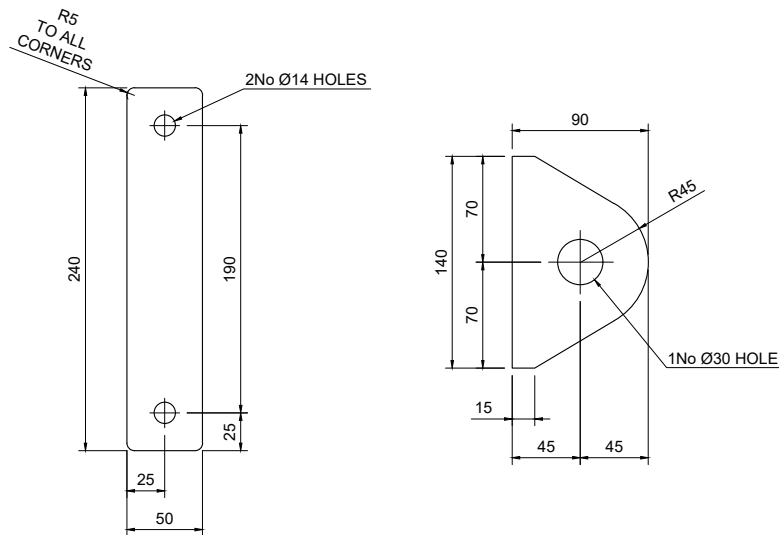


TPB-C-1 - 10mm THICK
Scale 1:5

TPB-C-2 - 10mm THICK
Scale 1:5

Parts list for TPB-C

Item	Part	Quantity	Part description	Length	Material	Weight
01	TPB-C-1	1	240x50x10mm	N/A	S275J0	0.94 kg
02	TPB-C-2	1	140x90x10mm	N/A	S275J0	0.99 kg
03	STUDS	1	M12 STUDDING	350mm	GRADE 8.8	0.31 kg
Total Weight:						2.24 kg

- All steel hot dip galvanized
- Each STUD to be supplied with 4 Full Nuts, 2 Flat Washers and 2 Spring Washers
- For fabrication notes see drawing 302

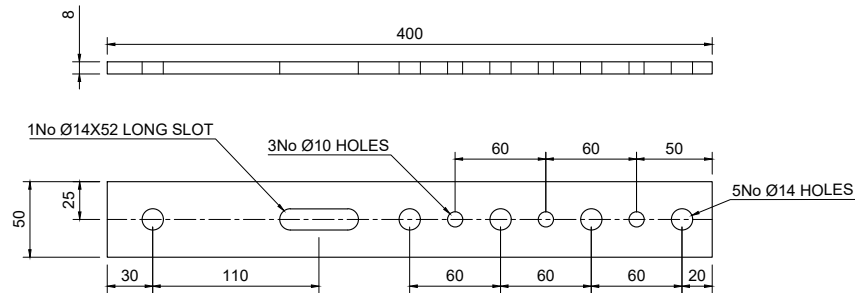


TPA-PD - 8mm THICK
Scale 1:5

Parts list for TPA-PD


Item	Part	Quantity	Part description	Length	Material	Weight
01	TPA-PD	1	Plate 400x50x8mm	N/A	S275J0	1.26 kg
02	U-BOLT	1	M12 U-BOLT FOR CHS 76.1mm	N/A	GRADE 8.8	-
Total Weight:						1.26 kg

- All steel hot dip galvanized
- Each U-BOLT to be supplied with 4 Full Nuts, 2 Flat Washers and 2 Spring Washers
- For fabrication notes see drawing 302

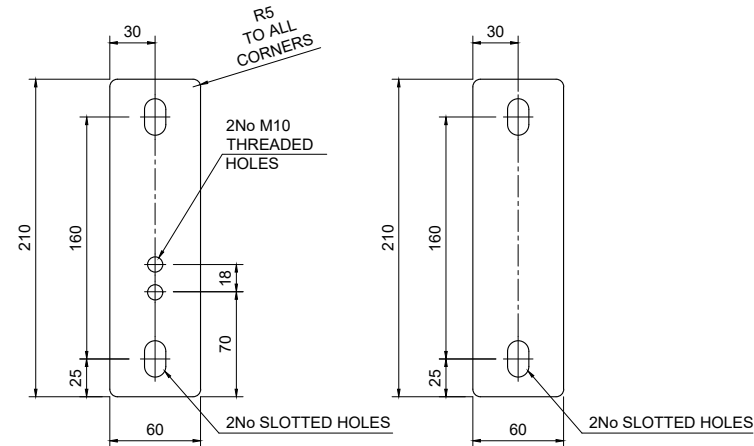

PART TPS-R-1
Scale 1:5

PART TPS-R-2
Scale 1:5

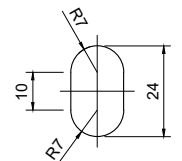


SLOTTED HOLE DETAIL
Scale 1:2

Parts list for TPS-R

Item	Part	Quantity	Part description	Length	Material	Weight
01	TPS-R-1	1	210x60x15mm	N/A	S275J0	1.48 kg
02	TPS-R-2	1	210x60x5mm	N/A	S275J0	0.49 kg
03	STUDS	2	M12 STUDDING	500mm	GRADE 8.8	0.44 kg
04	NUT-S	2	M12 SHALLOW NUT	N/A	GRADE 8.8	-
05	NUT	4	M12 NUT	N/A	GRADE 8.8	-
06	WSH	4	M12 WASHER	N/A	GRADE 8.8	-
Total Weight:						2.41 kg

- All steel hot dip galvanized
- For fabrication notes see drawing 302

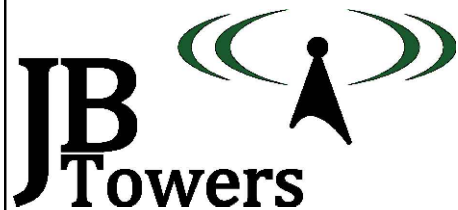

01	FIRST ISSUE	TT	24/06/19
REV	REV	BY	DATE
SCALE AS SHOWN WHEN PRINTED AT A3	DRAWN AM DATE 24/06/19	CHECKED MP DATE 24/06/19	APPROVED JBT DATE 24/06/19
ALL DIMENSIONS IN mm UNLESS OTHERWISE STATED. THIS DRAWING TO BE READ IN CONJUNCTION WITH OTHER RELEVANT DRAWINGS.			

TITLE
**ATTACHMENT POINT ,
TEMPORARY STEP DETAILS
& POWER DIVIDER STRAP**


PARTS: TPB-C; TPS-R;
TPA-PD

SITE ADDRESS STRONTIAN ACHARACLE HIGHLAND PH36 4JB		
ARQIVA REF. 141617	DRG No. 300	REV 01


ALL SCALES AS SHOWN WHEN PRINTED AT A3




ALL SCALES AS SHOWN WHEN PRINTED AT A3

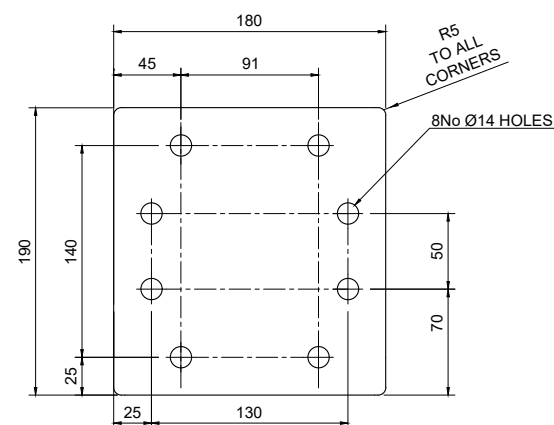


TPB-B-5 - 10mm THICK
Scale 1:5

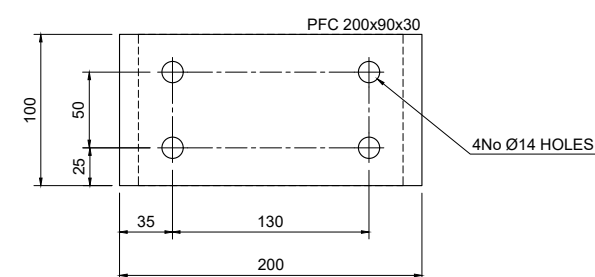



TPB-B-2 - PFC 200x90x30
Scale 1:5

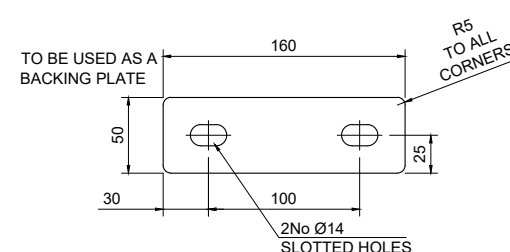

TPB-B-4 - 5mm THICK
Scale 1:5

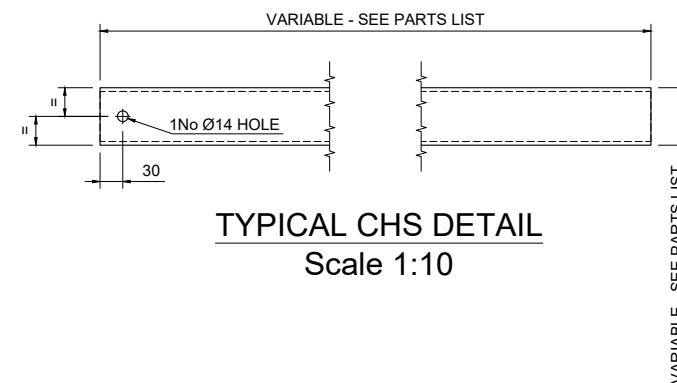


TYPICAL CHS DETAIL
Scale 1:10

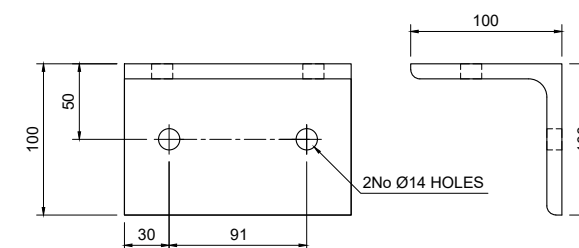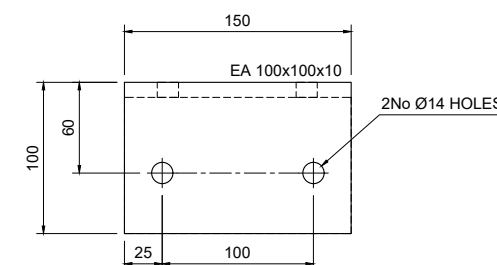

TPL-A - EA100x100x10
Scale 1:5

Total Weight:	11.33 kg
---------------	----------

- All steel hot dip galvanized
- Each STUD & U-BOLT to be supplied with 4 Full Nuts, 2 Flat Washers and 2 Spring Washers
- Each BOLT to be supplied with 1 Full Nut, 1 Form E FLat Washer and 1 Spring Washer
- For fabrication notes see drawing 302

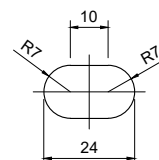

SLOTTED HOLE DETAIL
Scale 1:2

Total Weight:	2.25 kg
---------------	---------

- All steel hot dip galvanized
- Each STUD & U-BOLT to be supplied with 4 Full Nuts, 2 Flat Washers and 2 Spring Washers
- Each BOLT to be supplied with 1 Full Nut, 1 Form E Flat Washer and 1 Spring Washer
- For fabrication notes see drawing 302



01	FIRST ISSUE			TT	24/06/
REV	REV			BY	DAT
SCALE AS SHOWN WHEN PRINTED AT A3		DRAWN AM	CHECKED MP	APPROVED JB	
		DATE 24/06/19	DATE 24/06/19	DATE 24/06/19	
ALL DIMENSIONS IN mm UNLESS OTHERWISE STATED. THIS DRAWING TO BE READ IN CONJUNCTION WITH OTHER RELEVANT DRAWINGS.					

TITLE

STEELWORK BRACKET & TYPICAL CHS DETAIL

PART: TPB-A

SITE ADDRESS

STRONTIAN
ACHARACLE
HIGHLAND
PH36 4JB

ARQIVA REF.
141617

DRG No.
301REV
01

ALL SCALES AS SHOWN WHEN PRINTED AT A3

ALL SCALES AS SHOWN WHEN PRINTED AT A3


Item	Part	Drawing	Quantity	Part description	Length	Material	Weight
01	01	200	1	3 MAN LATCHWAY SYSTEM & 3No. WIRE GUIDES FOR FACE MOUNTED MONOPOLE	15000	N/A	-
02	TPB-C	300	2	FALL ARREST ATTACHMENT POINT	N/A	S275J0	4.48 kg
03	03	200	38	PERMANENT BT STEP c/w 3No 10x75mm ZINC-PLATED COACH SCREWS	N/A	S275J0	25.75 kg
04	TPS-R	300	9	'MonoStep' ASSEMBLY	N/A	S275J0	21.69 kg
05	TPB-B	301	3	MOUNTING BRACKET	N/A	S275J0	33.99 kg
06	06	204	1	CHS 76.1x5mm	600mm	S355J2H	5.26 kg
07	TPL-A	301	3	MOUNTING BRACKET	N/A	S275J0	6.75 kg
08	08	200	1	FEEDER COVER - 2/CG/100	3500mm	UV RESISTANT PLASTIC	-
09	09	200	15	FEEDER CLAMP - 2/FCD/028	N/A	POLYPROPYLENE	-
10	10	200	15	M10 SCREW DOWELS WTH M10 NUT	100mm	STAINLESS STEEL	-
11	11	200	1	PoleSaver	750mm	N/A	-
12	12	200	6	M12 STUD + 4No NUTS + 2No FLAT WASHERS + 1No Ø50mm WASHER (FOR FALL ARREST SYSTEM)	500mm	GRADE 8.8	2.64 kg
13	13	203	1	CHS 76.1 x 5mm	2000mm	S355J2H	17.54 kg
14	14	203	12	M12 WASHER	N/A	GRADE 8.8	-
15	TPA-PD	300	2	POWER DIVIDER STRAP	N/A	S275J0	2.52 kg
Total Weight:							120.62 kg

- All steel hot dip galvanized

- All U-BOLTS to be FLA supply, each Supplied with 4 Full Nuts, 2 Flat Washers and 2 Spring Washers

NOTES:

1. WELDING TO BE IN ACCORDANCE WITH BS EN 1011-1:2009
2. LINEAR DIMS TO BE WITHIN ±1mm;
3. ANGULAR TOLERANCES TO BE WITHIN 0.5°
4. WELDING SYMBOLS ARE IN ACCORDANCE WITH BS EN 22553:1995
5. ALL PROFILE EDGES TO BE DRESSED AND SHARP CORNERS REMOVED
6. ALL WELD SIZES ARE FINAL SIZES
7. ALL WELDED JOINTS ARE TO BE PICKLE TIGHT
8. ALL STEELWORK TO BE BS EN 10025 GRADE S275 J0 UNO
9. HOT DIPPED GALVANISED TO BS EN ISO 1461. (ALL HOLLOW SECTIONS TO BE GRADE S355 J0H)
10. ALL STEEL IS TO BE SUPPLIED IN ACCORDANCE WITH EN 1090 TO EXECUTION CLASS 2
11. ALL NON PRE-LOADED BOLTS TO BE COMPLIANT STRUCTURAL BOLTS TO BS EN ISO 15048 PARTS 1&2.
12. STEELWORK COMPONENTS SHALL BE HOT DIP GALVANISED TO ACHIEVE A "VERY HIGH" DURABILITY FOR AN ENVIRONMENT CATEGORY CODE C4 FROM TABLE 1 IN BS EN ISO 14713
13. BOLTS AND NUTS SHALL BE SUPPLIED IN ACCORDANCE WITH BS 7371, SPUN GALVANISED IN ACCORDANCE WITH ISO 10684, THE NUTS RE-TAPPED AFTER GALVANISING, AND THE THREADS TREATED WITH GREASE.
14. ALL BOLTS TO BE CUT ON SITE TO EXTEND MAX 10mm BEYOND THE NUT WHEN TIGHTENED UNO.
15. ALL SITE DRILLED HOLE/CUT ENDS TO BE TREATED WITH METAFLUX 70-40 ZINC PASTE FOLLOWED BY 1 COAT OF 7-42 ZINC ALU OR 70-16 ALUMINIUM SPRAY

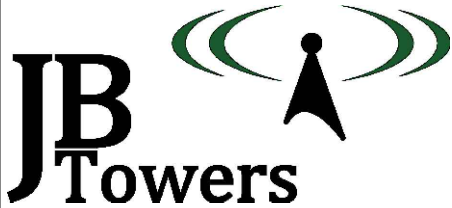

01	FIRST ISSUE	TT	24/06/19
REV	REV	BY	DATE
SCALE AS SHOWN WHEN PRINTED AT A3	DRAWN AM DATE 24/06/19	CHECKED MP DATE 24/06/19	APPROVED JBT DATE 24/06/19
ALL DIMENSIONS IN mm UNLESS OTHERWISE STATED. THIS DRAWING TO BE READ IN CONJUNCTION WITH OTHER RELEVANT DRAWINGS.			

TITLE
PARTS LIST

SITE ADDRESS		
STRONTIAN ACHARACLE HIGHLAND PH36 4JB		
ARQIVA REF. 141617	DRG No. 302	REV 01

ALL SCALES AS SHOWN WHEN PRINTED AT A3




ALL SCALES AS SHOWN WHEN PRINTED AT A3


01	FIRST ISSUE			TT	24/06/19
REV	REV			BY	DATE
SCALE AS SHOWN WHEN PRINTED AT A3		DRAWN AM	CHECKED MP	APPROVED JBT	
		DATE 24/06/19	DATE 24/06/19	DATE 24/06/19	
ALL DIMENSIONS IN mm UNLESS OTHERWISE STATED. THIS DRAWING TO BE READ IN CONJUNCTION WITH OTHER RELEVANT DRAWINGS.					

TITLE		
FOUNDATION DETAILS		



SITE ADDRESS		
STRONTIAN ACHARACLE HIGHLAND PH36 4JB		
ARQIVA REF. 141617	DRG No. 400	REV 01

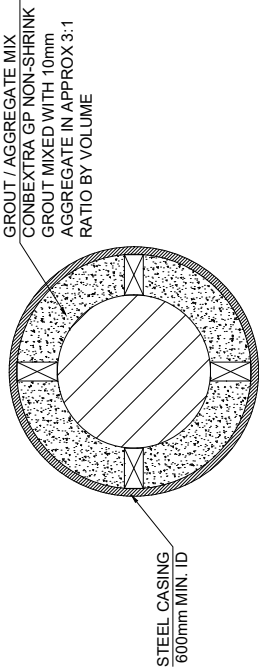

POROPOSED INSTALLATION
PLAN VIEW
Scale 1:20

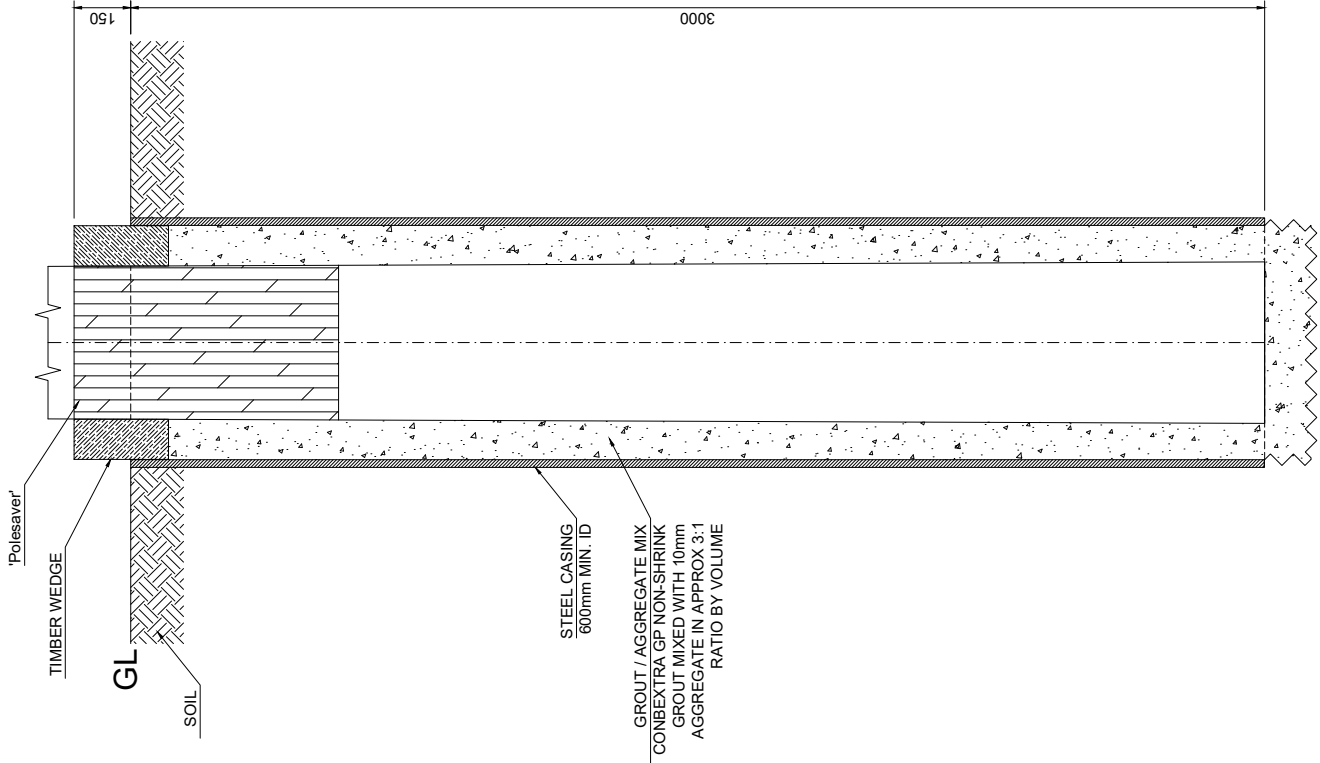

POROPOSED INSTALLATION
ELEVATION
Scale 1:20

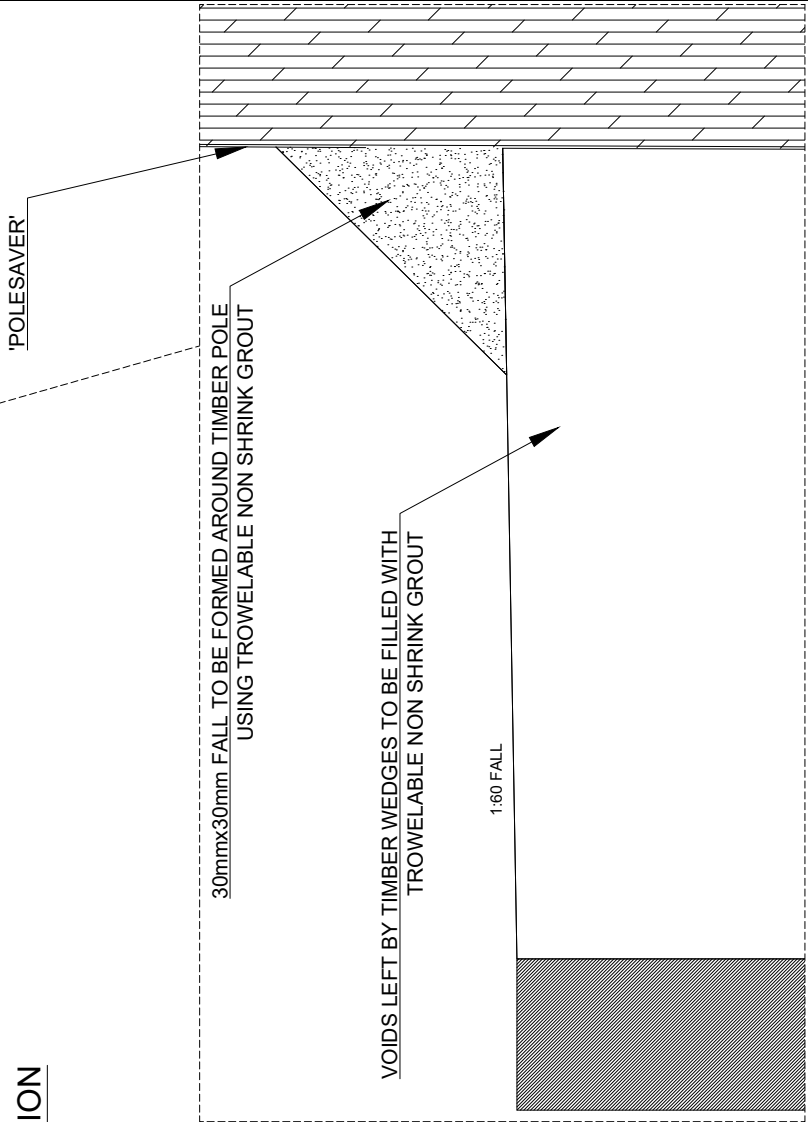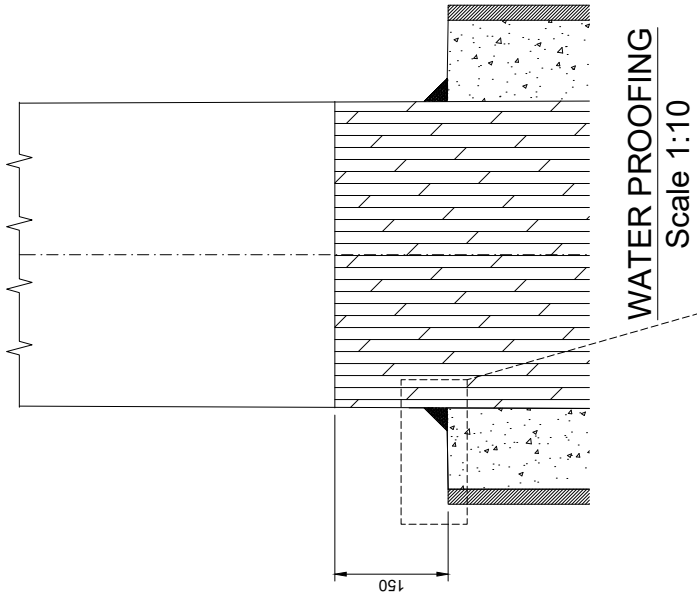

ENLARGED DETAIL
Scale 1:1

TIMBER POLE INSTALLATION:

1. REFER TO DRG 200 FOR TIMBER POLE ORIENTATION.
2. OVERDIG AT BASE OF HOLE FROM INSTALLATION OF SLEEVE TO BE FILLED WITH GROUT /AGGREGATE MIX.
3. POLE TO BE WRAPPED IN 'POLESAVER' AND INSTALLED AND LEVELED IN OPENING. TIMBERS TO BE USED TO HOLD POLE IN POSITION & THEN ANNULUS FILLED WITH GROUT/AGGREGATE MIX. ONCE GROUT HAS CURED REMOVE TIMBER WEDGES AND FILL REMAINING VOIDS WITH NON-SHRINK GROUT. A 1:60 FALL SHALL BE FORMED AROUND TIMBER POLE TO ALLOW WATER TO DRAIN AWAY FROM POLE.
- 4.