
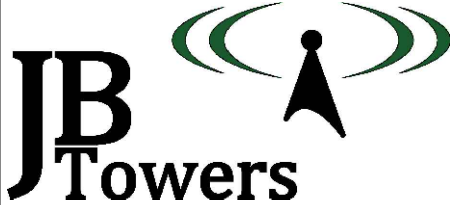
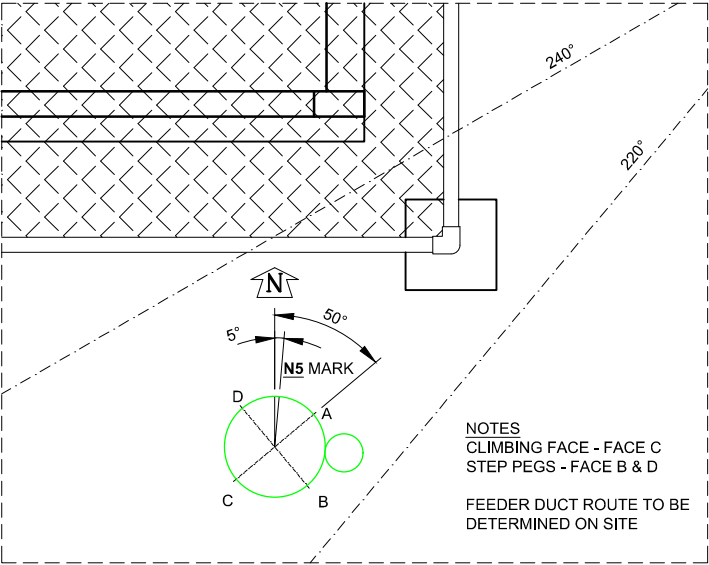


DRAWING ISSUE SHEET

[illegible]

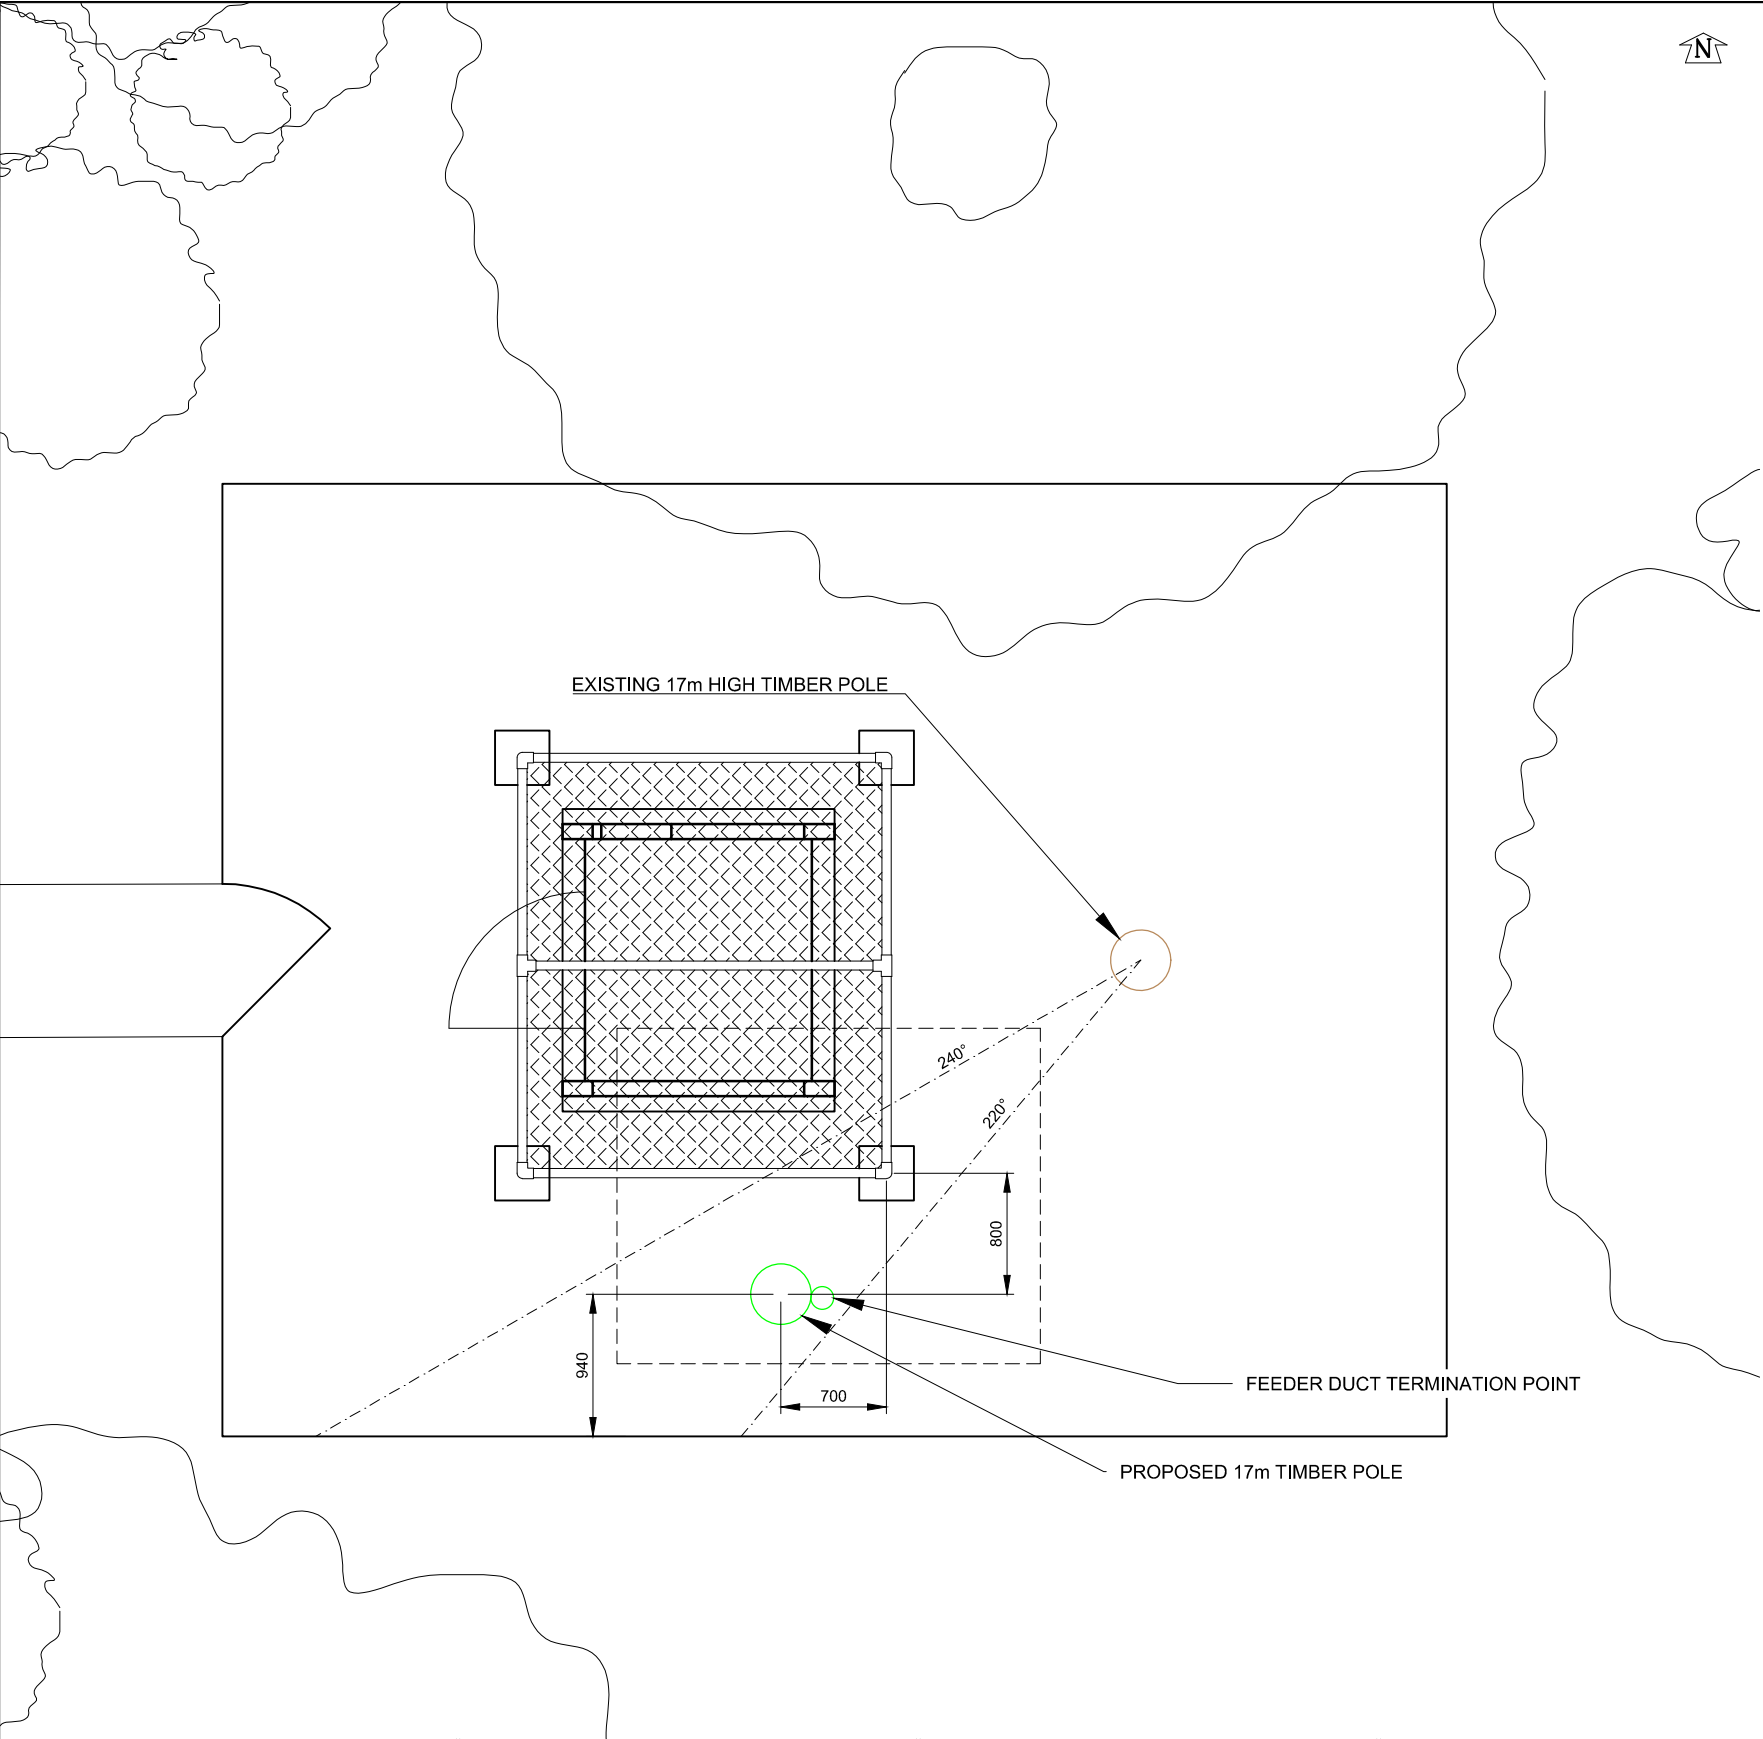


02	REVISED POSITION OF PROPOSED TIMBER POLE			AM	20/11/20
01	FIRST ISSUE			AM	22/10/20
REV	REV			BY	DATE
SCALE AS SHOWN		DRAWN	AM	CHECKED	MP
WHEN PRINTED AT A3		DATE	22/10/20	DATE	22/10/20
		APPROVED	JBT	DATE	22/10/20
ALL DIMENSIONS IN mm UNLESS OTHERWISE STATED. THIS DRAWING TO BE READ IN CONJUNCTION WITH OTHER RELEVANT DRAWINGS.					

TITLE
SUNDERLAND
SITE PLAN

SITE ADDRESS THE PRECINCT TUNSTALL HILL SUNDERLAND TYNE AND WEAR SR2 9DN		
ARQIVA REF. 141622	DRG No. 100	REV 02

ALL SCALES AS SHOWN WHEN PRINTED AT A3



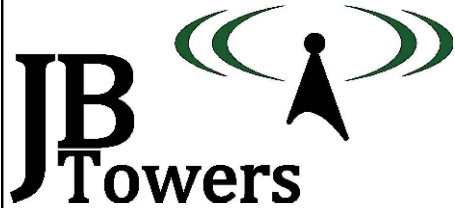

01	FIRST ISSUE			AM	22/10/20
REV	REV			BY	DATE
SCALE AS SHOWN		DRAWN	AM	CHECKED	MP
WHEN PRINTED AT A3		DATE	22/10/20	DATE	22/10/20
		APPROVED	JBT	DATE	22/10/20
ALL DIMENSIONS IN mm UNLESS OTHERWISE STATED. THIS DRAWING TO BE READ IN CONJUNCTION WITH OTHER RELEVANT DRAWINGS.					



TITLE
SUNDERLAND
GENERAL ARRANGEMENT
SHEET 1 OF 3

SITE ADDRESS
THE PRECINCT
TUNSTALL HILL
SUNDERLAND
TYNE AND WEAR
SR2 9DN

ARQIVA REF.
141622

DRG No.
200

REV
01

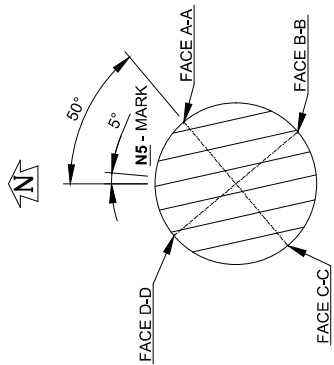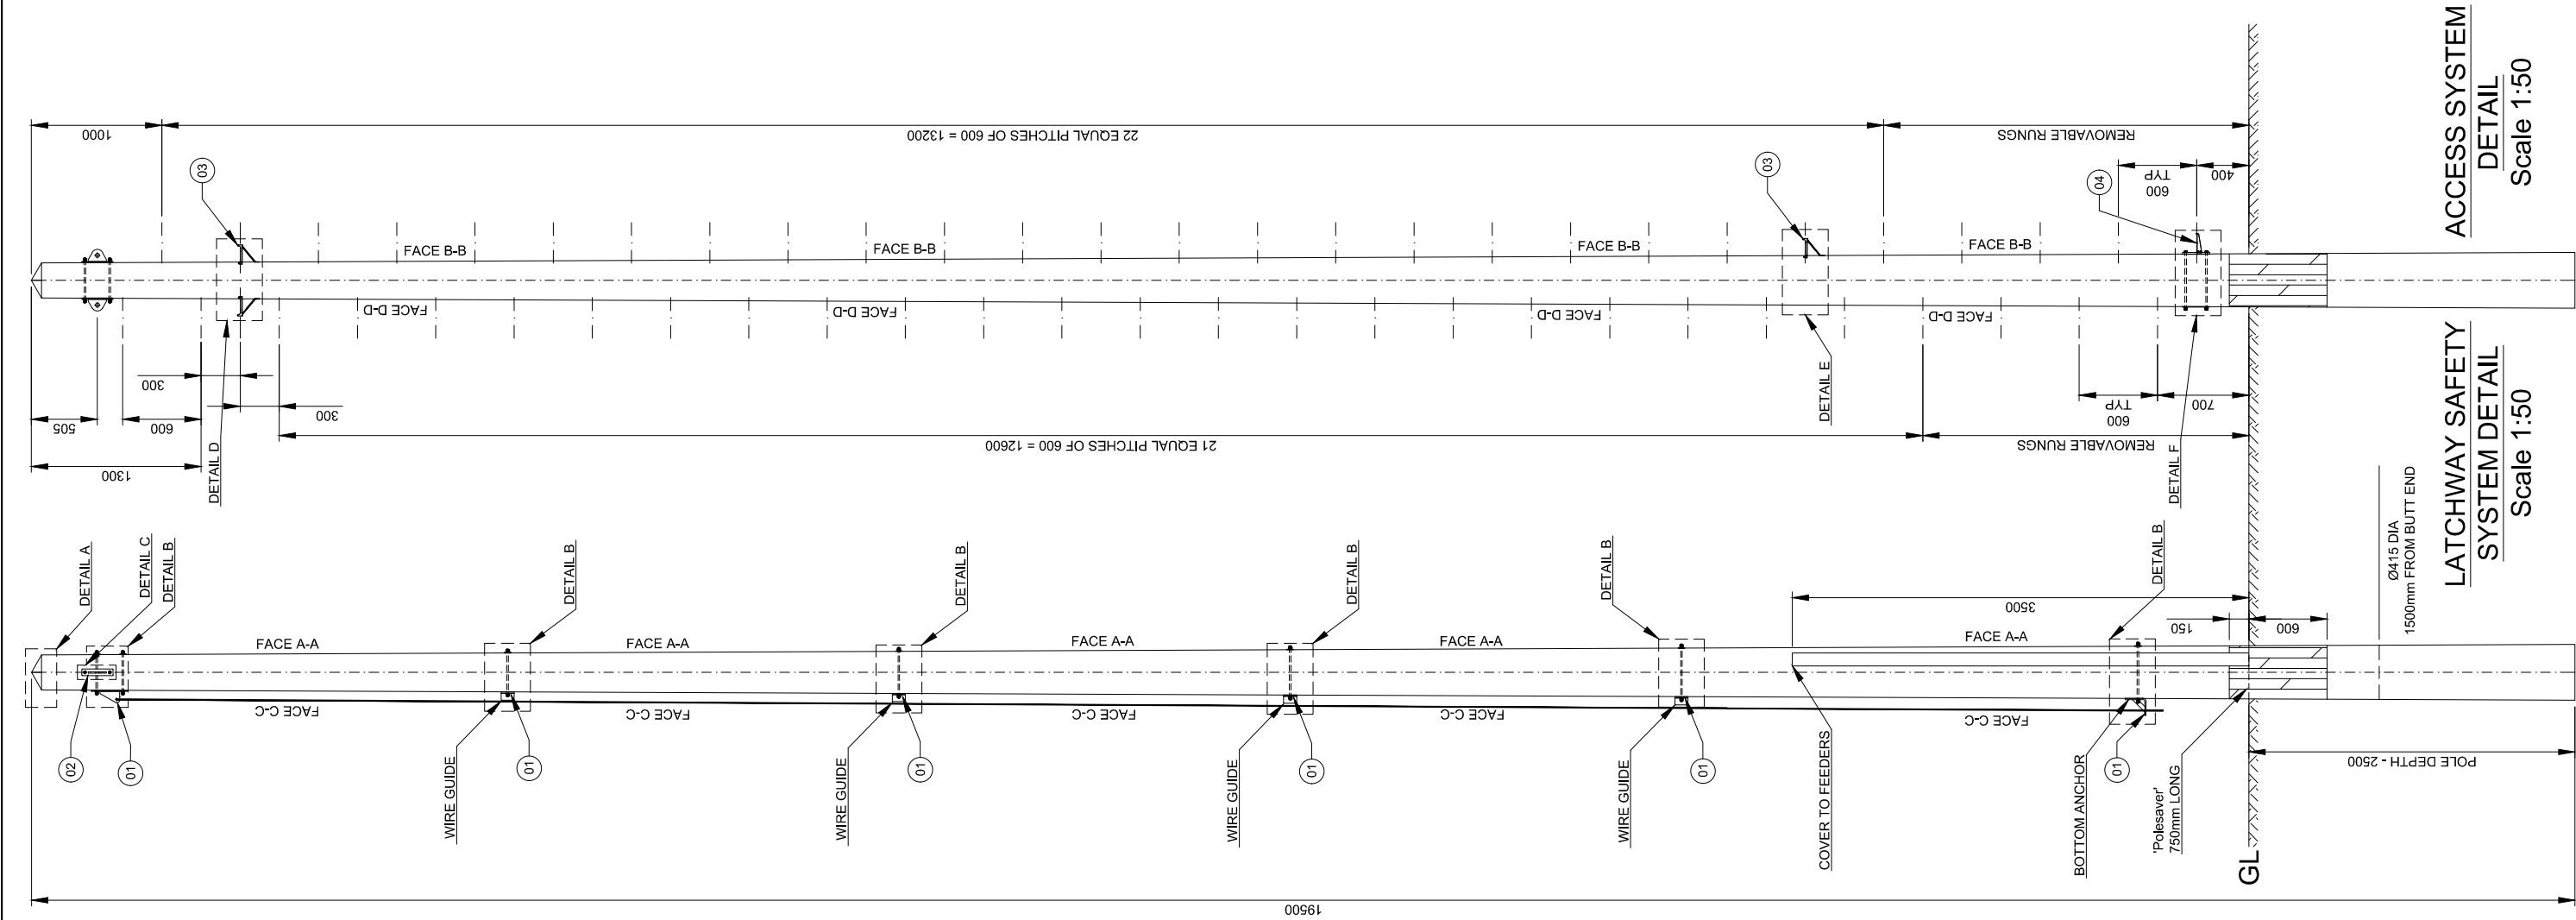

NOTES

1. SEE DRAWING 305 FOR PARTS LIST
2. ALL BOLTS TO BE CUT ON SITE TO EXTEND MAX 10mm BEYOND THE NUT WHEN TIGHTENED UNO.
3. ALL SITE DRILLED HOLE/CUT ENDS TO BE TREATED WITH METALUX 70-40 ZINC PASTE FOLLOWED BY 1 COAT OF 7-42 ZINC ALU OR 70-16 ALUMINIUM SPRAY

TIMBER POLE

1. POLE TO BE SUPPLIED IN ACCORDANCE WITH BS EN14229 & SHALL HAVE MIN. CHARACTERISTIC BENDING STRENGTH OF 30N/mm² & MIN. YOUNGS MODULUS (PARALLEL TO GRAIN) OF 10kN/mm².
2. MARKINGS ON FINISHED POLE SHALL BE AT 4m FROM BUTT AND COMPLY WITH BS EN 14229 UNO
3. AS FAR AS PRACTICABLE ALL CUTTING, SCARFING & DRILLING TO BE DONE BEFORE CREOSOTING. IF NOT ALL CUT, DRILLED & SCARFED SURFACES TO BE COATED WITH A MIXTURE OF CREOSOTE & TAR.
4. POLE TO BE PRESSURE IMPREGNATED WITH CREOSOTE IN ACCORDANCE WITH BS EN 14229
5. MINIMUM DIAMETERS
TOP - Ø205mm
BOTTOM - Ø430mm
6. 19.5m LONG POLE TO BE SOURCED BY TRIMMING 20m LONG POLE BY 0.5m AT THE TOP

PLANTING


1. CAT SCANNER IS TO BE USED IN ORDER TO CONFIRM THE POSITIONS OF BURIED SERVICES.
2. TIMBER POLE TO BE PLANTED WITH N5 MARKING AT 3.5m FROM BUT FACING 5° FROM NORTH (CLOCKWISE)
3. SEE DRAWING 400 FOR FOUNDATION DETAILS

ACCESS SYSTEM
DETAIL
Scale 1:50

LATCHWAY SAFETY
SYSTEM DETAIL
Scale 1:50

ALL SCALES AS SHOWN WHEN PRINTED AT A3

ALL SCALES AS SHOWN WHEN PRINTED AT A3

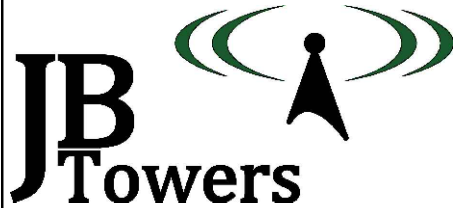

01	FIRST ISSUE			AM	22/10/20
REV	REV			BY	DATE
SCALE AS SHOWN		DRAWN	AM	CHECKED	MP
WHEN PRINTED AT A3		DATE	22/10/20	DATE	22/10/20
		APPROVED	JBT	DATE	22/10/20
ALL DIMENSIONS IN mm UNLESS OTHERWISE STATED. THIS DRAWING TO BE READ IN CONJUNCTION WITH OTHER RELEVANT DRAWINGS.					

TITLE

SUNDERLAND

GENERAL ARRANGEMENT

SHEET 2 OF 3

SITE ADDRESS

THE PRECINCT

TUNSTALL HILL

SUNDERLAND

TYNE AND WEAR

SR2 9DN

ARQIVA REF.




141622

DRG No.

200

REV

01

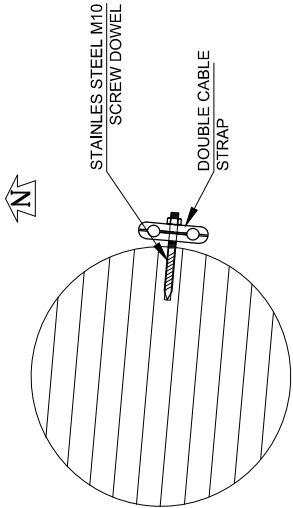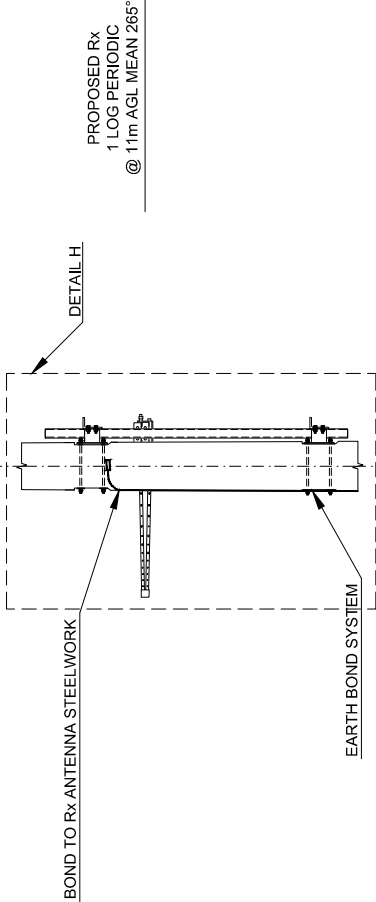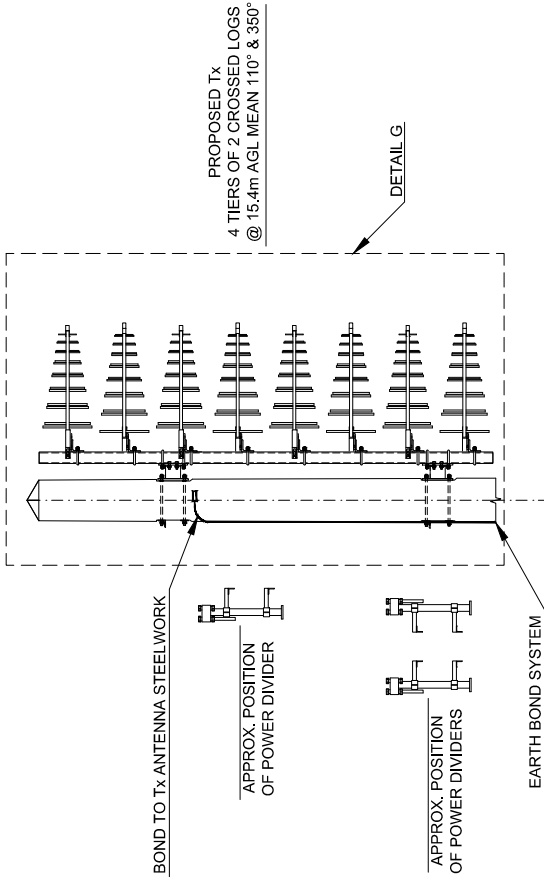

FEEDER
MANAGEMENT

Scale 1:10

NOTES


1. AS FAR AS IS PRACTICABLE ALL CUTTING SCARFING AND DRILLING TO BE DONE BEFORE CREOSOTING. WHERE THIS IS NOT POSSIBLE ALL CUT, DRILLED, AND SCARFED SURFACES TO BE COATED WITH A MIXTURE OF CREOSOTE AND TAR

FEEDERS

1. SUPPLY OF FEEDERS BY OTHERS LCF7/8-50 TO Tx ANTENNA & LCF12-50 TO Rx ANTENNA
2. FEEDERS FIXED AT 1000mm CENTRES

EARTHING

1. CONNECT EARTH BOND TO NEW EARTHING SYSTEM
2. MAXIMUM VALUE FOR GROUND RESISTANCE TO BE 10 OHMS
3. CABLE OR TAPE TO BE FIXED TO POLE AT 1000mm CENTRES
4. EARTHING SHOULD COMPLY WITH ARQIVA'S DOCUMENT BOS147

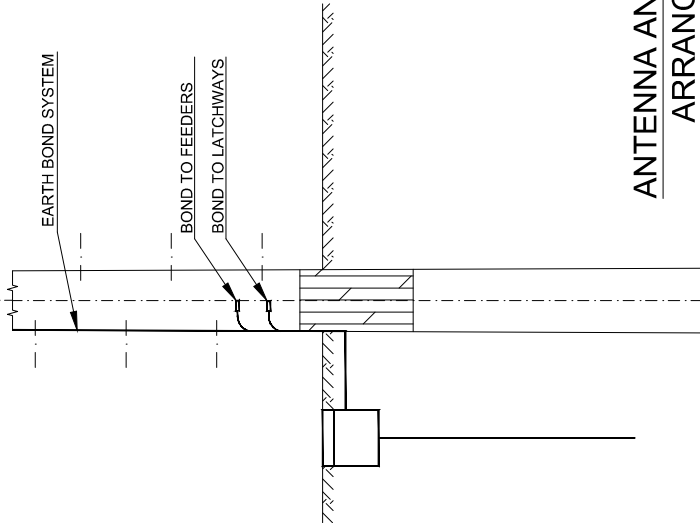


ANTENNA AND EARTHING
ARRANGEMENT

Scale 1:50




ALL SCALES AS SHOWN WHEN PRINTED AT A3

ALL SCALES AS SHOWN WHEN PRINTED AT A3

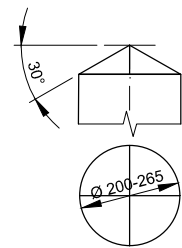


- NOTES:
1. A SINGLE COAT OF TIMBER COMPATIBLE BITUMINOUS PAINT (E.G. BIRD BRAND BLACK BITUMINOUS PAINT OR SIMILAR APPROVED PRODUCT) TO BE APPLIED TO THE UPPER SURFACES AT THE TOP OF THE POLE.
 2. PAINT TO BE APPLIED ON SITE JUST BEFORE ERECTION
- FORM: 4 WAY PYRAMID / CONE


DETAIL A - TIMBER POLE TOP
Scale 1:20

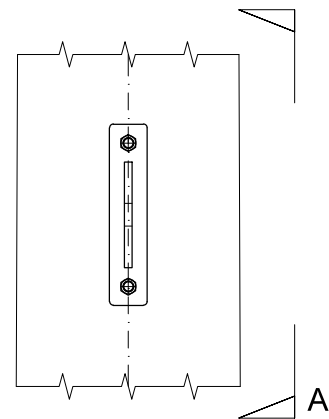

DETAIL C - FALL ARREST
ATTACHMENT POINT
Scale 1:10

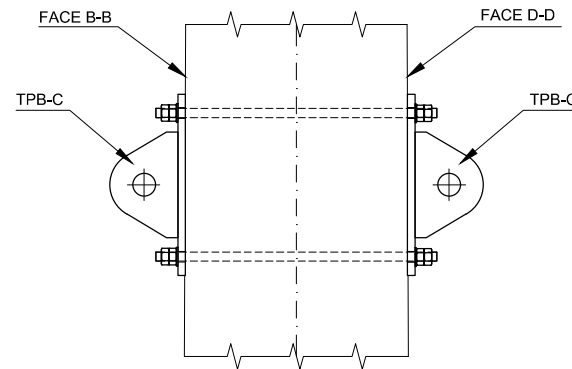


VIEW A-A
Scale 1:10

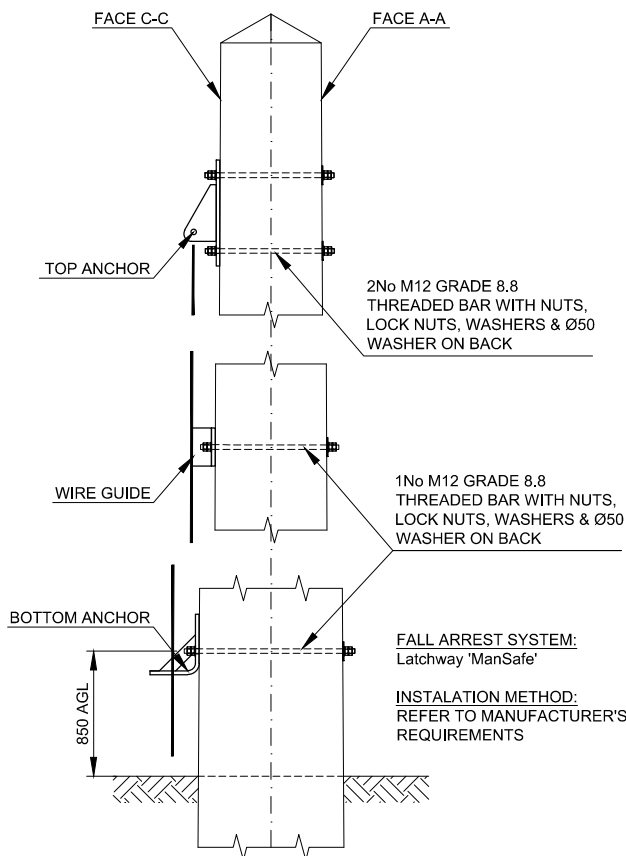


DETAIL B - FALL ARREST SYSTEM
Scale 1:20


DETAIL D - ANTENNA
ACCESS CLIMBING STEP
Scale 1:10

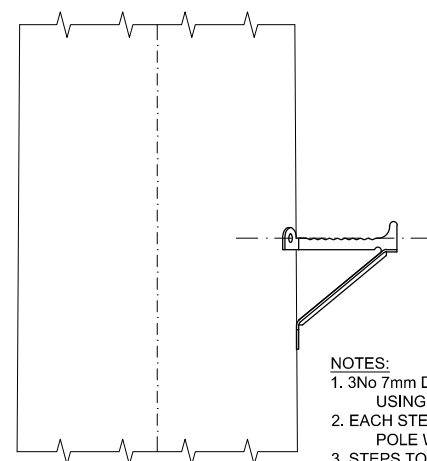

- NOTES:
1. 3No 7mm DIA 70mm LONG PILOT HOLES TO BE DRILLED USING THE STEP AS A TEMPLATE
 2. EACH STEP SHOULD BE FIXED TO THE TIMBER POLE WITH 3No 10mm COACH SCREWS 75mm LONG
 3. STEPS TO BE INSTALLED ON FACES B-B & D-D ONLY

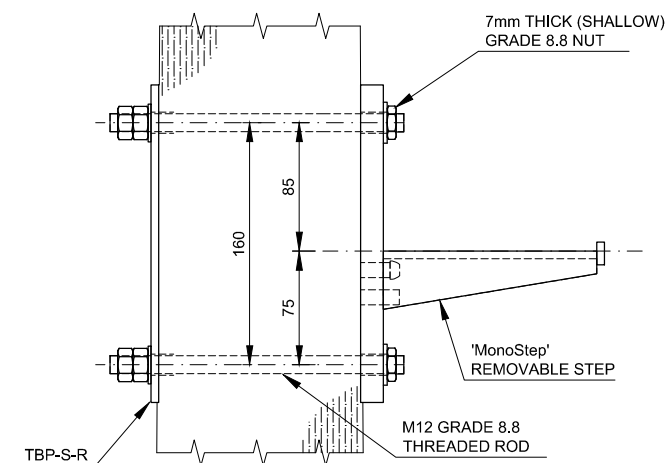

DETAIL F - REMOVABLE
CLIMBING STEPS
Scale 1:5

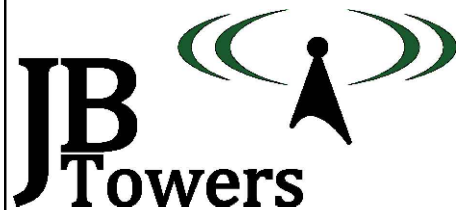

01	FIRST ISSUE			AM	22/10/20
REV	REV			BY	DATE
SCALE AS SHOWN WHEN PRINTED AT A3		DRAWN	AM	CHECKED	MP
		DATE	22/10/20	DATE	22/10/20
		DATE	22/10/20	DATE	22/10/20
ALL DIMENSIONS IN mm UNLESS OTHERWISE STATED. THIS DRAWING TO BE READ IN CONJUNCTION WITH OTHER RELEVANT DRAWINGS.					

TITLE
SUNDERLAND
GENERAL ARRANGEMENT
SHEET 3 OF 3

SITE ADDRESS
THE PRECINCT
TUNSTALL HILL
SUNDERLAND
TYNE AND WEAR
SR2 9DN

ARQIVA REF.
141622


DRG No.
200

REV
01

ALL SCALES AS SHOWN WHEN PRINTED AT A3



ALL SCALES AS SHOWN WHEN PRINTED AT A3

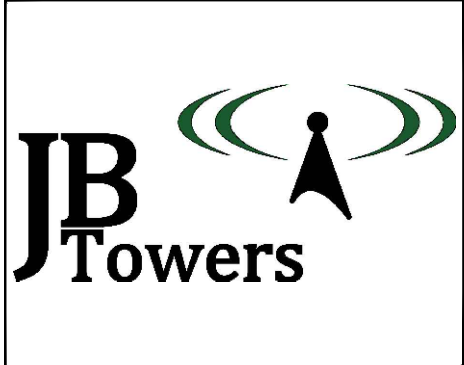

01	FIRST ISSUE							AM	22/10/20
REV	REV							BY	DATE
SCALE AS SHOWN WHEN PRINTED AT A3		DRAWN AM		CHECKED MP		APPROVED JBT			
		DATE 22/10/20		DATE 22/10/20		DATE 22/10/20			
ALL DIMENSIONS IN mm UNLESS OTHERWISE STATED. THIS DRAWING TO BE READ IN CONJUNCTION WITH OTHER RELEVANT DRAWINGS.									

TITLE

SUNDERLAND




TIMBER POLE HOLE SET OUT

SHEET 1 OF 2


SITE ADDRESS

THE PRECINCT
TUNSTALL HILL
SUNDERLAND
TYNE AND WEAR
SR2 9DN


ARQIVA REF. 141622	DRG No. 201	REV 01
-----------------------	----------------	-----------

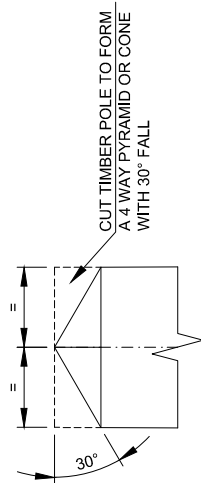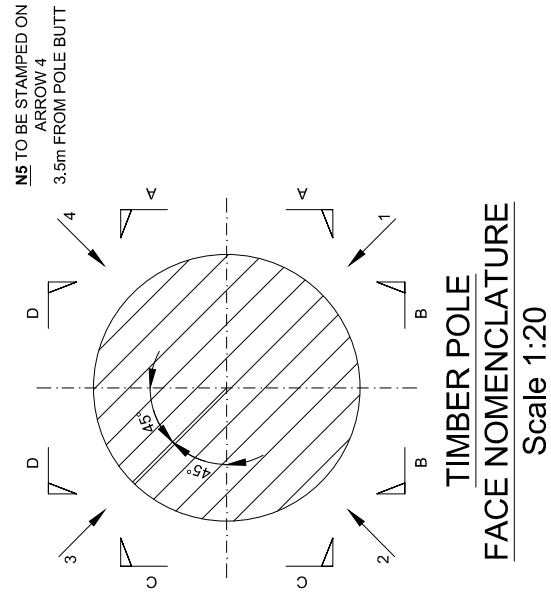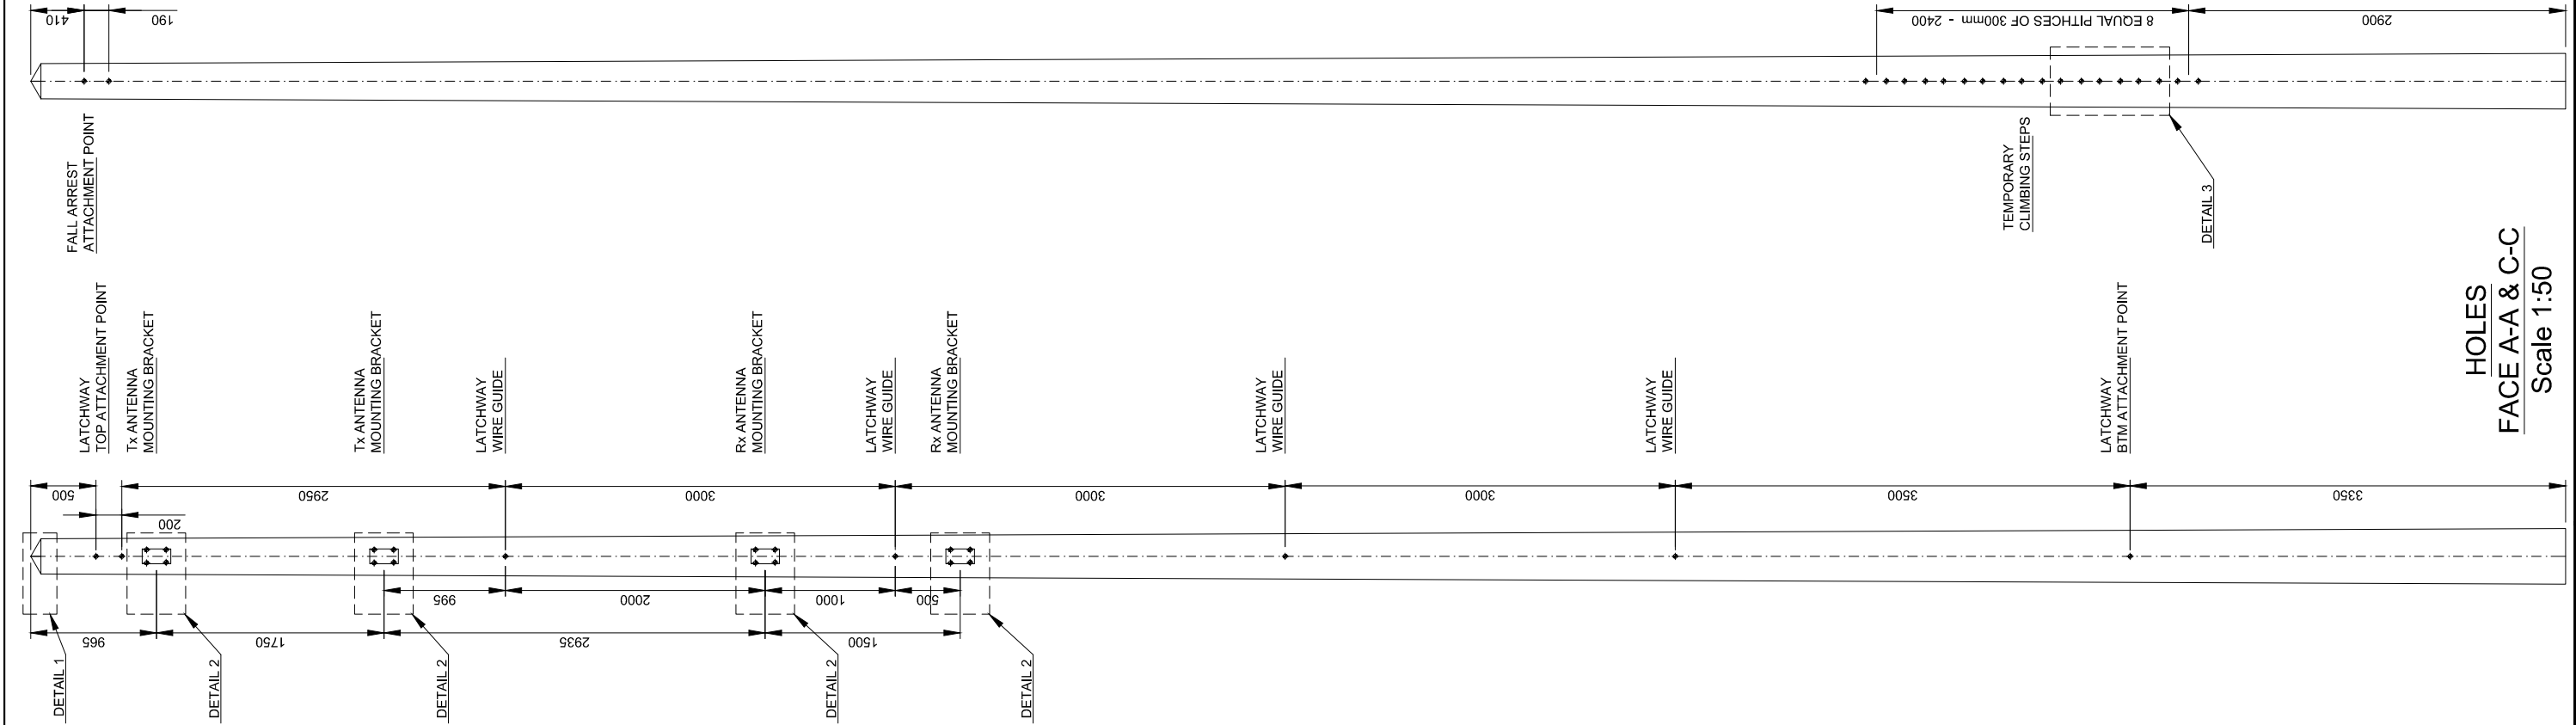REV
01

DETAIL 1
Scale 1:10

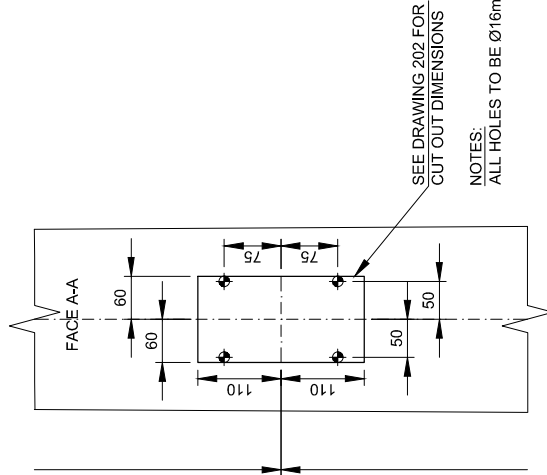

DETAIL 2 - TYPICAL
Scale 1:10

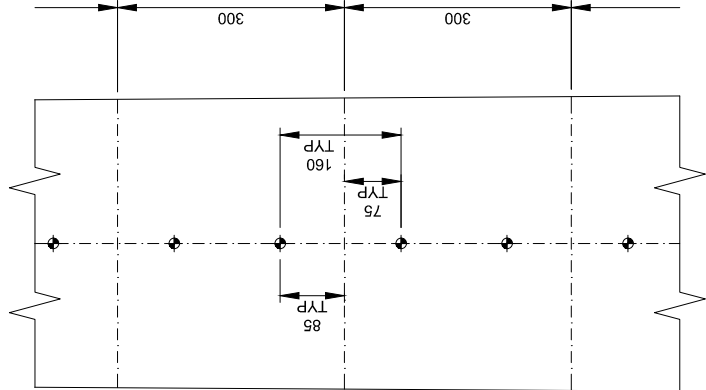

DETAIL 3 - TYPICAL
Scale 1:10




HOLES
FACE B-B & D-D
Scale 1:50

HOLES
FACE A-A & C-C
Scale 1:50



ALL SCALES AS SHOWN WHEN PRINTED AT A3

ALL SCALES AS SHOWN WHEN PRINTED AT A3

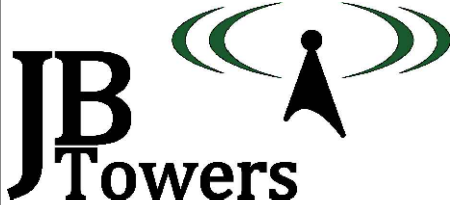

01	FIRST ISSUE			AM	22/10/20
REV	REV			BY	DATE
SCALE AS SHOWN		DRAWN	AM	CHECKED	MP
WHEN PRINTED AT A3		DATE	22/10/20	DATE	22/10/20
		APPROVED	JBT	DATE	22/10/20
ALL DIMENSIONS IN mm UNLESS OTHERWISE STATED. THIS DRAWING TO BE READ IN CONJUNCTION WITH OTHER RELEVANT DRAWINGS.					

TITLE

SUNDERLAND

TIMBER POLE HOLE SET OUT

SHEET 2 OF 2

SITE ADDRESS

THE PRECINCT

TUNSTALL HILL

SUNDERLAND

TYNE AND WEAR

SR2 9DN

ARQIVA REF.


141622

DRG No.

201

REV

01

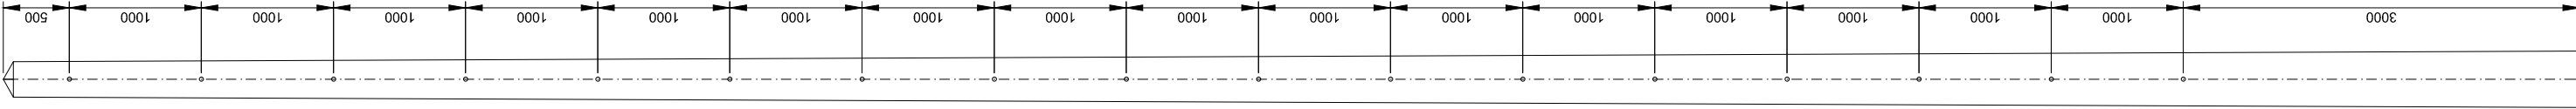



FEEDER BRACKETS

ALL HOLES ON ARROW 1
TO BE Ø8mm & 70mm LONG

HOLES

ARROW 1

Scale 1:50

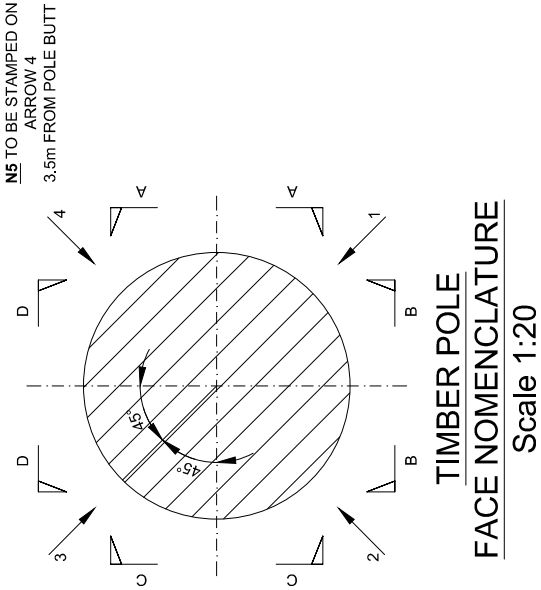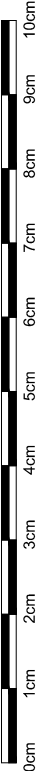

ALL SCALES AS SHOWN WHEN PRINTED AT A3


01	FIRST ISSUE			AM	22/10/20
REV	REV			BY	DATE
SCALE AS SHOWN		DRAWN	AM	CHECKED	MP
WHEN PRINTED AT A3		DATE	22/10/20	DATE	22/10/20
APPROVED		JBT			
DATE		22/10/20			
ALL DIMENSIONS IN mm UNLESS OTHERWISE STATED. THIS DRAWING TO BE READ IN CONJUNCTION WITH OTHER RELEVANT DRAWINGS.					


TITLE

SUNDERLAND

TIMBER POLE CUT OUT
DETAIL


SITE ADDRESS		
THE PRECINCT TUNSTALL HILL SUNDERLAND TYNE AND WEAR SR2 9DN		
ARQIVA REF. 141622	DRG No. 202	REV 01

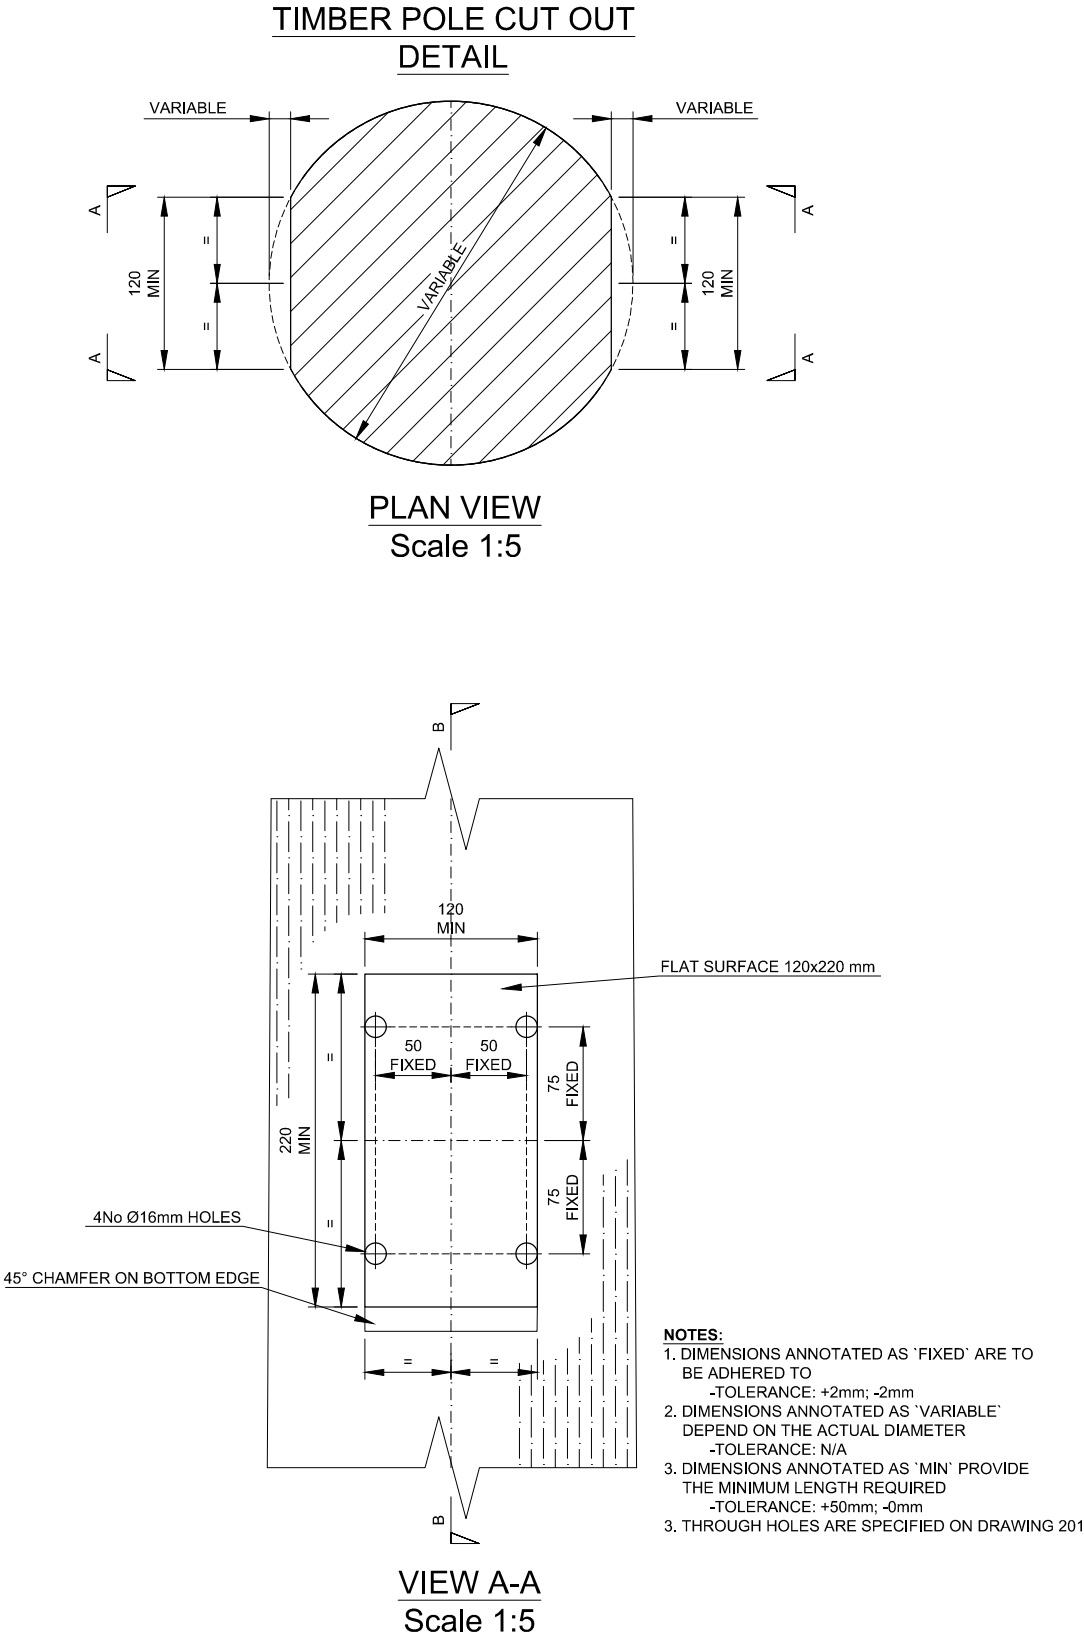

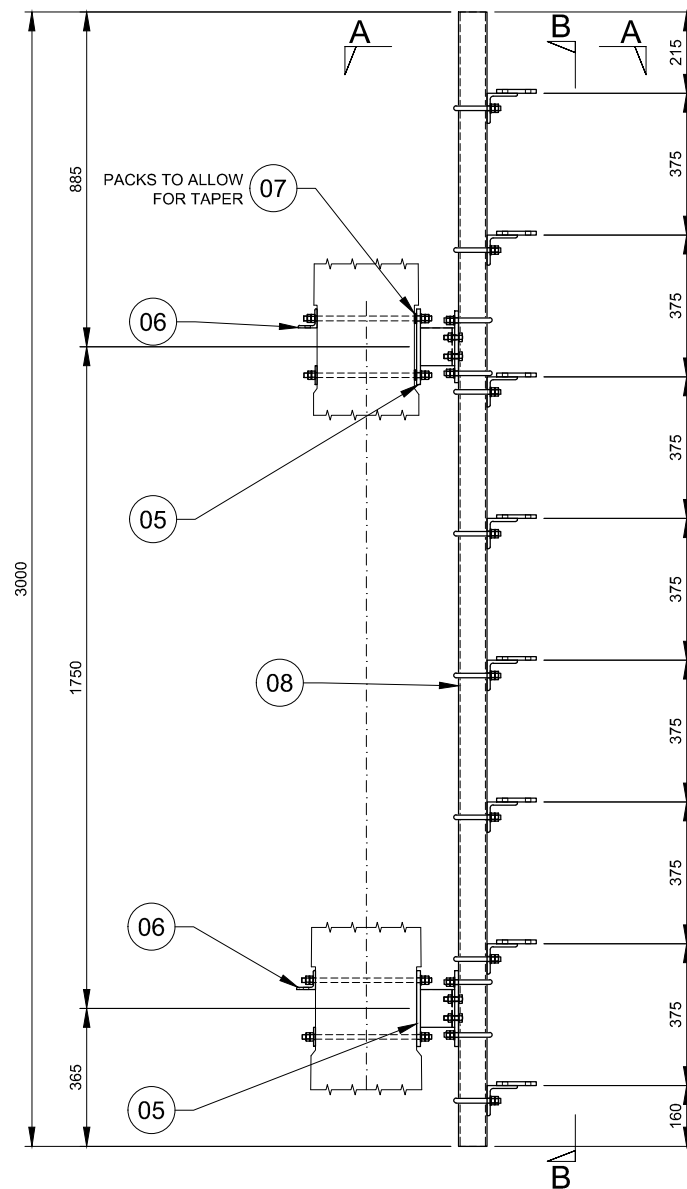


DETAIL G - Tx ANTENNA MOUNT
Scale 1:20

POSITION OF POWER
DIVIDER
TO BE DETERMINED
ON SITE

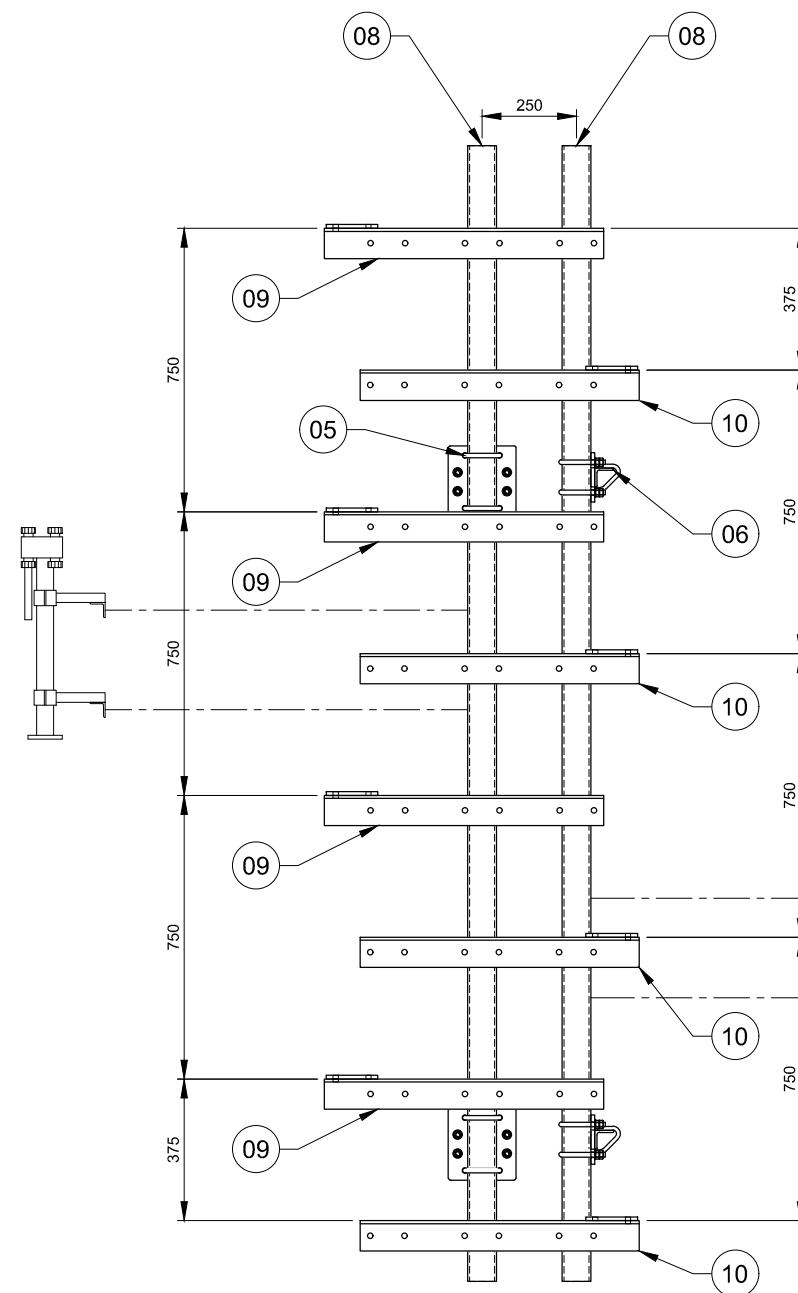


SECTION B-B
Scale 1:20

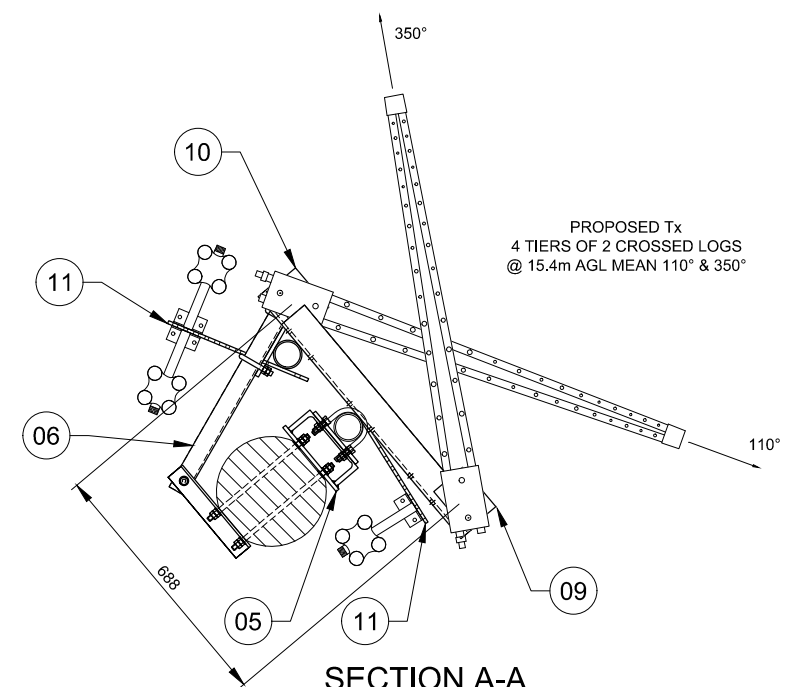

SECTION A-A
Scale 1:20


POSITION OF POWER
DIVIDERS
TO BE DETERMINED
ON SITE

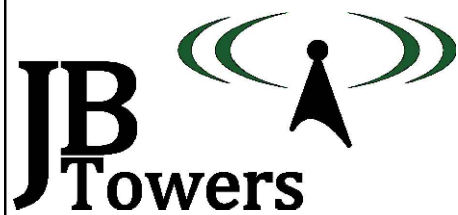

02	MINOR UPDATE			AM 20/11/2
01	FIRST ISSUE			AM 22/10/2
REV	REV			BY DATE
SCALE AS SHOWN		DRAWN AM	CHECKED MP	APPROVED JBT
WHEN PRINTED AT A3		DATE 22/10/20	DATE 22/10/20	DATE 22/10/20
ALL DIMENSIONS IN mm UNLESS OTHERWISE STATED. THIS DRAWING TO BE READ IN CONJUNCTION WITH OTHER RELEVANT DRAWINGS.				


TITLE	SUNDERLAND		SITE ADDRESS	
	Tx ANTENNA MOUNT		THE PRECINCT	
	DETAIL G		TUNSTALL HILL	
			SUNDERLAND	
			TYNE AND WEAR	
			SR2 9DN	
	ARQIVA REF.	DRG No.	REV	
	141622	203	02	

ALL SCALES AS SHOWN WHEN PRINTED AT A3

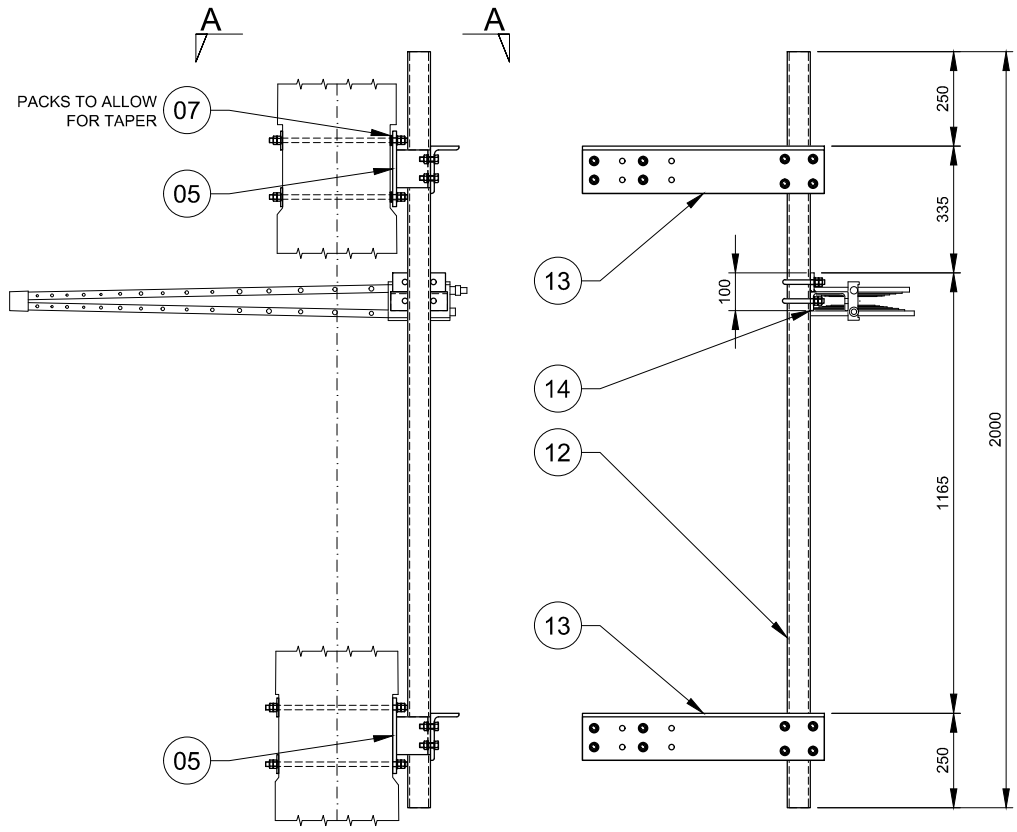


DETAIL H - Rx ANTENNA MOUNT
Scale 1:20

SECTION B-B
Scale 1:20

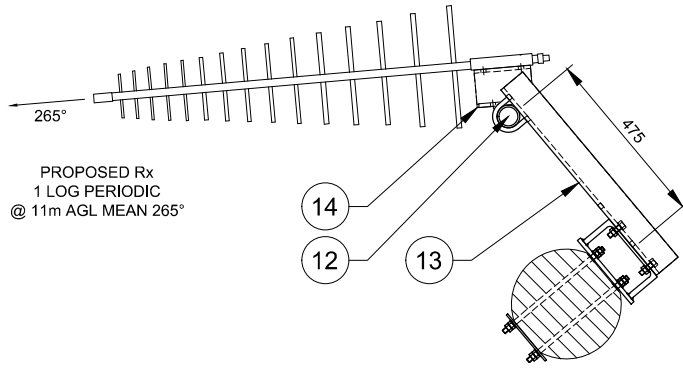

SECTION A-A
Scale 1:20

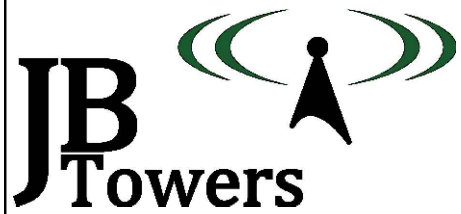


01	FIRST ISSUE					AM	22/10/20
REV	REV					BY	DATE
SCALE AS SHOWN		DRAWN AM		CHECKED MP		APPROVED JBT	
WHEN PRINTED AT A3		DATE 22/10/20		DATE 22/10/20		DATE 22/10/20	
ALL DIMENSIONS IN mm UNLESS OTHERWISE STATED. THIS DRAWING TO BE READ IN CONJUNCTION WITH OTHER RELEVANT DRAWINGS.							


TITLE
SUNDERLAND
Rx ANTENNA MOUNT
DETAIL H

SITE ADDRESS THE PRECINCT TUNSTALL HILL SUNDERLAND TYNE AND WEAR SR2 9DN		
ARQIVA REF. 141622	DRG No. 204	REV 01

ALL SCALES AS SHOWN WHEN PRINTED AT A3

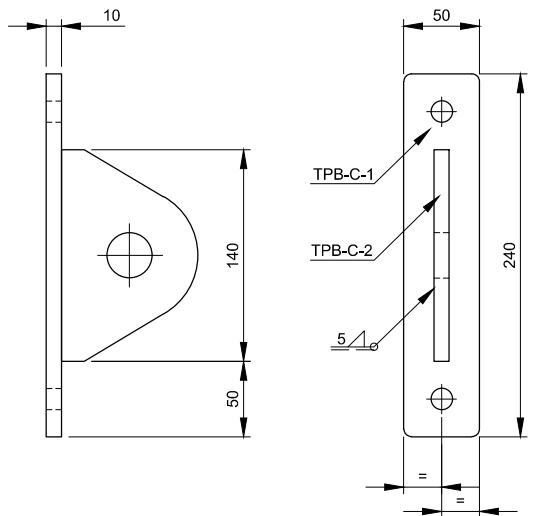

PART TPB-C
Scale 1:5

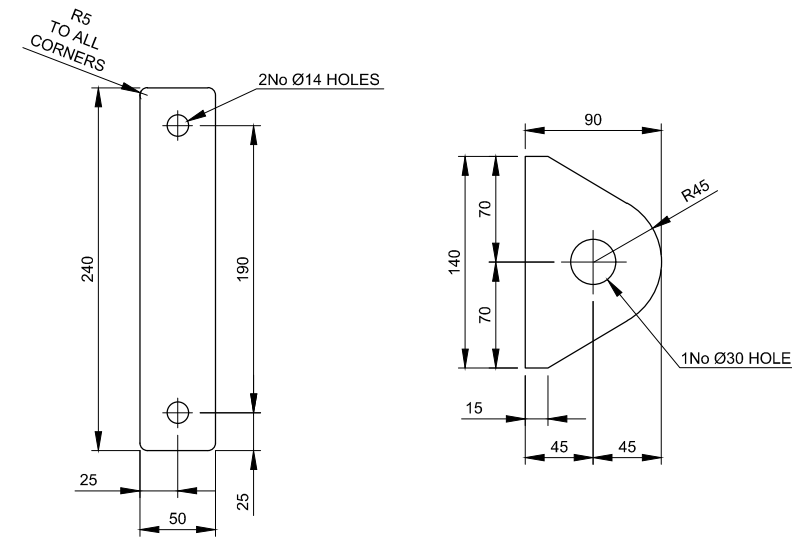


TPB-C-1 - 10mm THICK
Scale 1:5

TPB-C-2 - 10mm THICK
Scale 1:5


Parts list for TPB-C

Item	Part	Quantity	Part description	Length	Material	Weight
01	TPB-C-1	1	Plate 240x50x10mm	N/A	S275J0	0.94 kg
02	TPB-C-2	1	Plate 140x90x10mm	N/A	S275J0	0.99 kg
03	STUDS	1	M12 STUDDING	350mm	GRADE 8.8	0.31 kg
Total Weight:						2.24 kg

- All steel hot dip galvanized
- Each STUD to be supplied with 4 Full Nuts, 2 Flat Washers and 2 Spring Washers
- For fabrication notes see drawing 305

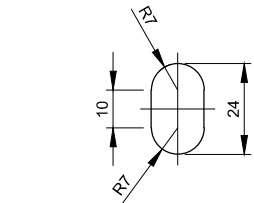

SLOTTED HOLE DETAIL
Scale 1:2

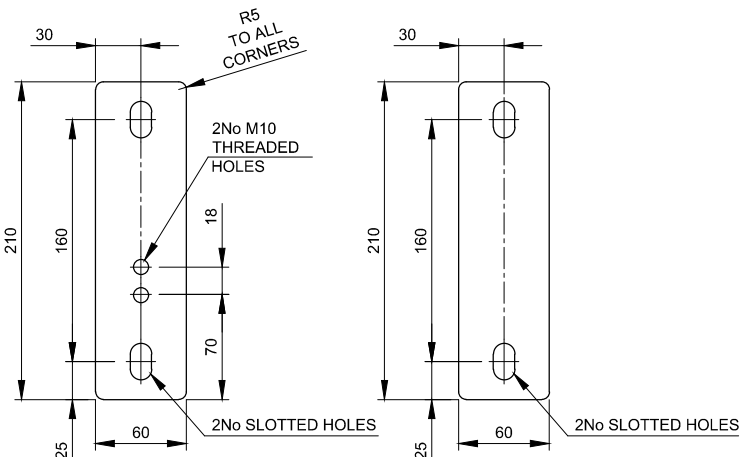


PART TPS-R-1
Scale 1:5

PART TPS-R-2
Scale 1:5

Parts list for TPS-R

Item	Part	Quantity	Part description	Length	Material	Weight
01	TPS-R-1	1	Plate 210x60x15mm	N/A	S275J0	1.48 kg
02	TPS-R-2	1	Plate 210x60x5mm	N/A	S275J0	0.49 kg
03	STUDS	2	M12 STUDDING	500mm	GRADE 8.8	0.44 kg
04	NUT-S	2	M12 SHALLOW NUT	N/A	GRADE 8.8	-
05	NUT	4	M12 NUT	N/A	GRADE 8.8	-
06	WSH	4	M12 WASHER	N/A	GRADE 8.8	-
Total Weight:						2.41 kg

- All steel hot dip galvanized
- For fabrication notes see drawing 305

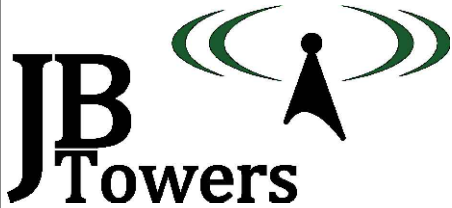

01	FIRST ISSUE			AM	22/10/20
REV	REV			BY	DATE
SCALE AS SHOWN WHEN PRINTED AT A3		DRAWN AM	CHECKED MP	APPROVED	JBT
		DATE 22/10/20	DATE 22/10/20	DATE 22/10/20	
ALL DIMENSIONS IN mm UNLESS OTHERWISE STATED. THIS DRAWING TO BE READ IN CONJUNCTION WITH OTHER RELEVANT DRAWINGS.					








TITLE
SUNDERLAND
ATTACHMENT POINT &
TEMPORARY STEP DETAILS
PARTS: TPB-C; TPS-R

SITE ADDRESS
THE PRECINCT
TUNSTALL HILL
SUNDERLAND
TYNE AND WEAR
SR2 9DN
ARQIVA REF.
141622
DRG No.
300
REV
01

ALL SCALES AS SHOWN WHEN PRINTED AT A3



ALL SCALES AS SHOWN WHEN PRINTED AT A3

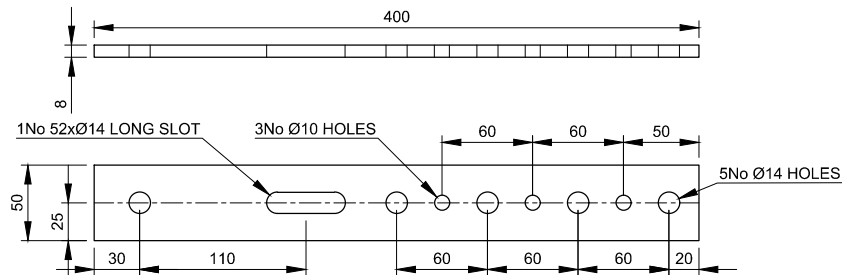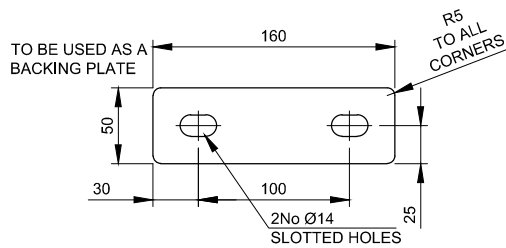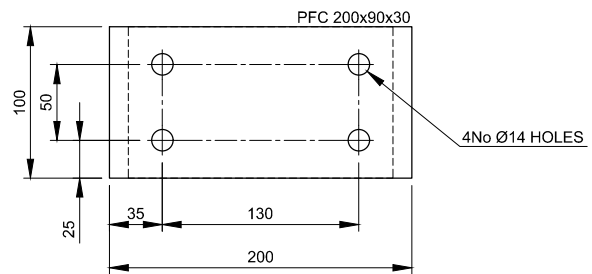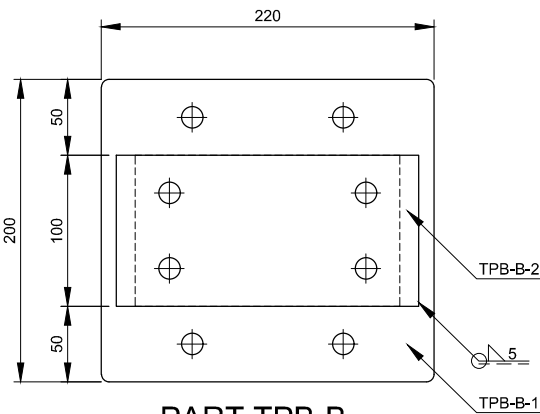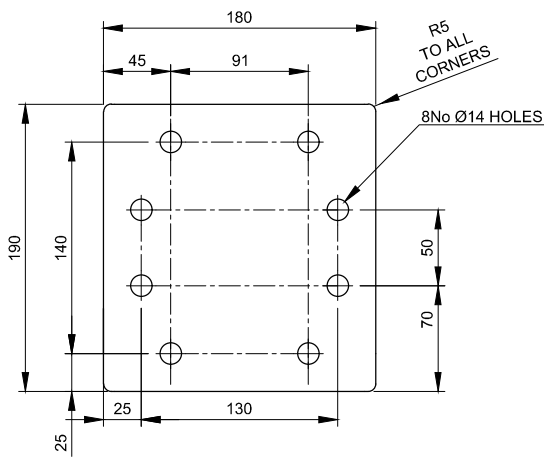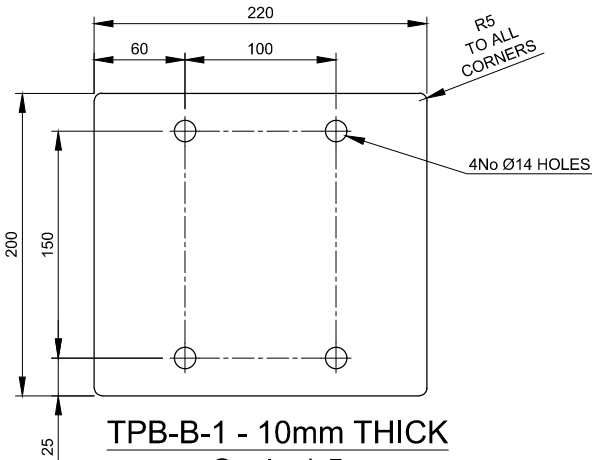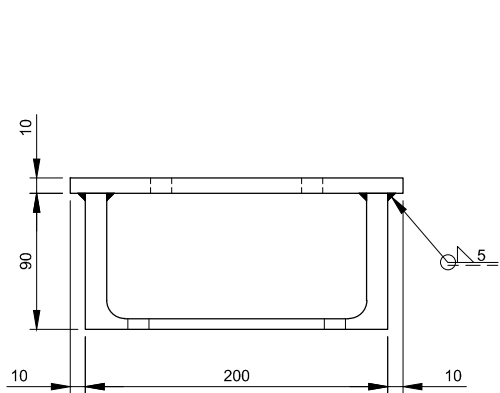


Parts list for TPB-B

Item	Part	Quantity	Part description	Length	Material	Weight
01	TPB-B-1	1	Plate 220x200x10mm	N/A	S275J0	3.45 kg
02	TPB-B-2	1	PFC 200x90x30	100mm	S275J0	3.00 kg
03	TPB-B-4	2	Plate 160x50x5mm	N/A	S275J0	0.31 kg
04	TPB-B-5	1	Plate 190x180x10mm	N/A	S275J0	2.70 kg
05	STUDS	4	M12 STUDDING	450mm	GRADE 8.8	0.39 kg
06	BOLT	4	M12 45mm LONG (2D+6)	45mm	GRADE 8.8	-
07	U-BOLT	2	M12 U-BOLT FOR CHS 76.1	N/A	GRADE 8.8	-

- All steel hot dip galvanized
- Each STUD & U-BOLT to be supplied with 4 Full Nuts, 2 Flat Washers and 2 Spring Washers
- Each BOLT to be supplied with 1 Full Nut, 1 Form E FLat Washer and 1 Spring Washer
- For fabrication notes see drawing 305

Total Weight: 11.33 kg

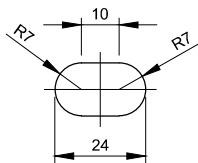


SLOTTED HOLE DETAIL
Scale 1:2

Parts list for TPA-PD

Item	Part	Quantity	Part description	Length	Material	Weight
01	TPA-PD	1	400x50x8mm	N/A	S275J0	1.26 kg
02	U-BOLT	1	M12 U-BOLT FOR CHS 76.1mm	N/A	GRADE 8.8	-

Total Weight: 1.26 kg

- All steel hot dip galvanized
- Each U-BOLT to be supplied with 4 Full Nuts, 2 Flat Washers and 2 Spring Washers
- For fabrication notes see drawing 305

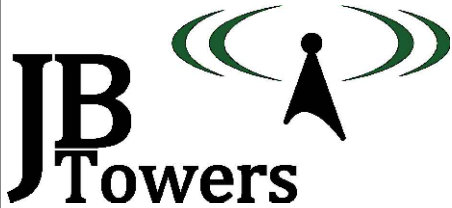

01	FIRST ISSUE	AM	22/10/20
REV	REV	BY	DATE
SCALE AS SHOWN	DRAWN	CHECKED	APPROVED
WHEN PRINTED AT A3	DATE	DATE	DATE
ALL DIMENSIONS IN mm UNLESS OTHERWISE STATED. THIS DRAWING TO BE READ IN CONJUNCTION WITH OTHER RELEVANT DRAWINGS.			

TITLE
SUNDERLAND
STEELWORK BRACKET,
POWER DIVIDER STRAP
PARTS: TPB-B, TPA-PD


SITE ADDRESS
THE PRECINCT
TUNSTALL HILL
SUNDERLAND
TYNE AND WEAR
SR2 9DN

ARQIVA REF. 141622	DRG No. 301	REV 01
-----------------------	----------------	-----------

ALL SCALES AS SHOWN WHEN PRINTED AT A3





ALL SCALES AS SHOWN WHEN PRINTED AT A3

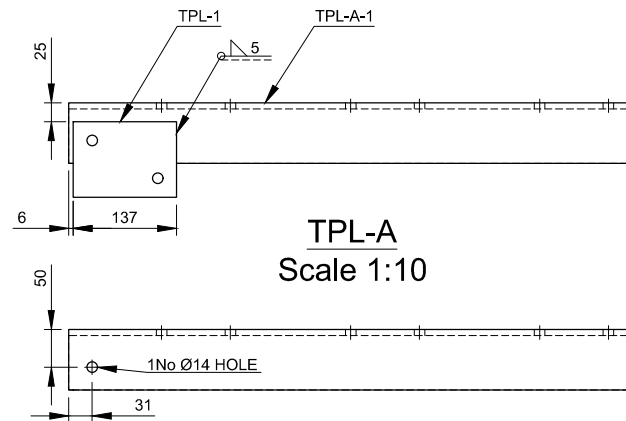



TPL-A
Scale 1:10

TPL-A-1 - EA 80x80x8
Scale 1:10

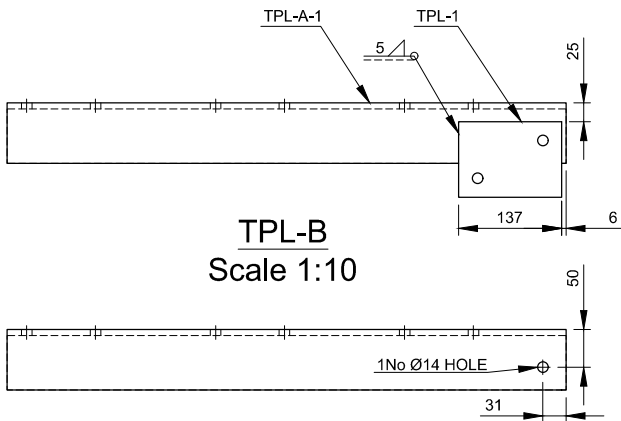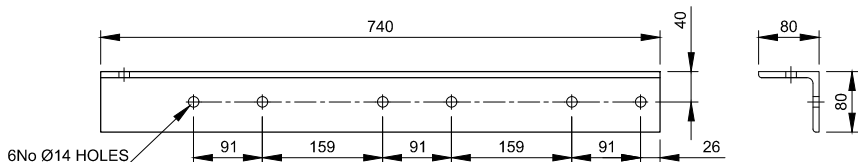

TPL-B
Scale 1:10

TPL-B-1 - EA 80x80x8
Scale 1:10

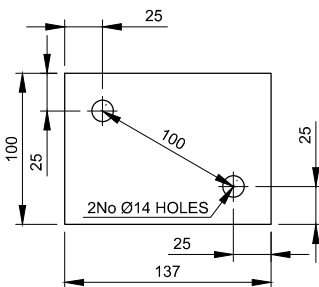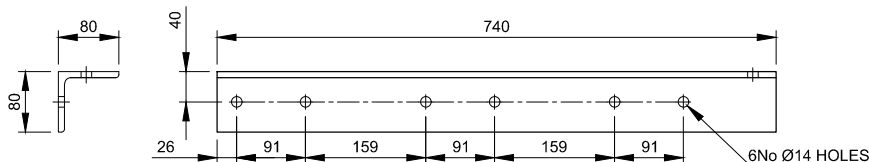

TPL-1 - 10mm THICK
Scale 1:5

Parts list for TPL-A


Item	Part	Quantity	Part description	Length	Material	Weight
01	TPL-A-1	1	EA 80x80x8	740mm	S275J0	7.20 kg
02	TPL-1	1	Plate 137x100x10	N/A	S275J0	1.10 kg
03	U-BOLT	2	M12 U-BOLT FOR CHS 76.1mm	N/A	GRADE 8.8	-
Total Weight:						8.30 kg

- All steel hot dip galvanized
- Each U-BOLT to be supplied with 4 Full Nuts, 2 Flat Washers and 2 Spring Washers
- For fabrication notes see drawing 305

Parts list for TPL-B

Item	Part	Quantity	Part description	Length	Material	Weight
01	TPL-B-1	1	EA 80x80x8	740mm	S275J0	7.20 kg
02	TPL-1	1	Plate 137x100x10	N/A	S275J0	1.10 kg
03	U-BOLT	2	M12 U-BOLT FOR CHS 76.1mm	N/A	GRADE 8.8	-
Total Weight:						8.30 kg

- All steel hot dip galvanized
- Each U-BOLT to be supplied with 4 Full Nuts, 2 Flat Washers and 2 Spring Washers
- For fabrication notes see drawing 305

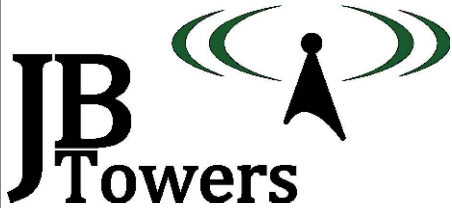

01	FIRST ISSUE	AM	22/10/20
REV	REV	BY	DATE
SCALE AS SHOWN	DRAWN	CHECKED	APPROVED
WHEN PRINTED AT A3	DATE	DATE	DATE
ALL DIMENSIONS IN mm UNLESS OTHERWISE STATED. THIS DRAWING TO BE READ IN CONJUNCTION WITH OTHER RELEVANT DRAWINGS.			


TITLE
SUNDERLAND
LOG MOUNTS
PARTS: TPL-A; TPL-B

SITE ADDRESS
THE PRECINCT
TUNSTALL HILL
SUNDERLAND
TYNE AND WEAR
SR2 9DN

ARQIVA REF.
141622

DRG No.
302

REV
01

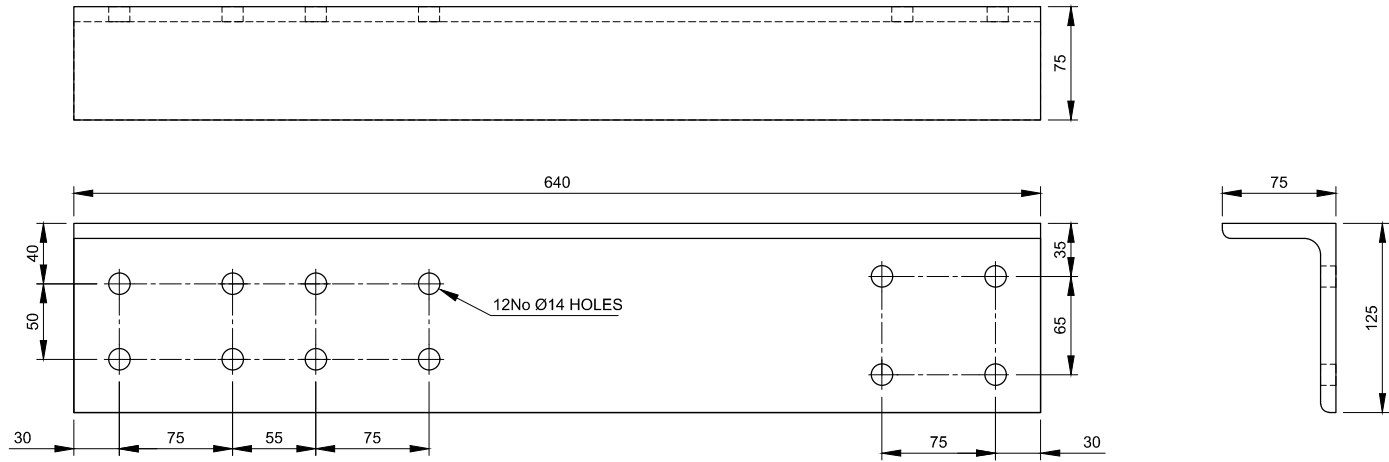


TPL-C - UA125x75x10
Scale 1:5

Parts list for 1No. TPL-C

Item	Part	Quantity	Part description	Length	Material	Weight
01	TPL-C	1	UA125x75x10	640mm	S275J0	9.60 kg
02	U-BOLT	2	M12 U-BOLT FOR CHS 60.3mm	N/A	GRADE 8.8	-
03	BOLT	4	M12x45 (2D+6) BOLT	N/A	GRADE 8.8	-
Total Weight:						9.60 kg

- Each STUD & U-BOLT to be supplied with 4 Full Nuts, 2 Flat Washers and 2 Spring Washers
- Each BOLT to be supplied with 1 Full Nut, 1 Form E FLat Washer and 1 Spring Washer

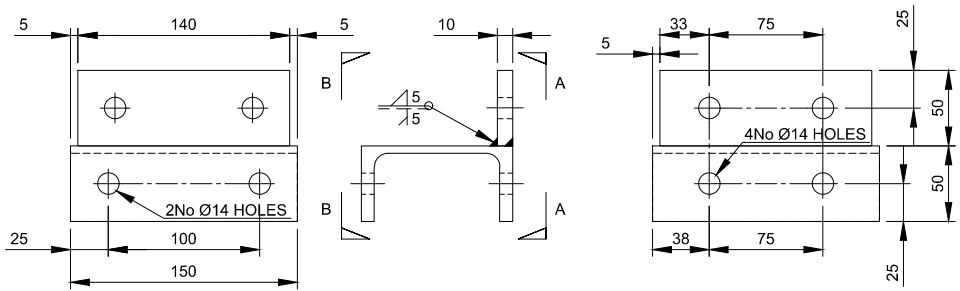

VIEW B-B
Scale 1:5


TPL-D
Scale 1:5

VIEW A-A
Scale 1:5

Parts list for TPL-D

Item	Part	Quantity	Part description	Length	Material	Weight
01	TPL-C-1	1	PFC100x50x10	150mm	S275J0	1.50 kg
02	TPL-2	1	PLATE 140x50x10	-	S275J0	0.55 kg
03	U-BOLT	2	M12 U-BOLT FOR CHS 60.3mm	N/A	GRADE 8.8	-
Total Weight:						2.05 kg

- All steel hot dip galvanized
- Each U-BOLT to be supplied with 4 Full Nuts, 2 Flat Washers and 2 Spring Washers
- For fabrication notes see drawing 305

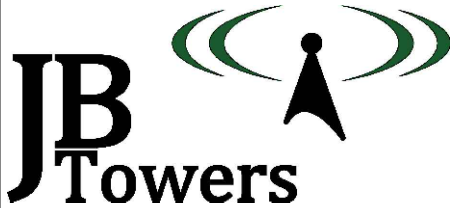

01	FIRST ISSUE			AM	22/10/20
REV	REV			BY	DATE
SCALE AS SHOWN WHEN PRINTED AT A3		DRAWN AM	CHECKED MP	APPROVED	JBT
		DATE 22/10/20	DATE 22/10/20	DATE 22/10/20	
ALL DIMENSIONS IN mm UNLESS OTHERWISE STATED. THIS DRAWING TO BE READ IN CONJUNCTION WITH OTHER RELEVANT DRAWINGS.					

TITLE
SUNDERLAND
LOG MOUNTS
PARTS: TPL-C; TPL-D

SITE ADDRESS
THE PRECINCT
TUNSTALL HILL
SUNDERLAND
TYNE AND WEAR
SR2 9DN

ARQIVA REF.
141622


DRG No.
303

REV
01


ALL SCALES AS SHOWN WHEN PRINTED AT A3



ALL SCALES AS SHOWN WHEN PRINTED AT A3


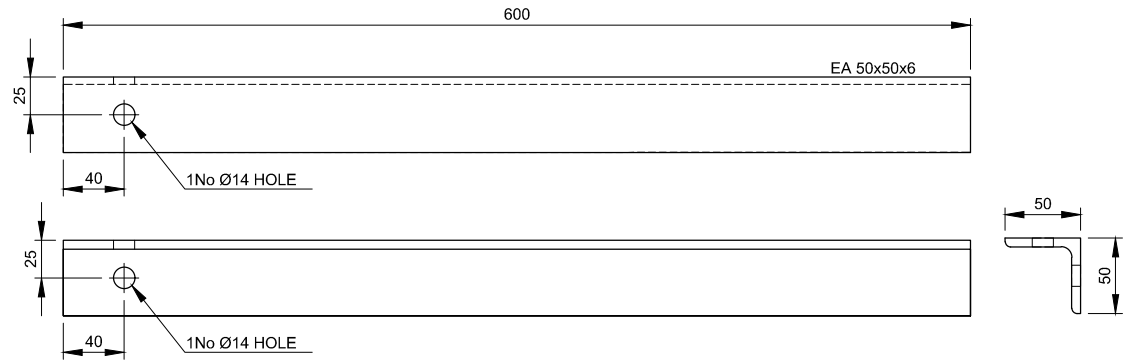


TPB-BR-1 - EA50x50x6
Scale 1:5

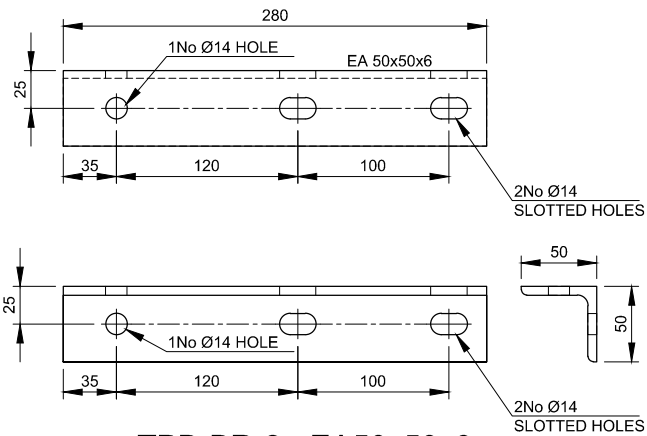

TPB-BR-2 - EA50x50x6
Scale 1:5


TPB-BR-3 - 10mm THICK
Scale 1:5

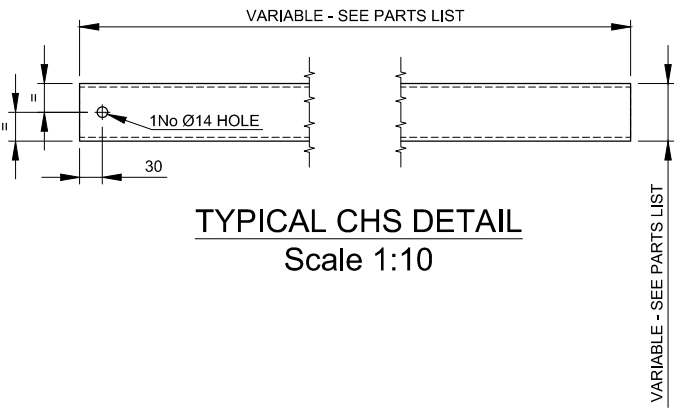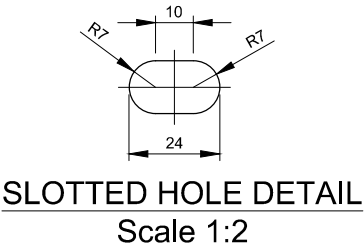

Parts list for TPB-BR

Item	Part	Quantity	Part description	Length	Material	Weight
01	TPB-BR-1	1	EA 50x50x6	280mm	S275J0	1.25 kg
02	TPB-BR-2	1	EA 50x50x6	600mm	S275J0	2.50 kg
03	TPB-BR-3	1	Plate 130x190x10mm	N/A	S275J0	1.95 kg
04	BOLT	1	M12 SET BOLT - 30mm LONG	N/A	GRADE 8.8	-
05	N-BOLT	2	M12 N-BOLT FOR EA 50x50x6	N/A	GRADE 8.8	-
06	U-BOLT	2	M12 U-BOLT FOR CHS 76.1mm	N/A	GRADE 8.8	-
Total Weight:						5.70 kg

- All steel hot dip galvanized
- Each BOLT to be supplied with 1 Full Nut, 1 Form E FLat Washer and 1 Spring Washer
- Each STUD & U-BOLT to be supplied with 4 Full Nuts, 2 Flat Washers and 2 Spring Washers
- For fabrication notes see drawing 305

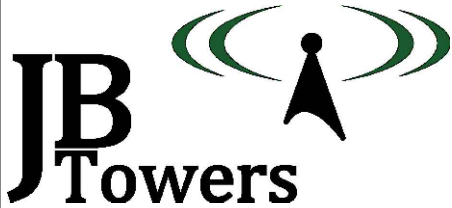


01	FIRST ISSUE			AM	22/10/20
REV	REV			BY	DATE
SCALE AS SHOWN WHEN PRINTED AT A3		DRAWN AM	CHECKED MP	APPROVED	JBT
		DATE 22/10/20	DATE 22/10/20	DATE 22/10/20	
ALL DIMENSIONS IN mm UNLESS OTHERWISE STATED. THIS DRAWING TO BE READ IN CONJUNCTION WITH OTHER RELEVANT DRAWINGS.					

TITLE
SUNDERLAND
BRACING ARM & TYPICAL
CHS DETAIL
PART: TPB-BR

SITE ADDRESS
THE PRECINCT
TUNSTALL HILL
SUNDERLAND
TYNE AND WEAR
SR2 9DN
ARQIVA REF.
141622
DRG No.
304
REV
01

ALL SCALES AS SHOWN WHEN PRINTED AT A3

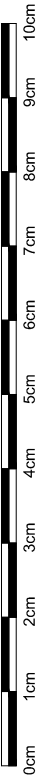


ALL SCALES AS SHOWN WHEN PRINTED AT A3

Item	Part	Drawing	Quantity	Part description	Length	Material	Weight
01	01	200	1	3 MAN LATCHWAY SYSTEM & 4No. WIRE GUIDES FOR FACE MOUNTED MONOPOLE	17000	N/A	-
02	TPB-C	300	2	FALL ARREST ATTACHMENT POINT	N/A	S275J0	4.50 kg
03	03	200	46	PERMANENT BT STEP c/w 3No 10x75mm ZINC-PLATED COACH SCREWS	N/A	S275J0	14.40 kg
04	TPS-R	300	9	'MonoStep' ASSEMBLY	N/A	S275J0	21.70 kg
05	TPB-B	301	4	MOUNTING BRACKET	N/A	S275J0	45.30 kg
06	TPB-BR	304	2	BRACING ARM	N/A	S275J0	11.40 kg
07	07	203	24	M12 WASHER	N/A	GRADE 8.8	-
08	08	203	2	CHS 76.1x5mm	3000mm	S355J2H	52.60 kg
09	TPL-A	302	4	LOG MOUNTING BRACKET	740mm	S275J0	33.20 kg
10	TPL-B	302	4	LOG MOUNTING BRACKET	740mm	S275J0	33.20 kg
11	TPA-PD	301	6	POWER DIVIDER STRAP	N/A	S275J0	7.60 kg
12	12	204	1	CHS 60.3x5mm	2000mm	S355J2H	14.00 kg
13	TPL-C	303	2	LOG MOUNTING BRACKET	640mm	S275J0	19.20 kg
14	TPL-D	303	1	LOG MOUNTING BRACKET	100mm	S275J0	2.05 kg
14	14	200	1	PoleSaver	750mm	N/A	-
15	15	200	7	M12 STUD + 4No NUTS + 2No FLAT WASHERS + 1No Ø50mm WASHER (FOR FALL ARREST SYSTEM)	500mm	GRADE 8.8	3.10 kg
16	16	200	1	FEEDER COVER - 2/CG/100	3500mm	UV RESISTANT PLASTIC	-
17	17	200	17	FEEDER CLAMP - 2/FCD/028	N/A	POLYPROPYLENE	-
18	18	200	17	M10 SCREW DOWELS WTH M10 NUT	100mm	STAINLESS STEEL	-
Total Weight:							262.25 kg

- All steel hot dip galvanized
- All U-BOLTS to be FLA supply, each Supplied with 4 Full Nuts, 2 Flat Washers and 2 Spring Washers

NOTES:

1. WELDING TO BE IN ACCORDANCE WITH BS EN 1011-1:2009
2. LINEAR DIMS TO BE WITHIN ±1mm;
3. ANGULAR TOLERANCES TO BE WITHIN 0.5°
4. WELDING SYMBOLS ARE IN ACCORDANCE WITH BS EN 22553:1995
5. ALL PROFILE EDGES TO BE DRESSED AND SHARP CORNERS REMOVED
6. ALL WELD SIZES ARE FINAL SIZES
7. ALL WELDED JOINTS ARE TO BE PICKLE TIGHT
8. ALL STEELWORK TO BE BS EN 10025 GRADE S275 J0 UNO, HOT DIPPED GALVANISED TO BS EN ISO 1461. (ALL HOLLOW SECTIONS TO BE GRADE S355 J0H)
9. ALL STEEL IS TO BE SUPPLIED IN ACCORDANCE WITH EN 1090 TO EXECUTION CLASS 2
10. ALL NON PRE-LOADED BOLTS TO BE COMPLIANT STRUCTURAL BOLTS TO BS EN ISO 15048 PARTS 1&2.
11. STEELWORK COMPONENTS SHALL BE HOT DIP GALVANISED TO ACHIEVE A "VERY HIGH" DURABILITY FOR AN ENVIRONMENT CATEGORY CODE C4 FROM TABLE 1 IN BS EN ISO 14713
12. BOLTS AND NUTS SHALL BE SUPPLIED IN ACCORDANCE WITH BS 7371, SPUN GALVANISED IN ACCORDANCE WITH ISO 10684, THE NUTS RE-TAPPED AFTER GALVANISING, AND THE THREADS TREATED WITH GREASE.
13. ALL BOLTS TO BE CUT ON SITE TO EXTEND MAX 10mm BEYOND THE NUT WHEN TIGHTENED UNO.
14. ALL SITE DRILLED HOLE/CUT ENDS TO BE TREATED WITH METAFLUX 70-40 ZINC PASTE FOLLOWED BY 1 COAT OF 7-42 ZINC ALU OR 70-16 ALUMINIUM SPRAY

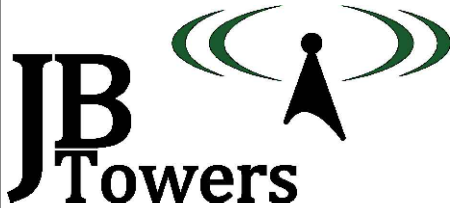

01	FIRST ISSUE			AM	22/10/20
REV	REV			BY	DATE
SCALE AS SHOWN		DRAWN	AM	CHECKED	MP
WHEN PRINTED AT A3		DATE	22/10/20	DATE	22/10/20
APPROVED		JBT			
ALL DIMENSIONS IN mm UNLESS OTHERWISE STATED.		THIS DRAWING TO BE READ IN CONJUNCTION WITH OTHER RELEVANT DRAWINGS.			

TITLE

SUNDERLAND

PARTS LIST

SITE ADDRESS


THE PRECINCT
TUNSTALL HILL
SUNDERLAND
TYNE AND WEAR
SR2 9DN

ARQIVA REF. 141622	DRG No. 305	REV 01
-----------------------	----------------	-----------


ALL SCALES AS SHOWN WHEN PRINTED AT A3



ALL SCALES AS SHOWN WHEN PRINTED AT A3

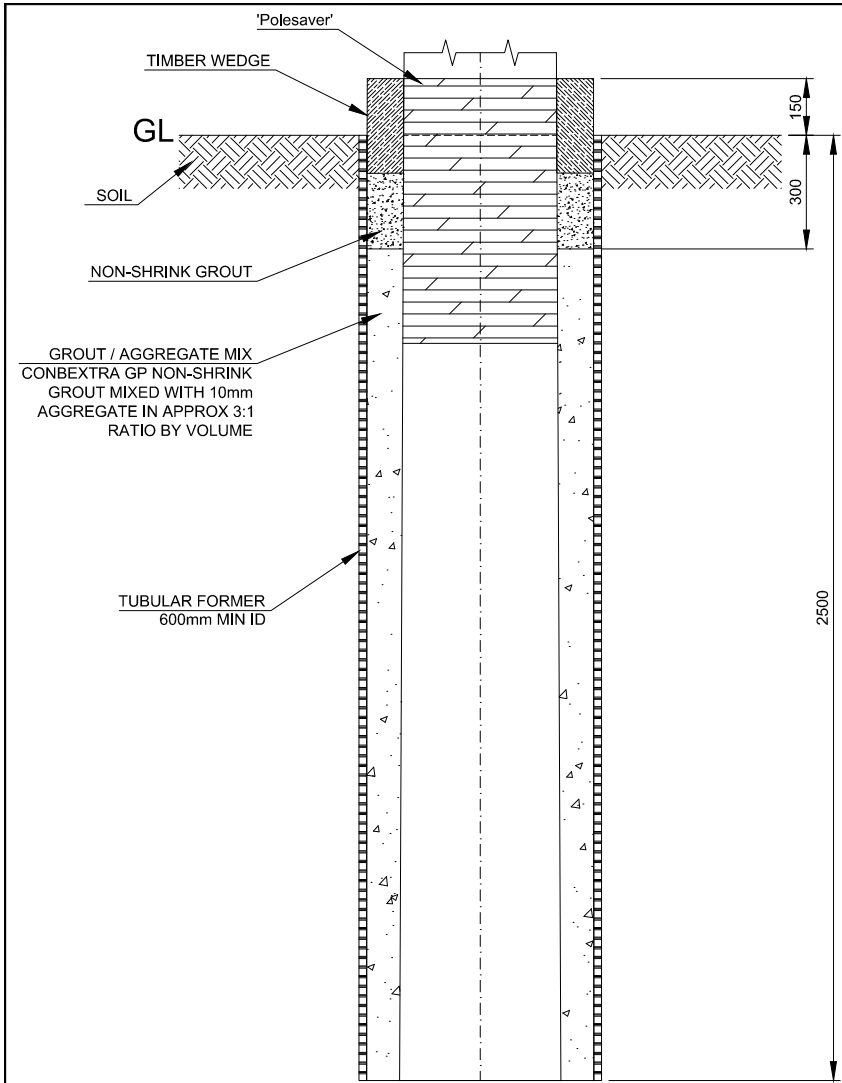


POROPOSED INSTALLATION
ELEVATION
Scale 1:20

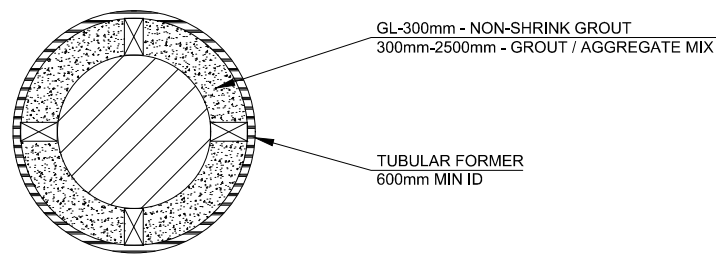


POROPOSED INSTALLATION
PLAN VIEW
Scale 1:20


- TIMBER POLE INSTALLATION:**
1. REFER TO DRAWING 200 FOR TIMBER POLE ORIENTATION
 2. HOLE TO BE AUGURED TO REQUIRED DEPTH
 3. IF REQUIRED A TUBULAR FORMER IS TO BE INSERTED AND THE ANNULUS BETWEEN THE FORMER AND THE SOIL GROUTED UP
 4. POLE TO BE WRAPPED IN 'POLESAVER' AND INSTALLED AND LEVELLED IN OPENING. TIMBERS TO BE USED TO HOLD POLE IN POSITION
 5. ANNULUS SHALL BE FILLED WITH GROUT / AGGREGATE MIX TO 300mm BELOW GL
 6. TOP 300mm SHALL BE FILLED WITH NON-SHRINK GROUT. A 1:60 FALL SHALL BE FORMED AROUND TIMBER POLE TO ALLOW WATER TO DRAIN AWAY FROM POLE
 7. ONCE GROUT HAS CURED REMOVE TIMBER WEDGES AND FILL REMAINING VOIDS WITH NON-SHRINK GROUT

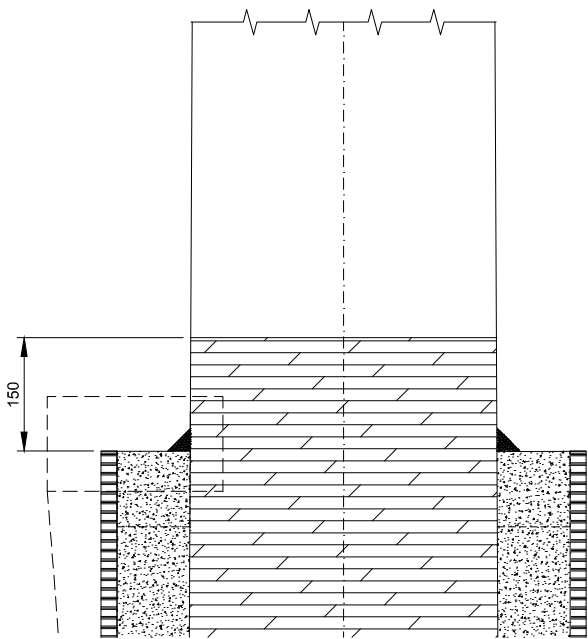

WATER PROOFING
Scale 1:10

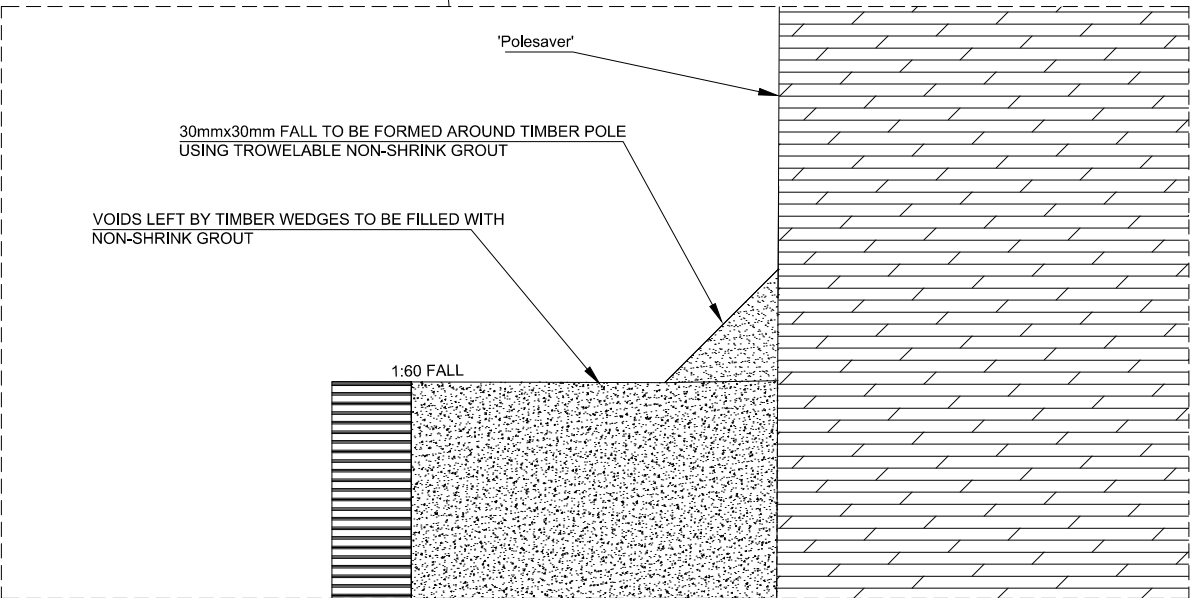

ENLARGED DETAIL
Scale 1:2

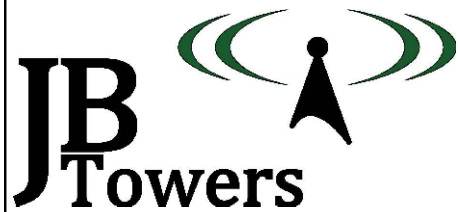


01	FIRST ISSUE			AM	22/10/20
REV	REV			BY	DATE
SCALE AS SHOWN WHEN PRINTED AT A3		DRAWN	AM	CHECKED	MP
		DATE	22/10/20	DATE	22/10/20
				APPROVED	JBT
				DATE	22/10/20
ALL DIMENSIONS IN mm UNLESS OTHERWISE STATED. THIS DRAWING TO BE READ IN CONJUNCTION WITH OTHER RELEVANT DRAWINGS.					

TITLE
SUNDERLAND
TIMBER POLE FOUNDATION
DETAILS

SITE ADDRESS
THE PRECINCT
TUNSTALL HILL
SUNDERLAND
TYNE AND WEAR
SR2 9DN

ARQIVA REF.
141622
DRG No.
400
REV
01

ALL SCALES AS SHOWN WHEN PRINTED AT A3

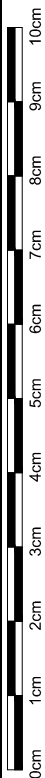

ALL SCALES AS SHOWN WHEN PRINTED AT A3