
 
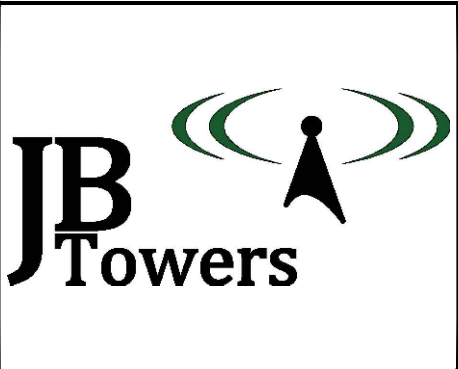


DRAWING ISSUE SHEET

[illegible]

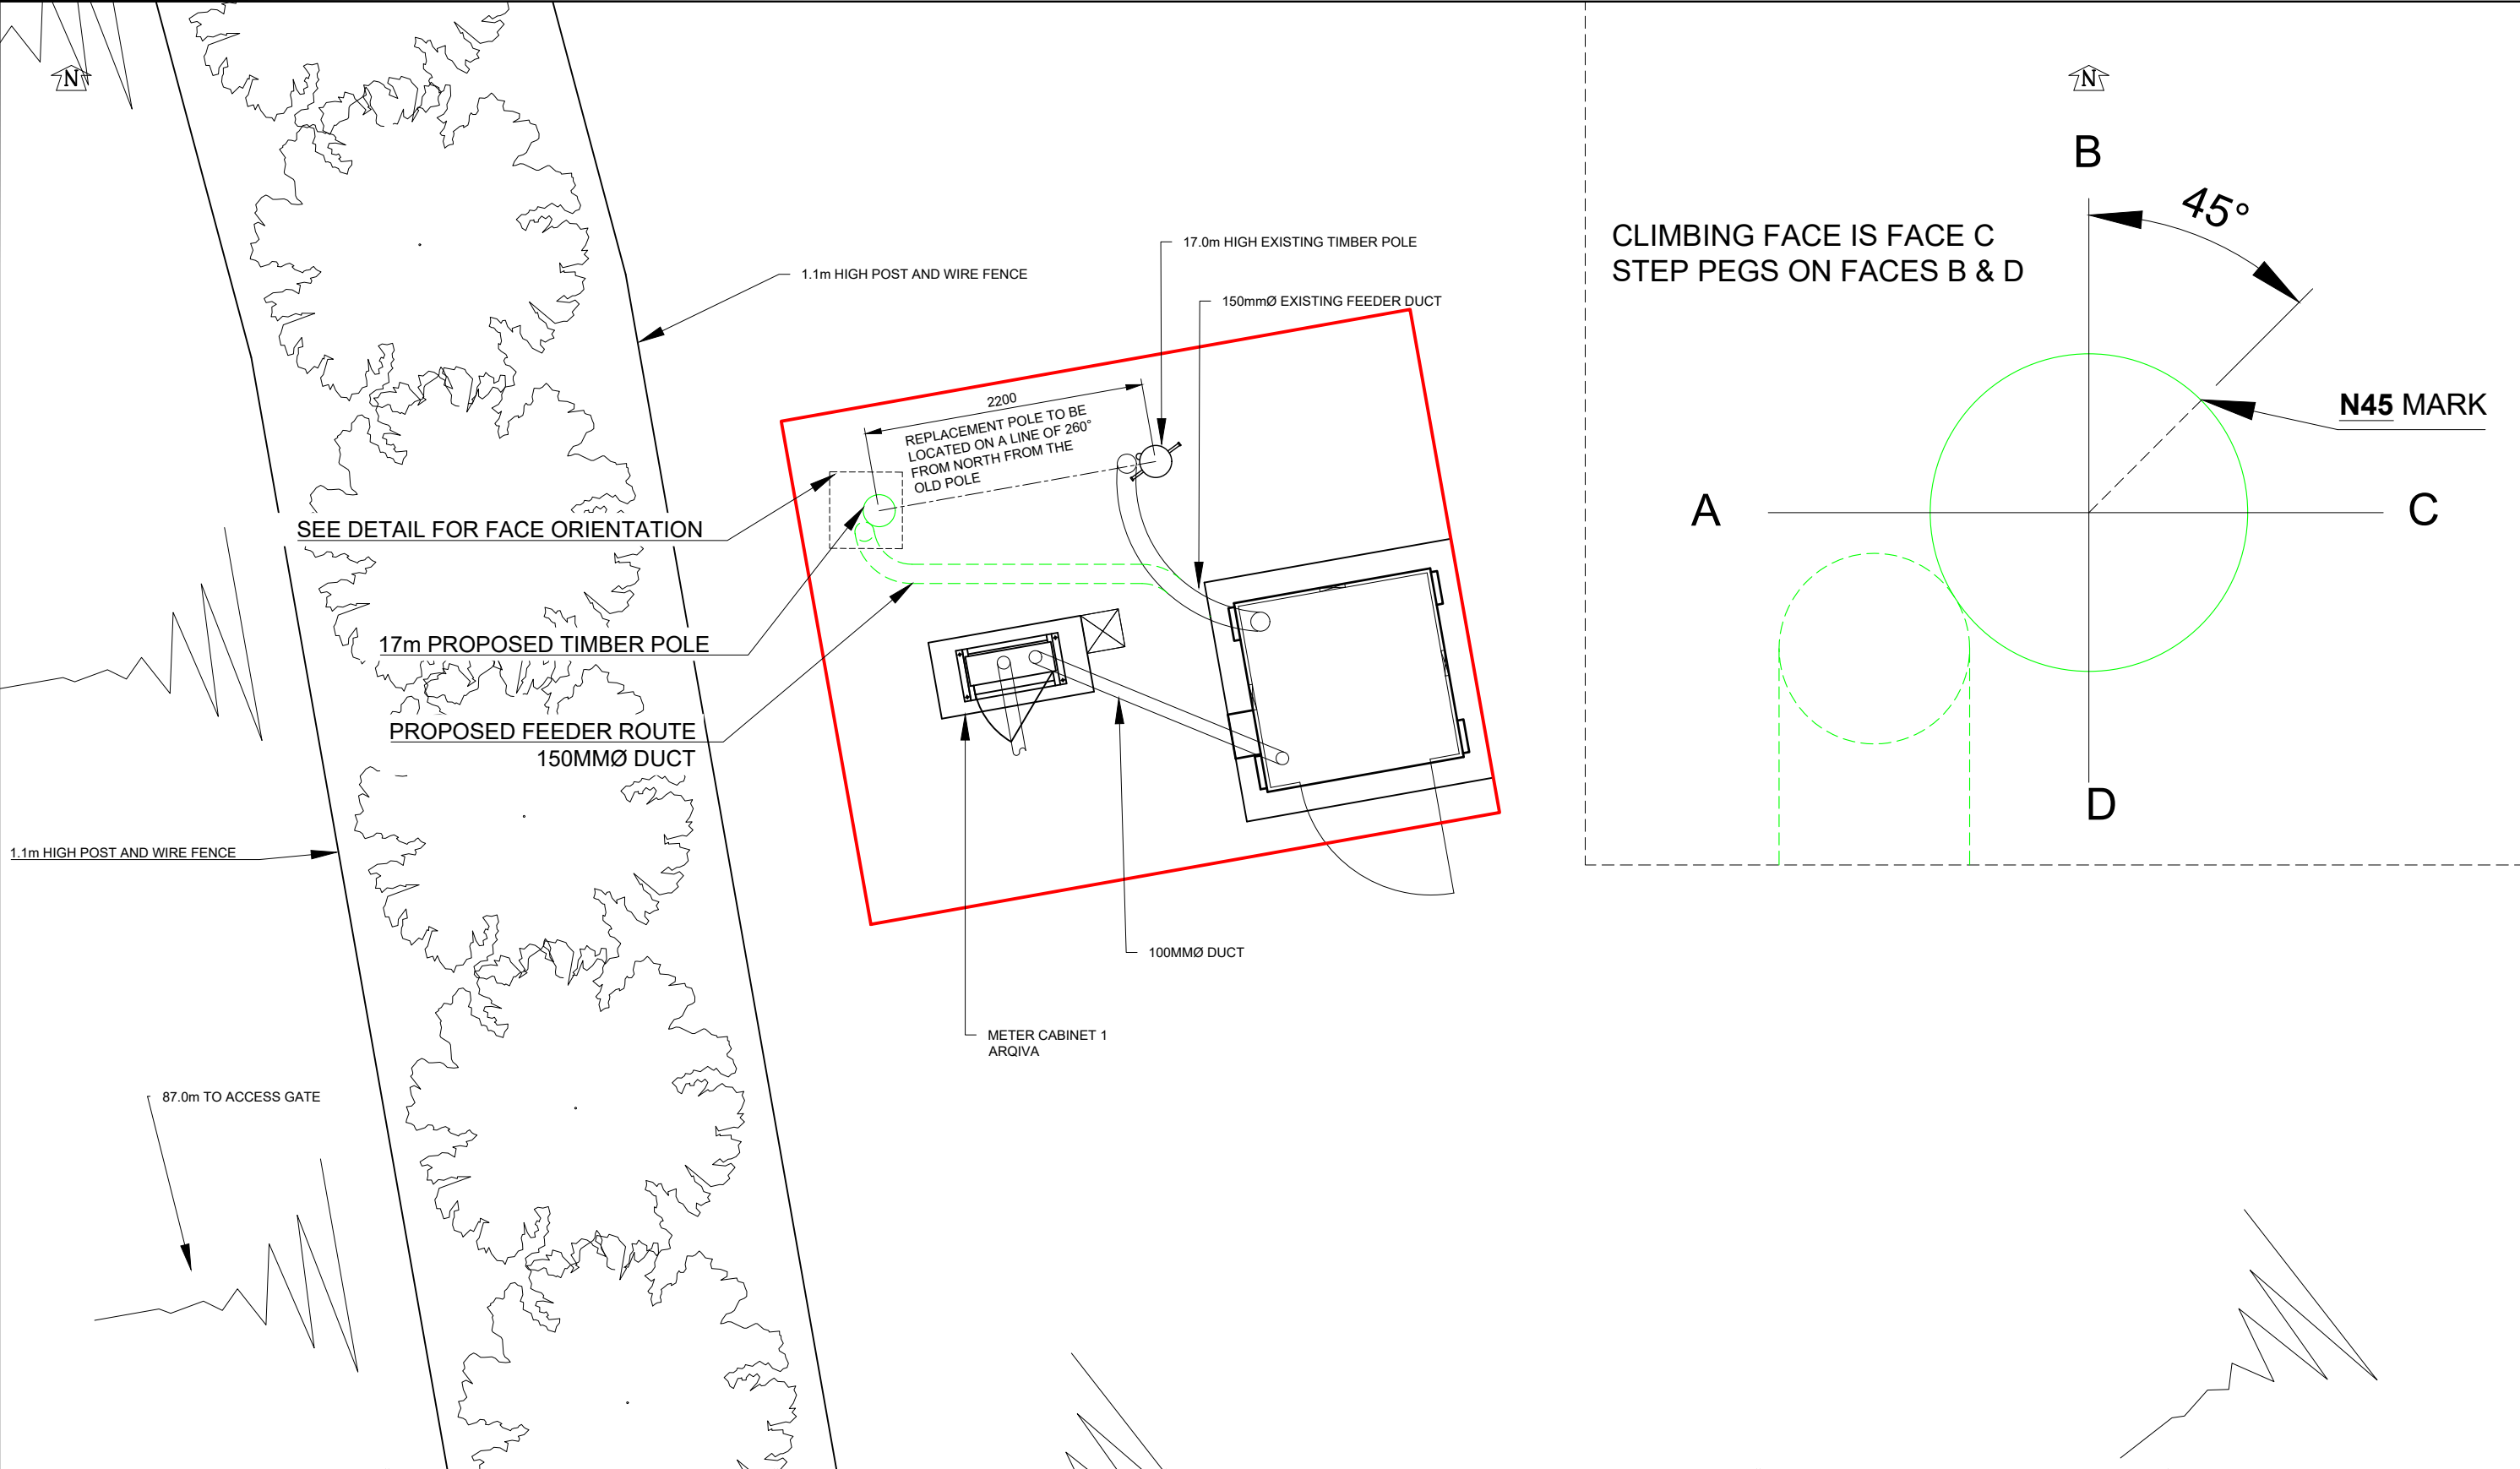


02	UPDATED PROPOSED POLE POSITION			AM	02/05/19
01	FIRST ISSUE			TT	25/04/19
REV	REV			BY	DATE
SCALE AS SHOWN WHEN PRINTED AT A3		DRAWN	AM	CHECKED	MP
		DATE	25/04/19	DATE	25/04/19
APPROVED JBT					
DATE 25/04/19					
ALL DIMENSIONS IN mm UNLESS OTHERWISE STATED. THIS DRAWING TO BE READ IN CONJUNCTION WITH OTHER RELEVANT DRAWINGS.					

TITLE
TALLEY
SITE PLAN

SITE ADDRESS		
TALLEY ARQIVA SITE PENLAN FACH TALLEY, LLANDEILO CARMARTHENSHIRE SA19 7YN		
ARQIVA REF. 141680	DRG No. 100	REV 02

ALL SCALES AS SHOWN WHEN PRINTED AT A3

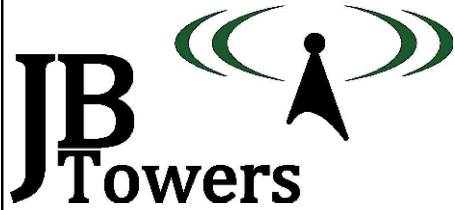

01	FIRST ISSUE			TT	25/04/19
REV	REV			BY	DATE
SCALE AS SHOWN		DRAWN	AM	CHECKED	MP
WHEN PRINTED AT A3		DATE	25/04/19	DATE	25/04/19
		DATE	25/04/19	DATE	25/04/19
ALL DIMENSIONS IN mm UNLESS OTHERWISE STATED. THIS DRAWING TO BE READ IN CONJUNCTION WITH OTHER RELEVANT DRAWINGS.					



TITLE
TALLEY
GENERAL ARRANGEMENT
SHEET 1 OF 3

SITE ADDRESS
TALLEY
ARQIVA SITE
PENLAN FACH
TALLEY, LLANDEILO
CARMARTHENSHIRE
SA19 7YN

ARQIVA REF.
141680

DRG No.
200

REV
01

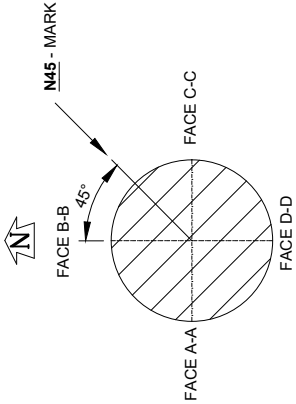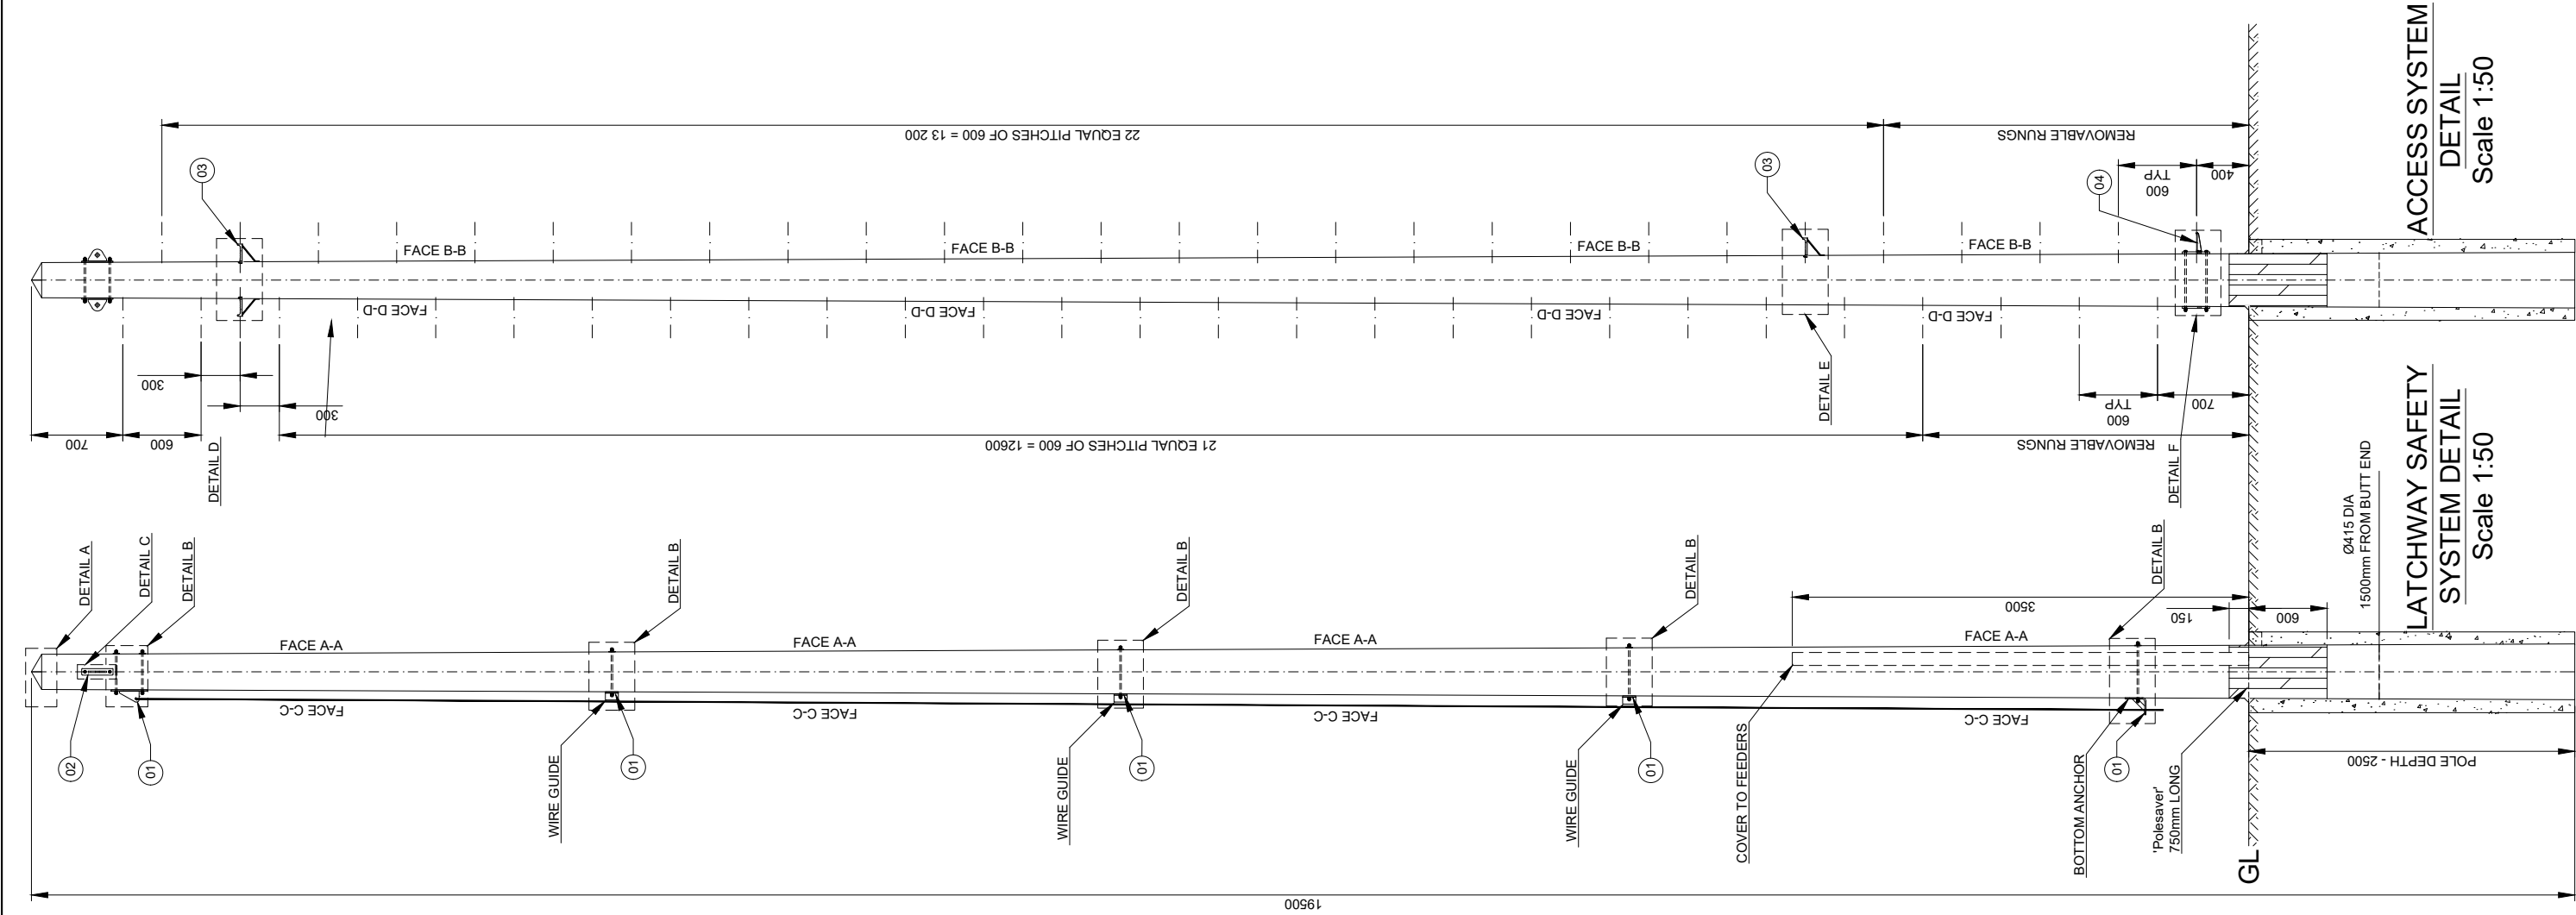

POLE ORIENTATION
Scale 1:20

NOTES

1. SEE DRAWING 304 FOR PARTS LIST
2. ALL BOLTS TO BE CUT ON SITE TO EXTEND MAX 10mm BEYOND THE NUT WHEN TIGHTENED UNO.
3. ALL SITE DRILLED HOLE/CUT ENDS TO BE TREATED WITH METAFUX 70-40 ZINC PASTE FOLLOWED BY 1 COAT OF 7-42 ZINC ALU OR 70-16 ALUMINIUM SPRAY

TIMBER POLE

1. POLE TO BE SUPPLIED IN ACCORDANCE WITH BS EN14229 & SHALL HAVE MIN. CHARACTERISTIC BENDING STRENGTH OF 30N/mm2 & MIN. YOUNGS MODULUS (PARALLEL TO GRAIN) OF 10KN/mm2.
2. MARKINGS ON FINISHED POLE SHALL BE AT 4m FROM BUTT AND COMPLY WITH BS EN 14229 UNO
3. AS FAR AS PRACTICABLE ALL CUTTING, SCARFING & DRILLING TO BE DONE BEFORE CREOSOTING. IF NOT ALL CUT, DRILLED & SCARFED SURFACES TO BE COATED WITH A MIXTURE OF CREOSOTE & TAR.
4. POLE TO BE PRESSURE IMPREGNATED WITH CREOSOTE IN ACCORDANCE WITH BS EN 14229
5. MINIMUM DIAMETERS
TOP - Ø205mm
BOTTOM - Ø430mm
6. 19.5m LONG POLE TO BE SOURCED BY TRIMMING 20m LONG POLE BY 0.5m AT THE TOP




PLANTING

1. CAT SCANNER IS TO BE USED IN ORDER TO CONFIRM THE POSITIONS OF BURIED SERVICES.
2. 'Perma-Soil Stabiliser' OR A SIMILAR APPROVED SHOULD BE USED IN ACCORDANCE WITH THE MANUFACTURER'S RECOMMENDATION.
3. ANY MATERIAL USED FOR BACK-FILLING IS TO BE OF EQUAL OR BETTER QUALITY THAN THE EXCAVATED MATERIAL.
4. ALL BACK-FILLING MATERIAL IS TO BE PLACED AND COMPACTED IN 150mm THICK LAYERS.
5. TIMBER POLE TO BE PLANTED WITH N45 MARKING AT 3.5m FROM BUT FACING 45° FROM NORTH (CLOCKWISE)

ALL SCALES AS SHOWN WHEN PRINTED AT A3



ALL SCALES AS SHOWN WHEN PRINTED AT A3

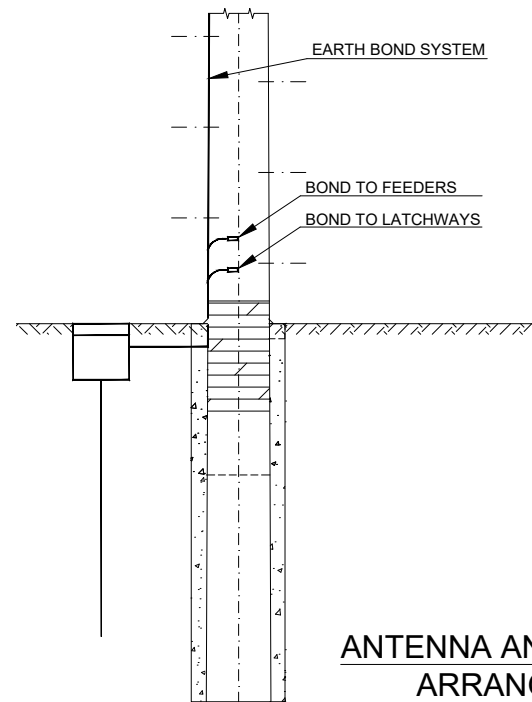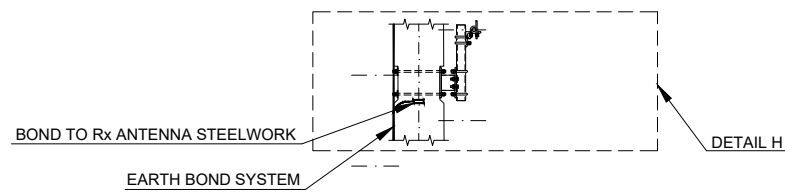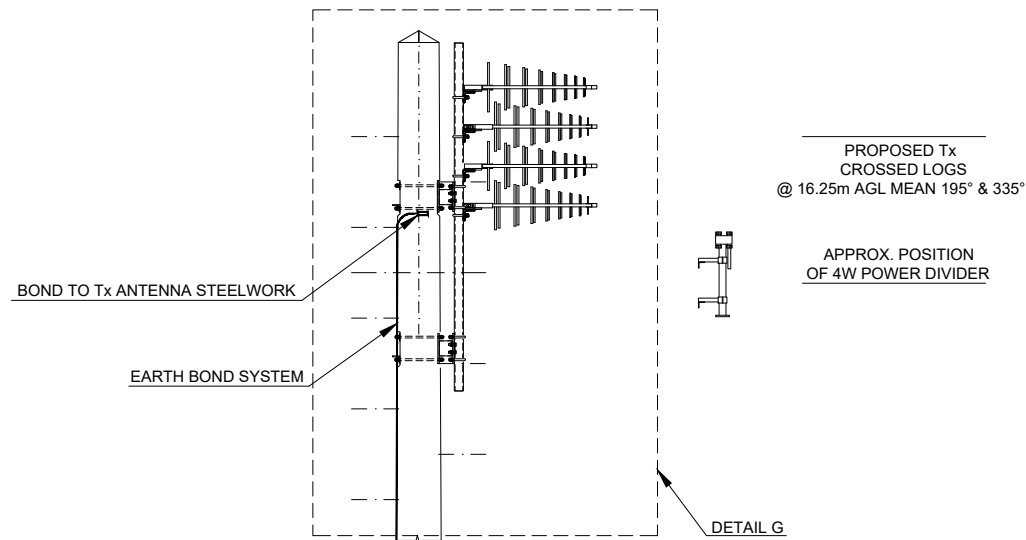

ANTENNA AND EARTHING
ARRANGEMENT
Scale 1:50

NOTES


- 1. AS FAR AS IS PRACTICABLE ALL CUTTING SCARFING AND DRILLING TO BE DONE BEFORE CREOSOTING. WHERE THIS IS NOT POSSIBLE ALL CUT, DRILLED, AND SCARFED SURFACES TO BE COATED WITH A MIXTURE OF CREOSOTE AND TAR

FEEDERS


- 1. SUPPLY OF FEEDERS BY OTHERS LCF78-50 TO Tx ANTENNA & LCF12-50 TO Rx ANTENNA
- 2. FEEDERS FIXED AT 1000mm CENTRES

EARTHING

- 1. CONNECT EARTH BOND TO NEW EARTHING SYSTEM
- 2. MAXIMUM VALUE FOR GROUND RESISTANCE TO BE 10 OHMS
- 3. CABLE OR TAPE TO BE FIXED TO POLE AT 1000mm CENTRES
- 4. EARTHING SHOULD COMPLY WITH ARQIVA'S DOCUMENT BOS147

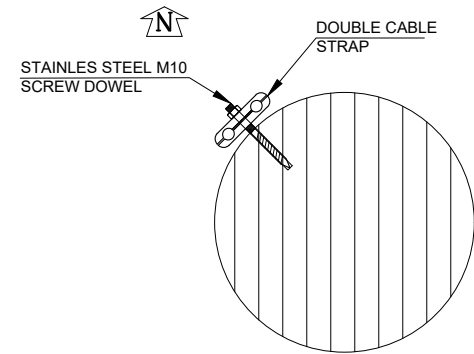

FEEDER
MANAGEMENT
Scale 1:10

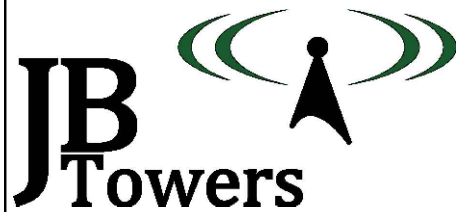


02	Tx ANTENNA MEAN HEIGHT UPDATED	AM	02/05/19
01	FIRST ISSUE	TT	25/04/19
REV	REV	BY	DATE
SCALE AS SHOWN WHEN PRINTED AT A3	DRAWN DATE 25/04/19	CHECKED DATE 25/04/19	APPROVED DATE 25/04/19
ALL DIMENSIONS IN mm UNLESS OTHERWISE STATED. THIS DRAWING TO BE READ IN CONJUNCTION WITH OTHER RELEVANT DRAWINGS.			

TITLE		SITE ADDRESS		
TALLEY GENERAL ARRANGEMENT SHEET 2 OF 3		TALLEY ARQIVA SITE PENLAN FACH TALLEY, LLANDEILO CARMARTHENSHIRE SA19 7YN		
ARQIVA REF. 141680		DRG No. 200	REV 02	

ALL SCALES AS SHOWN WHEN PRINTED AT A3




ALL SCALES AS SHOWN WHEN PRINTED AT A3

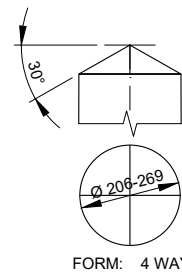


- NOTES:
1. A SINGLE COAT OF TIMBER COMPATIBLE BITUMINOUS PAINT (E.G. BIRD BRAND BLACK BITUMINOUS PAINT OR SIMILAR APPROVED PRODUCT) TO BE APPLIED TO THE UPPER SURFACES AT THE TOP OF THE POLE.
 2. PAINT TO BE APPLIED ON SITE JUST BEFORE ERECTION
- FORM: 4 WAY PYRAMID / CONE


DETAIL A - TIMBER POLE TOP
Scale 1:20

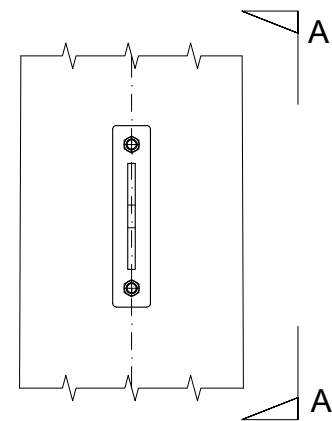


DETAIL C - FALL ARREST
ATTACHMENT POINT
Scale 1:10

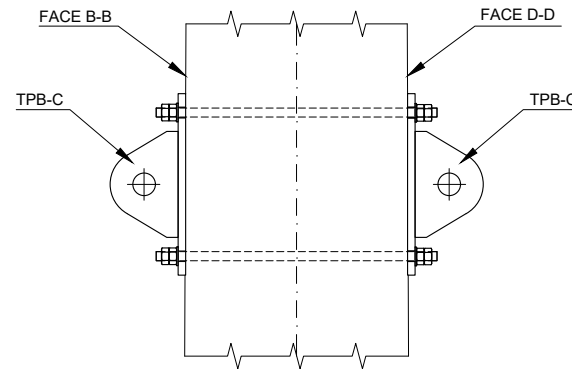


VIEW A-A
Scale 1:10

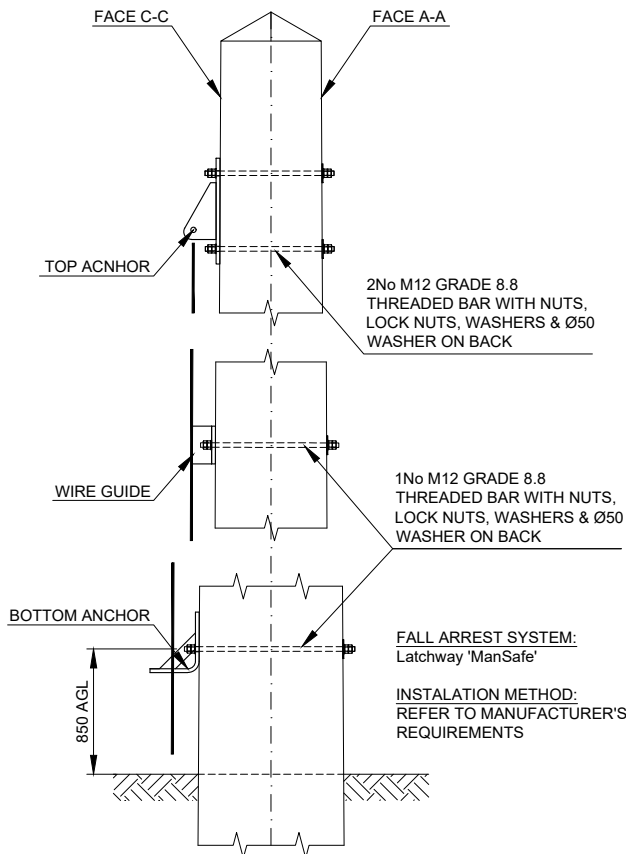

DETAIL B - FALL ARREST SYSTEM
Scale 1:20

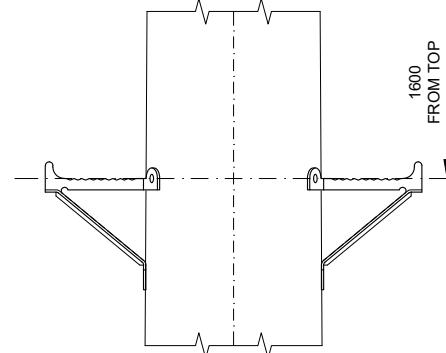


DETAIL D - ANTENNA
ACCESS CLIMBING STEP
Scale 1:10

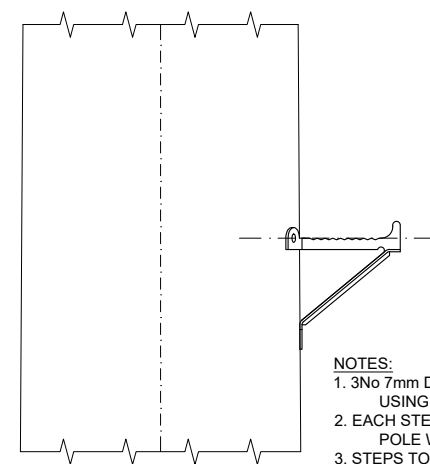


DETAIL E - PERMANENT
CLIMBING STEPS
Scale 1:10

- NOTES:
1. 3No 7mm DIA 70mm LONG PILOT HOLES TO BE DRILLED USING THE STEP AS A TEMPLATE
 2. EACH STEP SHOULD BE FIXED TO THE TIMBER POLE WITH 3No 10mm COACH SCREWS 75mm LONG
 3. STEPS TO BE INSTALLED ON FACES B-B & D-D ONLY

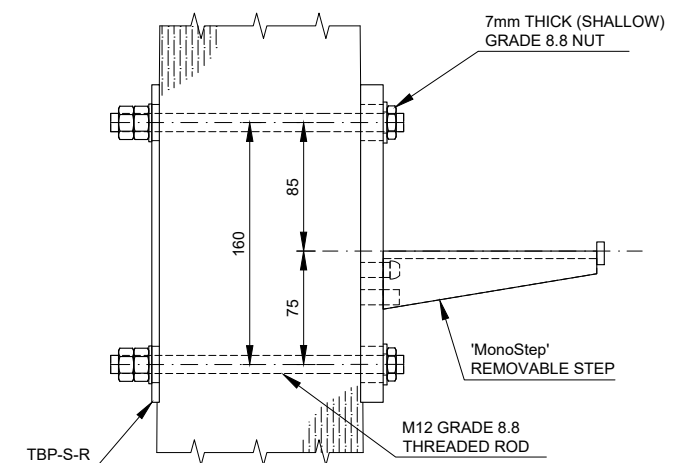

DETAIL F - REMOVABLE
CLIMBING STEPS
Scale 1:5

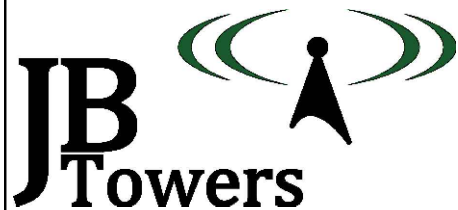

01	FIRST ISSUE	TT	25/04/19
REV	REV	BY	DATE
SCALE AS SHOWN WHEN PRINTED AT A3	DRAWN DATE 25/04/19	AM DATE 25/04/19	CHECKED DATE 25/04/19
ALL DIMENSIONS IN mm UNLESS OTHERWISE STATED. THIS DRAWING TO BE READ IN CONJUNCTION WITH OTHER RELEVANT DRAWINGS.			

TITLE
TALLEY
GENERAL ARRANGEMENT
SHEET 3 OF 3

SITE ADDRESS
TALLEY
ARQIVA SITE
PENLAN FACH
TALLEY, LLANDEILO
CARMARTHENSHIRE
SA19 7YN

ARQIVA REF.
141680


DRG No.
200

REV
01

ALL SCALES AS SHOWN WHEN PRINTED AT A3







ALL SCALES AS SHOWN WHEN PRINTED AT A3

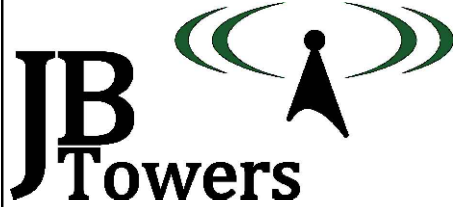


01	FIRST ISSUE			TT	25/04/19
REV	REV			BY	DATE
SCALE AS SHOWN		DRAWN	AM	CHECKED	MP
WHEN PRINTED AT A3		DATE	25/04/19	DATE	25/04/19
		APPROVED	JBT	DATE	25/04/19
ALL DIMENSIONS IN mm UNLESS OTHERWISE STATED. THIS DRAWING TO BE READ IN CONJUNCTION WITH OTHER RELEVANT DRAWINGS.					

TITLE	
TALLEY TIMBER POLE HOLE SET OUT SHEET 1 OF 2	

SITE ADDRESS		
TALLEY ARQIVA SITE PENLAN FACH TALLEY, LLANDEILO CARMARTHENSHIRE SA19 7YN		
ARQIVA REF. 141680	DRG No. 201	REV 01

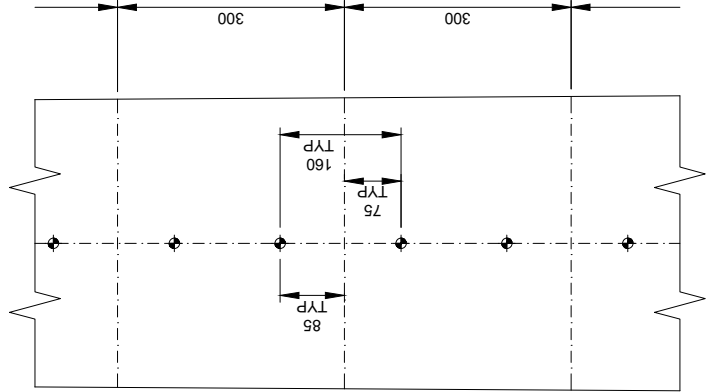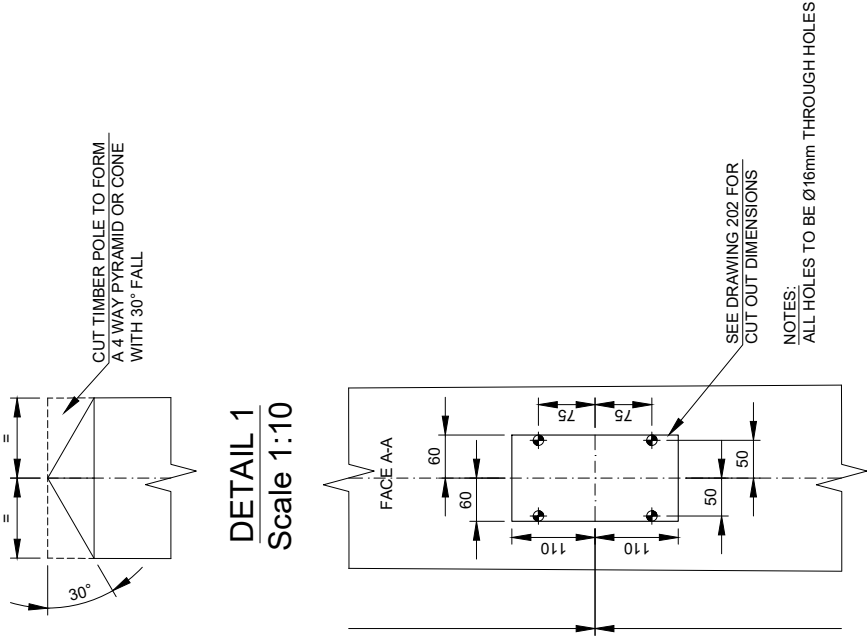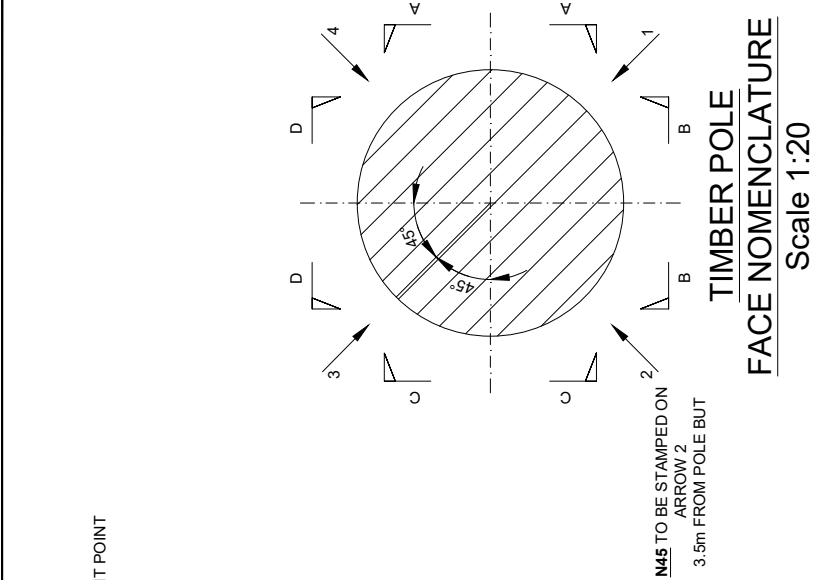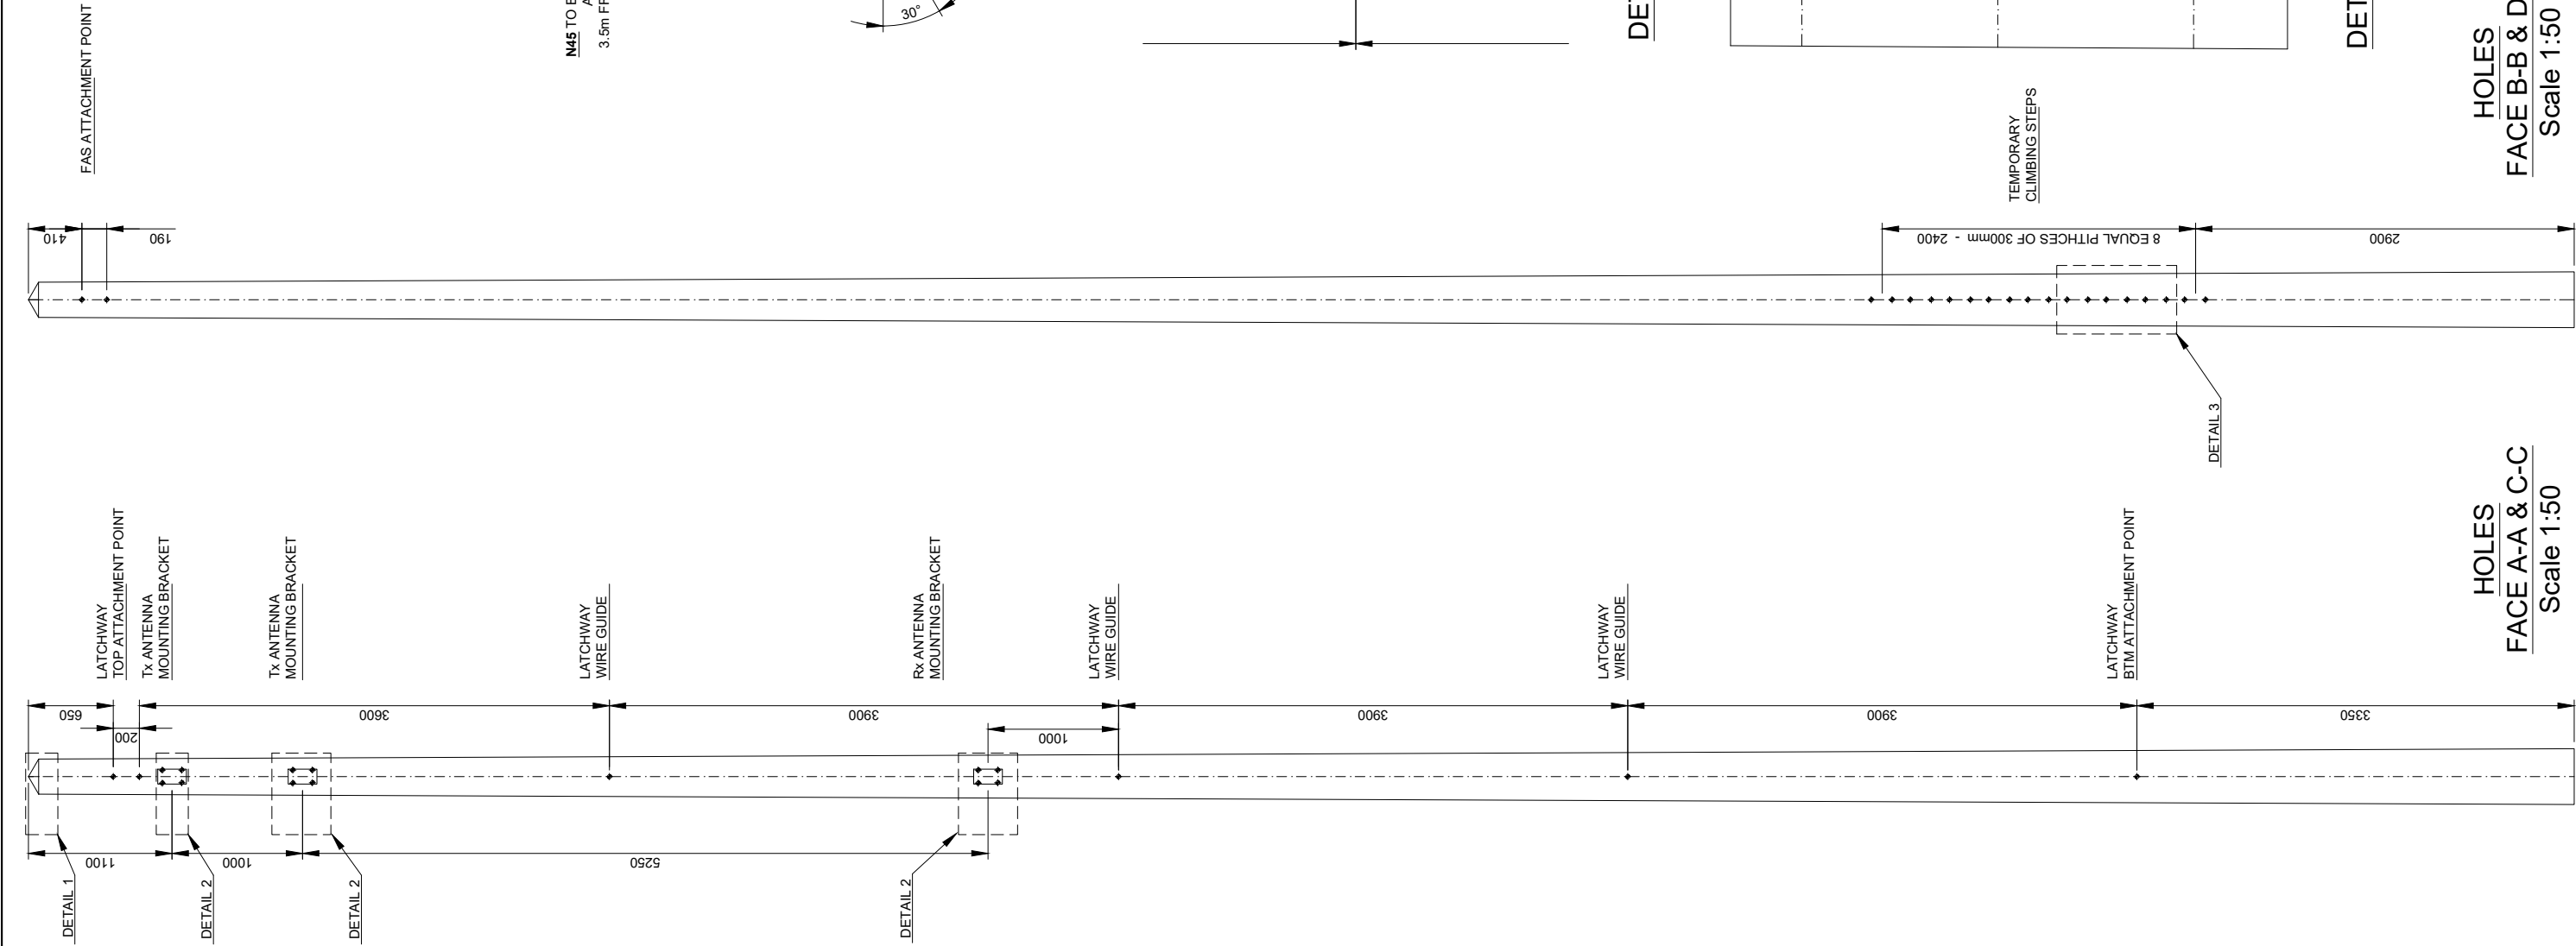

ALL SCALES AS SHOWN WHEN PRINTED AT A3

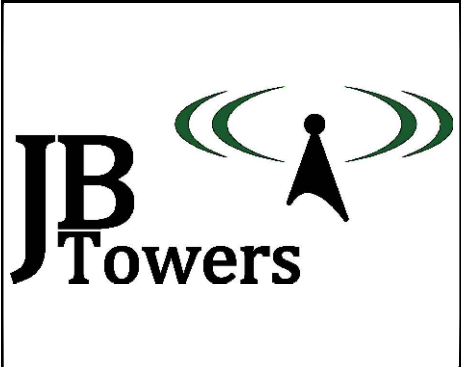


01	FIRST ISSUE			TT	25/04/19
REV	REV			BY	DATE
SCALE AS SHOWN		DRAWN	AM	CHECKED	MP
WHEN PRINTED AT A3		DATE	25/04/19	DATE	25/04/19
		APPROVED	JBT	DATE	25/04/19
ALL DIMENSIONS IN mm UNLESS OTHERWISE STATED. THIS DRAWING TO BE READ IN CONJUNCTION WITH OTHER RELEVANT DRAWINGS.					

TITLE


TALLEY

TIMBER POLE HOLE SET OUT
SHEET 2 OF 2

SITE ADDRESS TALLEY ARQIVA SITE PENLAN FACH TALLEY, LLANDEILO CARMARTHENSHIRE SA19 7YN		
ARQIVA REF. 141680	DRG No. 201	REV 01

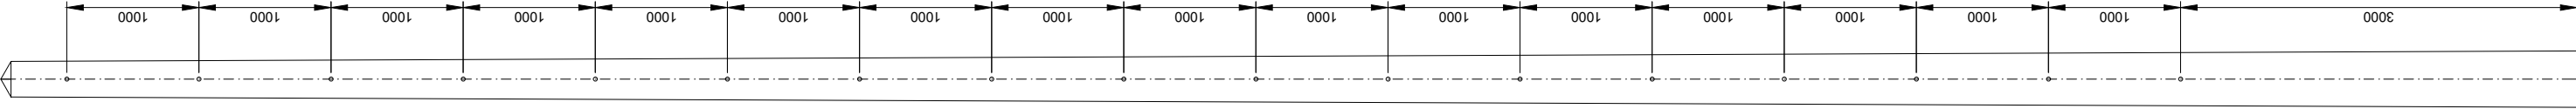

FEEDER BRACKETS

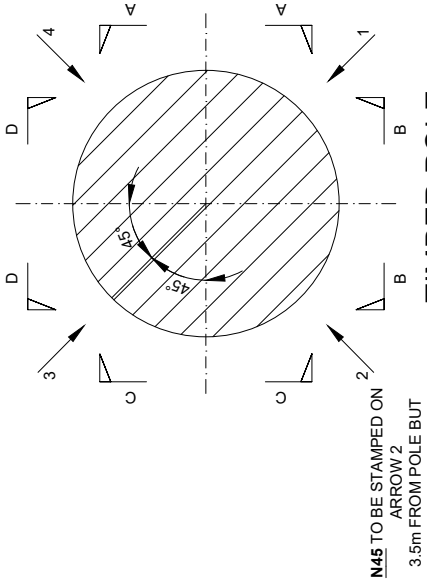

TIMBER POLE
FACE NOMENCLATURE
Scale 1:20

ALL HOLES ON ARROW 1
TO BE Ø8mm & 70mm LONG

HOLES
ARROW 1
Scale 1:50



ALL SCALES AS SHOWN WHEN PRINTED AT A3

ALL SCALES AS SHOWN WHEN PRINTED AT A3



01	FIRST ISSUE			TT	25/04/19
REV	REV			BY	DATE
SCALE AS SHOWN		DRAWN	AM	CHECKED	MP
WHEN PRINTED AT A3		DATE	25/04/19	DATE	25/04/19
		APPROVED	JBT	DATE	25/04/19
ALL DIMENSIONS IN mm UNLESS OTHERWISE STATED. THIS DRAWING TO BE READ IN CONJUNCTION WITH OTHER RELEVANT DRAWINGS.					


TITLE
TALLEY
TIMBER POLE CUT OUT
DETAIL


SITE ADDRESS
TALLEY
ARQIVA SITE
PENLAN FACH
TALLEY, LLANDEILO
CARMARTHENSHIRE
SA19 7YN

ARQIVA REF.
141680


DRG No.
202

REV
01

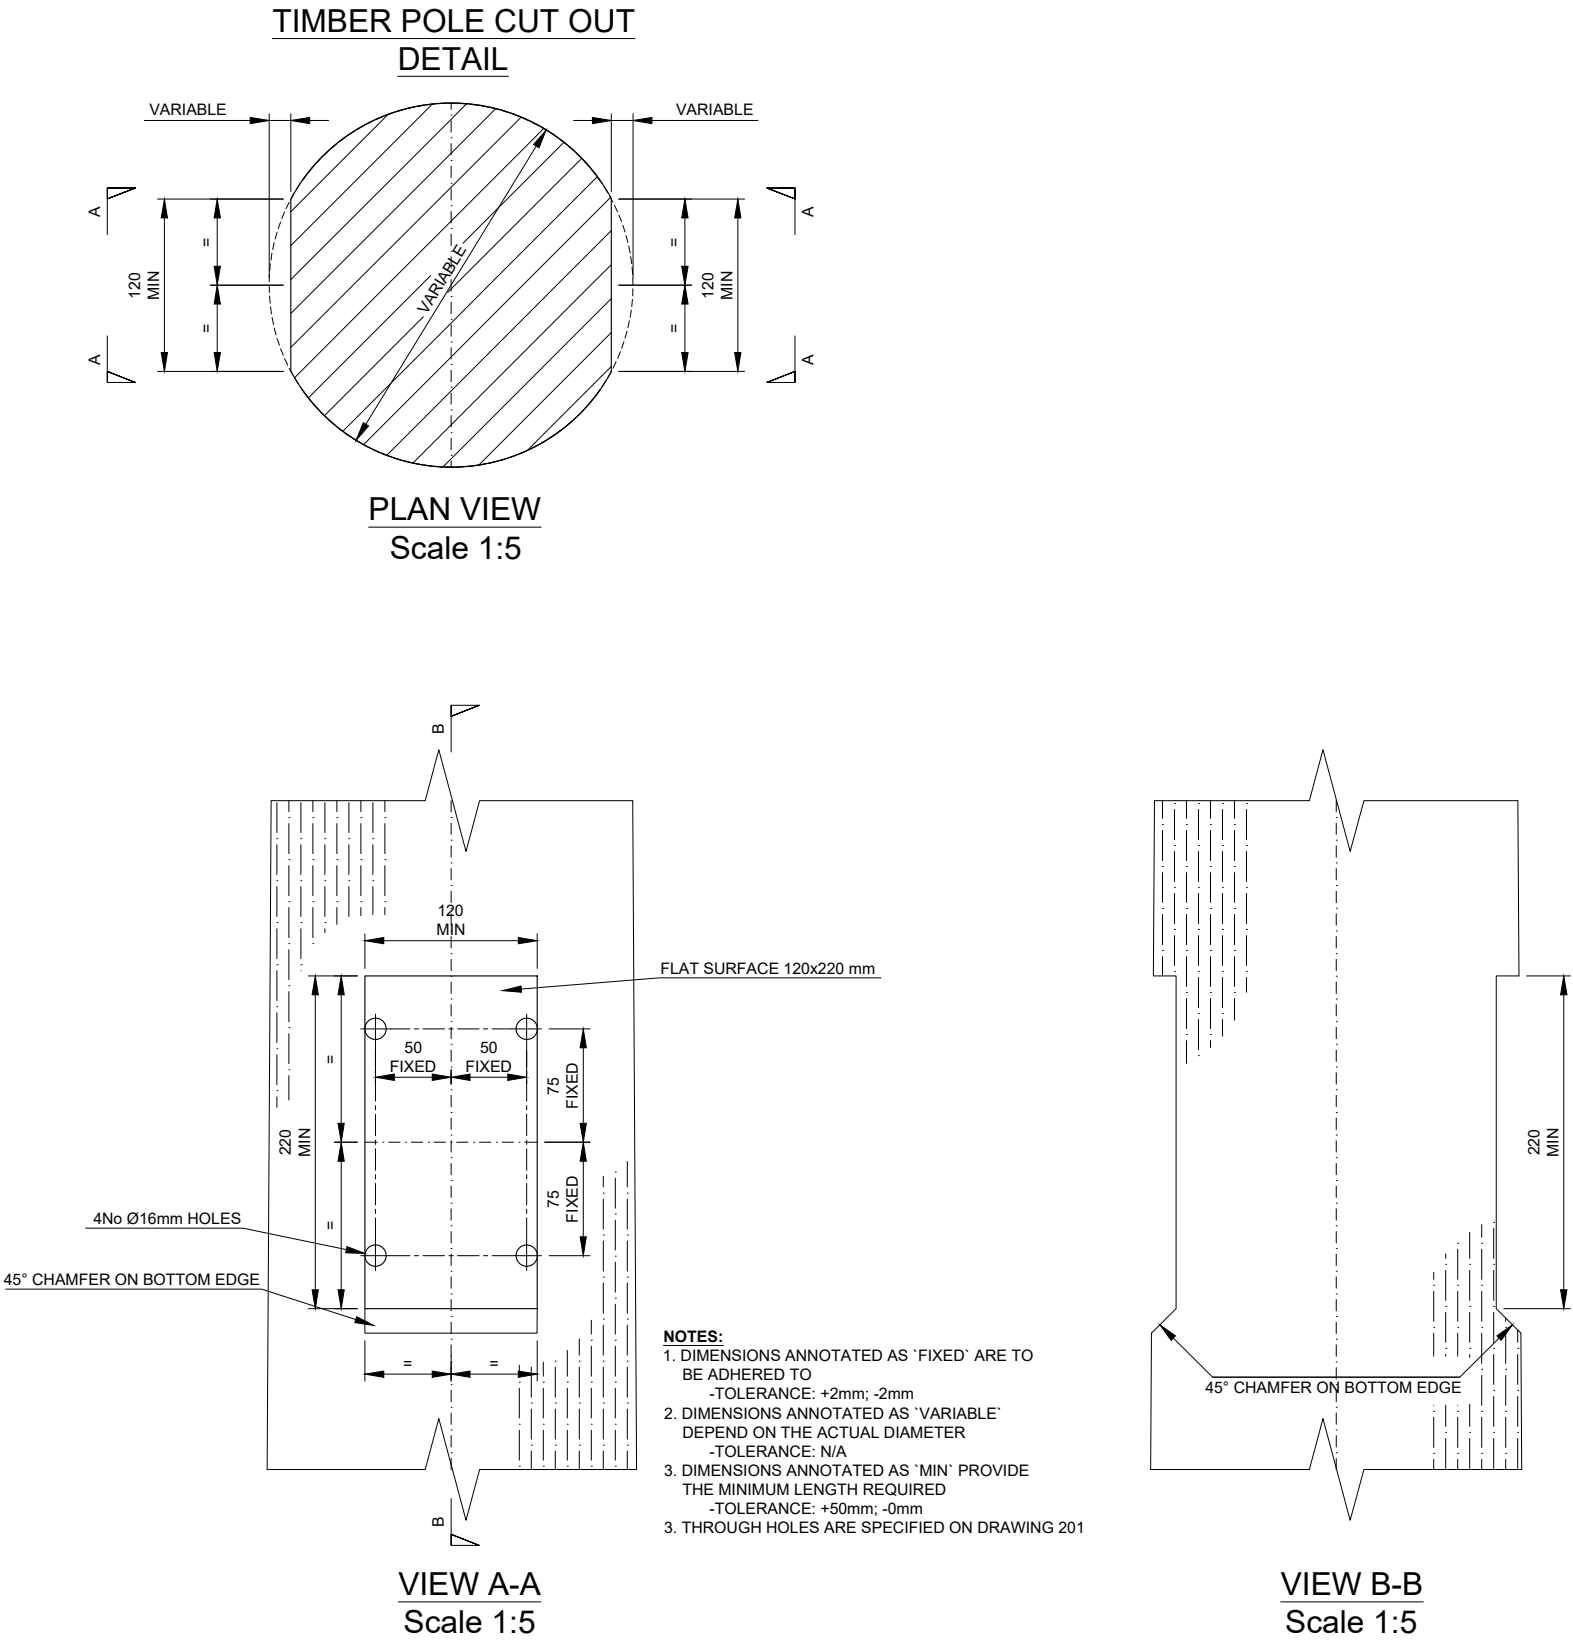


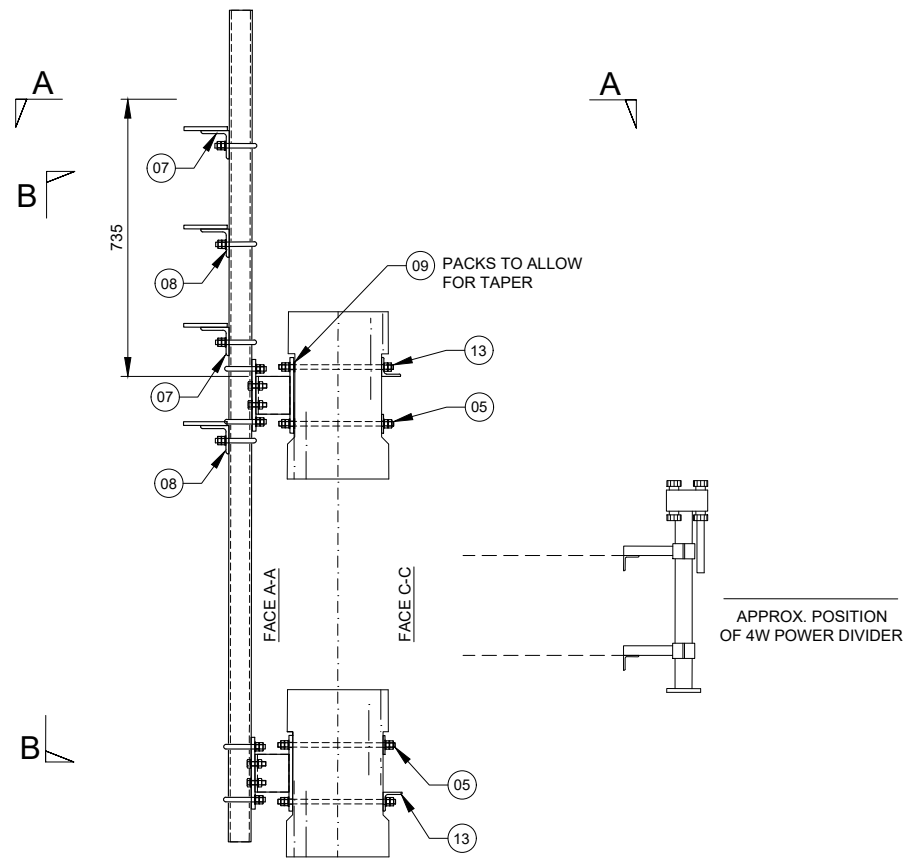


DETAIL G - Tx ANTENNA MOUNT
Scale 1:20

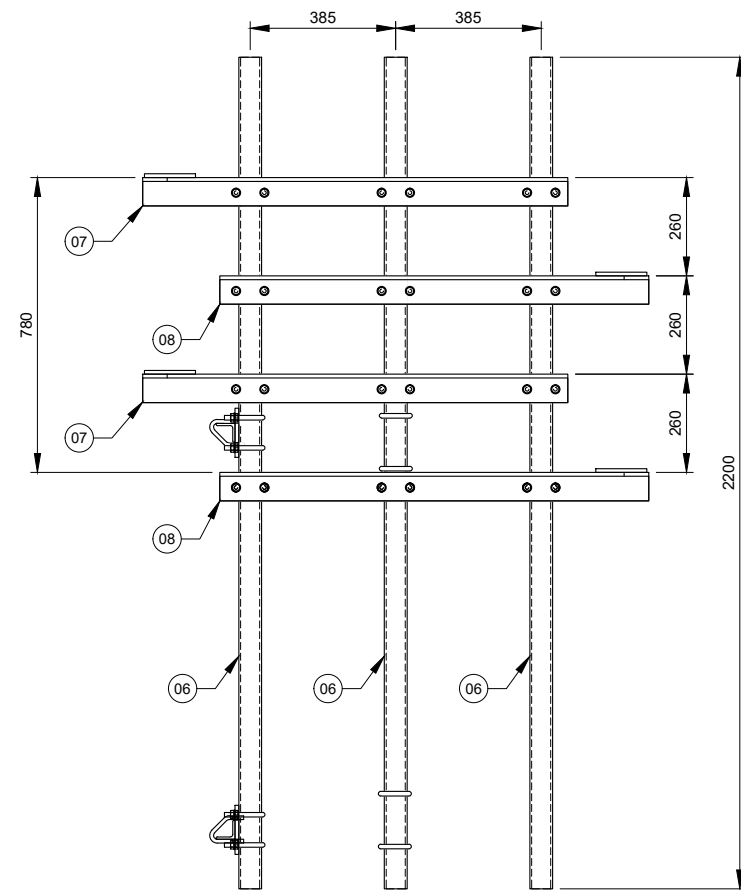

VIEW B-B
Scale 1:20

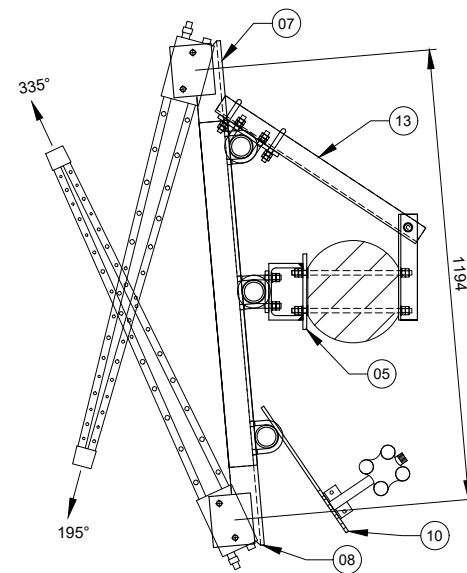

SECTION A-A
Scale 1:20

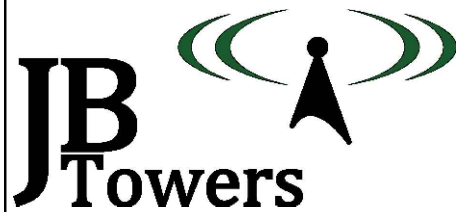

01	FIRST ISSUE	TT	25/04/19
REV	REV	BY	DATE
SCALE AS SHOWN WHEN PRINTED AT A3	DRAWN DATE 25/04/19	CHECKED DATE 25/04/19	APPROVED DATE 25/04/19
ALL DIMENSIONS IN mm UNLESS OTHERWISE STATED. THIS DRAWING TO BE READ IN CONJUNCTION WITH OTHER RELEVANT DRAWINGS.			

TITLE
ANTENNA MOUNT
DETAIL G

SITE ADDRESS
TALLEY
ARQIVA SITE
PENLAN FACH
TALLEY, LLANDEILO
CARMARTHENSHIRE
SA19 7YN

ARQIVA REF.
141680


DRG No.
203

REV
01


ALL SCALES AS SHOWN WHEN PRINTED AT A3



ALL SCALES AS SHOWN WHEN PRINTED AT A3

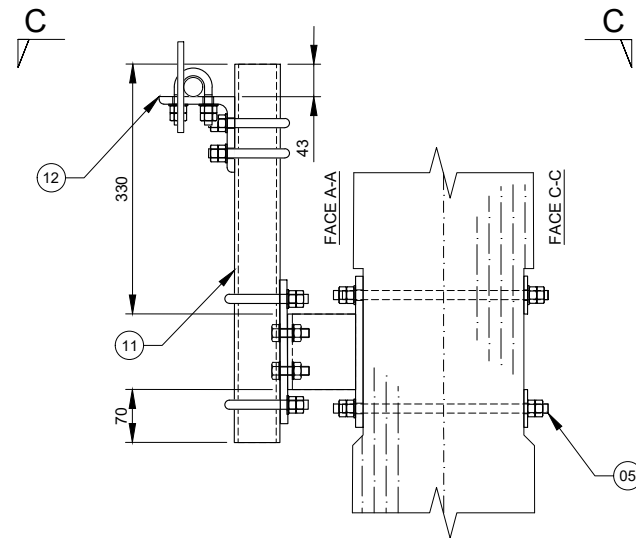

DETAIL H - Rx ANTENNA MOUNT
Scale 1:10

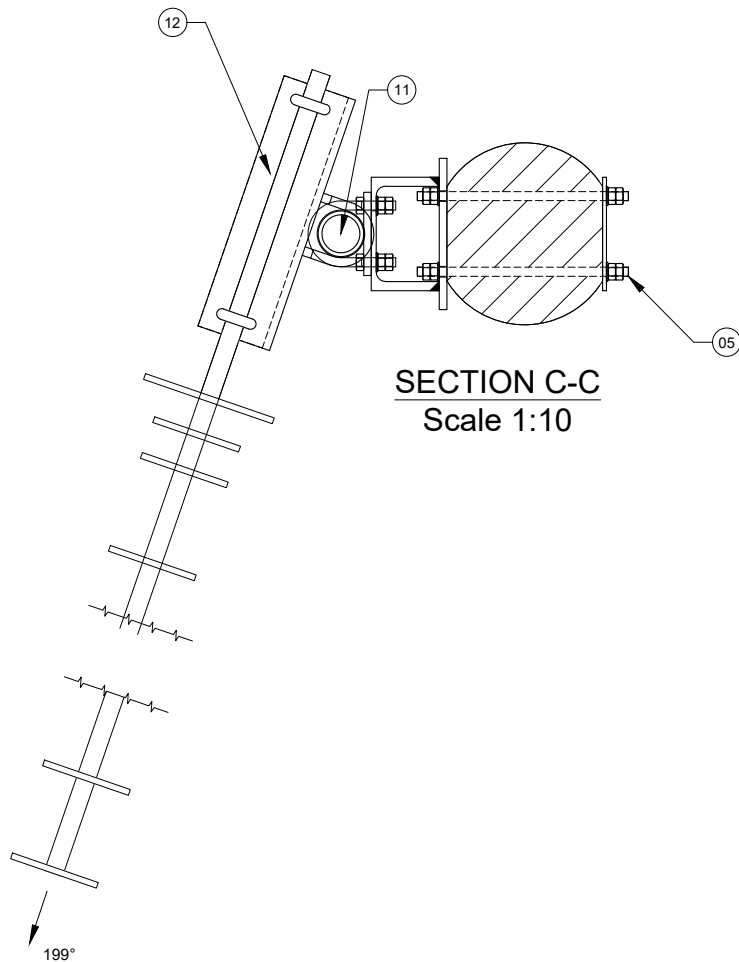


SECTION C-C
Scale 1:10

ALL SCALES AS SHOWN WHEN PRINTED AT A3



ALL SCALES AS SHOWN WHEN PRINTED AT A3

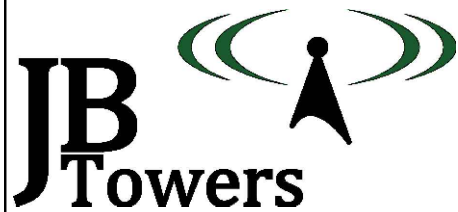

01	FIRST ISSUE			TT	25/04/19
REV	REV			BY	DATE
SCALE AS SHOWN WHEN PRINTED AT A3		DRAWN AM DATE 25/04/19	CHECKED MP DATE 25/04/19	APPROVED JBT DATE 25/04/19	
ALL DIMENSIONS IN mm UNLESS OTHERWISE STATED. THIS DRAWING TO BE READ IN CONJUNCTION WITH OTHER RELEVANT DRAWINGS.					


TITLE
ANTENNA MOUNT
DETAIL H

SITE ADDRESS
TALLEY
ARQIVA SITE
PENLAN FACH
TALLEY, LLANDEILO
CARMARTHENSHIRE
SA19 7YN

ARQIVA REF.
141680


DRG No.
204

REV
01

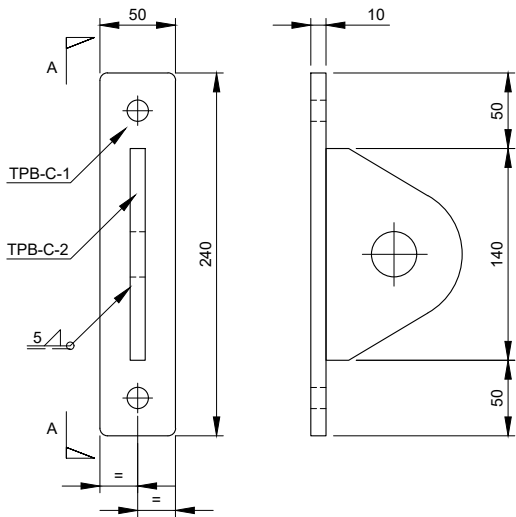

PART TPB-C
Scale 1:5

VIEW A-A
Scale 1:5

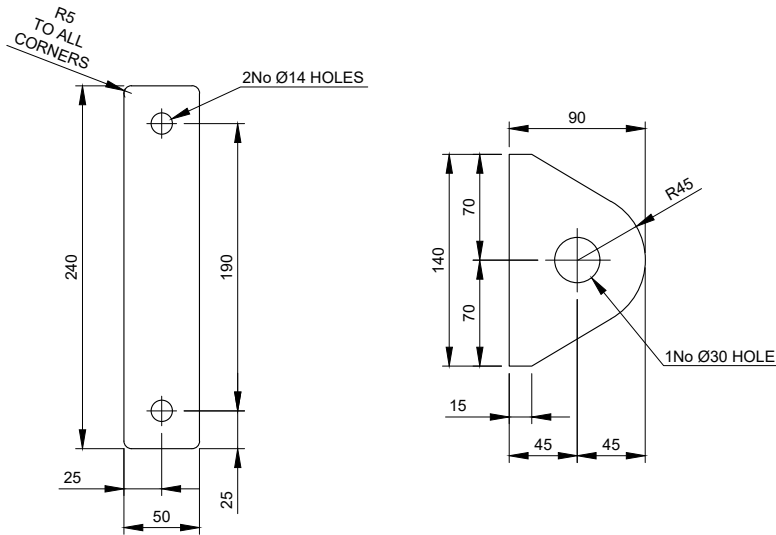


TPB-C-1 - 10mm THICK
Scale 1:5

TPB-C-2 - 10mm THICK
Scale 1:5

Parts list for TPB-C


Item	Part	Quantity	Part description	Length	Material	Weight
01	TPB-C-1	1	240x50x10mm	N/A	S275J0	0.94 kg
02	TPB-C-2	1	140x90x10mm	N/A	S275J0	0.99 kg
03	STUDS	1	M12 STUDDING	350mm	GRADE 8.8	0.31 kg
Total Weight:						2.24 kg

- All steel hot dip galvanized
- Each STUD to be supplied with 4 Full Nuts, 2 Flat Washers and 2 Spring Washers
- For fabrctation notes see drawing 304

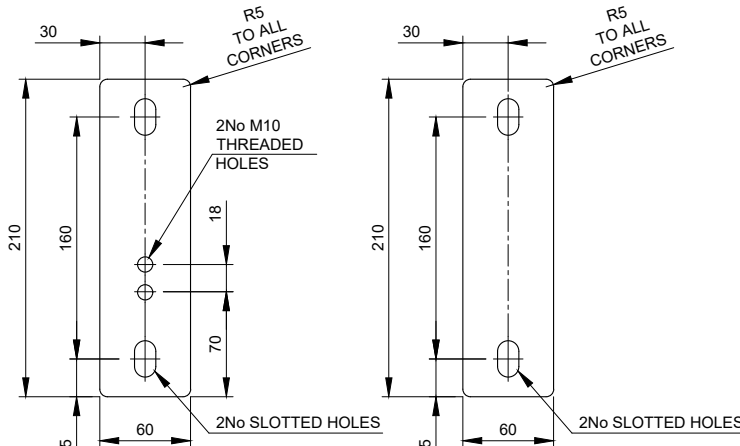

PART TPS-R-1
Scale 1:5

PART TPS-R-2
Scale 1:5

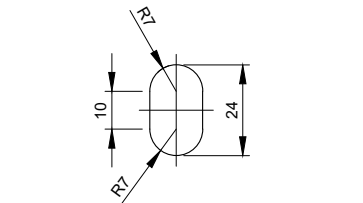


SLOTTED HOLE DETAIL
Scale 1:2

Parts list for TPS-R

Item	Part	Quantity	Part description	Length	Material	Weight
01	TPS-R-1	1	210x60x15mm	N/A	S275J0	1.48 kg
02	TPS-R-2	1	210x60x5mm	N/A	S275J0	0.49 kg
03	STUDS	2	M12 STUDDING	500mm	GRADE 8.8	0.44 kg
04	NUT-S	2	M12 SHALLOW NUT	N/A	GRADE 8.8	-
05	NUT	4	M12 NUT	N/A	GRADE 8.8	-
06	WSH	4	M12 WASHER	N/A	GRADE 8.8	-
Total Weight:						2.85 kg

- All steel hot dip galvanized
- For fabrctation notes see drawing 304

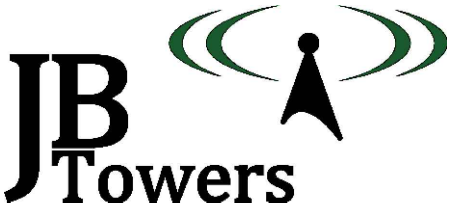

01	FIRST ISSUE	TT	25/04/19
REV	REV	BY	DATE
SCALE AS SHOWN WHEN PRINTED AT A3	DRAWN DATE 25/04/19	CHECKED DATE 25/04/19	APPROVED DATE 25/04/19
ALL DIMENSIONS IN mm UNLESS OTHERWISE STATED. THIS DRAWING TO BE READ IN CONJUNCTION WITH OTHER RELEVANT DRAWINGS.			

TITLE
ATTACHMENT POINT &
TEMPORARY STEP DETAILS
PARTS: TPB-C; TPS-R









SITE ADDRESS
TALLEY
ARQIVA SITE
PENLAN FACH
TALLEY, LLANDEILO
CARMARTHENSHIRE
SA19 7YN

ARQIVA REF.
141680
DRG No.
300
REV
01

ALL SCALES AS SHOWN WHEN PRINTED AT A3




ALL SCALES AS SHOWN WHEN PRINTED AT A3

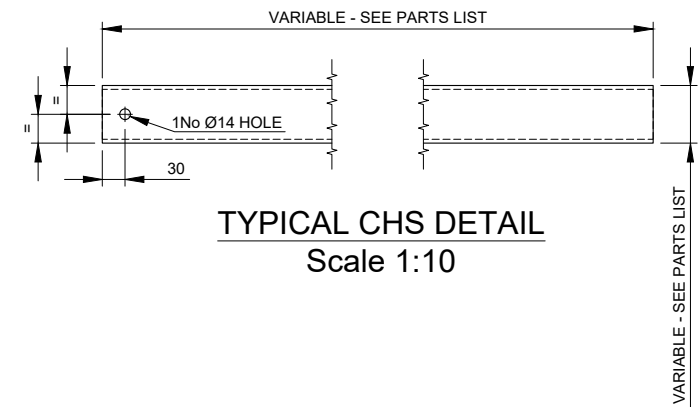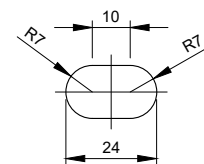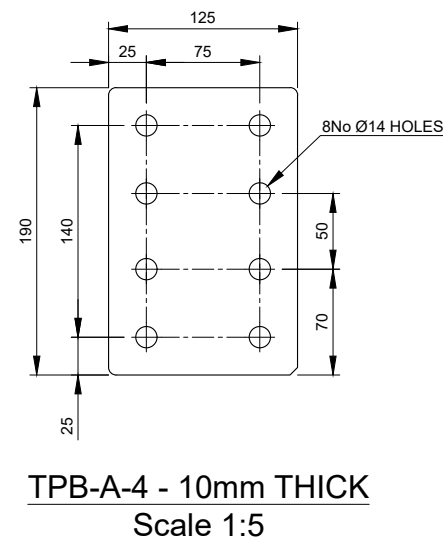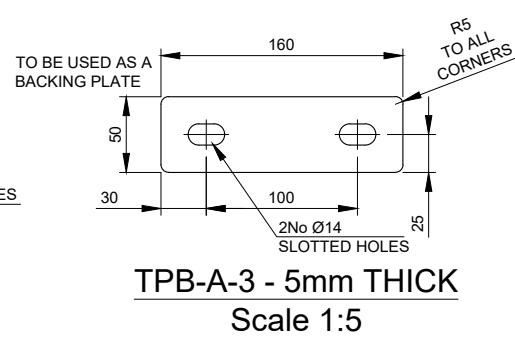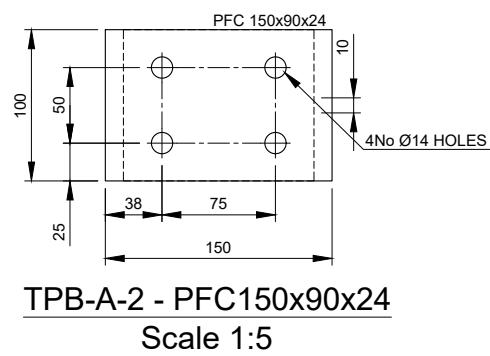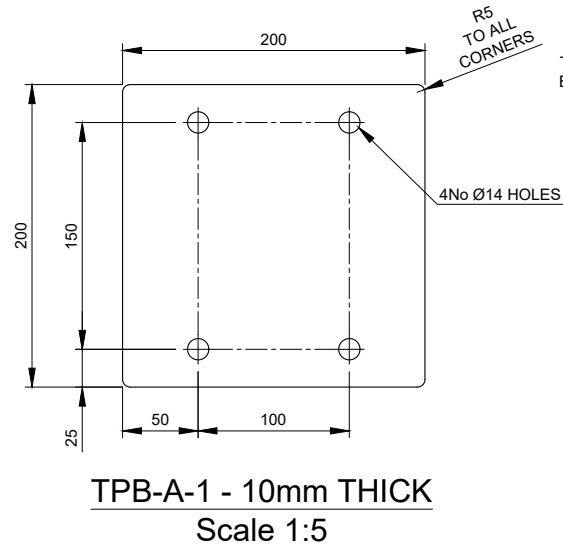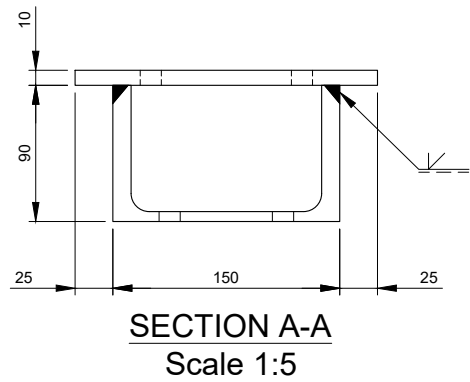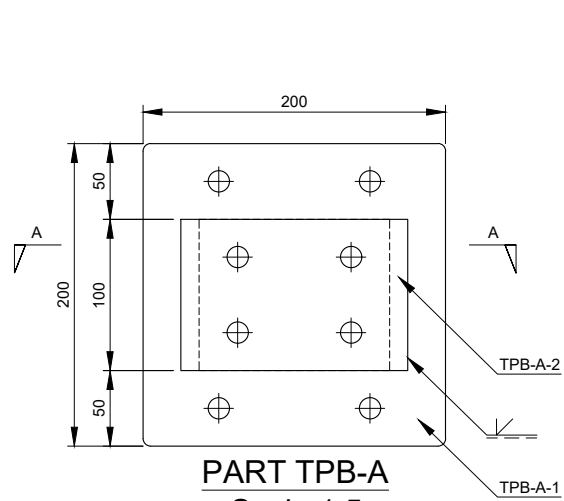

Parts list for TPB-A

Item	Part	Quantity	Part description	Length	Material	Weight
01	TPB-A-1	1	200x200x10mm	N/A	S275J0	3.14 kg
02	TPB-A-2	1	PFC 150x90x24	100mm	S275J0	2.4 kg
03	TPB-A-3	2	160x50x5mm	N/A	S275J0	0.31 kg
04	TPB-A-4	1	190x125x10mm	N/A	S275J0	1.86 kg
05	BOLT	4	M12 45mm LONG (2D+6)	45mm	GRADE 8.8	-
06	STUDS	4	M12 STUDDING	400mm	GRADE 8.8	0.36 kg
07	U-BOLT	2	M12 U-BOLT FOR CHS 60.3mm	N/A	GRADE 8.8	-
						Total Weight: 8.07 kg

- All steel hot dip galvanized
- Each BOLT to be supplied with 1 Full Nut, 1 Form E Flat Washer and 1 Spring Washer
- Each STUD & U-BOLT to be supplied with 4 Full Nuts, 2 Flat Washers and 2 Spring Washers
- For fabrication notes see drawing 304

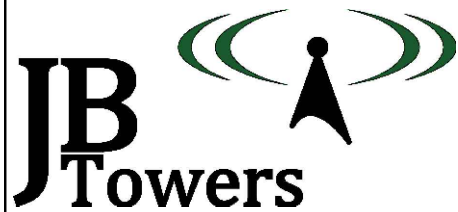


02	TPB-A-4 UPDATED	AM	02/05/19
01	FIRST ISSUE	TT	25/04/19
REV	REV	BY	DATE
SCALE AS SHOWN	DRAWN	CHECKED	APPROVED
WHEN PRINTED AT A3	DATE	DATE	DATE
AM	25/04/19	MP	JBT
ALL DIMENSIONS IN mm UNLESS OTHERWISE STATED. THIS DRAWING TO BE READ IN CONJUNCTION WITH OTHER RELEVANT DRAWINGS.			

TITLE		SITE ADDRESS		
STEELWORK BRACKET & TYPICAL CHS DETAIL		TALLEY ARQIVA SITE		
PART: TPB-A		PENLAN FACH		
		TALLEY, LLANDEILO		
		CARMARTHENSHIRE		
		SA19 7YN		
ARQIVA REF. 141680		DRG No. 301	REV 02	


ALL SCALES AS SHOWN WHEN PRINTED AT A3



ALL SCALES AS SHOWN WHEN PRINTED AT A3

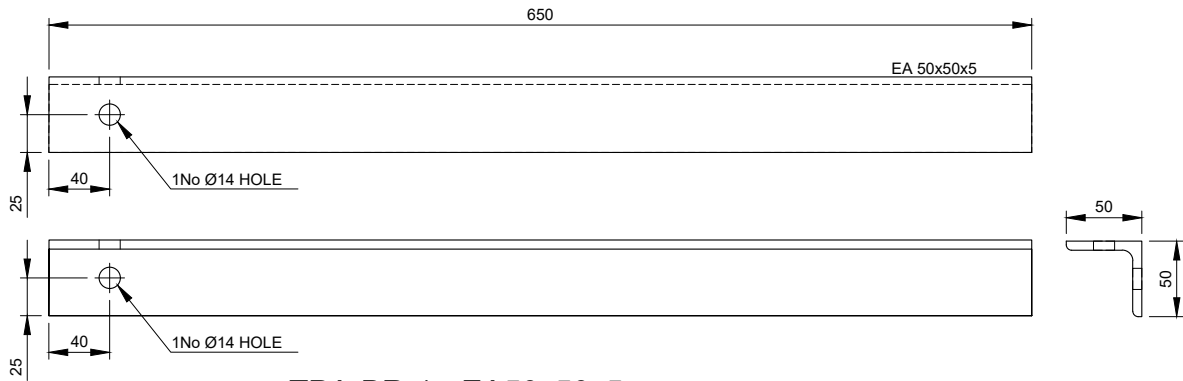

TPA-BR-1 - EA50x50x5
Scale 1:5

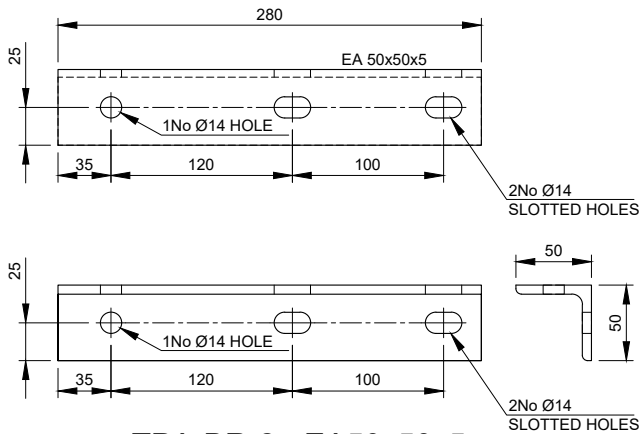


TPA-BR-2 - EA50x50x5
Scale 1:5


Parts list for TPA-BR

Item	Part	Quantity	Part description	Length	Material	Weight
01	TPB-BR-1	1	EA 50x50x5	280mm	S275J0	1.04 kg
02	TPB-BR-2	1	EA 50x50x5	650mm	S275J0	2.45 kg
03	TPB-BR-3	1	130x190x10mm	N/A	S275J0	1.94 kg
04	BOLT	1	M12 SET BOLT - 30mm LONG	N/A	GRADE 8.8	-
05	N-BOLT	2	M12 N-BOLT FOR EA 50x50x6	N/A	GRADE 8.8	-
06	U-BOLT	2	M12 U-BOLT FOR CHS 60.3mm	N/A	GRADE 8.8	-
Total Weight:						5.43 kg


- All steel hot dip galvanized
- Each BOLT to be supplied with 1 Full Nut, 1 Form E FLat Washer and 1 Spring Washer
- Each STUD & U-BOLT to be supplied with 4 Full Nuts, 2 Flat Washers and 2 Spring Washers
- For fabrctation notes see drawing 304

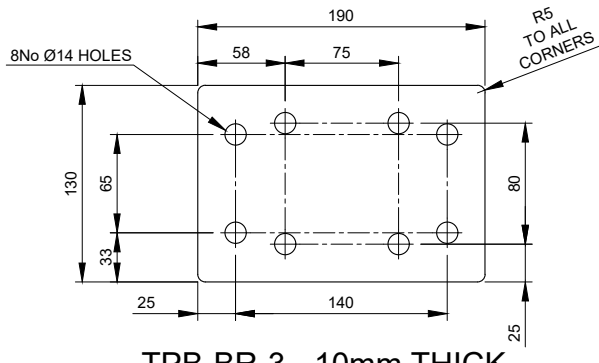

TPB-BR-3 - 10mm THICK
Scale 1:5

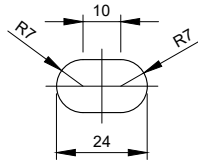

SLOTTED HOLE DETAIL
Scale 1:2

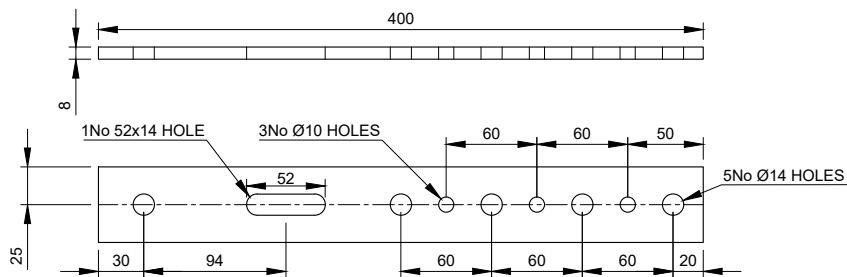


TPA-PD - 8mm THICK
Scale 1:5



Parts list for TPA-PD

Item	Part	Quantity	Part description	Length	Material	Weight
01	TPA-PD	1	400x50x8mm	N/A	S275J0	1.26 kg
02	U-BOLT	1	M12 U-BOLT FOR CHS 60.3mm	N/A	GRADE 8.8	-
Total Weight:						1.26 kg

- All steel hot dip galvanized
- Each U-BOLT to be supplied with 4 Full Nuts, 2 Flat Washers and 2 Spring Washers
- For fabrctation notes see drawing 304

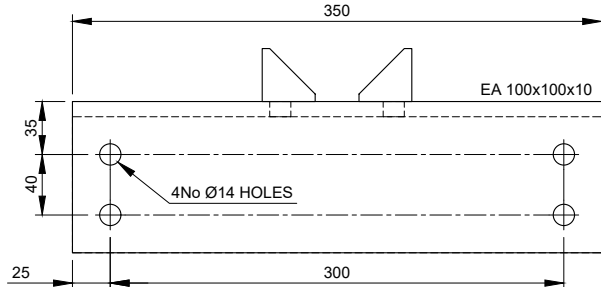


TPY-A - EA100x100x10
Scale 1:5

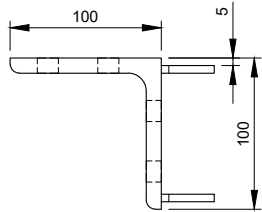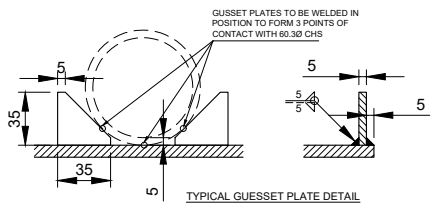

Parts list for TPY-A

Item	Part	Quantity	Part description	Length	Material	Weight
01	TPY-A	1	EA100x100x10	350mm	S275J0	5.25 kg
02	U-BOLT	2	M12 U-BOLT FOR CHS 25mm	N/A	GRADE 8.8	-
03	U-BOLT	2	M12 U-BOLT FOR CHS 60.3mm	N/A	GRADE 8.8	-
Total Weight:						5.25 kg

- All steel hot dip galvanized
- Each STUD & U-BOLT to be supplied with 4 Full Nuts, 2 Flat Washers and 2 Spring Washers
- Each BOLT to be supplied with 1 Full Nut, 1 Form E FLat Washer and 1 Spring Washer
- For fabrctation notes see drawing 304

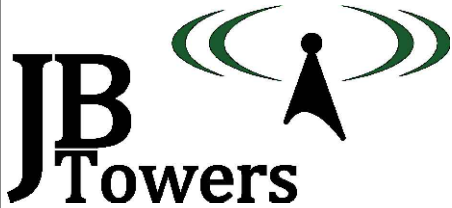

01	FIRST ISSUE	TT	25/04/19
REV	REV	BY	DATE
SCALE AS SHOWN WHEN PRINTED AT A3	DRAWN AM	CHECKED MP	APPROVED JBT
DATE 25/04/19	DATE 25/04/19	DATE 25/04/19	DATE 25/04/19
ALL DIMENSIONS IN mm UNLESS OTHERWISE STATED. THIS DRAWING TO BE READ IN CONJUNCTION WITH OTHER RELEVANT DRAWINGS.			

TITLE
BRACING KIT; POWER
DIVIDER STRAP; YAGI MOUNT

PARTS: TPA-BR; TPA-PD;
TPY-A



SITE ADDRESS
TALLEY
ARQIVA SITE
PENLAN FACH
TALLEY, LLANDEILO
CARMARTHENSHIRE
SA19 7YN

ARQIVA REF.
141680
DRG No.
302
REV
01

ALL SCALES AS SHOWN WHEN PRINTED AT A3





ALL SCALES AS SHOWN WHEN PRINTED AT A3

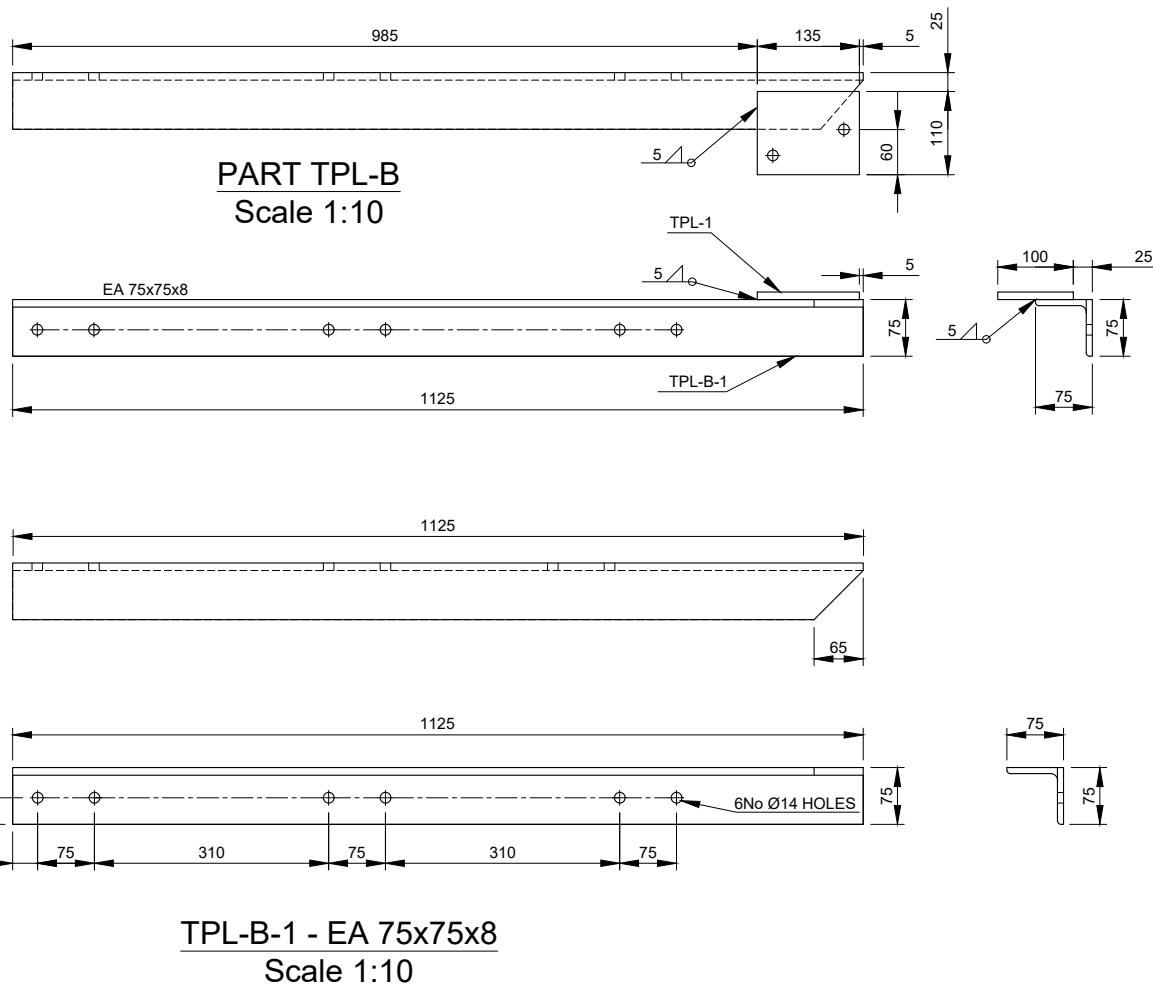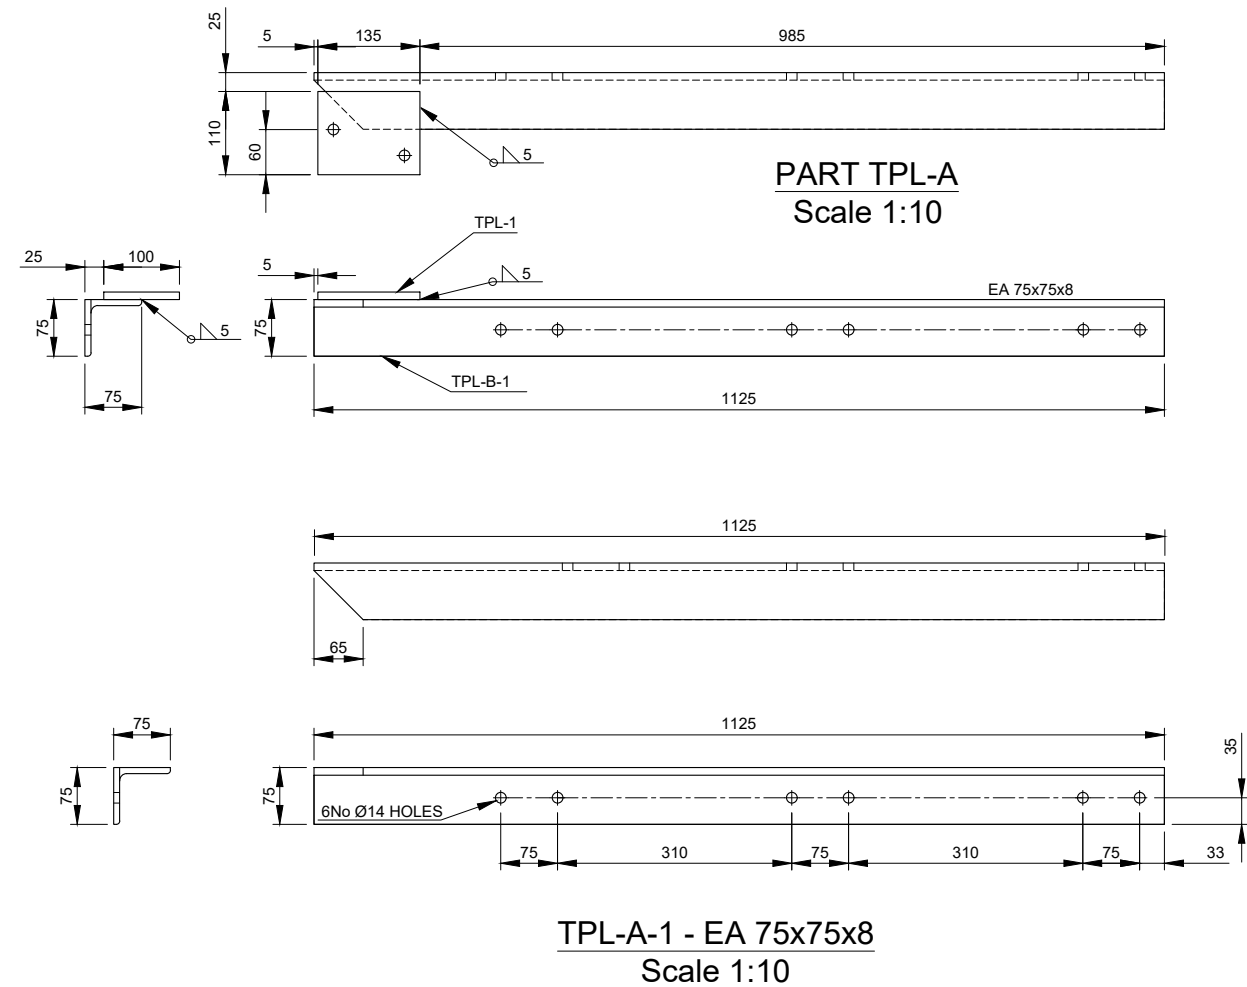

Parts list for TPL-A						
Item	Part	Quantity	Part description	Length	Material	Weight
01	TPL-A-1	1	EA 75x75x8	1125mm	S275J0	11.24 kg
02	TPL-1	1	110x135x10mm	N/A	S275J0	1.17 kg
03	U-BOLT	3	M12 U-BOLT FOR CHS 60.3mm	N/A	GRADE 8.8	-
Total Weight:						12.40 kg
- All steel hot dip galvanized						
- Each U-BOLT to be supplied with 4 Full Nuts, 2 Flat Washers and 2 Spring Washers						
- For fabrtaction notes see drawing 304						

Parts list for TPL-B						
Item	Part	Quantity	Part description	Length	Material	Weight
01	TPL-B-1	1	EA 75x75x8	1125mm	S275J0	11.24 kg
02	TPL-1	1	110x135x10mm	N/A	S275J0	1.17 kg
03	U-BOLT	3	M12 U-BOLT FOR CHS 60.3mm	N/A	GRADE 8.8	-
Total Weight:						12.40 kg
- All steel hot dip galvanized						
- Each U-BOLT to be supplied with 4 Full Nuts, 2 Flat Washers and 2 Spring Washers						
- For fabrtaction notes see drawing 304						

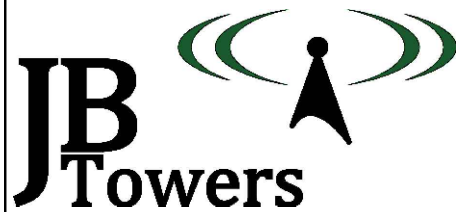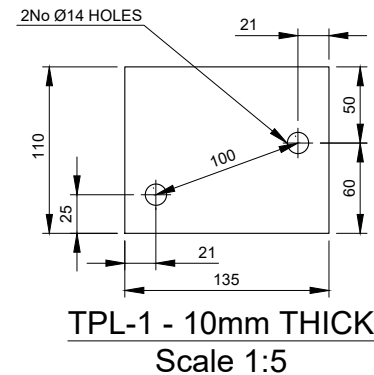

02	TPL-A-1 & TPL-B-1 UPDATED		AM 02/05/19
01	FIRST ISSUE		TT 25/04/19
REV	REV		BY DATE
SCALE AS SHOWN	DRAWN	AM	CHECKED
WHEN PRINTED AT A3	DATE	25/04/19	DATE
ALL DIMENSIONS IN mm UNLESS OTHERWISE STATED. THIS DRAWING TO BE READ IN CONJUNCTION WITH OTHER RELEVANT DRAWINGS.			

TITLE
LOG MOUNTING BRACKETS
PARTS: TPL-A; TPL-B

SITE ADDRESS
TALLEY
ARQIVA SITE
PENLAN FACH
TALLEY, LLANDEILO
CARMARTHENSHIRE
SA19 7YN

ARQIVA REF. 141680	DRG No. 303	REV 02
-----------------------	----------------	-----------

ALL SCALES AS SHOWN WHEN PRINTED AT A3




ALL SCALES AS SHOWN WHEN PRINTED AT A3

Item	Part	Drawing	Quantity	Part description	Length	Material	Weight
01	01	200	1	3 MAN LATCHWAY SYSTEM & 3No. WIRE GUIDES FOR FACE MOUNTED MONOPOLE	17000	N/A	-
02	TPB-C	300	2	FALL ARREST ATTACHMENT POINT	N/A	S275J0	4.48 kg
03	03	200	46	PERMANENT BT STEP c/w 3No 10x75mm ZINC-PLATED COACH SCREWS	N/A	S275J0	13.80 kg
04	TPS-R	300	9	'MonoStep' ASSEMBLY	N/A	S275J0	25.65 kg
05	TPB-A	301	3	MOUNTING BRACKET	N/A	S275J0	24.21 kg
06	06	203	3	CHS 60.3x5mm	2200mm	S355J2H	45.01 kg
07	TPL-A	303	2	LOG MOUNTING BRACKET	1125mm	S275J0	24.80 kg
08	TPL-B	303	2	LOG MOUNTING BRACKET	1125mm	S275J0	24.80 kg
09	09	203	24	M12 WASHER	N/A	GRADE 8.8	-
10	TPA-PD	302	2	POWER DIVIDER STRAP	N/A	S275J0	2.52 kg
11	11	204	1	CHS 60.3x5mm	500mm	S355J2H	3.41 kg
12	TPY-A	302	1	YAGI MOUNTING BRACKET	350mm	S275J0	5.25 kg
13	TPA-BR	303	2	BRACING KIT	N/A	S275J0	10.86 kg
14	14	200	1	FEEDER COVER - 2/CG/100	3500mm	UV RESISTANT PLASTIC	-
15	15	200	17	FEEDER CLAMP - 2/FCD/028	N/A	POLYPROPYLENE	-
16	16	200	17	M10 SCREW DOWELS WTH M10 NUT	100mm	STAINLESS STEEL	-
17	17	200	1	PoleSaver	750mm	N/A	-
18	18	200	8	M12 STUD + 4No NUTS + 2No FLAT WASHERS + 1No Ø50mm WASHER (FOR FALL ARREST SYSTEM)	500mm	GRADE 8.8	3.56 kg
Total Weight:							188.35 kg

- All steel hot dip galvanized
- All U-BOLTS to be FLA supply, each Supplied with 4 Full Nuts, 2 Flat Washers and 2 Spring Washers

NOTES:

1. WELDING TO BE IN ACCORDANCE WITH BS EN 1011-1:2009
2. LINEAR DIMS TO BE WITHIN ±1mm;
3. ANGULAR TOLERANCES TO BE WITHIN 0.5°
4. WELDING SYMBOLS ARE IN ACCORDANCE WITH BS EN 22553:1995
5. ALL PROFILE EDGES TO BE DRESSED AND SHARP CORNERS REMOVED
6. ALL WELD SIZES ARE FINAL SIZES
7. ALL WELDED JOINTS ARE TO BE PICKLE TIGHT
8. ALL STEELWORK TO BE BS EN 10025 GRADE S275 J0 UNO &
9. HOT DIPPED GALVANISED TO BS EN ISO 1461. (ALL HOLLOW SECTIONS TO BE GRADE S355 J0H)
10. ALL STEEL IS TO BE SUPPLIED IN ACCORDANCE WITH EN 1090 TO EXECUTION CLASS 2
11. ALL NON PRE-LOADED BOLTS TO BE COMPLIANT STRUCTURAL BOLTS TO BS EN ISO 15048 PARTS 1&2.
12. STEELWORK COMPONENTS SHALL BE HOT DIP GALVANISED TO ACHIEVE A "VERY HIGH" DURABILITY FOR AN ENVIRONMENT CATEGORY CODE C4 FROM TABLE 1 IN BS EN ISO 14713
13. BOLTS AND NUTS SHALL BE SUPPLIED IN ACCORDANCE WITH BS 7371, SPUN GALVANISED IN ACCORDANCE WITH ISO 10684, THE NUTS RE-TAPPED AFTER GALVANISING, AND THE THREADS TREATED WITH GREASE.
14. ALL BOLTS TO BE CUT ON SITE TO EXTEND MAX 10mm BEYOND THE NUT WHEN TIGHTENED UNO.
15. ALL SITE DRILLED HOLE/CUT ENDS TO BE TREATED WITH METAFLUX 70-40 ZINC PASTE FOLLOWED BY 1 COAT OF 7-42 ZINC ALU OR 70-16 ALUMINIUM SPRAY

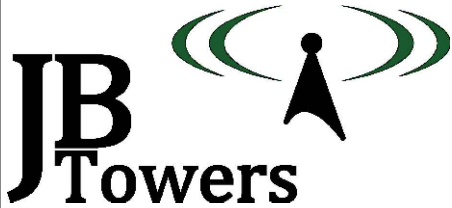

01	FIRST ISSUE			TT	25/04/19
REV	REV			BY	DATE
SCALE AS SHOWN		DRAWN	AM	CHECKED	MP
WHEN PRINTED AT A3		DATE	25/04/19	DATE	25/04/19
APPROVED		JBT			
ALL DIMENSIONS IN mm UNLESS OTHERWISE STATED. THIS DRAWING TO BE READ IN CONJUNCTION WITH OTHER RELEVANT DRAWINGS.					

TITLE


PARTS LIST

SITE ADDRESS		
TALLEY ARQIVA SITE PENLAN FACH TALLEY, LLANDEILO CARMARTHENSHIRE SA19 7YN		
ARQIVA REF. 141680	DRG No. 304	REV 01


ALL SCALES AS SHOWN WHEN PRINTED AT A3




ALL SCALES AS SHOWN WHEN PRINTED AT A3

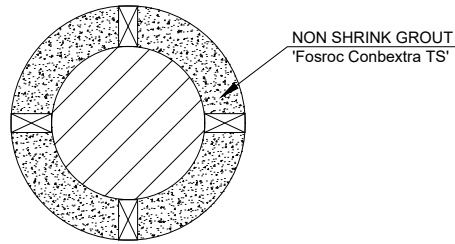

POROPOSED INSTALLATION
PLAN VIEW
Scale 1:20

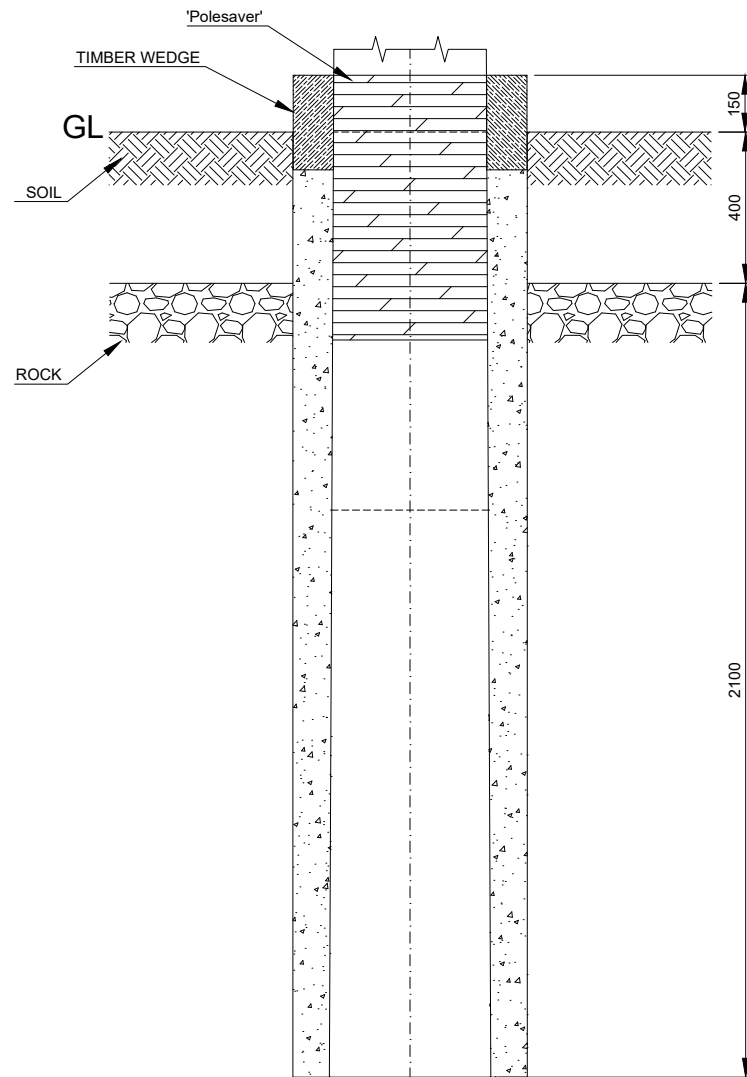


POROPOSED INSTALLATION
ELEVATION
Scale 1:20

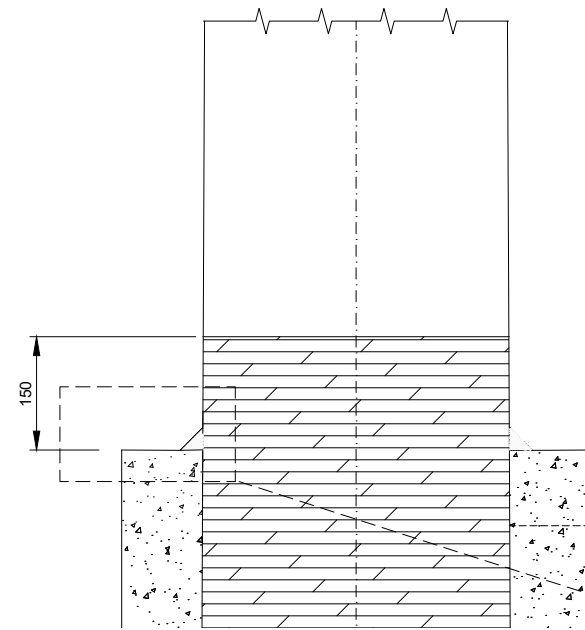


WATER PROOFING
Scale 1:10

TIMBER POLE INSTALLATION:

1. REFER TO DRAWING 200 FOR TIMBER POLE ORIENTATION
2. BASE OF TIMBER POLE TO BE WRAPPED IN 'polesaver' & INSTALLED AND LEVELLED IN OPENING. TIMBERS TO BE USED TO HOLD POLE IN POSITION & THEN ANNULUS GROUTED UP WITH NON SHRINK GROUT
3. 3.ONCE THE GROUT HAS CURED THE TIMBER WEDGES SHALL BE REMOVED AND VOIDS LEFT ARE TO BE FILLED WITH NON SHRINK GROUT. A 1:60 FALL SHALL BE FORMED AROUND THE TIMBER POLE TO ALLOW WATER TO DRAIN AWAY

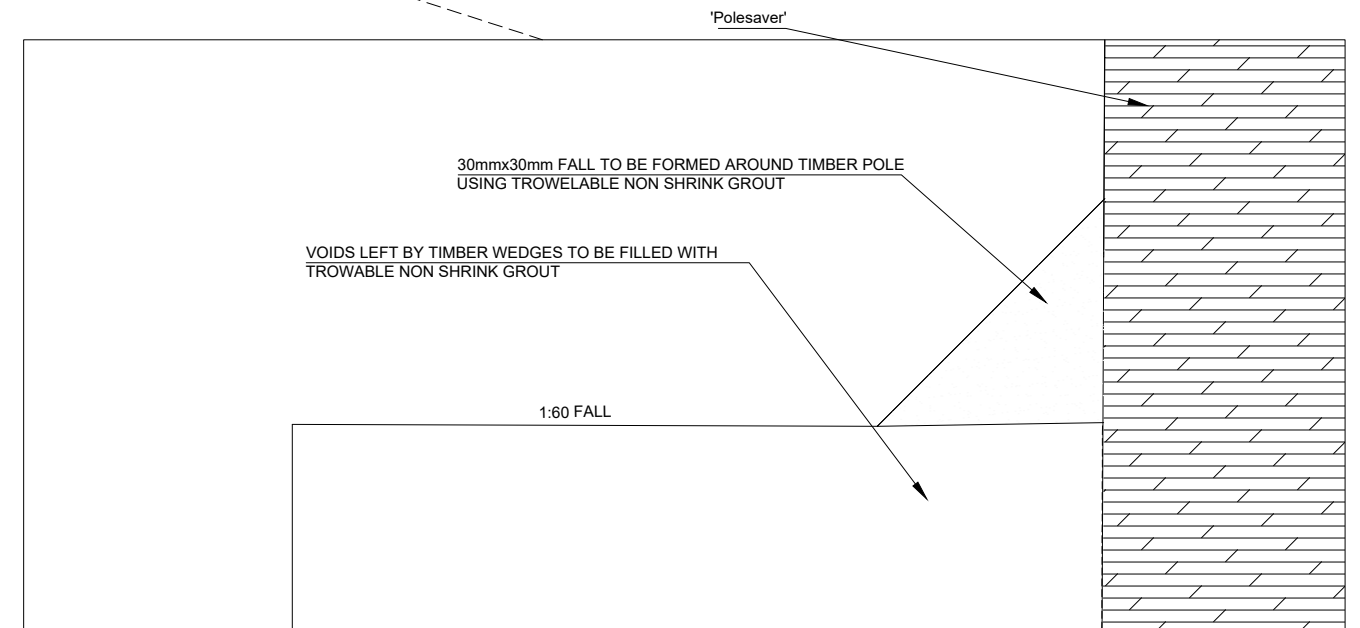

ENLARGED DETAIL
Scale 1:1

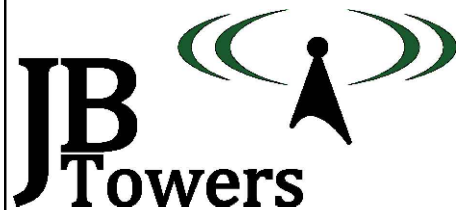

01	FIRST ISSUE			TT	25/04/19
REV	REV			BY	DATE
SCALE AS SHOWN WHEN PRINTED AT A3		DRAWN AM DATE 25/04/19	CHECKED MP DATE 25/04/19	APPROVED JB DATE 25/04/19	
ALL DIMENSIONS IN mm UNLESS OTHERWISE STATED. THIS DRAWING TO BE READ IN CONJUNCTION WITH OTHER RELEVANT DRAWINGS.					

TITLE	SITE ADDRESS
FOUNDATION DETAILS	TALLEY ARQIVA SITE PENLAN FACH TALLEY, LLANDEILO CARMARTHENSHIRE SA19 7YN
ARQIVA REF. 141680	DRG No. 400
REV 01	

ALL SCALES AS SHOWN WHEN PRINTED AT A3



ALL SCALES AS SHOWN WHEN PRINTED AT A3