




DRAWING ISSUE SHEET

[illegible]

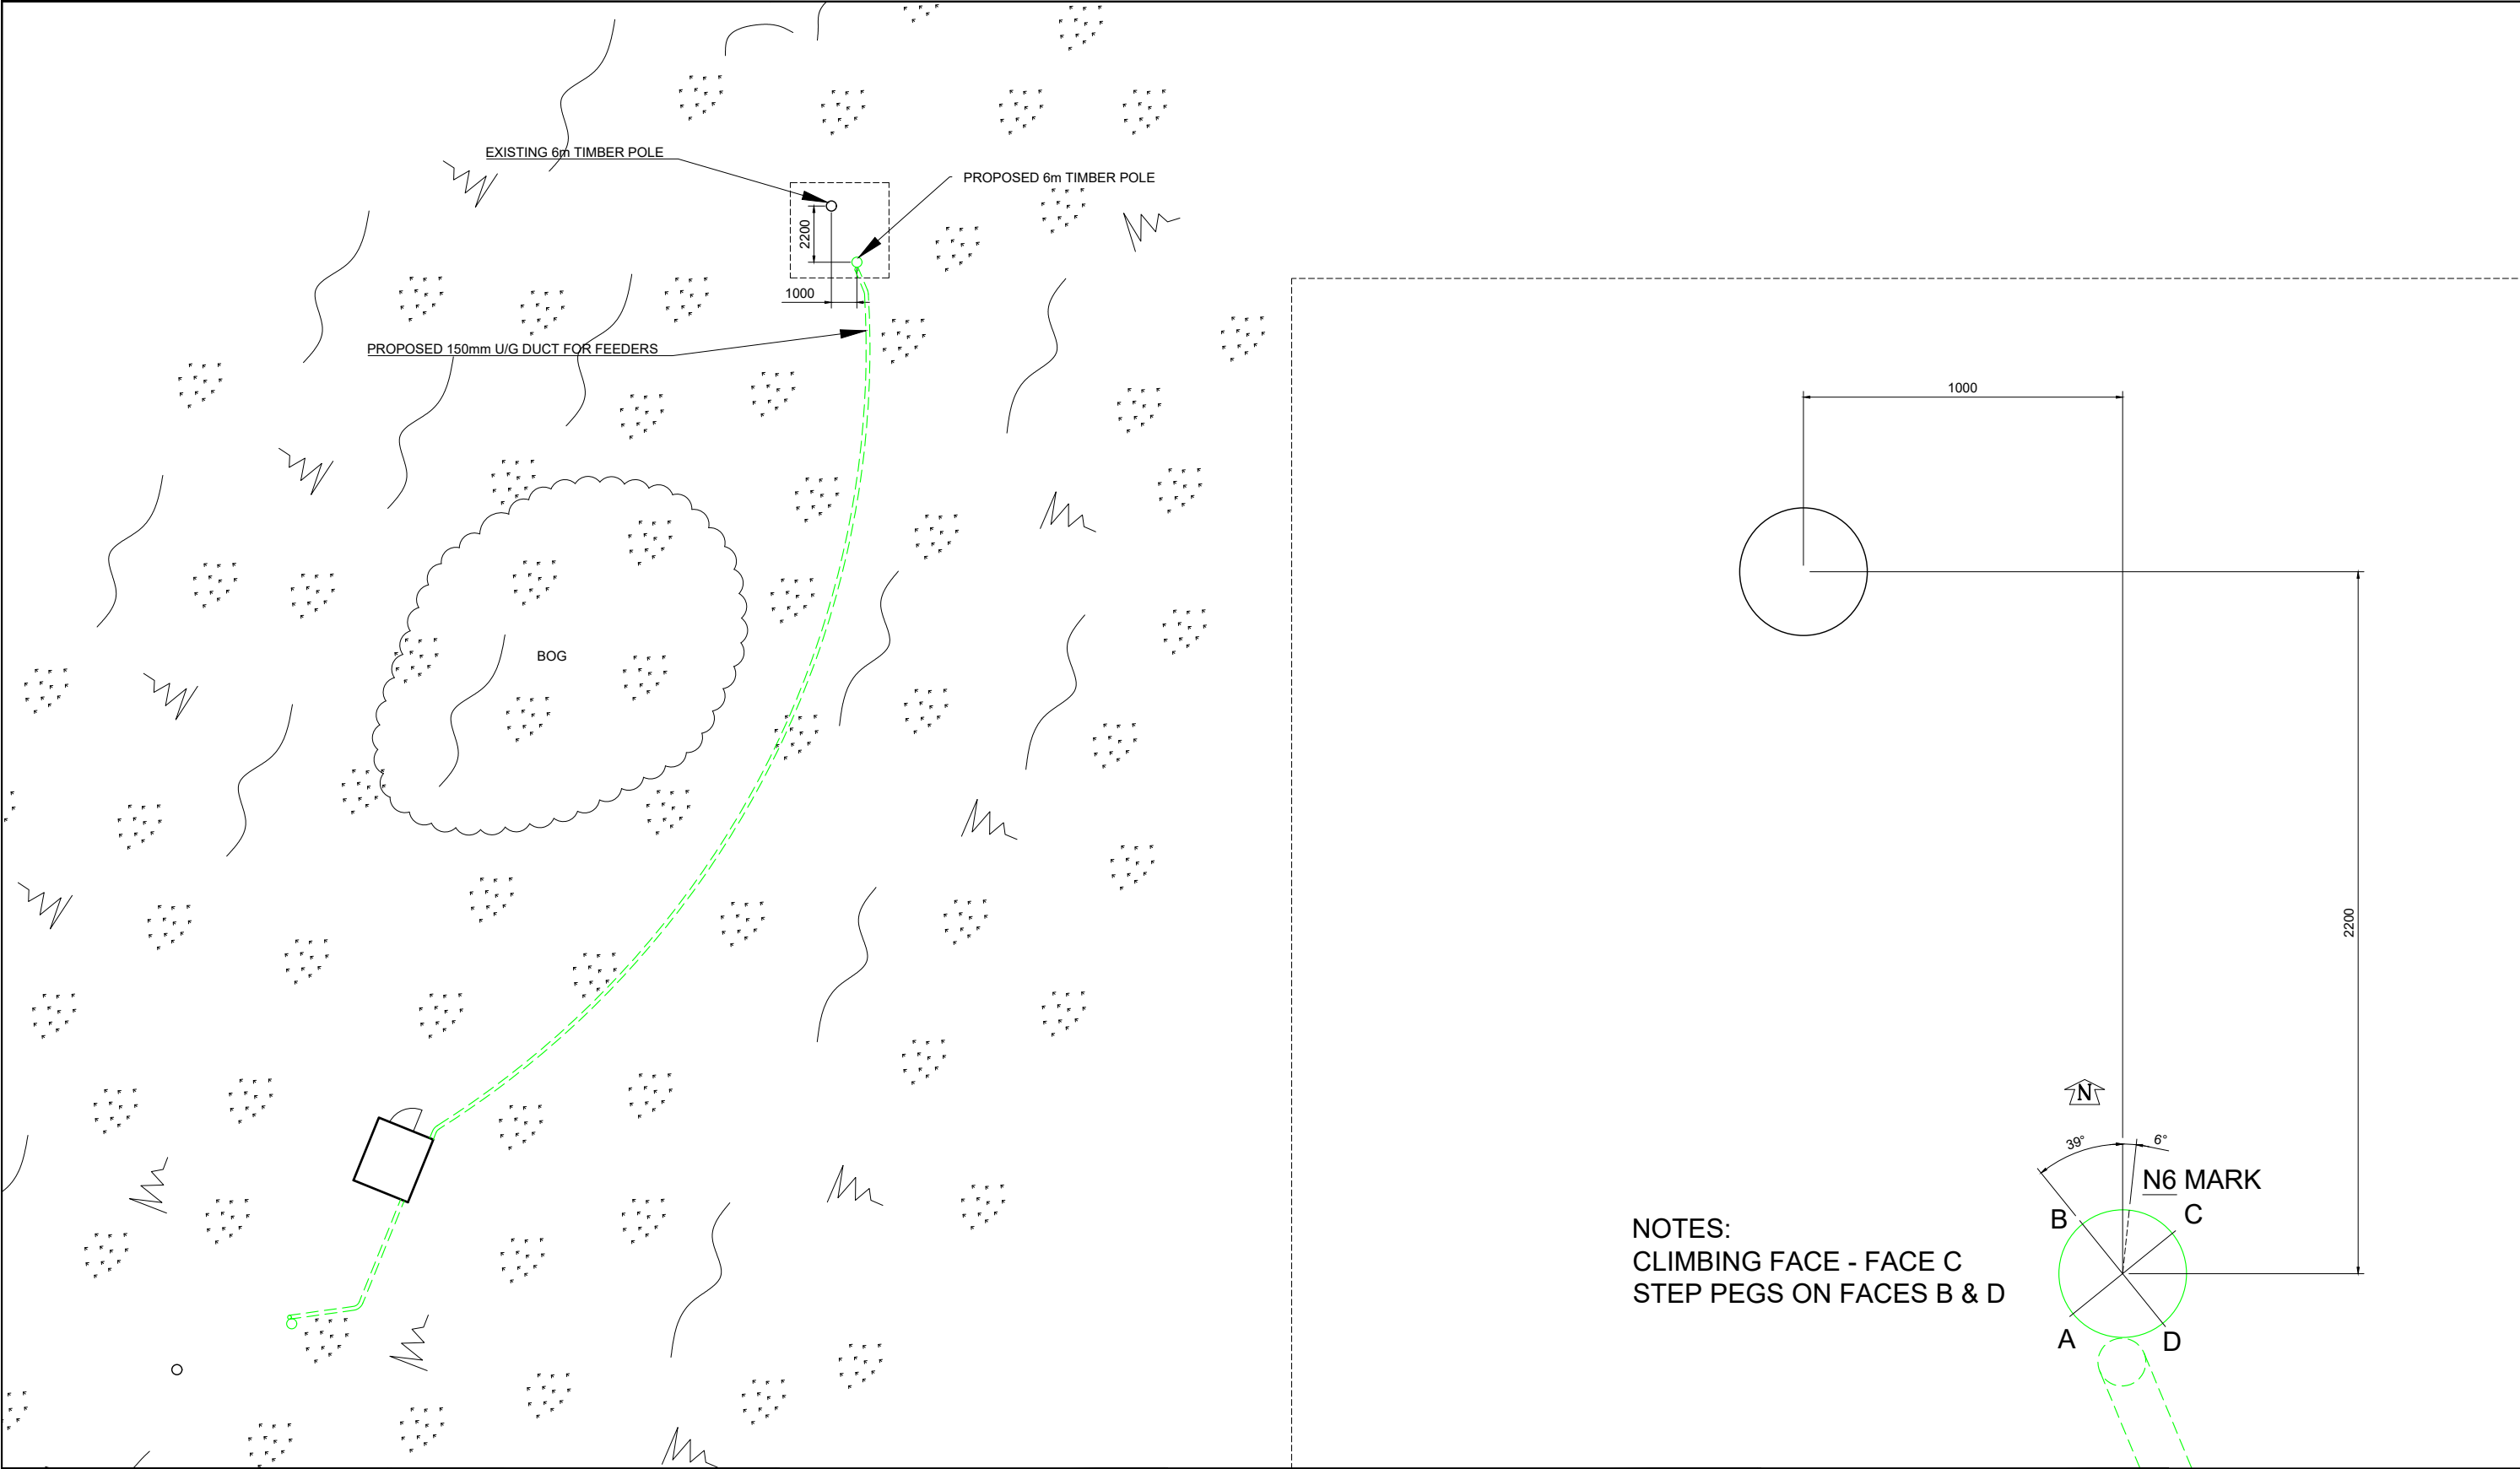

NOTES:
CLIMBING FACE - FACE C
STEP PEGS ON FACES B & D

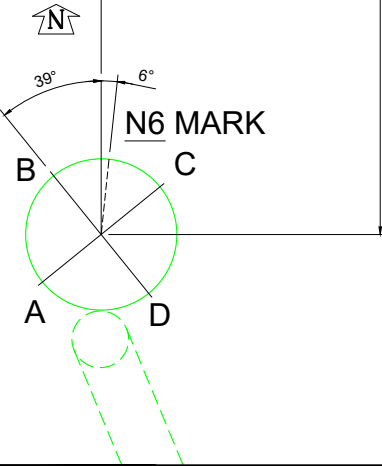

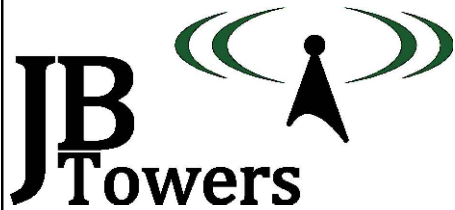



01	FIRST ISSUE	AM	23/07/19
REV	REV	BY	DATE
SCALE AS SHOWN WHEN PRINTED AT A3	DRAWN DATE 23/07/19	CHECKED DATE 23/07/19	MP DATE 23/07/19
ALL DIMENSIONS IN mm UNLESS OTHERWISE STATED. THIS DRAWING TO BE READ IN CONJUNCTION WITH OTHER RELEVANT DRAWINGS.			

TITLE
TOMICH LINK
SITE PLAN

SITE ADDRESS
GUISACHAN FARM
TOMICH
STRATHGLASS
HIGHLAND
IV4 7LF

ARQIVA REF.
141679


DRG No.
100

REV
01

ALL SCALES AS SHOWN WHEN PRINTED AT A3

0cm 1cm 2cm 3cm 4cm 5cm 6cm 7cm 8cm 9cm 10cm

ALL SCALES AS SHOWN WHEN PRINTED AT A3

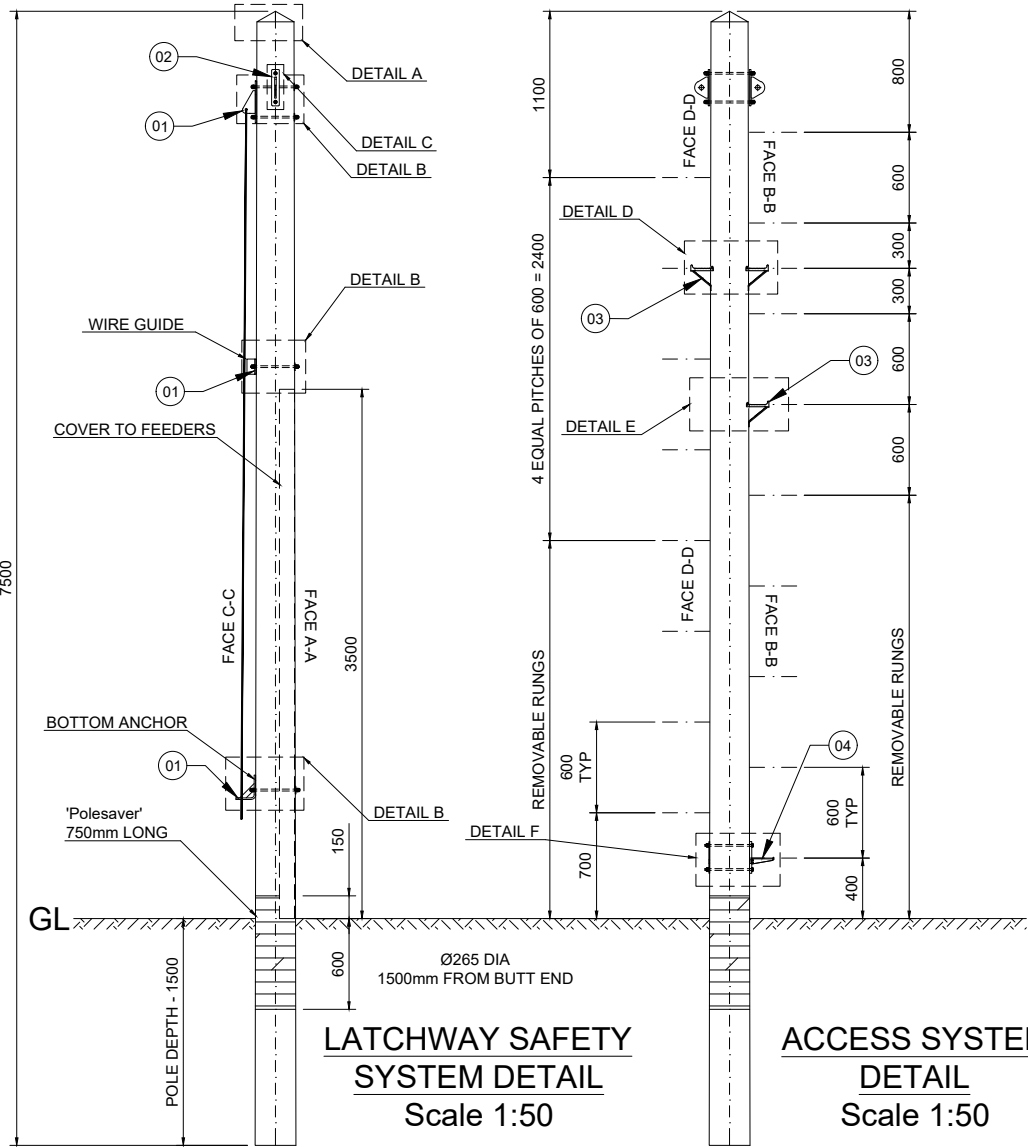

**LATCHWAY SAFETY
SYSTEM DETAIL**
Scale 1:50

**ACCESS SYSTEM
DETAIL**
Scale 1:50

NOTES


1. SEE DRAWING 305 FOR PARTS LIST
2. ALL BOLTS TO BE CUT ON SITE TO EXTEND MAX 10mm BEYOND THE NUT WHEN TIGHTENED UNO.
3. ALL SITE DRILLED HOLE/CUT ENDS TO BE TREATED WITH METAFUX 70-40 ZINC PASTE FOLLOWED BY 1 COAT OF 7-42 ZINC ALU OR 70-16 ALUMINIUM SPRAY

TIMBER POLE

1. POLE TO BE SUPPLIED IN ACCORDANCE WITH BS EN14229 & SHALL HAVE MIN. CHARACTERISTIC BENDING STRENGTH OF 30N/mm² & MIN. YOUNGS MODULUS (PARALLEL TO GRAIN) OF 10KN/mm².
2. MARKINGS ON FINISHED POLE SHALL BE AT 4m FROM BUTT AND COMPLY WITH BS EN 14229 UNO
3. AS FAR AS PRACTICABLE ALL CUTTING, SCARFING & DRILLING TO BE DONE BEFORE CREOSOTING. IF NOT ALL CUT, DRILLED & SCARFED SURFACES TO BE COATED WITH A MIXTURE OF CREOSOTE & TAR.
4. POLE TO BE PRESSURE IMPREGNATED WITH CREOSOTE IN ACCORDANCE WITH BS EN 14229
5. MINIMUM DIAMETERS
TOP - Ø205mm
BOTTOM - Ø270mm

PLANTING


1. CAT SCANNER IS TO BE USED IN ORDER TO CONFIRM THE POSITIONS OF BURIED SERVICES.
2. SEE DRAWING 400 FOR FOUNDATION DETAILS.
3. TIMBER POLE TO BE PLANTED WITH N6 MARKING AT 2.5m FROM BUT FACING 6° FROM NORTH (CLOCKWISE)

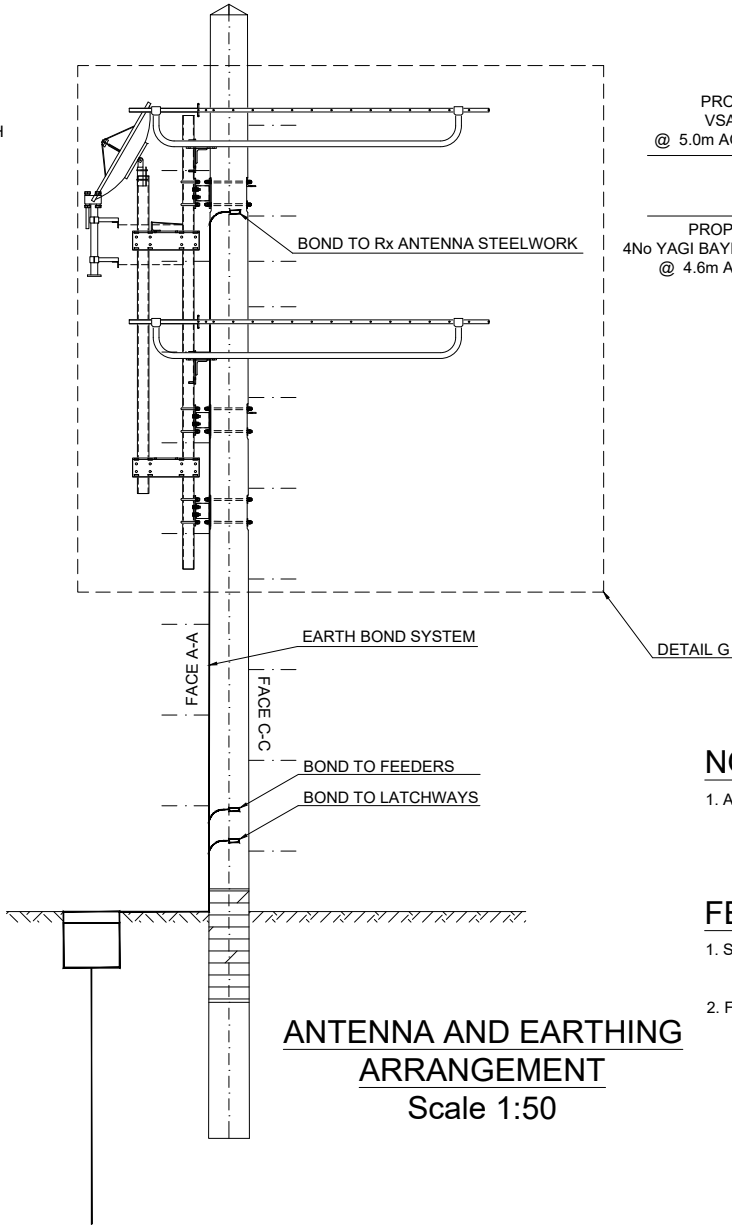


**ANTENNA AND EARTHING
ARRANGEMENT**
Scale 1:50

PROPOSED
VSAT DISH
@ 5.0m AGL MEAN 209°

PROPOSED Rx
4No YAGI BAYED AND STACKED
@ 4.6m AGL MEAN 51°

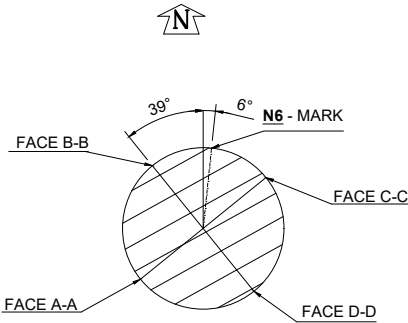

POLE ORIENTATION
Scale 1:20

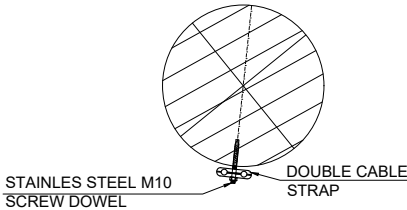

FEEDER MANAGEMENT
Scale 1:20

NOTES


1. AS FAR AS IS PRACTICABLE ALL CUTTING SCARFING AND DRILLING TO BE DONE BEFORE CREOSOTING. WHERE THIS IS NOT POSSIBLE ALL CUT, DRILLED, AND SCARFED SURFACES TO BE COATED WITH A MIXTURE OF CREOSOTE AND TAR

FEEDERS

1. SUPPLY OF FEEDERS BY OTHERS LCF12-50 TO Rx ANTENNA & RG11 TO VSAT DISH
2. FEEDERS FIXED AT 1000mm CENTRES

EARTHING

1. CONNECT EARTH BOND TO NEW EARTHING SYSTEM
2. MAXIMUM VALUE FOR GROUND RESISTANCE TO BE 10 OHMS
3. CABLE OR TAPE TO BE FIXED TO POLE AT 1000mm CENTRES
4. EARTHING SHOULD COMPLY WITH ARQIVA'S DOCUMENT BOS147

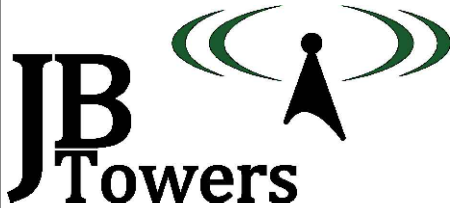

01	FIRST ISSUE	AM	23/07/19
REV	REV	BY	DATE
SCALE AS SHOWN WHEN PRINTED AT A3	DRAWN DATE 23/07/19	CHECKED DATE 23/07/19	APPROVED DATE 23/07/19
ALL DIMENSIONS IN mm UNLESS OTHERWISE STATED. THIS DRAWING TO BE READ IN CONJUNCTION WITH OTHER RELEVANT DRAWINGS.			

TITLE
TOMICH LINK
GENERAL ARRANGEMENT
SHEET 1 OF 2

SITE ADDRESS
GUISACHAN FARM
TOMICH
STRATHGLASS
HIGHLAND
IV4 7LF

ARQIVA REF.
141679


DRG No.
200

REV
01

ALL SCALES AS SHOWN WHEN PRINTED AT A3




ALL SCALES AS SHOWN WHEN PRINTED AT A3

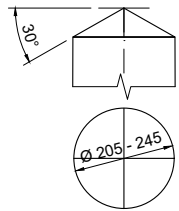


- NOTES:
1. A SINGLE COAT OF TIMBER COMPATIBLE BITUMINOUS PAINT (E.G. BIRD BRAND BLACK BITUMINOUS PAINT OR SIMILAR APPROVED PRODUCT) TO BE APPLIED TO THE UPPER SURFACES AT THE TOP OF THE POLE.
 2. PAINT TO BE APPLIED ON SITE JUST BEFORE ERECTION
- FORM: 4 WAY PYRAMID / CONE


DETAIL A - TIMBER POLE TOP
Scale 1:20

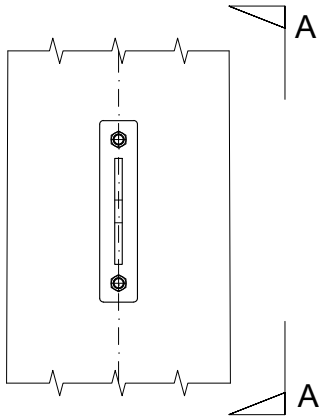


DETAIL C - FALL ARREST
ATTACHMENT POINT
Scale 1:10

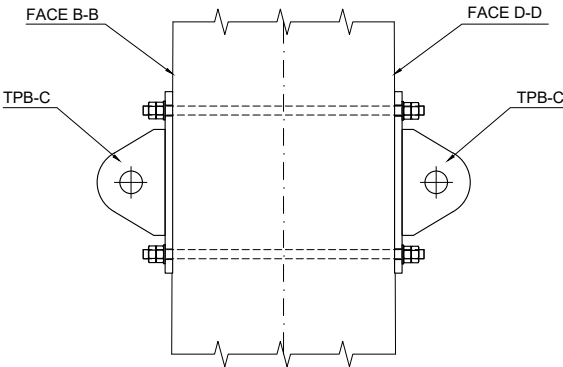

VIEW A-A
Scale 1:10

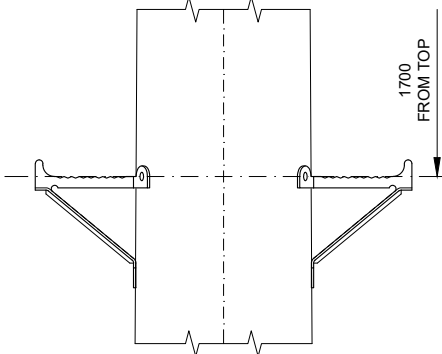


DETAIL D - ANTENNA
ACCESS CLIMBING STEP
Scale 1:10

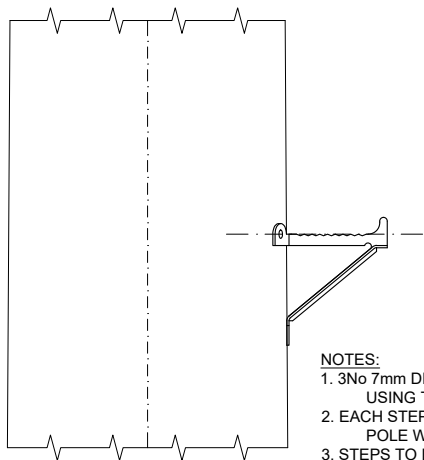


DETAIL E - PERMANENT
CLIMBING STEPS
Scale 1:10


- NOTES:
1. 3No 7mm DIA 70mm LONG PILOT HOLES TO BE DRILLED USING THE STEP AS A TEMPLATE
 2. EACH STEP SHOULD BE FIXED TO THE TIMBER POLE WITH 3No 10mm COACH SCREWS 75mm LONG
 3. STEPS TO BE INSTALLED ON FACES B-B & D-D ONLY

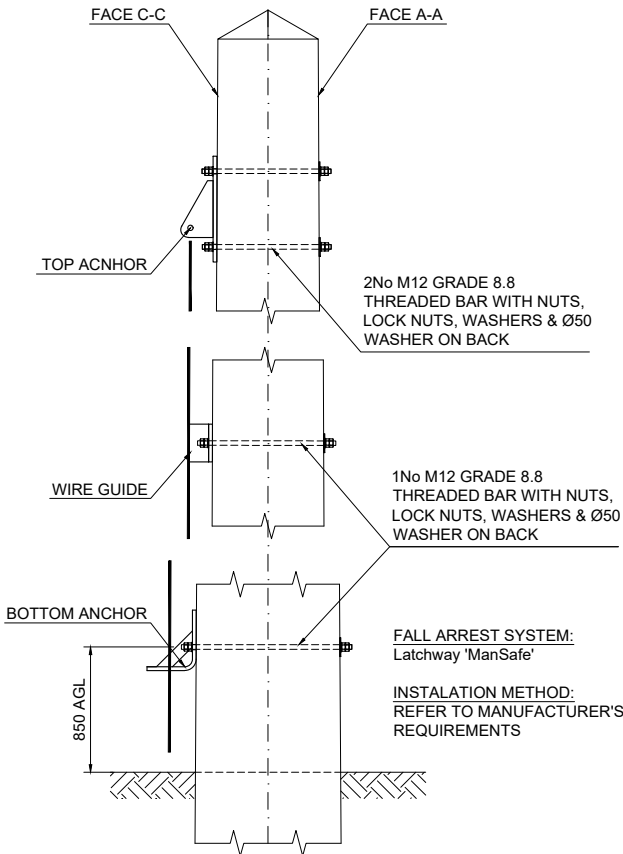

DETAIL B - FALL ARREST SYSTEM
Scale 1:20

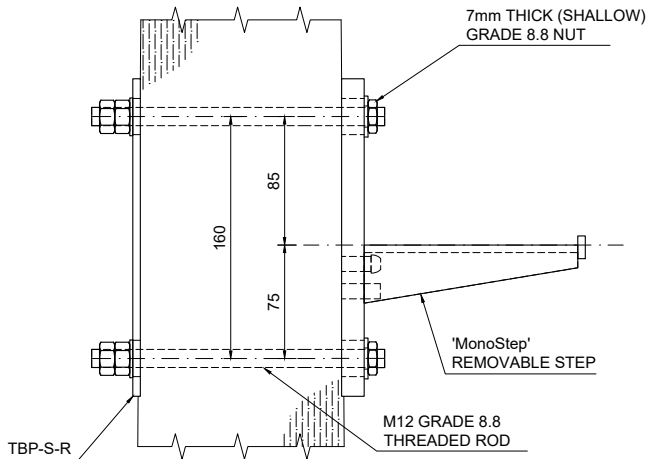

DETAIL F - REMOVABLE
CLIMBING STEPS
Scale 1:5

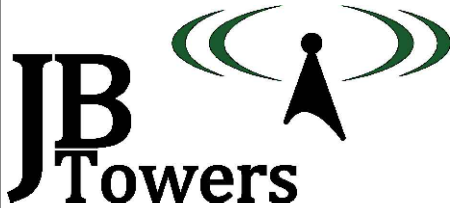

01	FIRST ISSUE	AM	23/07/19
REV	REV	BY	DATE
SCALE AS SHOWN	DRAWN	CHECKED	APPROVED
WHEN PRINTED AT A3	AM	MP	JBT
DATE	23/07/19	DATE	23/07/19
DATE	23/07/19	DATE	23/07/19
ALL DIMENSIONS IN mm UNLESS OTHERWISE STATED. THIS DRAWING TO BE READ IN CONJUNCTION WITH OTHER RELEVANT DRAWINGS.			

TITLE

TOMICH LINK

GENERAL ARRANGEMENT

SHEET 2 OF 2

SITE ADDRESS

GUISACHAN FARM

TOMICH

STRATHGLASS

HIGHLAND

IV4 7LF

ARQIVA REF.
141679







DRG No.
200

REV
01


ALL SCALES AS SHOWN WHEN PRINTED AT A3



ALL SCALES AS SHOWN WHEN PRINTED AT A3

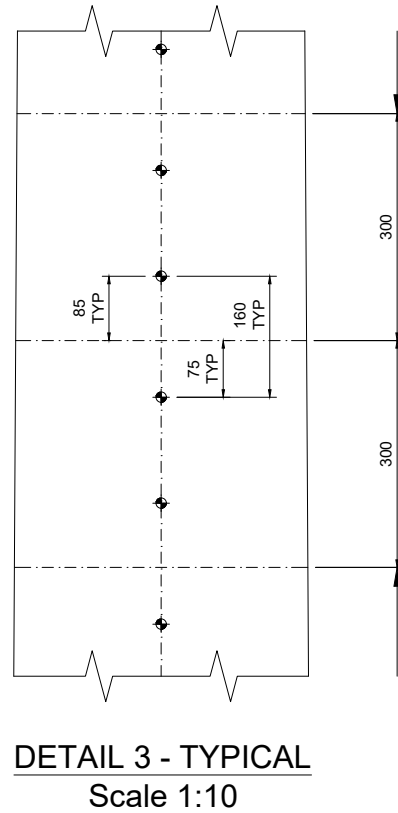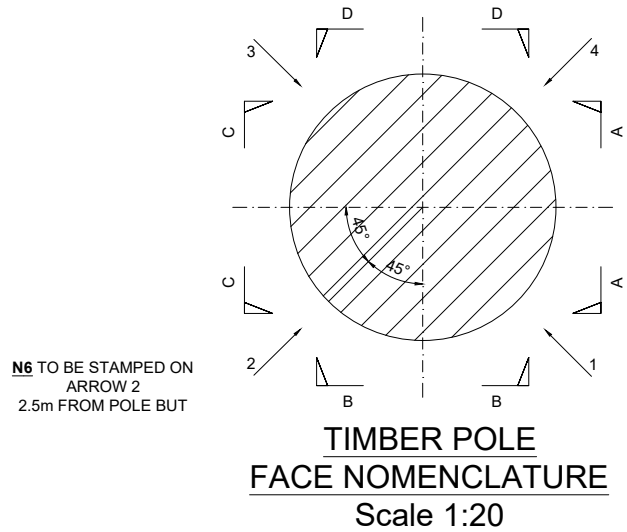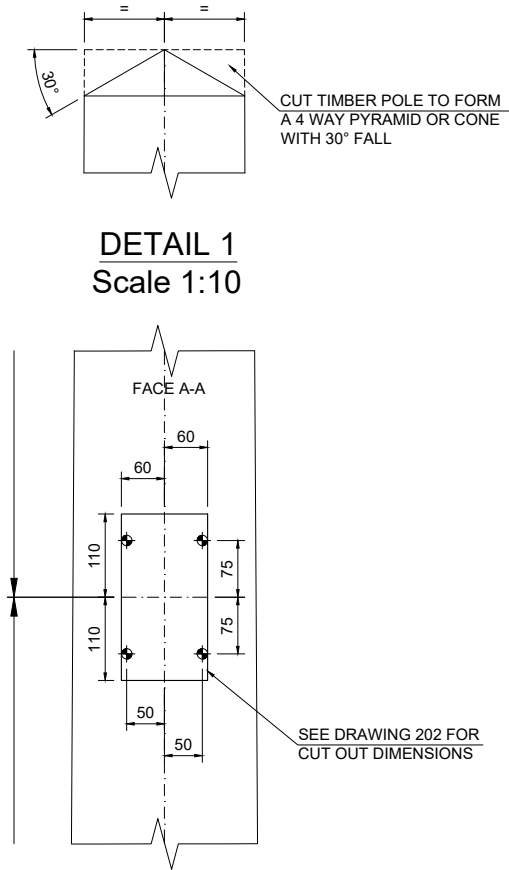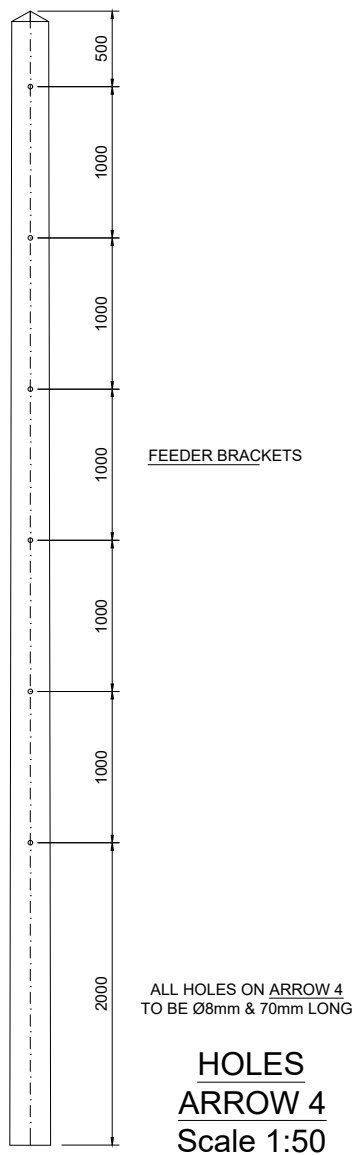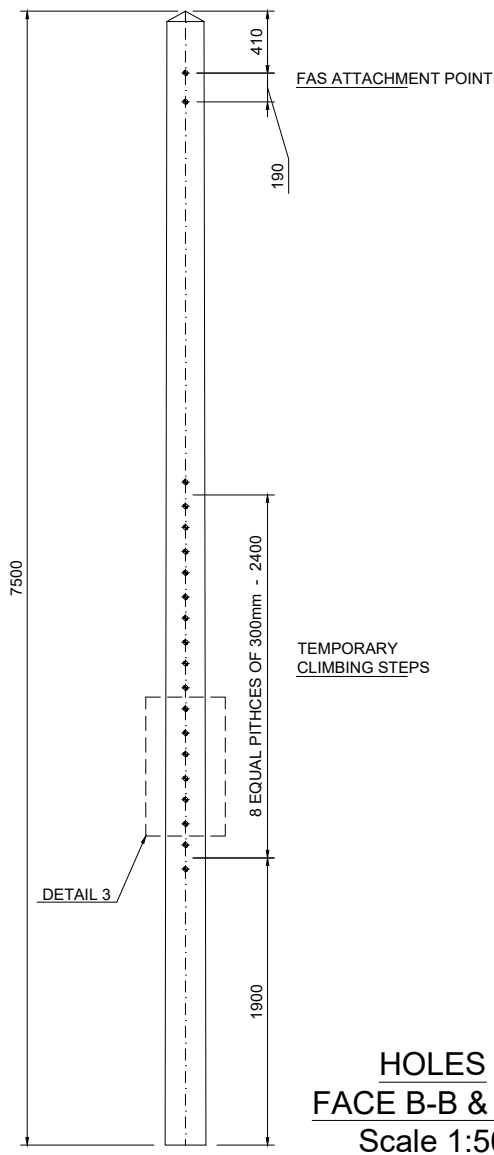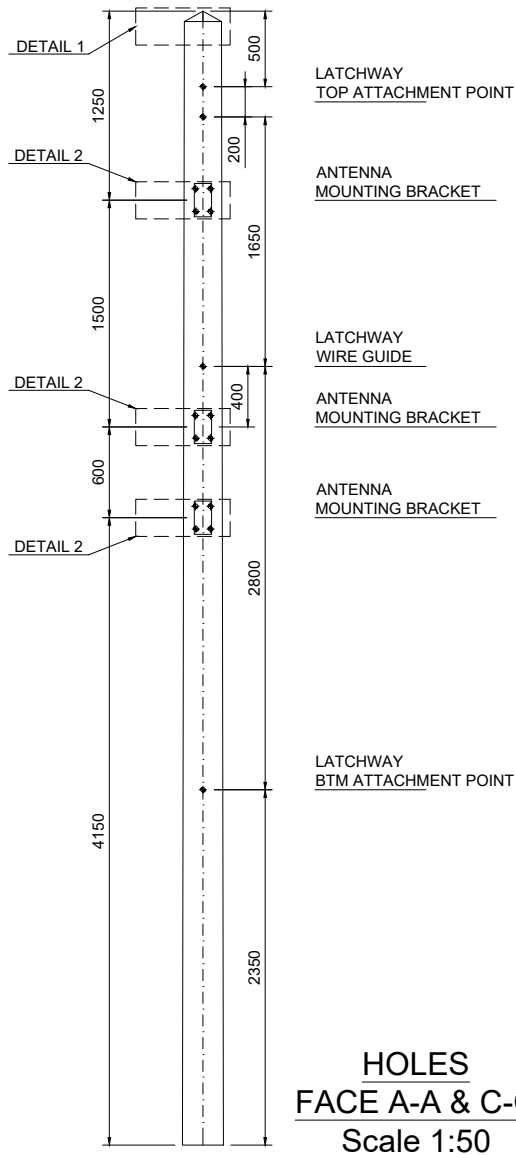

HOLE DIAMETERS	
	- 16mm THROUGH HOLE
	- 8mm HOLE 70mm LONG

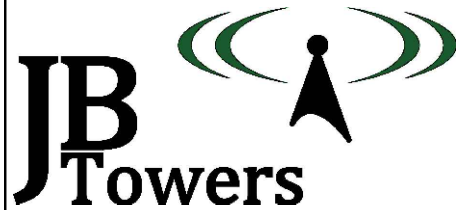

01	FIRST ISSUE	AM	23/07/19
REV	REV	BY	DATE
SCALE AS SHOWN WHEN PRINTED AT A3	DRAWN AM	CHECKED MP	APPROVED JBT
DATE 23/07/19	DATE 23/07/19	DATE 23/07/19	DATE 23/07/19
ALL DIMENSIONS IN mm UNLESS OTHERWISE STATED. THIS DRAWING TO BE READ IN CONJUNCTION WITH OTHER RELEVANT DRAWINGS.			

TITLE
TOMICH LINK
TIMBER POLE HOLE SET OUT

SITE ADDRESS
GUISACHAN FARM
TOMICH
STRATHGLASS
HIGHLAND
IV4 7LF

ARQIVA REF. 141679	DRG No. 201	REV 01
-----------------------	----------------	-----------

ALL SCALES AS SHOWN WHEN PRINTED AT A3



01	FIRST ISSUE					AM	23/07/19
REV	REV					BY	DATE
SCALE AS SHOWN WHEN PRINTED AT A3		DRAWN	AM	CHECKED	MP	APPROVED	JBT
		DATE	23/07/19	DATE	23/07/19	DATE	23/07/19
ALL DIMENSIONS IN mm UNLESS OTHERWISE STATED. THIS DRAWING TO BE READ IN CONJUNCTION WITH OTHER RELEVANT DRAWINGS.							


TITLE
TOMICH LINK
TIMBER POLE CUT OUT
DETAIL


SITE ADDRESS
GUISACHAN FARM
TOMICH
STRATHGLASS
HIGHLAND
IV4 7LF

ARQIVA REF.
141679

DRG No.
202


REV
01

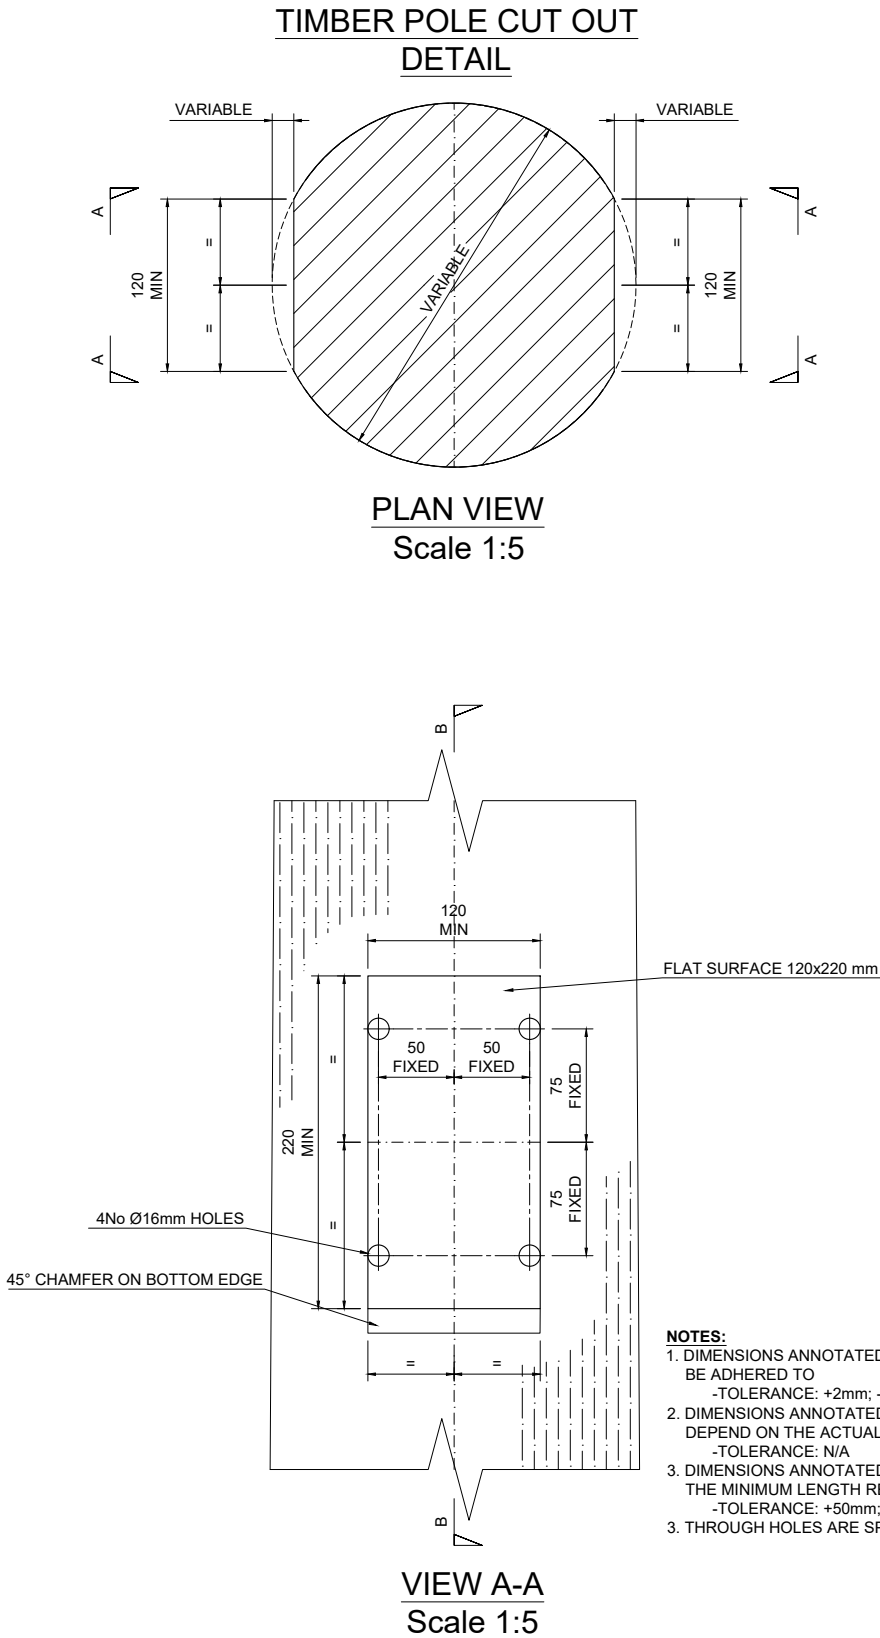

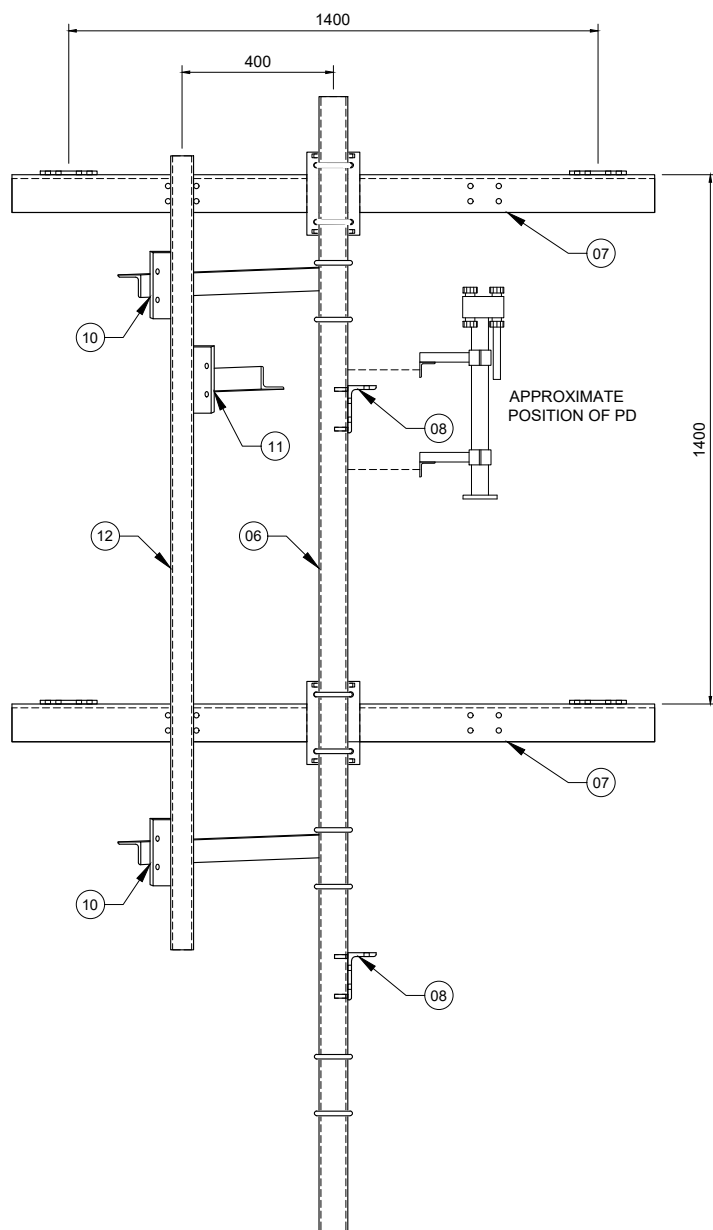


SECTION C-C
Scale 1:20


NOTE:
ALL M12 U/N-BOLTS TO BE
TIGHTENED TO 50Nm

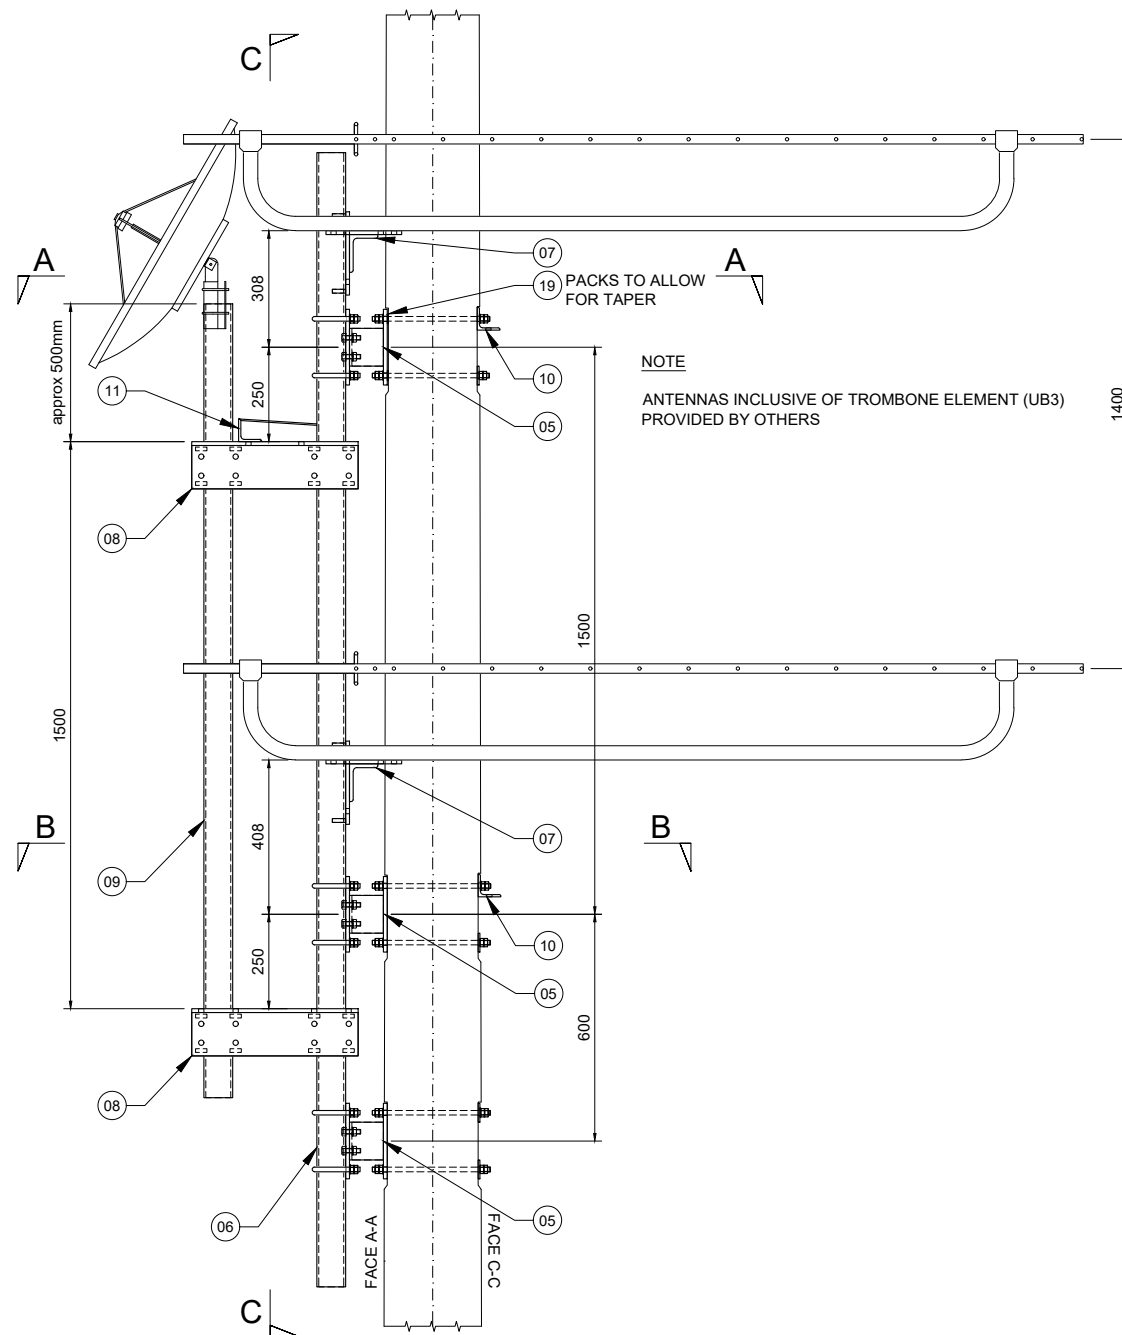


DETAIL G - ANTENNA MOUNTS
Scale 1:20

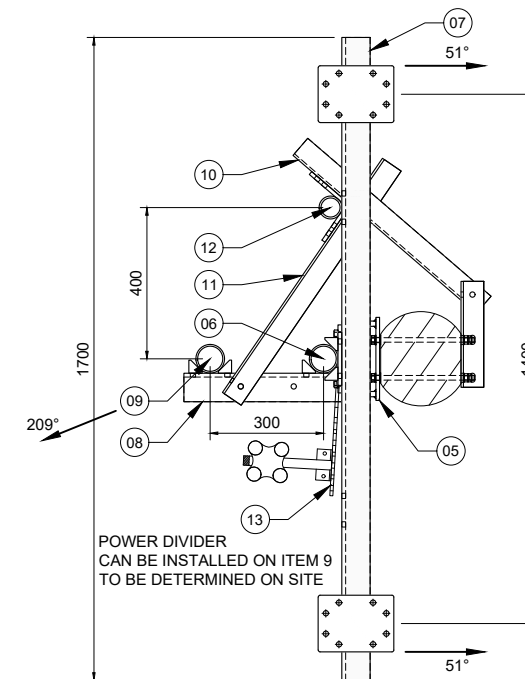

SECTION A-A
Scale 1:20

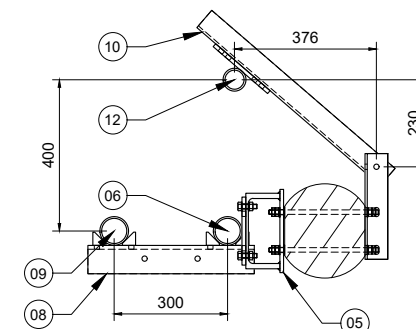

SECTION B-B
Scale 1:20

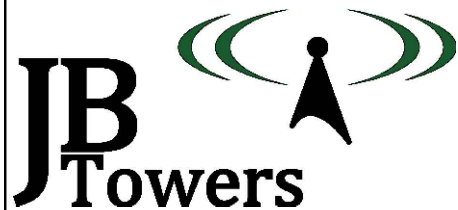


01	FIRST ISSUE				AM	23/07/19
REV	REV				BY	DATE
SCALE AS SHOWN		DRAWN	AM	CHECKED	MP	APPROVED JBT
WHEN PRINTED AT A3		DATE	23/07/19	DATE	23/07/19	DATE 23/07/19
ALL DIMENSIONS IN mm UNLESS OTHERWISE STATED. THIS DRAWING TO BE READ IN CONJUNCTION WITH OTHER RELEVANT DRAWINGS.						


TITLE	ANTENNA MOUNTS
DETAIL G	

SITE ADDRESS		
GUISACHAN FARM TOMICH STRATHGLASS HIGHLAND IV4 7LF		
ARQIVA REF. 141679	DRG No. 203	REV 01

ALL SCALES AS SHOWN WHEN PRINTED AT A3

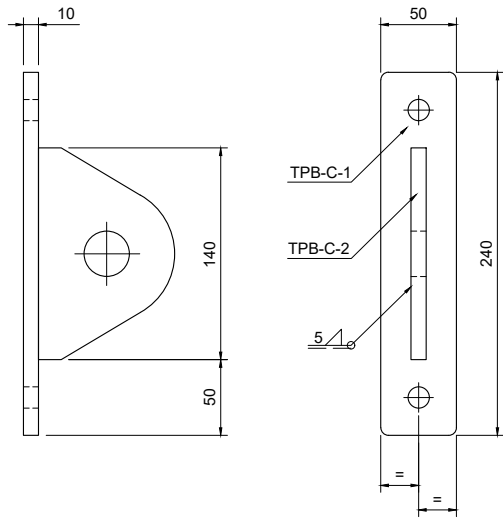

PART TPB-C
Scale 1:5

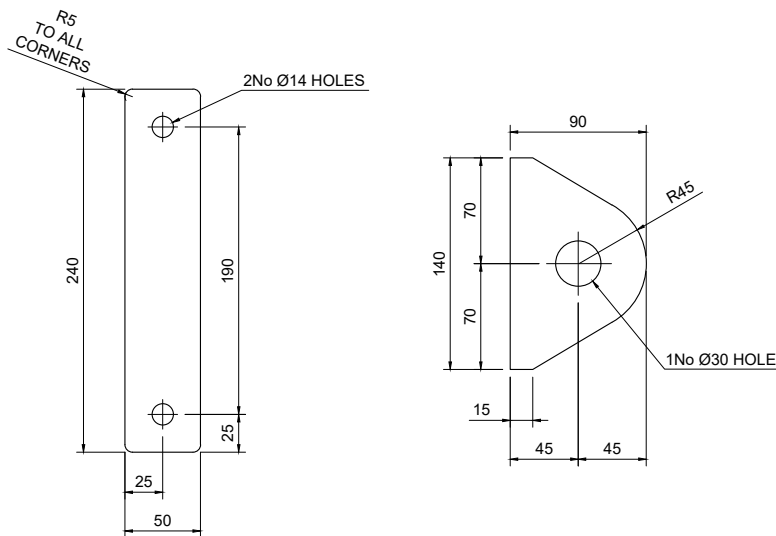


TPB-C-1 - 10mm THICK
Scale 1:5

TPB-C-2 - 10mm THICK
Scale 1:5

Parts list for TPB-C


Item	Part	Quantity	Part description	Length	Material	Weight
01	TPB-C-1	1	Plate 240x50x10mm	N/A	S275J0	0.94 kg
02	TPB-C-2	1	Plate 140x90x10mm	N/A	S275J0	0.99 kg
03	STUDS	1	M12 STUDDING	350mm	GRADE 8.8	0.31 kg
Total Weight:						2.24 kg

- All steel hot dip galvanized
- Each STUD to be supplied with 4 Full Nuts, 2 Flat Washers and 2 Spring Washers
- For fabrication notes see drawing 305

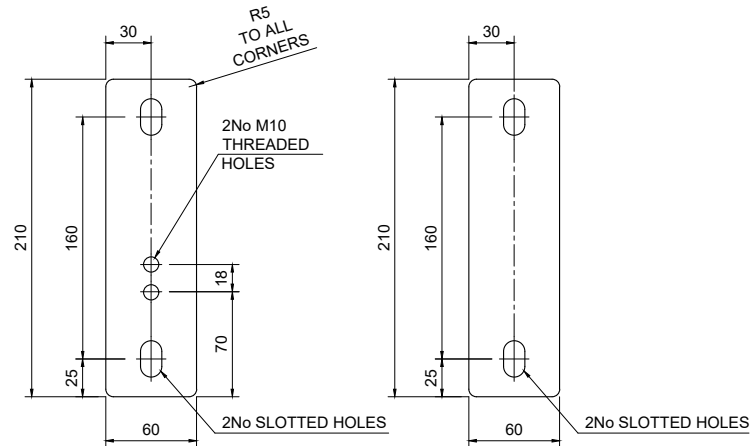

PART TPS-R-1
Scale 1:5

PART TPS-R-2
Scale 1:5

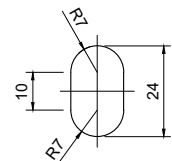


SLOTTED HOLE DETAIL
Scale 1:2

Parts list for TPS-R

Item	Part	Quantity	Part description	Length	Material	Weight
01	TPS-R-1	1	210x60x15mm	N/A	S275J0	1.48 kg
02	TPS-R-2	1	210x60x5mm	N/A	S275J0	0.49 kg
03	STUDS	2	M12 STUDDING	500mm	GRADE 8.8	0.44 kg
04	NUT-S	2	M12 SHALLOW NUT	N/A	GRADE 8.8	-
05	NUT	4	M12 NUT	N/A	GRADE 8.8	-
06	WSH	4	M12 WASHER	N/A	GRADE 8.8	-
Total Weight:						2.85 kg

- All steel hot dip galvanized
- For fabrication notes see drawing 305

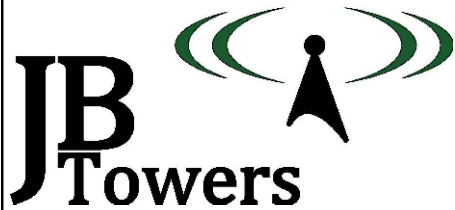



01	FIRST ISSUE	AM	23/07/19
REV	REV	BY	DATE
SCALE AS SHOWN WHEN PRINTED AT A3	DRAWN DATE 23/07/19	CHECKED DATE 23/07/19	APPROVED DATE 23/07/19
ALL DIMENSIONS IN mm UNLESS OTHERWISE STATED. THIS DRAWING TO BE READ IN CONJUNCTION WITH OTHER RELEVANT DRAWINGS.			

TITLE		SITE ADDRESS		
ATTACHMENT POINT & TEMPORARY STEP DETAILS		GUISACHAN FARM TOMICH STRATHGLASS HIGHLAND IV4 7LF		
PARTS: TPB-C; TPS-R		ARQIVA REF. 141679	DRG No. 300	REV 01


ALL SCALES AS SHOWN WHEN PRINTED AT A3




ALL SCALES AS SHOWN WHEN PRINTED AT A3

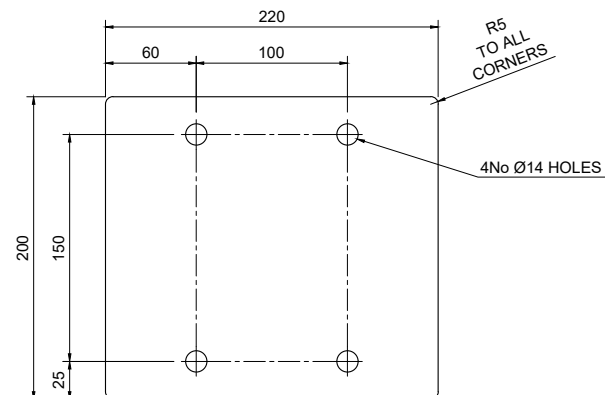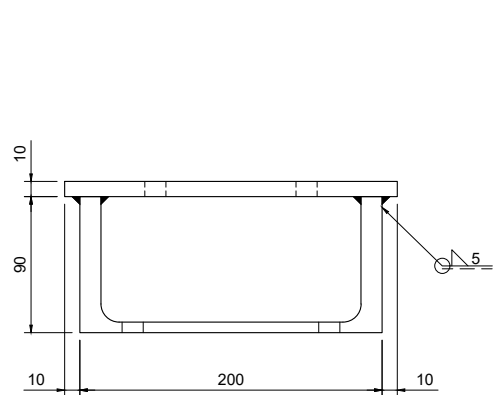


TPB-B-1 - 10mm THICK
Scale 1:5

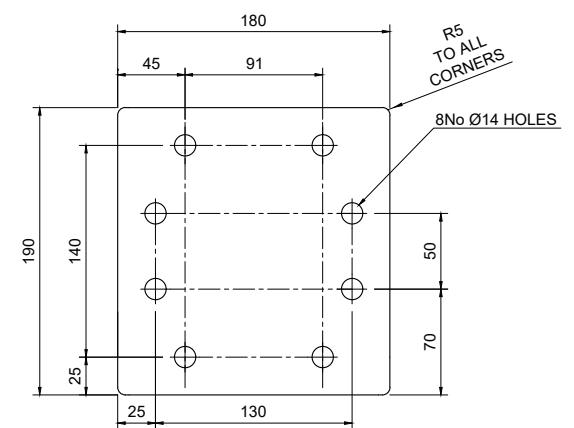


TPB-B-5 - 10mm THICK
Scale 1:5

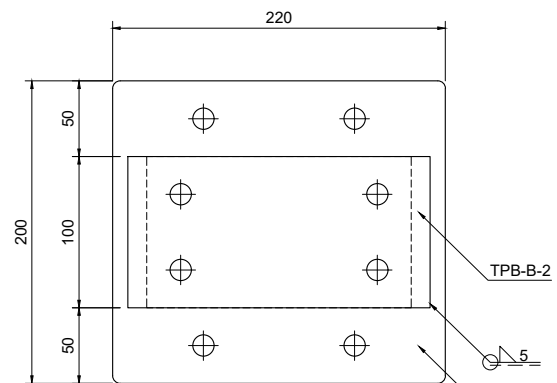

PART TPB-B
Scale 1:5

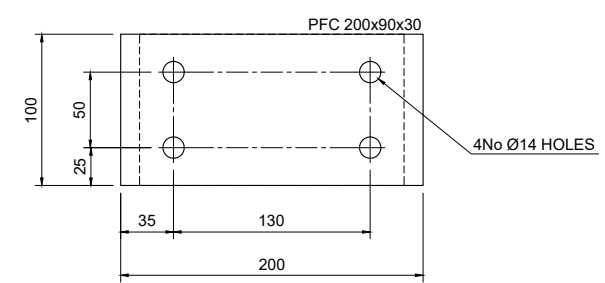

TPB-B-2 - PFC 200x90x30
Scale 1:5

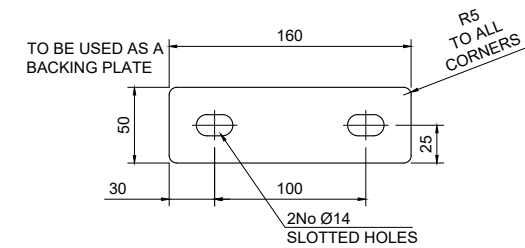


TPB-B-4 - 5mm THICK
Scale 1:5


Parts list for TPB-B

Item	Part	Quantity	Part description	Length	Material	Weight
01	TPB-B-1	1	Plate 220x200x10mm	N/A	S275J0	3.45 kg
02	TPB-B-2	1	PFC 200x90x30	100mm	S275J0	3.00 kg
03	TPB-B-4	2	Plate 160x50x5mm	N/A	S275J0	0.31 kg
04	TPB-B-5	1	Plate 190x180x10mm	N/A	S275J0	2.70 kg
05	STUDS	4	M12 STUDDING	450mm	GRADE 8.8	0.39 kg
06	BOLT	4	M12 45mm LONG (2D+6)	45mm	GRADE 8.8	-
07	U-BOLT	2	M12 U-BOLT FOR CHS 76.1	N/A	GRADE 8.8	-
Total Weight:						11.33 kg

- All steel hot dip galvanized
- Each STUD & U-BOLT to be supplied with 4 Full Nuts, 2 Flat Washers and 2 Spring Washers
- Each BOLT to be supplied with 1 Full Nut, 1 Form E FLat Washer and 1 Spring Washer
- For fabrication notes see drawing 305

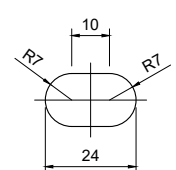






SLOTTED HOLE DETAIL
Scale 1:2

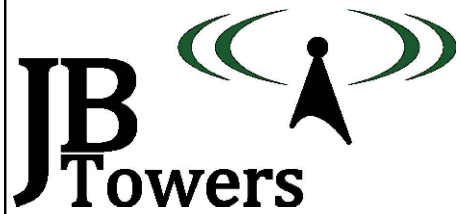

01	FIRST ISSUE	AM	23/07/19
REV	REV	BY	DATE
SCALE AS SHOWN	DRAWN	CHECKED	APPROVED
WHEN PRINTED AT A3	DATE	DATE	DATE
ALL DIMENSIONS IN mm UNLESS OTHERWISE STATED. THIS DRAWING TO BE READ IN CONJUNCTION WITH OTHER RELEVANT DRAWINGS.			

TITLE		SITE ADDRESS	
MOUNTING BRACKET		GUISACHAN FARM	
PART: TPB-B		TOMICH	
		STRATHGLASS	
		HIGHLAND	
		IV4 7LF	
ARQIVA REF.		DRG No.	REV
141679		301	01

ALL SCALES AS SHOWN WHEN PRINTED AT A3

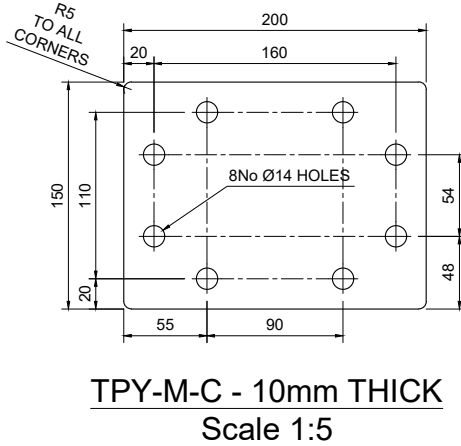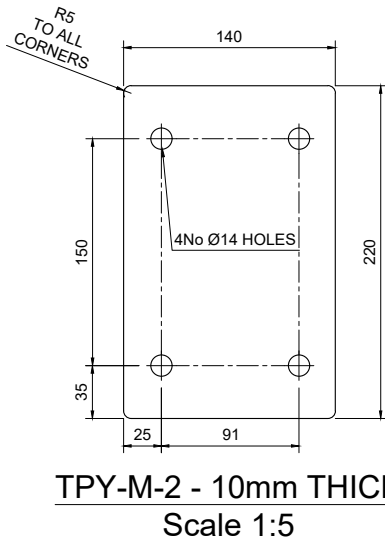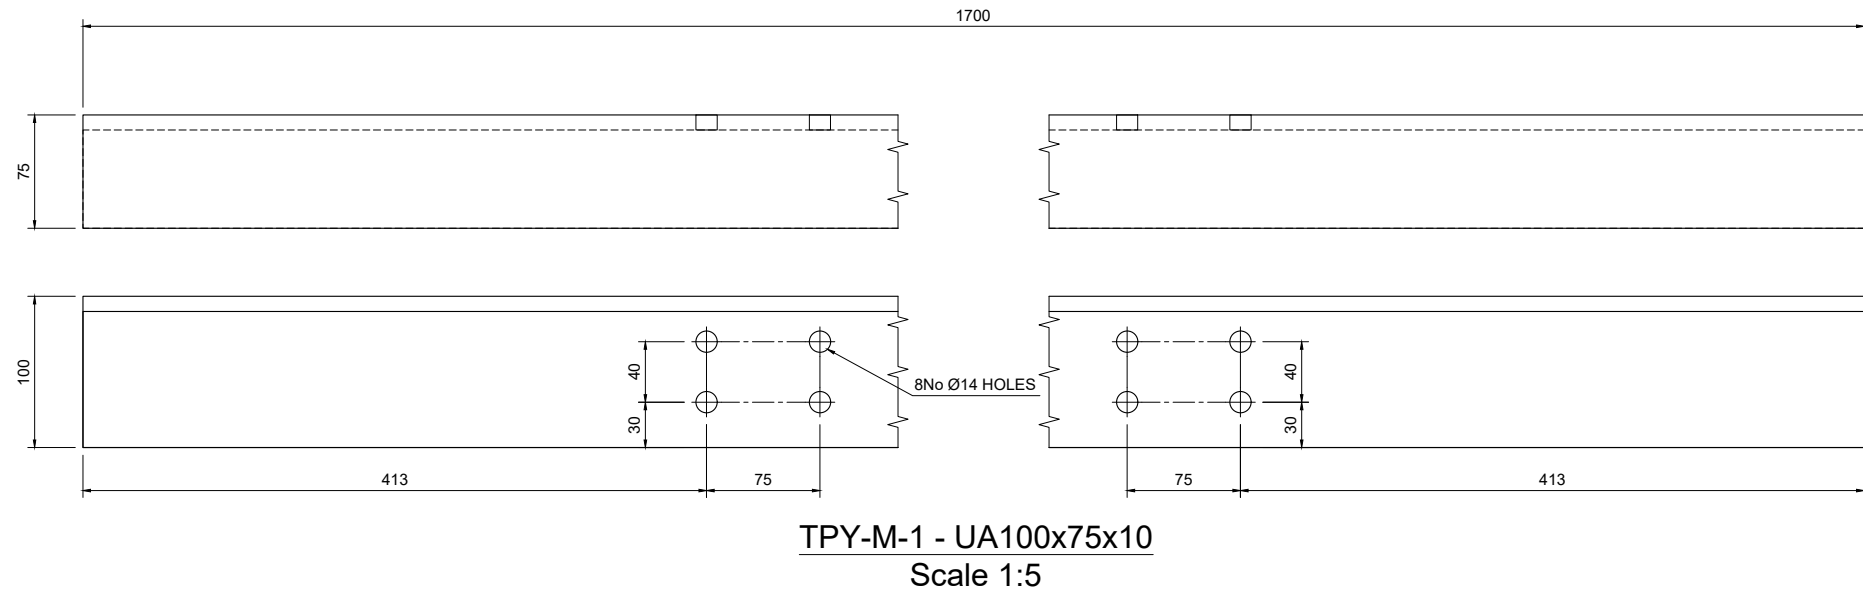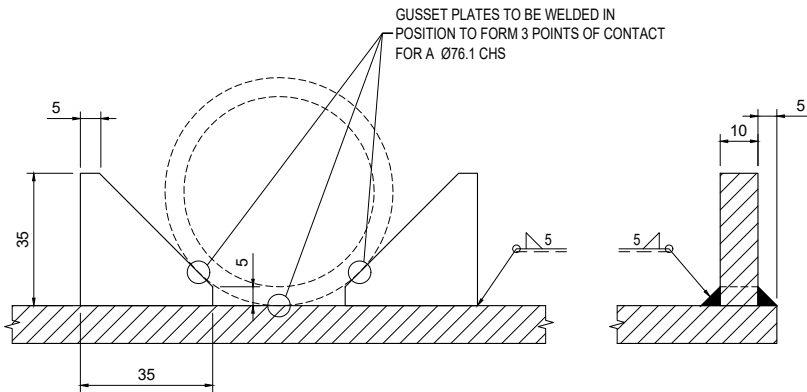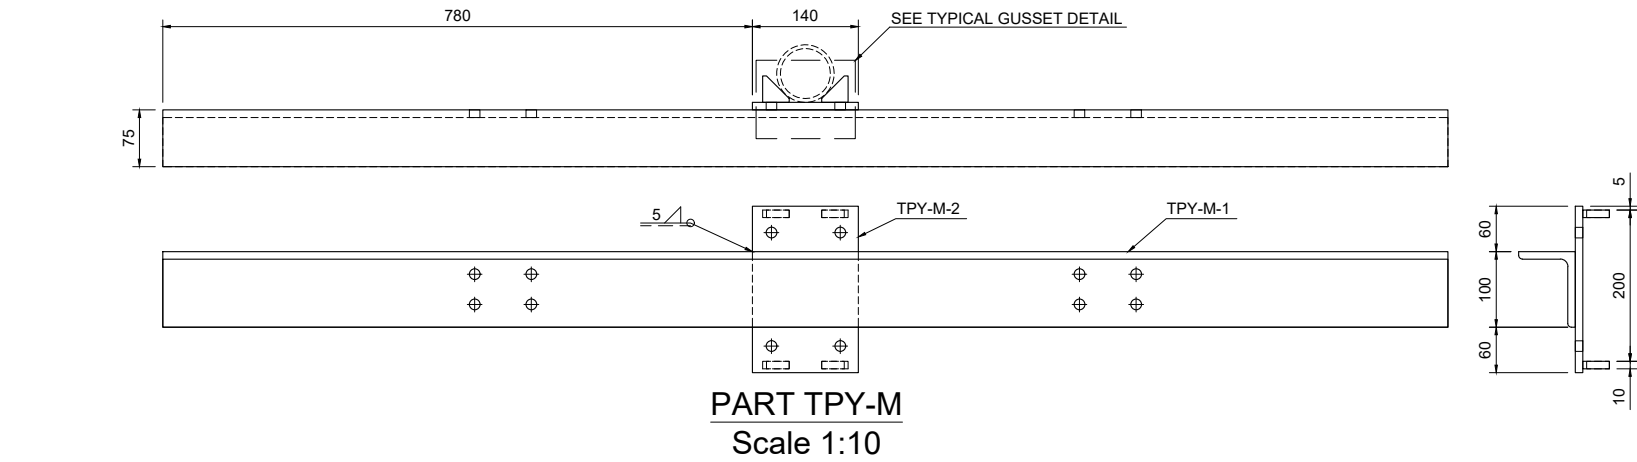


Parts list for TPY-M

Item	Part	Quantity	Part description	Length	Material	Weight
01	TPY-M-1	1	UA100x75x10	1700mm	S275J0	22.10 kg
02	TPY-M-2	1	PLATE 220x140x10mm C/W GUSSETS	N/A	S275J0	2.42 kg
03	TPY-M-C	2	PLATE 200x150x10mm	N/A	S275J0	2.36 kg
04	U-BOLT	4	M12 U-BOLT FOR CHS 40mm	N/A	GRADE 8.8	-
05	U-BOLT	2	M12 U-BOLT FOR CHS 60.3mm	N/A	GRADE 8.8	-
06	U-BOLT	2	M12 U-BOLT FOR CHS 76.1mm	N/A	GRADE 8.8	-
07	N-BOLT	4	M12 N-BOLT FOR UA100x75 (C/C 90mm)	N/A	GRADE 8.8	-
Total Weight:						29.24 kg

- All steel hot dip galvanized
- Each U-BOLT & N-BOLT to be supplied with 4 Full Nuts, 2 Flat Washers and 2 Spring Washers
- For fabrication notes see drawing 305

NOTE:

TPY-M COMPRISES OF ONE WELDED ASSEMBLY; 2No CROSS OVER PLATES (TPY-M-C) AND ALL ASSOCIATED FASTENERS

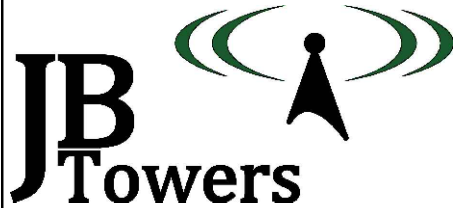

01	FIRST ISSUE							AM	23/07/19
REV	REV							BY	DATE
SCALE AS SHOWN WHEN PRINTED AT A3		DRAWN	AM	CHECKED	MP	APPROVED JBT			
		DATE	23/07/19	DATE	23/07/19	DATE 23/07/19			
ALL DIMENSIONS IN mm UNLESS OTHERWISE STATED. THIS DRAWING TO BE READ IN CONJUNCTION WITH OTHER RELEVANT DRAWINGS.									

TITLE
YAGI MOUNT ASSEMBLY
PART: TPY-M

SITE ADDRESS
GUISACHAN FARM
TOMICH
STRATHGLASS
HIGHLAND
IV4 7LF

ARQIVA REF.
141679


DRG No.
302

REV
01


ALL SCALES AS SHOWN WHEN PRINTED AT A3




ALL SCALES AS SHOWN WHEN PRINTED AT A3

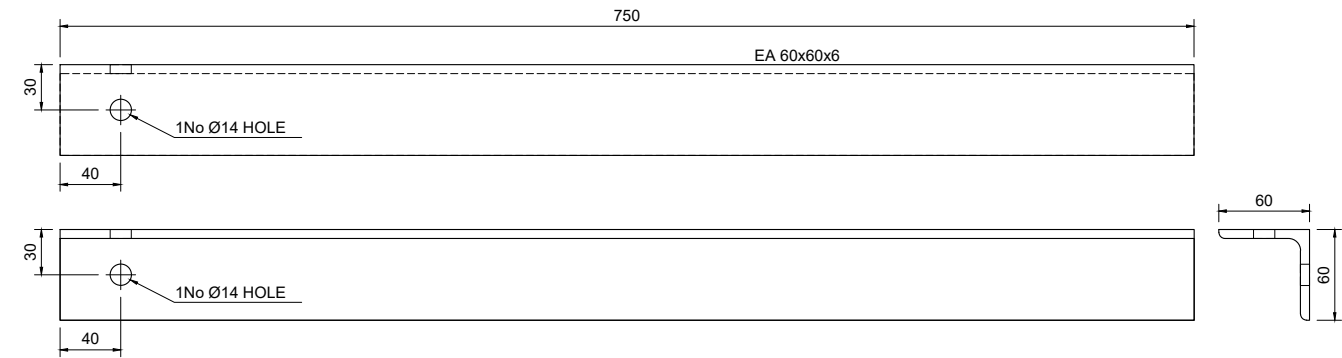


TPA-BR-1 - EA60x60x6
Scale 1:5

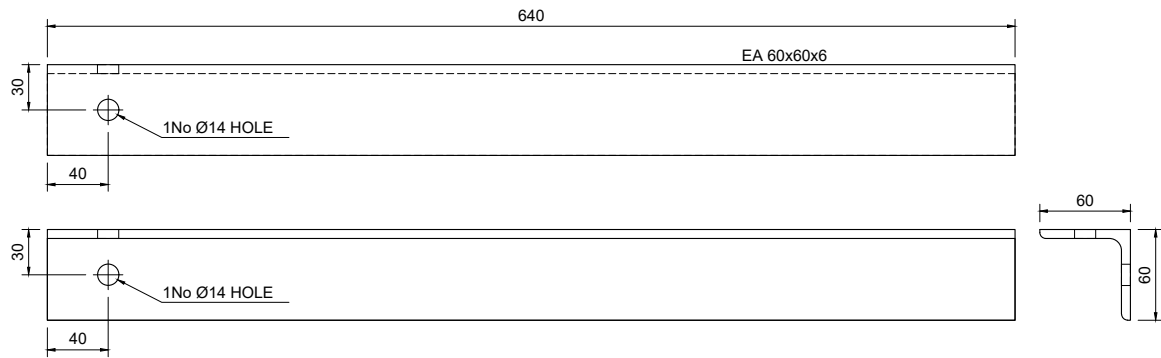


TPA-BR-2 - EA60x60x6
Scale 1:5

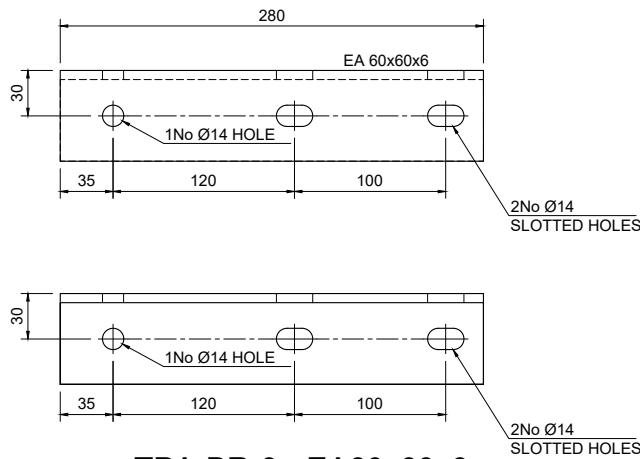

TPA-BR-3 - EA60x60x6
Scale 1:5

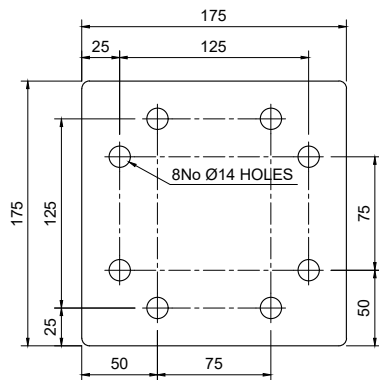

TPA-BR-4 - 10mm THICK
Scale 1:5

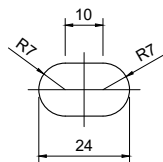

SLOTTED HOLE DETAIL
Scale 1:2

Parts list for TPA-BR-A


Item	Part	Quantity	Part description	Length	Material	Weight
01	TPB-BR-1	1	EA 60x60x6	750mm	S275J0	4.10 kg
02	TPB-BR-3	1	EA 60x60x6	280mm	S275J0	1.51 kg
03	TPB-BR-4	1	PLATE 175x175x10mm	N/A	S275J0	2.40 kg
04	BOLT	1	M12 SET BOLT - 40mm LONG	N/A	GRADE 8.8	-
05	N-BOLT	2	M12 N-BOLT FOR EA 60x60x6	N/A	GRADE 8.8	-
06	U-BOLT	2	M12 U-BOLT FOR CHS 60.3mm	N/A	GRADE 8.8	-
Total Weight:						8.01 kg

- All steel hot dip galvanized
- Each BOLT to be supplied with 1 Full Nut, 1 Form E FLat Washer and 1 Spring Washer
- Each U-BOLT to be supplied with 4 Full Nuts, 2 Flat Washers and 2 Spring Washers
- For fabrication notes see drawing 305

Parts list for TPA-BR-B

Item	Part	Quantity	Part description	Length	Material	Weight
01	TPB-BR-2	1	EA 60x60x6	640mm	S275J0	3.50 kg
02	TPB-BR-4	1	PLATE 175x175x10mm	N/A	S275J0	2.40 kg
03	BOLT	1	M12 SET BOLT - 40mm LONG	N/A	GRADE 8.8	-
04	N-BOLT	2	M12 N-BOLT FOR EA 60x60x6	N/A	GRADE 8.8	-
05	U-BOLT	2	M12 U-BOLT FOR CHS 60.3mm	N/A	GRADE 8.8	-
Total Weight:						5.90 kg

- All steel hot dip galvanized
- Each BOLT to be supplied with 1 Full Nut, 1 Form E FLat Washer and 1 Spring Washer
- Each U-BOLT to be supplied with 4 Full Nuts, 2 Flat Washers and 2 Spring Washers
- For fabrication notes see drawing 305

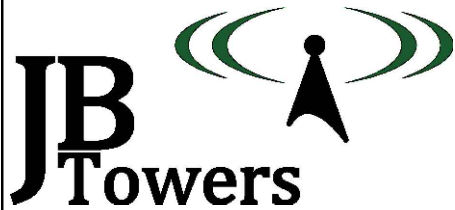

01	FIRST ISSUE	AM	23/07/19
REV	REV	BY	DATE
SCALE AS SHOWN WHEN PRINTED AT A3	DRAWN DATE 23/07/19	CHECKED DATE 23/07/19	APPROVED DATE 23/07/19
ALL DIMENSIONS IN mm UNLESS OTHERWISE STATED. THIS DRAWING TO BE READ IN CONJUNCTION WITH OTHER RELEVANT DRAWINGS.			

TITLE

BRACING ASSEMBLIES

PARTS: TPA-BR-A;
TPA-BR-B

SITE ADDRESS

GUISACHAN FARM
TOMICH
STRATHGLASS
HIGHLAND
IV4 7LF

ARQIVA REF.
141679


DRG No.
303

REV
01

ALL SCALES AS SHOWN WHEN PRINTED AT A3



ALL SCALES AS SHOWN WHEN PRINTED AT A3

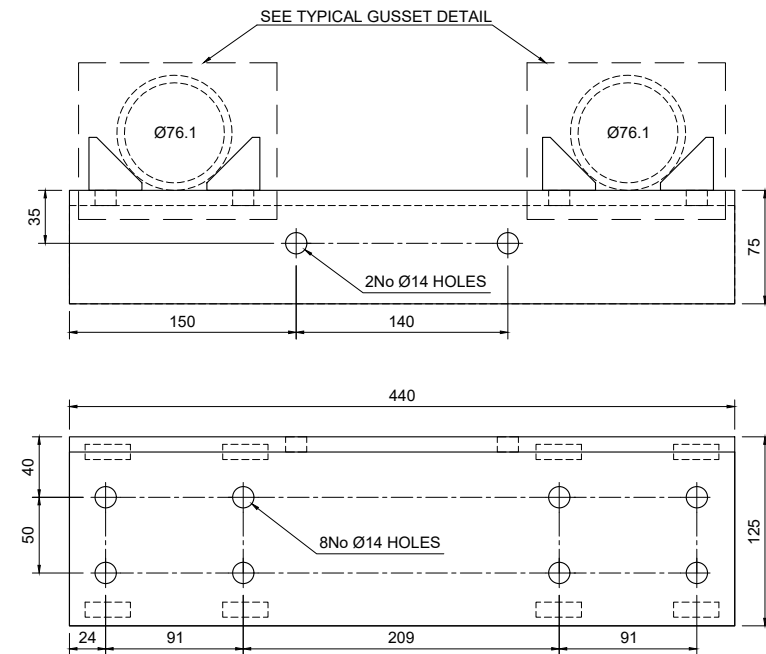


TPA-M - UA125x75x10
Scale 1:5


Parts list for TPA-M

Item	Part	Quantity	Part description	Length	Material	Weight
01	TPA-M	1	UA125x75x10 C/W GUSSETS	440mm	S275J0	6.60 kg
02	U-BOLT	4	M12 U-BOLT FOR CHS 76.1mm	N/A	GRADE 8.8	-
Total Weight:						6.60 kg


- All steel hot dip galvanized
- Each STUD & U-BOLT to be supplied with 4 Full Nuts, 2 Flat Washers and 2 Spring Washers
- Each BOLT to be supplied with 1 Full Nut, 1 Form E FLat Washer and 1 Spring Washer
- For fabrication notes see drawing 305

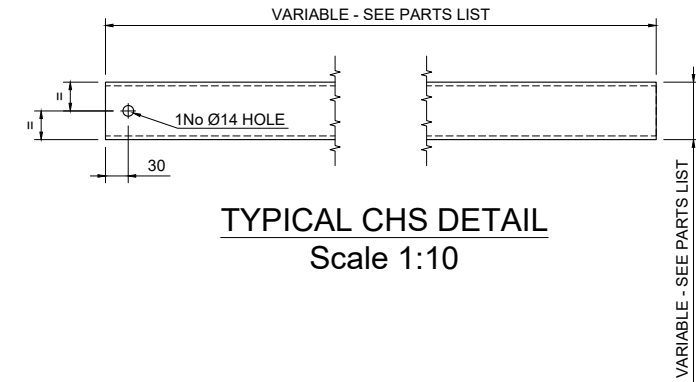

TYPICAL CHS DETAIL
Scale 1:10

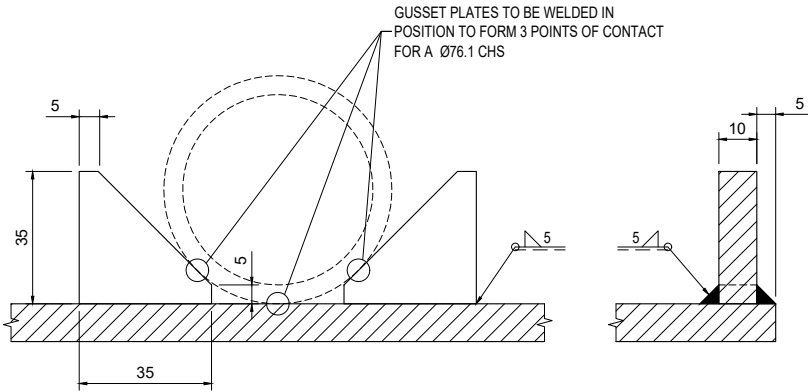

TYPICAL GUSSET PLATE DETAIL
Scale 1:2

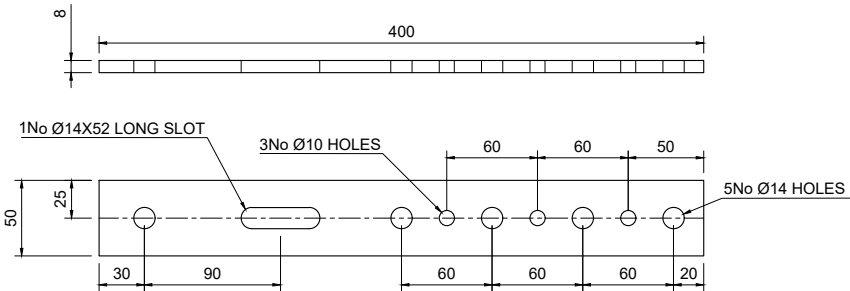


TPA-PD - 8mm THICK
Scale 1:5

Parts list for TPA-PD

Item	Part	Quantity	Part description	Length	Material	Weight
01	TPA-PD	1	Plate 400x50x8mm	N/A	S275J0	1.26 kg
02	U-BOLT	1	M12 U-BOLT FOR CHS 76.1mm	N/A	GRADE 8.8	-
Total Weight:						1.26 kg

- All steel hot dip galvanized
- Each U-BOLT to be supplied with 4 Full Nuts, 2 Flat Washers and 2 Spring Washers
- For fabrication notes see drawing 305

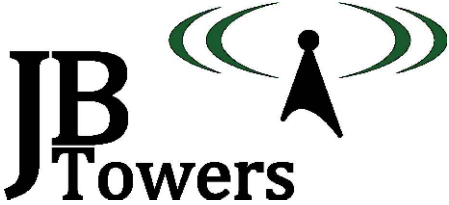

01	FIRST ISSUE					AM	23/07/19
REV	REV					BY	DATE
SCALE AS SHOWN WHEN PRINTED AT A3		DRAWN	AM	CHECKED	MP	APPROVED	JBT
		DATE	23/07/19	DATE	23/07/19	DATE	23/07/19
ALL DIMENSIONS IN mm UNLESS OTHERWISE STATED. THIS DRAWING TO BE READ IN CONJUNCTION WITH OTHER RELEVANT DRAWINGS.							

TITLE
VSAT DISH MOUNTING
BRACKET; PD STRAP; TYP
CHS DETAIL

PARTS: TPA-M; TPA-PD

SITE ADDRESS
GUISACHAN FARM
TOMICH
STRATHGLASS
HIGHLAND
IV4 7LF


ARQIVA REF.
141679
DRG No.
304
REV
01

Item	Part	Drawing	Quantity	Part description	Length	Material	Weight
01	01	200	1	3 MAN LATCHWAY SYSTEM & 4No. WIRE GUIDES FOR FACE MOUNTED MONOPOLE	17000	N/A	-
02	TPB-C	300	2	FALL ARREST AAMACHMENT POINT	N/A	S275J0	4.48 kg
03	03	200	9	PERMANENT BT STEP c/w 3No 10x75mm ZINC-PLATED COACH SCREWS	N/A	S275J0	2.70 kg
04	TPS-R	300	9	'MonoStep' ASSEMBLY	N/A	S275J0	25.65 kg
05	TPB-B	301	3	MOUNTING BRACKET	N/A	S275J0	33.99 kg
06	06	203	1	CHS 76.1x5mm	3000mm	S355J2H	26.31 kg
07	TPY-M	302	2	YAGI MOUNTING BRACKET	1700mm	S275J0	58.48 kg
08	TPA-M	304	2	VSAT DISH MOUNTING BRACKET	440mm	S275J0	13.20 kg
09	09	203	1	CHS 76.1x5mm	2200mm	S355J2H	19.29 kg
10	TPA-BR-A	303	2	BRACING ASSEMBLY - A	N/A	S275J0	10.08 kg
11	TPA-BR-B	303	1	BRACING ASSEMBLY - B	N/A	S355J2H	5.90 kg
12	12	203	1	CHS 60.3x5mm	2200mm	S275J0	15.00 kg
13	TPA-PD	305	2	POWER DIVIDER STRAP	400mm	S275J0	1.26 kg
14	14	200	1	FEEDER COVER - 2/CG/100	3500mm	UV RESISTANT PLASTIC	-
15	15	200	6	FEEDER CLAMP - 2/FCD/028	N/A	POLYPROPYLENE	-
16	16	200	6	M10 SCREW DOWELS WTH M10 NUT	100mm	STAINLESS STEEL	-
17	17	200	1	PoleSaver	750mm	N/A	-
18	18	200	4	M12 STUD + 4No NUTS + 2No FLAT WASHERS + 1No Ø50mm WASHER (FOR FALL ARREST SYSTEM)	500mm	GRADE 8.8	1.78 kg
19	19	203	24	M12 WASHER	N/A	GRADE 8.8	-
Total Weight:							218.12 kg

- All steel hot dip galvanized
- All U-BOLTS to be FLA supply, each Supplied with 4 Full Nuts, 2 Flat Washers and 2 Spring Washers

NOTES:

1. WELDING TO BE IN ACCORDANCE WITH BS EN 1011-1:2009
2. LINEAR DIMS TO BE WITHIN ±1mm;
3. ANGULAR TOLERANCES TO BE WITHIN 0.5°
4. WELDING SYMBOLS ARE IN ACCORDANCE WITH BS EN 22553:1995
5. ALL PROFILE EDGES TO BE DRESSED AND SHARP CORNERS REMOVED
6. ALL WELD SIZES ARE FINAL SIZES
7. ALL WELDED JOINTS ARE TO BE PICKLE TIGHT
8. ALL STEELWORK TO BE BS EN 10025 GRADE S275 J0 UNO
9. HOT DIPPED GALVANISED TO BS EN ISO 1461. (ALL HOLLOW SECTIONS TO BE GRADE S355 J0H)
10. ALL STEEL IS TO BE SUPPLIED IN ACCORDANCE WITH EN 1090 TO EXECUTION CLASS 2
11. ALL NON PRE-LOADED BOLTS TO BE COMPLIANT STRUCTURAL BOLTS TO BS EN ISO 15048 PARTS 1&2.
12. STEELWORK COMPONENTS SHALL BE HOT DIP GALVANISED TO ACHIEVE A "VERY HIGH" DURABILITY FOR AN ENVIRONMENT CATEGORY CODE C4 FROM TABLE 1 IN BS EN ISO 14713
13. BOLTS AND NUTS SHALL BE SUPPLIED IN ACCORDANCE WITH BS 7371, SPUN GALVANISED IN ACCORDANCE WITH ISO 10684, THE NUTS RE-TAPPED AFTER GALVANISING, AND THE THREADS TREATED WITH GREASE.
14. ALL BOLTS TO BE CUT ON SITE TO EXTEND MAX 10mm BEYOND THE NUT WHEN TIGHTENED UNO.
15. ALL SITE DRILLED HOLE/CUT ENDS TO BE TREATED WITH METAFLUX 70-40 ZINC PASTE FOLLOWED BY 1 COAT OF 7-42 ZINC ALU OR 70-16 ALUMINIUM SPRAY

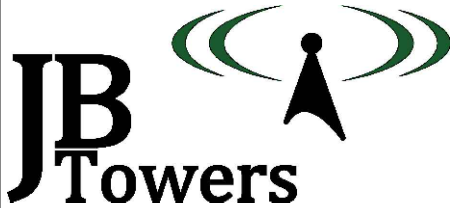

01	FIRST ISSUE			AM	23/07/19
REV	REV			BY	DATE
SCALE AS SHOWN WHEN PRINTED AT A3		DRAWN DATE	AM 23/07/19	CHECKED DATE	MP 23/07/19
				APPROVED DATE	JBT 23/07/19
ALL DIMENSIONS IN mm UNLESS OTHERWISE STATED. THIS DRAWING TO BE READ IN CONJUNCTION WITH OTHER RELEVANT DRAWINGS.					


TITLE
PARTS LIST

SITE ADDRESS		
GUISACHAN FARM TOMICH STRATHGLASS HIGHLAND IV4 7LF		
ARQIVA REF. 141679	DRG No. 305	REV 01


ALL SCALES AS SHOWN WHEN PRINTED AT A3



ALL SCALES AS SHOWN WHEN PRINTED AT A3

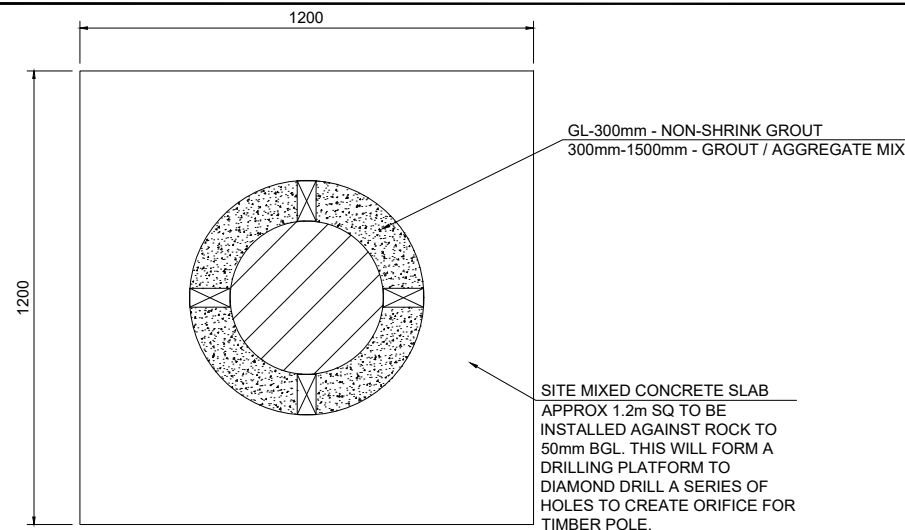

POROPOSED INSTALLATION
PLAN VIEW
Scale 1:20

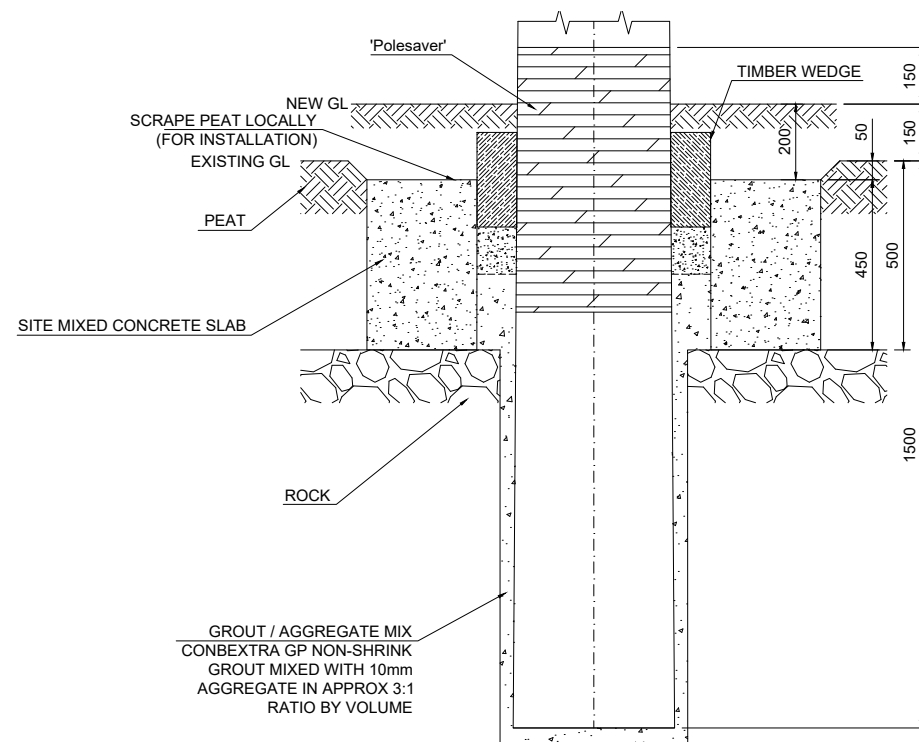


POROPOSED INSTALLATION
ELEVATION
Scale 1:20


TIMBER POLE INSTALLATION:

1. REFER TO DRG 200 FOR TIMBER POLE ORIENTATION.
2. APPROX 1.2m SQ SITE MIXED CONCRETE SLAB TO BE INSTALLED AGAINST ROCK TO 50mm BGL. TO FORM A DRILLING PLATFORM TO DIAMOND DRILL A SERIES OF HOLES TO CREATE ORIFICE FOR TIMBER POLE.
3. POLE TO BE WRAPPED IN 'POLESAVER' AND INSTALLED AND LEVELED IN OPENING. TIMBERS TO BE USED TO HOLD POLE IN POSITION.
4. ANNULUS SHALL BE FILLED WITH GROUT / AGGREGATE MIX TO 300mm BELOW GL
5. TOP 300mm SHALL BE FILLED WITH NON-SHRINK GROUT. A 1:60 FALL SHALL BE FORMED AROUND TIMBER POLE TO ALLOW WATER TO DRAIN AWAY FROM POLE
6. GROUT TO EXTEND APPROX 75MM ABOVE TOP OF CONCRETE
7. ONCE GROUT HAS CURED REMOVE TIMBER WEDGES AND FILL REMAINING VOIDS WITH NON-SHRINK GROUT
8. BACKFILL TOP OF CONCRETE SLAB WITH 200mm OF SOIL


BACKFILL 200mm OVER CONCRETE SLAB

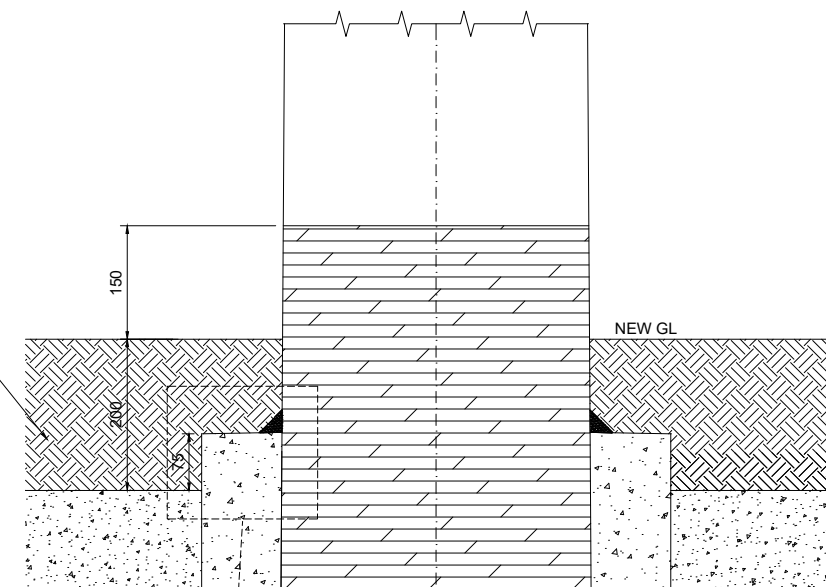

WATER PROOFING
Scale 1:10

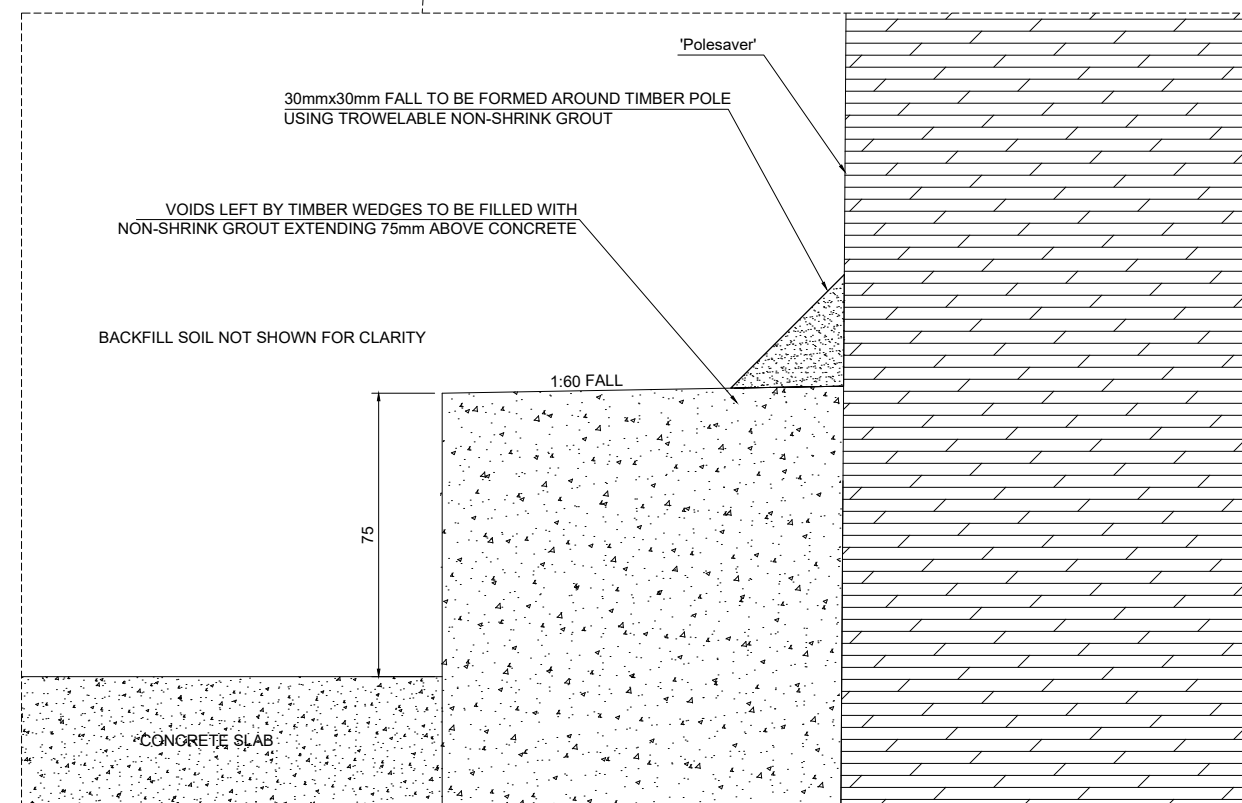

ENLARGED DETAIL
Scale 1:2

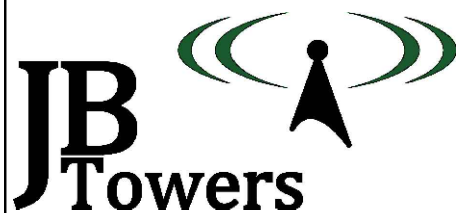

01	FIRST ISSUE	AM	23/07/19
REV	REV	BY	DATE
SCALE AS SHOWN WHEN PRINTED AT A3	DRAWN AM	CHECKED MP	APPROVED JBT
DATE 23/07/19	DATE 23/07/19	DATE 23/07/19	DATE 23/07/19
ALL DIMENSIONS IN mm UNLESS OTHERWISE STATED. THIS DRAWING TO BE READ IN CONJUNCTION WITH OTHER RELEVANT DRAWINGS.			

TITLE		SITE ADDRESS	
FOUNDATION DETAILS		GUISACHAN FARM TOMICH STRATHGLASS HIGHLAND IV4 7LF	
ARQIVA REF. 141679		DRG No. 400	REV 01

ALL SCALES AS SHOWN WHEN PRINTED AT A3