
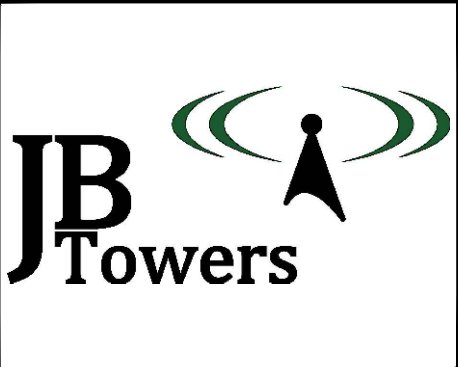
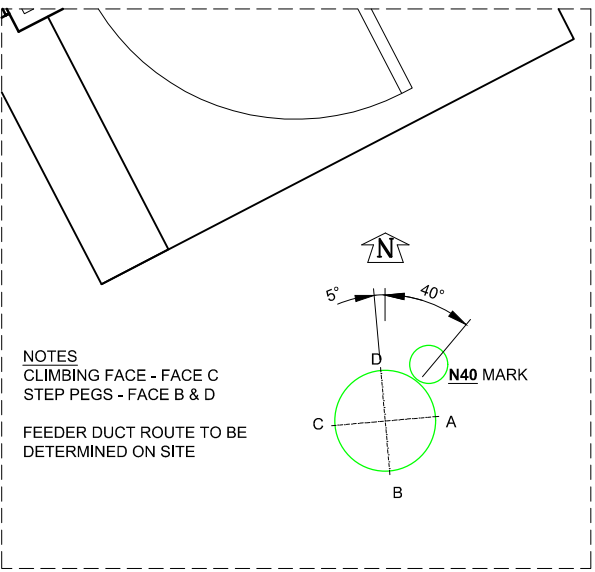


DRAWING ISSUE SHEET

[illegible]

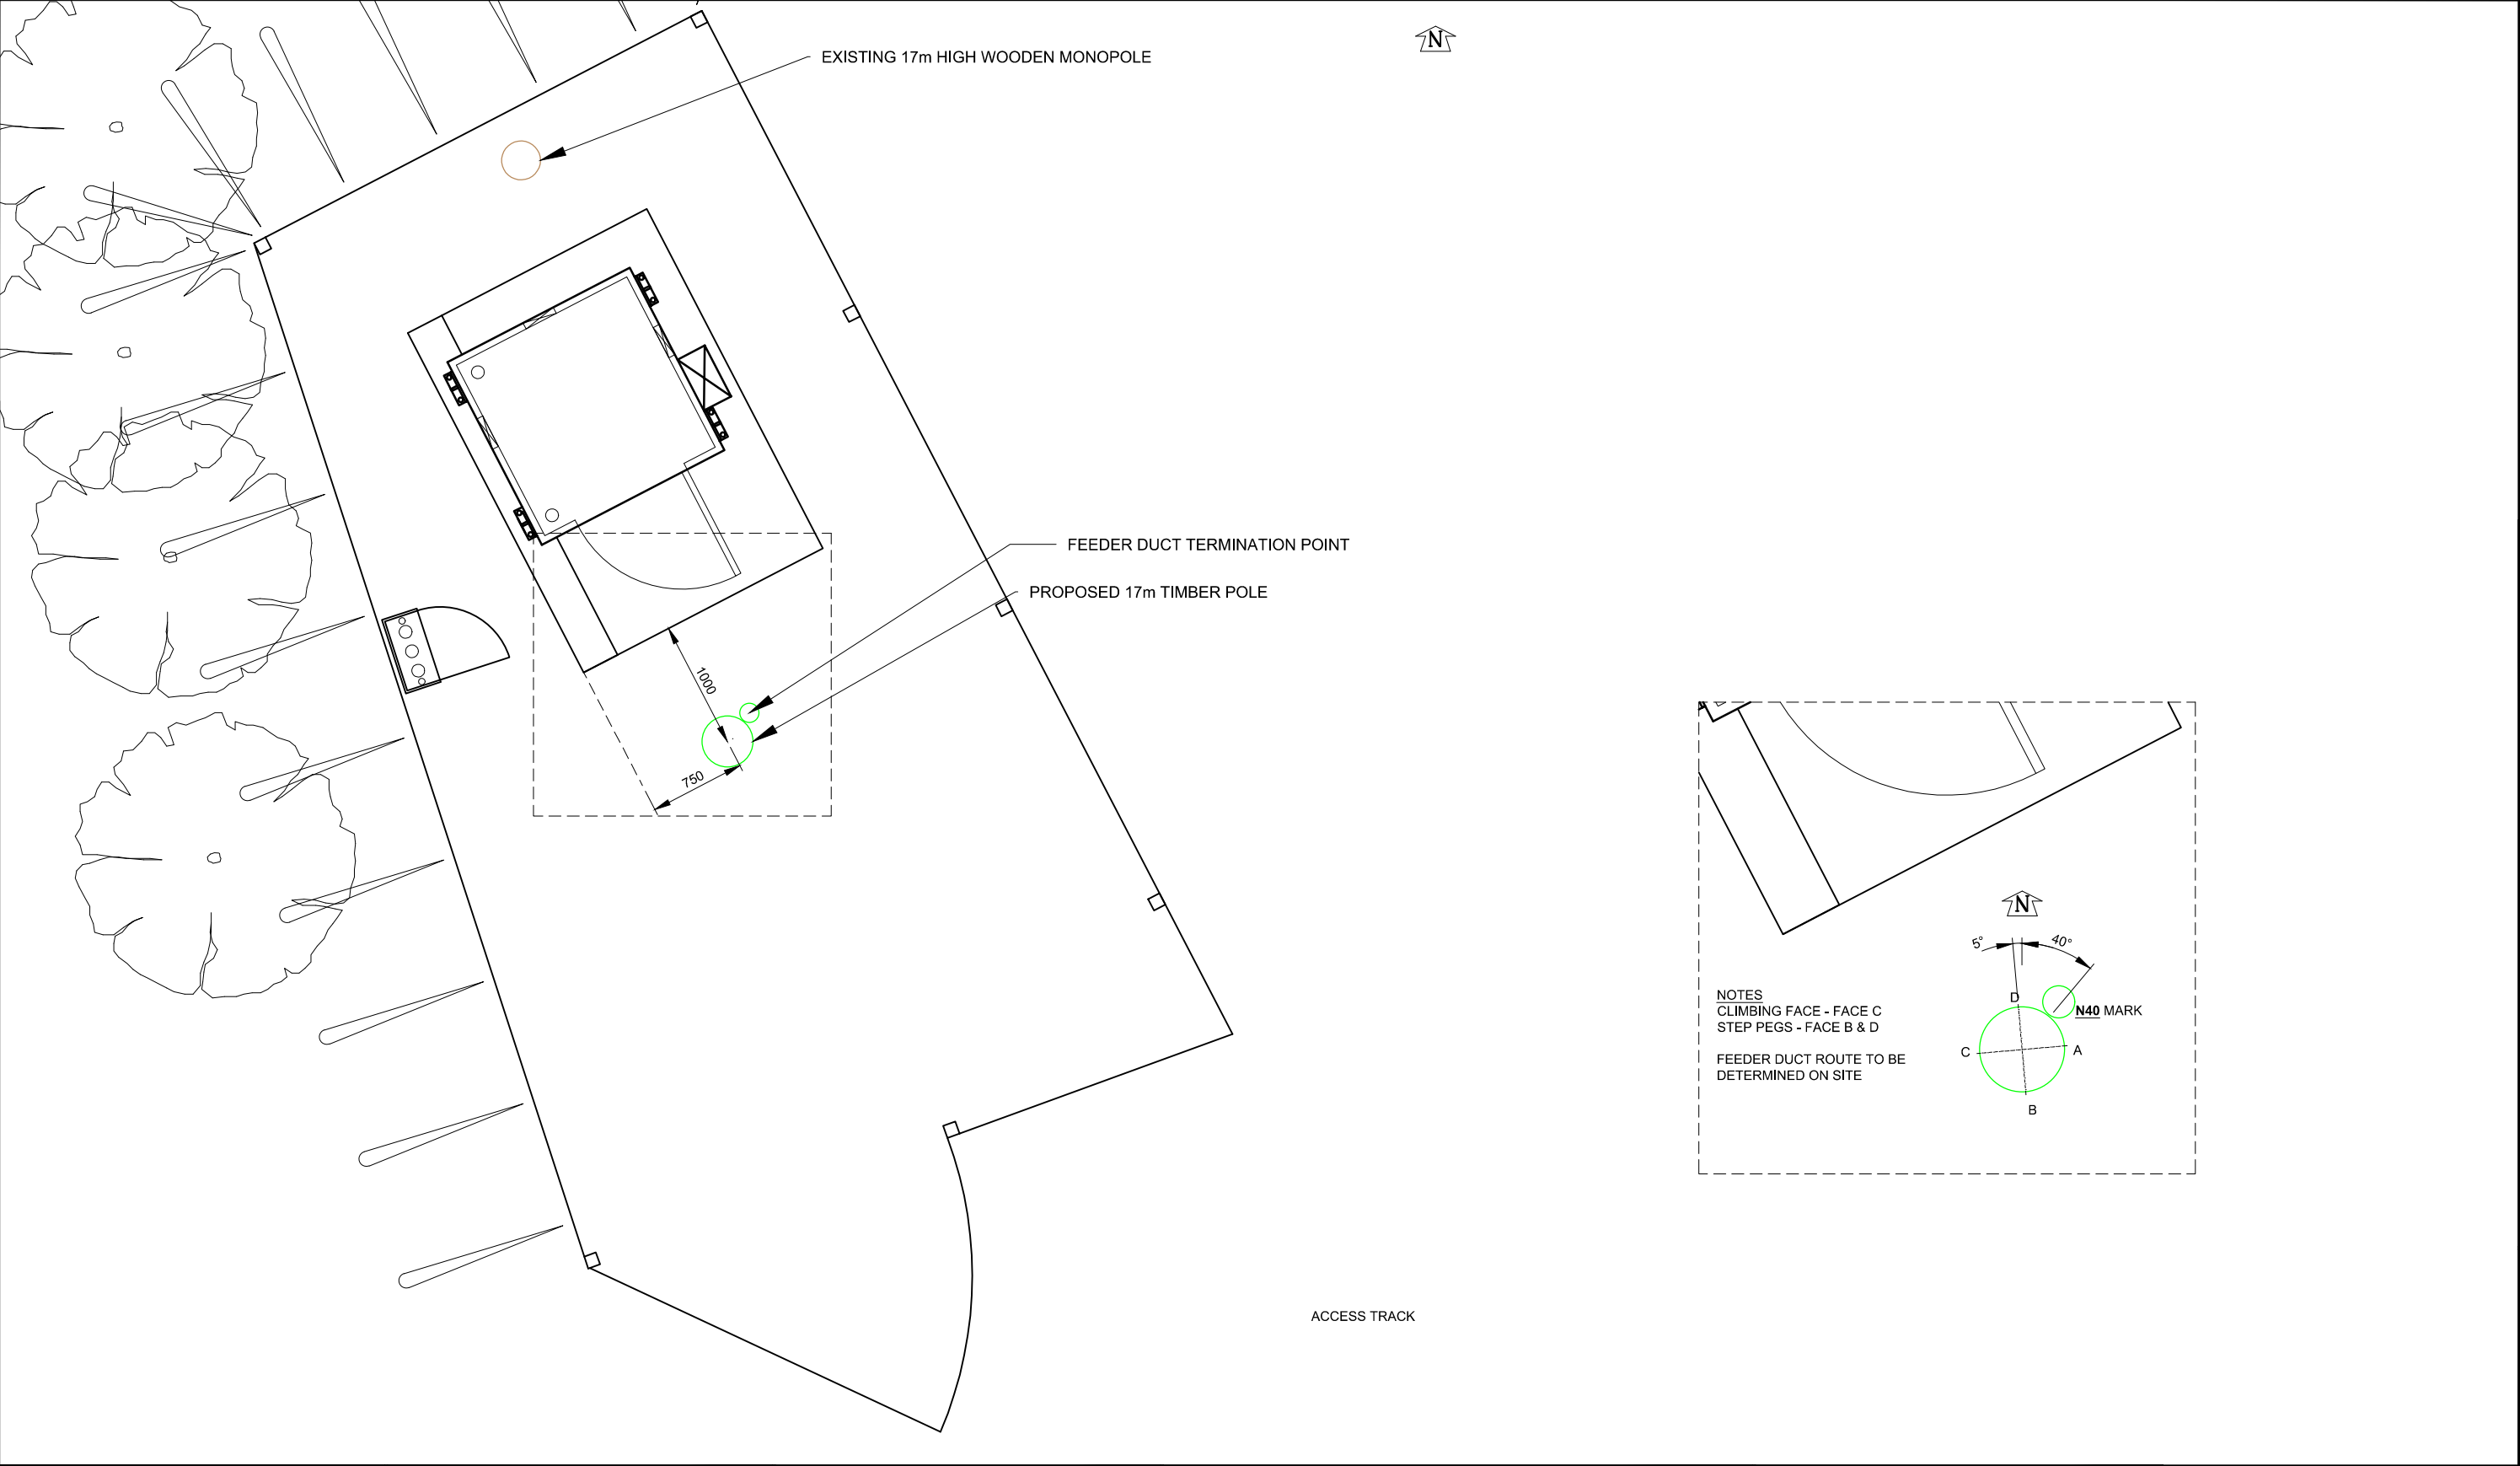

01	FIRST ISSUE				AM	23/04/20
REV	REV				BY	DATE
SCALE AS SHOWN		DRAWN	AM	CHECKED	MP	APPROVED JBT
WHEN PRINTED AT A3		DATE	23/04/20	DATE	23/04/20	DATE 23/04/20
ALL DIMENSIONS IN mm UNLESS OTHERWISE STATED. THIS DRAWING TO BE READ IN CONJUNCTION WITH OTHER RELEVANT DRAWINGS.						


TITLE

WALL

SITE PLAN

SITE ADDRESS THISTLE RIGGS FARM HOMER'S LANE WARDEN, HEXHAM NORTHUMBERLAND NE46 4SR		
ARQIVA REF. 141756	DRG No. 100	REV 01



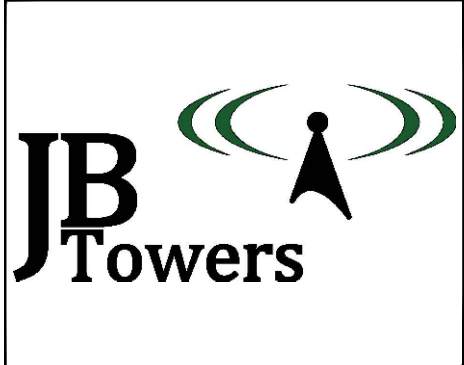

01	FIRST ISSUE			AM	23/04/20
REV	REV			BY	DATE
SCALE AS SHOWN WHEN PRINTED AT A3	DRAWN	AM	CHECKED	MP	APPROVED JBT
	DATE	23/04/20	DATE	23/04/20	DATE 23/04/20
ALL DIMENSIONS IN mm UNLESS OTHERWISE STATED. THIS DRAWING TO BE READ IN CONJUNCTION WITH OTHER RELEVANT DRAWINGS.					

TITLE

WALL

GENERAL ARRANGEMENT
SHEET 1 OF 3

SITE ADDRESS


THISTLE RIGGS FARM
HOMER'S LANE
WARDEN, HEXHAM
NORTHUMBERLAND
NE46 4SR

ARQIVA REF. 141756	DRG No. 200	REV 01
-----------------------	----------------	-----------

SITE ADDRESS

THISTLE RIGGS FARM
HOMER'S LANE
WARDEN, HEXHAM
NORTHUMBERLAND
NE46 4SR

ARQIVA REF. 141756	DRG No. 200	REV 01
-----------------------	----------------	-----------

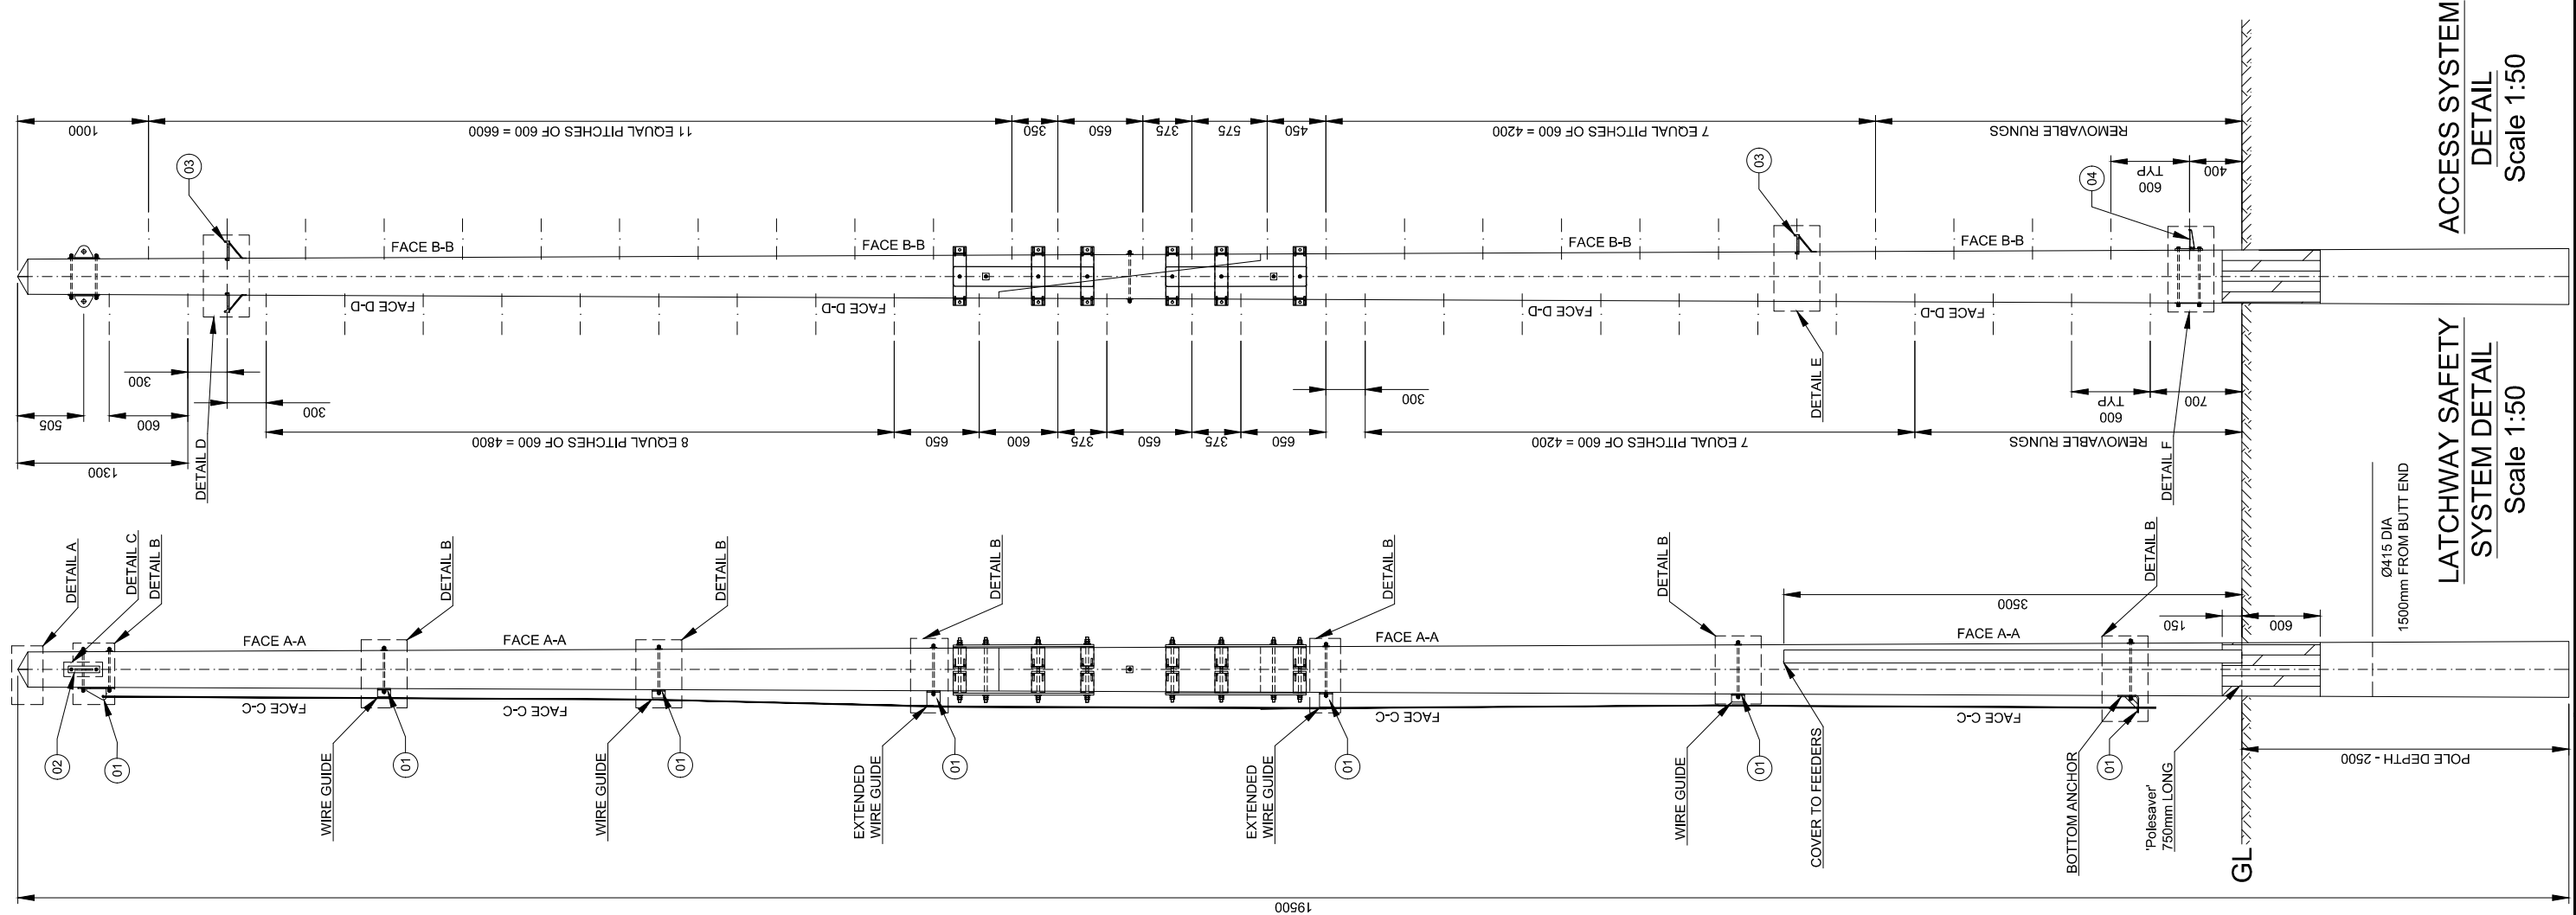

NOTES

1. SEE DRAWING 305 FOR PARTS LIST
2. ALL BOLTS TO BE CUT ON SITE TO EXTEND MAX 10mm BEYOND THE NUT WHEN TIGHTENED UNO.
3. ALL SITE DRILLED HOLE/CUT ENDS TO BE TREATED WITH METAFLOX 70-40 ZINC PASTE FOLLOWED BY 1 COAT OF 7-42 ZINC ALU OR 70-16 ALUMINIUM SPRAY

TIMBER POLE

1. POLE TO BE SUPPLIED IN ACCORDANCE WITH BS EN14229 & SHALL HAVE MIN. CHARACTERISTIC STRENGTH OF 30N/mm² & MIN. YOUNGS MODULUS (PARALLEL TO GRAIN) OF 10KN/mm².
2. MARKINGS ON FINISHED POLE SHALL BE AT 4m FROM BUTT AND COMPLY WITH BS EN 14229 UNO
3. AS FAR AS PRACTICABLE ALL CUTTING, SCARPING & DRILLING TO BE DONE BEFORE CREOSOTING. IF NOT ALL CUT, DRILLED & SCARFED SURFACES TO BE COATED WITH A MIXTURE OF CREOSOTE & TAR.
4. POLE TO BE PRESSURE IMPREGNATED WITH CREOSOTE IN ACCORDANCE WITH BS EN 14229
5. MINIMUM DIAMETERS
TOP - Ø2305mm
BOTTOM - Ø430mm
6. 19.5m LONG POLE TO BE SOURCED BY TRIMMING 20m LONG POLE BY 0.5m AT THE TOP

SPLICE CONNECTION


1. THE CONTACT SURFACES AND ALL THROUGH HOLES OF THE TIMBER POLE SPLICE ARE TO BE TREATED LIBERALLY WITH SINGLE COAT OF TIMBER COMPATIBLE BITUMINOUS PAINT (E.G. BIRD BRAND BLACK BITUMINOUS PAINT OR SIMILAR APPROVED PRODUCT).
2. PAINT TO BE APPLIED JUST BEFORE SPLICING THE TWO PARTS
3. ANY DISTURBED SURFACES SHALL HAVE THEIR WATERPROOFING REPAIRED WITH SINGLE COAT OF TIMBER COMPATIBLE BITUMINOUS PAINT (E.G. BIRD BRAND BLACK BITUMINOUS PAINT OR SIMILAR APPROVED PRODUCT).

PLANTING

1. CAT SCANNER IS TO BE USED IN ORDER TO CONFIRM THE POSITIONS OF BURIED SERVICES.
2. TIMBER POLE TO BE PLANTED WITH **N40** MARKING AT 3.5m FROM BUT FACING 40° FROM NORTH (CLOCKWISE)
3. SEE DRAWING 400 FOR FOUNDATION DETAILS

ALL SCALES AS SHOWN WHEN PRINTED AT A3

ALL SCALES AS SHOWN WHEN PRINTED AT A3

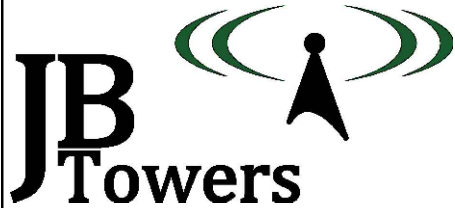

01	FIRST ISSUE			AM	23/04/20
REV	REV			BY	DATE
SCALE AS SHOWN		DRAWN	AM	CHECKED	MP
WHEN PRINTED AT A3		DATE	23/04/20	DATE	23/04/20
		APPROVED	JBT	DATE	23/04/20
ALL DIMENSIONS IN mm UNLESS OTHERWISE STATED. THIS DRAWING TO BE READ IN CONJUNCTION WITH OTHER RELEVANT DRAWINGS.					

TITLE

WALL

GENERAL ARRANGEMENT

SHEET 2 OF 3

SITE ADDRESS

THISTLE RIGGS FARM

HOMER'S LANE

WARDEN, HEXHAM

NORTHUMBERLAND

NE46 4SR

ARQIVA REF.




141756

DRG No.

200

REV

01

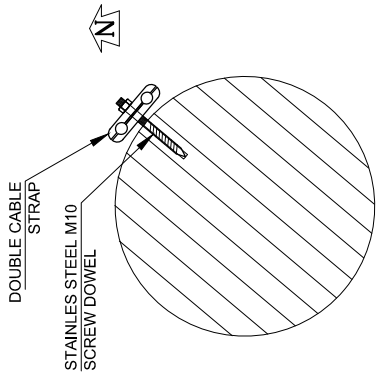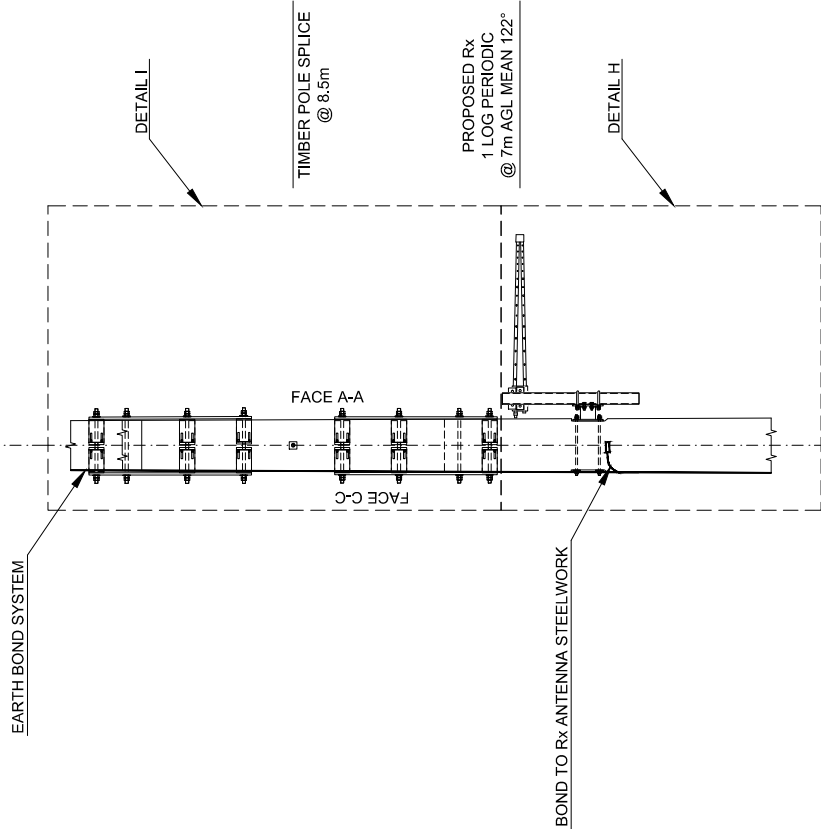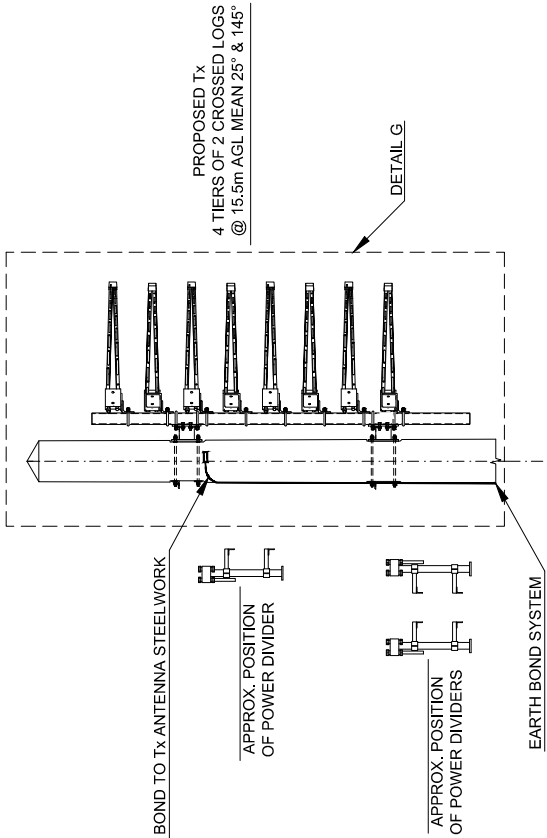

FEEDER
MANAGEMENT


Scale 1:10

NOTES

1. AS FAR AS IS PRACTICABLE ALL CUTTING SCARFING AND DRILLING TO BE DONE BEFORE CREOSOTING. WHERE THIS IS NOT POSSIBLE ALL CUT, DRILLED, AND SCARFED SURFACES TO BE COATED WITH A MIXTURE OF CREOSOTE AND TAR
- FEEDERS**
1. SUPPLY OF FEEDERS BY OTHERS LCF7/8-50 TO Tx ANTENNA & LCF12-50 TO Rx ANTENNA
2. FEEDERS FIXED AT 1000mm CENTRES
- EARTHING**
1. CONNECT EARTH BOND TO NEW EARTHING SYSTEM
2. MAXIMUM VALUE FOR GROUND RESISTANCE TO BE 10 OHMS
3. CABLE OR TAPE TO BE FIXED TO POLE AT 1000mm CENTRES
4. EARTHING SHOULD COMPLY WITH ARQIVA'S DOCUMENT BOS147


ANTENNA AND EARTHING
ARRANGEMENT

Scale 1:50

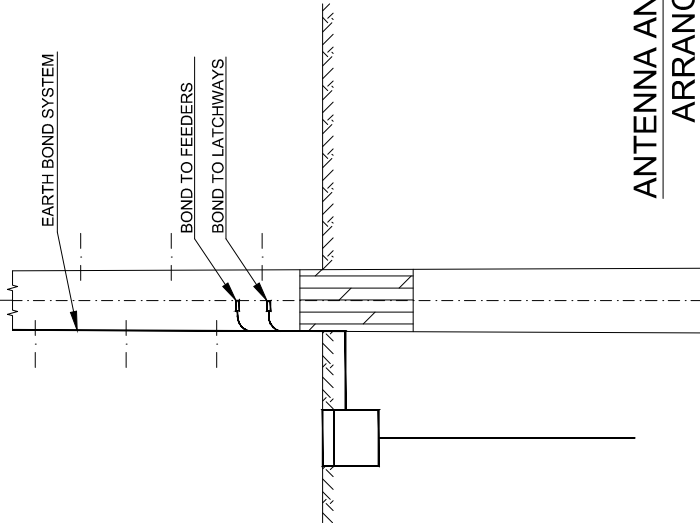


ALL SCALES AS SHOWN WHEN PRINTED AT A3

ALL SCALES AS SHOWN WHEN PRINTED AT A3

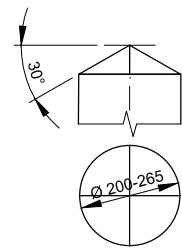


- NOTES:
1. A SINGLE COAT OF TIMBER COMPATIBLE BITUMINOUS PAINT (E.G. BIRD BRAND BLACK BITUMINOUS PAINT OR SIMILAR APPROVED PRODUCT) TO BE APPLIED TO THE UPPER SURFACES AT THE TOP OF THE POLE.
 2. PAINT TO BE APPLIED ON SITE JUST BEFORE ERECTION
- FORM: 4 WAY PYRAMID / CONE


DETAIL A - TIMBER POLE TOP
Scale 1:20

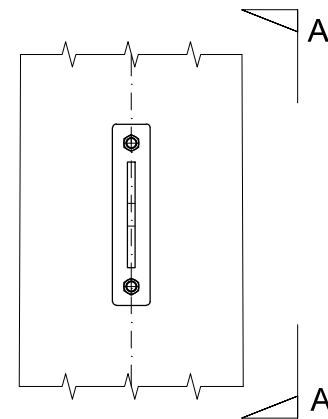


DETAIL C - FALL ARREST
ATTACHMENT POINT
Scale 1:10

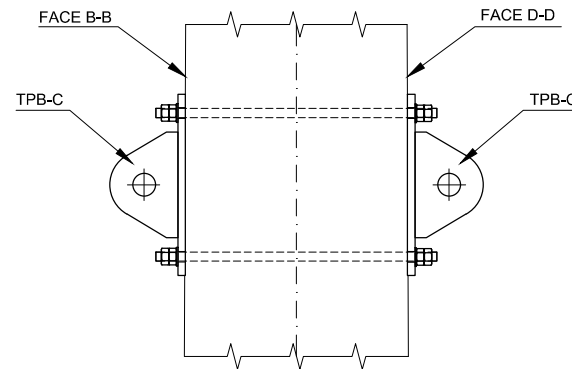


VIEW A-A
Scale 1:10

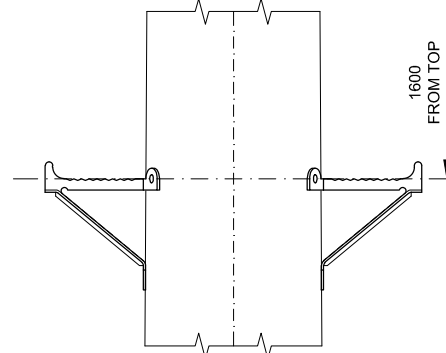

DETAIL D - ANTENNA
ACCESS CLIMBING STEP
Scale 1:10

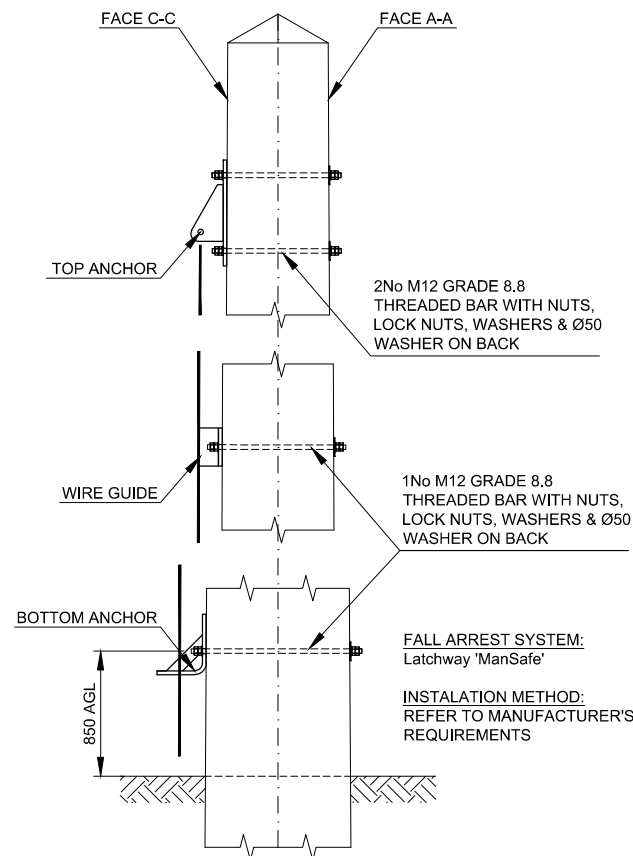


DETAIL B - FALL ARREST SYSTEM
Scale 1:20

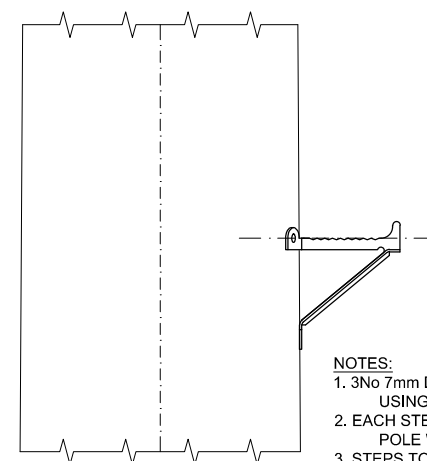


DETAIL E - PERMANENT
CLIMBING STEPS
Scale 1:10

- NOTES:
1. 3No 7mm DIA 70mm LONG PILOT HOLES TO BE DRILLED USING THE STEP AS A TEMPLATE
 2. EACH STEP SHOULD BE FIXED TO THE TIMBER POLE WITH 3No 10mm COACH SCREWS 75mm LONG
 3. STEPS TO BE INSTALLED ON FACES B-B & D-D ONLY

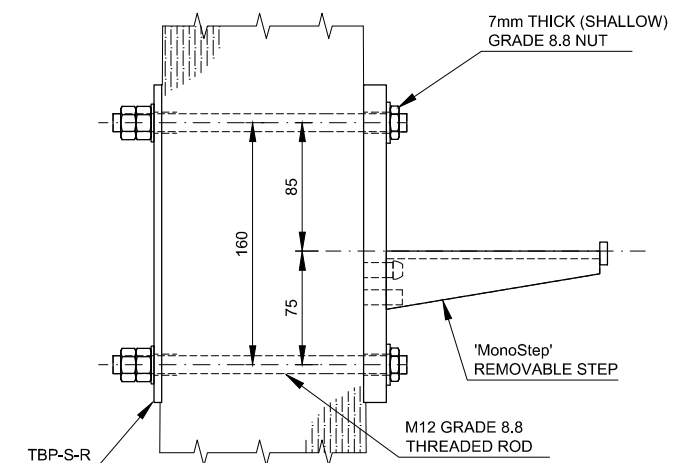

DETAIL F - REMOVABLE
CLIMBING STEPS
Scale 1:5

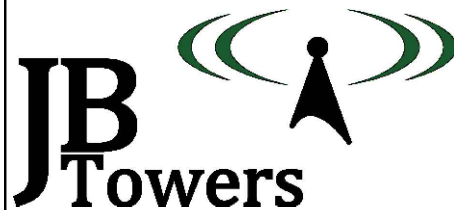

01	FIRST ISSUE			AM	23/04/20
REV	REV			BY	DATE
SCALE AS SHOWN WHEN PRINTED AT A3		DRAWN	AM	CHECKED	MP
		DATE	23/04/20	DATE	23/04/20
		DATE	23/04/20	DATE	23/04/20
ALL DIMENSIONS IN mm UNLESS OTHERWISE STATED. THIS DRAWING TO BE READ IN CONJUNCTION WITH OTHER RELEVANT DRAWINGS.					

TITLE
WALL
GENERAL ARRANGEMENT
SHEET 3 OF 3


SITE ADDRESS
THISTLE RIGGS FARM
HOMER'S LANE
WARDEN, HEXHAM
NORTHUMBERLAND
NE46 4SR

ARQIVA REF.
141756
DRG No.
200
REV
01

ALL SCALES AS SHOWN WHEN PRINTED AT A3



ALL SCALES AS SHOWN WHEN PRINTED AT A3

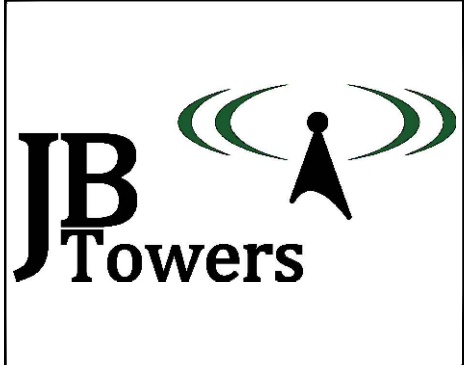

01	FIRST ISSUE							AM	23/04/20
REV	REV							BY	DATE
SCALE AS SHOWN WHEN PRINTED AT A3		DRAWN AM		CHECKED MP		APPROVED JBT			
		DATE 23/04/20		DATE 23/04/20		DATE 23/04/20			
ALL DIMENSIONS IN mm UNLESS OTHERWISE STATED. THIS DRAWING TO BE READ IN CONJUNCTION WITH OTHER RELEVANT DRAWINGS.									

TITLE

WALL


TIMBER POLE HOLE SET OUT

SHEET 1 OF 2

SITE ADDRESS


THISTLE RIGGS FARM
HOMER'S LANE
WARDEN, HEXHAM
NORTHUMBERLAND
NE46 4SR

ARQIVA REF. 141756	DRG No. 201
-----------------------	----------------

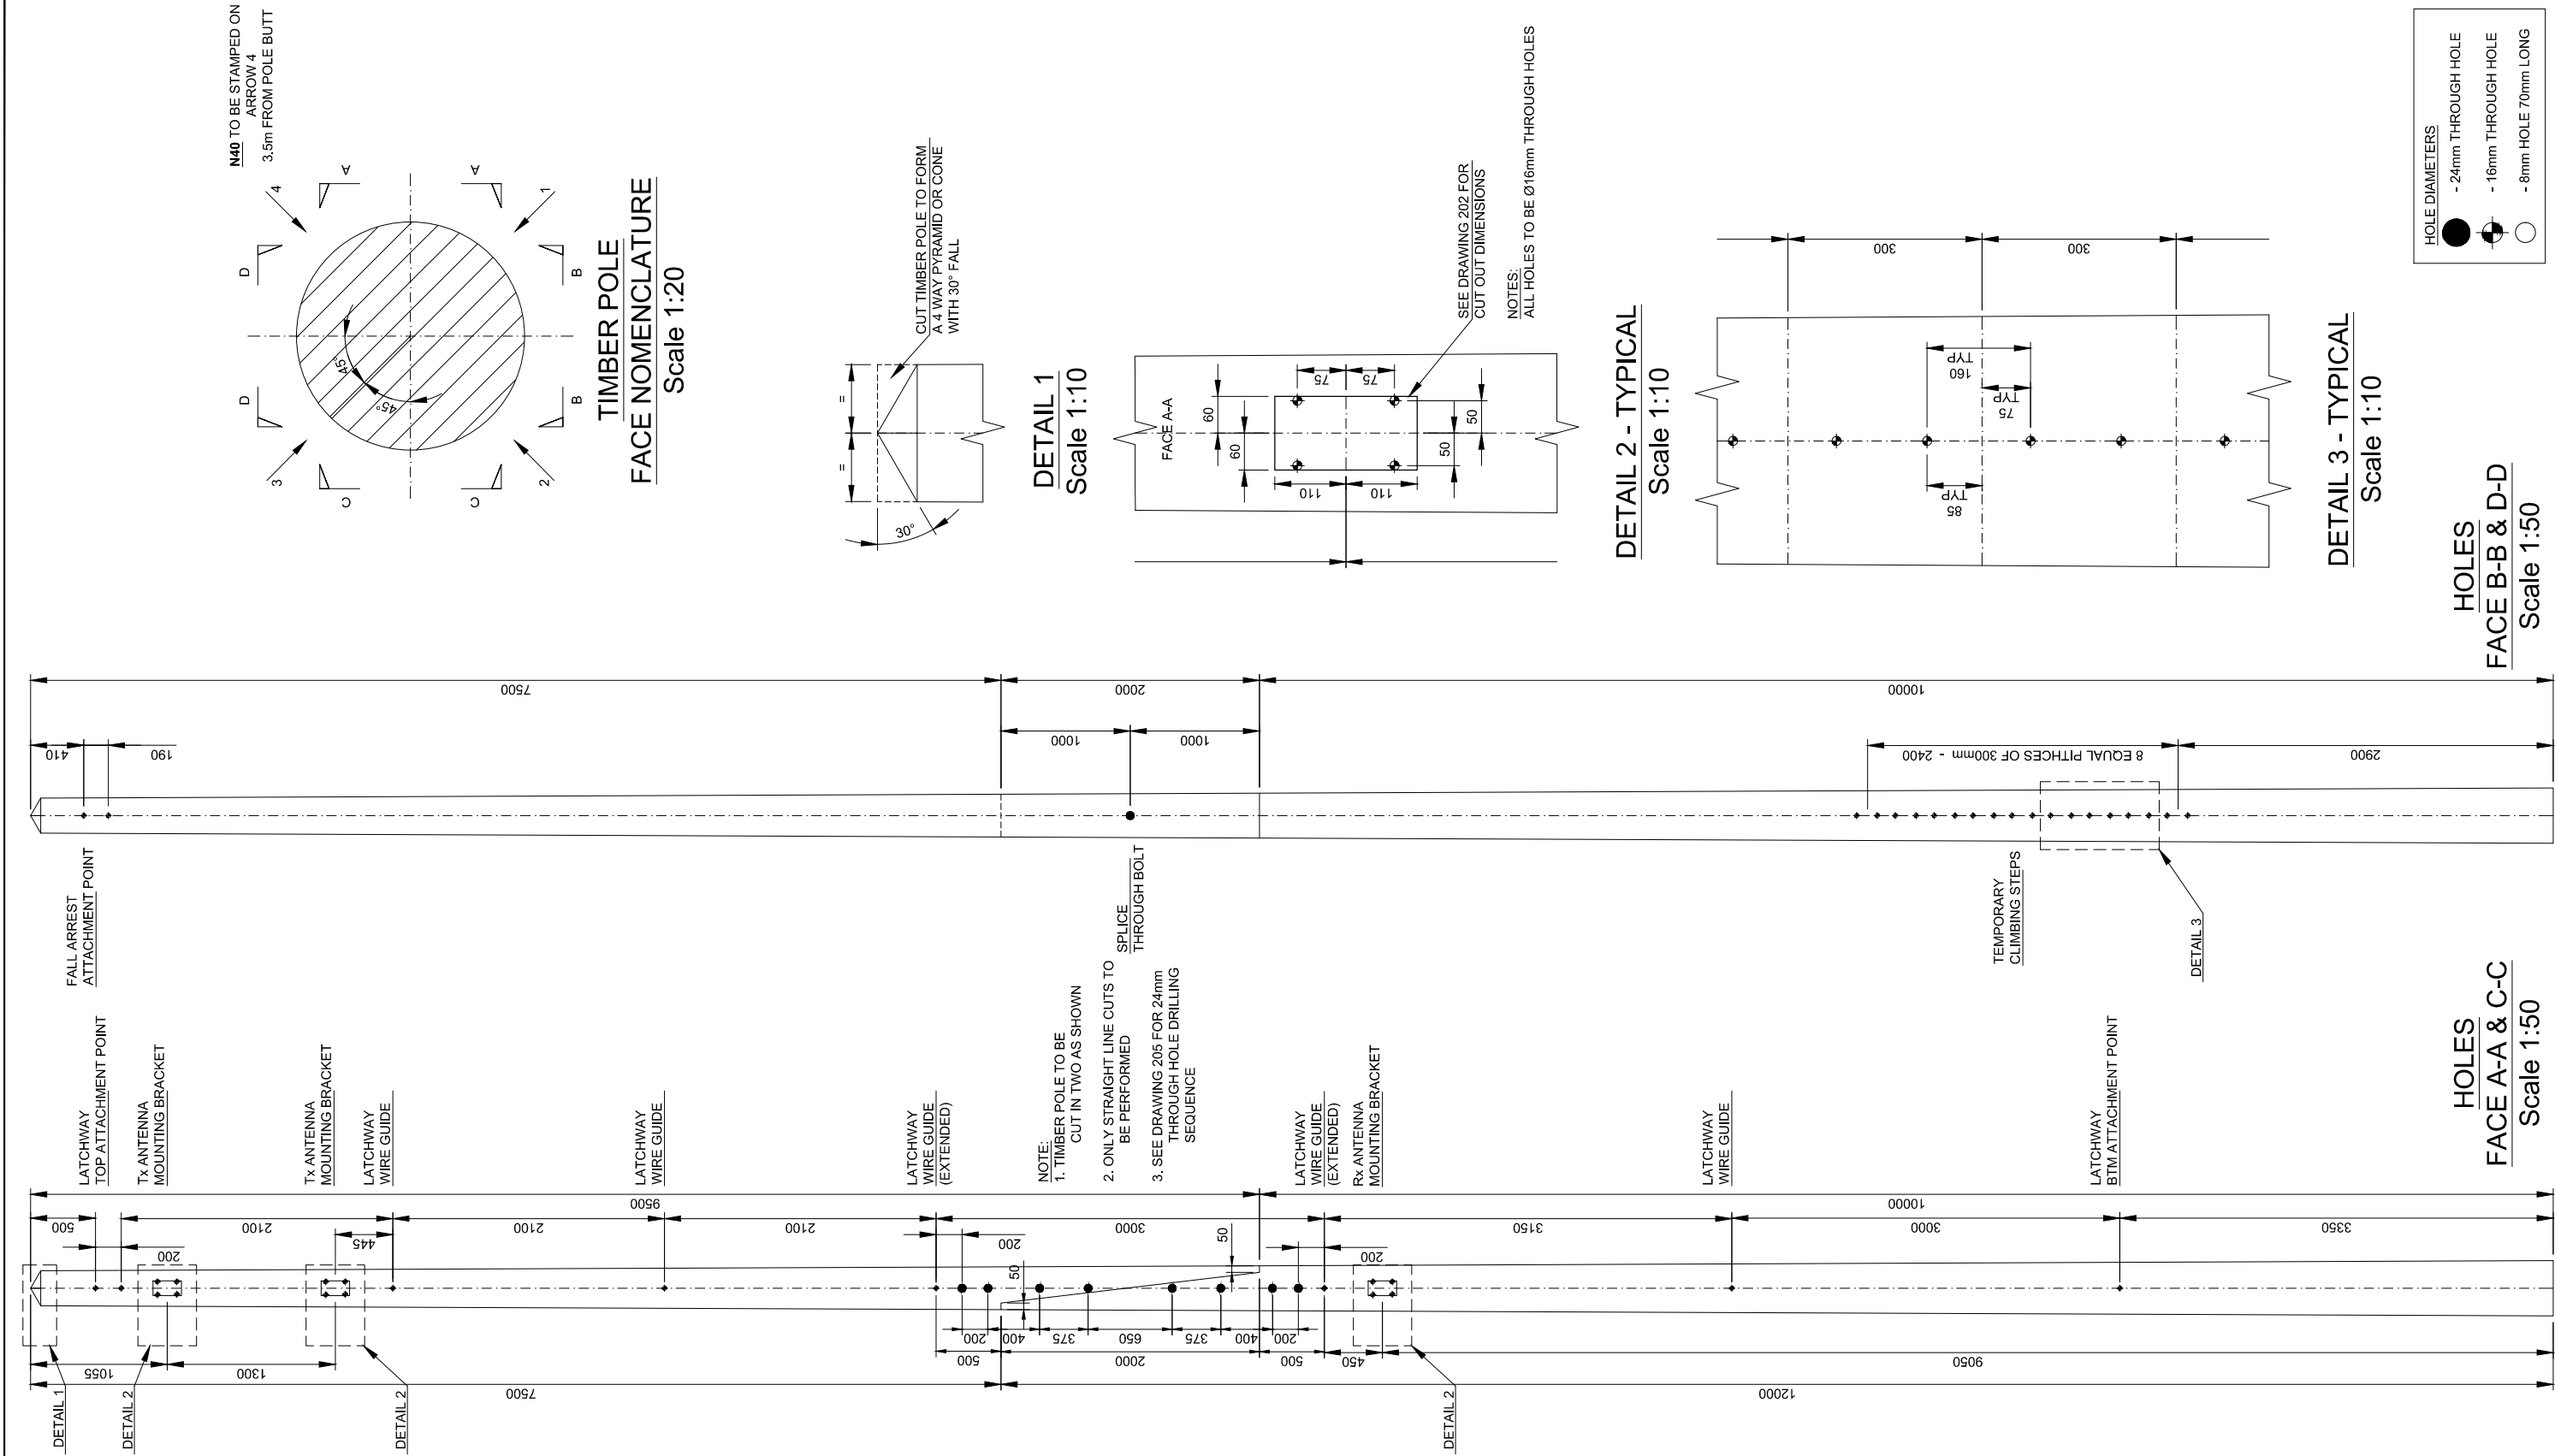REV
01

A vertical scale bar with alternating black and white segments, labeled from 0cm to 10cm in 1cm increments.

ALL SCALES AS SHOWN WHEN PRINTED AT A3

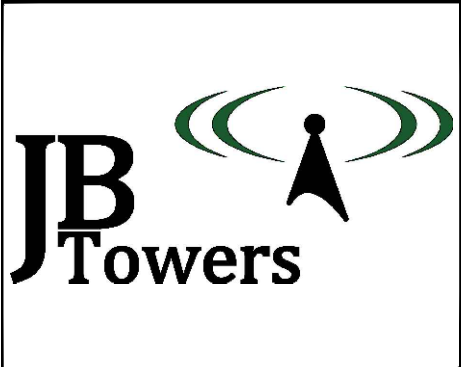

01	FIRST ISSUE			AM	23/04/20
REV	REV			BY	DATE
SCALE AS SHOWN		DRAWN	AM	CHECKED	MP
WHEN PRINTED AT A3		DATE	23/04/20	DATE	23/04/20
		APPROVED	JBT	DATE	23/04/20
ALL DIMENSIONS IN mm UNLESS OTHERWISE STATED. THIS DRAWING TO BE READ IN CONJUNCTION WITH OTHER RELEVANT DRAWINGS.					

TITLE

WALL

TIMBER POLE HOLE SET OUT

SHEET 2 OF 2

SITE ADDRESS

THISTLE RIGGS FARM

HOMER'S LANE

WARDEN, HEXHAM

NORTHUMBERLAND

NE46 4SR

ARQIVA REF.


141756

DRG No.

201

REV


01

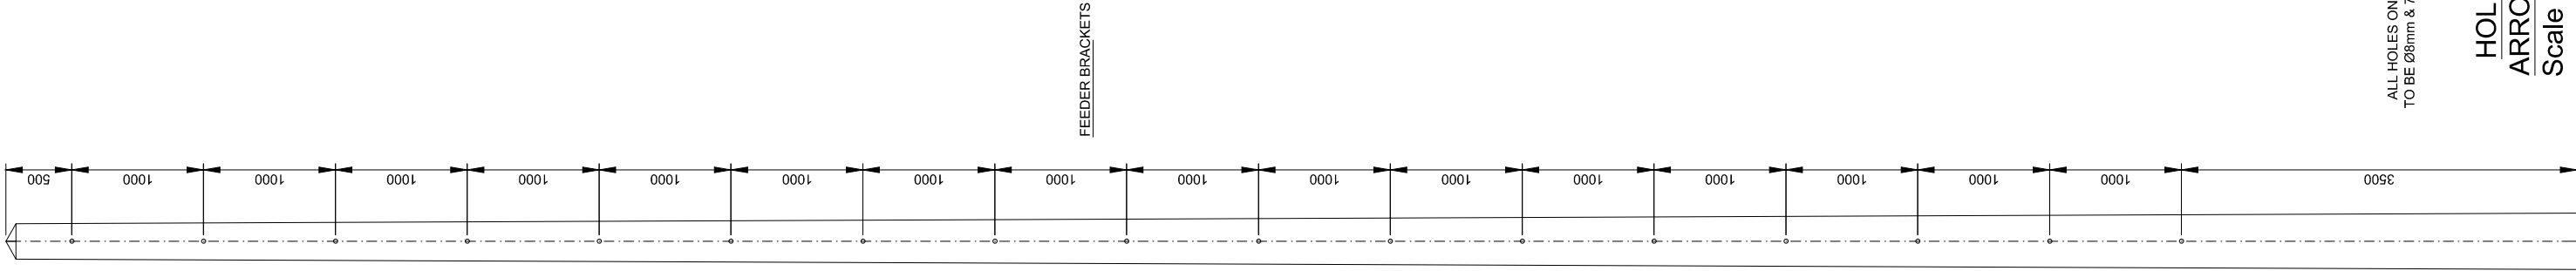

FEEDER BRACKETS

ALL HOLES ON ARROW 4
TO BE Ø8mm & 70mm LONG

HOLES
ARROW 4
Scale 1:50

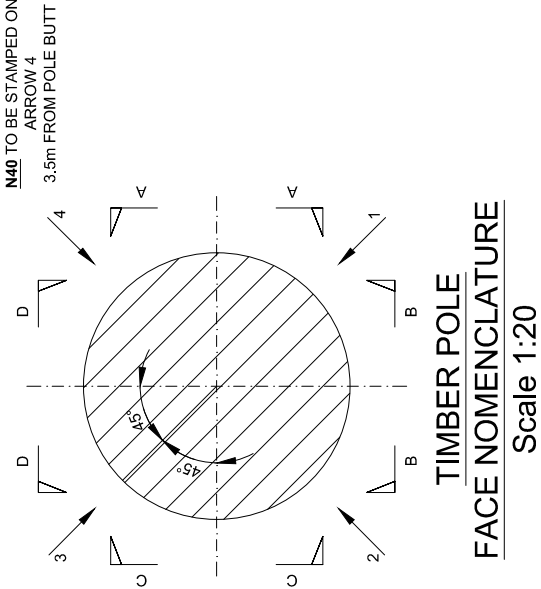

ALL SCALES AS SHOWN WHEN PRINTED AT A3

01	FIRST ISSUE					AM	23/04/20
REV	REV					BY	DATE
SCALE AS SHOWN		DRAWN	AM	CHECKED	MP	APPROVED	JBT
WHEN PRINTED AT A3		DATE	23/04/20	DATE	23/04/20	DATE	23/04/20
ALL DIMENSIONS IN mm UNLESS OTHERWISE STATED. THIS DRAWING TO BE READ IN CONJUNCTION WITH OTHER RELEVANT DRAWINGS.							


TITLE


WALL

TIMBER POLE CUT OUT
DETAIL

SITE ADDRESS




THISTLE RIGGS FARM
HOMER'S LANE
WARDEN, HEXHAM
NORTHUMBERLAND
NE46 4SR

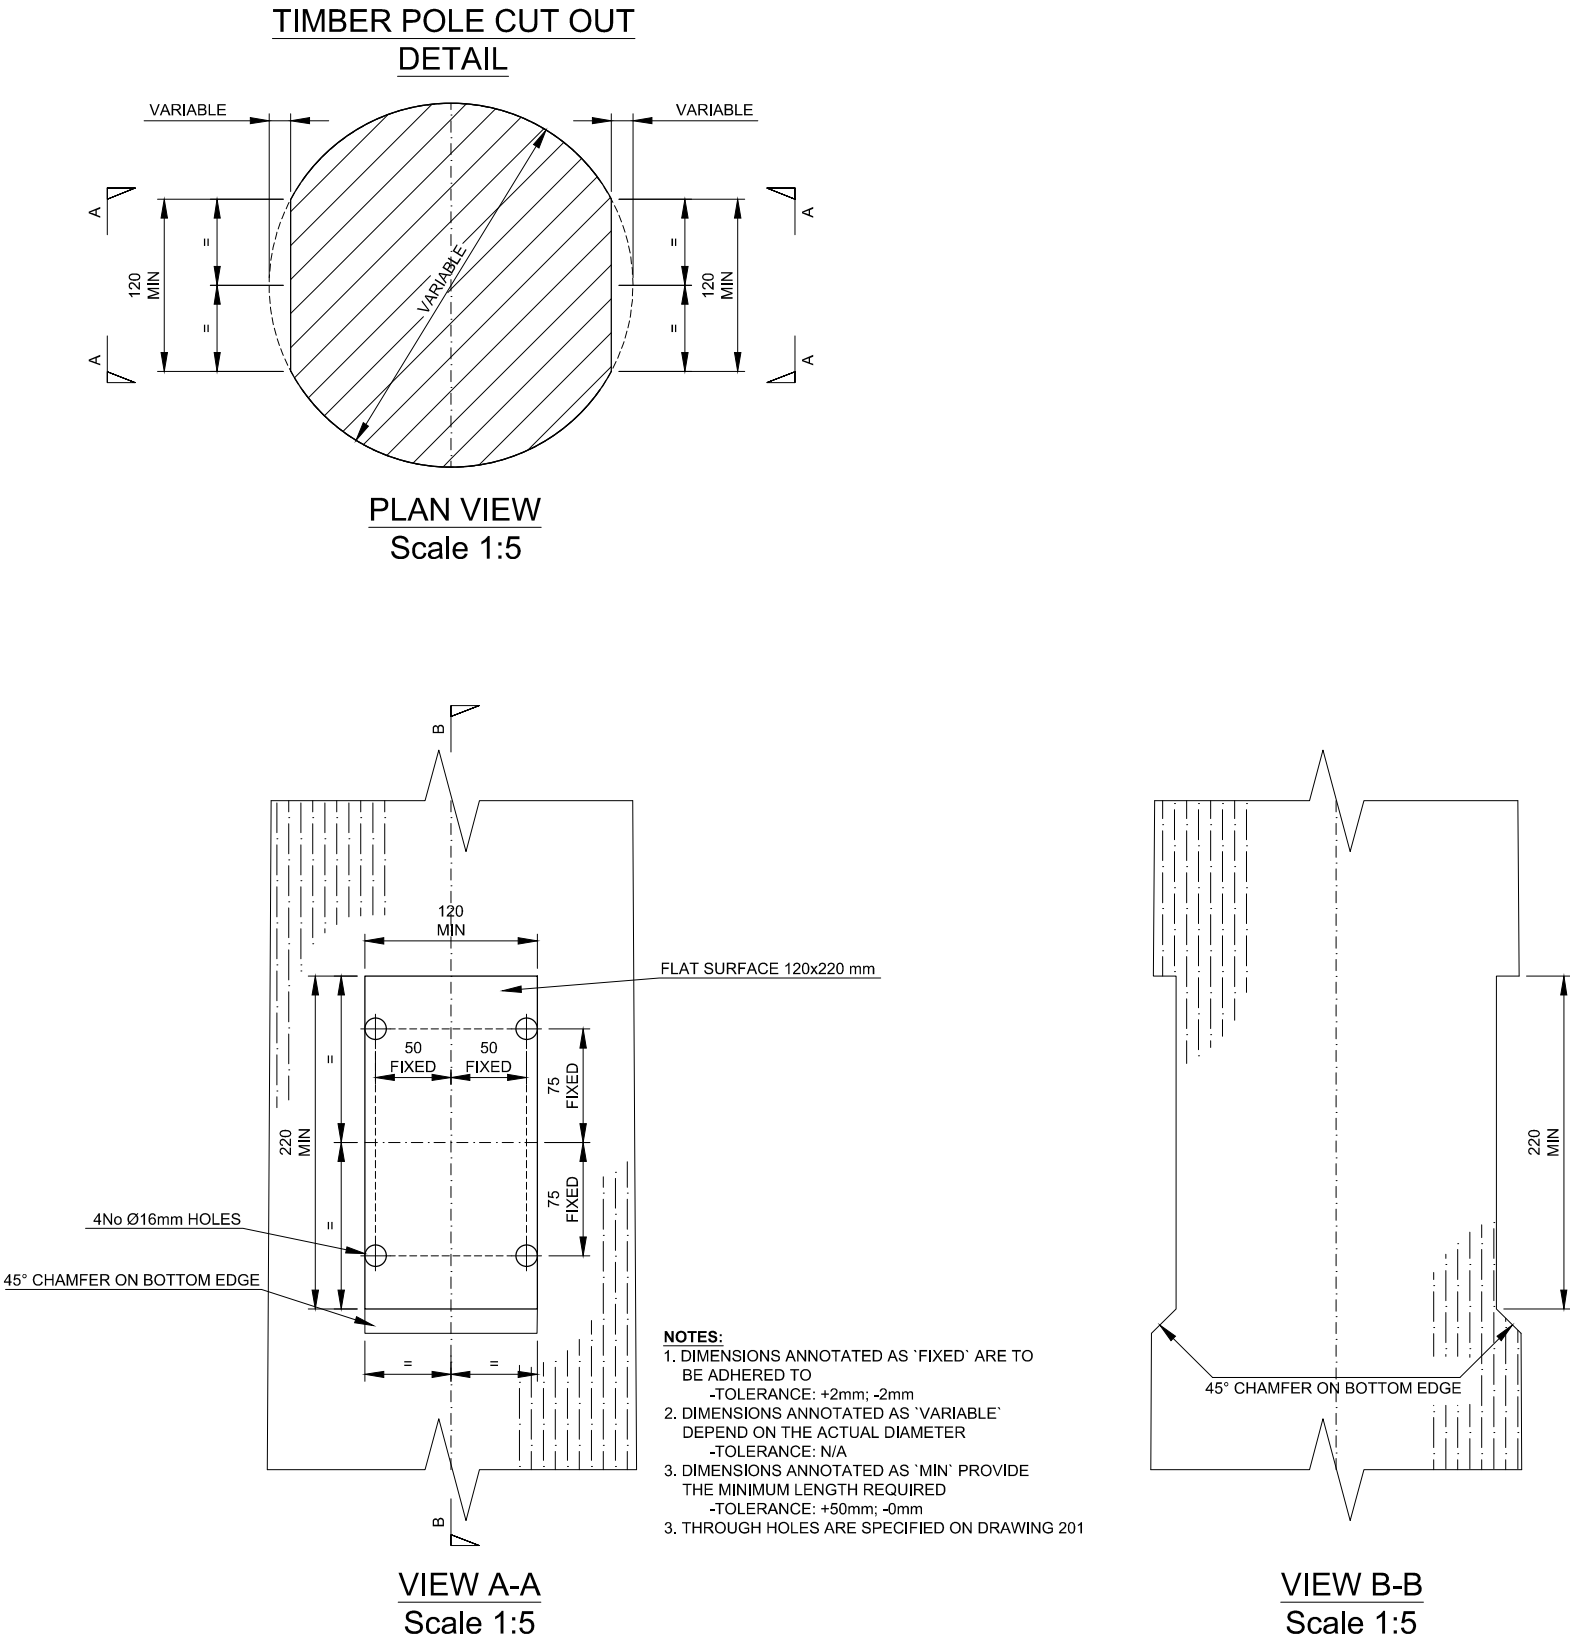

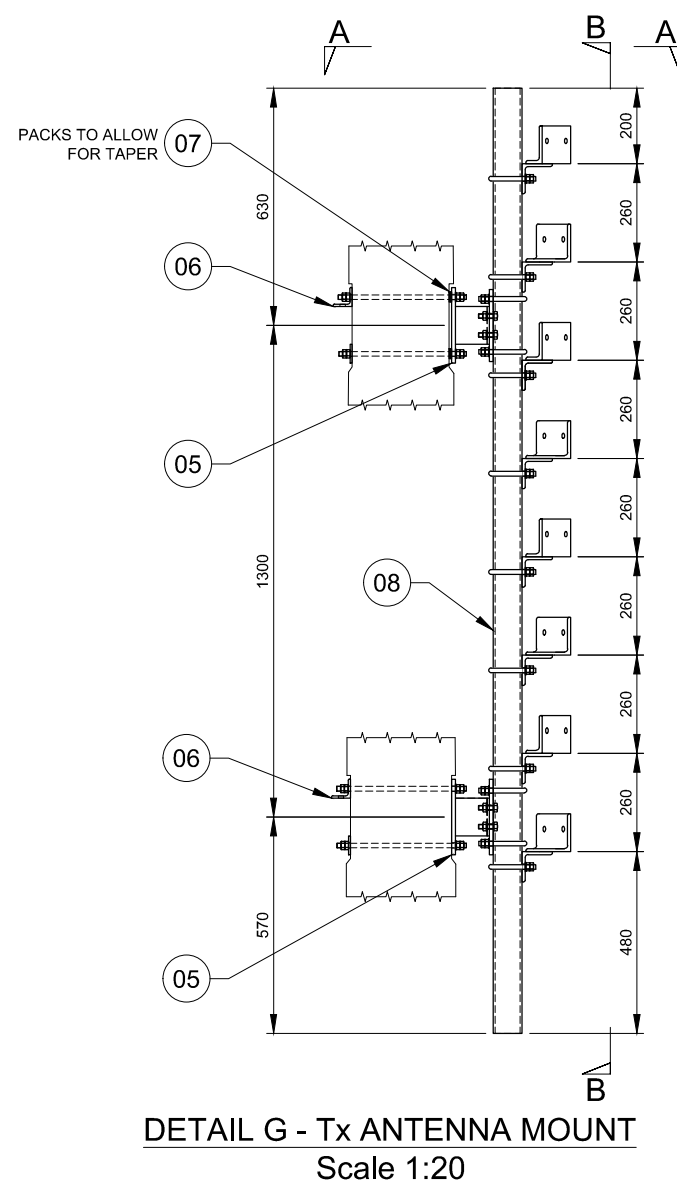

POSITION OF POWER
DIVIDER
TO BE DETERMINED
ON SITE

POSITION OF POWER
DIVIDER
TO BE DETERMINED
ON SITE

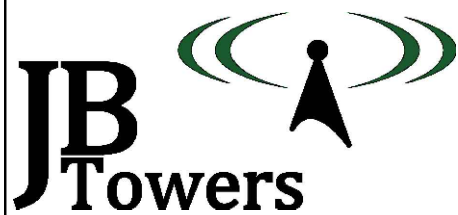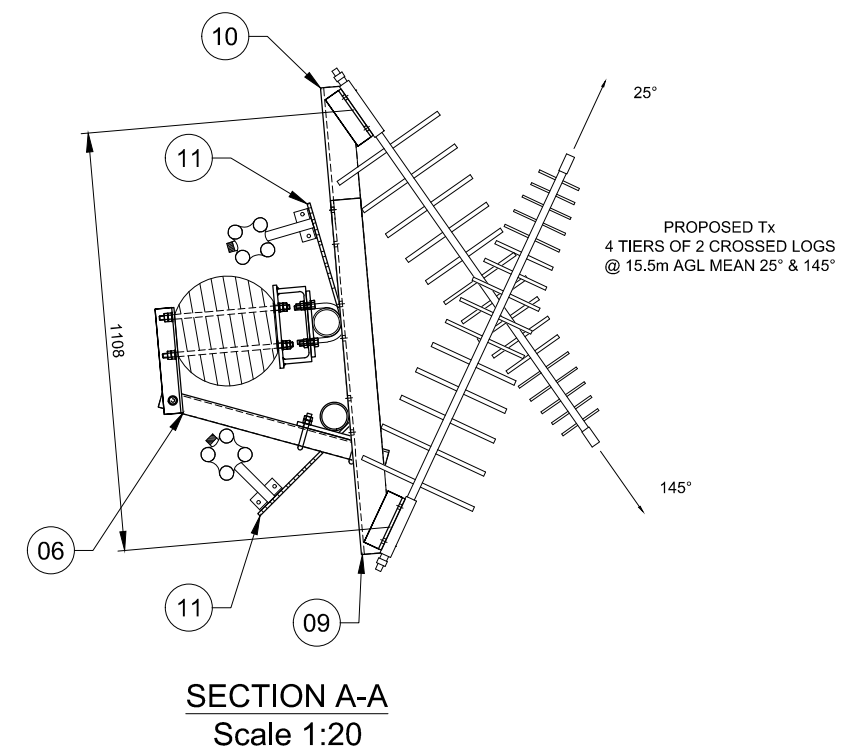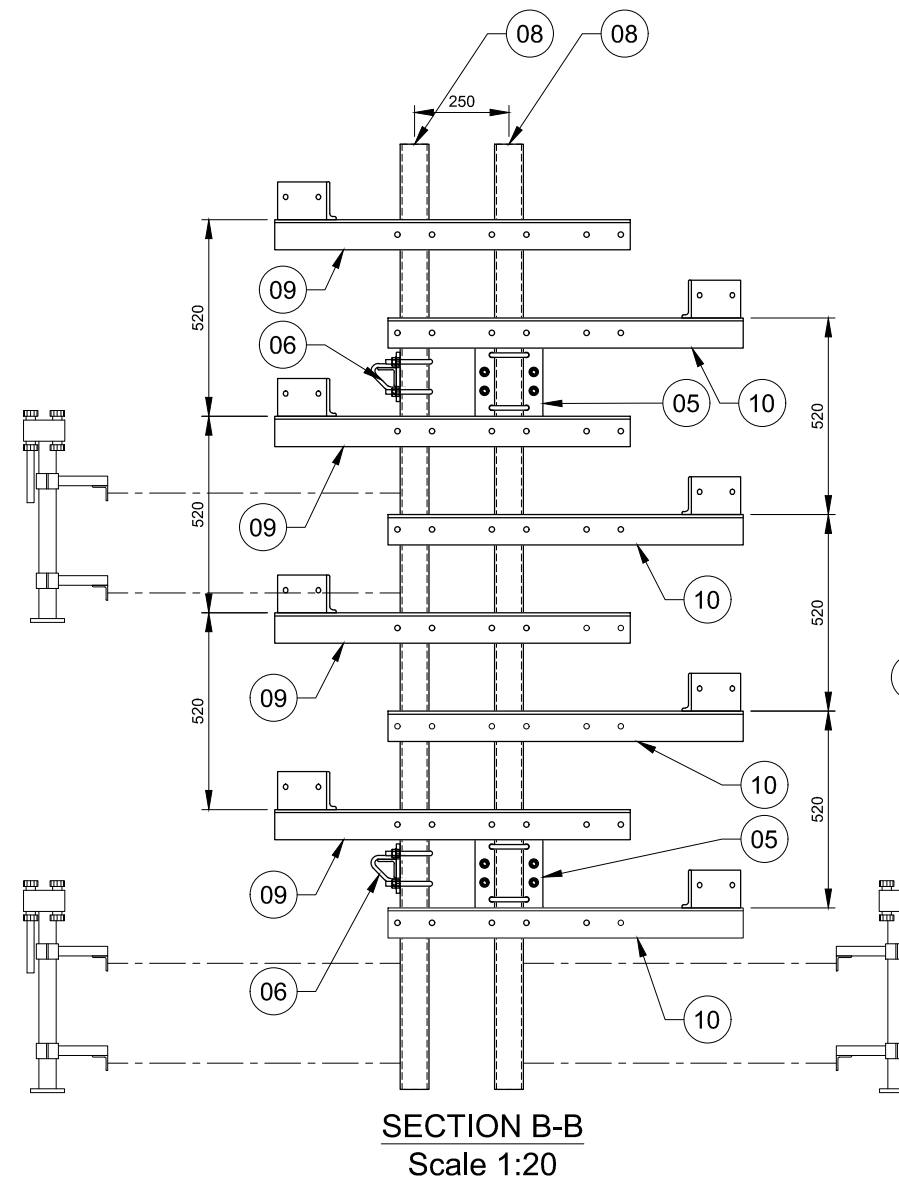


02	SITE NAME ADDED TO DRAWING TITLE			AM	28/04/20
01	FIRST ISSUE			AM	23/04/20
REV	REV			BY	DATE
SCALE AS SHOWN WHEN PRINTED AT A3		DRAWN AM DATE 23/04/20	CHECKED MP DATE 23/04/20	APPROVED JB DATE 23/04/20	
ALL DIMENSIONS IN mm UNLESS OTHERWISE STATED. THIS DRAWING TO BE READ IN CONJUNCTION WITH OTHER RELEVANT DRAWINGS.					

TITLE
WALL
Tx ANTENNA MOUNT
DETAIL G


SITE ADDRESS

THISTLE RIGGS FARM
HOMER'S LANE
WARDEN, HEXHAM
NORTHUMBERLAND
NE46 4SR


ARQIVA REF. 141756	DRG No. 203	REV 02
------------------------------	-----------------------	------------------

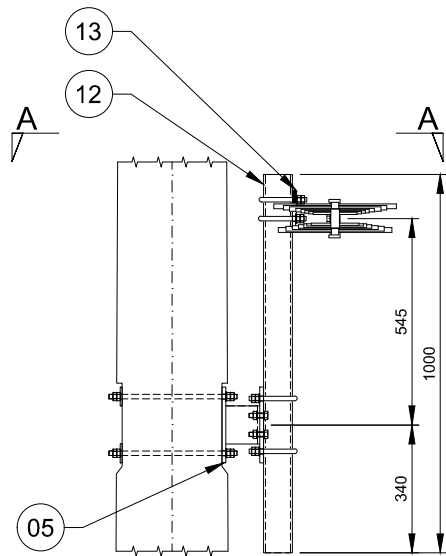

DETAIL H - Rx ANTENNA MOUNT
Scale 1:20

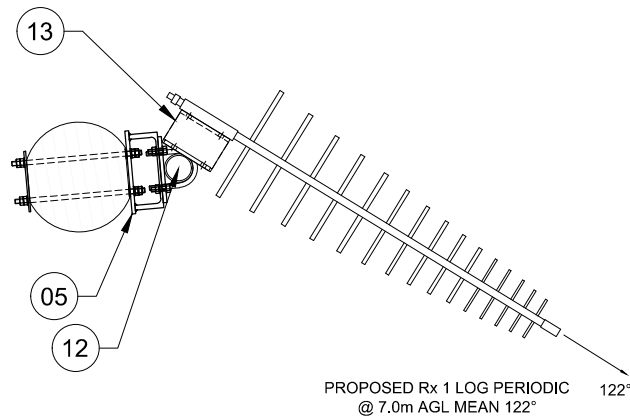

SECTION A-A
Scale 1:20

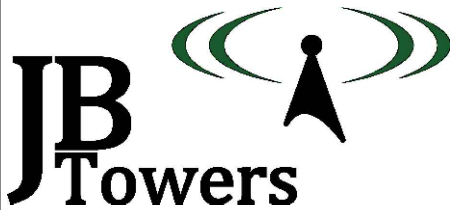

02	SITE NAME ADDED TO DRAWING TITLE			AM	28/04/20
01	FIRST ISSUE			AM	23/04/20
REV	REV			BY	DATE
SCALE AS SHOWN		DRAWN	AM	CHECKED	MP
WHEN PRINTED AT A3		DATE	23/04/20	DATE	23/04/20
		APPROVED	JBT	DATE	23/04/20
ALL DIMENSIONS IN mm UNLESS OTHERWISE STATED. THIS DRAWING TO BE READ IN CONJUNCTION WITH OTHER RELEVANT DRAWINGS.					

TITLE
WALL
Rx ANTENNA MOUNT
DETAIL H


SITE ADDRESS
THISTLE RIGGS FARM
HOMER'S LANE
WARDEN, HEXHAM
NORTHUMBERLAND
NE46 4SR

ARQIVA REF. 141756	DRG No. 204	REV 02
-----------------------	----------------	-----------



ALL SCALES AS SHOWN WHEN PRINTED AT A3




ALL SCALES AS SHOWN WHEN PRINTED AT A3

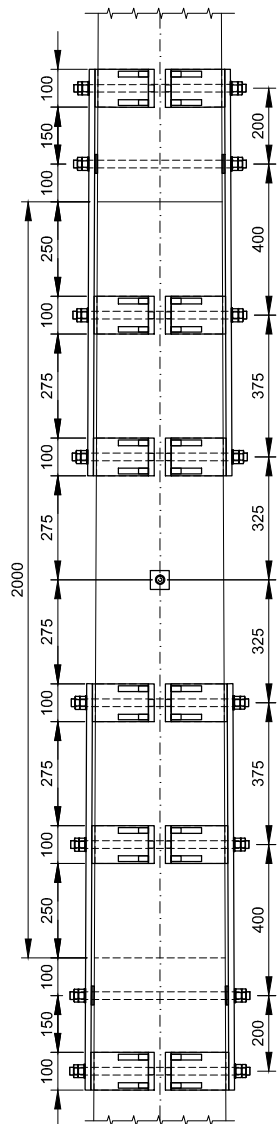

DETAIL I TIMBER POLE SPLICE
Scale 1:20

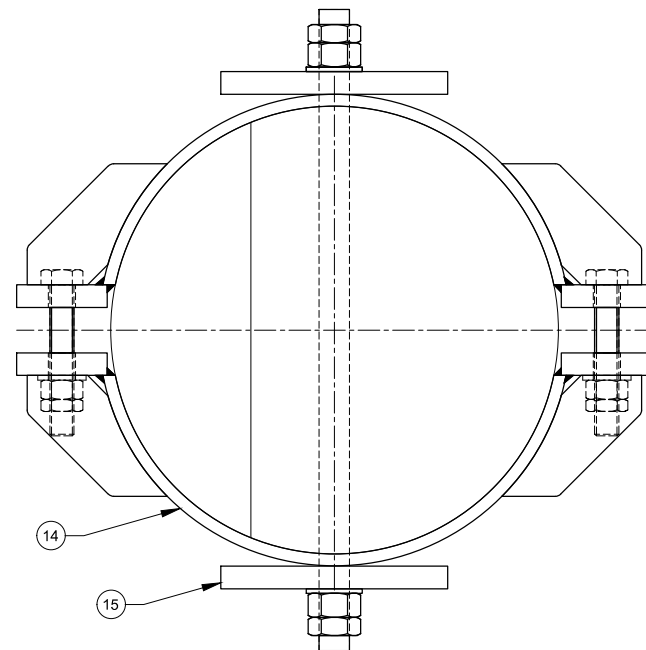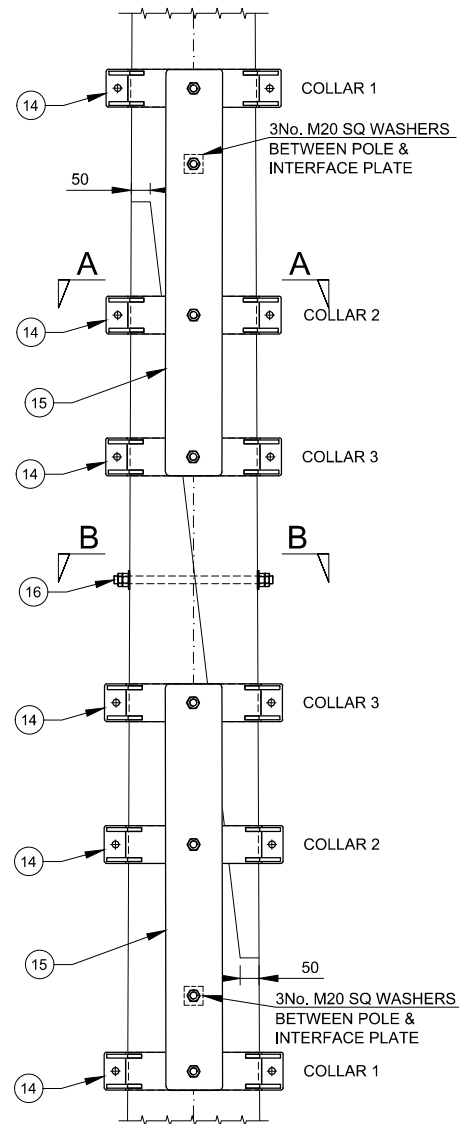

SECTION A-A
Scale 1:5

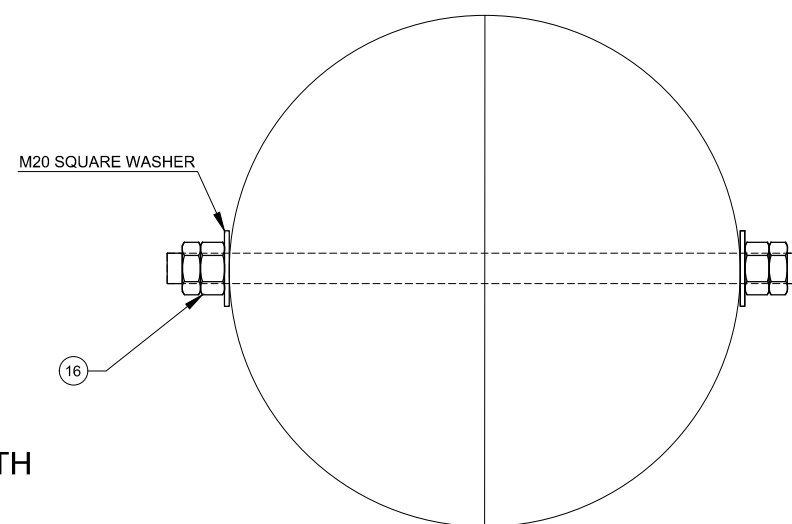


SECTION B-B
Scale 1:5

- WORK SEQUENCE (PRIOR TO POLE BEING SENT TO SITE):**
1. LOCATION OF COLLARS TO BE MARKED ON POLE AND POLE OD AT THESE LOCATIONS TO BE MEASURED AND USED TO INFORM THE FABRICATION OF THE STEEL COLLARS.
(COLLAR HOLES FOR THE THROUGH BOLTS ARE TO BE DRILLED LATER)
 2. HOLES IN POLE FOR ALL COLLAR THROUGH BOLTS TO BE DRILLED.
 3. SPLICE JOINT TO BE CUT IN POLE.
 4. POLE TO BE PRESSURE IMPREGNATED WITH CREOSOTE.
 5. POLE SECTIONS TO BE OFFERED TO ONE ANOTHER AND ONCE IN THE CORRECT POSITION COLLARS 2 SHALL BE INSTALLED TO HOLD THE POLE IN POSITION AND THE CLAMPING BOLTS TORQUED.
 6. THE THROUGH BOLT IN THE CENTRE OF THE SPLICE SHALL BE DRILLED AND THE THROUGH BOLT INSERTED.
 7. THE THROUGH BOLTS FOR COLLARS 1 & 3 SHALL BE INSTALLED AND THE COLLARS OFFERED UP AND THE REQD HOLE LOCATIONS IN THE COLLARS MARKED AND THEN DRILLED.
 8. THESE COLLARS SHALL BE INSTALLED OVER THE THROUGH BOLTS AND THEN THE CLAMPING BOLTS TORQUED.
 9. COLLARS 2 SHALL THEN BE REMOVED AND THE THROUGH BOLTS INSTALLED AND THE COLLARS OFFERED UP AND THE REQD HOLE LOCATIONS IN THE COLLARS MARKED AND THEN DRILLED.
 10. THESE COLLARS SHALL BE INSTALLED OVER THE THROUGH BOLTS AND THEN THE CLAMPING BOLTS TORQUED.
 11. THE VERTICAL PLATES STRAPPING THE COLLARS TOGETHER SHALL THEN BE INSTALLED.
 12. THE FIT OF ALL ELEMENTS OF THE SPLICE SHALL BE CHECKED AND ONCE SATISFACTORY FIT HAS BEEN CONFIRMED THE SPLICE JOINT CAN BE DISASSEMBLED.
 13. ANY DISTURBED SURFACES SHALL HAVE THEIR WATERPROOFING REPAIRED AS PER NOTES ON DRG 200
 14. THE CLAMPING BOLTS USED IN THE CHECK ERECTION SHALL BE DISCARDED AND NEW BOLTS SUPPLIED TO SITE.

NOTE:

- ALL M16 BOLTS TO BE TIGHTENED TO 90Nm
- ALL SITE DRILLED HOLE/CUT ENDS TO BE TREATED WITH METAFLUX 70-40 ZINC PASTE FOLLOWED BY 1 COAT OF 7-42 ZINC ALU OR 70-16 ALUMINIUM SPRAY

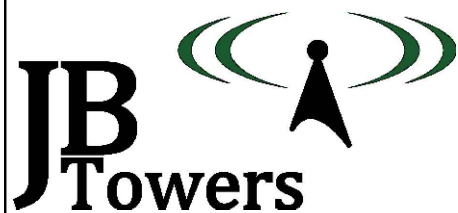


02	SITE NAME ADDED TO DRAWING TITLE			AM 28/04/20
01	FIRST ISSUE			AM 23/04/20
REV	REV			BY DATE
SCALE AS SHOWN WHEN PRINTED AT A3		DRAWN AM DATE 23/04/20	CHECKED MP DATE 23/04/20	APPROVED JB DATE 23/04/20
ALL DIMENSIONS IN mm UNLESS OTHERWISE STATED. THIS DRAWING TO BE READ IN CONJUNCTION WITH OTHER RELEVANT DRAWINGS.				

TITLE		SITE ADDRESS		
WALL		THISTLE RIGGS FARM		
TIMBER POLE SPLICE		HOMER'S LANE		
DETAIL I		WARDEN, HEXHAM		
		NORTHUMBERLAND		
		NE46 4SR		
ARQIVA REF.		DRG No.	REV	
141756		205	02	


ALL SCALES AS SHOWN WHEN PRINTED AT A3



ALL SCALES AS SHOWN WHEN PRINTED AT A3

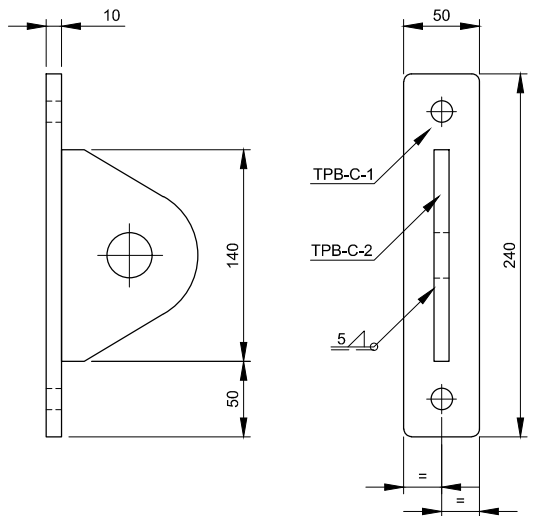

PART TPB-C
Scale 1:5

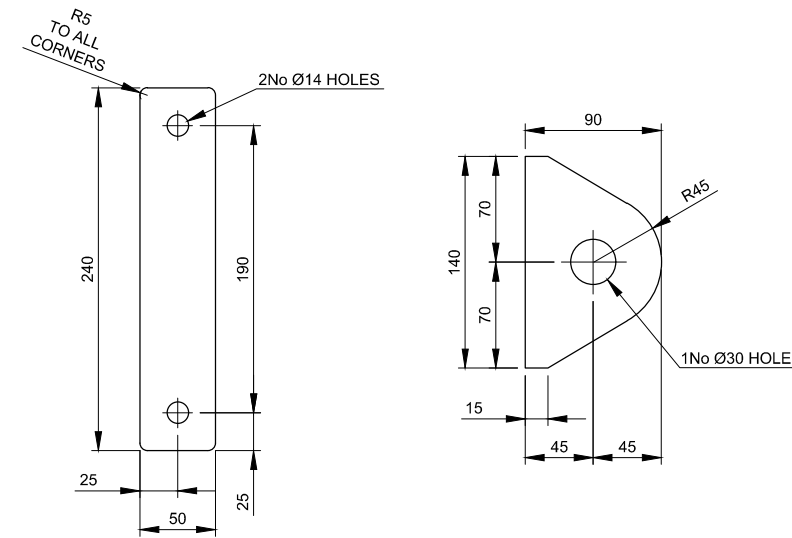


TPB-C-1 - 10mm THICK
Scale 1:5

TPB-C-2 - 10mm THICK
Scale 1:5


Parts list for TPB-C

Item	Part	Quantity	Part description	Length	Material	Weight
01	TPB-C-1	1	Plate 240x50x10mm	N/A	S275J0	0.94 kg
02	TPB-C-2	1	Plate 140x90x10mm	N/A	S275J0	0.99 kg
03	STUDS	1	M12 STUDDING	350mm	GRADE 8.8	0.31 kg
Total Weight:						2.24 kg

- All steel hot dip galvanized
- Each STUD to be supplied with 4 Full Nuts, 2 Flat Washers and 2 Spring Washers
- For fabrication notes see drawing 305

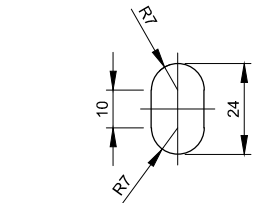

SLOTTED HOLE DETAIL
Scale 1:2

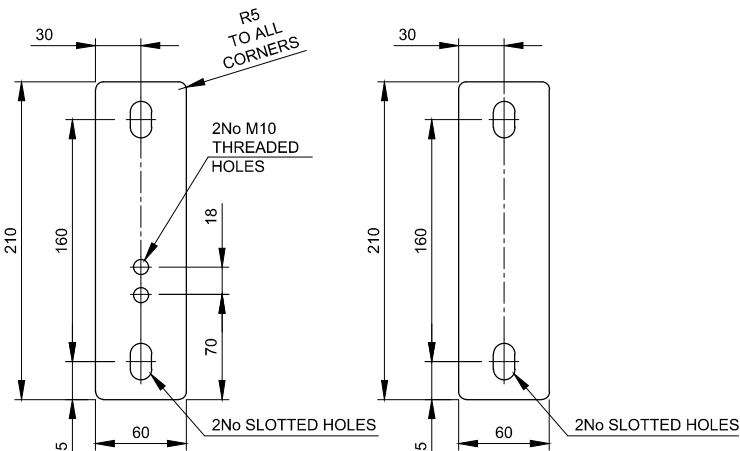


PART TPS-R-1
Scale 1:5

PART TPS-R-2
Scale 1:5

Parts list for TPS-R

Item	Part	Quantity	Part description	Length	Material	Weight
01	TPS-R-1	1	Plate 210x60x15mm	N/A	S275J0	1.48 kg
02	TPS-R-2	1	Plate 210x60x5mm	N/A	S275J0	0.49 kg
03	STUDS	2	M12 STUDDING	500mm	GRADE 8.8	0.44 kg
04	NUT-S	2	M12 SHALLOW NUT	N/A	GRADE 8.8	-
05	NUT	4	M12 NUT	N/A	GRADE 8.8	-
06	WSH	4	M12 WASHER	N/A	GRADE 8.8	-
Total Weight:						2.41 kg

- All steel hot dip galvanized
- For fabrication notes see drawing 305

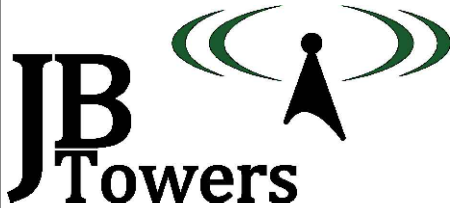

02	SITE NAME ADDED TO DRAWING TITLE			AM	28/04/20
01	FIRST ISSUE			AM	23/04/20
REV	REV			BY	DATE
SCALE AS SHOWN		DRAWN	AM	CHECKED	MP
WHEN PRINTED AT A3		DATE	23/04/20	DATE	23/04/20
APPROVED JBT					
DATE 23/04/20					
ALL DIMENSIONS IN mm UNLESS OTHERWISE STATED.					
THIS DRAWING TO BE READ IN CONJUNCTION WITH					
OTHER RELEVANT DRAWINGS.					

TITLE
WALL
ATTACHMENT POINT &
TEMPORARY STEP DETAILS
PARTS: TPB-C; TPS-R


SITE ADDRESS
THISTLE RIGGS FARM
HOMER'S LANE
WARDEN, HEXHAM
NORTHUMBERLAND
NE46 4SR

ARQIVA REF.
141756
DRG No.
300
REV
02

ALL SCALES AS SHOWN WHEN PRINTED AT A3




ALL SCALES AS SHOWN WHEN PRINTED AT A3

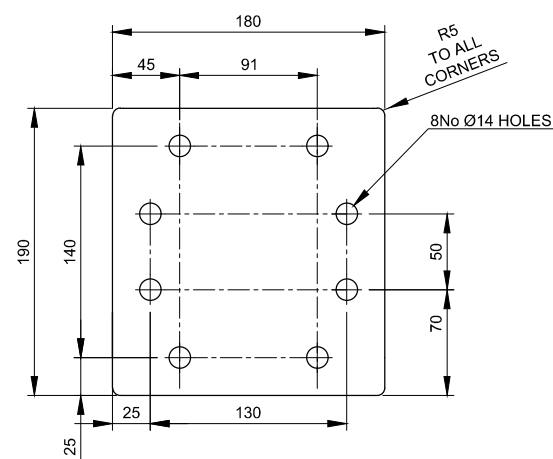

TPB-B-1 - 10mm THICK
Scale 1:5


TPB-B-5 - 10mm THICK
Scale 1:5

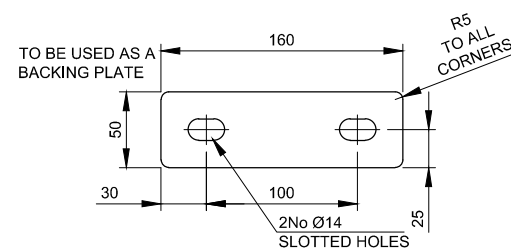

PART TPB-B
Scale 1:5

TPB-B-2 - PFC 200x90x30
Scale 1:5

TPB-B-4 - 5mm THICK
Scale 1:5

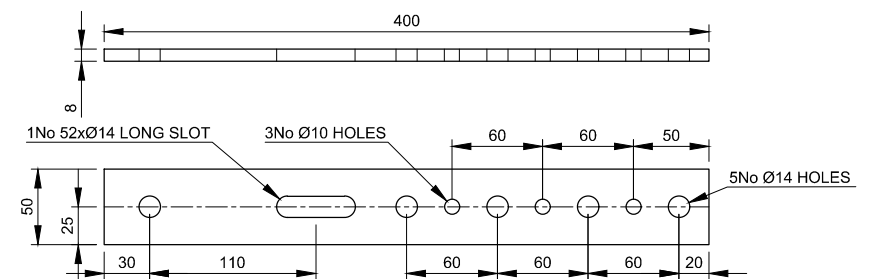

TPA-PD - 8mm THICK
Scale 1:5

Parts list for TPB-B


Item	Part	Quantity	Part description	Length	Material	Weight
01	TPB-B-1	1	Plate 220x200x10mm	N/A	S275J0	3.45 kg
02	TPB-B-2	1	PFC 200x90x30	100mm	S275J0	3.00 kg
03	TPB-B-4	2	Plate 160x50x5mm	N/A	S275J0	0.31 kg
04	TPB-B-5	1	Plate 190x180x10mm	N/A	S275J0	2.70 kg
05	STUDS	4	M12 STUDDING	450mm	GRADE 8.8	0.39 kg
06	BOLT	4	M12 45mm LONG (2D+6)	45mm	GRADE 8.8	-
07	U-BOLT	2	M12 U-BOLT FOR CHS 76.1	N/A	GRADE 8.8	-
- All steel hot dip galvanized					Total Weight:	11.33 kg

- All steel hot dip galvanized
- Each STUD & U-BOLT to be supplied with 4 Full Nuts, 2 Flat Washers and 2 Spring Washers
- Each BOLT to be supplied with 1 Full Nut, 1 Form E FLat Washer and 1 Spring Washer
- For fabrication notes see drawing 305


Parts list for TPA-PD

Item	Part	Quantity	Part description	Length	Material	Weight
01	TPA-PD	1	400x50x8mm	N/A	S275J0	1.26 kg
02	U-BOLT	1	M12 U-BOLT FOR CHS 76.1mm	N/A	GRADE 8.8	-
- All steel hot dip galvanized					Total Weight:	1.26 kg

- All steel hot dip galvanized
- Each U-BOLT to be supplied with 4 Full Nuts, 2 Flat Washers and 2 Spring Washers
- For fabrication notes see drawing 305

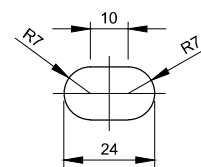

SLOTTED HOLE DETAIL
Scale 1:2

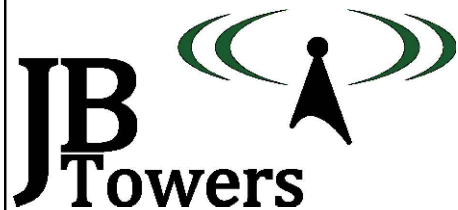

02	SITE NAME ADDED TO DRAWING TITLE			AM	28/04/20
01	FIRST ISSUE			AM	23/04/20
REV	REV			BY	DATE
SCALE AS SHOWN WHEN PRINTED AT A3		DRAWN	AM	CHECKED	MP
		DATE	23/04/20	DATE	23/04/20
				APPROVED	JB
				DATE	23/04/20
ALL DIMENSIONS IN mm UNLESS OTHERWISE STATED. THIS DRAWING TO BE READ IN CONJUNCTION WITH OTHER RELEVANT DRAWINGS.					

TITLE

WALL

STEELWORK BRACKET,
INTERFACE PLATE, POWER
DIVIDER STRAP

PARTS: TPB-B, TPA-PD

SITE ADDRESS

THISTLE RIGGS FARM
HOMER'S LANE
WARDEN, HEXHAM
NORTHUMBERLAND
NE46 4SR




ARQIVA REF.
141756

DRG No.
301REV
02

ALL SCALES AS SHOWN WHEN PRINTED AT A3



ALL SCALES AS SHOWN WHEN PRINTED AT A3

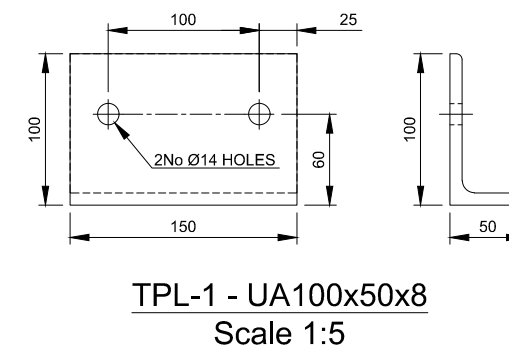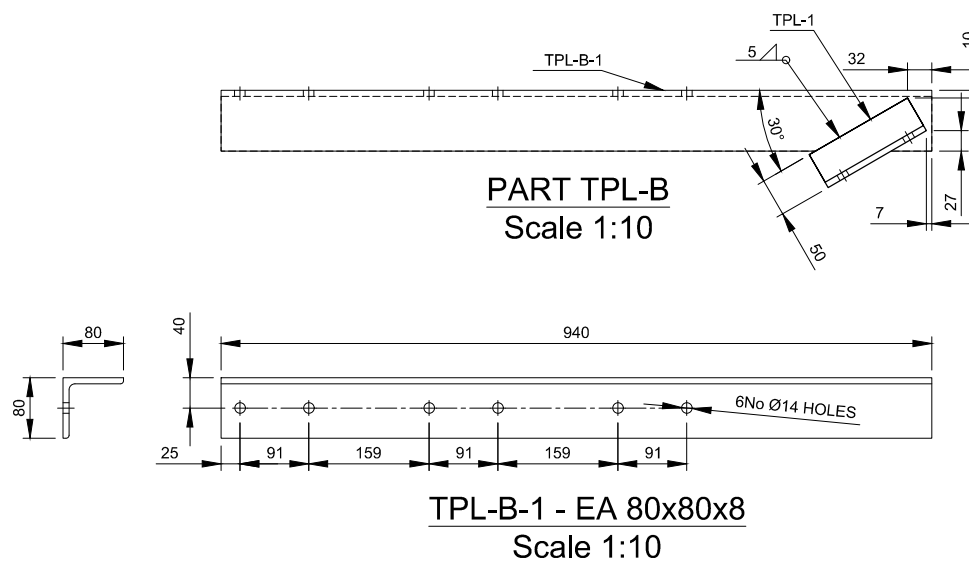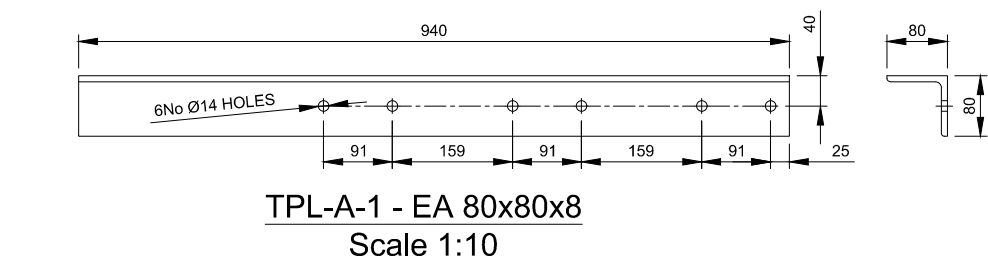


Item	Part	Quantity	Part description	Length	Material	Weight
01	TPL-A-1	1	EA 80x80x8	940mm	S275J0	9.10 kg
02	TPL-1	1	UA 100x50x8	150mm	S275J0	1.40 kg
03	U-BOLT	2	M12 U-BOLT FOR CHS 76.1mm	N/A	GRADE 8.8	-
- All steel hot dip galvanized					Total Weight:	10.50 kg

- All steel hot dip galvanized
- Each U-BOLT to be supplied with 4 Full Nuts, 2 Flat Washers and 2 Spring Washers
- For fabrication notes see drawing 305


Item	Part	Quantity	Part description	Length	Material	Weight
01	TPL-B-1	1	EA 80x80x8	940mm	S275J0	9.10 kg
02	TPL-1	1	UA 100x50x8	150mm	S275J0	1.40 kg
03	U-BOLT	2	M12 U-BOLT FOR CHS 76.1mm	N/A	GRADE 8.8	-
- All steel hot dip galvanized					Total Weight:	10.50 kg

- All steel hot dip galvanized
- Each U-BOLT to be supplied with 4 Full Nuts, 2 Flat Washers and 2 Spring Washers
- For fabrication notes see drawing 305

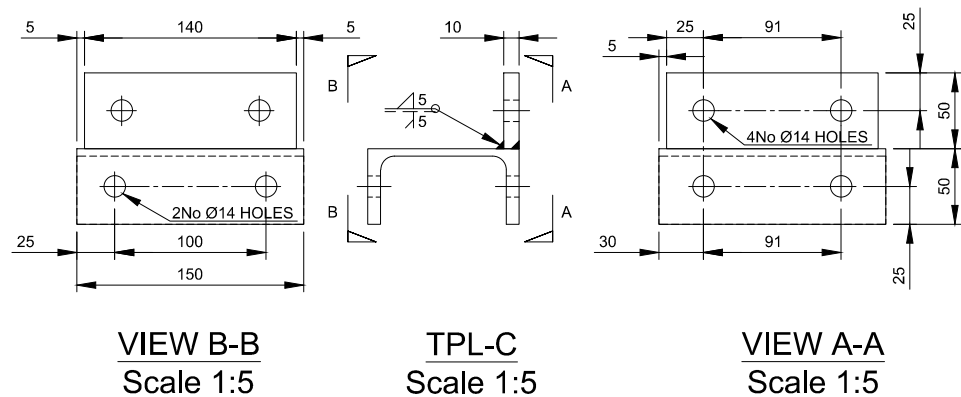

Item	Part	Quantity	Part description	Length	Material	Weight
01	TPL-C-1	1	PFC100x50x10	150mm	S275J0	1.50 kg
02	TPL-2	1	PLATE 140x50x10	-	S275J0	0.55 kg
03	U-BOLT	2	M12 U-BOLT FOR CHS 76.1mm	N/A	GRADE 8.8	-
- All steel hot dip galvanized					Total Weight:	2.05 kg

- All steel hot dip galvanized
- Each U-BOLT to be supplied with 4 Full Nuts, 2 Flat Washers and 2 Spring Washers
- For fabrication notes see drawing 305

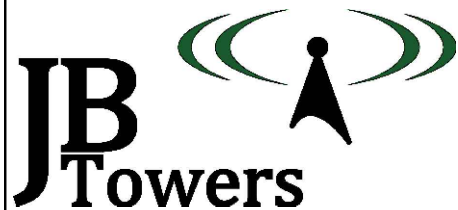

argiva

02	SITE NAME ADDED TO DRAWING TITLE		AM	28/04/20
01	FIRST ISSUE		AM	23/04/20
REV	REV		BY	DAT
SCALE AS SHOWN WHEN PRINTED AT A3	DRAWN AM DATE 23/04/20	CHECKED MP DATE 23/04/20	APPROVED JB DATE 23/04/20	
ALL DIMENSIONS IN mm UNLESS OTHERWISE STATED. THIS DRAWING TO BE READ IN CONJUNCTION WITH OTHER RELEVANT DRAWINGS.				


PARTS: TPL-A; TPL-B; TPL-C

THISTLE RIGGS FARM
HOMER'S LANE
WARDEN, HEXHAM
NORTHUMBERLAND
NE46 4SR


ARQIVA REF.
141756

DRG No.
302REV
02


ALL SCALES AS SHOWN WHEN PRINTED AT A3

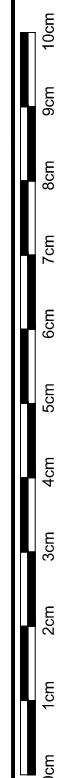

ALL SCALES AS SHOWN WHEN PRINTED AT A3


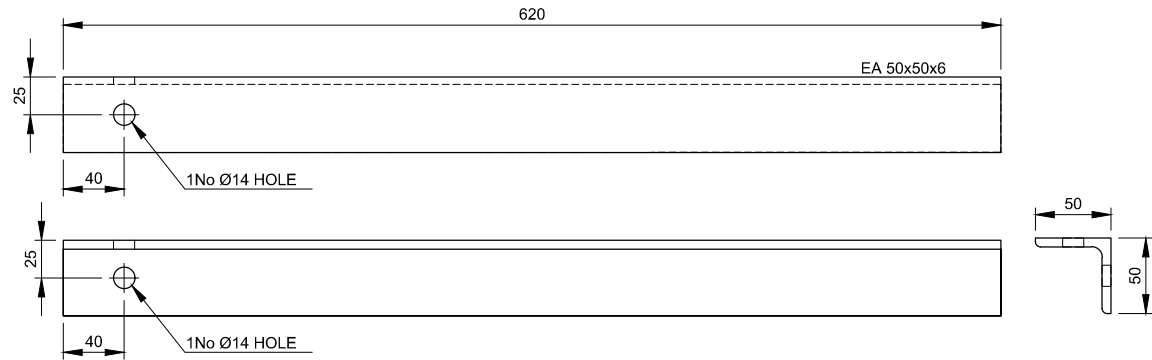


TPB-BR-1 - EA50x50x6
Scale 1:5

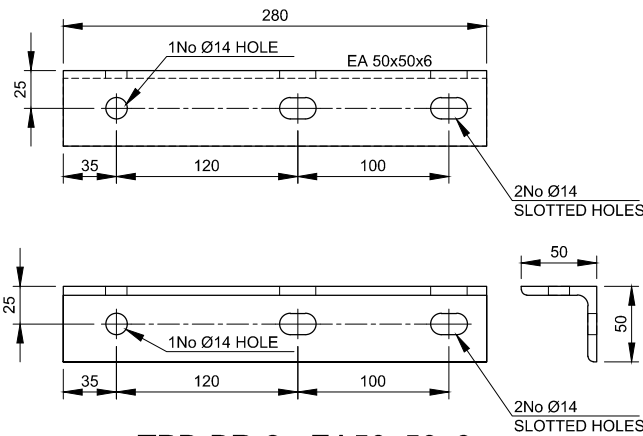

TPB-BR-2 - EA50x50x6
Scale 1:5

TPB-BR-3 - 10mm THICK
Scale 1:5

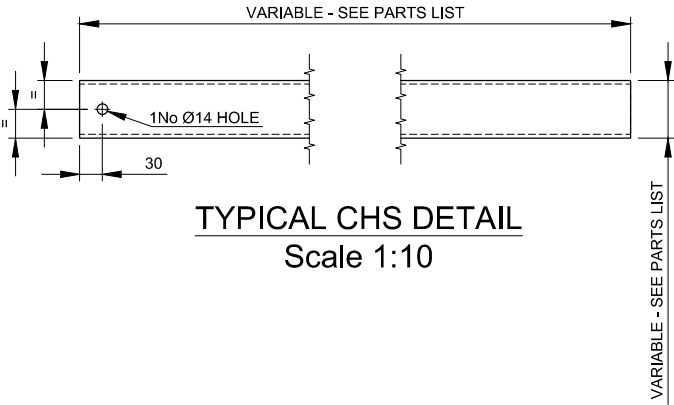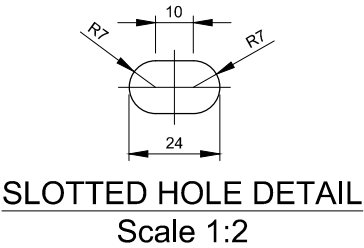


TYPICAL CHS DETAIL
Scale 1:10

Parts list for TPB-BR

Item	Part	Quantity	Part description	Length	Material	Weight
01	TPB-BR-1	1	EA 50x50x6	280mm	S275J0	1.25 kg
02	TPB-BR-2	1	EA 50x50x6	620mm	S275J0	2.80 kg
03	TPB-BR-3	1	Plate 130x190x10mm	N/A	S275J0	1.95 kg
04	BOLT	1	M12 SET BOLT - 30mm LONG	N/A	GRADE 8.8	-
05	N-BOLT	2	M12 N-BOLT FOR EA 50x50x6	N/A	GRADE 8.8	-
06	U-BOLT	2	M12 U-BOLT FOR CHS 76.1mm	N/A	GRADE 8.8	-
Total Weight:						6.00 kg

- All steel hot dip galvanized
- Each BOLT to be supplied with 1 Full Nut, 1 Form E FLat Washer and 1 Spring Washer
- Each STUD & U-BOLT to be supplied with 4 Full Nuts, 2 Flat Washers and 2 Spring Washers
- For fabrication notes see drawing 305

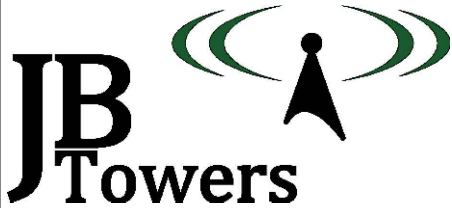


02	SITE NAME ADDED TO DRAWING TITLE			AM	28/04/20	
01	FIRST ISSUE			AM	23/04/20	
REV	REV			BY	DATE	
SCALE AS SHOWN	DRAWN	AM	CHECKED	MP	APPROVED	JBT
WHEN PRINTED AT A3	DATE	23/04/20	DATE	23/04/20	DATE	23/04/20
ALL DIMENSIONS IN mm UNLESS OTHERWISE STATED. THIS DRAWING TO BE READ IN CONJUNCTION WITH OTHER RELEVANT DRAWINGS.						

TITLE
WALL
BRACING ARM & TYPICAL
CHS DETAIL
PART: TPB-BR

SITE ADDRESS THISTLE RIGGS FARM HOMER'S LANE WARDEN, HEXHAM NORTHUMBERLAND NE46 4SR		
ARQIVA REF. 141756	DRG No. 303	REV 02



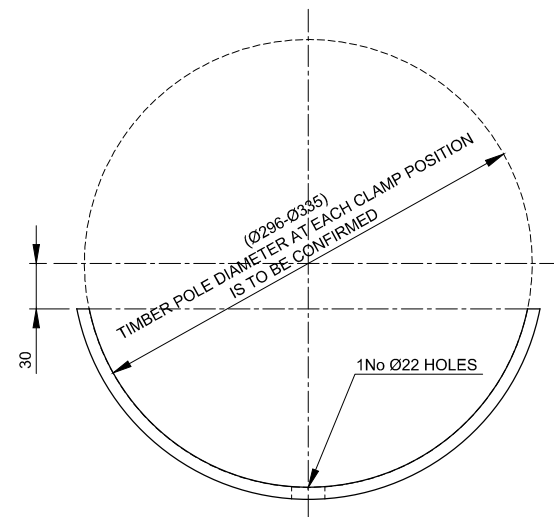

TPC-A-3 - 100x8mm PLATE
Scale 1:5



Technical drawing of a vertical plate with the following dimensions and features:

- Overall height: 1075
- Overall width: 150
- Top edge: 50
- Top edge chamfer: 75
- Vertical dimensions from top: 200, 400, 375
- Four circular holes are spaced vertically along the centerline.
- Feature callout: 4No 22x32mm SLOTTED HOLES
- Bottom edge chamfer: R10 TYP

Technical drawings of a mechanical part, showing front and side views with dimensions and annotations.

Front View (Left):

- Overall width: 60
- Overall height: 100
- Top-left corner: Radius R5
- Bottom-left corner: Radius R5
- Central hole: 1 No Ø18 HOLE
- Distance from bottom edge to hole center: 50
- Distance from right edge to hole center: 30

Side View (Right):

- Overall width: 92 - INDICATIVE
- Overall height: 80
- Top edge: Chamfer 10x10
- Top-left corner: Radius R5
- Bottom-left corner: Radius R5
- Bottom-right corner: Radius R5
- Distance from top edge to start of chamfer: 25
- Distance from bottom edge to start of chamfer: 55
- Distance from left edge to start of chamfer: 40
- Distance from left edge to end of chamfer: 50
- Distance from left edge to hole center: 55
- Distance from hole center to right edge: VARIABLE TO FIT RADIUS min 10mm
- Surface finish: TBC (To Be Confirmed)

TPC-A-2 - 10mm THICK
Scale 1:2

Parts list for TPC-B - 1No SET OF 2No INTERFACE PLATES (2No SETS REQUIRED)

Item	Part	Quantity	Part description	Length	Material	Weight
01	TPC-B	2	PLATE 1075x150x15mm	N/A	S275J0	19.00 kg
02	STUD	4	M20 STUD	500mm	GRADE 8.8	1.25 kg
03	SQ-WSH	6	M20 50x50x3mm SQUARE WASHER	N/A	GRADE 8.8	-
- All steel hot dip galvanized					Total Weight:	43.00 kg

- All steel hot dip galvanized
- Each STUD to be supplied with 2 Full Nuts, 2 Half Nuts, 2 Flat Washers and 2 Spring Washers
- For fabrication notes see drawing 305



02	SITE NAME ADDED TO DRAWING TITLE			AM	28/04/20
01	FIRST ISSUE			AM	23/04/20
REV	REV			BY	DATE
SCALE AS SHOWN WHEN PRINTED AT A3		DRAWN AM DATE 23/04/20	CHECKED MP DATE 23/04/20	APPROVED JB DATE 23/04/20	
ALL DIMENSIONS IN mm UNLESS OTHERWISE STATED. THIS DRAWING TO BE READ IN CONJUNCTION WITH OTHER RELEVANT DRAWINGS.					

SITE ADDRESS

THISTLE RIGGS FARM
HOMER'S LANE
WARDEN, HEXHAM
NORTHUMBERLAND
NE46 4SR

ARQIVA REF. 141756	DRG No. 304	REV 02
------------------------------	-----------------------	------------------

ALL SCALES AS SHOWN WHEN PRINTED AT A3



ALL SCALES AS SHOWN WHEN PRINTED AT A3


NOTE:
2No. EXTENDED WIRE GUIDES - PART NO. 35397-00
3No. REGULAR WIRE GUIDES - PART NO. 30050-00

Item	Part	Drawing	Quantity	Part description	Length	Material	Weight
01	01	200	1	3 MAN LATCHWAY SYSTEM & *5No. WIRE GUIDES FOR FACE MOUNTED MONOPOLE (SEE NOTES)	17000	N/A	-
02	TPB-C	300	2	FALL ARREST ATTACHMENT POINT	N/A	S275J0	4.48 kg
03	03	200	48	PERMANENT BT STEP c/w 3No 10x75mm ZINC-PLATED COACH SCREWS	N/A	S275J0	14.40 kg
04	TPS-R	300	9	'MonoStep' ASSEMBLY	N/A	S275J0	21.69 kg
05	TPB-B	301	3	MOUNTING BRACKET	N/A	S275J0	34.00 kg
06	TPB-BR	303	2	BRACING ARM	N/A	S275J0	12.00 kg
07	07	203	12	M12 WASHER	N/A	GRADE 8.8	-
08	08	203	2	CHS 76.1x5mm	2500mm	S355J2H	43.90 kg
09	TPL-A	302	4	LOG MOUNTING BRACKET	940mm	S275J0	42.00 kg
10	TPL-B	302	4	LOG MOUNTING BRACKET	940mm	S275J0	42.00 kg
11	TPA-PD	301	6	POWER DIVIDER STRAP	N/A	S275J0	7.56 kg
12	12	204	1	CHS 76.1x5mm	1000mm	S355J2H	8.80 kg
13	TPL-C	302	1	LOG MOUNTING BRACKET	150mm	S275J0	2.05 kg
14	TPC-A	304	6	TIMBER POLE SPLICE COLLAR	N/A	S275J0	67.44 kg
15	TPC-B	304	2	TIMBER POLE SPLICE INTERFACE PLATE	N/A	S275J0	86.00 kg
16	16	205	1	M20 STUD C/W 4No NUTS & 2No SQ WSH	450mm	GRADE 8.8	1.11 kg
17	17	200	1	PoleSaver	750mm	N/A	-
18	18	200	8	M12 STUD + 4No NUTS + 2No FLAT WASHERS + 1No Ø50mm WASHER (FOR FALL ARREST SYSTEM)	500mm	GRADE 8.8	3.56 kg
Total Weight:							391.00 kg

- All steel hot dip galvanized
- All U-BOLTS to be FLA supply, each Supplied with 4 Full Nuts, 2 Flat Washers and 2 Spring Washers

NOTES:

1. WELDING TO BE IN ACCORDANCE WITH BS EN 1011-1:2009
2. LINEAR DIMS TO BE WITHIN ±1mm;
3. ANGULAR TOLERANCES TO BE WITHIN 0.5°
4. WELDING SYMBOLS ARE IN ACCORDANCE WITH BS EN 22553:1995
5. ALL PROFILE EDGES TO BE DRESSED AND SHARP CORNERS REMOVED
6. ALL WELD SIZES ARE FINAL SIZES
7. ALL WELDED JOINTS ARE TO BE PICKLE TIGHT
8. ALL STEELWORK TO BE BS EN 10025 GRADE S275 J0 UNO, HOT DIPPED GALVANISED TO BS EN ISO 1461. (ALL HOLLOW SECTIONS TO BE GRADE S355 J0H)
9. ALL STEEL IS TO BE SUPPLIED IN ACCORDANCE WITH EN 1090 TO EXECUTION CLASS 2
10. ALL NON PRE-LOADED BOLTS TO BE COMPLIANT STRUCTURAL BOLTS TO BS EN ISO 15048 PARTS 1&2.
11. STEELWORK COMPONENTS SHALL BE HOT DIP GALVANISED TO ACHIEVE A "VERY HIGH" DURABILITY FOR AN ENVIRONMENT CATEGORY CODE C4 FROM TABLE 1 IN BS EN ISO 14713
12. BOLTS AND NUTS SHALL BE SUPPLIED IN ACCORDANCE WITH BS 7371, SPUN GALVANISED IN ACCORDANCE WITH ISO 10684, THE NUTS RE-TAPPED AFTER GALVANISING, AND THE THREADS TREATED WITH GREASE.
13. ALL BOLTS TO BE CUT ON SITE TO EXTEND MAX 10mm BEYOND THE NUT WHEN TIGHTENED UNO.
14. ALL SITE DRILLED HOLE/CUT ENDS TO BE TREATED WITH METAFLUX 70-40 ZINC PASTE FOLLOWED BY 1 COAT OF 7-42 ZINC ALU OR 70-16 ALUMINIUM SPRAY

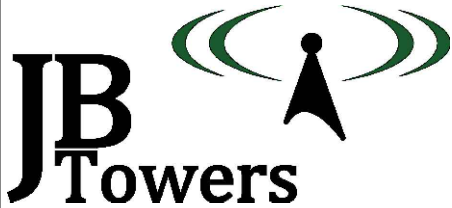

02	SITE NAME ADDED TO DRAWING TITLE			AM	28/04/20
01	FIRST ISSUE			AM	23/04/20
REV	REV			BY	DATE
SCALE AS SHOWN		DRAWN	AM	CHECKED	MP
WHEN PRINTED AT A3		DATE	23/04/20	DATE	23/04/20
ALL DIMENSIONS IN mm UNLESS OTHERWISE STATED. THIS DRAWING TO BE READ IN CONJUNCTION WITH OTHER RELEVANT DRAWINGS.					

TITLE

WALL

PARTS LIST

SITE ADDRESS

THISTLE RIGGS FARM
HOMER'S LANE
WARDEN, HEXHAM
NORTHUMBERLAND
NE46 4SR

ARQIVA REF.
141756



DRG No.
305

REV
02

ALL SCALES AS SHOWN WHEN PRINTED AT A3






ALL SCALES AS SHOWN WHEN PRINTED AT A3

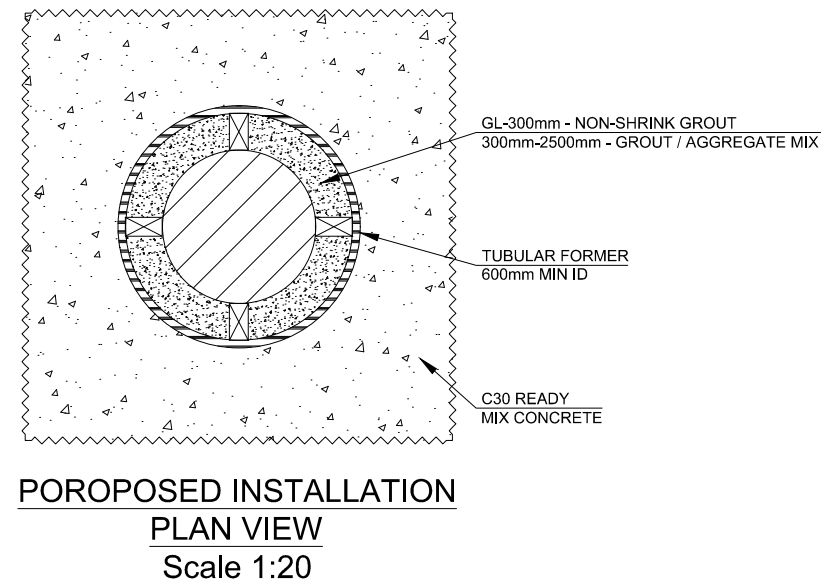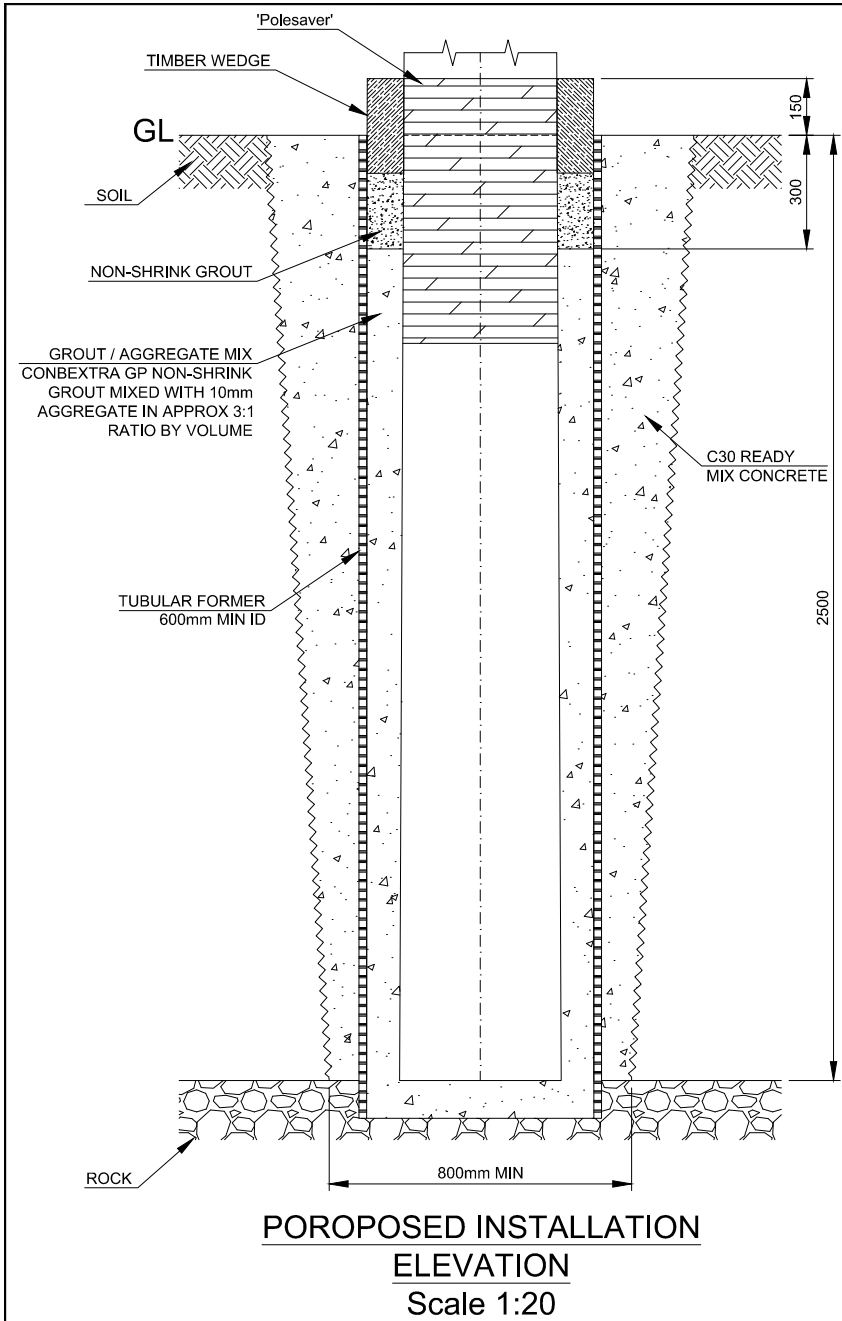


TIMBER POLE INSTALLATION:

1. REFER TO DRAWING 200 FOR TIMBER POLE ORIENTATION
2. EXCAVATE A HOLE MIN. 800mm SQUARE TO A DEPTH OF 2500mm
3. INSERT FORMER WITH APPROPRIATE SUPPORT TO ENSURE IT HOLDS ITS SHAPE
4. SLOWLY POUR CONCRETE TO FILL ANNULUS BETWEEN HOLE & FORMER
5. POLE TO BE WRAPPED IN 'POLESAVER' AND INSTALLED AND LEVELLED IN OPENING. TIMBERS TO BE USED TO HOLD POLE IN POSITION
6. ANNULUS SHALL BE FILLED WITH GROUT / AGGREGATE MIX TO 300mm BELOW GL
7. TOP 300mm SHALL BE FILLED WITH NON-SHRINK GROUT. A 1:60 FALL SHALL BE FORMED AROUND TIMBER POLE TO ALLOW WATER TO DRAIN AWAY FROM POLE
8. ONCE GROUT HAS CURED REMOVE TIMBER WEDGES AND FILL REMAINING VOIDS WITH NON-SHRINK GROUT

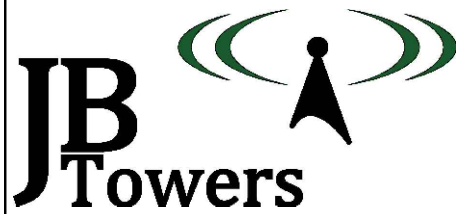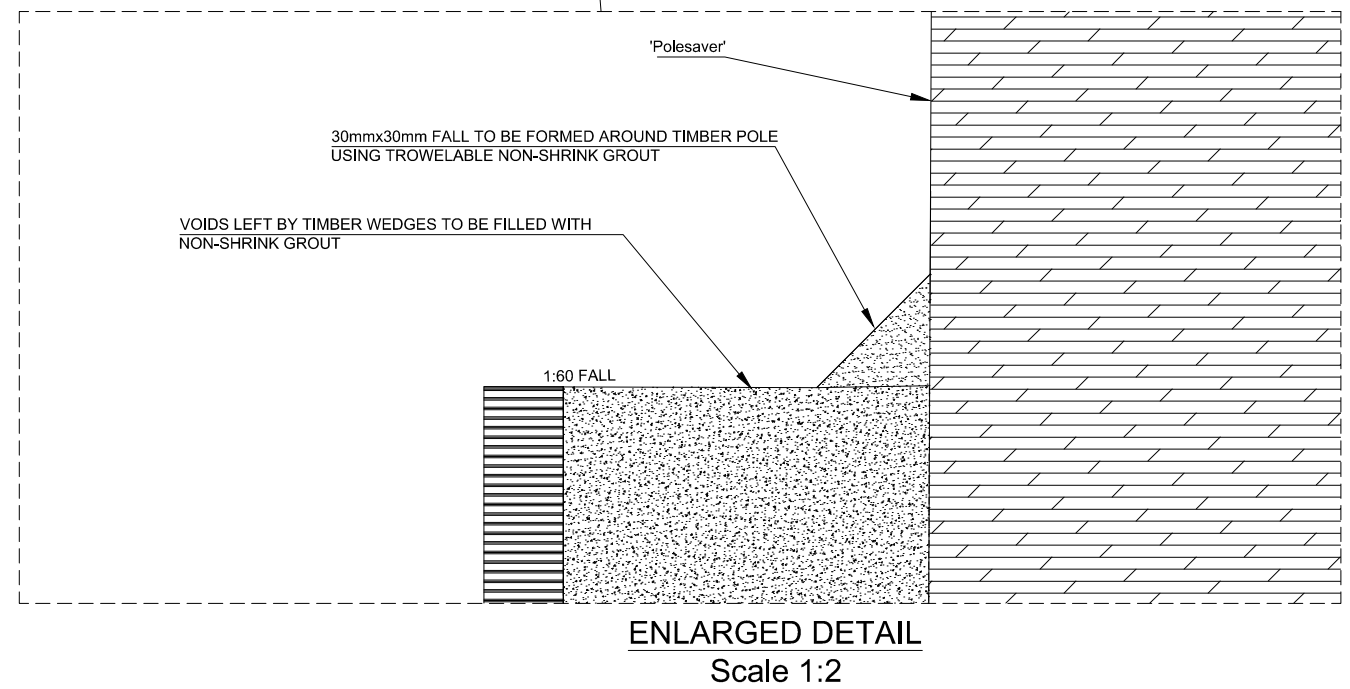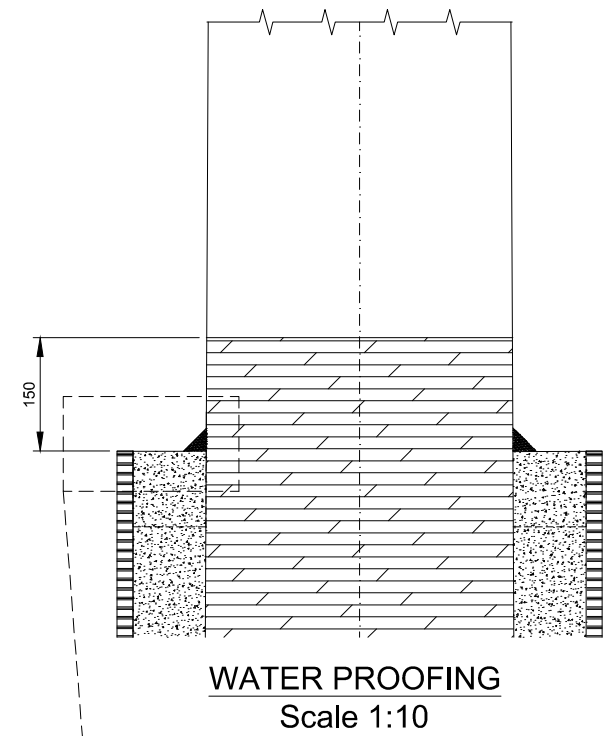

02	SITE NAME ADDED TO DRAWING TITLE			AM	28/04/20
01	FIRST ISSUE			AM	23/04/20
REV	REV			BY	DATE
SCALE AS SHOWN WHEN PRINTED AT A3		DRAWN	AM	CHECKED	MP
		DATE	23/04/20	DATE	23/04/20
ALL DIMENSIONS IN mm UNLESS OTHERWISE STATED. THIS DRAWING TO BE READ IN CONJUNCTION WITH OTHER RELEVANT DRAWINGS.					

TITLE		SITE ADDRESS		
WALL		THISTLE RIGGS FARM		
TIMBER POLE FOUNDATION DETAILS		HOMER'S LANE		
		WARDEN, HEXHAM		
		NORTHUMBERLAND		
		NE46 4SR		
ARQIVA REF.		DRG No.	REV	
141756		400	02	

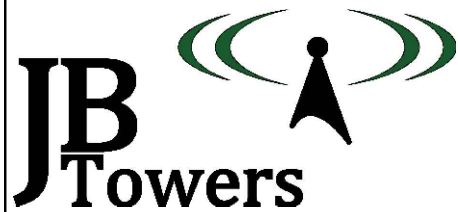

arqiva

01	FIRST ISSUE			AM	23/04/20
REV	REV			BY	DATE
SCALE AS SHOWN WHEN PRINTED AT A3	DRAWN	AM	CHECKED	MP	APPROVED
	DATE	23/04/20	DATE	23/04/20	DATE
ALL DIMENSIONS IN mm UNLESS OTHERWISE STATED. THIS DRAWING TO BE READ IN CONJUNCTION WITH OTHER RELEVANT DRAWINGS.					

TITLE


WALL

PERMANENT STEPS
ENLARGED DETAIL


SITE ADDRESS

THISTLE RIGGS FARM
HOMER'S LANE
WARDEN, HEXHAM
NORTHUMBERLAND
NE46 4SR

ARQIVA REF.
141756

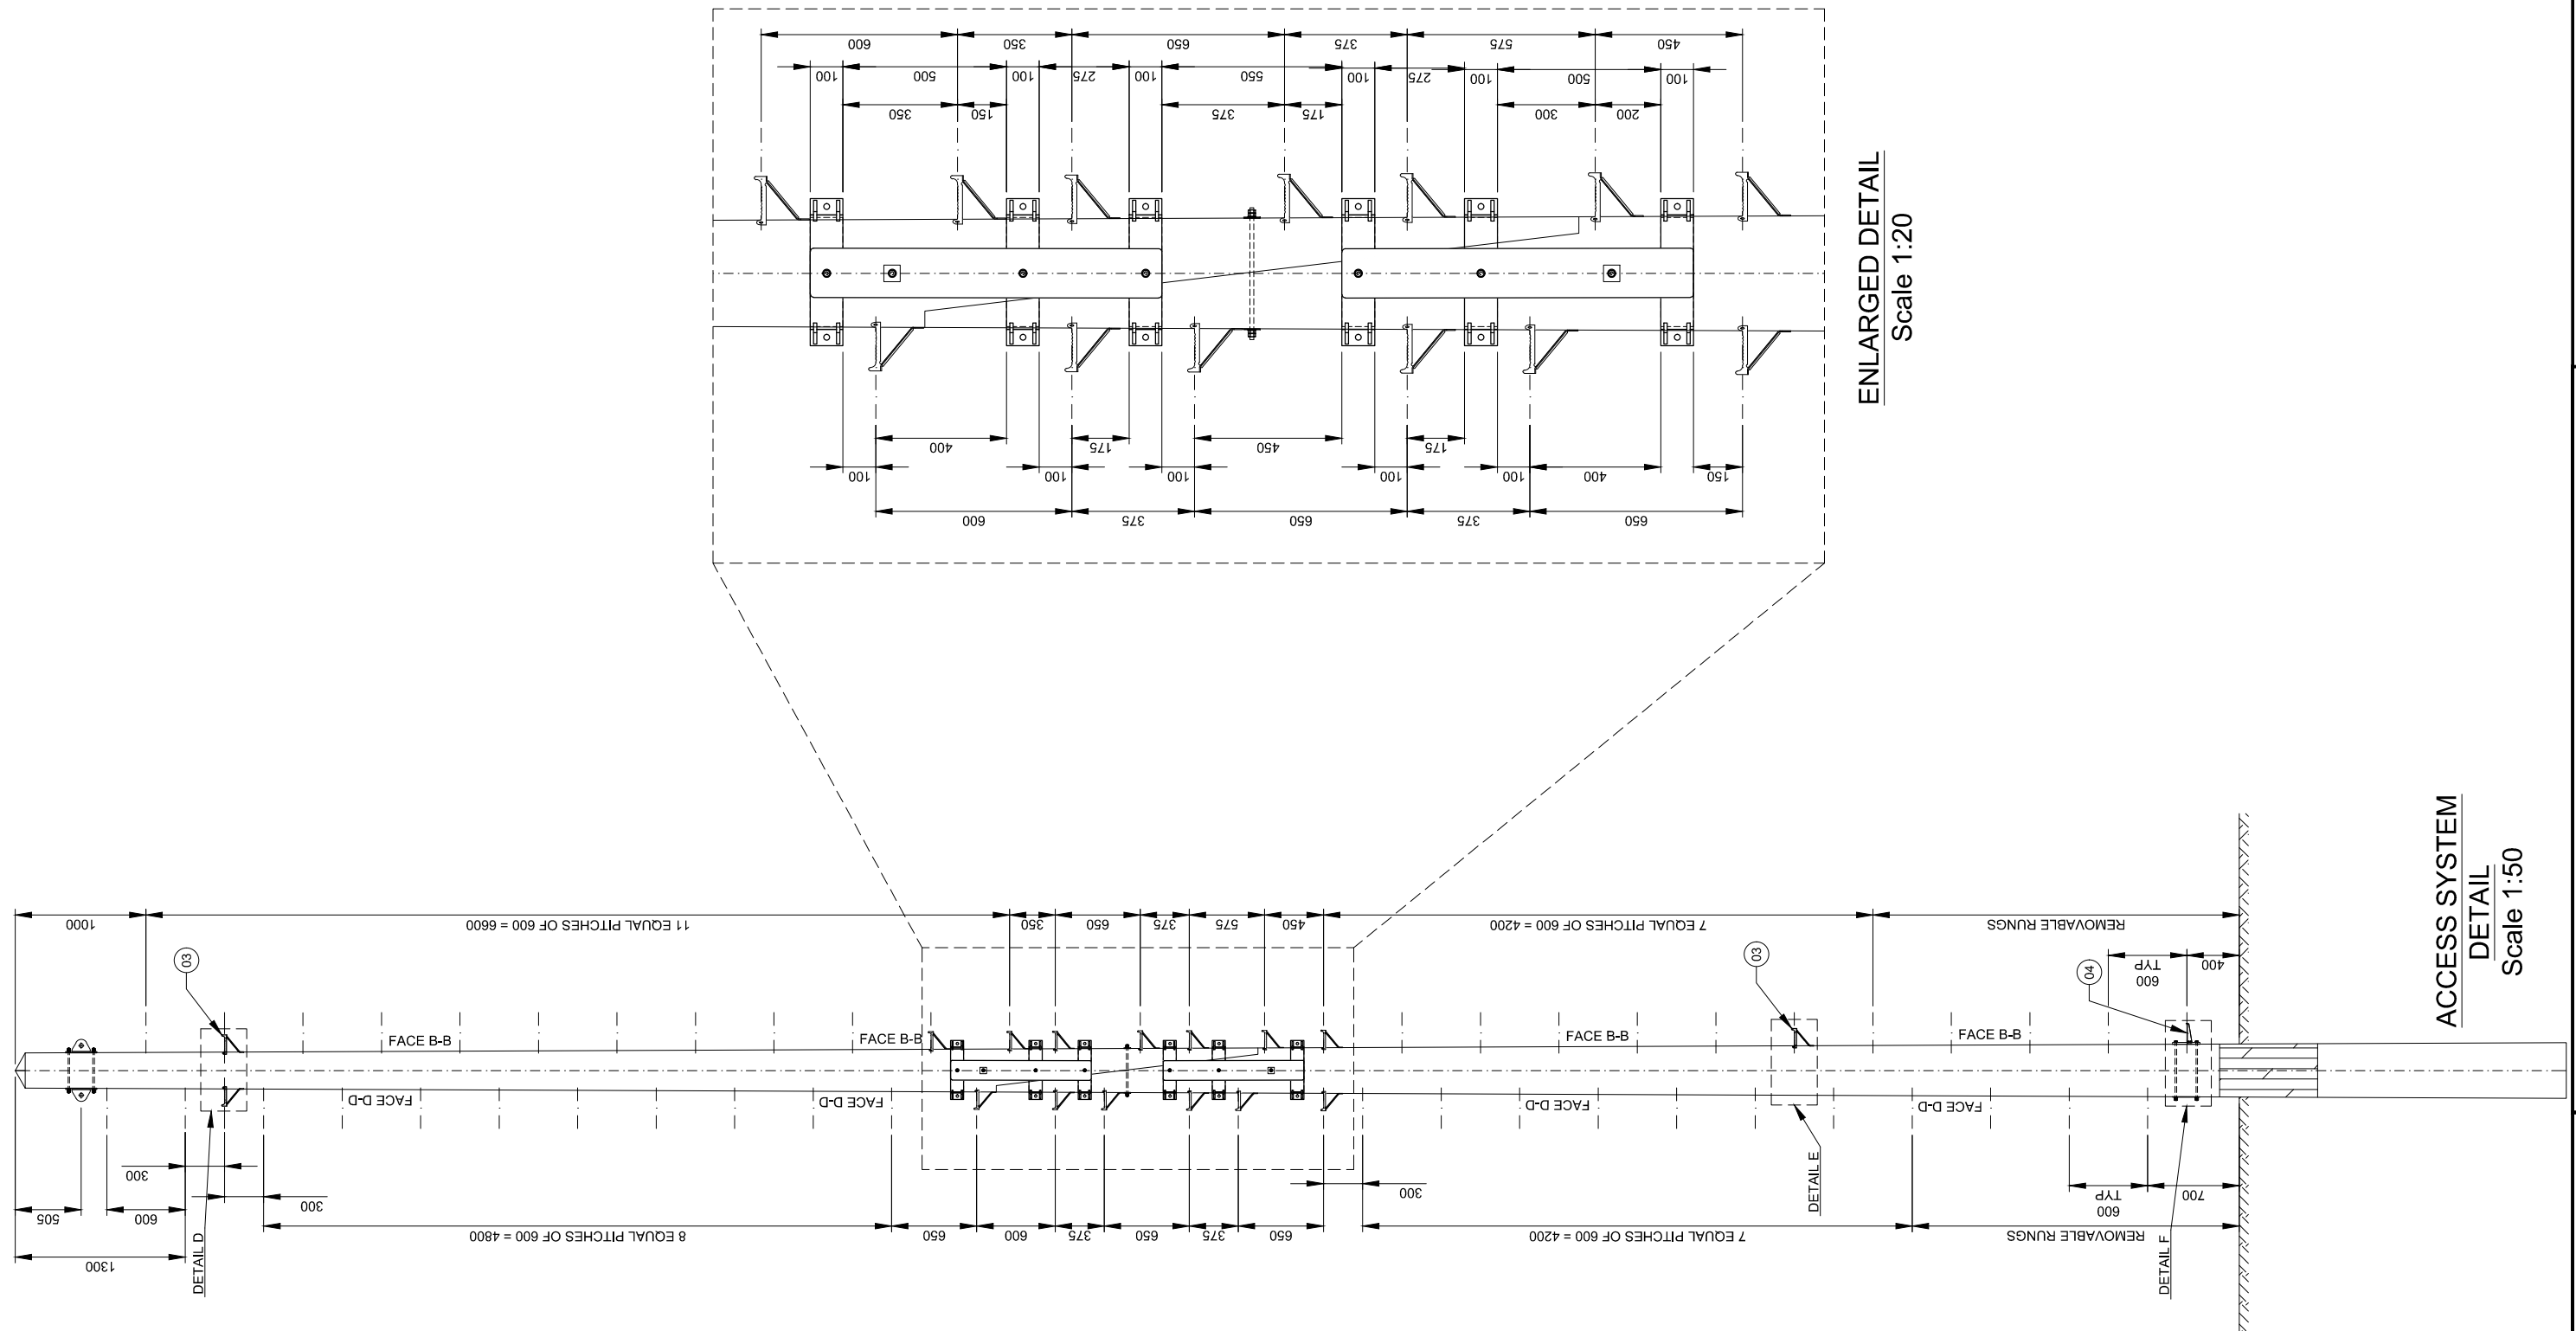DRG No.
401REV
01

ALL SCALES AS SHOWN WHEN PRINTED AT A3

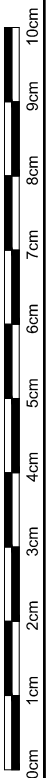

ALL SCALES AS SHOWN WHEN PRINTED AT A3