
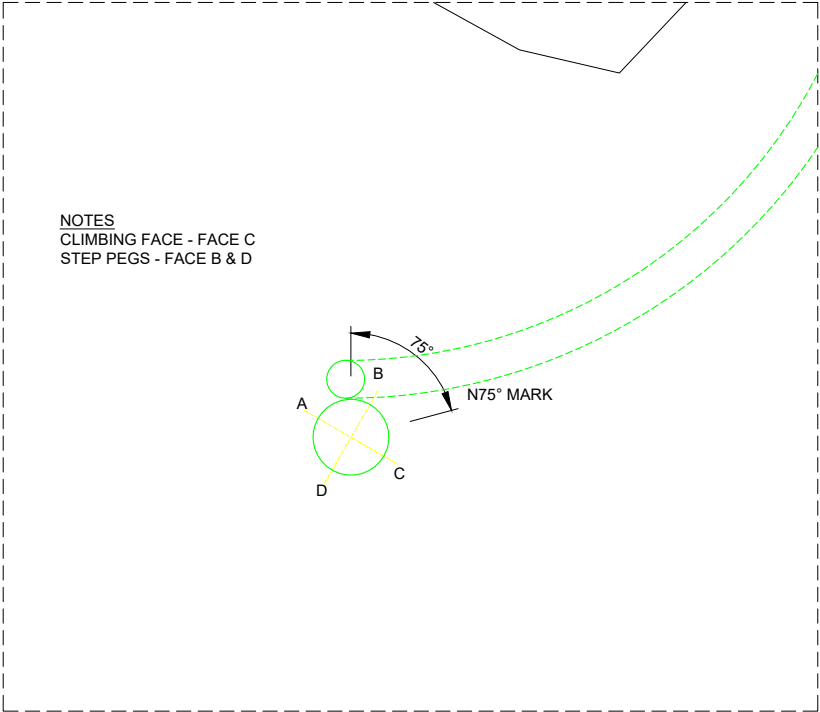


DRAWING ISSUE SHEET


[illegible]

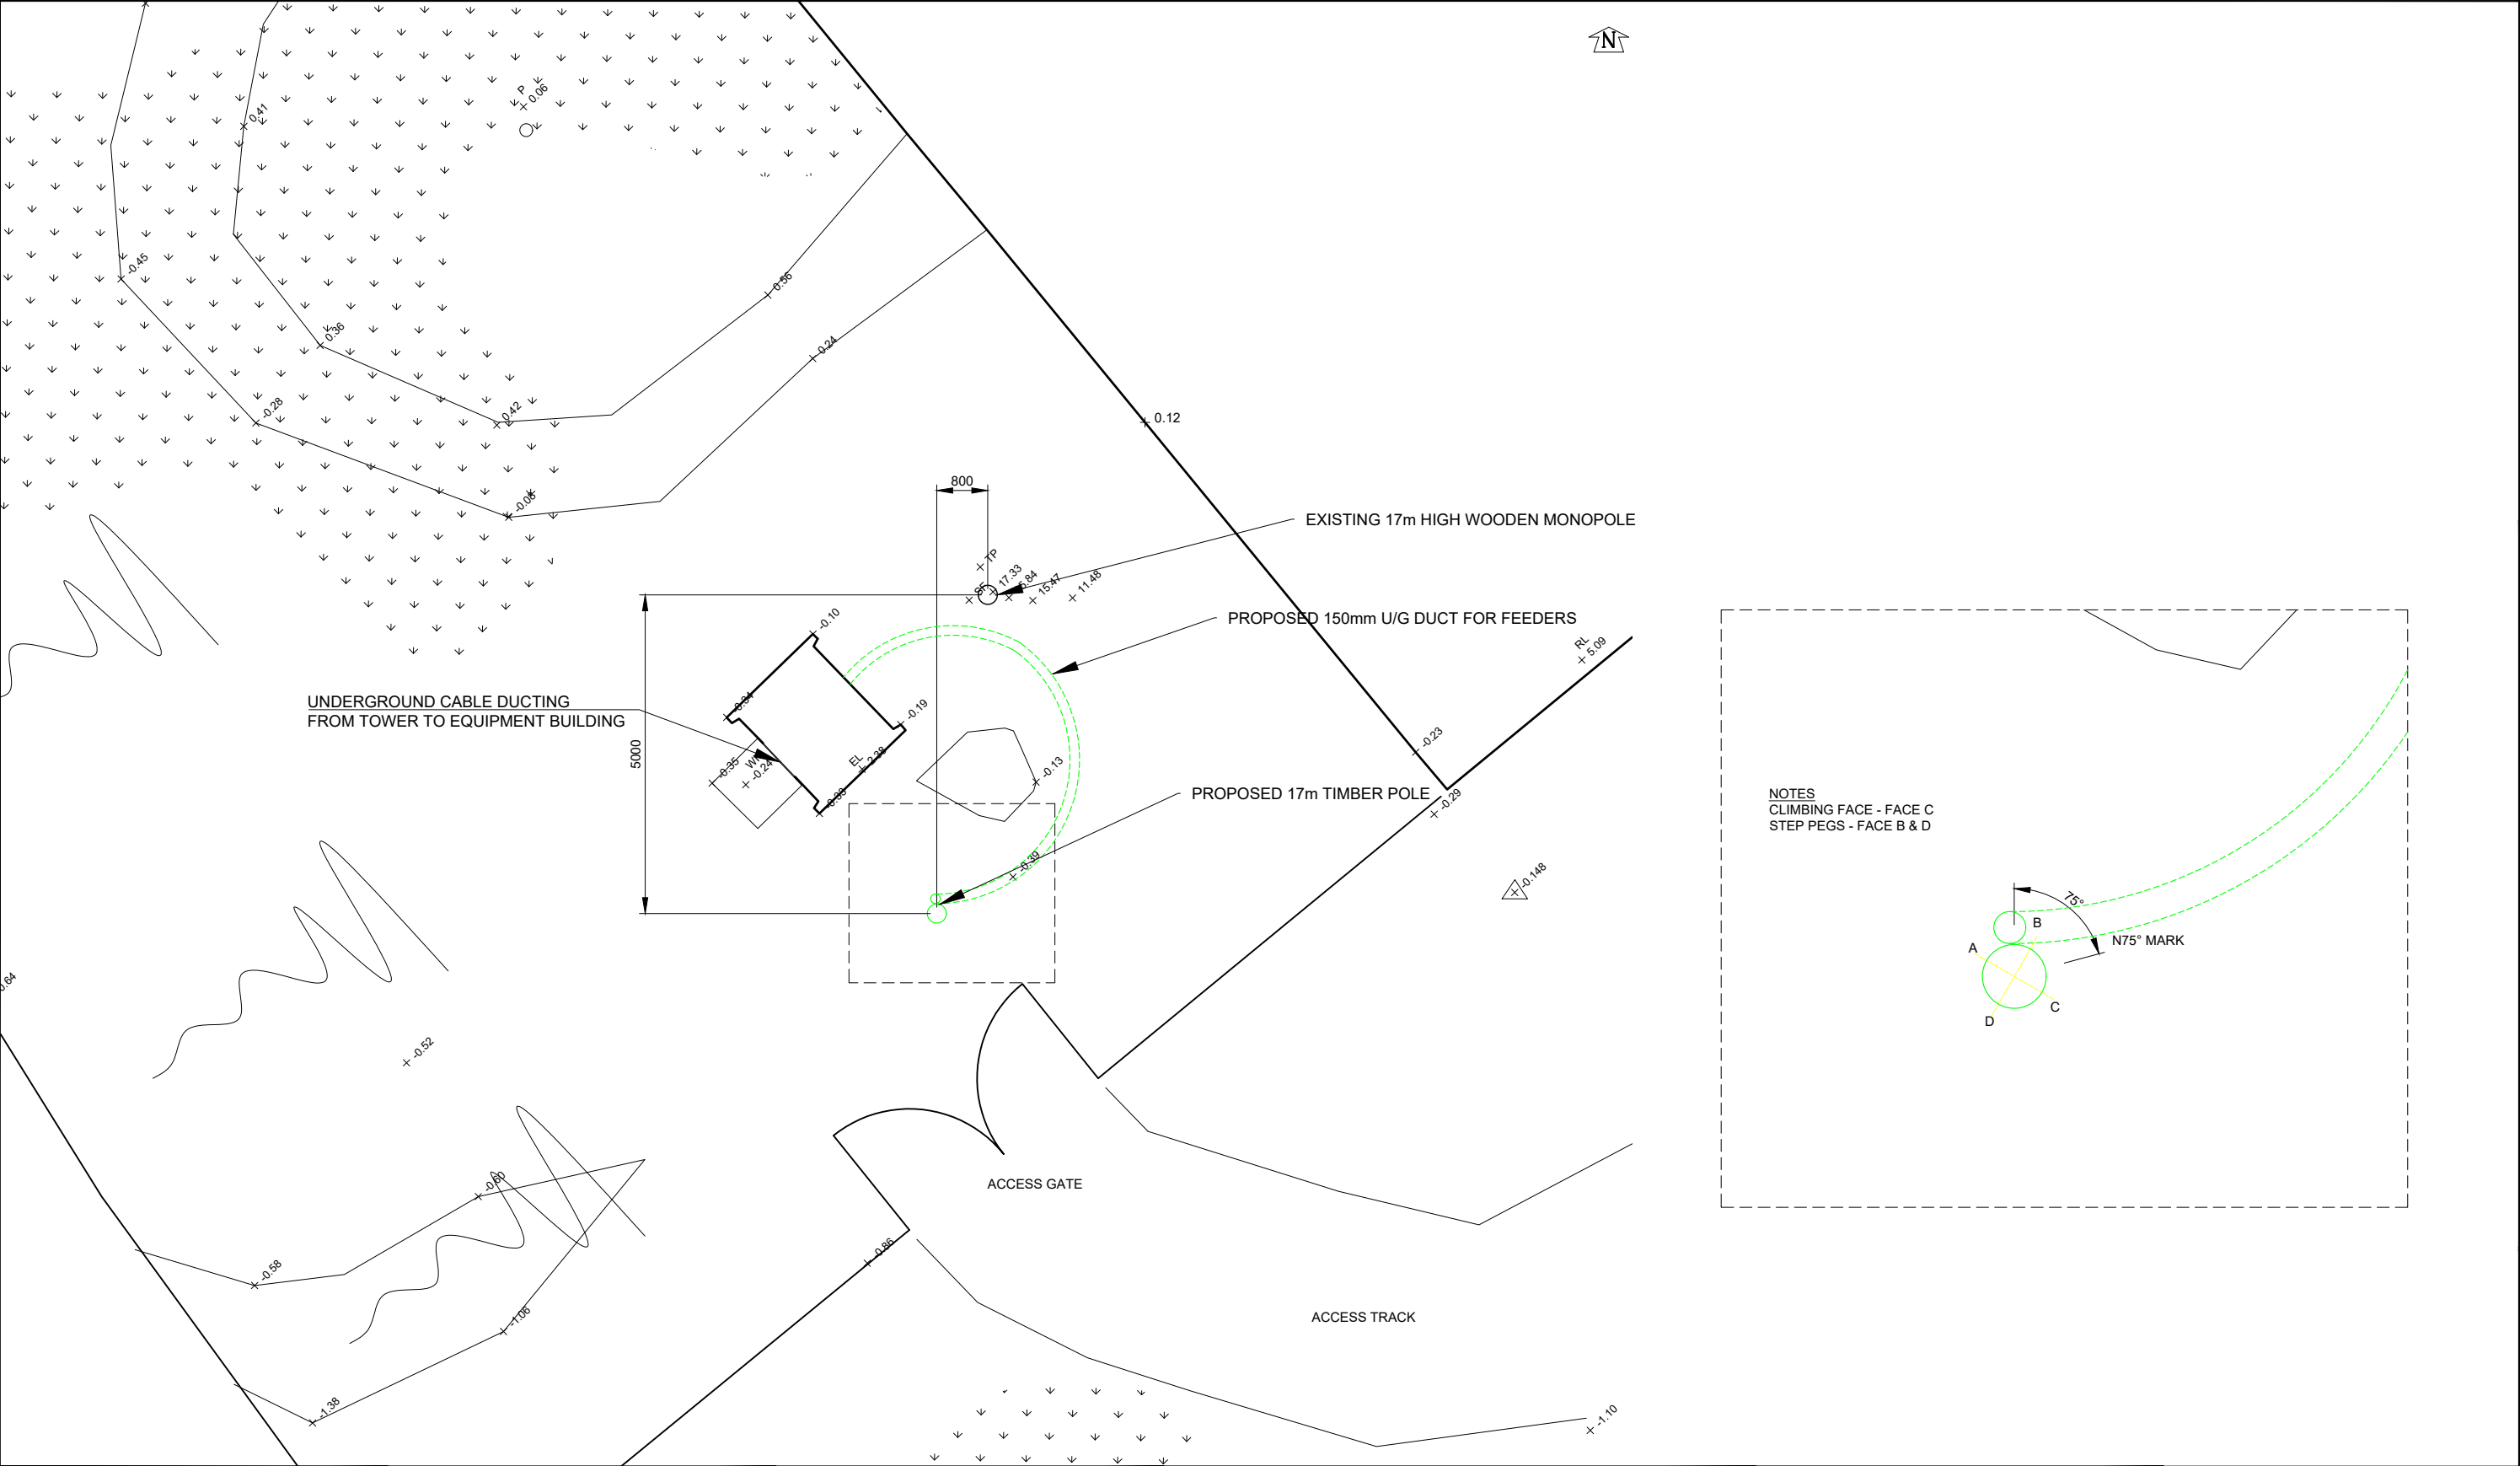

											TITLE WESTER ERCHITE SITE PLAN	SITE ADDRESS WESTER ERCHITE DORES, INVERNESS HIGHLAND IV2 6TX		
01		FIRST ISSUE						TT	03/06/19					
REV		REV						BY	DATE					
SCALE AS SHOWN		DRAWN		AM		CHECKED		MP		APPROVED		JBT		
WHEN PRINTED AT A3		DATE		03/06/19		DATE		03/06/19		DATE		03/06/19		
ALL DIMENSIONS IN mm UNLESS OTHERWISE STATED. THIS DRAWING TO BE READ IN CONJUNCTION WITH OTHER RELEVANT DRAWINGS.														

ARQIVA REF. 141776		DRG No. 100	REV 01
-----------------------	--	----------------	-----------

ALL SCALES AS SHOWN WHEN PRINTED AT A3

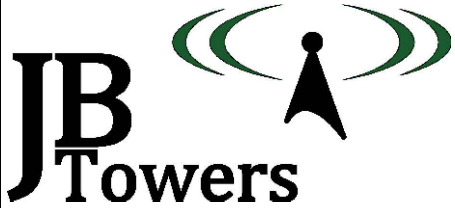

01	FIRST ISSUE			TT	03/06/19
REV	REV			BY	DATE
SCALE AS SHOWN		DRAWN	AM	CHECKED	MP
WHEN PRINTED AT A3		DATE	03/06/19	DATE	03/06/19
		APPROVED	JBT	DATE	03/06/19
ALL DIMENSIONS IN mm UNLESS OTHERWISE STATED. THIS DRAWING TO BE READ IN CONJUNCTION WITH OTHER RELEVANT DRAWINGS.					

TITLE

WESTER ERCHITE

GENERAL ARRANGEMENT

SHEET 1 OF 3

SITE ADDRESS

WESTER ERCHITE

DORES, INVERNESS

HIGHLAND

IV2 6TX

ARQIVA REF.



141776

DRG No.

200

REV

01

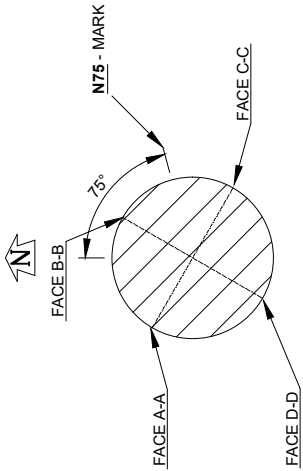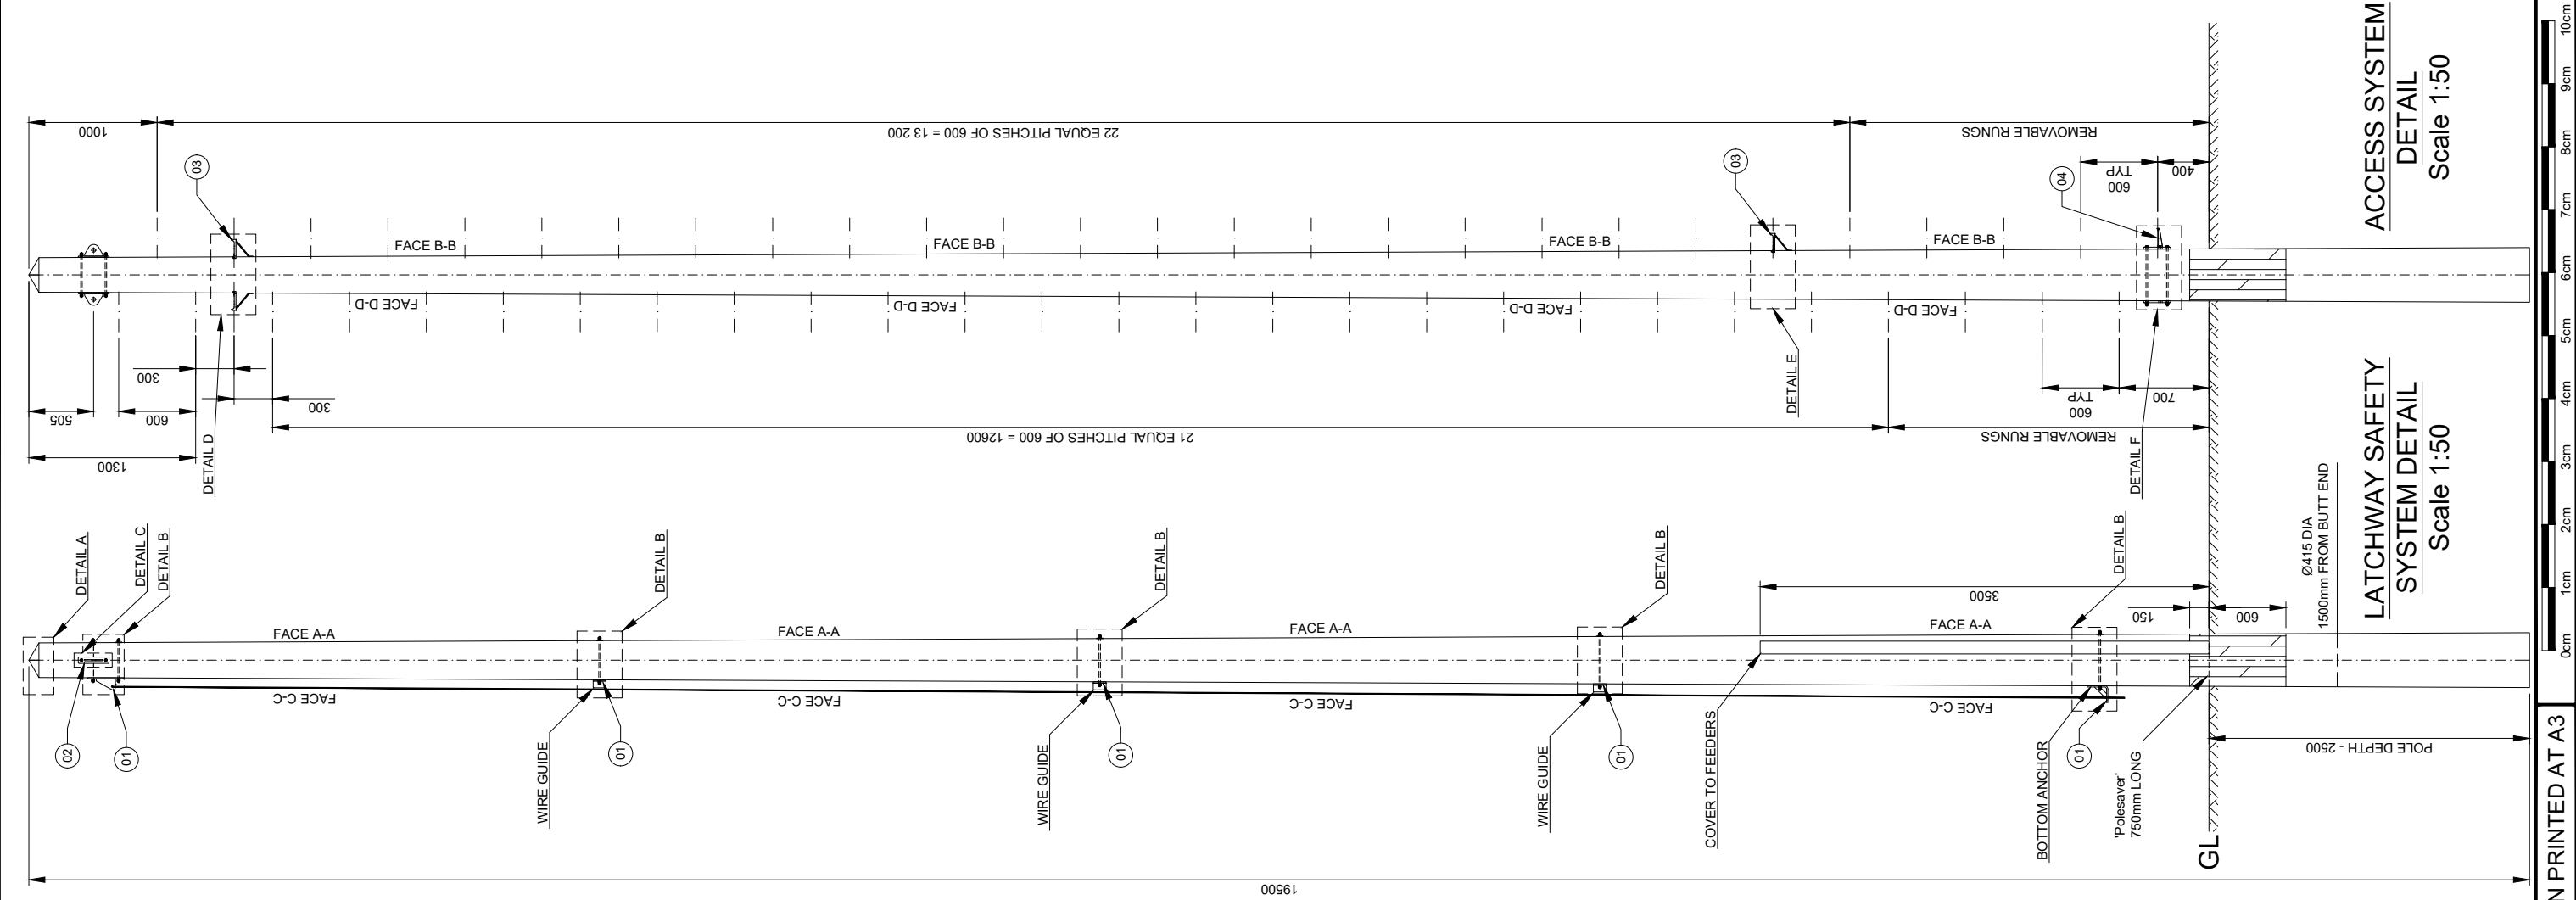

POLE ORIENTATION

Scale 1:20

NOTES

1. SEE DRAWING 305 FOR PARTS LIST
2. ALL BOLTS TO BE CUT ON SITE TO EXTEND MAX 10mm BEYOND THE NUT WHEN TIGHTENED UNO.
3. ALL SITE DRILLED HOLE/CUT ENDS TO BE TREATED WITH METALUX 70-40 ZINC PASTE FOLLOWED BY 1 COAT OF 7-42 ZINC ALU OR 70-16 ALUMINIUM SPRAY

TIMBER POLE

1. POLE TO BE SUPPLIED IN ACCORDANCE WITH BS EN14229 & SHALL HAVE MIN. CHARACTERISTIC BENDING STRENGTH OF 30N/mm2 & MIN. YOUNGS MODULUS (PARALLEL TO GRAIN) OF 10KN/mm2.
2. MARKINGS ON FINISHED POLE SHALL BE AT 4m FROM BUTT AND COMPLY WITH BS EN 14229 UNO
3. AS FAR AS PRACTICABLE ALL CUTTING, SCARFING & DRILLING TO BE DONE BEFORE CREOSOTING. IF NOT ALL CUT, DRILLED & SCARFED SURFACES TO BE COATED WITH A MIXTURE OF CREOSOTE & TAR.
4. POLE TO BE PRESSURE IMPREGNATED WITH CREOSOTE IN ACCORDANCE WITH BS EN 14229
5. MINIMUM DIAMETERS
TOP - Ø206mm
BOTTOM - Ø430mm
6. 19.5m LONG POLE TO BE SOURCED BY TRIMMING 20m LONG POLE BY 0.5m AT THE TOP

PLANTING

1. CAT SCANNER IS TO BE USED IN ORDER TO CONFIRM THE POSITIONS OF BURIED SERVICES.
2. 'Perma-Soil Stabiliser' OR A SIMILAR APPROVED SHOULD BE USED IN ACCORDANCE WITH THE MANUFACTURER'S RECOMMENDATION.
3. ANY MATERIAL USED FOR BACK-FILLING IS TO BE OF EQUAL OR BETTER QUALITY THAN THE EXCAVATED MATERIAL.
4. ALL BACK-FILLING MATERIAL IS TO BE PLACED AND COMPACTED IN 150mm THICK LAYERS.
5. TIMBER POLE TO BE PLANTED WITH N75 MARKING AT 3.5m FROM BUTT FACING 75° FROM NORTH (CLOCKWISE)

ACCESS SYSTEM
DETAIL

Scale 1:50

LATCHWAY SAFETY
SYSTEM DETAIL

Scale 1:50

ALL SCALES AS SHOWN WHEN PRINTED AT A3



ALL SCALES AS SHOWN WHEN PRINTED AT A3

01	FIRST ISSUE				TT	03/06/19
REV	REV				BY	DATE
SCALE AS SHOWN		DRAWN	AM	CHECKED	MP	APPROVED JBT
WHEN PRINTED AT A3		DATE	03/06/19	DATE	03/06/19	DATE 03/06/19
ALL DIMENSIONS IN mm UNLESS OTHERWISE STATED. THIS DRAWING TO BE READ IN CONJUNCTION WITH OTHER RELEVANT DRAWINGS.						

TITLE
WESTER ERCHITE
GENERAL ARRANGEMENT
SHEET 2 OF 3






SITE ADDRESS
WESTER ERCHITE
DORES, INVERNESS
HIGHLAND
IV2 6TX

ARQIVA REF.
141776

DRG No.
200

REV
01

ALL SCALES AS SHOWN WHEN PRINTED AT A3

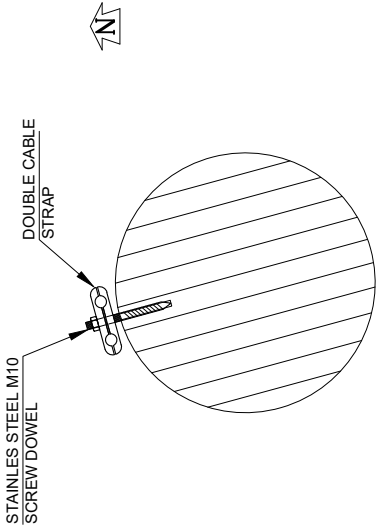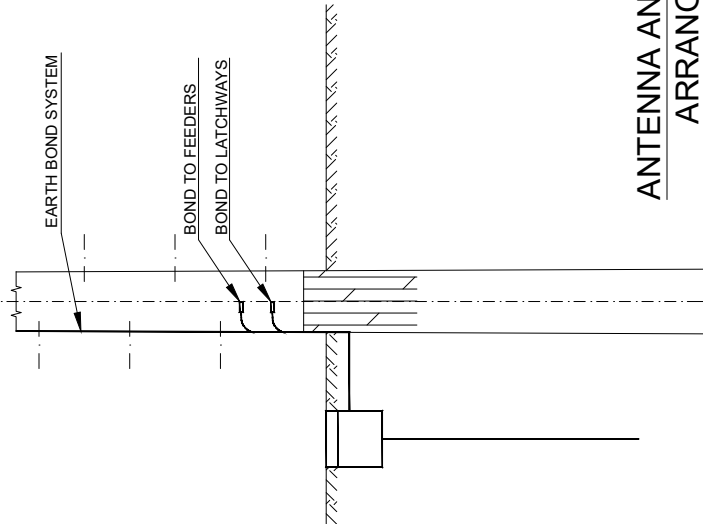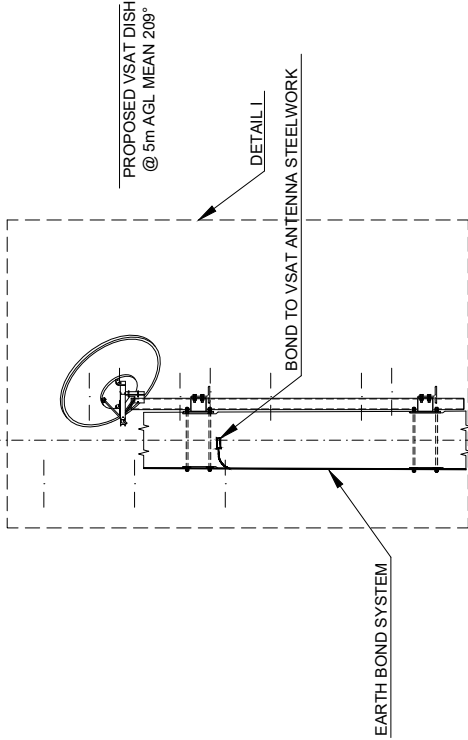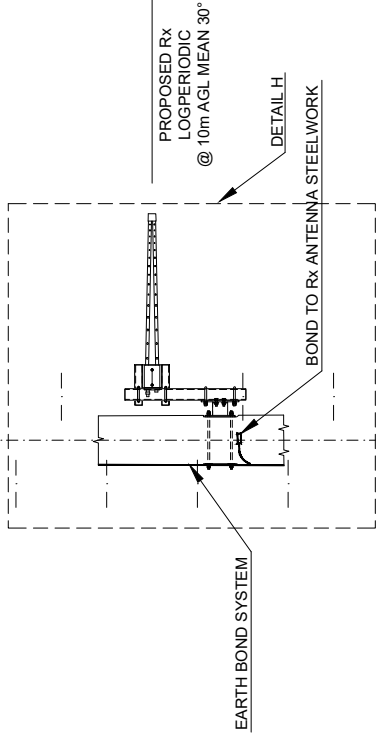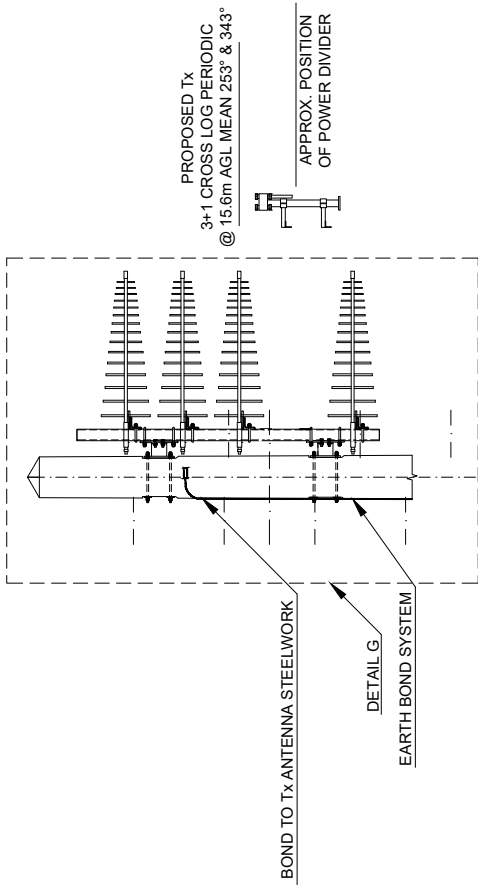

NOTES

1. AS FAR AS IS PRACTICABLE ALL CUTTING SCARFING AND DRILLING TO BE DONE BEFORE CREOSOTING. WHERE THIS IS NOT POSSIBLE ALL CUT, DRILLED, AND SCARFED SURFACES TO BE COATED WITH A MIXTURE OF CREOSOTE AND TAR


FEEDERS

1. SUPPLY OF FEEDERS BY OTHERS LCF78-50 TO Tx ANTENNA & LCF12-50 TO Rx ANTENNA UNKNOWN TO VSAT DISH (ARQIVA TO CONFIRM)

2. FEEDERS FIXED AT 1000mm CENTRES


EARTHING

1. CONNECT EARTH BOND TO NEW EARTHING SYSTEM
2. MAXIMUM VALUE FOR GROUND RESISTANCE TO BE 10 OHMS
3. CABLE OR TAPE TO BE FIXED TO POLE AT 1000mm CENTRES
4. EARTHING SHOULD COMPLY WITH ARQIVA'S DOCUMENT BOS147

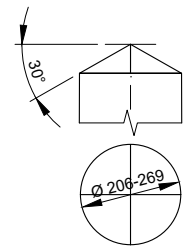


- NOTES:
1. A SINGLE COAT OF TIMBER COMPATIBLE BITUMINOUS PAINT (E.G. BIRD BRAND BLACK BITUMINOUS PAINT OR SIMILAR APPROVED PRODUCT) TO BE APPLIED TO THE UPPER SURFACES AT THE TOP OF THE POLE.
 2. PAINT TO BE APPLIED ON SITE JUST BEFORE ERECTION
- FORM: 4 WAY PYRAMID / CONE


DETAIL A - TIMBER POLE TOP
Scale 1:20

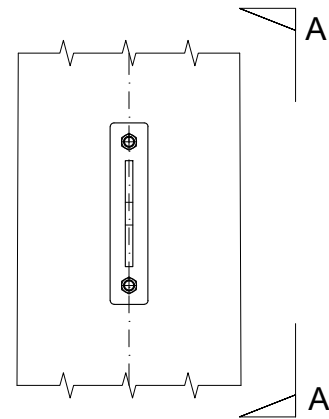


DETAIL C - FALL ARREST
ATTACHMENT POINT
Scale 1:10

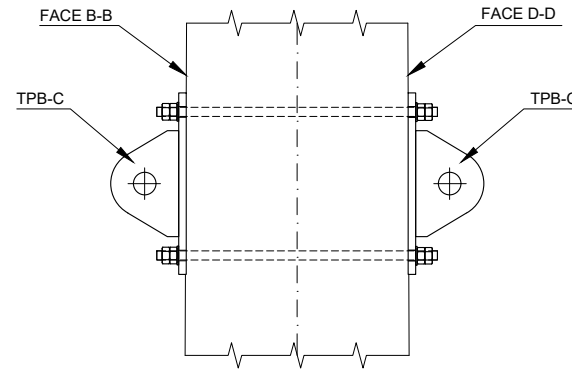


VIEW A-A
Scale 1:10

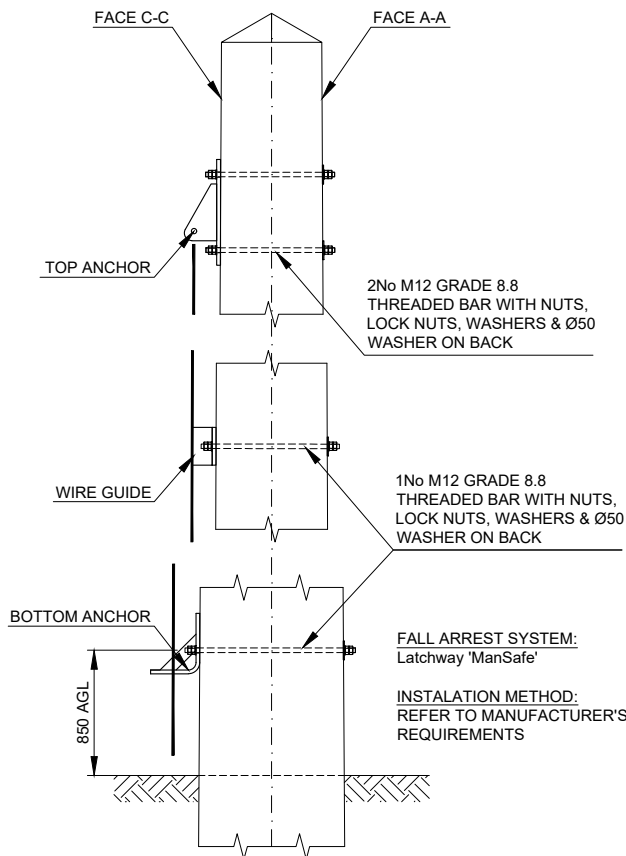

DETAIL B - FALL ARREST SYSTEM
Scale 1:20

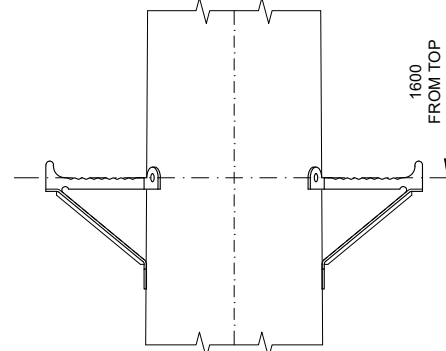


DETAIL D - ANTENNA
ACCESS CLIMBING STEP
Scale 1:10

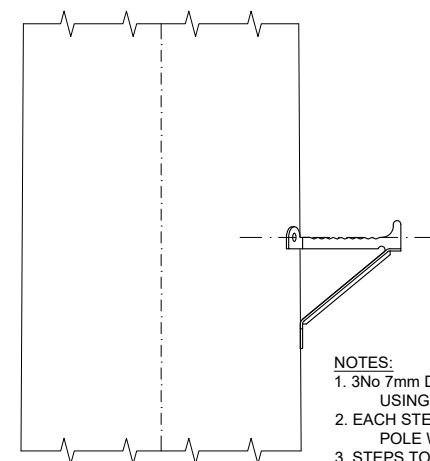


DETAIL E - PERMANENT
CLIMBING STEPS
Scale 1:10

- NOTES:
1. 3No 7mm DIA 70mm LONG PILOT HOLES TO BE DRILLED USING THE STEP AS A TEMPLATE
 2. EACH STEP SHOULD BE FIXED TO THE TIMBER POLE WITH 3No 10mm COACH SCREWS 75mm LONG
 3. STEPS TO BE INSTALLED ON FACES B-B & D-D ONLY

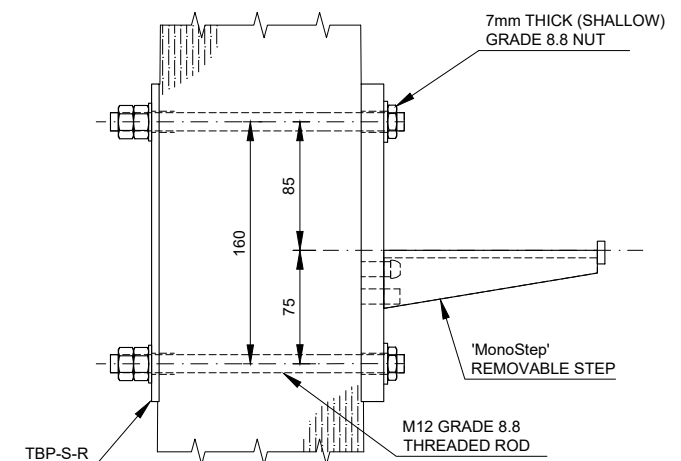

DETAIL F - REMOVABLE
CLIMBING STEPS
Scale 1:5

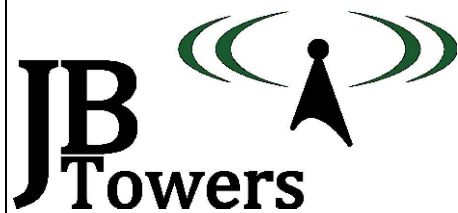

01	FIRST ISSUE	TT	03/06/19
REV	REV	BY	DATE
SCALE AS SHOWN WHEN PRINTED AT A3	DRAWN DATE 03/06/19	CHECKED DATE 03/06/19	APPROVED DATE 03/06/19
ALL DIMENSIONS IN mm UNLESS OTHERWISE STATED. THIS DRAWING TO BE READ IN CONJUNCTION WITH OTHER RELEVANT DRAWINGS.			

TITLE
WESTER ERCHITE
GENERAL ARRANGEMENT
SHEET 3 OF 3

SITE ADDRESS
WESTER ERCHITE
DORES, INVERNESS
HIGHLAND
IV2 6TX

ARQIVA REF.
141776


DRG No.
200

REV
01

ALL SCALES AS SHOWN WHEN PRINTED AT A3



ALL SCALES AS SHOWN WHEN PRINTED AT A3

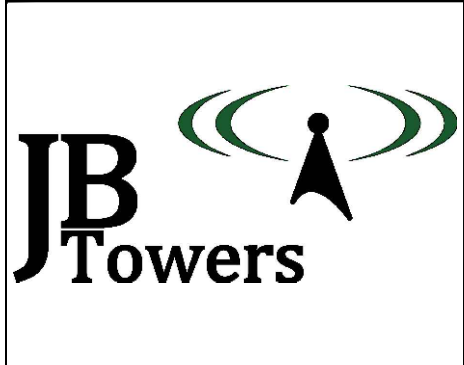

01	FIRST ISSUE							TT	03/06/19
REV	REV							BY	DATE
SCALE AS SHOWN WHEN PRINTED AT A3		DRAWN	AM	CHECKED	MP	APPROVED JBT			
		DATE	03/06/19	DATE	03/06/19	DATE 03/06/19			
ALL DIMENSIONS IN mm UNLESS OTHERWISE STATED. THIS DRAWING TO BE READ IN CONJUNCTION WITH OTHER RELEVANT DRAWINGS.									

TITLE


WESTER ERCHITE

TIMBER POLE HOLE SET OUT


SHEET 1 OF 2

SITE ADDRESS		
WESTER ERCHITE DORES, INVERNESS HIGHLAND IV2 6TX		
ARQIVA REF. 141776	DRG No. 201	REV 01

SITE ADDRESS		
WESTER ERCHITE DORES, INVERNESS HIGHLAND IV2 6TX		
ARQIVA REF. 141776	DRG No. 201	REV 01

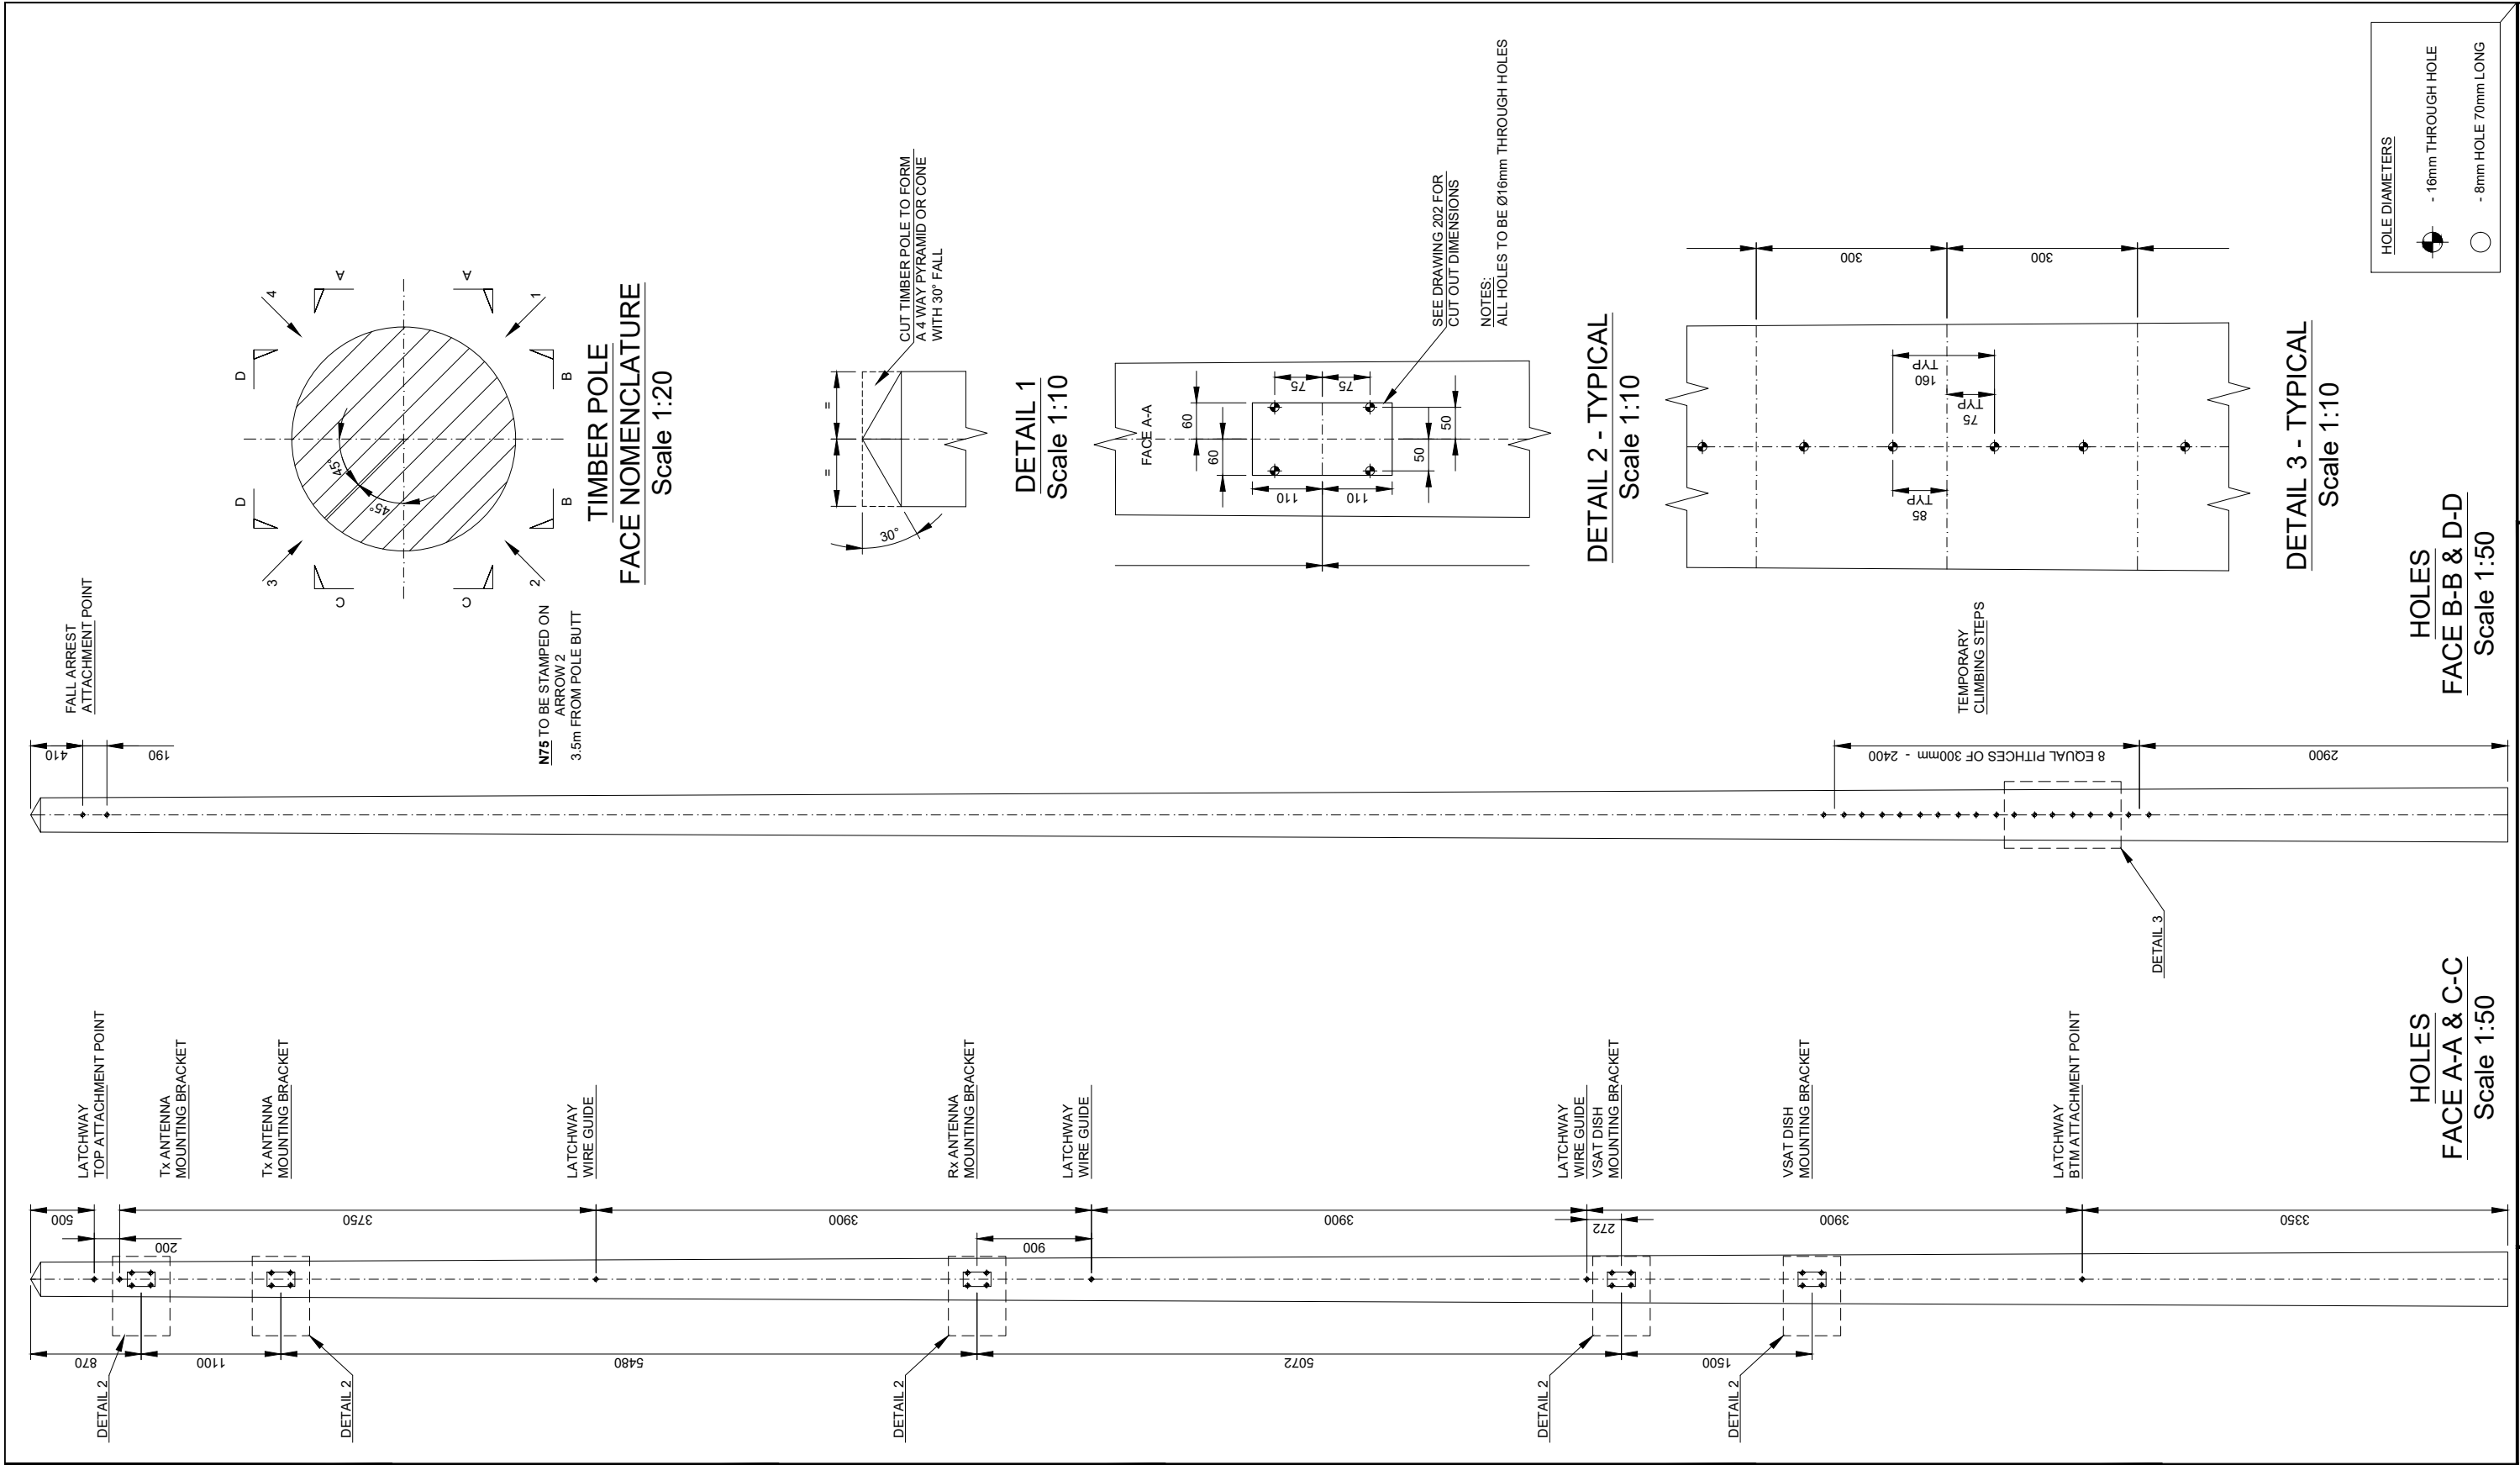

ALL SCALES AS SHOWN WHEN PRINTED AT A3										
0cm	1cm	2cm	3cm	4cm	5cm	6cm	7cm	8cm	9cm	10cm

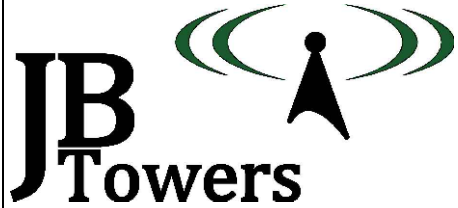

01	FIRST ISSUE			TT	03/06/19
REV	REV			BY	DATE
SCALE AS SHOWN		DRAWN	AM	CHECKED	MP
WHEN PRINTED AT A3		DATE	03/06/19	DATE	03/06/19
		APPROVED	JBT	DATE	03/06/19
ALL DIMENSIONS IN mm UNLESS OTHERWISE STATED. THIS DRAWING TO BE READ IN CONJUNCTION WITH OTHER RELEVANT DRAWINGS.					



TITLE
WESTER ERCHITE
TIMBER POLE HOLE SET OUT
SHEET 2 OF 2

SITE ADDRESS
WESTER ERCHITE
DORES, INVERNESS
HIGHLAND
IV2 6TX

ARQIVA REF.
141776

DRG No.
201

REV
01

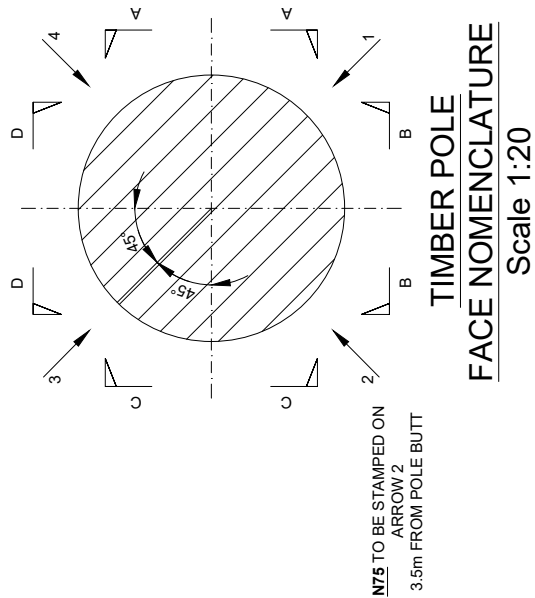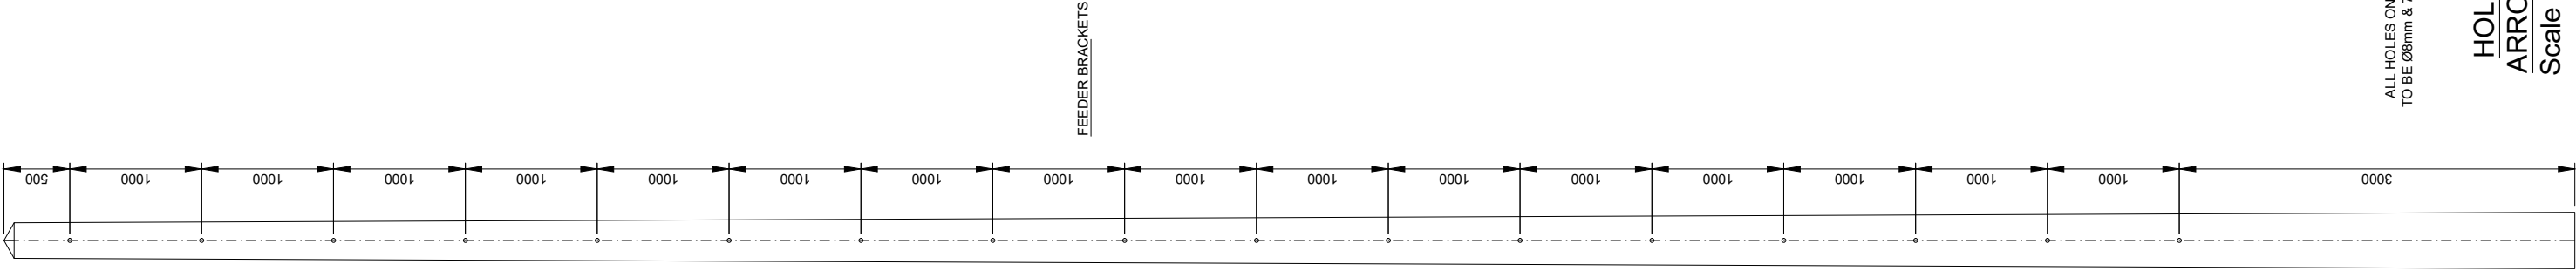

ALL HOLES ON ARROW 1
TO BE Ø8mm & 70mm LONG

HOLES
ARROW 1
Scale 1:50





ALL SCALES AS SHOWN WHEN PRINTED AT A3

ALL SCALES AS SHOWN WHEN PRINTED AT A3


01	FIRST ISSUE			TT	03/06/19
REV	REV			BY	DATE
SCALE AS SHOWN		DRAWN	AM	CHECKED	MP
WHEN PRINTED AT A3		DATE	03/06/19	DATE	03/06/19
		APPROVED	JBT	DATE	03/06/19
ALL DIMENSIONS IN mm UNLESS OTHERWISE STATED. THIS DRAWING TO BE READ IN CONJUNCTION WITH OTHER RELEVANT DRAWINGS.					

TITLE		SITE ADDRESS		
WESTER ERCHITE		WESTER ERCHITE		
TIMBER POLE CUT OUT		DORES, INVERNESS		
DETAIL		HIGHLAND		
		IV2 6TX		
ARQIVA REF.		DRG No.	REV	
141776		202	01	

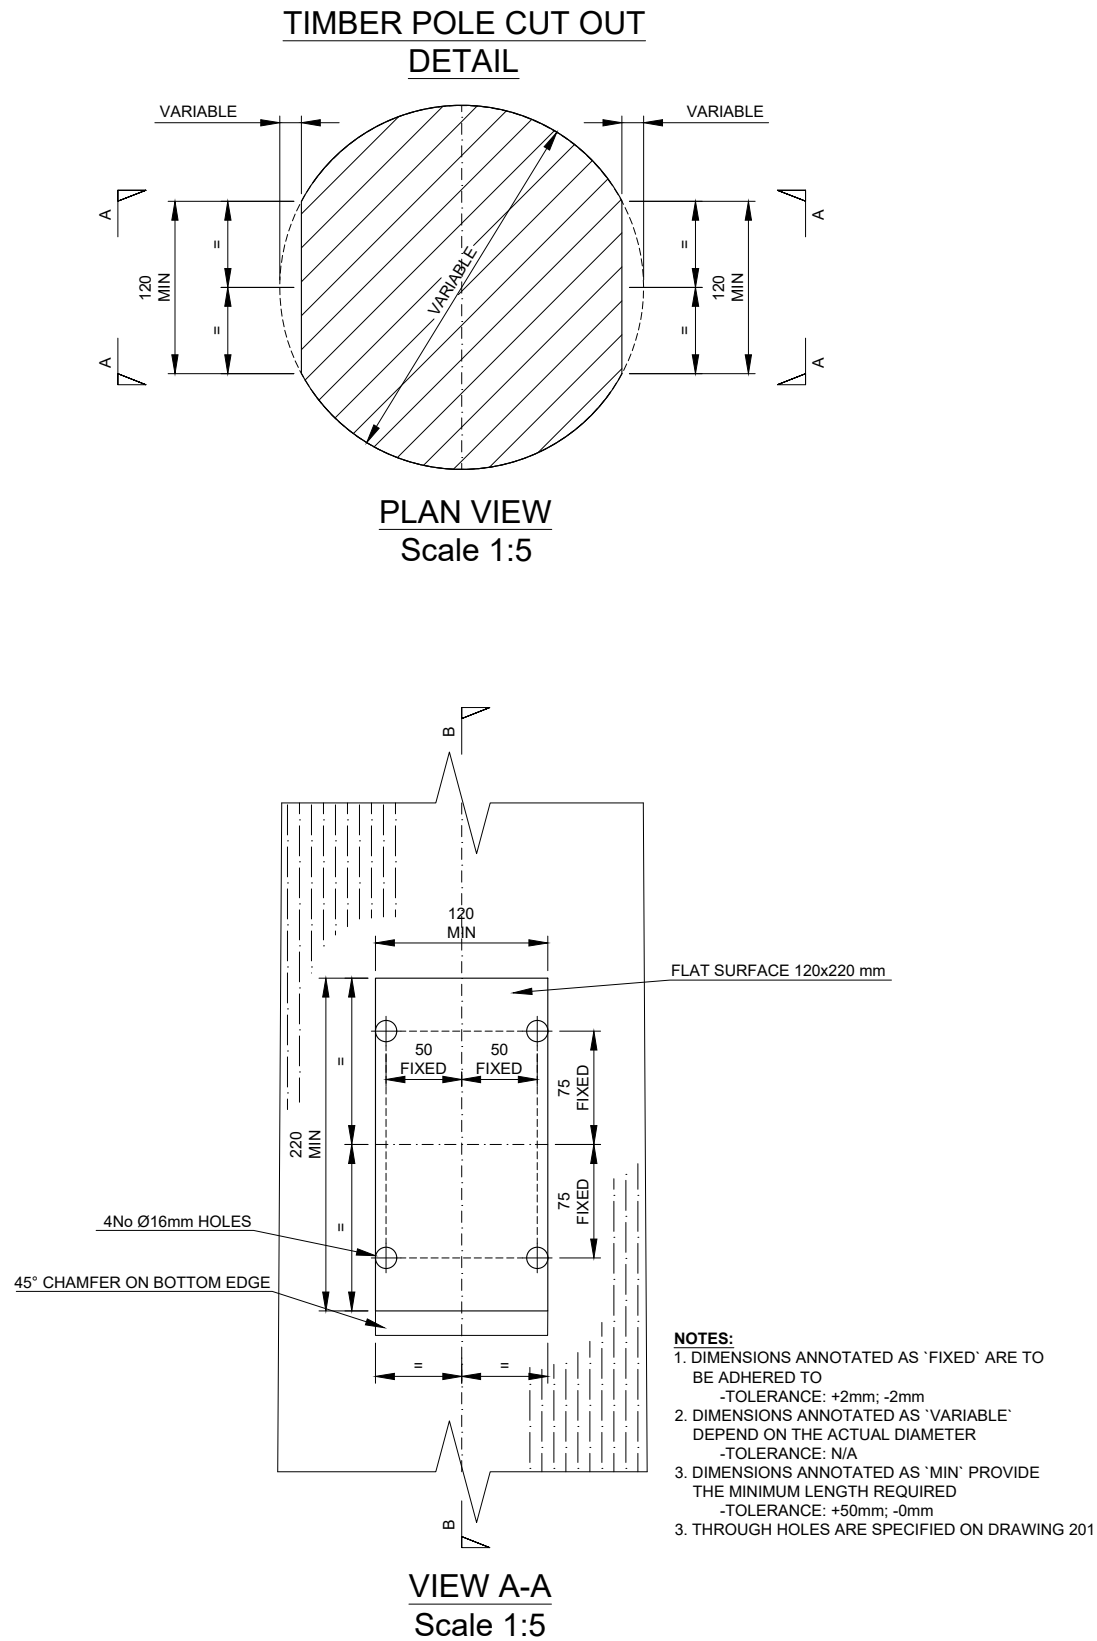

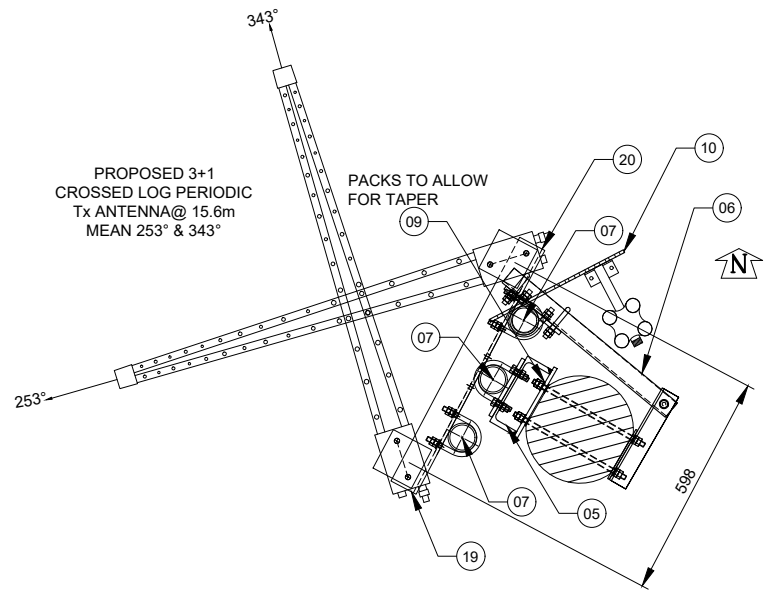


VIEW A-A
Scale 1:20

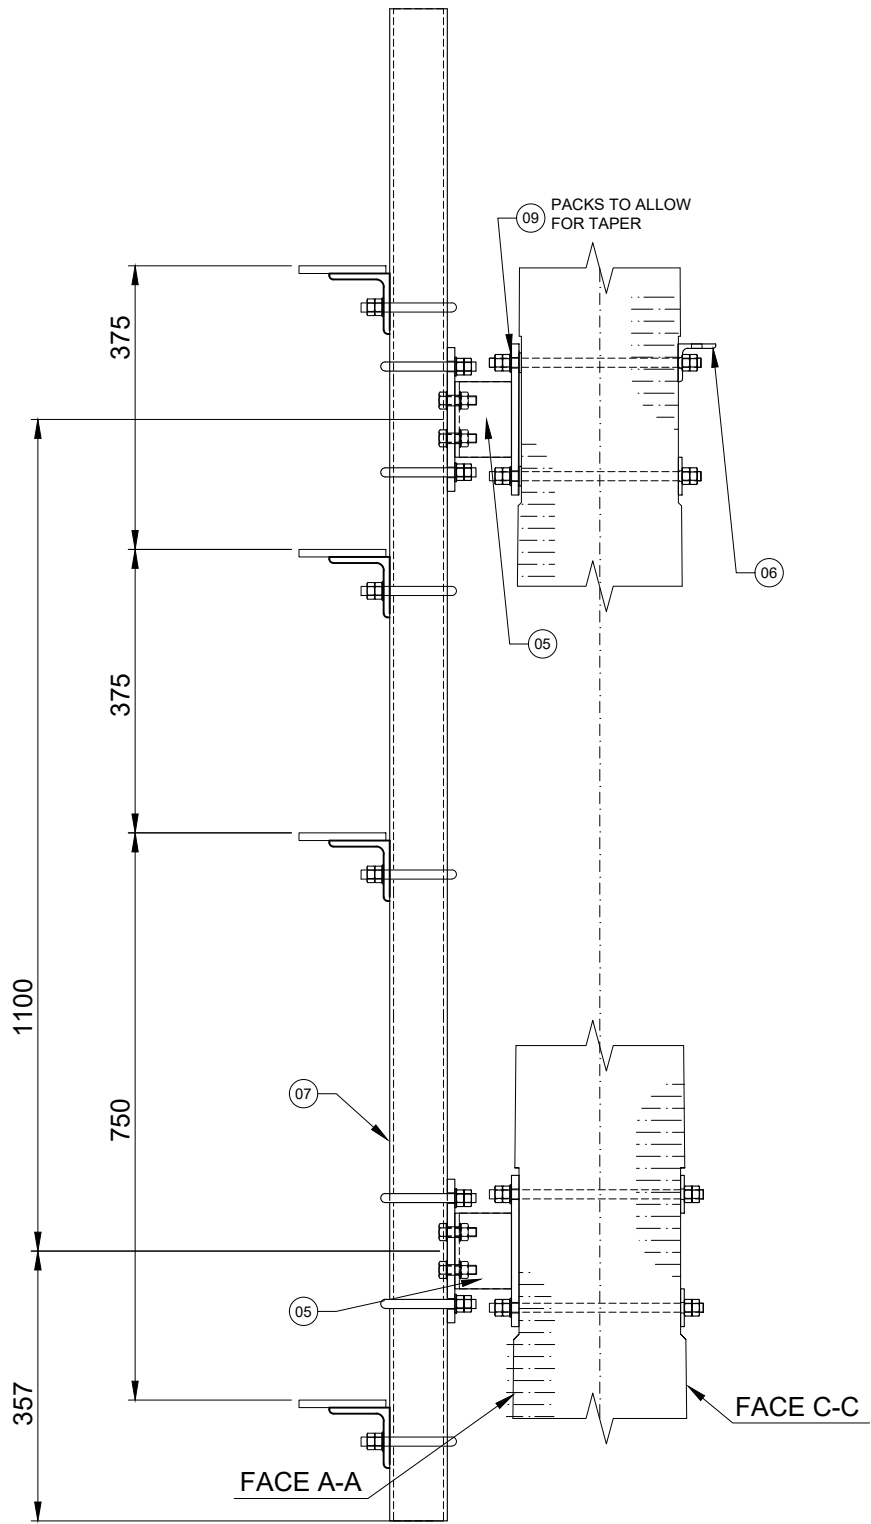


DETAIL G - Tx ANTENNA MOUNT
Scale 1:10

APPROXIMATE
POSITION
OF 4W POWER
DIVIDER

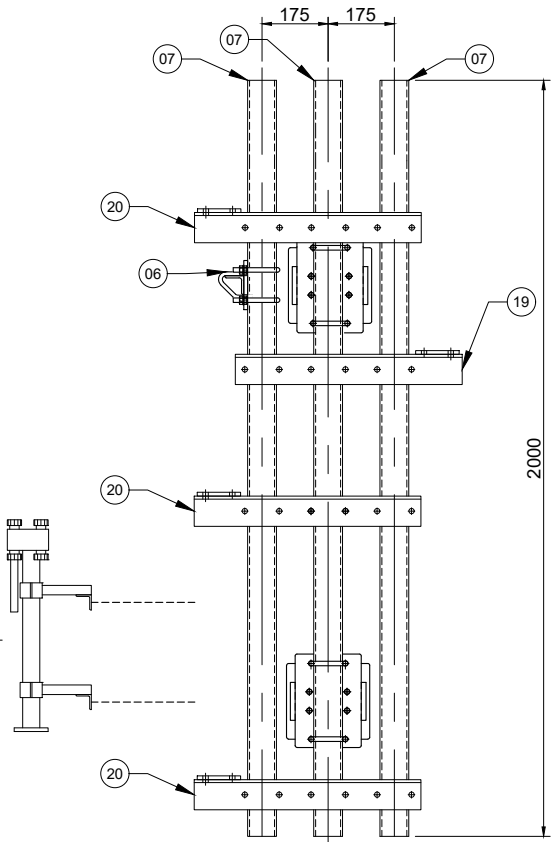

VIEW B-B
Scale 1:20

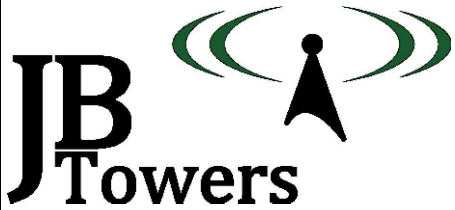

01	FIRST ISSUE				TT	03/06/19
REV	REV				BY	DATE
SCALE AS SHOWN		DRAWN	AM	CHECKED	MP	APPROVED JBT
WHEN PRINTED AT A3		DATE	03/06/19	DATE	03/06/19	DATE 03/06/19


ALL DIMENSIONS IN mm UNLESS OTHERWISE STATED.
THIS DRAWING TO BE READ IN CONJUNCTION WITH
OTHER RELEVANT DRAWINGS.

TITLE
Tx ANTENNA MOUNT
DETAIL G


SITE ADDRESS
WESTER ERCHITE
DORES, INVERNESS
HIGHLAND
IV2 6TX

ARQIVA REF. 141776	DRG No. 203	REV 01
-----------------------	----------------	-----------



ALL SCALES AS SHOWN WHEN PRINTED AT A3

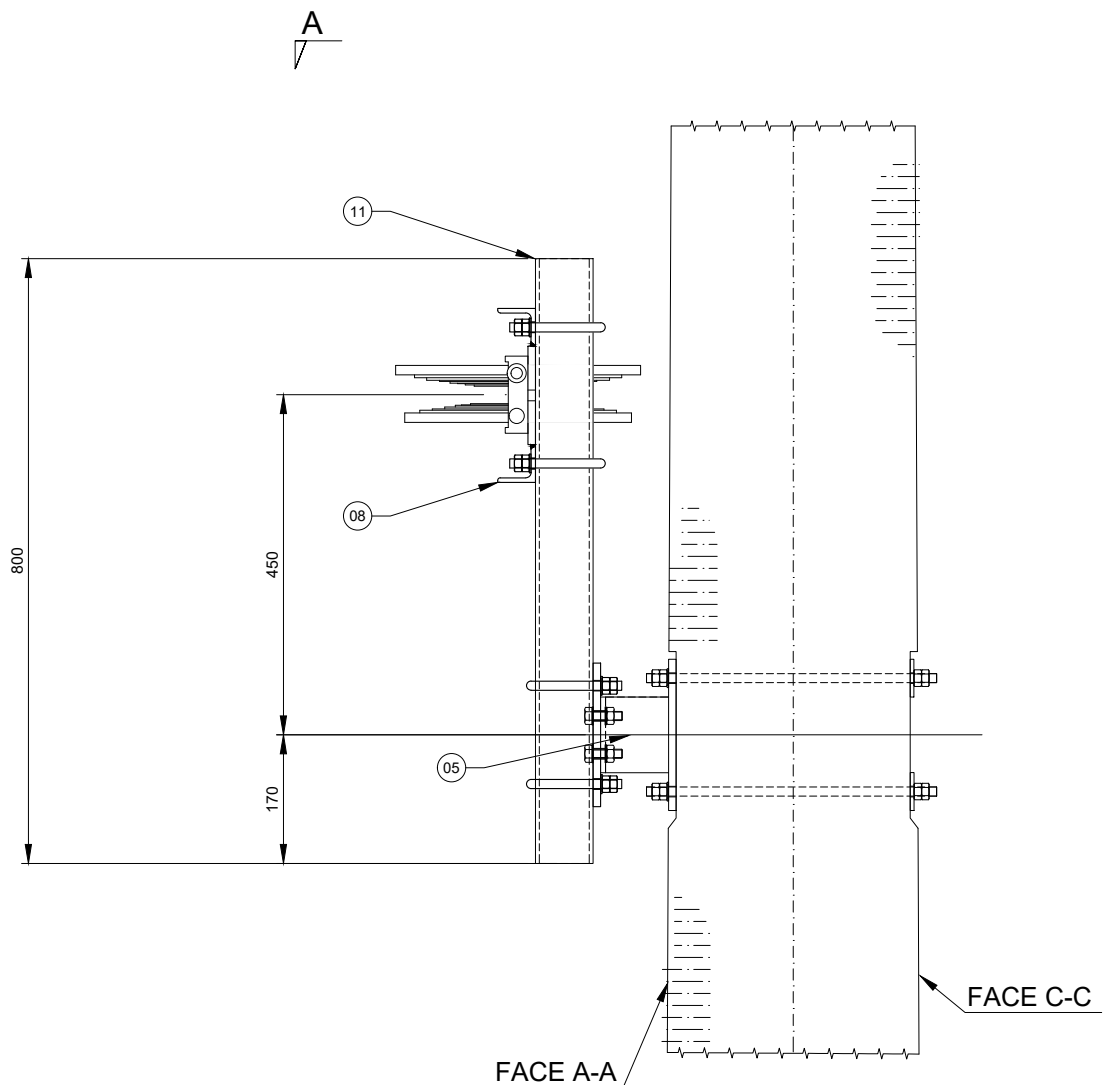

DETAIL H - Rx ANTENNA MOUNT
Scale 1:10

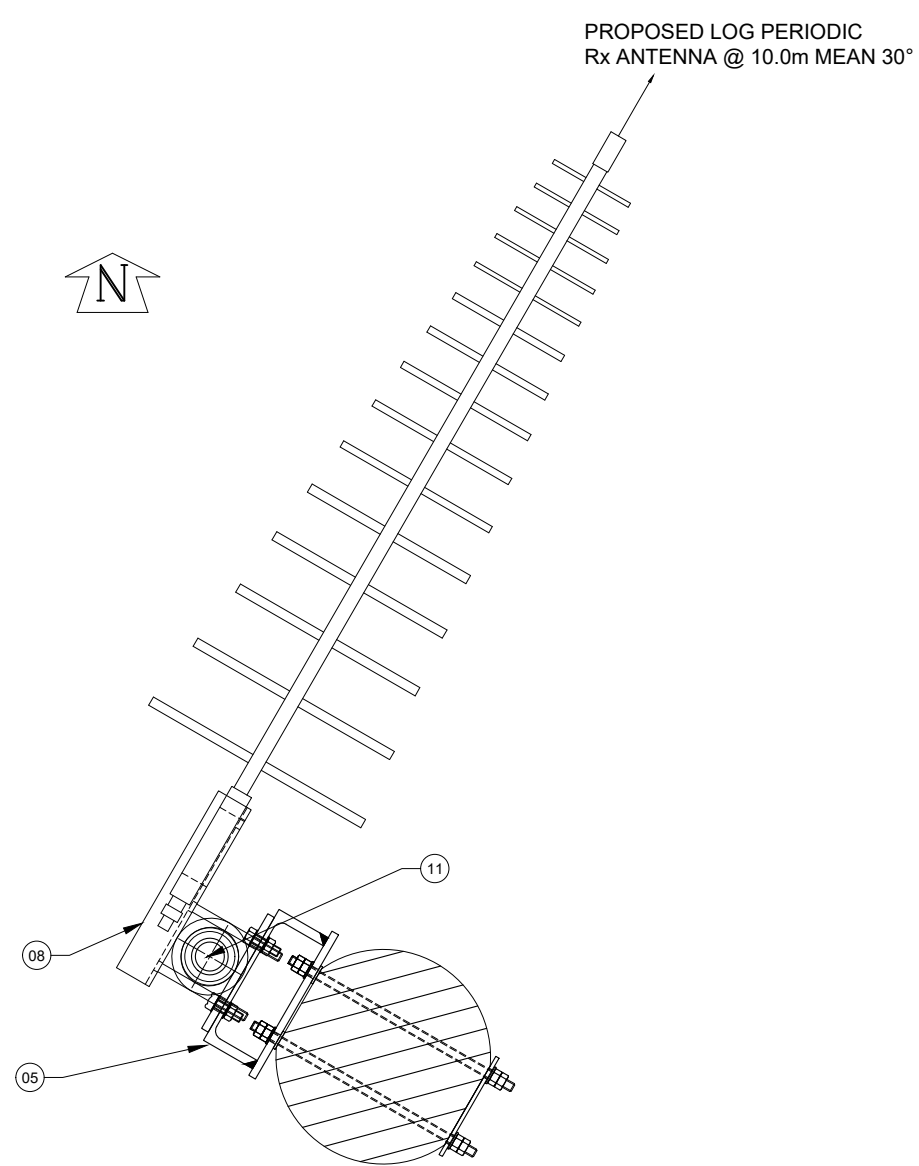

VIEW A-A
Scale 1:10

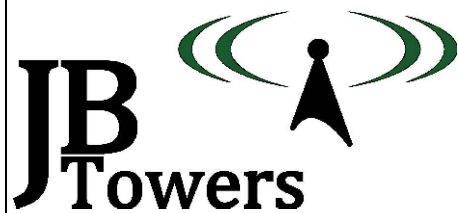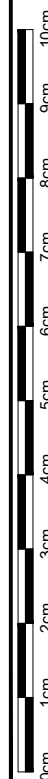

01	FIRST ISSUE			TT	03/06/19
REV	REV			BY	DATE
SCALE AS SHOWN		DRAWN	AM	CHECKED	MP
WHEN PRINTED AT A3		DATE	03/06/19	DATE	03/06/19
APPROVED		JBT			
ALL DIMENSIONS IN mm UNLESS OTHERWISE STATED. THIS DRAWING TO BE READ IN CONJUNCTION WITH OTHER RELEVANT DRAWINGS.					

TITLE
Rx ANTENNA MOUNT
DETAIL H

SITE ADDRESS
WESTER ERCHITE
DORES, INVERNESS
HIGHLAND
IV2 6TX




ARQIVA REF.
141776

DRG No.
204

REV
01

ALL SCALES AS SHOWN WHEN PRINTED AT A3

ALL SCALES AS SHOWN WHEN PRINTED AT A3

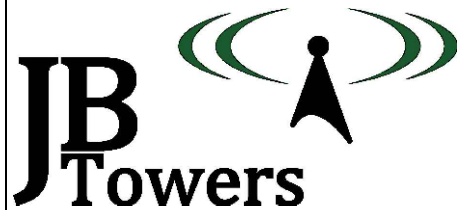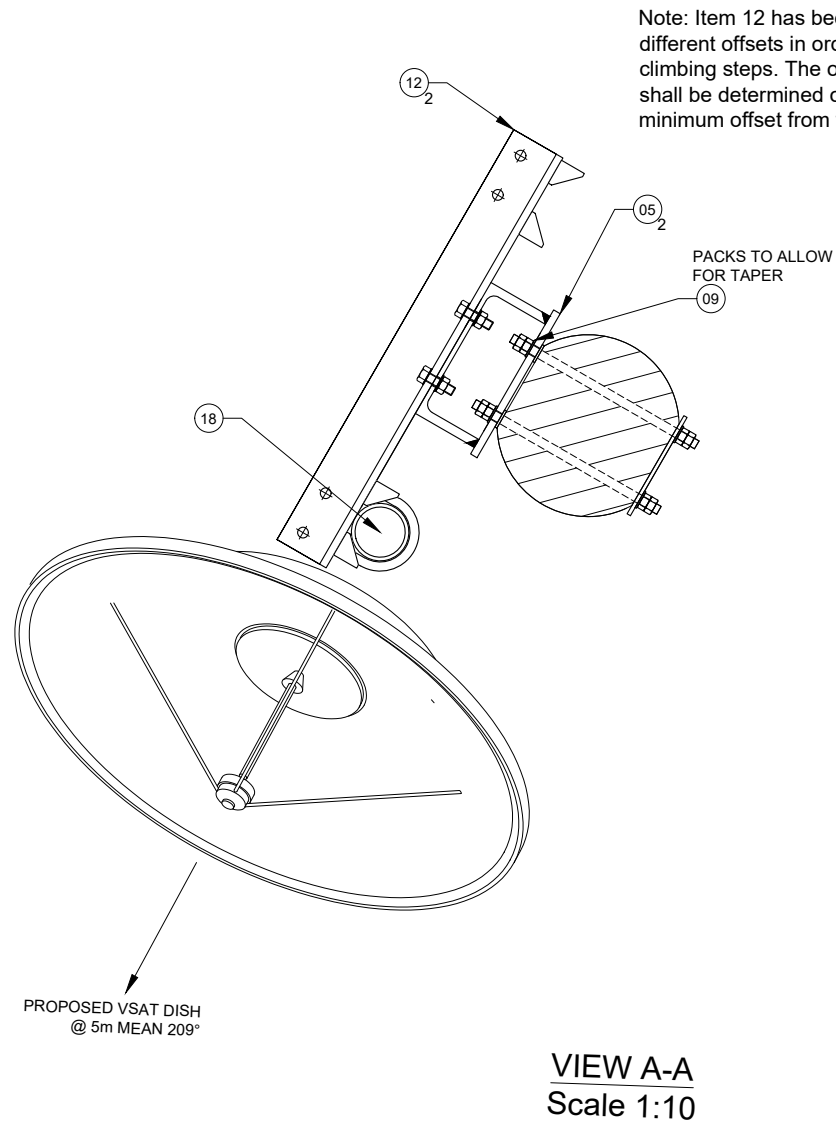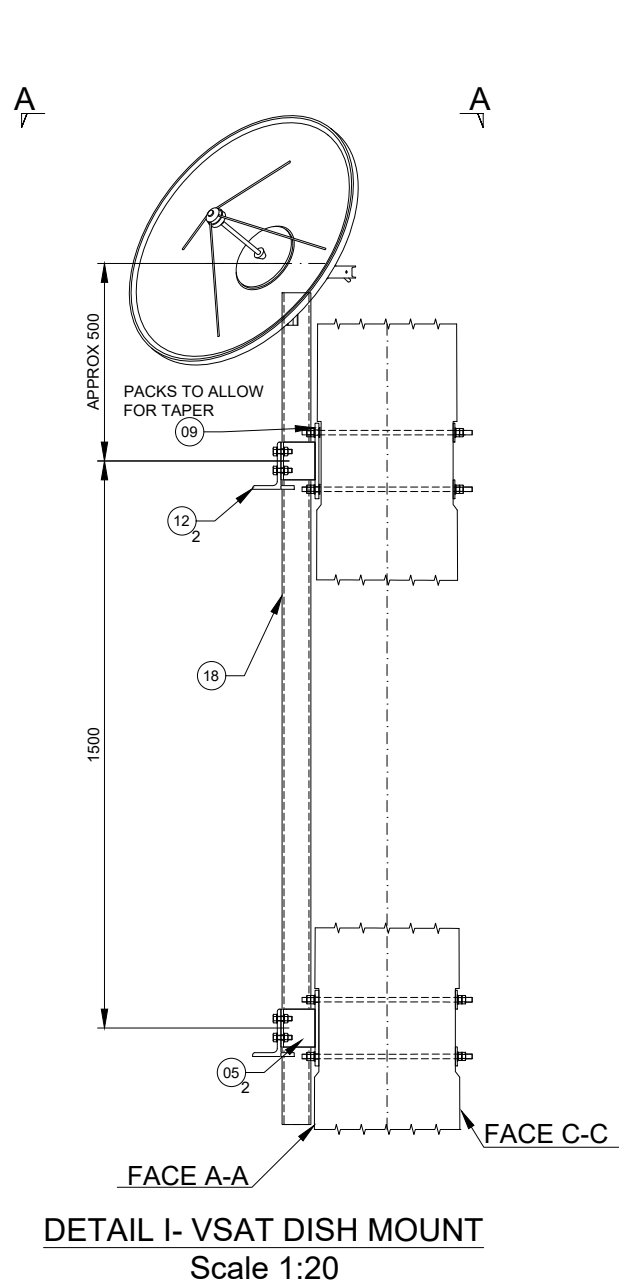


arqiva


01	FIRST ISSUE				TT	03/06/19
REV	REV				BY	DATE
SCALE AS SHOWN		DRAWN	AM	CHECKED	MP	APPROVED JBT
WHEN PRINTED AT A3		DATE	03/06/19	DATE	03/06/19	DATE 03/06/19
ALL DIMENSIONS IN mm UNLESS OTHERWISE STATED. THIS DRAWING TO BE READ IN CONJUNCTION WITH OTHER RELEVANT DRAWINGS.						

TITLE		SITE ADDRESS		
VSAT DISH MOUNT		WESTER ERCHITE		
DETAIL I		DORES, INVERNESS		
		HIGHLAND		
		IV2 6TX		
ARQIVA REF.		DRG No.	REV	
141776		205	01	

ALL SCALES AS SHOWN WHEN PRINTED AT A3

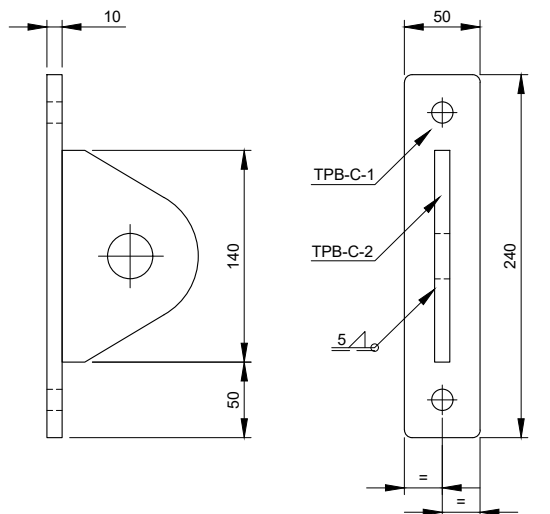

PART TPB-C
Scale 1:5

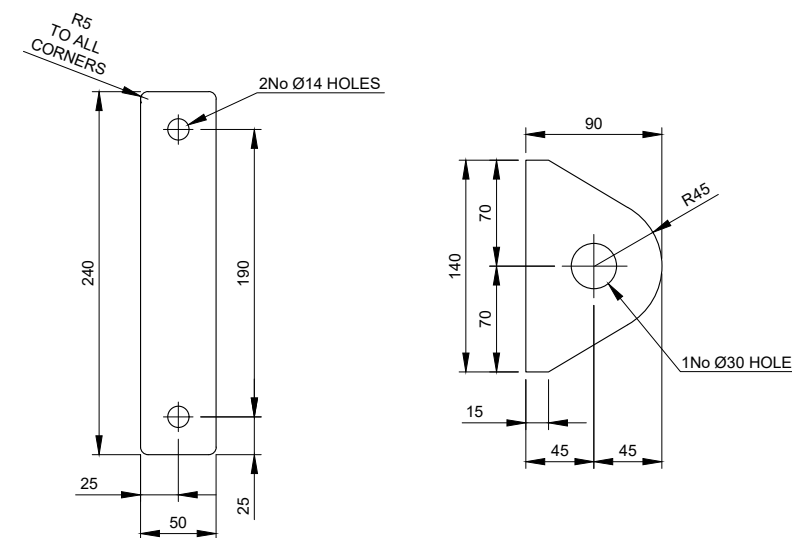


TPB-C-1 - 10mm THICK
Scale 1:5

TPB-C-2 - 10mm THICK
Scale 1:5


Parts list for TPB-C

Item	Part	Quantity	Part description	Length	Material	Weight
01	TPB-C-1	1	Plate 240x50x10mm	N/A	S275J0	0.94 kg
02	TPB-C-2	1	Plate 140x90x10mm	N/A	S275J0	0.99 kg
03	STUDS	1	M12 STUDDING	350mm	GRADE 8.8	0.31 kg
Total Weight:						2.24 kg

- All steel hot dip galvanized
- Each STUD to be supplied with 4 Full Nuts, 2 Flat Washers and 2 Spring Washers
- For fabrication notes see drawing 305

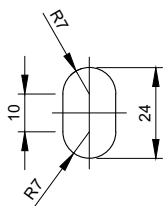

SLOTTED HOLE DETAIL
Scale 1:2

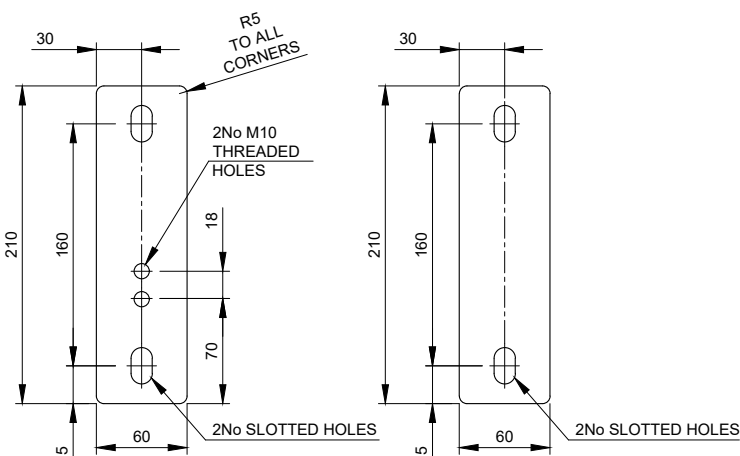


PART TPS-R-1
Scale 1:5

PART TPS-R-2
Scale 1:5

Parts list for TPS-R

Item	Part	Quantity	Part description	Length	Material	Weight
01	TPS-R-1	1	Plate 210x60x15mm	N/A	S275J0	1.48 kg
02	TPS-R-2	1	Plate 210x60x5mm	N/A	S275J0	0.49 kg
03	STUDS	2	M12 STUDDING	500mm	GRADE 8.8	0.44 kg
04	NUT-S	2	M12 SHALLOW NUT	N/A	GRADE 8.8	-
05	NUT	4	M12 NUT	N/A	GRADE 8.8	-
06	WSH	4	M12 WASHER	N/A	GRADE 8.8	-
Total Weight:						2.41 kg

- All steel hot dip galvanized
- For fabrication notes see drawing 305

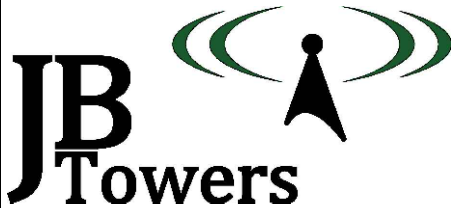

01	FIRST ISSUE	TT	03/06/19
REV	REV	BY	DATE
SCALE AS SHOWN WHEN PRINTED AT A3	DRAWN DATE 03/06/19	AM DATE 03/06/19	CHECKED DATE 03/06/19
APPROVED DATE 03/06/19			
ALL DIMENSIONS IN mm UNLESS OTHERWISE STATED. THIS DRAWING TO BE READ IN CONJUNCTION WITH OTHER RELEVANT DRAWINGS.			

TITLE
ATTACHMENT POINT &
TEMPORARY STEP DETAILS
PARTS: TPB-C; TPS-R


SITE ADDRESS
WESTER ERCHITE
DORES, INVERNESS
HIGHLAND
IV2 6TX

ARQIVA REF.
141776
DRG No.
300
REV
01


ALL SCALES AS SHOWN WHEN PRINTED AT A3




ALL SCALES AS SHOWN WHEN PRINTED AT A3

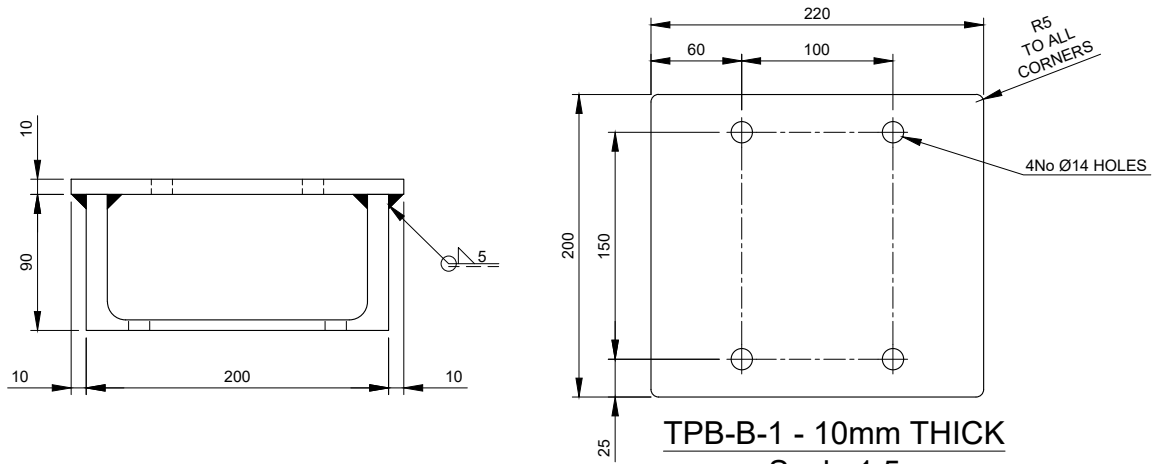


TPB-B-1 - 10mm THICK
Scale 1:5

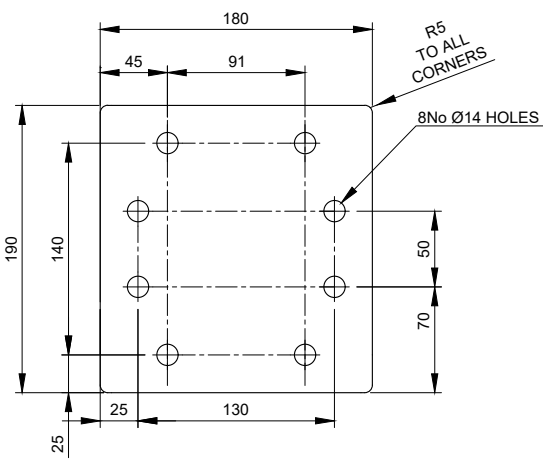


TPB-B-5 - 10mm THICK
Scale 1:5

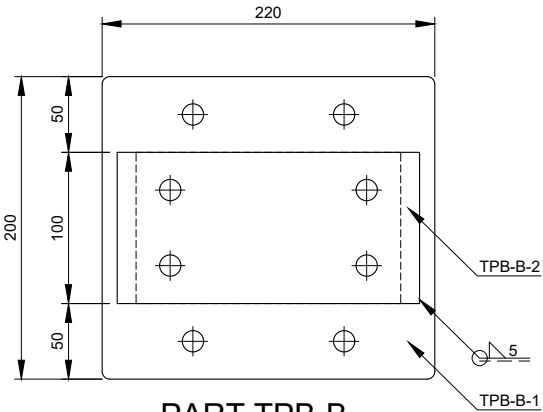


PART TPB-B
Scale 1:5

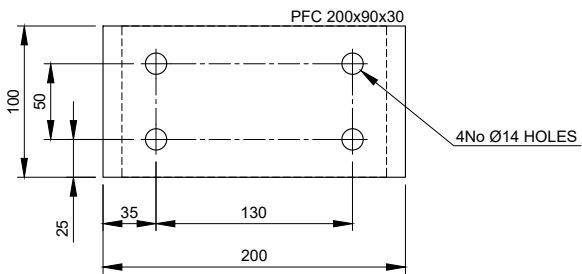

TPB-B-2 - PFC 200x90x30
Scale 1:5

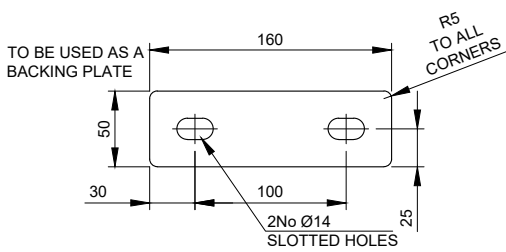

TPB-B-4 - 5mm THICK
Scale 1:5

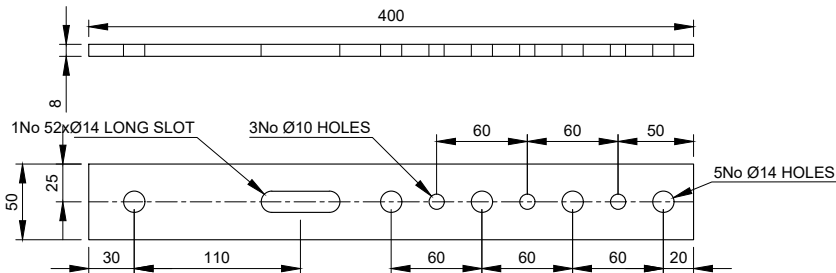


TPA-PD - 8mm THICK
Scale 1:5

Parts list for TPB-B

Item	Part	Quantity	Part description	Length	Material	Weight
01	TPB-B-1	1	Plate 220x200x10mm	N/A	S275J0	3.45 kg
02	TPB-B-2	1	PFC 200x90x30	100mm	S275J0	2.30 kg
03	TPB-B-4	2	Plate 160x50x5mm	N/A	S275J0	0.31 kg
04	TPB-B-5	1	Plate 190x180x10mm	N/A	S275J0	3.45 kg
05	STUDS	4	M12 STUDDING	450mm	GRADE 8.8	0.39 kg
06	BOLT	4	M12 45mm LONG (2D+6)	45mm	GRADE 8.8	-
07	U-BOLT	2	M12 U-BOLT FOR CHS 76.1	N/A	GRADE 8.8	-

- All steel hot dip galvanized
- Each STUD & U-BOLT to be supplied with 4 Full Nuts, 2 Flat Washers and 2 Spring Washers
- Each BOLT to be supplied with 1 Full Nut, 1 Form E Flat Washer and 1 Spring Washer
- For fabrication notes see drawing 305

Total Weight: 9.9 kg

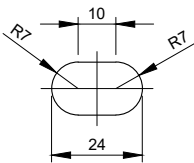


SLOTTED HOLE DETAIL
Scale 1:2

Parts list for TPA-PD

Item	Part	Quantity	Part description	Length	Material	Weight
01	TPA-PD	1	400x50x8mm	N/A	S275J0	1.26 kg
02	U-BOLT	1	M12 U-BOLT FOR CHS 76.1mm	N/A	GRADE 8.8	-

- All steel hot dip galvanized
- Each U-BOLT to be supplied with 4 Full Nuts, 2 Flat Washers and 2 Spring Washers
- For fabrication notes see drawing 305

Total Weight: 1.26 kg

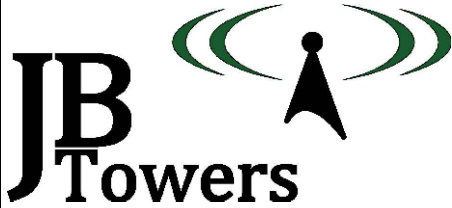

01	FIRST ISSUE			TT	03/06/19
REV	REV			BY	DATE
SCALE AS SHOWN	DRAWN	AM	CHECKED	MP	APPROVED JBT
WHEN PRINTED AT A3	DATE	03/06/19	DATE	03/06/19	DATE 03/06/19
ALL DIMENSIONS IN mm UNLESS OTHERWISE STATED. THIS DRAWING TO BE READ IN CONJUNCTION WITH OTHER RELEVANT DRAWINGS.					

TITLE
STEELWORK BRACKET,
INTERFACE PLATE, POWER
DIVIDER STRAP

PART: TPB-B, TPA-PD

SITE ADDRESS
WESTER ERCHITE
DORES, INVERNESS
HIGHLAND
IV2 6TX

ARQIVA REF.
141776


DRG No.
301

REV
01

ALL SCALES AS SHOWN WHEN PRINTED AT A3



ALL SCALES AS SHOWN WHEN PRINTED AT A3

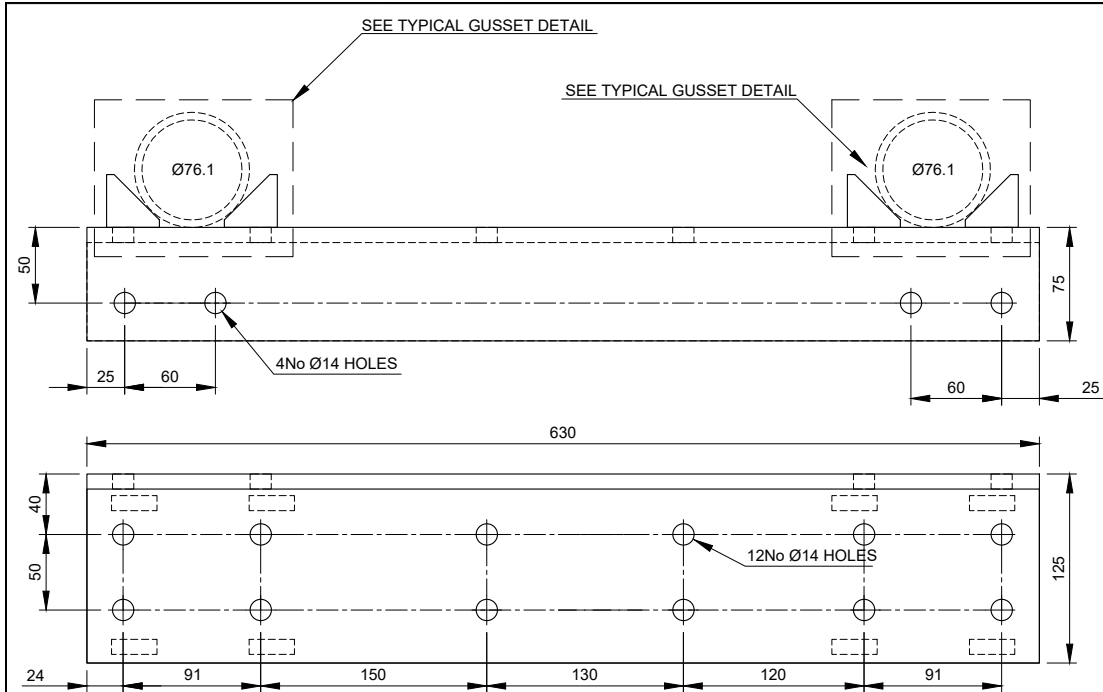

TPA-M - UA125x75x10
Scale 1:5

Parts list for TPA-M



Item	Part	Quantity	Part description	Length	Material	Weight
01	TPA-M	1	UA125x75x10 C/W GUSSETS	630mm	S275J0	9.45 kg
02	U-BOLT	2	M12 U-BOLT FOR CHS 76.1mm	N/A	GRADE 8.8	-
03	BOLT	4	M12x45 (2D+6) BOLT	N/A	GRADE 8.8	-
Total Weight:						9.45 kg

- All steel hot dip galvanized
- Each STUD & U-BOLT to be supplied with 4 Full Nuts, 2 Flat Washers and 2 Spring Washers
- Each BOLT to be supplied with 1 Full Nut, 1 Form E FLat Washer and 1 Spring Washer
- For fabrication notes see drawing 305



Parts list for TPL-C

Item	Part	Quantity	Part description	Length	Material	Weight
01	TPL-C-1	1	EA 50x50x6	270mm	S275J0	1.205 kg
02	TPL-C-1 X	1	EA 50x50x6	270mm	S275J0	1.205 kg
03	TPL-C-2	1	Plate 150x130x10mm	N/A	S275J0	1.53 kg
04	U-BOLT	2	M12 U-BOLT FOR CHS 76.1mm	N/A	GRADE 8.8	-
Total Weight:						3.95 kg


- All steel hot dip galvanized
- Each U-BOLT to be supplied with 4 Full Nuts, 2 Flat Washers and 2 Spring Washers
- For fabrication notes see drawing 305

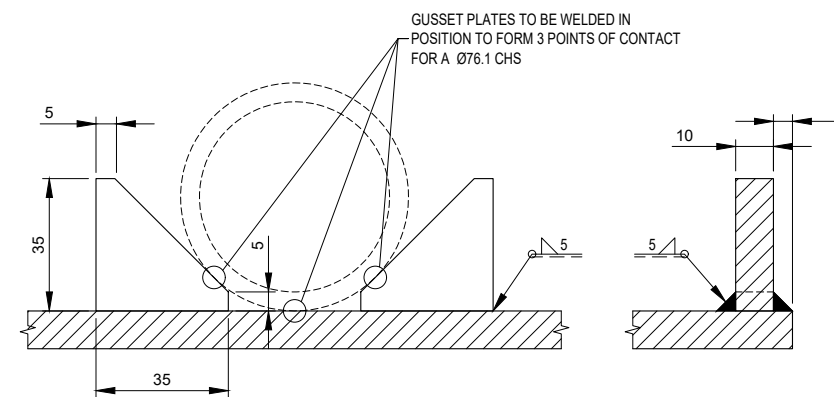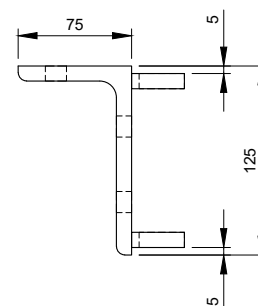


TYPICAL GUSSET PLATE DETAIL
Scale 1:2

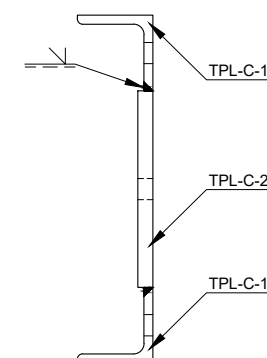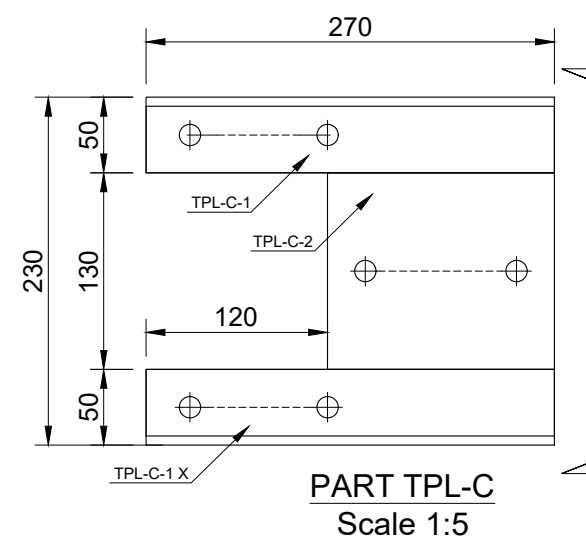


VIEW A-A
Scale 1:5

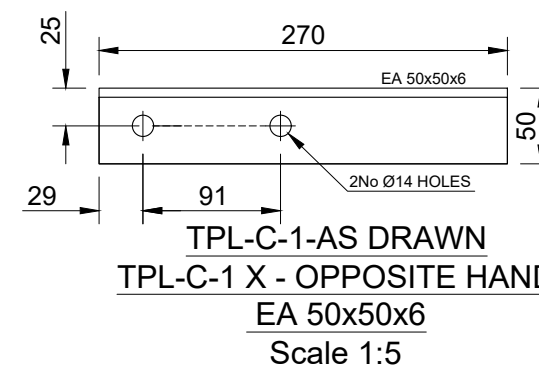

TPL-C-1-AS DRAWN
TPL-C-1 X - OPPOSITE HAND
EA 50x50x6
Scale 1:5

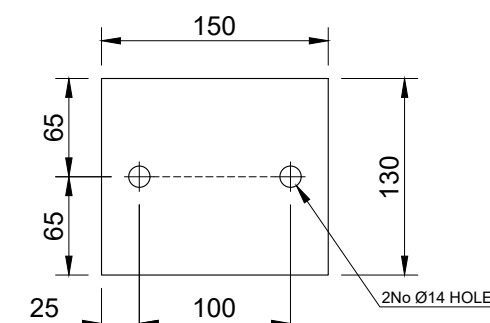

TPL-C-2 - 10mm THICK
Scale 1:5

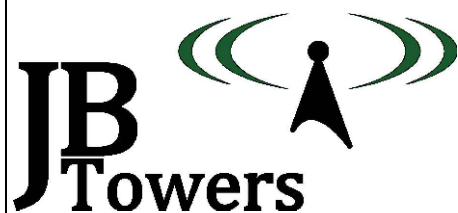

01	FIRST ISSUE				TT	03/06/19
REV	REV				BY	DATE
SCALE AS SHOWN		DRAWN	AM	CHECKED	MP	APPROVED
WHEN PRINTED AT A3		DATE	03/06/19	DATE	03/06/19	DATE
ALL DIMENSIONS IN mm UNLESS OTHERWISE STATED.		THIS DRAWING TO BE READ IN CONJUNCTION WITH OTHER RELEVANT DRAWINGS.				

TITLE
VSAT DISH BRACKET & LOG MOUNT

PARTS: TPA-M; TPL-C;


SITE ADDRESS
**WESTER ERCHITE
DORES, INVERNESS
HIGHLAND
IV2 6TX**


ARQIVA REF.
141776

DRG No.
302

REV
01

ALL SCALES AS SHOWN WHEN PRINTED AT A3

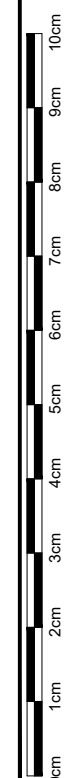

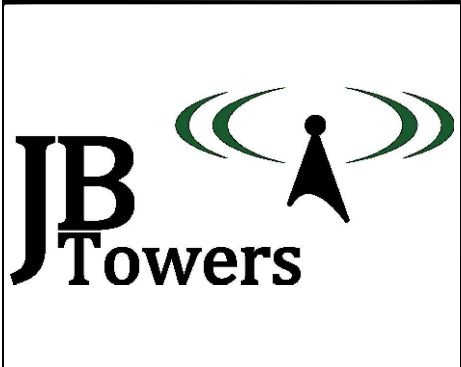


01	FIRST ISSUE			TT	03/06/19
REV	REV			BY	DATE
SCALE AS SHOWN		DRAWN	AM	CHECKED	MP
WHEN PRINTED AT A3		DATE	03/06/19	DATE	03/06/19
		APPROVED	JBT	DATE	03/06/19
ALL DIMENSIONS IN mm UNLESS OTHERWISE STATED. THIS DRAWING TO BE READ IN CONJUNCTION WITH OTHER RELEVANT DRAWINGS.					

TITLE
Tx LOG MOUNTING BRACKET
PARTS: TPL-A , TPL-B

SITE ADDRESS
WESTER ERCHITE
DORES, INVERNESS
HIGHLAND
IV2 6TX


ARQIVA REF. 141776	DRG No. 303	REV 01
-----------------------	----------------	-----------

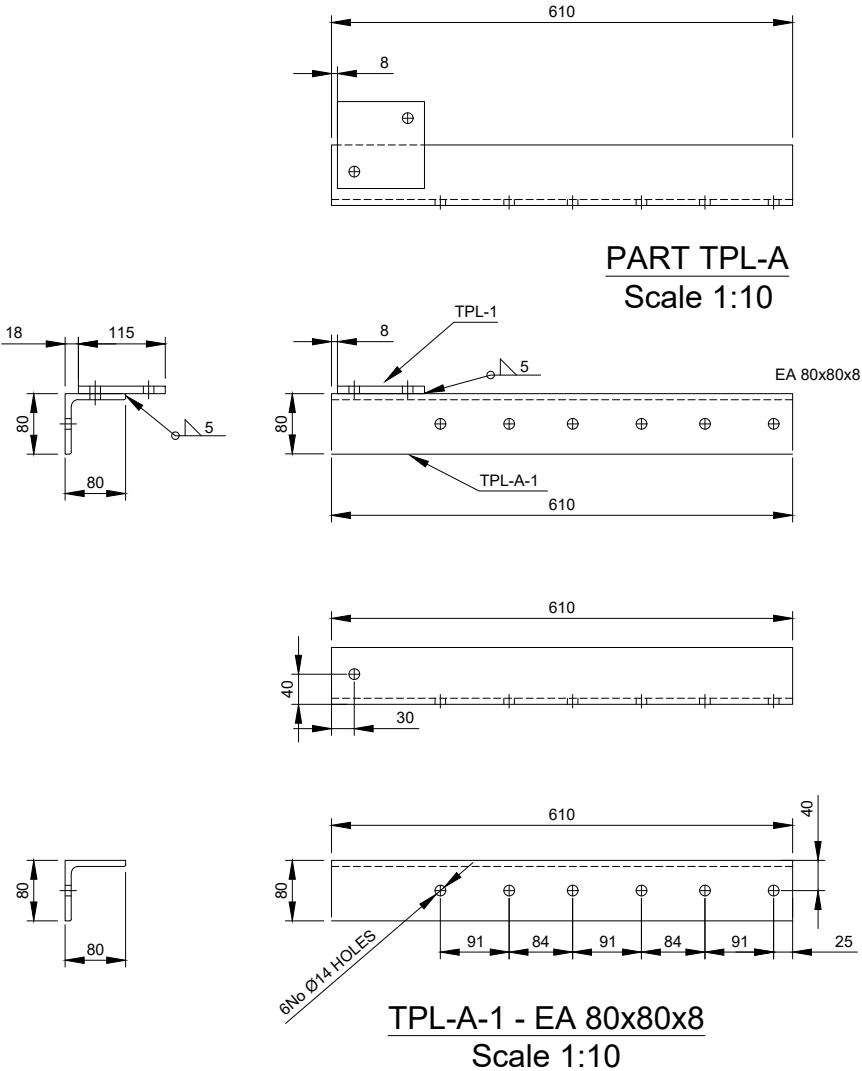

Parts list for TPL-A

Item	Part	Quantity	Part description	Length	Material	Weight
01	TPL-A-1	1	EA 80x80x8	610mm	S275J0	5.87 kg
02	TPL-1	1	Plate 115x115x10mm	N/A	S275J0	1.04 kg
03	U-BOLT	3	M12 U-BOLT FOR CHS 76.1mm	N/A	GRADE 8.8	-
Total Weight:						6.91 kg


- All steel hot dip galvanized
- Each U-BOLT to be supplied with 4 Full Nuts, 2 Flat Washers and 2 Spring Washers
- For fabrication notes see drawing 305

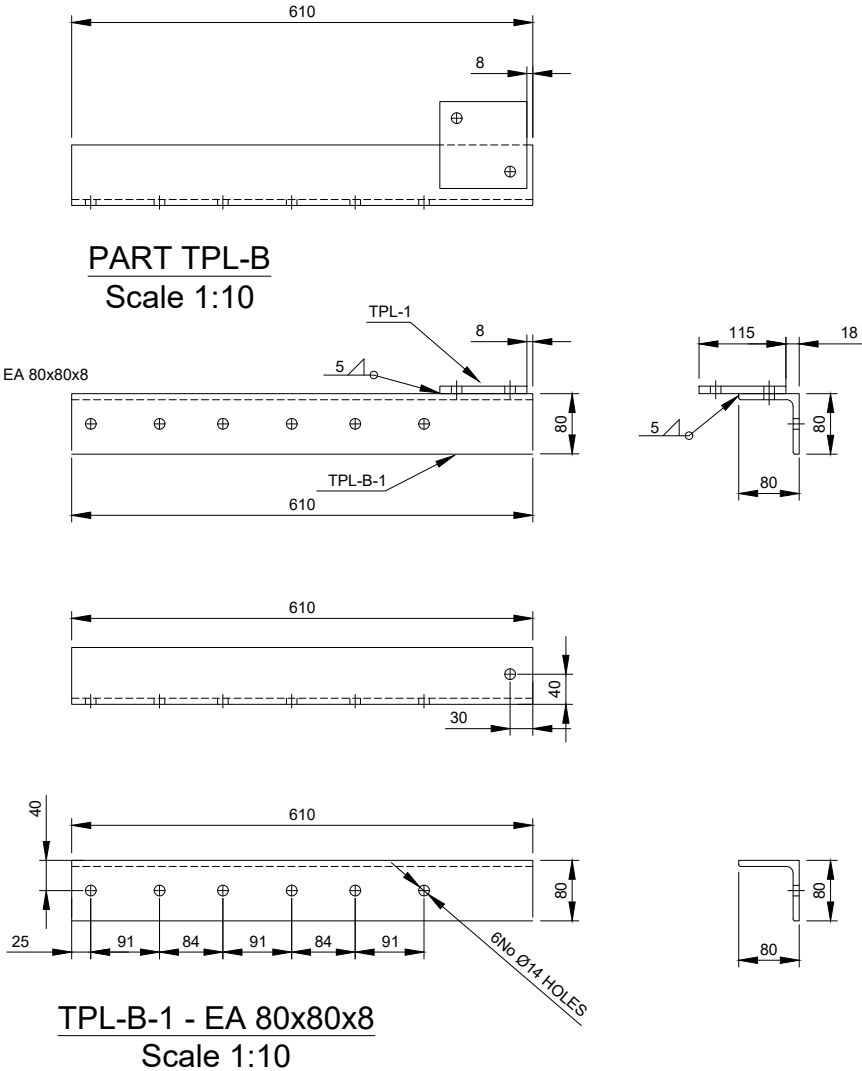

Parts list for TPL-B

Item	Part	Quantity	Part description	Length	Material	Weight
01	TPL-B-1	1	EA 80x80x8	610mm	S275J0	5.87 kg
02	TPL-1	1	Plate 115x115x10mm	N/A	S275J0	1.04 kg
03	U-BOLT	3	M12 U-BOLT FOR CHS 76.1mm	N/A	GRADE 8.8	-
Total Weight:						6.91 kg


- All steel hot dip galvanized
- Each U-BOLT to be supplied with 4 Full Nuts, 2 Flat Washers and 2 Spring Washers
- For fabrication notes see drawing 305

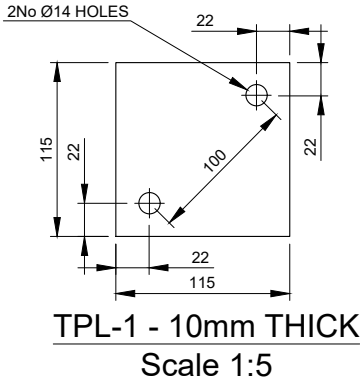



ALL SCALES AS SHOWN WHEN PRINTED AT A3




ALL SCALES AS SHOWN WHEN PRINTED AT A3

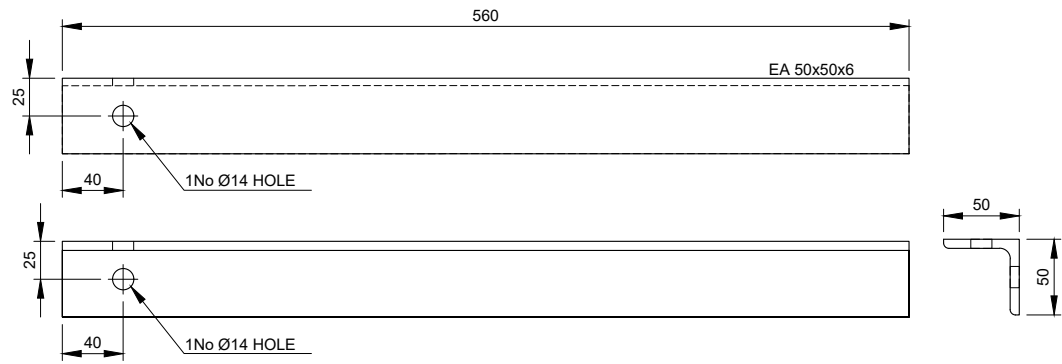

TPB-BR-1 - EA50x50x6
Scale 1:5

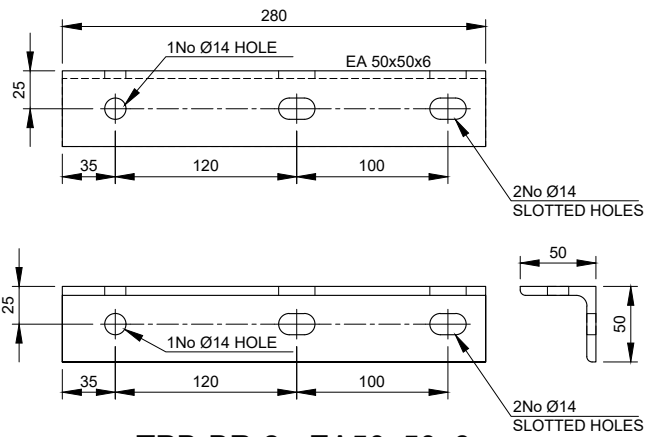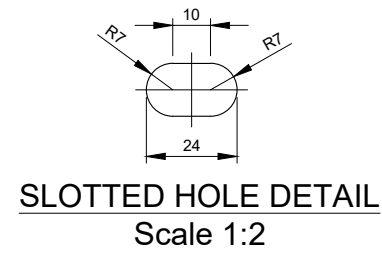

TPB-BR-2 - EA50x50x6
Scale 1:5

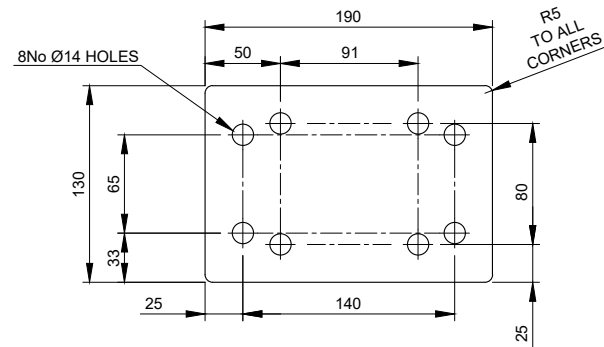


TPB-BR-3 - 10mm THICK
Scale 1:5

Parts list for TPB-BR

Item	Part	Quantity	Part description	Length	Material	Weight
01	TPB-BR-1	1	EA 50x50x6	280mm	S275J0	1.25 kg
02	TPB-BR-2	1	EA 50x50x6	560mm	S275J0	2.5 kg
03	TPB-BR-3	1	Plate 130x190x10mm	N/A	S275J0	1.94 kg
04	BOLT	1	M12 SET BOLT - 30mm LONG	N/A	GRADE 8.8	-
05	N-BOLT	2	M12 N-BOLT FOR EA 50x50x6	N/A	GRADE 8.8	-
06	U-BOLT	2	M12 U-BOLT FOR CHS 76.1mm	N/A	GRADE 8.8	-
Total Weight:						5.69 kg

- All steel hot dip galvanized
- Each BOLT to be supplied with 1 Full Nut, 1 Form E FLat Washer and 1 Spring Washer
- Each STUD & U-BOLT to be supplied with 4 Full Nuts, 2 Flat Washers and 2 Spring Washers
- For fabrication notes see drawing 305

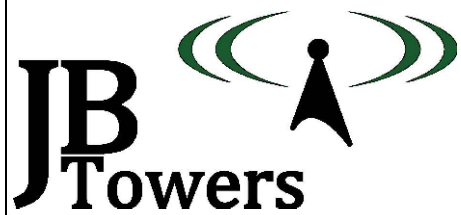

arqiva

01	FIRST ISSUE			TT	03/06/19
REV	REV			BY	DATE
SCALE AS SHOWN WHEN PRINTED AT A3		DRAWN AM DATE 03/06/19	CHECKED MP DATE 03/06/19	APPROVED JBT DATE 03/06/19	
ALL DIMENSIONS IN mm UNLESS OTHERWISE STATED. THIS DRAWING TO BE READ IN CONJUNCTION WITH OTHER RELEVANT DRAWINGS.					

TITLE		SITE ADDRESS		
BRACING ARM		WESTER ERCHITE		
PARTS: TPB-BR		DORES, INVERNESS		
		HIGHLAND		
		IV2 6TX		
ARQIVA REF.		DRG No.	REV	
141776		304	01	

ALL SCALES AS SHOWN WHEN PRINTED AT A3




ALL SCALES AS SHOWN WHEN PRINTED AT A3

Item	Part	Drawing	Quantity	Part description	Length	Material	Weight
01	01	200	1	3 MAN LATCHWAY SYSTEM & 3No. WIRE GUIDES FOR FACE MOUNTED MONOPOLE	17000	N/A	-
02	TPB-C	300	2	FALL ARREST ATTACHMENT POINT	N/A	S275J0	4.48 kg
03	03	200	46	PERMANENT BT STEP c/w 3No 10x75mm ZINC-PLATED COACH SCREWS	N/A	S275J0	13.80 kg
04	TPS-R	300	9	'MonoStep' ASSEMBLY	N/A	S275J0	21.69 kg
05	TPB-B	301	5	MOUNTING BRACKET	N/A	S275J0	47.55 kg
06	TPB-BR	304	1	BRACING ARM	N/A	S275J0	5.69 kg
07	07	203	3	CHS 76.1x5mm	2000mm	S355J2H	52.62 kg
08	TPL-C	302	1	LOG MOUNTING BRACKET	270mm	S275J0	7.89 kg
09	09	203/205	20	M12 WASHER	N/A	GRADE 8.8	-
10	TPA-PD	301	2	POWER DIVIDER STRAP	N/A	S275J0	2.52 kg
11	11	204	1	CHS 76.1x5mm	800mm	S355J2H	7.02 kg
12	TPA-M	302	2	VSAT DISH LOG MOUNT	630mm	S275J0	18.9 kg
13	13	200	1	FEEDER COVER - 2/CG/100	3500mm	UV RESISTANT PLASTIC	-
14	14	200	17	FEEDER CLAMP - 2/FCD/028	N/A	POLYPROPYLENE	-
15	15	200	17	M10 SCREW DOWELS WTH M10 NUT	100mm	STAINLESS STEEL	-
16	16	200	1	PoleSaver	750mm	N/A	-
17	17	200	8	M12 STUD + 4No NUTS + 2No FLAT WASHERS + 1No Ø50mm WASHER (FOR FALL ARREST SYSTEM)	500mm	GRADE 8.8	3.56 kg
18	18	205	1	CHS 76.1x5mm	2200mm	S355J2H	19.29 kg
19	TPL-A	303	1	LOG MOUNTING BRACKET	610mm	S355J2H	6.91 kg
20	TPL-B	303	3	LOG MOUNTING BRACKET	610mm	S355J2H	20.73 kg
						Total Weight:	234.6 kg

- All steel hot dip galvanized
- All U-BOLTS to be FLA supply, each Supplied with 4 Full Nuts, 2 Flat Washers and 2 Spring Washers

NOTES:

1. WELDING TO BE IN ACCORDANCE WITH BS EN 1011-1:2009
2. LINEAR DIMS TO BE WITHIN ±1mm;
3. ANGULAR TOLERANCES TO BE WITHIN 0.5°
4. WELDING SYMBOLS ARE IN ACCORDANCE WITH BS EN 22553:1995
5. ALL PROFILE EDGES TO BE DRESSED AND SHARP CORNERS REMOVED
6. ALL WELD SIZES ARE FINAL SIZES
7. ALL WELDED JOINTS ARE TO BE PICKLE TIGHT
8. ALL STEELWORK TO BE BS EN 10025 GRADE S275 J0 UNO
9. HOT DIPPED GALVANISED TO BS EN ISO 1461. (ALL HOLLOW SECTIONS TO BE GRADE S355 J0H)
10. ALL STEEL IS TO BE SUPPLIED IN ACCORDANCE WITH EN 1090 TO EXECUTION CLASS 2
11. ALL NON PRE-LOADED BOLTS TO BE COMPLIANT STRUCTURAL BOLTS TO BS EN ISO 15048 PARTS 1&2.
12. STEELWORK COMPONENTS SHALL BE HOT DIP GALVANISED TO ACHIEVE A "VERY HIGH" DURABILITY FOR AN ENVIRONMENT CATEGORY CODE C4 FROM TABLE 1 IN BS EN ISO 14713
13. BOLTS AND NUTS SHALL BE SUPPLIED IN ACCORDANCE WITH BS 7371, SPUN GALVANISED IN ACCORDANCE WITH ISO 10684, THE NUTS RE-TAPPED AFTER GALVANISING, AND THE THREADS TREATED WITH GREASE.
14. ALL BOLTS TO BE CUT ON SITE TO EXTEND MAX 10mm BEYOND THE NUT WHEN TIGHTENED UNO.
15. ALL SITE DRILLED HOLE/CUT ENDS TO BE TREATED WITH METAFLUX 70-40 ZINC PASTE FOLLOWED BY 1 COAT OF 7-42 ZINC ALU OR 70-16 ALUMINIUM SPRAY

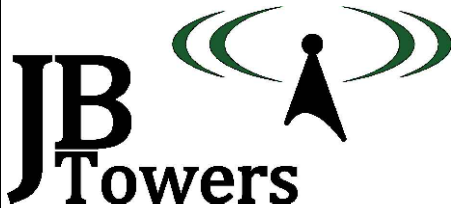

01	FIRST ISSUE				TT	03/06/19
REV	REV				BY	DATE
SCALE AS SHOWN		DRAWN	AM	CHECKED	MP	APPROVED JBT
WHEN PRINTED AT A3		DATE	03/06/19	DATE	03/06/19	DATE 03/06/19
ALL DIMENSIONS IN mm UNLESS OTHERWISE STATED. THIS DRAWING TO BE READ IN CONJUNCTION WITH OTHER RELEVANT DRAWINGS.						

TITLE
PARTS LIST


SITE ADDRESS
WESTER ERCHITE
DORES, INVERNESS
HIGHLAND
IV2 6TX

ARQIVA REF. 141776	DRG No. 305	REV 01
-----------------------	----------------	-----------

ALL SCALES AS SHOWN WHEN PRINTED AT A3




ALL SCALES AS SHOWN WHEN PRINTED AT A3

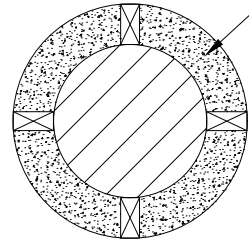


BACKFILL WITH EXCAVATED SPOIL MIXED WITH PERMA-SOIL SOIL STABILISER (OR SIMILAR APPROVED) AS PER MANUFACTURER'S RECOMMENDATIONS

PORPOSED INSTALLATION
PLAN VIEW
Scale 1:20

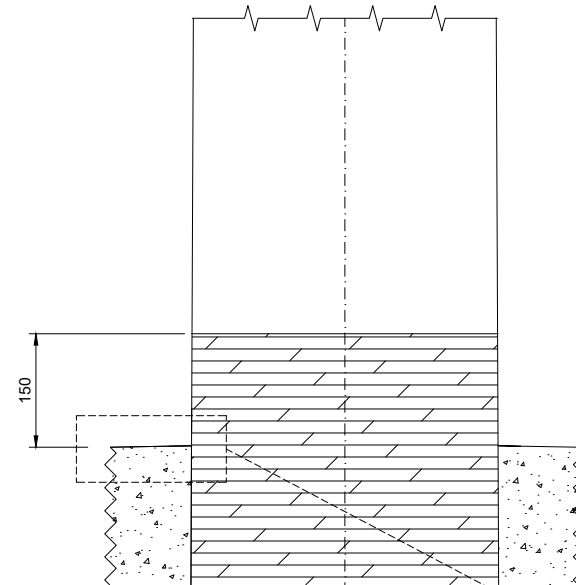

WATER PROOFING
Scale 1:10

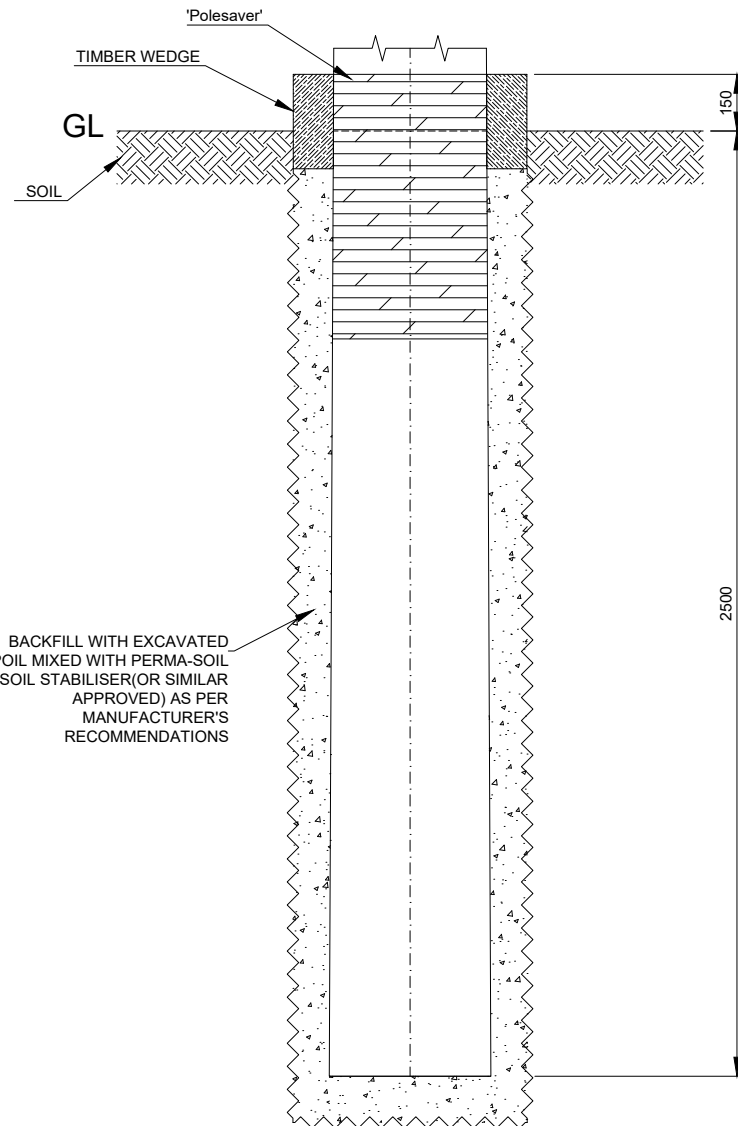

PORPOSED INSTALLATION
ELEVATION
Scale 1:20

TIMBER POLE INSTALLATION:


1. REFER TO DRG 200 FOR TIMBER POLE ORIENTATION.
2. ANY OVERDIG AT BASE OF HOLE TO BE FILLED WITH EXCAVATED SPOIL MIXED WITH PERMA-SOIL STABILISER.
3. POLE TO BE WRAPPED IN 'POLESAVER' AND INSTALLED AND LEVELED IN OPENING. TIMBERS TO BE USED TO HOLD POLE IN POSITION & THEN ANNULUS FILLED WITH EXCAVATED SPOIL MIXED WITH PERMA-SOIL SOIL STABILISER.
4. REMOVE TIMBER WEDGES ONCE BACKFILL HAS ALMOST REACHED UNDERSIDE OF WEDGES & CONTINUE TO BACKFILL TO GL.
5. ALL BACK-FILL MATERIAL TO BE PLACED AND COMPACTED IN 150mm THICK LAYERS.

VOIDS LEFT BY TIMBER WEDGES TO BE FILLED WITH EXCAVATED SPOIL MIXED WITH PERMA-SOIL SOIL STABILISER

1:60 FALL

'POLESAVER'

ENLARGED DETAIL
Scale 1:11

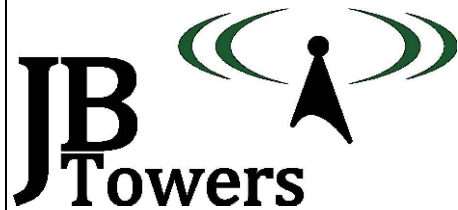

01	FIRST ISSUE				TT	13/06/19
REV	REV				BY	DATE
SCALE AS SHOWN		DRAWN	AM	CHECKED	MP	APPROVED JBT
WHEN PRINTED AT A3		DATE	13/06/19	DATE	13/06/19	DATE 13/06/19
ALL DIMENSIONS IN mm UNLESS OTHERWISE STATED.						THIS DRAWING TO BE READ IN CONJUNCTION WITH OTHER RELEVANT DRAWINGS.

TITLE
FOUNDATION DETAILS

SITE ADDRESS

WESTER ERCHITE
DORES, INVERNESS
HIGHLAND
IV2 6TX

ARQIVA REF.
141776

DRG No.
400

REV
01

ALL SCALES AS SHOWN WHEN PRINTED AT A3



ALL SCALES AS SHOWN WHEN PRINTED AT A3