

DRAWING ISSUE SHEET

[illegible]



ASSUMED EXISTING
FEEDER ROUTE

ARQIVA CABIN

17.0m PROPOSED TIMBER POLE

17.0m EXISTING TIMBER POLE

PROPOSED FEEDER ROUTE

1500

1000



C

B

A


N90 MARK

NOTES:
CLIMBING FACE - FACE C
STEP PEGS ON FACES B & D

ALL SCALES AS SHOWN WHEN PRINTED AT A3



ALL SCALES AS SHOWN WHEN PRINTED AT A3

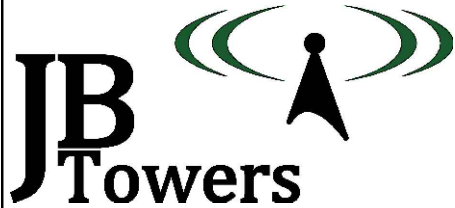

01	FIRST ISSUE				AM	24/04/19
REV	REV				BY	DATE
SCALE AS SHOWN WHEN PRINTED AT A3		DRAWN	AM	CHECKED	MP	APPROVED JBT
		DATE	24/04/19	DATE	24/04/19	DATE 24/04/19
ALL DIMENSIONS IN mm UNLESS OTHERWISE STATED. THIS DRAWING TO BE READ IN CONJUNCTION WITH OTHER RELEVANT DRAWINGS.						


TITLE
YNYS PENNAL
SITE PLAN

SITE ADDRESS
YNYS FARM
YNYS PENNAL
MACHYNLLETH
GWYNEDD
SY20 9LD

ARQIVA REF.
141871

DRG No.
100

REV
01

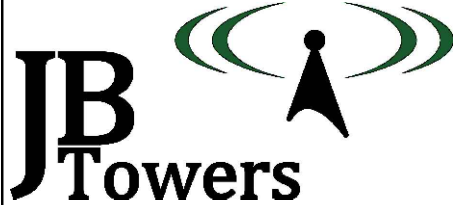

01	FIRST ISSUE			AM	24/04/19
REV	REV			BY	DATE
SCALE AS SHOWN		DRAWN	AM	CHECKED	MP
WHEN PRINTED AT A3		DATE	24/04/19	DATE	24/04/19
		DATE	24/04/19	DATE	24/04/19
ALL DIMENSIONS IN mm UNLESS OTHERWISE STATED. THIS DRAWING TO BE READ IN CONJUNCTION WITH OTHER RELEVANT DRAWINGS.					

TITLE

YNYS PENNAL

GENERAL ARRANGEMENT

SHEET 1 OF 3

SITE ADDRESS

YNYS FARM

YNYS PENNAL

MACHYNLLETH

GWYNEDD

SY20 9LD

ARQIVA REF.



141871

DRG No.

200

REV

01

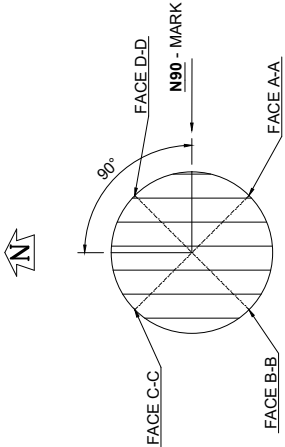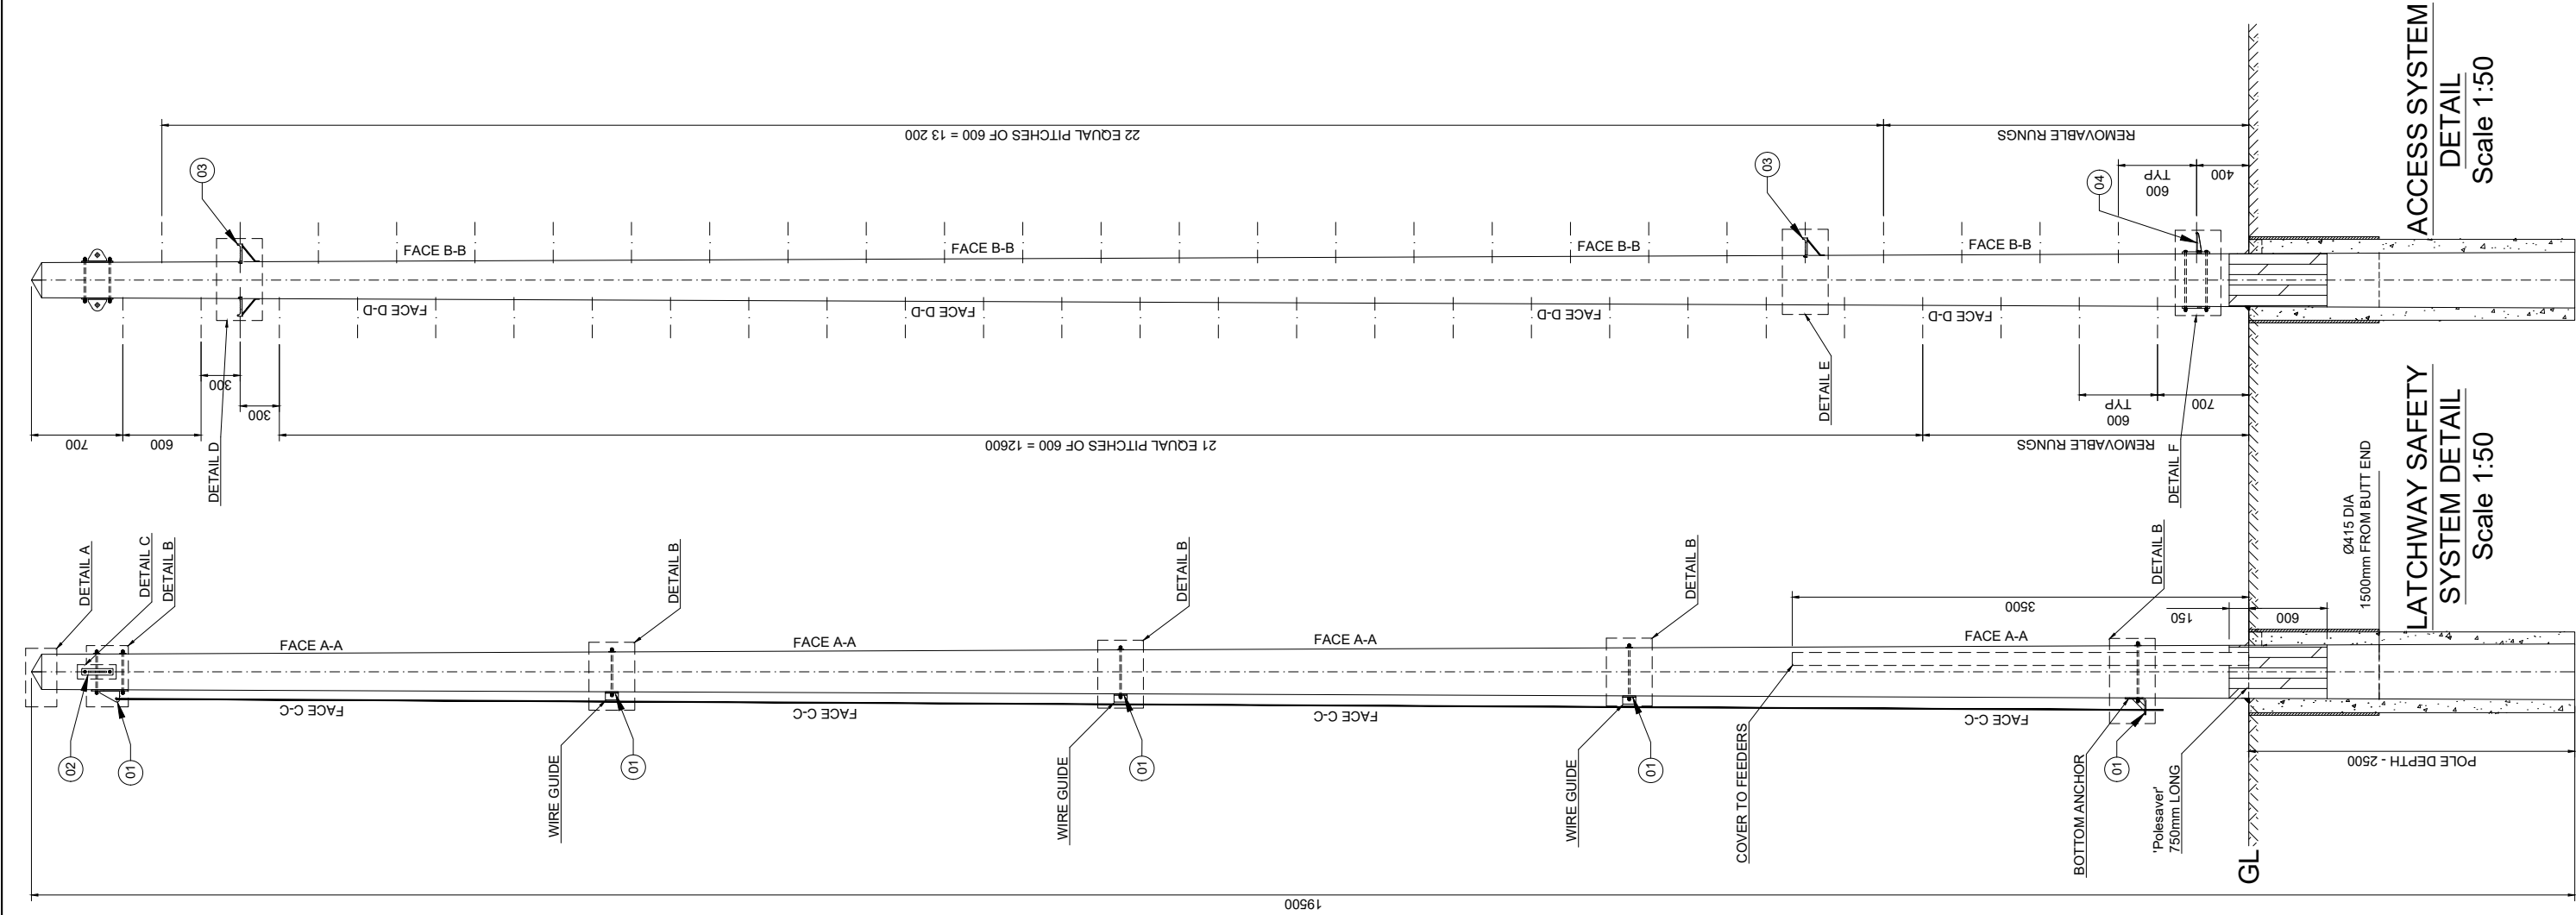

POLE ORIENTATION

Scale 1:20

NOTES

1. SEE DRAWING 304 FOR PARTS LIST
2. ALL BOLTS TO BE CUT ON SITE TO EXTEND MAX 10mm BEYOND THE NUT WHEN TIGHTENED UNO.
3. ALL SITE DRILLED HOLE/CUT ENDS TO BE TREATED WITH METAFUX 70-40 ZINC PASTE FOLLOWED BY 1 COAT OF 7-42 ZINC ALU OR 70-16 ALUMINIUM SPRAY

TIMBER POLE

1. POLE TO BE SUPPLIED IN ACCORDANCE WITH BS EN14229 & SHALL HAVE MIN. CHARACTERISTIC BENDING STRENGTH OF 30N/mm2 & MIN. YOUNGS MODULUS (PARALLEL TO GRAIN) OF 10KN/mm2.
2. MARKINGS ON FINISHED POLE SHALL BE AT 4m FROM BUTT AND COMPLY WITH BS EN 14229 UNO
3. AS FAR AS PRACTICABLE ALL CUTTING, SCARFING & DRILLING TO BE DONE BEFORE CREOSOTING. IF NOT ALL CUT, DRILLED & SCARFED SURFACES TO BE COATED WITH A MIXTURE OF CREOSOTE & TAR.
4. POLE TO BE PRESSURE IMPREGNATED WITH CREOSOTE IN ACCORDANCE WITH BS EN 14229
5. MINIMUM DIAMETERS
TOP - Ø205mm
BOTTOM - Ø430mm
6. 19.5m LONG POLE TO BE SOURCED BY TRIMMING 20m LONG POLE BY 0.5m AT THE TOP

PLANTING




1. CAT SCANNER IS TO BE USED IN ORDER TO CONFIRM THE POSITIONS OF BURIED SERVICES.
2. 'Perma-Soil Stabiliser' OR A SIMILAR APPROVED SHOULD BE USED IN ACCORDANCE WITH THE MANUFACTURER'S RECOMMENDATION.
3. ANY MATERIAL USED FOR BACK-FILLING IS TO BE OF EQUAL OR BETTER QUALITY THAN THE EXCAVATED MATERIAL.
4. ALL BACK-FILLING MATERIAL IS TO BE PLACED AND COMPACTED IN 150mm THICK LAYERS.
5. TIMBER POLE TO BE PLANTED WITH N90 MARKING AT 3.5m FROM BUT FACING 90° FROM NORTH (CLOCKWISE)

ACCESS SYSTEM
DETAIL

Scale 1:50

LATCHWAY SAFETY
SYSTEM DETAIL

Scale 1:50

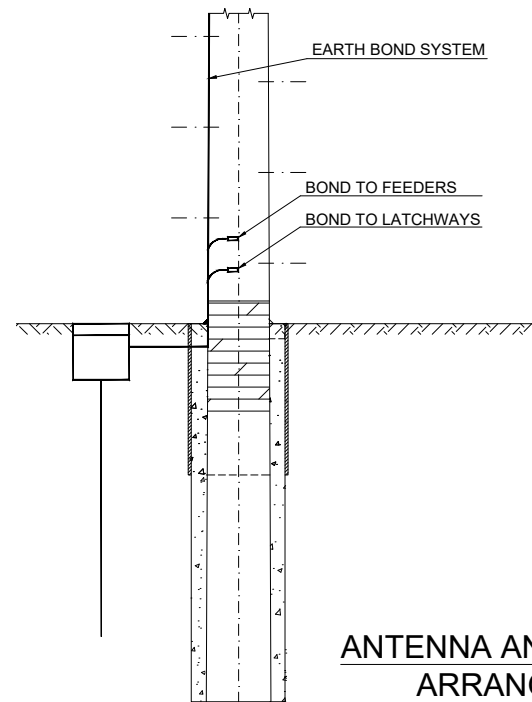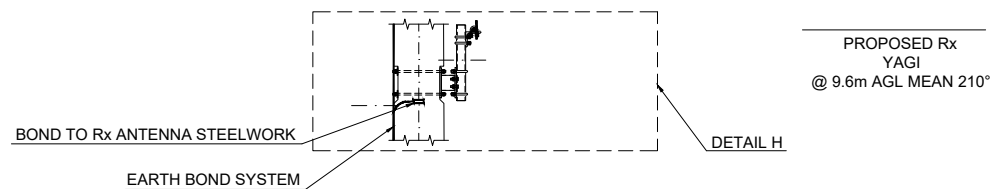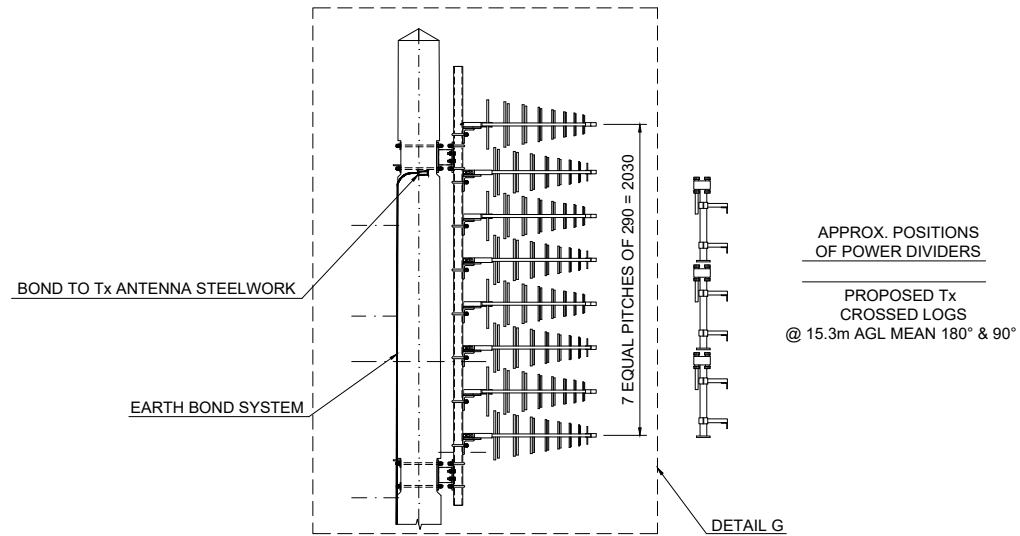

NOTES



1. AS FAR AS IS PRACTICABLE ALL CUTTING SCARFING AND DRILLING TO BE DONE BEFORE CREOSOTING. WHERE THIS IS NOT POSSIBLE ALL CUT, DRILLED, AND SCARFED SURFACES TO BE COATED WITH A MIXTURE OF CREOSOTE AND TAR

FEEDERS

1. SUPPLY OF FEEDERS BY OTHERS LCF78-50 TO Tx ANTENNA & LCF12-50 TO Rx ANTENNA
2. FEEDERS FIXED AT 1000mm CENTRES

EARTHING

1. CONNECT EARTH BOND TO NEW EARTHING SYSTEM
2. MAXIMUM VALUE FOR GROUND RESISTANCE TO BE 10 OHMS
3. CABLE OR TAPE TO BE FIXED TO POLE AT 1000mm CENTRES
4. EARTHING SHOULD COMPLY WITH ARQIVA'S DOCUMENT BOS147

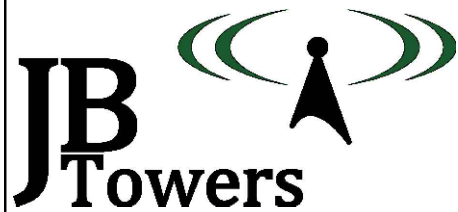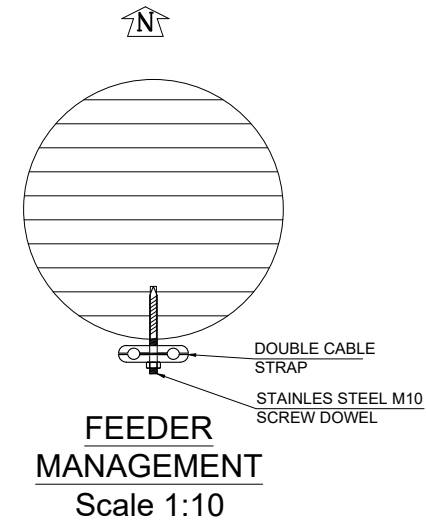


01	FIRST ISSUE		AM 24/04/19
REV	REV		BY DATE
SCALE AS SHOWN WHEN PRINTED AT A3		DRAWN AM DATE 24/04/19	CHECKED MP DATE 24/04/19
		APPROVED JBT DATE 24/04/19	
ALL DIMENSIONS IN mm UNLESS OTHERWISE STATED. THIS DRAWING TO BE READ IN CONJUNCTION WITH OTHER RELEVANT DRAWINGS.			

TITLE		SITE ADDRESS		
YNYS PENNAL		YNYS FARM		
GENERAL ARRANGEMENT		YNYS PENNAL		
SHEET 2 OF 3		MACHYNLLETH		
		GWYNEDD		
		SY20 9LD		
ARQIVA REF. 141871		DRG No. 200	REV 01	

ALL SCALES AS SHOWN WHEN PRINTED AT A3




ALL SCALES AS SHOWN WHEN PRINTED AT A3

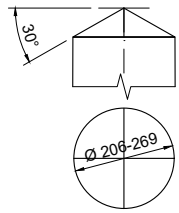


- NOTES:
1. A SINGLE COAT OF TIMBER COMPATIBLE BITUMINOUS PAINT (E.G. BIRD BRAND BLACK BITUMINOUS PAINT OR SIMILAR APPROVED PRODUCT) TO BE APPLIED TO THE UPPER SURFACES AT THE TOP OF THE POLE.
 2. PAINT TO BE APPLIED ON SITE JUST BEFORE ERECTION
- FORM: 4 WAY PYRAMID / CONE


DETAIL A - TIMBER POLE TOP
Scale 1:20

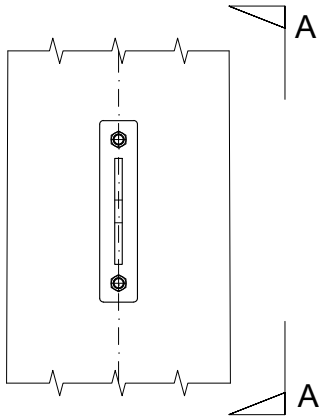


DETAIL C - FALL ARREST
ATTACHMENT POINT
Scale 1:10

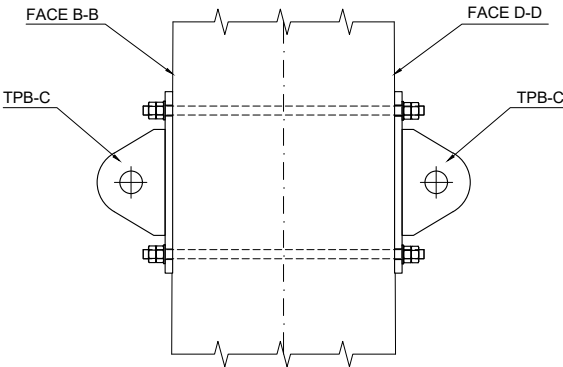

VIEW A-A
Scale 1:10

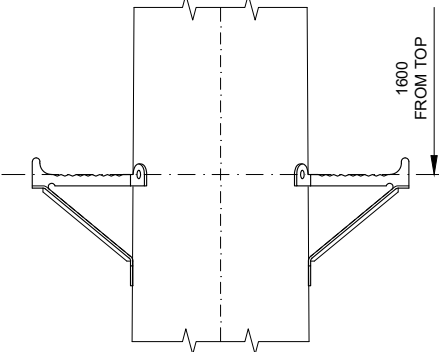


DETAIL D - ANTENNA
ACCESS CLIMBING STEP
Scale 1:10

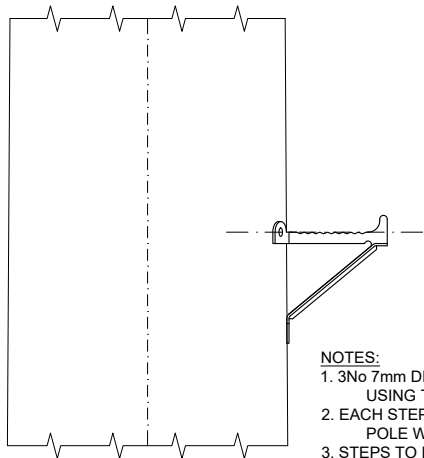


DETAIL E - PERMANENT
CLIMBING STEPS
Scale 1:10


- NOTES:
1. 3No 7mm DIA 70mm LONG PILOT HOLES TO BE DRILLED USING THE STEP AS A TEMPLATE
 2. EACH STEP SHOULD BE FIXED TO THE TIMBER POLE WITH 3No 10mm COACH SCREWS 75mm LONG
 3. STEPS TO BE INSTALLED ON FACES B-B & D-D ONLY

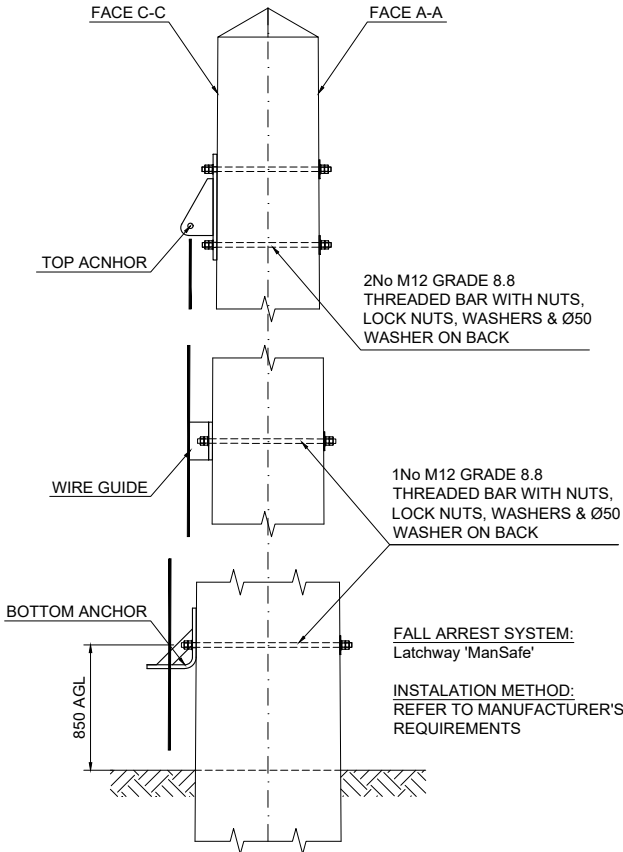

DETAIL B - FALL ARREST SYSTEM
Scale 1:20

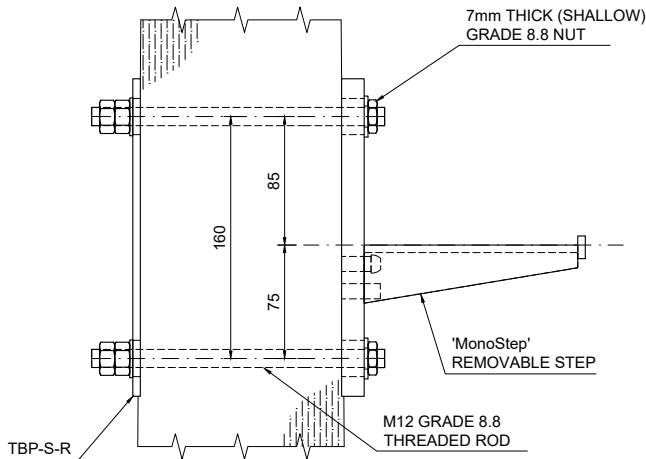

DETAIL F - REMOVABLE
CLIMBING STEPS
Scale 1:5

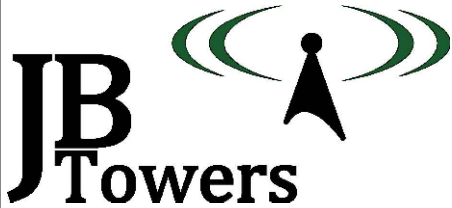

01	FIRST ISSUE	AM	24/04/19
REV	REV	BY	DATE
SCALE AS SHOWN WHEN PRINTED AT A3	DRAWN DATE	AM 24/04/19	CHECKED DATE
	MP 24/04/19	APPROVED DATE	JBT 24/04/19
ALL DIMENSIONS IN mm UNLESS OTHERWISE STATED. THIS DRAWING TO BE READ IN CONJUNCTION WITH OTHER RELEVANT DRAWINGS.			

TITLE
YNYS PENNAL
GENERAL ARRANGEMENT
SHEET 3 OF 3

SITE ADDRESS
YNYS FARM
YNYS PENNAL
MACHYNLLETH
GWYNEDD
SY20 9LD

ARQIVA REF.
141871


DRG No.
200

REV
01

ALL SCALES AS SHOWN WHEN PRINTED AT A3



ALL SCALES AS SHOWN WHEN PRINTED AT A3

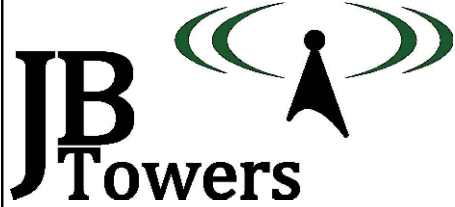

01	FIRST ISSUE			AM	24/04/19
REV	REV			BY	DATE
SCALE AS SHOWN		DRAWN	AM	CHECKED	MP
WHEN PRINTED AT A3		DATE	24/04/19	DATE	24/04/19
				APPROVED	JBT
				DATE	24/04/19
ALL DIMENSIONS IN mm UNLESS OTHERWISE STATED. THIS DRAWING TO BE READ IN CONJUNCTION WITH OTHER RELEVANT DRAWINGS.					

TITLE

YNYS PENNAL

TIMBER POLE HOLE SET OUT

SHEET 1 OF 2

SITE ADDRESS

YNYS FARM

YNYS PENNAL

MACHYNLLETH

GWYNEDD

SY20 9LD

ARQIVA REF.


141871

DRG No.


201

REV

01

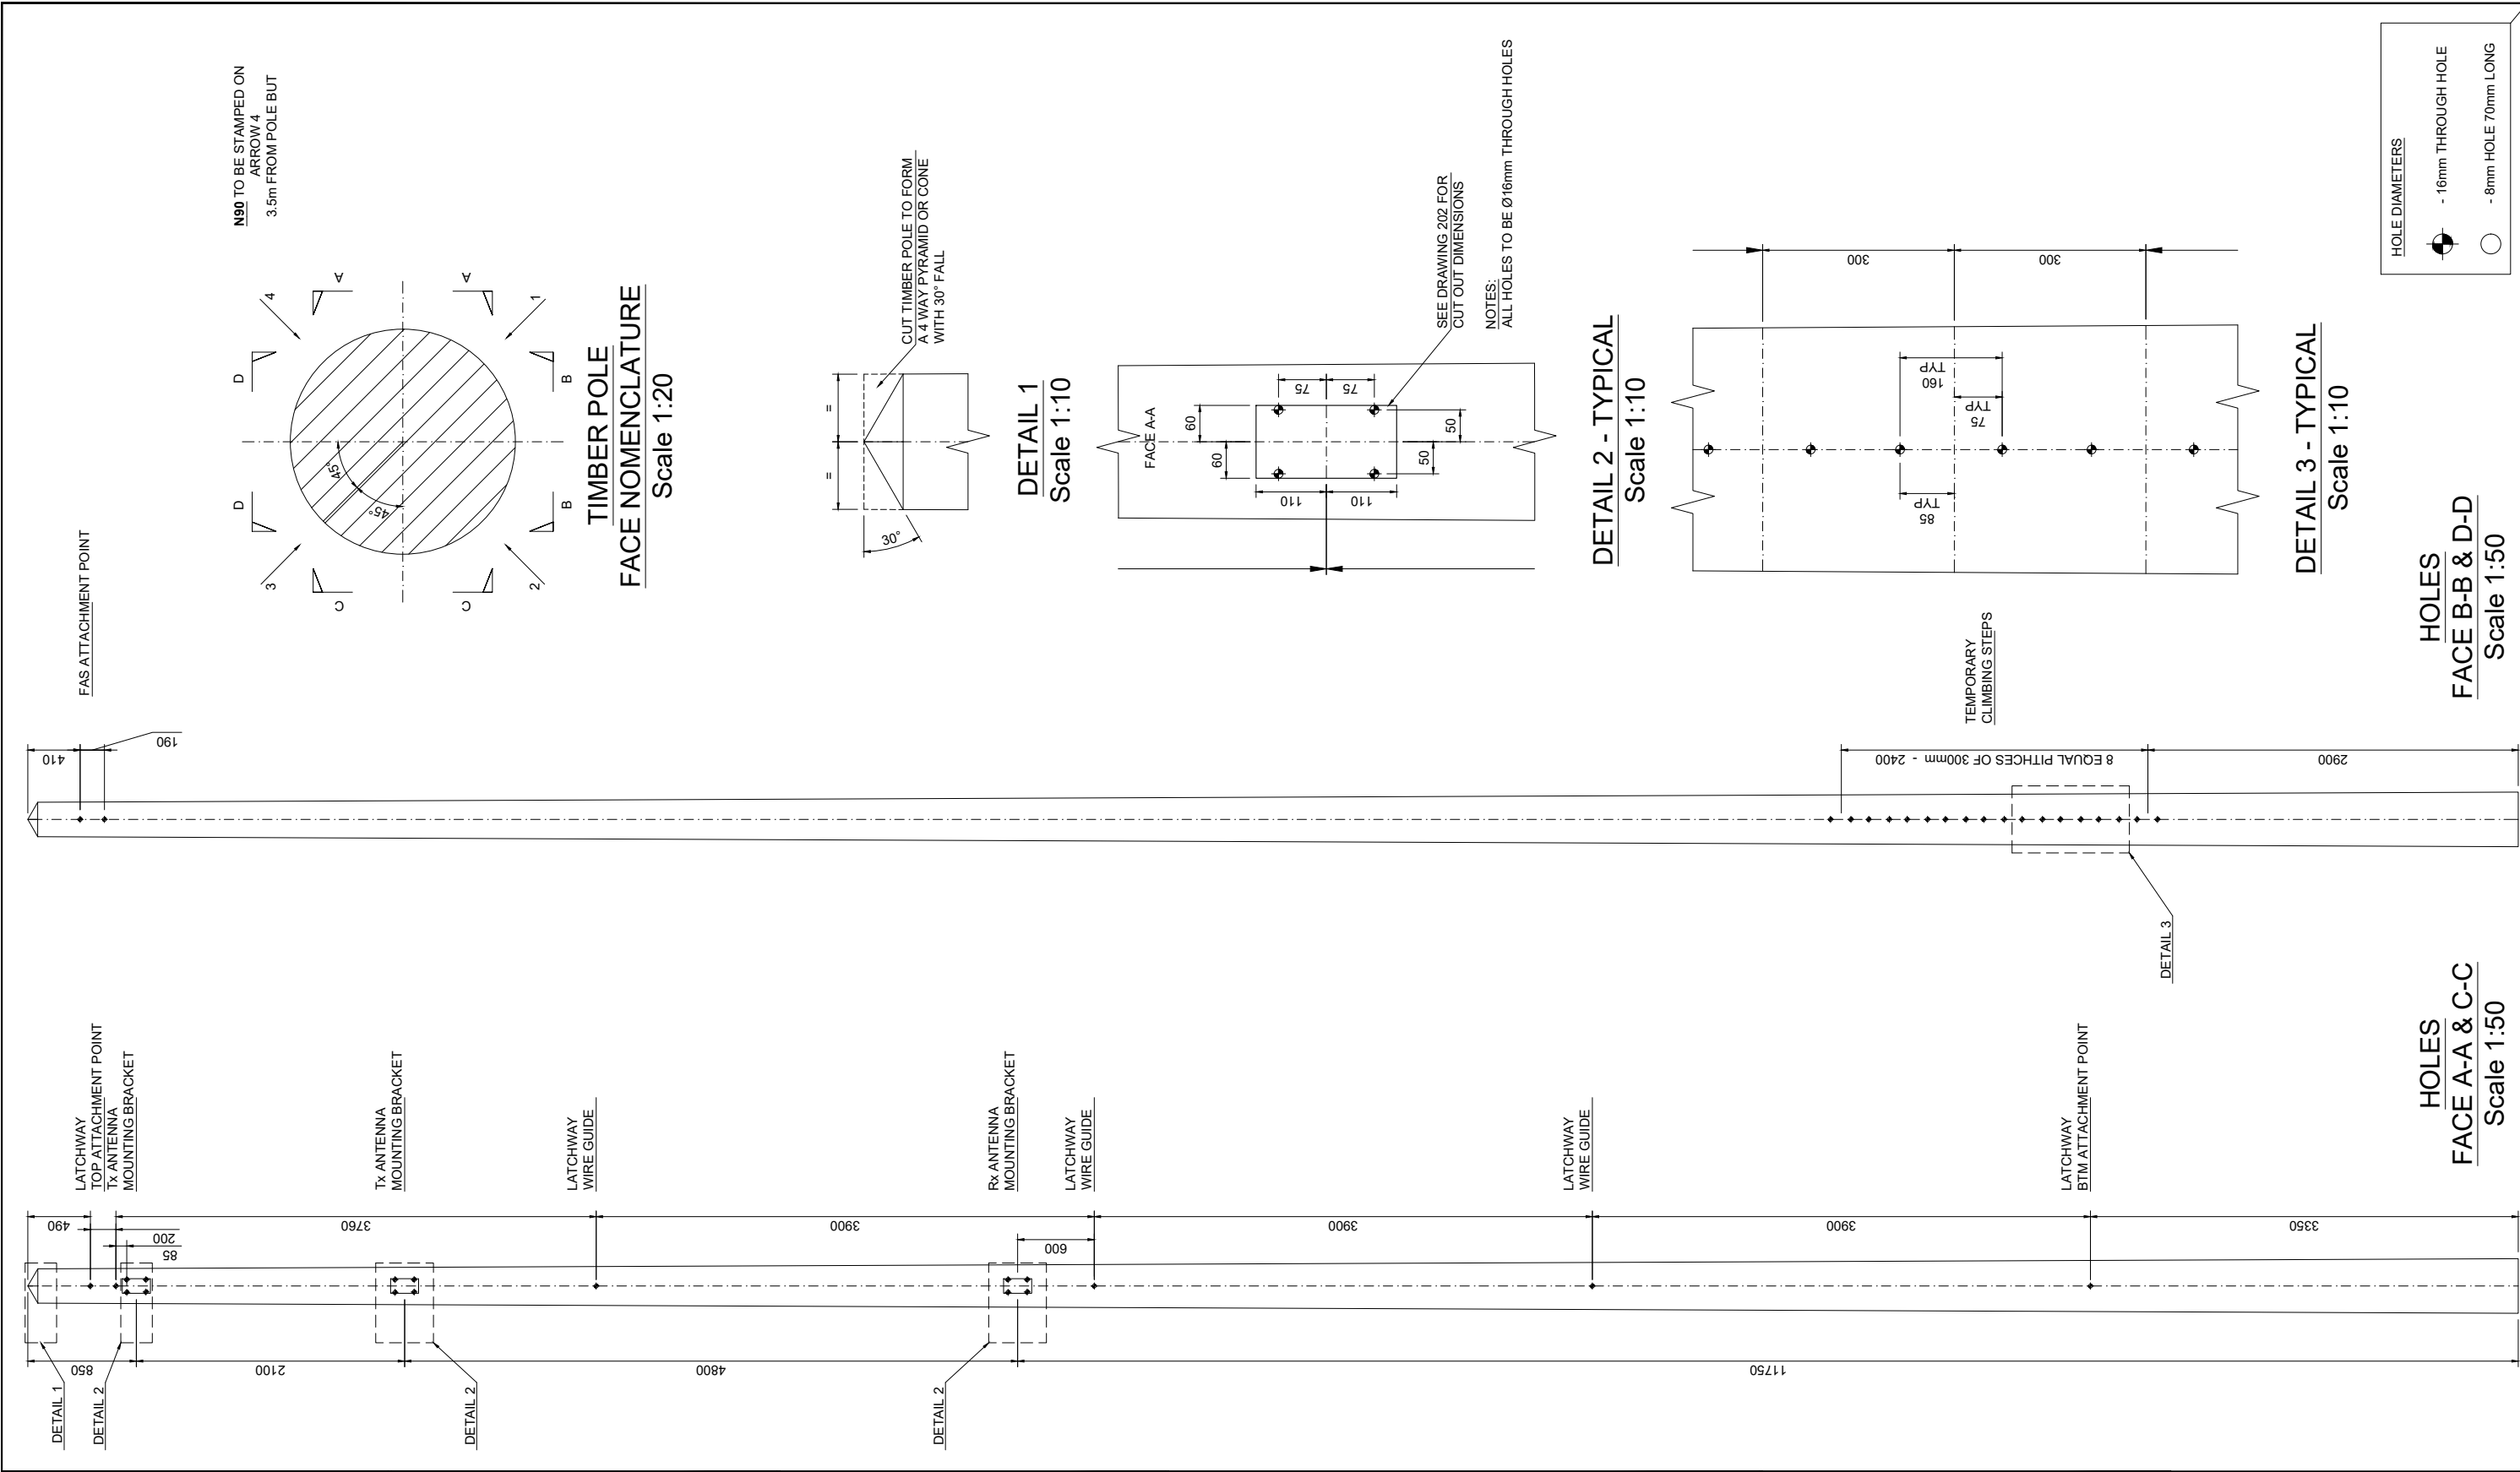

ALL SCALES AS SHOWN WHEN PRINTED AT A3

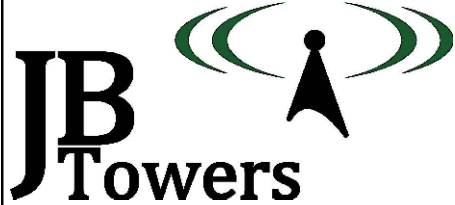

01	FIRST ISSUE			AM	24/04/19
REV	REV			BY	DATE
SCALE AS SHOWN		DRAWN	AM	CHECKED	MP
WHEN PRINTED AT A3		DATE	24/04/19	DATE	24/04/19
		APPROVED		JBT	
		DATE		24/04/19	
ALL DIMENSIONS IN mm UNLESS OTHERWISE STATED. THIS DRAWING TO BE READ IN CONJUNCTION WITH OTHER RELEVANT DRAWINGS.					

TITLE

YNYS PENNAL

TIMBER POLE HOLE SET OUT

SHEET 2 OF 2

SITE ADDRESS

YNYS FARM

YNYS PENNAL

MACHYNLLETH

GWYNEDD

SY20 9LD

ARQIVA REF.


141871

DRG No.

201


REV

01

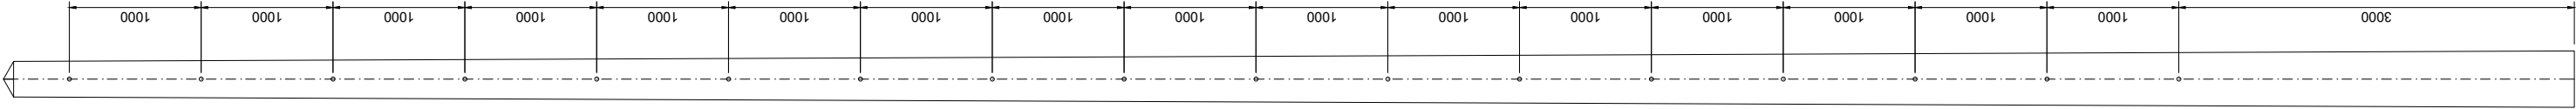

FEEDER BRACKETS

N90 TO BE STAMPED ON
ARROW 4
3.5m FROM POLE BUT

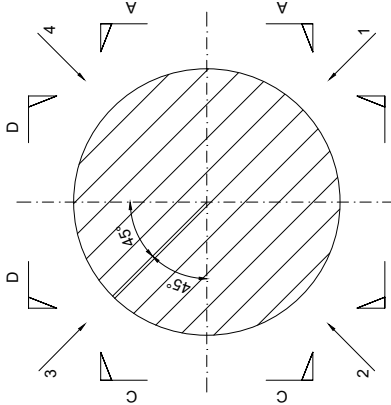

TIMBER POLE
FACE NOMENCLATURE
Scale 1:20

ALL HOLES ON ARROW 1
TO BE Ø8mm & 70mm LONG

HOLES
ARROW 1
Scale 1:50



ALL SCALES AS SHOWN WHEN PRINTED AT A3

ALL SCALES AS SHOWN WHEN PRINTED AT A3

Technical drawing of a rectangular plate with the following specifications:


- Dimensions:**
 - Width: 220 MIN
 - Length: 120 MIN
 - Distance between hole centers (horizontal): 50 FIXED
 - Distance between hole centers (vertical): 75 FIXED
 - Distance from hole center to edge (horizontal): 75 FIXED
 - Distance from hole center to edge (vertical): 75 FIXED
- Holes:** 4No Ø16mm HOLES
- Chamfer:** 45° CHAMFER ON BOTTOM EDGE
- Surface:** FLAT SURFACE 120x220 mm

NOTES:

- DIMENSIONS ANNOTATED AS 'FIXED' ARE TO BE ADHERED TO
-TOLERANCE: +2mm; -2mm
- DIMENSIONS ANNOTATED AS 'VARIABLE' DEPEND ON THE ACTUAL DIAMETER
-TOLERANCE: N/A
- DIMENSIONS ANNOTATED AS 'MIN' PROVIDE THE MINIMUM LENGTH REQUIRED
-TOLERANCE: +50mm; -0mm
- THROUGH HOLES ARE SPECIFIED ON DRAWING 201

Technical drawing of a rectangular plate. The drawing shows a top view with a 45° chamfer on the bottom edge. A dimension line indicates a minimum length of 220 MIN. The drawing is oriented vertically on the page.

ALL SCALES AS SHOWN WHEN PRINTED AT A3

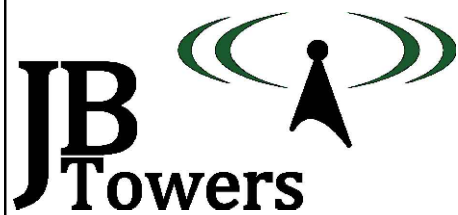

argiva

01	FIRST ISSUE			AM	24/04/19
REV	REV			BY	DATE
SCALE AS SHOWN WHEN PRINTED AT A3	DRAWN	AM	CHECKED	MP	APPROVED
	DATE	24/04/19	DATE	24/04/19	DATE 24/04/19
ALL DIMENSIONS IN mm UNLESS OTHERWISE STATED. THIS DRAWING TO BE READ IN CONJUNCTION WITH OTHER RELEVANT DRAWINGS.					

TITLE

YNYS PENNAL


TIMBER POLE CUT OUT DETAIL

SITE ADDRESS


YNYS FARM
YNYS PENNAL
MACHYNLLETH
GWYNEDD
SY20 9LD

ARQIVA REF.
141871


DRG No.
202REV
01

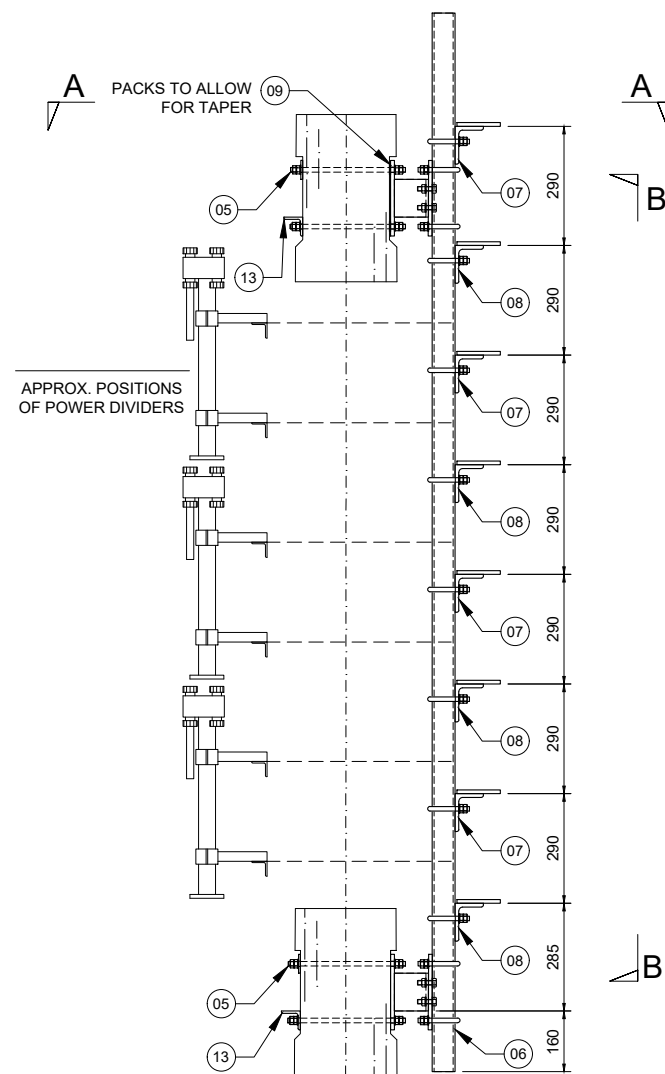


DETAIL G - Tx ANTENNA MOUNT
Scale 1:20

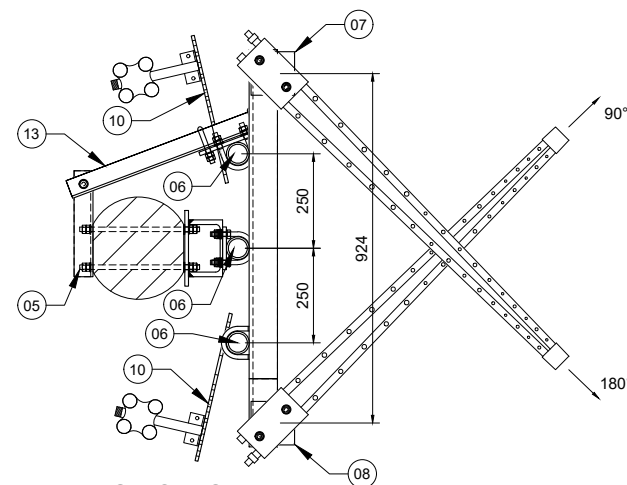

SECTION A-A
Scale 1:20

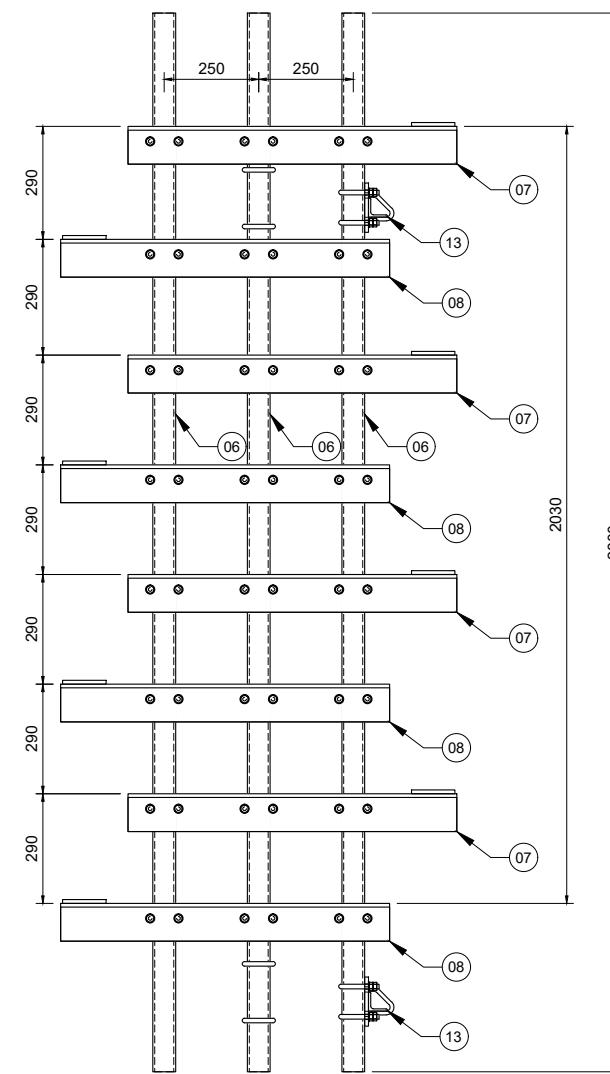

VIEW B-B
Scale 1:20

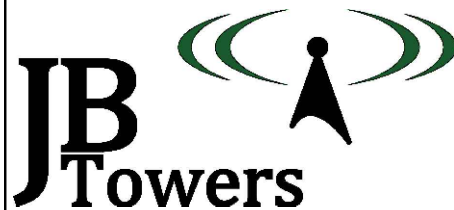


01	FIRST ISSUE			AM	24/04/19
REV	REV			BY	DATE
SCALE AS SHOWN WHEN PRINTED AT A3		DRAWN	AM	CHECKED	MP
		DATE	24/04/19	DATE	24/04/19
				DATE	24/04/19
ALL DIMENSIONS IN mm UNLESS OTHERWISE STATED. THIS DRAWING TO BE READ IN CONJUNCTION WITH OTHER RELEVANT DRAWINGS.					


TITLE		SITE ADDRESS	
ANTENNA MOUNT		YNYS FARM	
DETAIL G		YNYS PENNAL	
		MACHYNLLETH	
		GWYNEDD	
		SY20 9LD	
ARQIVA REF.		DRG No.	REV
141871		203	01

ALL SCALES AS SHOWN WHEN PRINTED AT A3

ALL SCALES AS SHOWN WHEN PRINTED AT A3

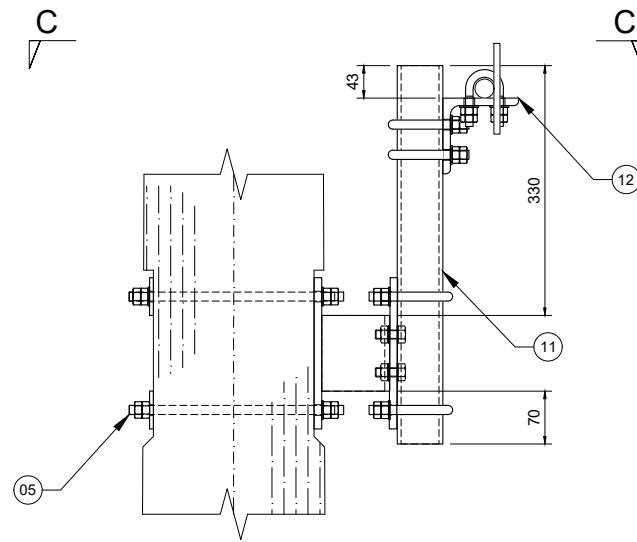

DETAIL H - Rx ANTENNA MOUNT
Scale 1:10

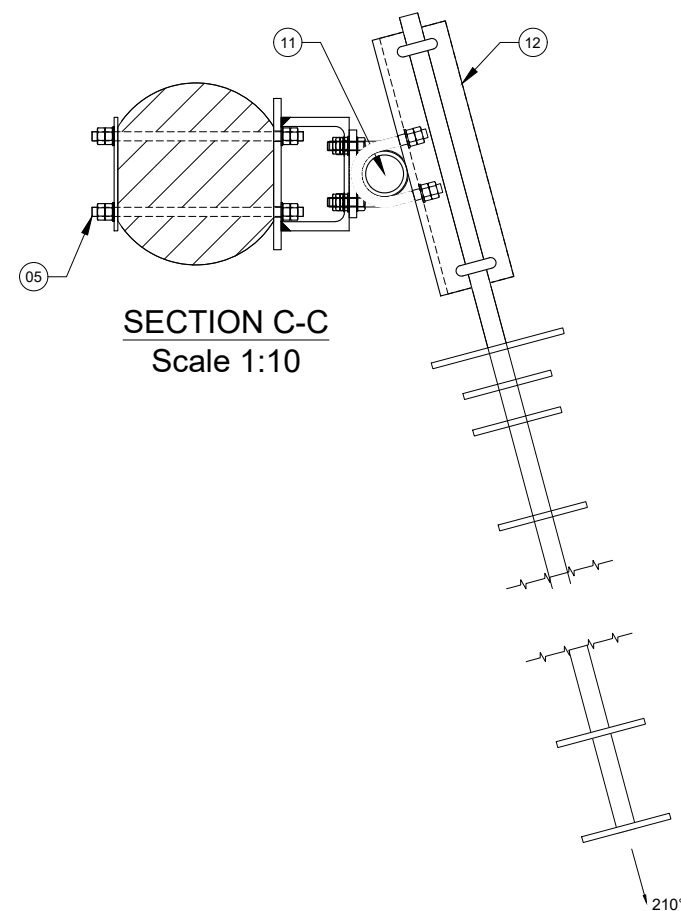


SECTION C-C
Scale 1:10

ALL SCALES AS SHOWN WHEN PRINTED AT A3




ALL SCALES AS SHOWN WHEN PRINTED AT A3

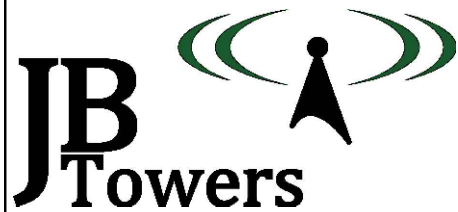

01	FIRST ISSUE			AM	24/04/19
REV	REV			BY	DATE
SCALE AS SHOWN WHEN PRINTED AT A3		DRAWN	AM	CHECKED	MP
		DATE	24/04/19	DATE	24/04/19
		DATE	24/04/19	DATE	24/04/19
ALL DIMENSIONS IN mm UNLESS OTHERWISE STATED. THIS DRAWING TO BE READ IN CONJUNCTION WITH OTHER RELEVANT DRAWINGS.					


TITLE
ANTENNA MOUNT
DETAIL H

SITE ADDRESS		
YNYS FARM YNYS PENNAL MACHYNLLETH GWYNEDD SY20 9LD		
ARQIVA REF. 141871	DRG No. 204	REV 01

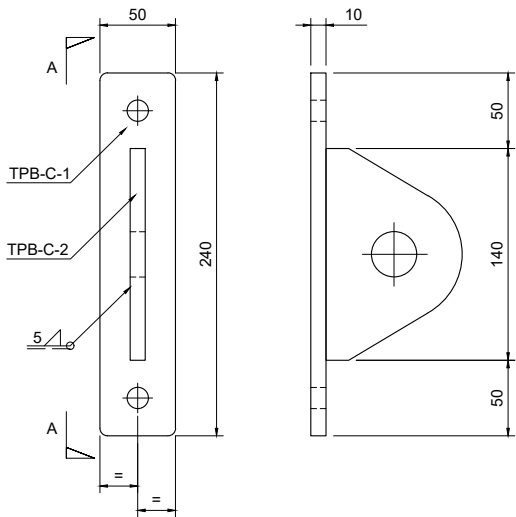

PART TPB-C
Scale 1:5

VIEW A-A
Scale 1:5

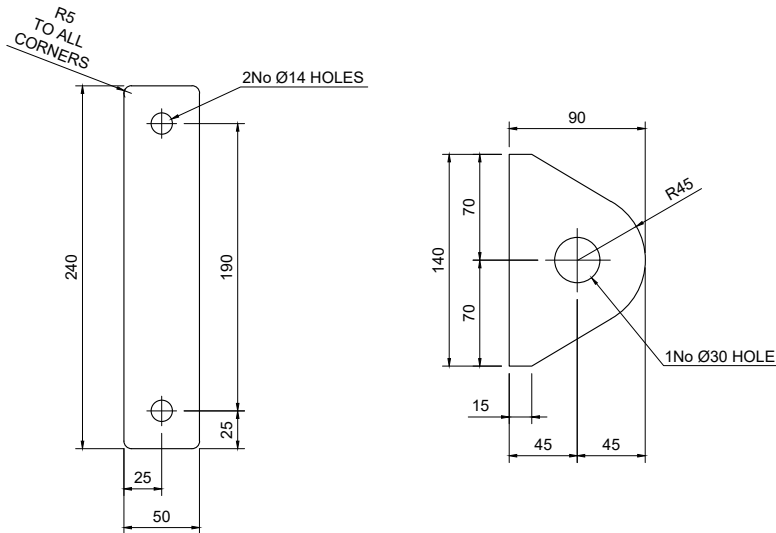


TPB-C-1 - 10mm THICK
Scale 1:5

TPB-C-2 - 10mm THICK
Scale 1:5

Parts list for TPB-C


Item	Part	Quantity	Part description	Length	Material	Weight
01	TPB-C-1	1	240x50x10mm	N/A	S275J0	0.94 kg
02	TPB-C-2	1	140x90x10mm	N/A	S275J0	0.99 kg
03	STUDS	1	M12 STUDDING	350mm	GRADE 8.8	0.31 kg
Total Weight:						2.24 kg

- All steel hot dip galvanized
- Each STUD to be supplied with 4 Full Nuts, 2 Flat Washers and 2 Spring Washers
- For fabrication notes see drawing 304

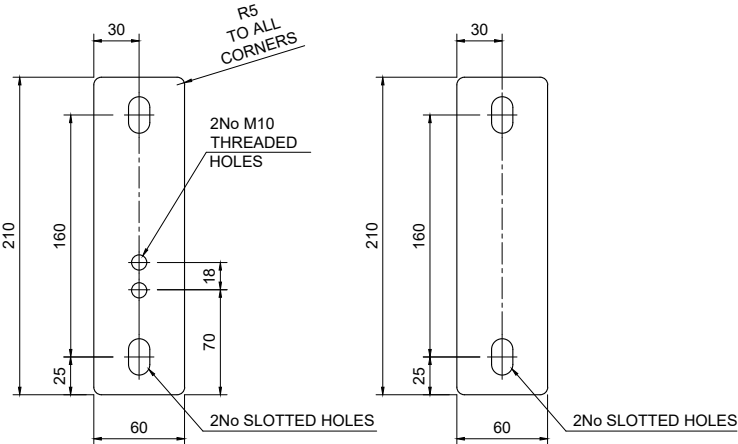

PART TPS-R-1
Scale 1:5

PART TPS-R-2
Scale 1:5

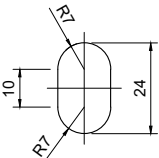


SLOTTED HOLE DETAIL
Scale 1:2

Parts list for TPS-R

Item	Part	Quantity	Part description	Length	Material	Weight
01	TPS-R-1	1	210x60x15mm	N/A	S275J0	1.48 kg
02	TPS-R-2	1	210x60x5mm	N/A	S275J0	0.49 kg
03	STUDS	2	M12 STUDDING	500mm	GRADE 8.8	0.44 kg
04	NUT-S	2	M12 SHALLOW NUT	N/A	GRADE 8.8	-
05	NUT	4	M12 NUT	N/A	GRADE 8.8	-
06	WSH	4	M12 WASHER	N/A	GRADE 8.8	-
Total Weight:						2.85 kg

- All steel hot dip galvanized
- For fabrication notes see drawing 304

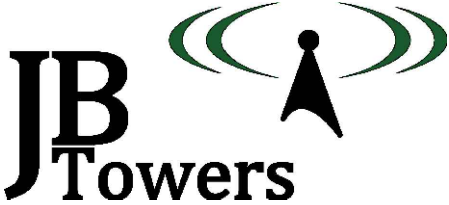

01	FIRST ISSUE	AM	24/04/19
REV	REV	BY	DATE
SCALE AS SHOWN	DRAWN	CHECKED	APPROVED
WHEN PRINTED AT A3	DATE	DATE	DATE
ALL DIMENSIONS IN mm UNLESS OTHERWISE STATED.	THIS DRAWING TO BE READ IN CONJUNCTION WITH OTHER RELEVANT DRAWINGS.		

TITLE
ATTACHMENT POINT &
TEMPORARY STEP DETAILS
PARTS: TPB-C; TPS-R









SITE ADDRESS
YNYS FARM
YNYS PENNAL
MACHYNLLETH
GWYNEDD
SY20 9LD

ARQIVA REF.
141871
DRG No.
300
REV
01

ALL SCALES AS SHOWN WHEN PRINTED AT A3



ALL SCALES AS SHOWN WHEN PRINTED AT A3

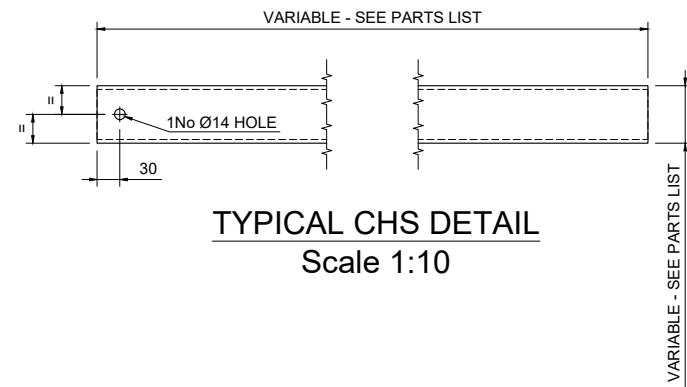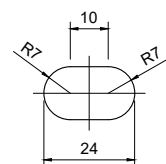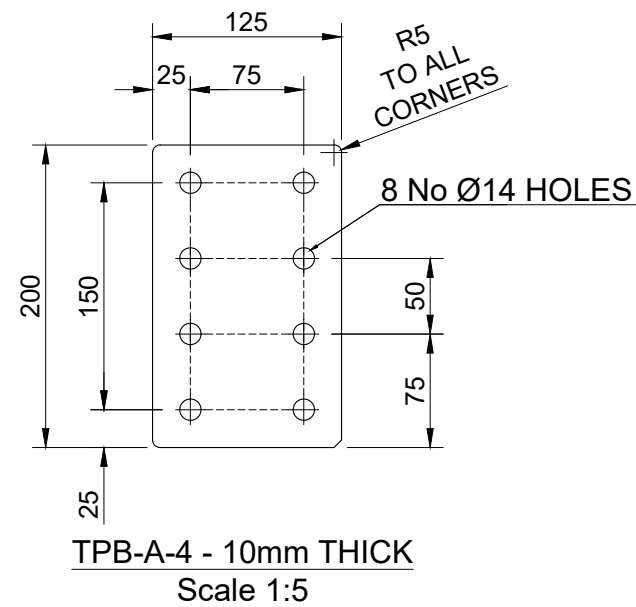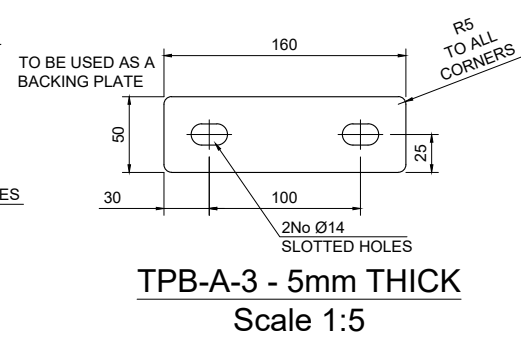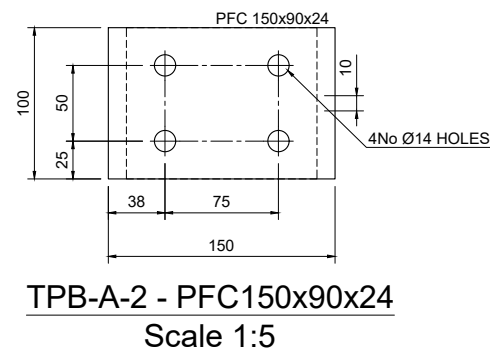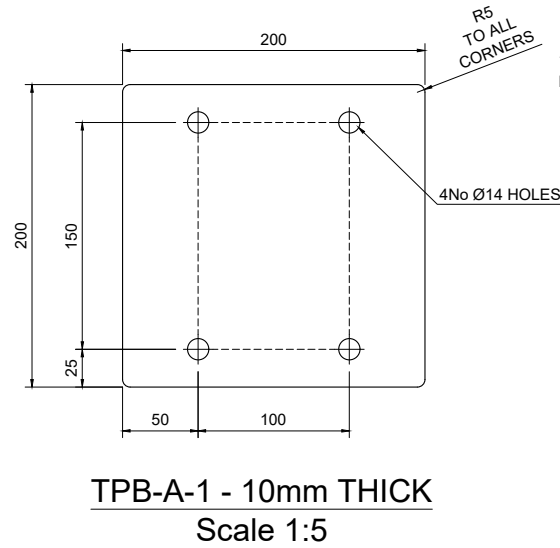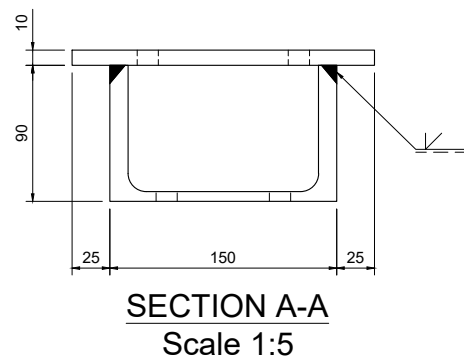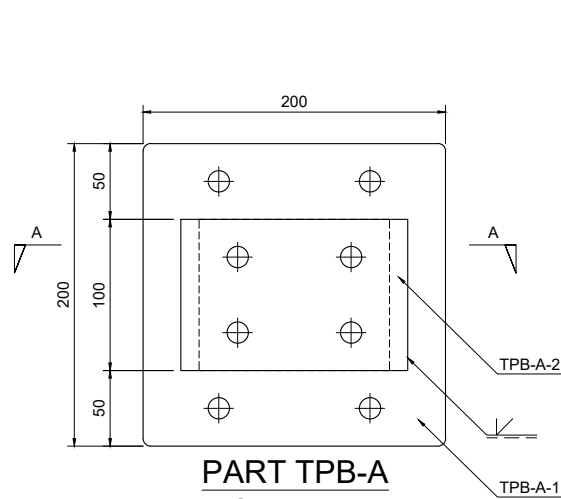


Parts list for TPB-A

Item	Part	Quantity	Part description	Length	Material	Weight
01	TPB-A-1	1	200x200x10mm	N/A	S275J0	3.14 kg
02	TPB-A-2	1	PFC 150x90x24	100mm	S275J0	2.4 kg
03	TPB-A-3	2	160x50x5mm	N/A	S275J0	0.31 kg
04	TPB-A-4	1	200x125x10mm	N/A	S275J0	1.96 kg
05	BOLT	4	M12 45mm LONG (2D+6)	45mm	GRADE 8.8	-
06	STUDS	4	M12 STUDDING	400mm	GRADE 8.8	0.36 kg
07	U-BOLT	2	M12 U-BOLT FOR CHS 60.3mm	N/A	GRADE 8.8	-

- All steel hot dip galvanized
- Each BOLT to be supplied with 1 Full Nut, 1 Form E Flat Washer and 1 Spring Washer
- Each STUD & U-BOLT to be supplied with 4 Full Nuts, 2 Flat Washers and 2 Spring Washers
- For fabrication notes see drawing 304

Total Weight: 8.17 kg

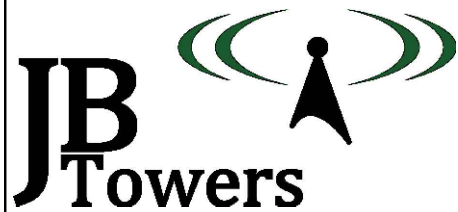


01	FIRST ISSUE	AM	24/04/19
REV	REV	BY	DATE
SCALE AS SHOWN	DRAWN	CHECKED	APPROVED
WHEN PRINTED AT A3	DATE	DATE	DATE
ALL DIMENSIONS IN mm UNLESS OTHERWISE STATED.	THIS DRAWING TO BE READ IN CONJUNCTION WITH OTHER RELEVANT DRAWINGS.		


TITLE	STEELWORK BRACKET & TYPICAL CHS DETAIL		
PART: TPB-A			
SITE ADDRESS	YNYS FARM YNYS PENNAL MACHYNLLETH GWYNEDD SY20 9LD		
ARQIVA REF. 141871	DRG No. 301	REV 01	

ALL SCALES AS SHOWN WHEN PRINTED AT A3



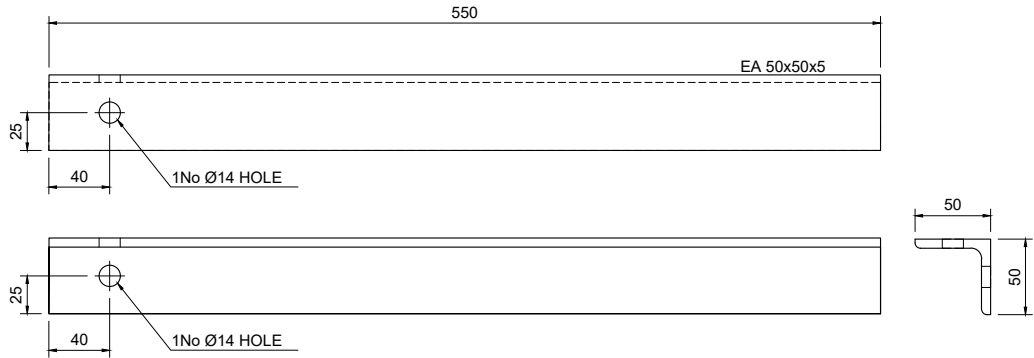

TPA-BR-1 - EA50x50x5
Scale 1:5

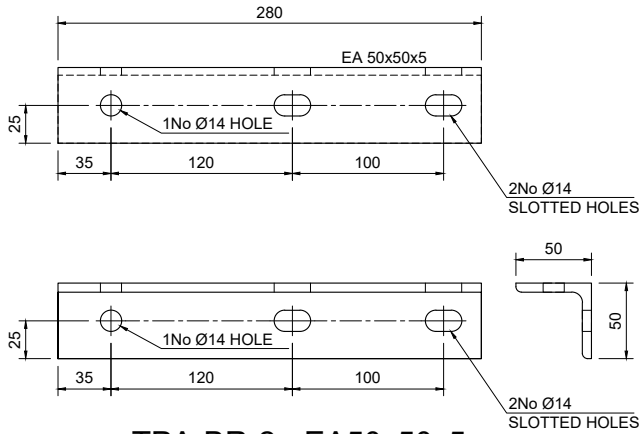


TPA-BR-2 - EA50x50x5
Scale 1:5


Parts list for TPA-BR

Item	Part	Quantity	Part description	Length	Material	Weight
01	TPB-BR-1	1	EA 50x50x5	280mm	S275J0	1.04 kg
02	TPB-BR-2	1	EA 50x50x5	550mm	S275J0	2.05 kg
03	TPB-BR-3	1	130x190x10mm	N/A	S275J0	1.94 kg
04	BOLT	1	M12 SET BOLT - 30mm LONG	N/A	GRADE 8.8	-
05	N-BOLT	2	M12 N-BOLT FOR EA 50x50x6	N/A	GRADE 8.8	-
06	U-BOLT	2	M12 U-BOLT FOR CHS 60.3mm	N/A	GRADE 8.8	-
Total Weight:						5.03 kg


- All steel hot dip galvanized
- Each BOLT to be supplied with 1 Full Nut, 1 Form E FLat Washer and 1 Spring Washer
- Each STUD & U-BOLT to be supplied with 4 Full Nuts, 2 Flat Washers and 2 Spring Washers
- For fabrication notes see drawing 304

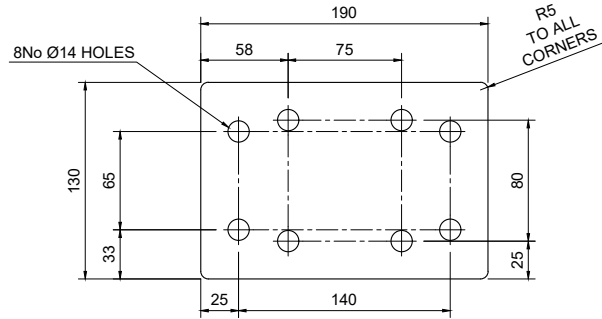

TPB-BR-3 - 10mm THICK
Scale 1:5

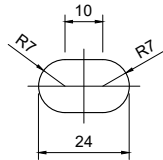

SLOTTED HOLE DETAIL
Scale 1:2



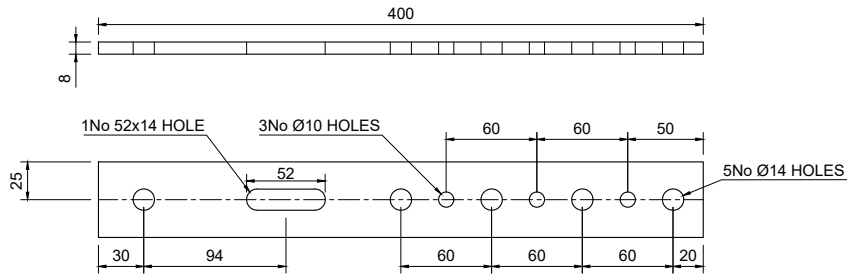


TPA-PD - 8mm THICK
Scale 1:5

Parts list for TPA-PD

Item	Part	Quantity	Part description	Length	Material	Weight
01	TPA-PD	1	400x50x8mm	N/A	S275J0	1.26 kg
02	U-BOLT	1	M12 U-BOLT FOR CHS 60.3mm	N/A	GRADE 8.8	-
Total Weight:						1.26 kg

- All steel hot dip galvanized
- Each U-BOLT to be supplied with 4 Full Nuts, 2 Flat Washers and 2 Spring Washers
- For fabrication notes see drawing 304

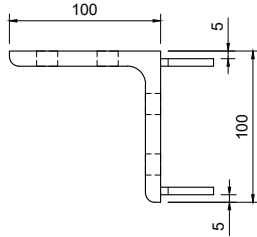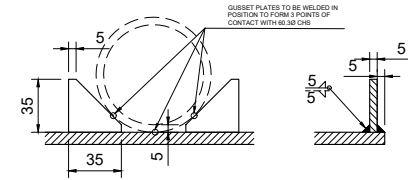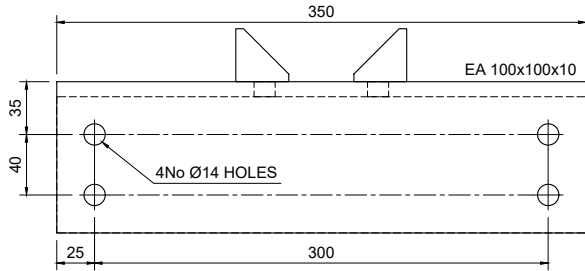


TPY-A - EA100x100x10
Scale 1:5

Parts list for TPY-A

Item	Part	Quantity	Part description	Length	Material	Weight
01	TPY-A	1	EA100x100x10	350mm	S275J0	5.25 kg
02	U-BOLT	2	M12 U-BOLT FOR CHS 25mm	N/A	GRADE 8.8	-
03	U-BOLT	2	M12 U-BOLT FOR CHS 60.3mm	N/A	GRADE 8.8	-
Total Weight:						5.25 kg

- All steel hot dip galvanized
- Each STUD & U-BOLT to be supplied with 4 Full Nuts, 2 Flat Washers and 2 Spring Washers
- Each BOLT to be supplied with 1 Full Nut, 1 Form E FLat Washer and 1 Spring Washer
- For fabrication notes see drawing 304

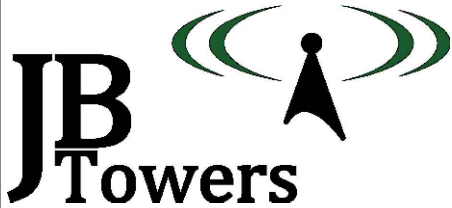

01	FIRST ISSUE	AM	24/04/19
REV	REV	BY	DATE
SCALE AS SHOWN	DRAWN	CHECKED	APPROVED
WHEN PRINTED AT A3	DATE	DATE	DATE
24/04/19	24/04/19	24/04/19	24/04/19
ALL DIMENSIONS IN mm UNLESS OTHERWISE STATED. THIS DRAWING TO BE READ IN CONJUNCTION WITH OTHER RELEVANT DRAWINGS.			

TITLE
BRACING KIT; POWER
DIVIDER STRAP; YAGI MOUNT
PARTS: TPA-BR; TPA-PD;
TPY-A

SITE ADDRESS
YNYS FARM
YNYS PENNAL
MACHYNLLETH
GWYNEDD
SY20 9LD

ARQIVA REF.
141871




DRG No.
302

REV
01

ALL SCALES AS SHOWN WHEN PRINTED AT A3




ALL SCALES AS SHOWN WHEN PRINTED AT A3

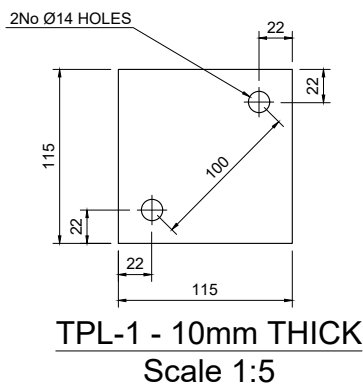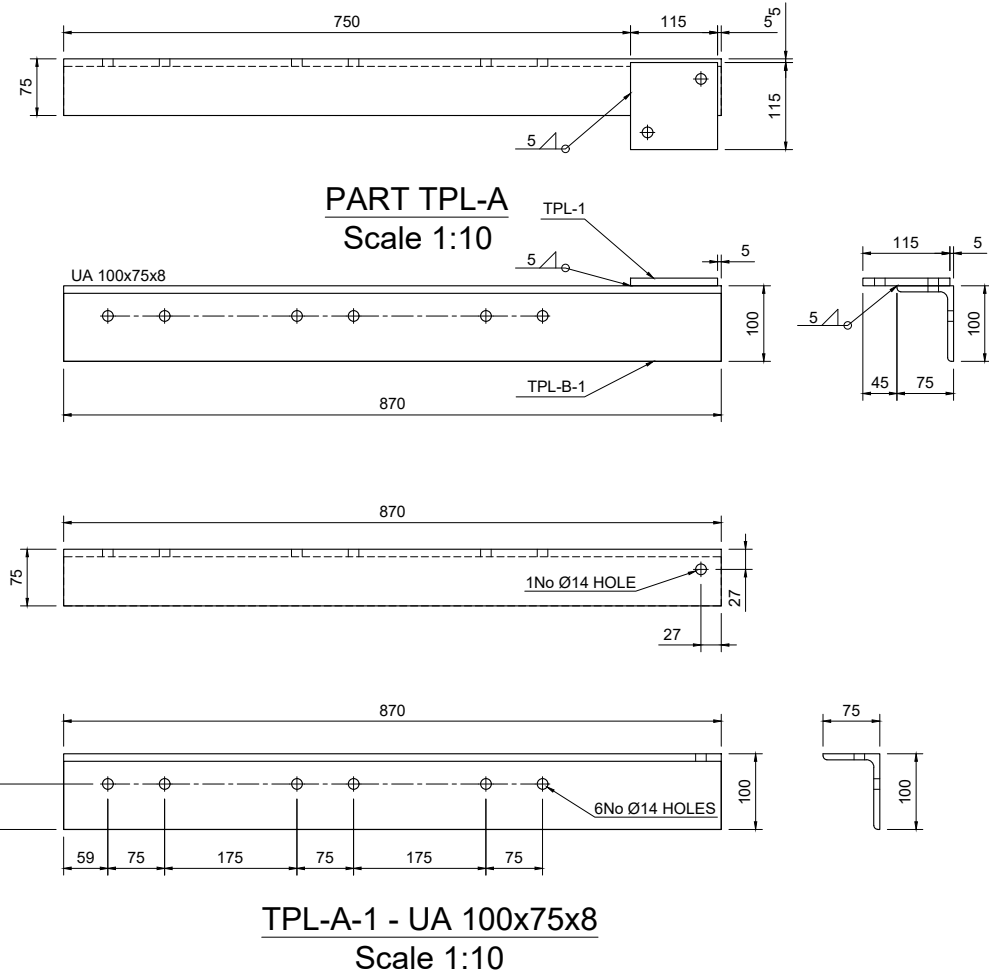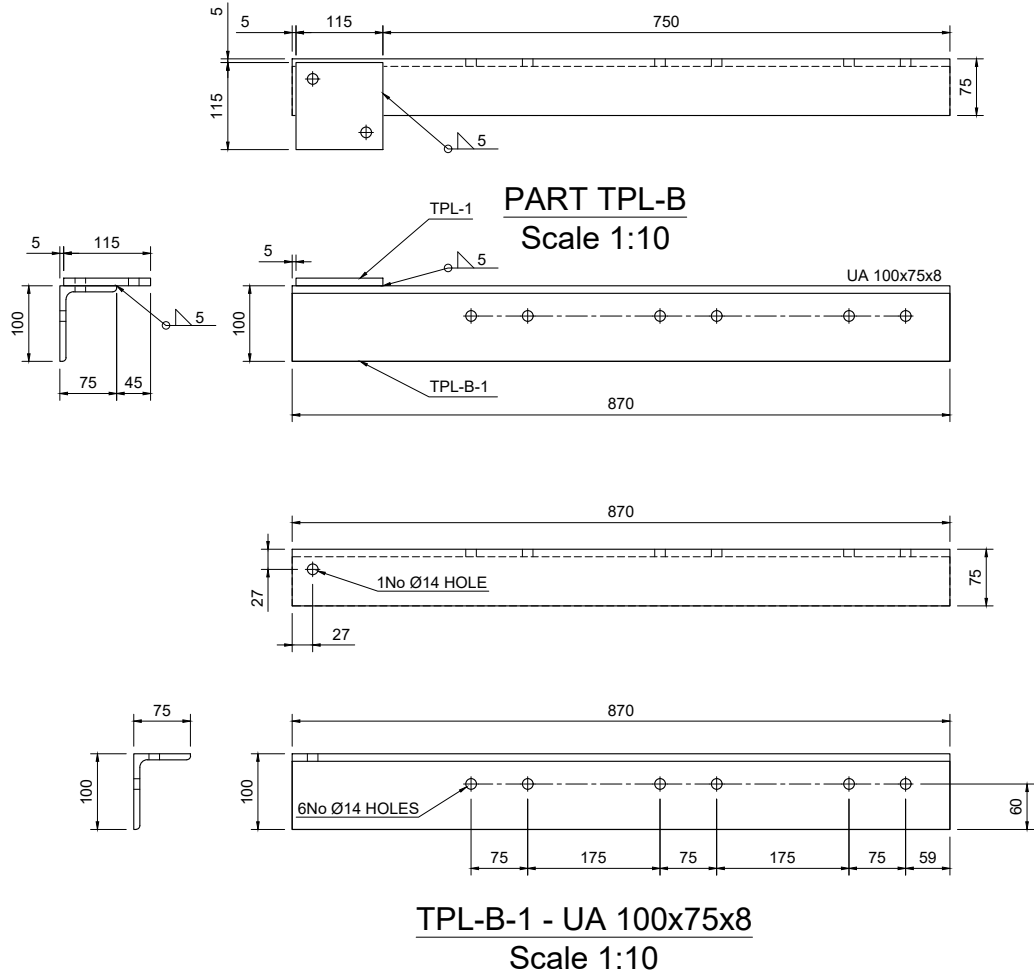

Parts list for TPL-B						
Item	Part	Quantity	Part description	Length	Material	Weight
01	TPL-B-1	1	UA 100x75x8	870mm	S275J0	9.22 kg
02	TPL-1	1	115x115x10mm	N/A	S275J0	1.04 kg
03	U-BOLT	3	M12 U-BOLT FOR CHS 60.3mm	N/A	GRADE 8.8	-
Total Weight:						10.26 kg
- All steel hot dip galvanized - Each U-BOLT to be supplied with 4 Full Nuts, 2 Flat Washers and 2 Spring Washers - For fabrication notes see drawing 304						

Parts list for TPL-A						
Item	Part	Quantity	Part description	Length	Material	Weight
01	TPL-A-1	1	UA 100x75x8	870mm	S275J0	9.22 kg
02	TPL-1	1	115x115x10mm	N/A	S275J0	1.04 kg
03	U-BOLT	3	M12 U-BOLT FOR CHS 60.3mm	N/A	GRADE 8.8	-
Total Weight:						10.26 kg
- All steel hot dip galvanized - Each U-BOLT to be supplied with 4 Full Nuts, 2 Flat Washers and 2 Spring Washers - For fabrication notes see drawing 304						

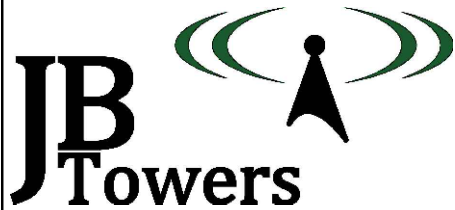

01	FIRST ISSUE			AM	24/04/19
REV	REV			BY	DATE
SCALE AS SHOWN WHEN PRINTED AT A3		DRAWN	AM	CHECKED	MP
		DATE	24/04/19	DATE	24/04/19
				APPROVED	JBT
				DATE	24/04/19
ALL DIMENSIONS IN mm UNLESS OTHERWISE STATED. THIS DRAWING TO BE READ IN CONJUNCTION WITH OTHER RELEVANT DRAWINGS.					

TITLE
LOG MOUNTING BRACKETS
PARTS: TPL-A; TPL-B

SITE ADDRESS
YNYS FARM
YNYS PENNAL
MACHYNLLETH
GWYNEDD
SY20 9LD

ARQIVA REF. 141871	DRG No. 303	REV 01
-----------------------	----------------	-----------

ALL SCALES AS SHOWN WHEN PRINTED AT A3




ALL SCALES AS SHOWN WHEN PRINTED AT A3

Item	Part	Drawing	Quantity	Part description	Length	Material	Weight
01	01	200	1	3 MAN LATCHWAY SYSTEM & 3No. WIRE GUIDES FOR FACE MOUNTED MONOPOLE	17000	N/A	-
02	TPB-C	300	2	FALL ARREST ATTACHMENT POINT	N/A	S275J0	4.48 kg
03	03	200	46	PERMANENT BT STEP c/w 3No 10x75mm ZINC-PLATED COACH SCREWS	N/A	S275J0	13.80 kg
04	TPS-R	300	9	'MonoStep' ASSEMBLY	N/A	S275J0	25.65 kg
05	TPB-A	301	3	MOUNTING BRACKET	N/A	S275J0	20.97 kg
06	06	203	3	CHS 60.3x5mm	2800mm	S355J2H	57.30 kg
07	TPL-A	303	4	LOG MOUNTING BRACKET	870mm	S275J0	41.04 kg
08	TPL-B	303	4	LOG MOUNTING BRACKET	870mm	S275J0	41.04 kg
09	09	203	12	M12 WASHER	N/A	GRADE 8.8	-
10	TPA-PD	302	6	POWER DIVIDER STRAP	N/A	S275J0	7.56 kg
11	11	204	1	CHS 60.3x5mm	500mm	S355J2H	3.41 kg
12	TPY-A	302	1	YAGI MOUNTING BRACKET	350mm	S275J0	5.25 kg
13	TPA-BR	302	2	BRACING KIT	N/A	S275J0	10.06 kg
14	14	200	1	FEEDER COVER - 2/CG/100	3500mm	UV RESISTANT PLASTIC	-
15	15	200	17	FEEDER CLAMP - 2/FCD/028	N/A	POLYPROPYLENE	-
16	16	200	17	M10 SCREW DOWELS WTH M10 NUT	100mm	STAINLESS STEEL	-
17	17	200	1	PoleSaver	750mm	N/A	-
18	18	200	8	M12 STUD + 4No NUTS + 2No FLAT WASHERS + 1No Ø50mm WASHER (FOR FALL ARREST SYSTEM)	500mm	GRADE 8.8	3.56 kg
Total Weight:							234.12 kg

- All steel hot dip galvanized
- All U-BOLTS to be FLA supply, each Supplied with 4 Full Nuts, 2 Flat Washers and 2 Spring Washers

NOTES:

1. WELDING TO BE IN ACCORDANCE WITH BS EN 1011-1:2009
2. LINEAR DIMS TO BE WITHIN ±1mm;
3. ANGULAR TOLERANCES TO BE WITHIN 0.5°
4. WELDING SYMBOLS ARE IN ACCORDANCE WITH BS EN 22553:1995
5. ALL PROFILE EDGES TO BE DRESSED AND SHARP CORNERS REMOVED
6. ALL WELD SIZES ARE FINAL SIZES
7. ALL WELDED JOINTS ARE TO BE PICKLE TIGHT
8. ALL STEELWORK TO BE BS EN 10025 GRADE S275 J0 UNO &
9. HOT DIPPED GALVANISED TO BS EN ISO 1461. (ALL HOLLOW SECTIONS TO BE GRADE S355 J0H)
10. ALL STEEL IS TO BE SUPPLIED IN ACCORDANCE WITH EN 1090 TO EXECUTION CLASS 2
11. ALL NON PRE-LOADED BOLTS TO BE COMPLIANT STRUCTURAL BOLTS TO BS EN ISO 15048 PARTS 1&2.
12. STEELWORK COMPONENTS SHALL BE HOT DIP GALVANISED TO ACHIEVE A "VERY HIGH" DURABILITY FOR AN ENVIRONMENT CATEGORY CODE C4 FROM TABLE 1 IN BS EN ISO 14713
13. BOLTS AND NUTS SHALL BE SUPPLIED IN ACCORDANCE WITH BS 7371, SPUN GALVANISED IN ACCORDANCE WITH ISO 10684, THE NUTS RE-TAPPED AFTER GALVANISING, AND THE THREADS TREATED WITH GREASE.
14. ALL BOLTS TO BE CUT ON SITE TO EXTEND MAX 10mm BEYOND THE NUT WHEN TIGHTENED UNO.
15. ALL SITE DRILLED HOLE/CUT ENDS TO BE TREATED WITH METAFLUX 70-40 ZINC PASTE FOLLOWED BY 1 COAT OF 7-42 ZINC ALU OR 70-16 ALUMINIUM SPRAY

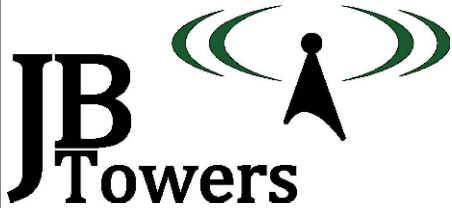

01	FIRST ISSUE							AM	24/04/19
REV	REV							BY	DATE
SCALE AS SHOWN		DRAWN	AM	CHECKED	MP	APPROVED		JBT	
WHEN PRINTED AT A3		DATE	24/04/19	DATE	24/04/19	DATE		24/04/19	
ALL DIMENSIONS IN mm UNLESS OTHERWISE STATED. THIS DRAWING TO BE READ IN CONJUNCTION WITH OTHER RELEVANT DRAWINGS.									

TITLE

PARTS LIST

SITE ADDRESS

YNYS FARM
YNYS PENNAL
MACHYNLLETH
GWYNEDD
SY20 9LD

ARQIVA REF.
141871



DRG No.
304

REV
01

ALL SCALES AS SHOWN WHEN PRINTED AT A3





ALL SCALES AS SHOWN WHEN PRINTED AT A3

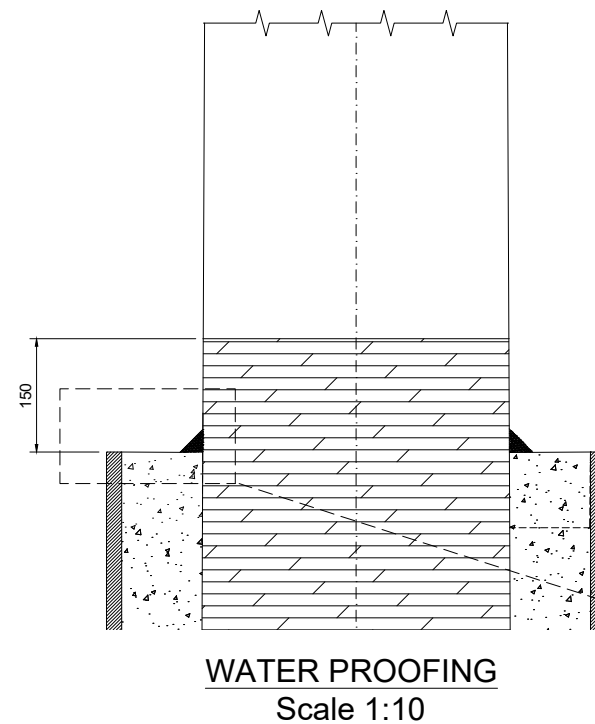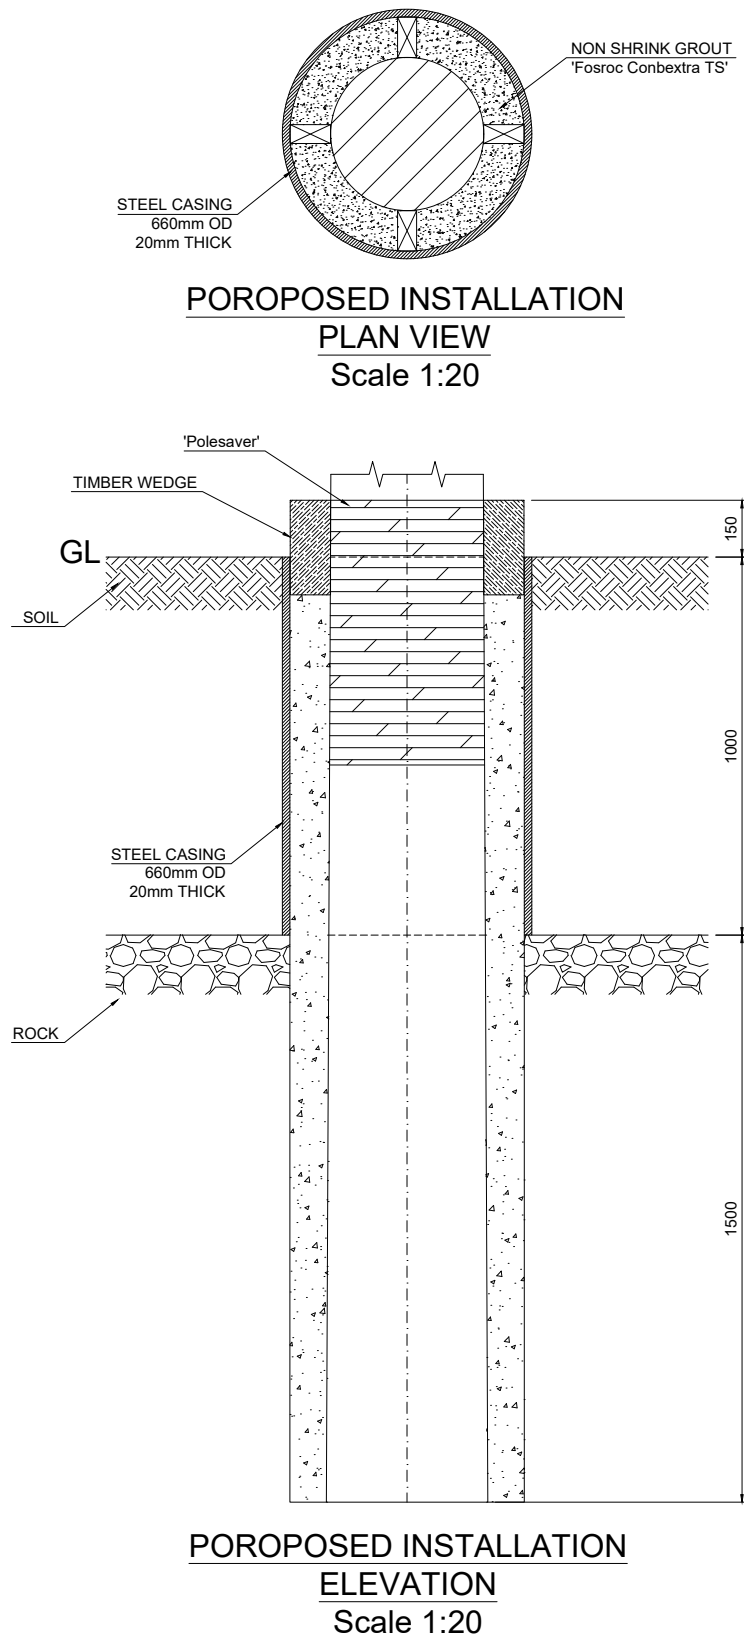

TIMBER POLE INSTALLATION:

1. REFER TO DRAWING 200 FOR TIMBER POLE ORIENTATION
2. BASE OF TIMBER POLE TO BE WRAPPED IN 'polesaver' & INSTALLED AND LEVELLED IN OPENING. TIMBERS TO BE USED TO HOLD POLE IN POSITION & THEN ANNULUS GROUTED UP WITH NON SHRINK GROUT
3. 3.ONCE THE GROUT HAS CURED THE TIMBER WEDGES SHALL BE REMOVED AND VOIDS LEFT ARE TO BE FILLED WITH NON SHRINK GROUT. A 1:60 FALL SHALL BE FORMED AROUND THE TIMBER POLE TO ALLOW WATER TO DRAIN AWAY

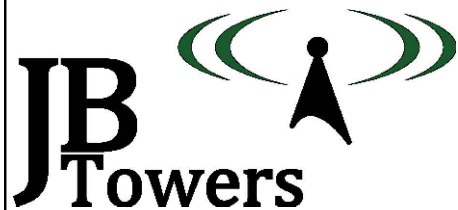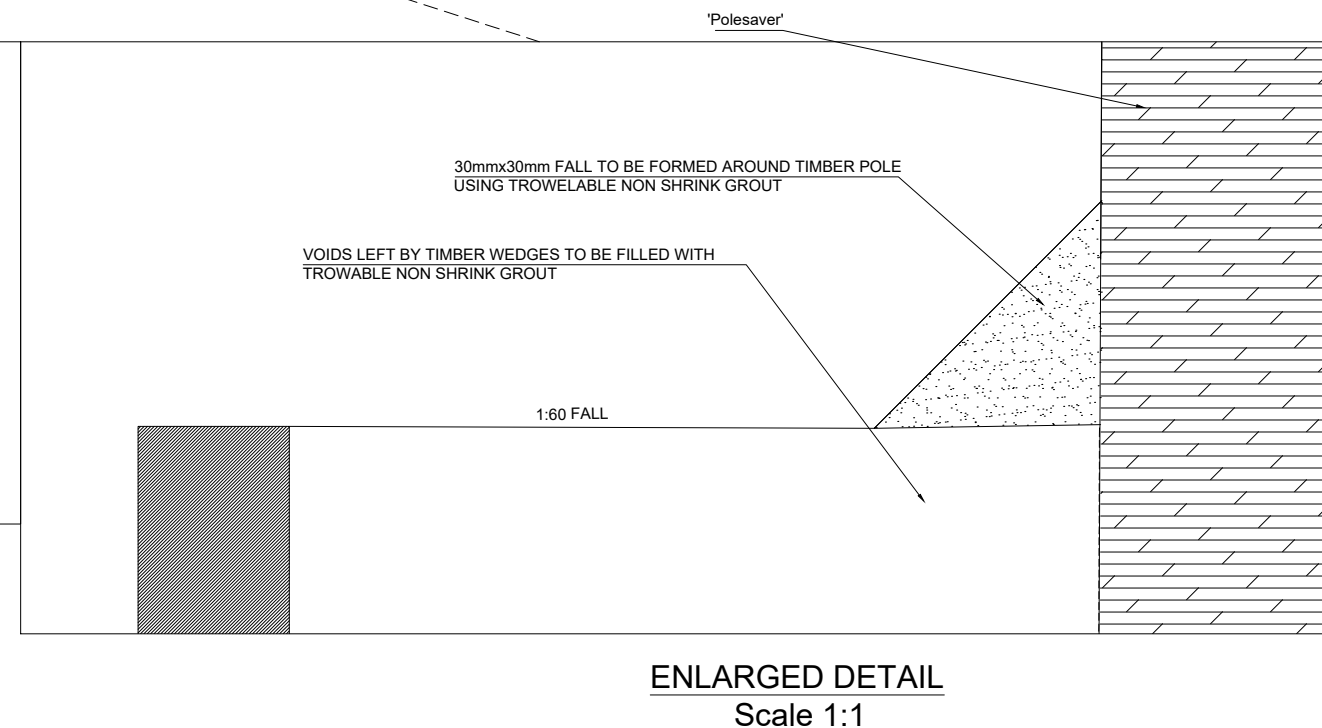


arqiva

01	FIRST ISSUE			AM	24/04/19
REV	REV			BY	DATE
SCALE AS SHOWN		DRAWN	AM	CHECKED	MP
WHEN PRINTED AT A3		DATE	24/04/19	DATE	24/04/19
				APPROVED	JBT
				DATE	24/04/19
ALL DIMENSIONS IN mm UNLESS OTHERWISE STATED. THIS DRAWING TO BE READ IN CONJUNCTION WITH OTHER RELEVANT DRAWINGS.					

TITLE		SITE ADDRESS	
FOUNDATION DETAILS		YNYS FARM YNYS PENNAL MACHYNLLETH GWYNEDD SY20 9LD	
		ARQIVA REF. 141871	DRG No. 400
		REV	01

ALL SCALES AS SHOWN WHEN PRINTED AT A3

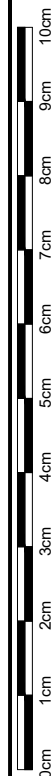

ALL SCALES AS SHOWN WHEN PRINTED AT A3