

DESCRIPTION		FIRST ISSUE				
REV	A	DATE	15/09/15	BY	JDH	CHKD
						OC
						APPD
						KM


GENERAL NOTES

1. STEELWORK TO BE PROTOTYPE CHECK ERECTED BEFORE MASS PRODUCTION.
2. SAFETY SIGNS INSTALLED TO POWERSYSTEMS PROCEDURES.
- 3.FOR FRONT ELEVATION SEE 15_15229_41
4. FOR SIDE ELEVATION SEE 15_15229_42
5. FOR MATERIAL LIST SEE 19_15229_43
6. OPGW AND BACKSTAY ARRGT CAN BE MOUNTED EITHER SIDE OF STRUCTURE. SEE PLAN VIEW.
- 7.FOR STAY WIRE SETTING OUT DETAILS SEE 15_15229_44.
- 8.FOR MAINTENANCE ATTACHMENT LOCATIONS SEE LSTC/STD/GNA/553.


FOR FOUNDATION DETAILS FOR VARYING SOIL CONDITIONS SEE INFORMATION LISTED BELOW:

GOOD: AS PER THIS DWG
AVERAGE: AS PER THIS DWG
POOR: 16_15229_50
VERY POOR: 16_15229_51

ALTERNATIVE U/GROUND CABLE ARRANGEMENT WITH REDUCED BEND RADIUS SHOWN DOTTED

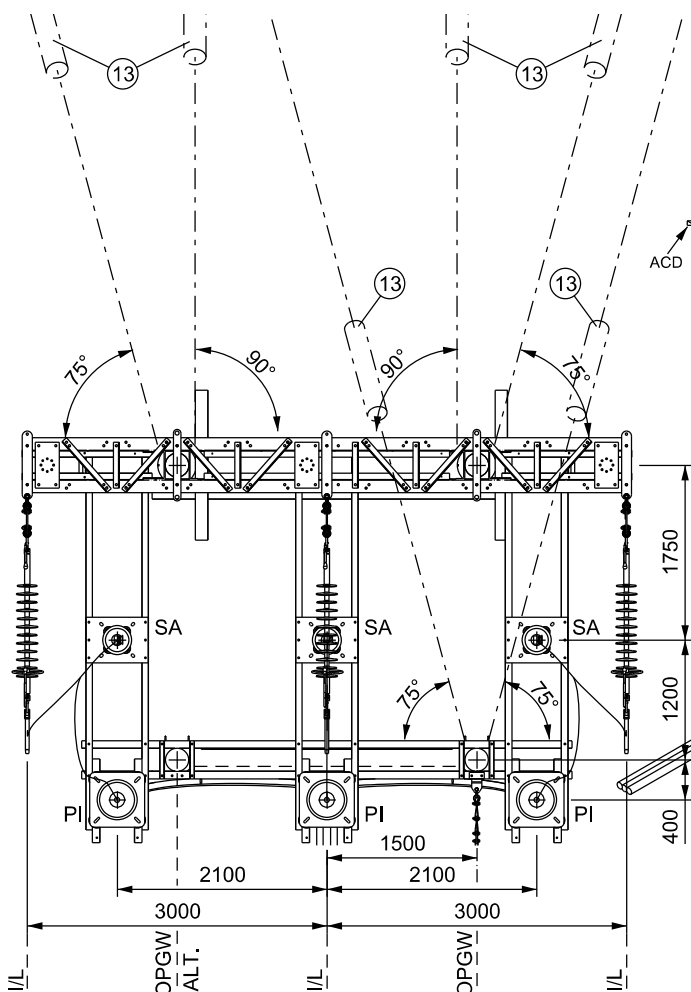

PLAN VIEW

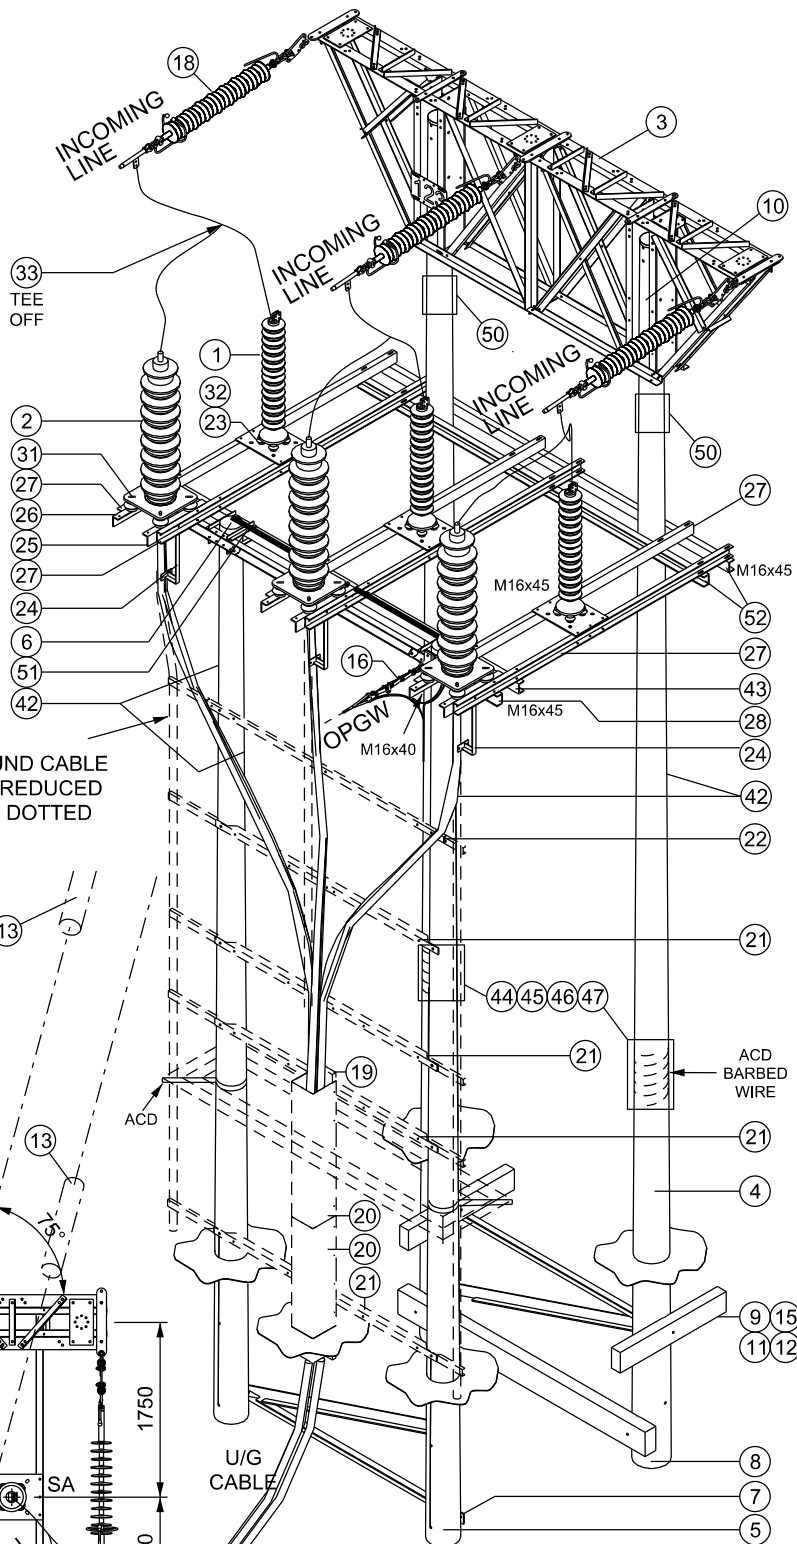

ISOMETRIC VIEW

(BACKSTAYS NOT SHOWN FOR CLARITY)

ALL CABLE FIXINGS, SUPPORTS AND GUARDING TO BE SPECIFIED AND SUPPLIED BY CABLE CONTRACTOR